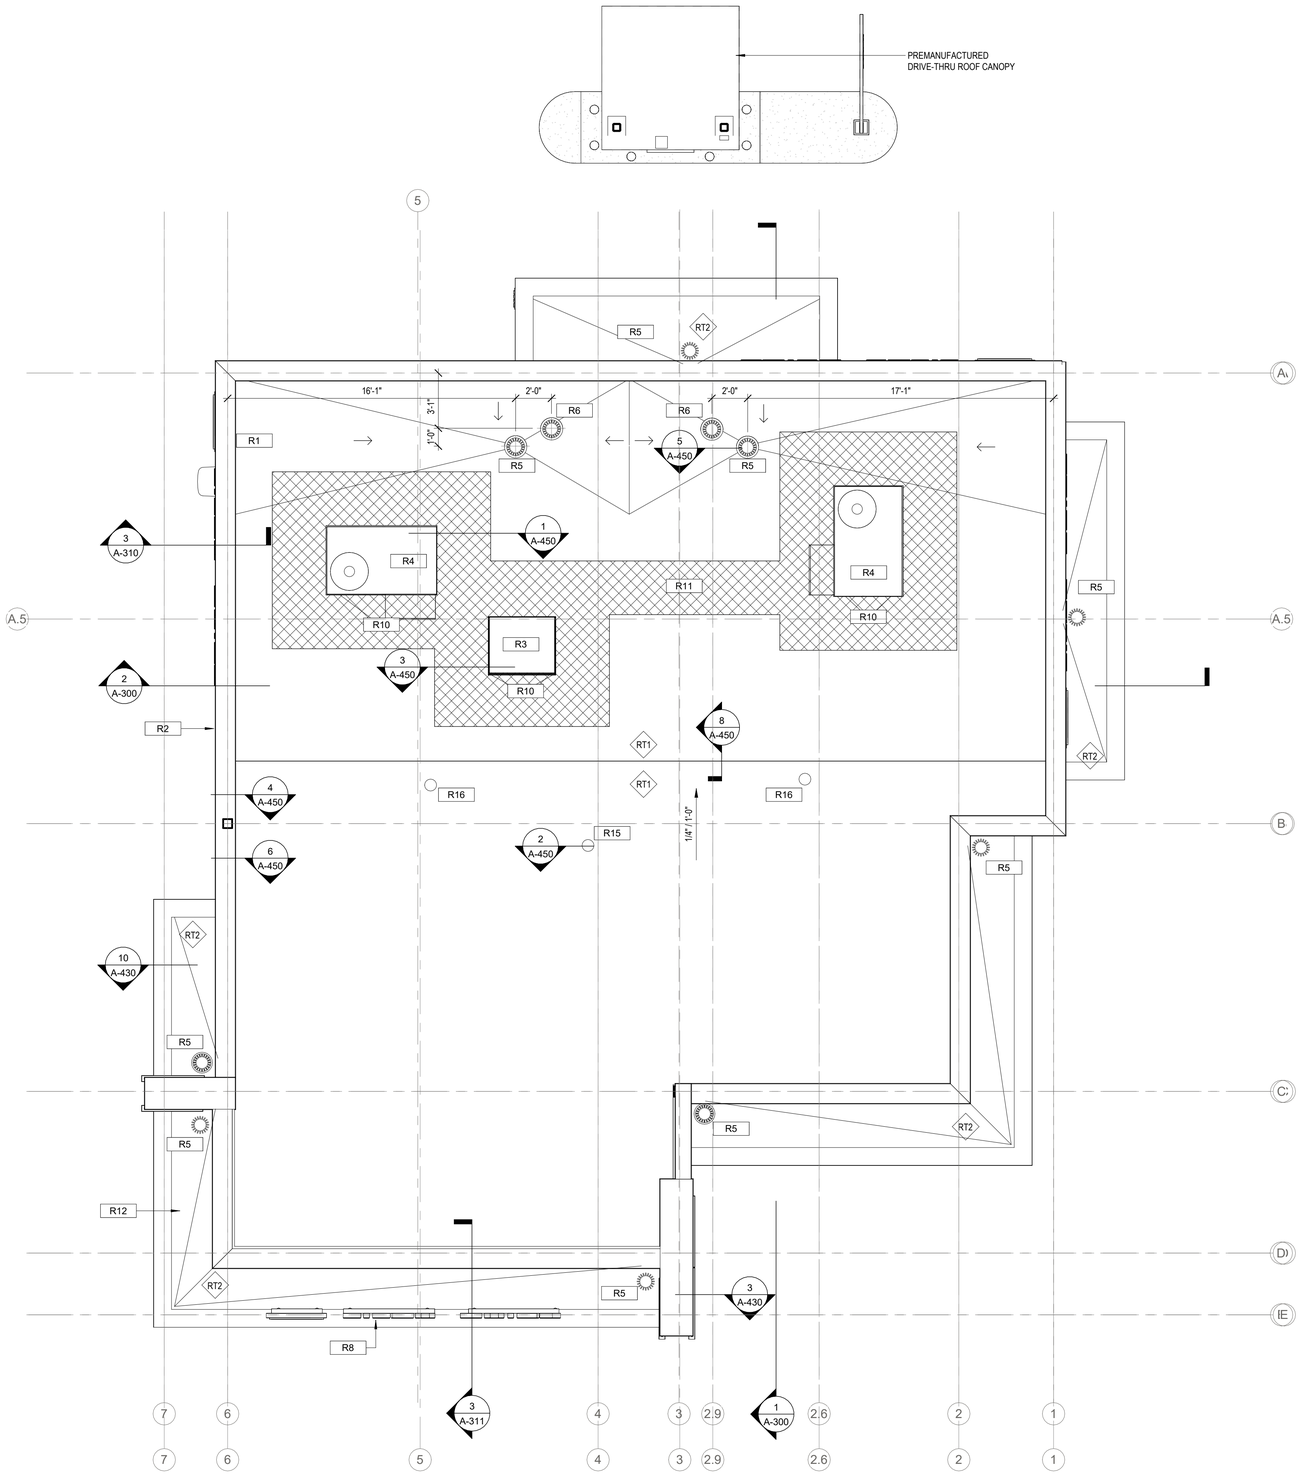



GENERAL NOTES - ROOF PLAN

1. ROOF CRICKETS 1/4" PER FOOT MINIMUM, FULLY TAPERED POLYISOCYANURATE INSULATION
2. INSTALL ALL ROOF SYSTEMS AND RELATED COMPONENTS IN STRICT ACCORDANCE WITH MANUFACTURER'S SPECIFICATIONS AND INSTALLATION INSTRUCTIONS
3. VERIFY AND COORDINATE LOCATION OF ALL ROOF PENETRATIONS WITH STRUCTURAL, MECHANICAL, ELECTRICAL, AND PLUMBING.
4. ALL ROOF PENETRATIONS REQUIRE PRESSURE TREATED 2x6 BLOCKING AT INSULATION AROUND ENTIRE PERIMETER FOR FLASHING ATTACHMENT.
5. OMISSION OF ANY ACCESSORY FROM THE ROOF PLAN SHALL NOT RELIEVE THE CONTRACTOR FROM THE RESPONSIBILITY FOR SUCH ITEMS.


KEY NOTES - ROOF PLAN

R1	WEATHER SENSOR, REF. LANDSCAPE
R2	CONT. METAL COPING TO COVER ENTIRE TOP OF PARAPET
R3	30" x 36" ROOF ACCESS HATCH
R4	MECHANICAL ROOF TOP UNIT
R5	ROOF DRAIN
R6	OVERFLOW ROOF DRAI
R7	RESERVED
R8	MAIN ENTRY CANOPY MOUNTED SIGNAGE
R9	RESERVED
R10	TAPERED INSULATION / ROOF CRICKETS POSITIVE SLOPE TOWARDS DRAIN
R11	HATCH INDICATES TPO WALKWAY PAD MEMBRANE
R12	PRE-FINISHED ALUMINUM COMPOSITE CLAD AWNING, ACM-3
R15	VENT STACK. REFER TO PLUMBING DRAWINGS FOR LOCATION
R16	NO VENT STACK SHALL BE LOCATED WITHIN 10'-0" RADIUS OF AN RTU INTAKE. COORDINATE WITH MECHANICAL.

ROOF TYPES

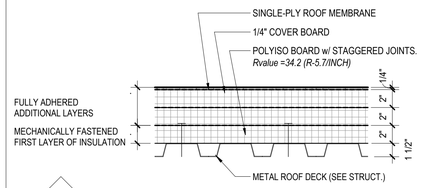

RT1 — ROOF MEMBRANE SYSTEM OVER SLOPED METAL ROOF DECK (SEE STRUCT)
(6" MIN INSULATION THICKNESS) R-VALUE = 34
NOTE: SEE ROOF PLAN FOR TAPERED INSULATION LOCATIONS

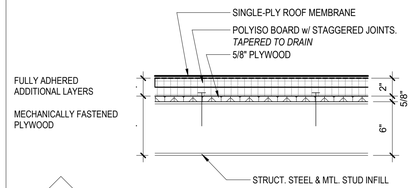

RT2 — ROOF MEMBRANE SYSTEM OVER FLAT ROOF DECK (SEE STRUCT)
NOTE: TAPER INSULATION TO ROOF DRAIN, 1" MIN. INSULATION THICKNESS

NOTE: PROJECT NORTH IS FOR CONSTRUCTION PURPOSES ONLY. REFER TO CIVIL DRAWING FOR TRUE NORTH AND CORRECT BUILDING ORIENTATION AS IT RELATES TO THE SITE.

ROOF PLAN | 1/4" = 1'-0" | 1

PRAXIS3
100 Peachtree St NW
Suite 1450
Atlanta, GA 30303
404-875-4500 tel
www.praxis3.com

STATE OF GEORGIA
STUART M. ROMM
07/02/26
CERTIFICATE NO. 3457
REGISTERED ARCHITECT

Copyright (c) 2026 Praxis3, LLC

All reports, plans, specifications, computer files, field data, notes and other documents and instruments prepared by Praxis3 shall retain all common law, statutory and other reserved rights, including copyright thereto.

This drawing may not be reproduced in whole or in part without written permission of Praxis3. It is to be returned upon request. Scales as stated are valid on the original drawings.

Rev	Date	Comments
	07/02/2026	PERMIT SET

Client:
FIFTH THIRD BANK

Project Number: 26302
Project Name:
WATSON BLVD.

2711 WATSON BOULEVARD
WARNER ROBINS, GA 31093

Key Plan:

Sheet Title:
ROOF PLAN

Sheet Number:
A-140

7/8/2026 2:37:50 PM