SWATCHES

ACM-1

ACM-2

ACM-3
M-1
AL-1
AL-2

EIFS-1

EXT-1
EXT-2


GL-1

EXTERIOR FINISH SCHEDULE


ITEM	EXTERIOR FINISH	MANUFACTURER	COLOR	COMMENTS
ACM-1	ALUMINUM COMPOSITE METAL PANEL	ALCOA ARCHITECTURAL REYNOBOND	CUSTOM FIFTH THIRD BLUE	4MM FR CORE ALUM. COMPOSITE PANEL, DURAGLOSS 3000
ACM-2	ALUMINUM COMPOSITE METAL PANEL	ALCOA ARCHITECTURAL REYNOBOND	CUSTOM FIFTH THIRD GREEN	4MM FR CORE ALUM. COMPOSITE PANEL, DURAGLOSS 3000
ACM-3	ALUMINUM COMPOSITE METAL PANEL	ALCOA ARCHITECTURAL REYNOBOND	ANODIC CLEAR	4MM FR CORE ALUM. COMPOSITE PANEL, COLORWELD 500
AL-1	ANODIZED ALUMINUM	YKK	CLEAR ANODIZED	BASIS OF DESIGN: 2" X 4 1/2" YKK YES45 TU CENTER SET STOREFRONT
EIFS-1	EIFS BARRIER SYSTEM	DRYVIT OUTSULATION PLUS MD	DOVER SKY	3" EIFS SYSTEM - TYP., SANDBLAST FINISH
EIFS-2	EIFS BARRIER SYSTEM	DRYVIT OUTSULATION PLUS MD	DOVER SKY	5" EIFS SYSTEM @ VESTIBULE PARAPET, SANDBLAST FINISH
EPT-1	PAINTED GALVANIZED STEEL GATE	BENJAMIN MOORE	BALBOA MIST - OC27	SEMI-GLOSS @ STEEL, SATIN FINISH @ WALLS
EXT-1	STANDARD MODULAR BRICK VENEER	ACME BRICK	SLATE GRAY	MORTAR MANUFACTURER: COOSA , MORTAR COLOR: OLD LIME PUTTY
GL-1	EXTERIOR GLAZING	VITRO	SOLARBAN 90 ACUITY + ACUITY	ARGON U-0.24, SHCC=0.23
M-1	PREFINISHED METAL COPING	PAC-CLAD	MATCH ACM-3	




SOUTH ELEVATION | 3/16" = 1'-0" | 4

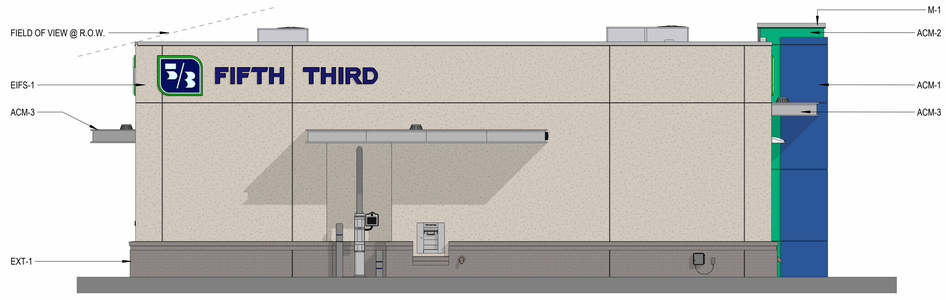

EAST ELEVATION | 3/16" = 1'-0" | 3

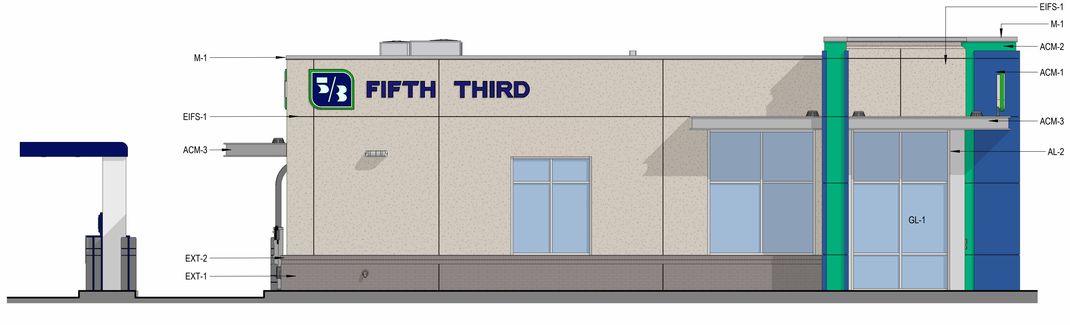

NORTH ELEVATION | 3/16" = 1'-0" | 2

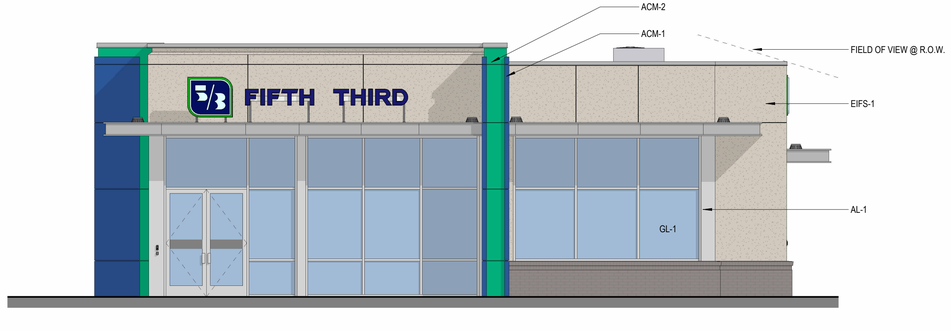

WEST ELEVATION | 3/16" = 1'-0" | 1

7/8/2026 2:38:22 PM

PRAXIS3

100 Peachtree St NW
Suite 1450
Atlanta, GA 30303

404-875-4500 tel
www.praxis3.com

STATE OF GEORGIA
STUART M. ROMM
07/02/26
CERTIFICATE NO. 34521
REGISTERED ARCHITECT

Copyright (c) 2026 Praxis3, LLC

All reports, plans, specifications, computer files, field data, notes and other documents and instruments prepared by Praxis3 shall retain all common law, statutory and other reserved rights, including copyright thereto.

This drawing may not be reproduced in whole or in part without written permission of Praxis3. It is to be returned upon request. Scales as stated are valid on the original drawings.

Rev	Date	Comments
	07/02/2026	PERMIT SET

Client:
FIFTH THIRD BANK

Project Number: 26302
Project Name:
WATSON BLVD.

2711 WATSON BOULEVARD
WARNER ROBINS, GA 31093

Key Plan:

Sheet Title:
COLOR EXTERIOR ELEVATIONS

Sheet Number:
A-202