

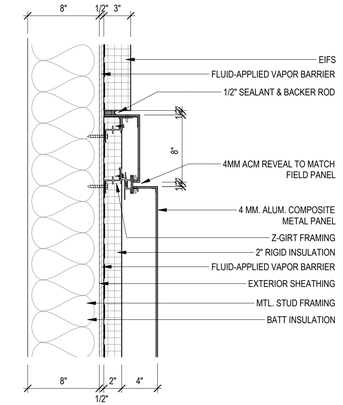


WING WALL JOINT @ EIFS | 1 1/2" = 1'-0" | 11

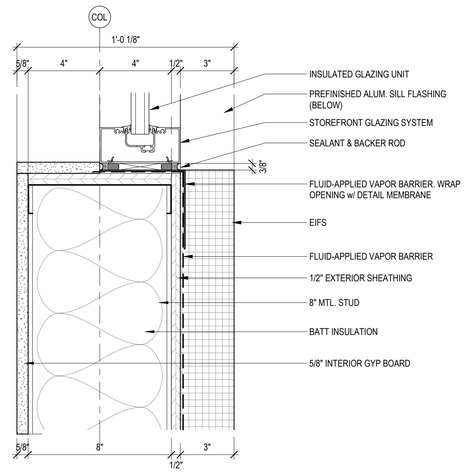


STOREFRONT JAMB @ TYP. EIFS | 3" = 1'-0" | 10

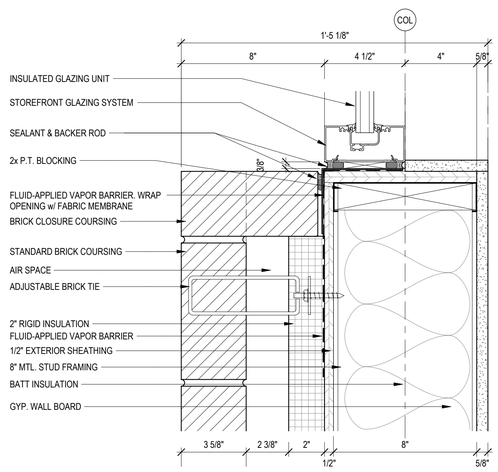


STOREFRONT JAMB @ TYP. BRICK | 3" = 1'-0" | 9

VAPOR BARRIER FLASHING SEQUENCE:
1. INSTALL FLUID-APPLIED AIR BARRIER TO ENTIRE FACADE AND TAKE MATERIAL TO EDGE OF ALL OPENINGS
2. INSTALL FLASHING TAPE AT SILL
3. INSTALL CORNER FLASHING OVER TAPE
4. INSTALL SELF-ADHERING METAL CLAD FLASHING TO SILL
5. INSTALL FLASHING TAPE AT JAMBS
6. INSTALL FLASHING TAPE AT HEAD
7. INSTALL SELF-ADHERING METAL CLAD FLASHING AT HEAD
8. INSTALL TERMINATION BAR AND SEALANT AT TOP OF HEAD FLASHING


NOTE:
-NO REVERSE LAPS
-INTERIOR AND EXTERIOR LAPS TO BE 4" MIN.

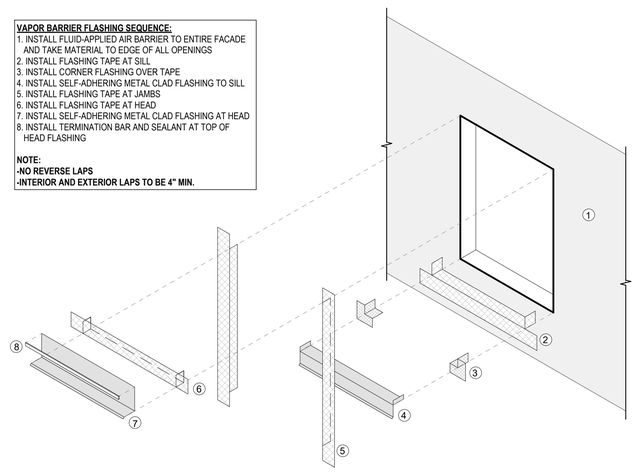


VAPOR BARRIER FLASHING SEQUENCE | 1/2" = 1'-0" | 8

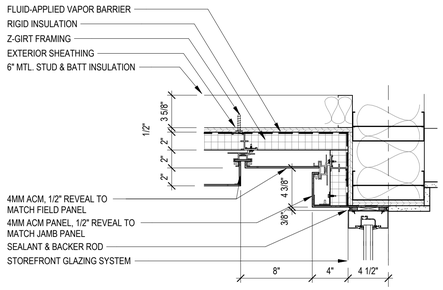


STOREFRONT JAMB @ WING WALL | 1 1/2" = 1'-0" | 7

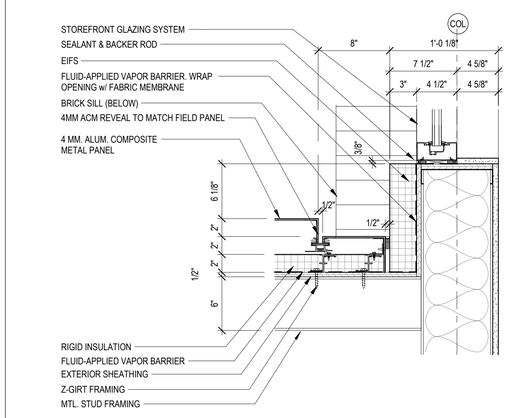


STOREFRONT JAMB @ WING WALL | 1 1/2" = 1'-0" | 6

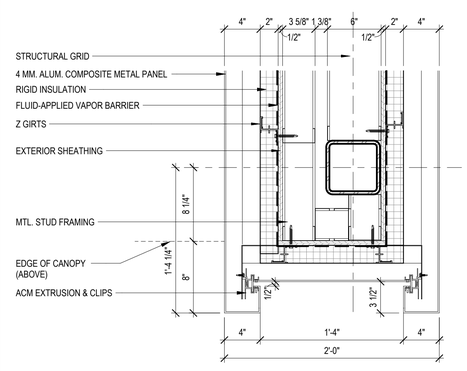


WING WALL (LONG) PLAN DETAIL | 1 1/2" = 1'-0" | 5

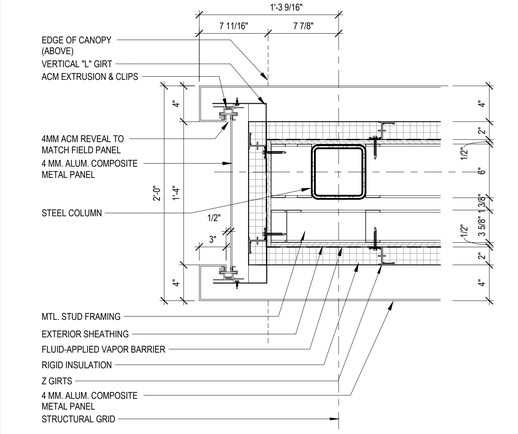


WING WALL (SHORT) PLAN DETAIL | 1 1/2" = 1'-0" | 4

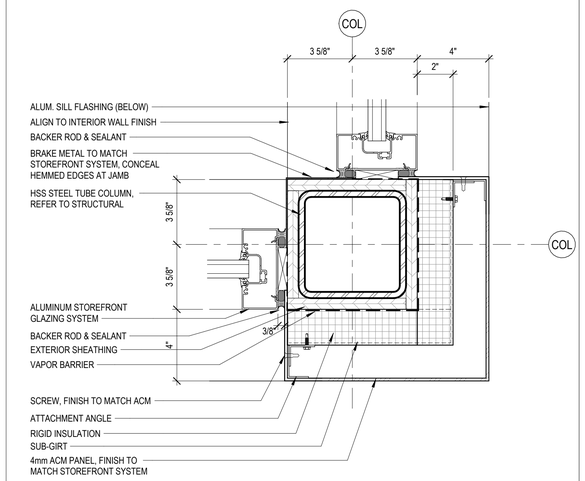

STOREFRONT JAMB @ CORNER | 3" = 1'-0" | 3

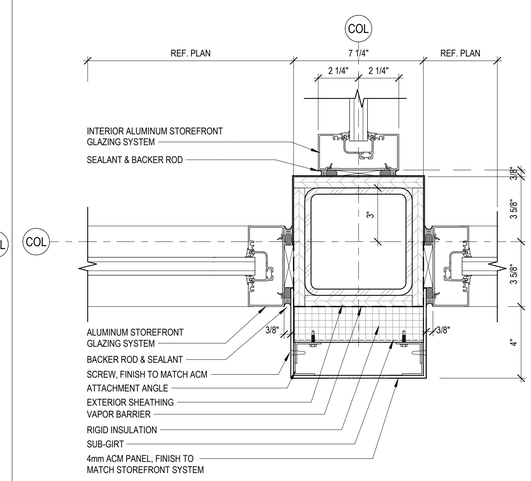

STOREFRONT JAMB @ VESTIBULE CORNER | 3" = 1'-0" | 2

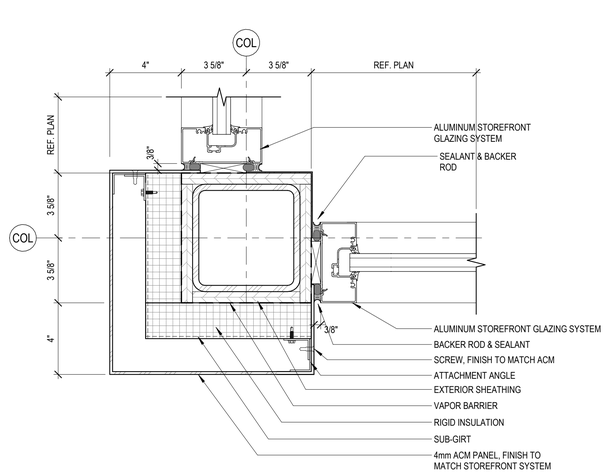

STOREFRONT JAMB @ VESTIBULE COLUMN | 3" = 1'-0" | 1

PRAXIS3
100 Peachtree St NW
Suite 1450
Atlanta, GA 30303
404-875-4500 tel
www.praxis3.com

STATE OF GEORGIA
STUART M. ROMM
07/02/26
CERTIFICATE NO. 3457
REGISTERED ARCHITECT

Copyright (c) 2026 Praxis3, LLC

All reports, plans, specifications, computer files, field data, notes and other documents and instruments prepared by Praxis3 shall retain all common law, statutory and other reserved rights, including copyright thereto.

This drawing may not be reproduced in whole or in part without written permission of Praxis3. It is to be returned upon request. Scales as stated are valid on the original drawings.

Rev	Date	Comments
	07/02/2026	PERMIT SET

Client:
FIFTH THIRD BANK

Project Number: 26302
Project Name:
WATSON BLVD.

2711 WATSON BOULEVARD
WARNER ROBINS, GA 31093

Key Plan:

Sheet Title:
PLAN DETAILS

Sheet Number:
A-440

7/8/2026 2:38:42 PM