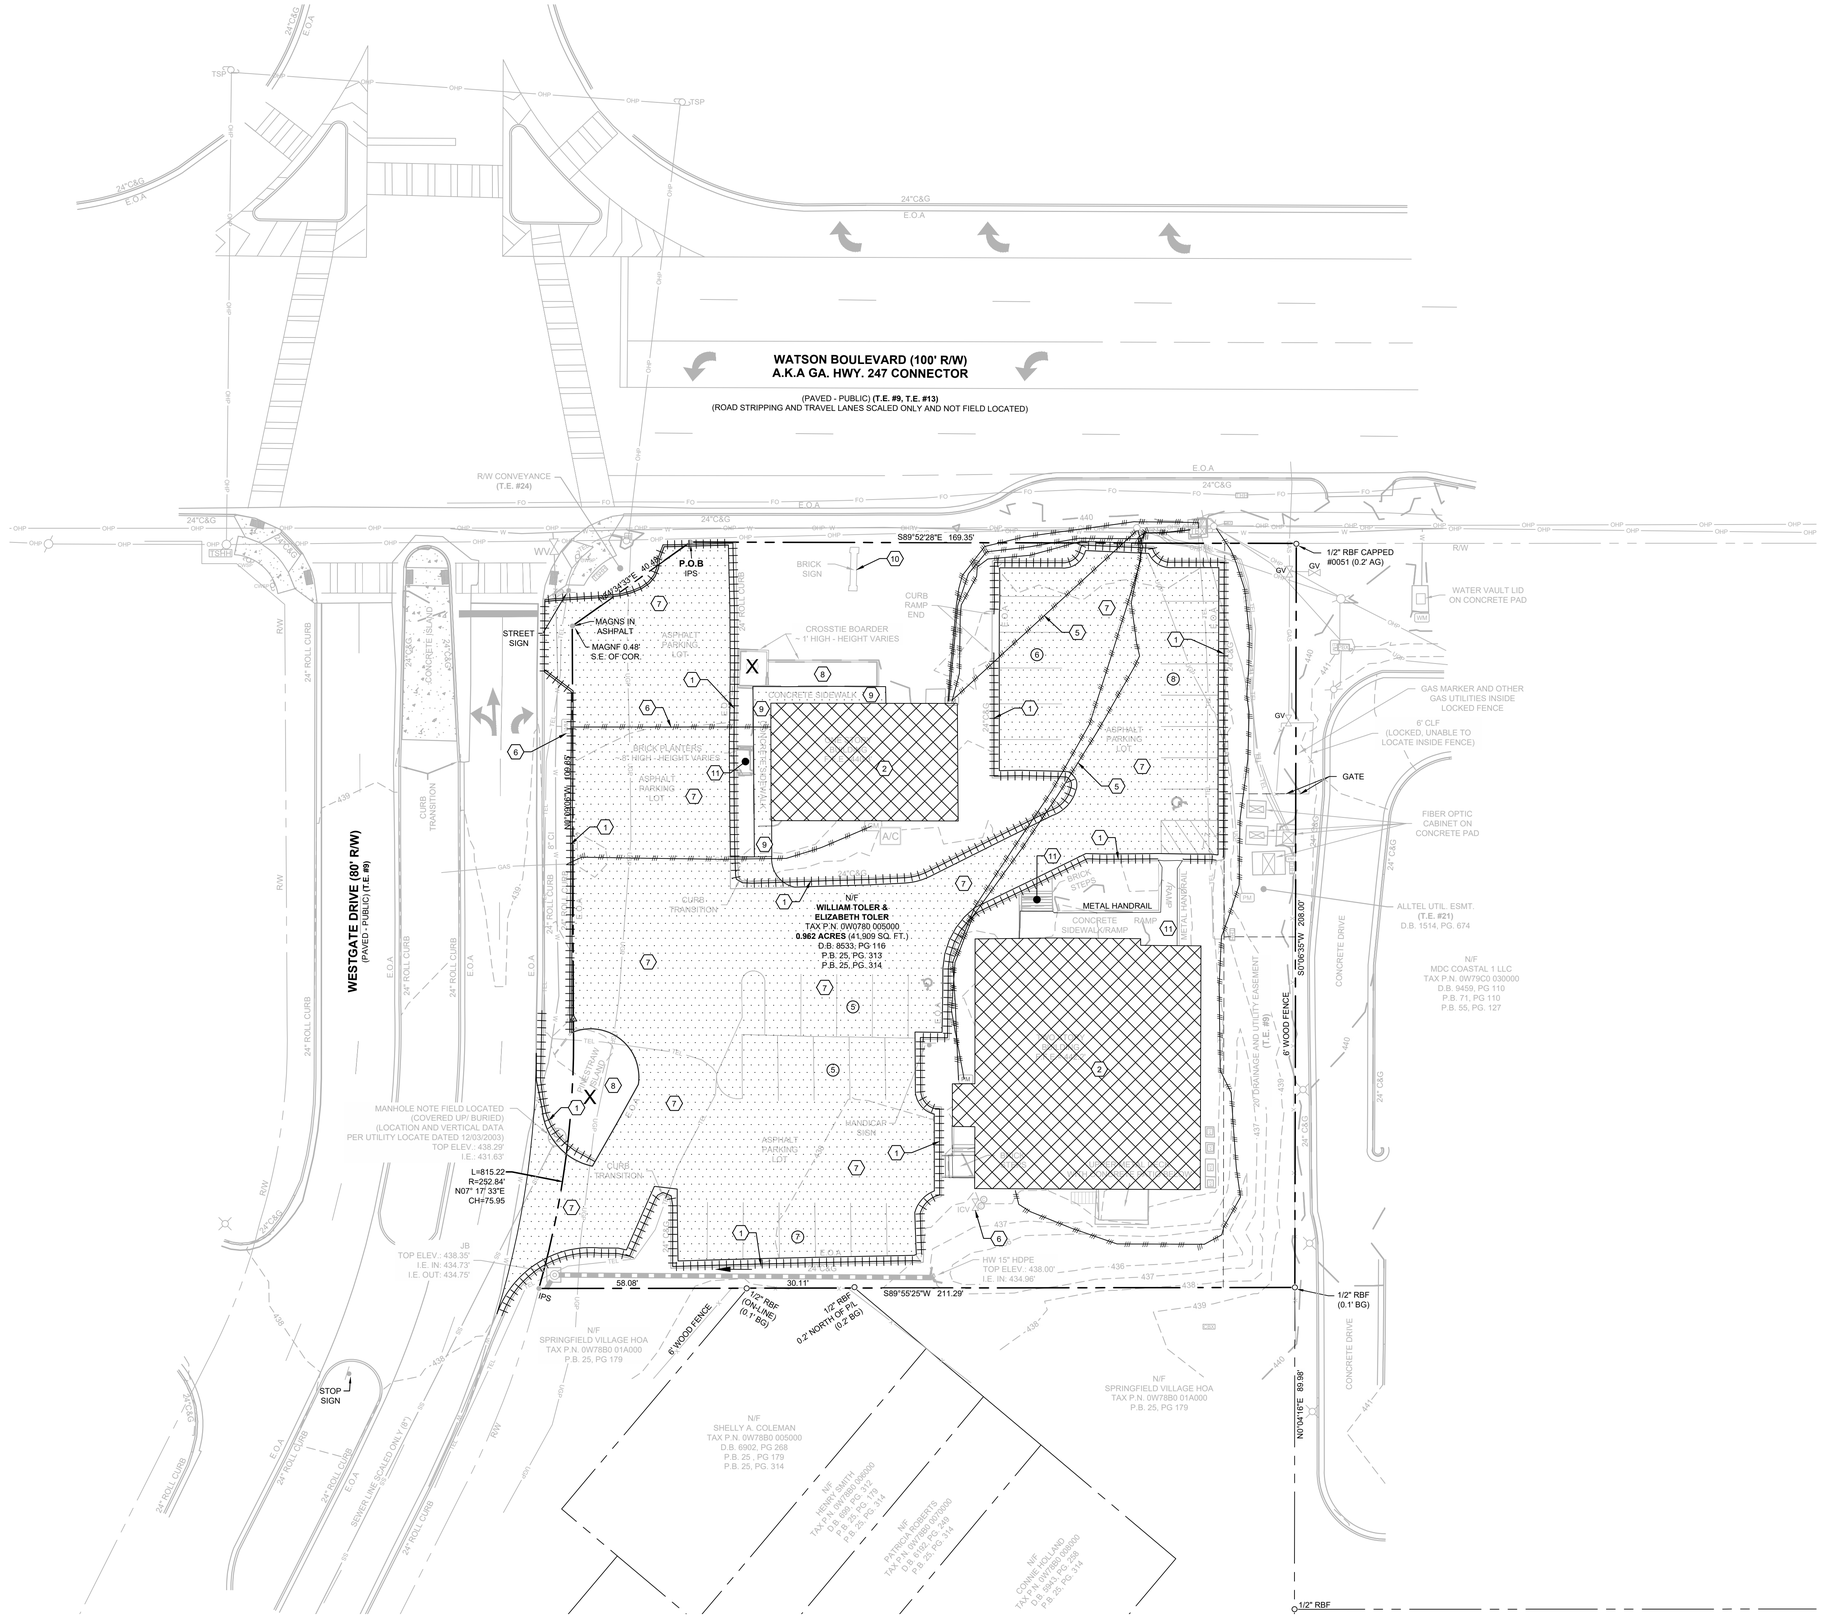


GENERAL DEMOLITION NOTES

1) CONTRACTOR TO ENSURE ALL APPROPRIATE EROSION CONTROL MEASURES, INCLUDING TREE PROTECTION FENCING, ARE IN PLACE PRIOR TO ANY DEMOLITION ACTIVITY TAKING PLACE.

2) CONTRACTOR TO ABIDE BY ALL APPLICABLE FEDERAL, STATE, AND LOCAL LAWS CONCERNING THE REMOVAL, DEMOLITION, AND/OR DISPOSAL OF POSSIBLE HARMFUL MATERIALS INCLUDING LEAD PAINT, ASBESTOS, ETC. DURING ALL PHASES OF CONSTRUCTION.

3) CONTRACTOR TO SAW CUT EXISTING PAVEMENT FULL DEPTH AT EDGE OF DEMOLITION LIMITS.

4) ALL ITEMS NOTED FOR REMOVAL/DEMOLITION SHALL BE REMOVED FROM THE SITE OR DISPOSED OF IN A LEGAL MANNER.

5) BOUNDARY & TOPOGRAPHIC SURVEY BY GASKINS+LECRAW, A PAPE DAWSON COMPANY, DATED 05.08.2026. BENCHMARK IS NOTED ON SURVEY.

6) FLOOD PLAIN IS NOT PRESENT ON THIS SITE AS SHOWN ON THE FEMA FIRM MAP NUMBER 13153C0085E, DATED 09.28.2007.

7) VERTICAL DEPTH OF ALL DRY AND PRESSURIZED UTILITIES IS UNKNOWN. CONTRACTOR TO NOTIFY OWNER AND ENGINEER IMMEDIATELY IF ANY CONFLICTS ARE FOUND.

LEGEND

- DEMOLISH EXISTING STRUCTURES
- DEMOLISH EXISTING PAVEMENT
- DEMOLISH EXISTING UTILITIES
- DEMOLISH EXISTING CURB/GUTTER
- X — DEMOLISH EXISTING TREE

KEY NOTES

1	REMOVE EXISTING CURB & GUTTER
2	REMOVE EXISTING BUILDING/STRUCTURE AND FOUNDATION
3	REMOVE EXISTING SANITARY SEWER LINE AND ASSOCIATED STRUCTURES, CONTRACTOR TO COORDINATE WITH APPROPRIATE UTILITY COMPANY AS NECESSARY
4	REMOVE EXISTING STORM SEWER LINE AND ASSOCIATED STRUCTURES, CONTRACTOR TO COORDINATE WITH APPROPRIATE UTILITY COMPANY AS NECESSARY
5	REMOVE EXISTING POWER LINE AND ASSOCIATED STRUCTURES, CONTRACTOR TO COORDINATE WITH APPROPRIATE UTILITY COMPANY AS NECESSARY
6	REMOVE EXISTING WATER LINE AND ASSOCIATED STRUCTURES, CONTRACTOR TO COORDINATE WITH APPROPRIATE UTILITY COMPANY AS NECESSARY
7	EXISTING PAVEMENT TO BE REMOVED
8	EXISTING TREE/VEGETATION TO BE REMOVED
9	REMOVE EXISTING SIDEWALK
10	REMOVE EXISTING MONUMENT SIGN
11	REMOVE EXISTING CONCRETE RAMP AND STAIRS

CAUTION

THE UTILITES SHOWN ARE SHOWN FOR THE CONTRACTORS CONVENIENCE ONLY. THERE MAY BE OTHER UTILITIES NOT SHOWN ON THESE PLANS. THE ENGINEER ASSUMES NO RESPONSIBILITY FOR THE LOCATIONS OF UNDERGROUND UTILITIES, AND IT SHALL BE THE CONTRACTORS RESPONSIBILITY TO VERIFY THE LOCATIONS OF ALL UTILITIES SHOWN AS WELL AS THOSE NOT SHOWN WITHIN THE CONSTRUCTION LIMITS. ALL DAMAGE MADE TO EXISTING UTILITIES BY THE CONTRACTOR SHALL BE THE RESPONSIBILITY OF THE CONTRACTOR.

PREPARED IN THE OFFICE OF:
GASKINS +LECRAW
a PAPE-DAWSON company

© 2026 GASKINS + LECRAW

3475 CORPORATE WAY
SUITE A
DULUTH, GA 30096
PHONE - 678.546.8100
www.gaskinslecraw.com
PEF008127

REVISIONS:

REV. #	DATE	DRAWN BY:	CHECKED BY:
1			

CLIENT
PRAXIS3
100 PEACHTREE STREET NW, SUITE 1450, ATLANTA, GEORGIA 30303

PROJECT
FIFTH THIRD BANK - WARNER ROBINS, GA
2711 WATSON BLVD
PARCEL ID: 0W0780-005000
WARNER ROBINS, HOUSTON COUNTY, GEORGIA

SEAL:

GEORGIA REGISTERED No. PE036681 PROFESSIONAL ENGINEER TIMOTHY KYLE SHARPE
7/9/2026

CALL BEFORE YOU DIG
811 Know what's below. Call before you dig.

SCALE & NORTH ARROW:
NORTH ARROW
0' 10' 20' 40'
SCALE: 1" = 20'

DESIGN INFO:

DRAWN BY:	JOA
DESIGNED BY:	MAT
REVIEWED BY:	TKS
JOB #:	7567007
DATE:	JULY 9, 2026

DEMOLITION PLAN

C-1.0

Drawing name: C:\Users\kdentz\Gaskins+LeCraw Dropbox\Shared Folders\Engineering\7567007 - Praxis3 - Fifth Third - Warner Robins_GA\CADD\CONSTR\7567007 - 02 - DEMO.dwg DEMOLITION PLAN Jul 09, 2026 10:49am by: cklentz

This document, together with the concepts and designs presented herein, as an instrument of service, is intended only for the specific purpose and client for which it was prepared. Reuse of and improper reliance on this document without written authorization and adaptation by Gaskins + LeCraw, a Pape-Dawson Company shall be without liability to Gaskins + LeCraw, a Pape-Dawson Company, Copyright Gaskins + LeCraw, a Pape-Dawson Company, 2026