

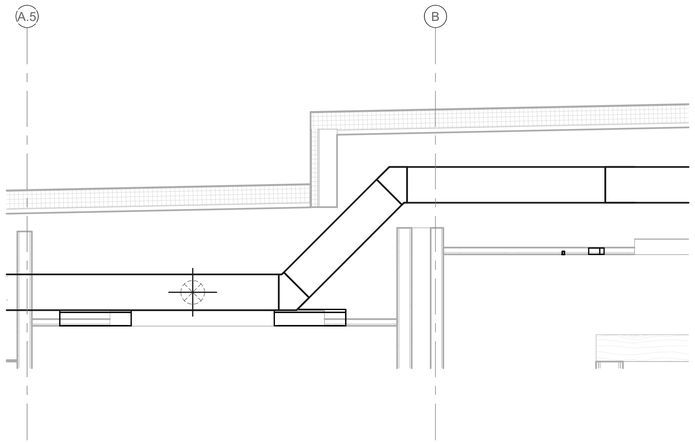



1 M-402 RTU-1 Supply Duct Up
1/2" = 1'-0"

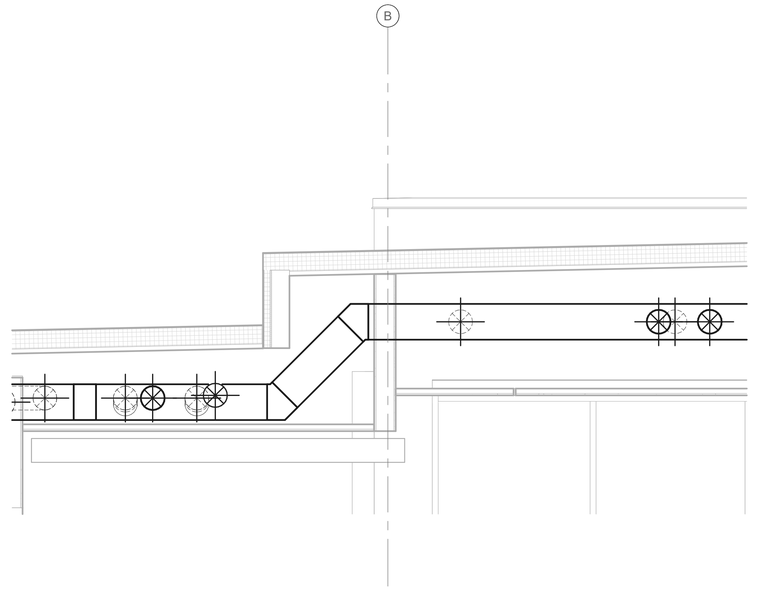

2 M-402 RTU-2 Supply Duct Up
1/2" = 1'-0"

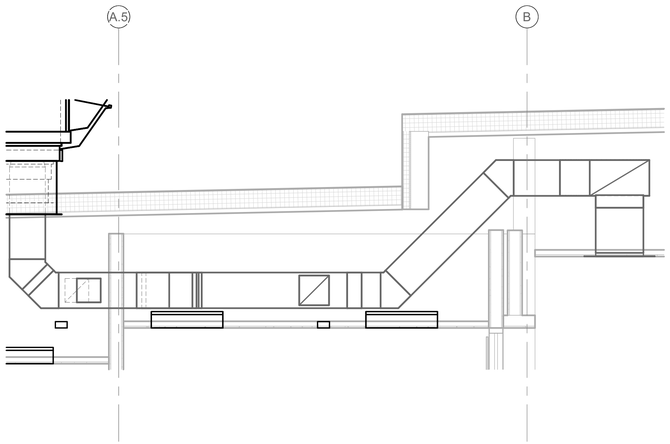

3 M-402 RTU-1 Return Duct Up
1/2" = 1'-0"

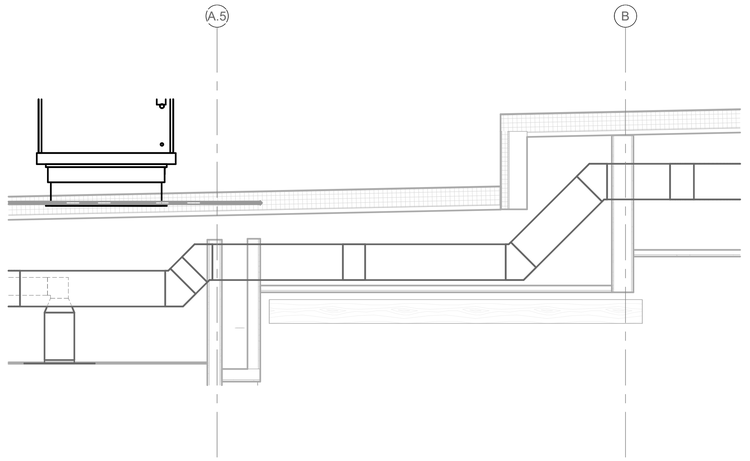

4 M-402 RTU-2 Return Duct Up
1/2" = 1'-0"

6/30/2026 4:55:06 PM

PRAXIS3

100 Peachtree St NW
Suite 1450
Atlanta, GA 30303

404-875-4500 tel
www.praxis3.com

Copyright (c) 2024 Praxis3, LLC

All reports, plans, specifications, computer files, field data, notes and other documents and instruments prepared by Praxis3 shall retain all common law, statutory and other reserved rights, including copyright thereto.

This drawing may not be reproduced in whole or in part without written permission of Praxis3. It is to be returned upon request. Scales as stated are valid on the original drawings.

Rev	Date	Comments
	07/02/2026	PERMIT SET

Client:

FIFTH THIRD BANK

Project Number: 26032
Project Name:

FIFTH THIRD BANK
WATSON
1,900 SF

2711 WATSON BOULEVARD
WARNER ROBBINS, GA 31093

Key Plan:

Sheet Title:

MECHANICAL DUCT SECTION VIEWS

Sheet Number:

M-402