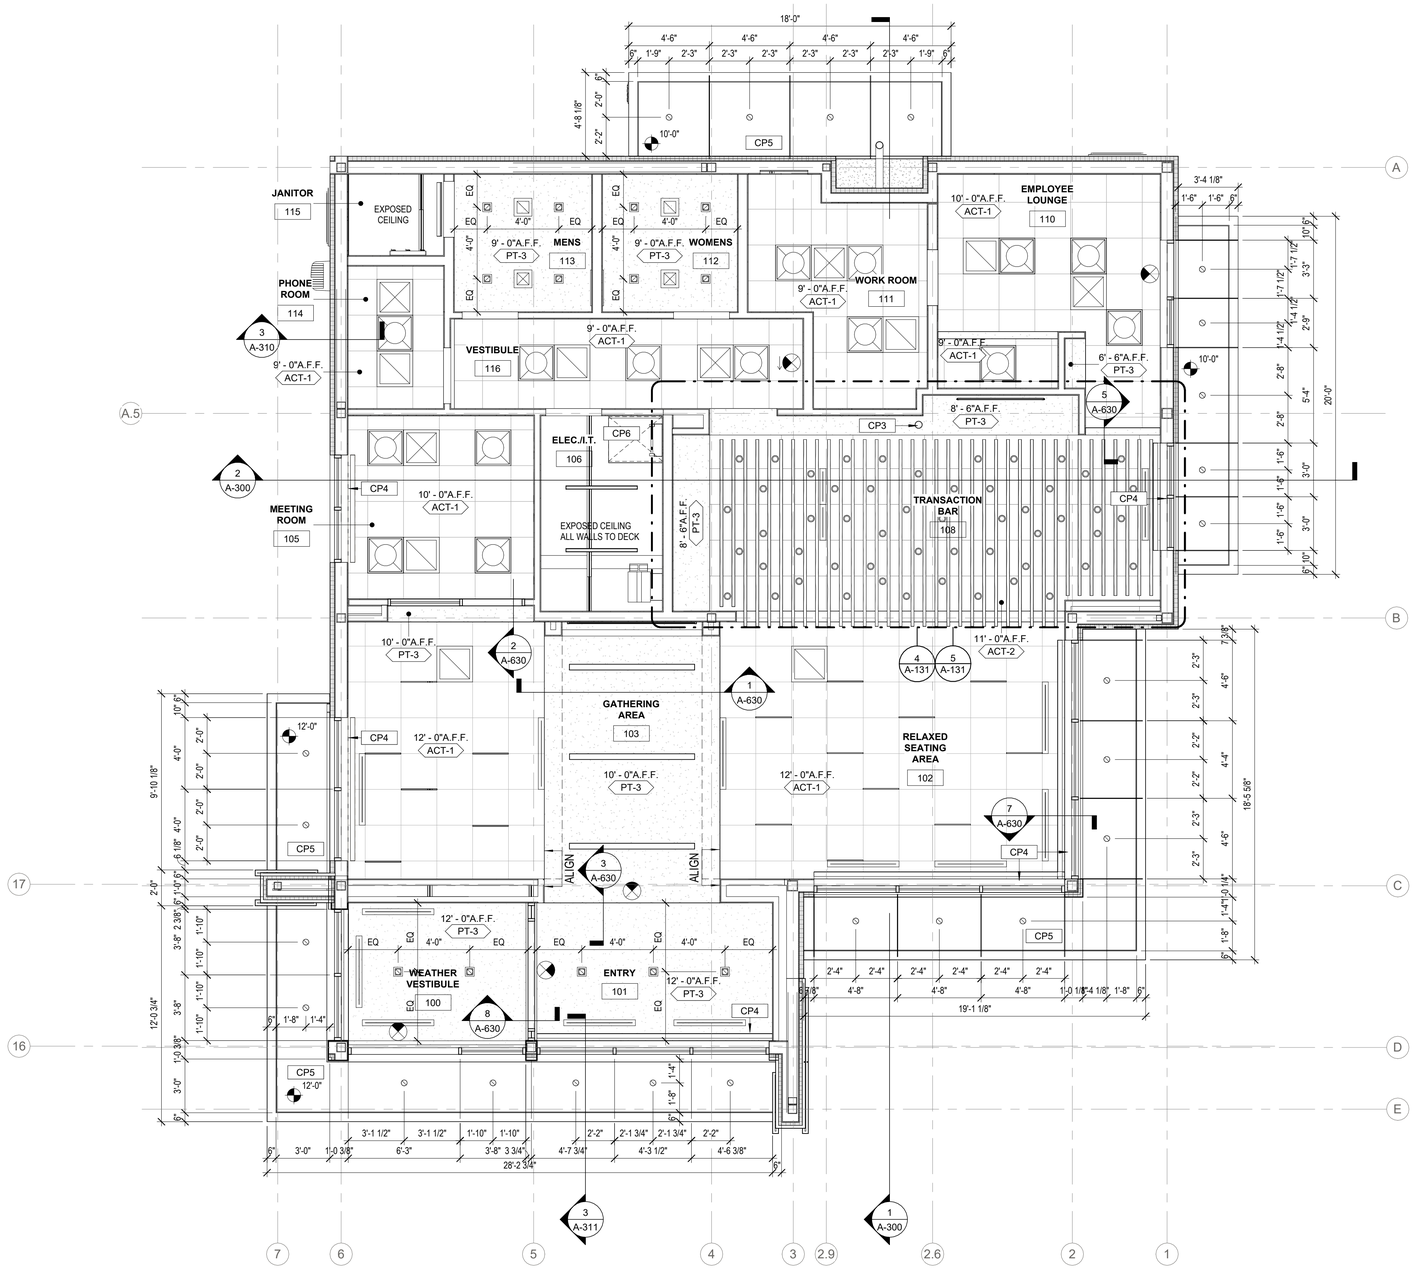


GENERAL NOTES - RCP

A. REFLECTED CEILING PLAN IS SHOWN FOR GENERAL LAYOUT PURPOSES ONLY. REFER TO MECHANICAL AND ELECTRICAL PLANS FOR ALL FIXTURES, DIFFUSERS, AND ANY OTHER REQUIREMENTS

B. REFER TO SECURITY PLAN FOR REQUIRED LIGHTING LEVELS

C. COORDINATE LENGTHS OF UNDER CABINET FIXTURES WITH SCHEDULED MILLWORK CABINETS.

D. MECHANICAL REGISTERS IN FUR DOWN ARE TO ALIGN WITH GRID

E. ALL GYPSUM BOARD CEILING PAINTED AND SUSPENDED GYPSUM BOARD ELEMENTS ARE TO BE PT-1, EXCEPT FOR THE CEILING OVER THE TRANSACTION BAR

F. CONTRACTOR TO INSTALL HVAC DUCTWORK AS HIGH AS POSSIBLE AND COORDINATE LIGHT FIXTURE LOCATIONS IN ORDER TO MAINTAIN DESIGN AT INTENDED CEILING HEIGHTS

G. GC TO PROVIDE, INSTALL AND COORDINATE PROGRAMMING OF MOTORIZED MECHOSHADES.

H. CEILING GRID MAIN TEE MUST BE PERPENDICULAR TO DIRECTION OF LINER GRID LIGHTING. G.C. TO COORDINATE.

KEY NOTES - RCP

CP1	SURFACE MOUNTED SIGN CABINET. COORDINATE SIGNAGE SIZE WITH VENDOR.
CP2	HEADACHE BAR BY BANK VENDOR
CP3	VAT TUBE - COORDINATE WITH BANK EQUIPMENT VENDOR
CP4	MOTORIZED MECHOSHADE, SEE RCP PLAN LEGEND
CP5	RECESSED CANOPY LIGHT TO BE CENTERED IN ACM, UNLESS NOTED OTHERWISE
CP6	ROOF ACCESS LADDER. REFER TO SECTION 1/A-312

LEGEND - RCP

- 2'X2' - ACOUSTIC CEILING TILE & GRID
- EXPOSED CEILING
- PAINTED GYP. CEILING
- PLASTIC LAMINATED PANEL, PL-1
- EXTERIOR GYP. CEILING
- BAR-1 BEAM BAFFLE SYSTEM
- AIR RETURN VENTS
- AIR SUPPLY VENTS
- 30" X 24" ACCESS PANEL PAINT TO MATCH CEILING
- LINEAR AIR DIFFUSER
- MOTORIZED MECHOSHADE
- EF — EXHAUST FAN
- PENDANT LIGHT
- LINEAR LIGHT
- INTEGRAL LINEAR CEILING GRID FIXTURE
- TROFFER LIGHT
- 4" RECESSED CAN DOWNLIGHT
- 6" SQUARE RECESSED CAN LIGHT
- EXIT SIGN
- SUSPENDED LINEAR STRIP LIGHT
- EXTERIOR WALL MOUNTED FIXTURE

NOTE: PROJECT NORTH IS FOR CONSTRUCTION PURPOSES ONLY. REFER TO CIVIL DRAWING FOR TRUE NORTH AND CORRECT BUILDING ORIENTATION AS IT RELATES TO THE SITE.

REFLECTED CEILING PLAN | 1/4" = 1'-0" | 1

PRAXIS3
100 Peachtree St NW
Suite 1450
Atlanta, GA 30303
404-875-4500 tel
www.praxis3.com

STATE OF GEORGIA
STUART M. ROMM
07/02/26
CERTIFICATE NO. 3457
REGISTERED ARCHITECT

Copyright (c) 2026 Praxis3, LLC

All reports, plans, specifications, computer files, field data, notes and other documents and instruments prepared by Praxis3 shall retain all common law, statutory and other reserved rights, including copyright thereto.

This drawing may not be reproduced in whole or in part without written permission of Praxis3. It is to be returned upon request. Scales as stated are valid on the original drawings.

Rev	Date	Comments
	07/02/2026	PERMIT SET

Client:
FIFTH THIRD BANK

Project Number: 26302
Project Name:
WATSON BLVD.

2711 WATSON BOULEVARD
WARNER ROBINS, GA 31093

Key Plan:

Sheet Title:
REFLECTED CEILING PLAN

Sheet Number:
A-130

7/8/2026 2:37:46 PM