

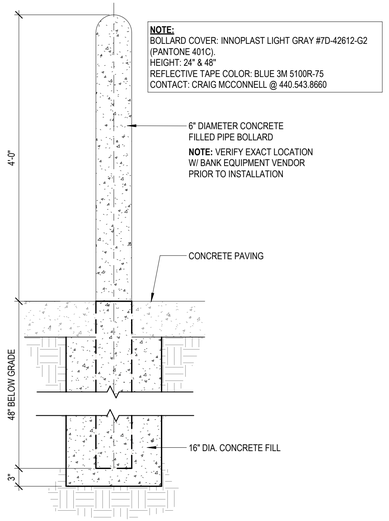



TYPICAL BOLLARD | 1" = 1'-0" | 8

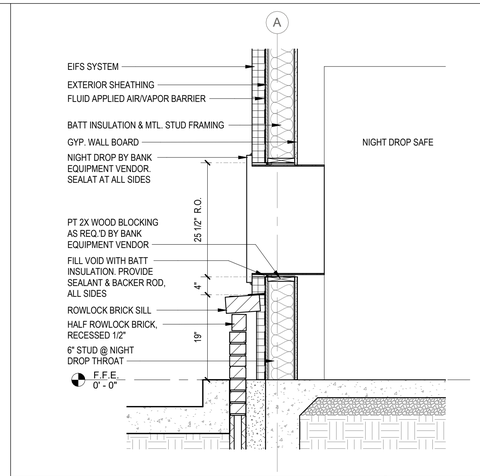


SECTION AT NIGHT DROP | 3/4" = 1'-0" | 7

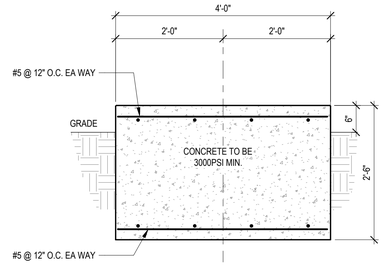


DRIVE-THRU FOUNDATION | 3/4" = 1'-0" | 6

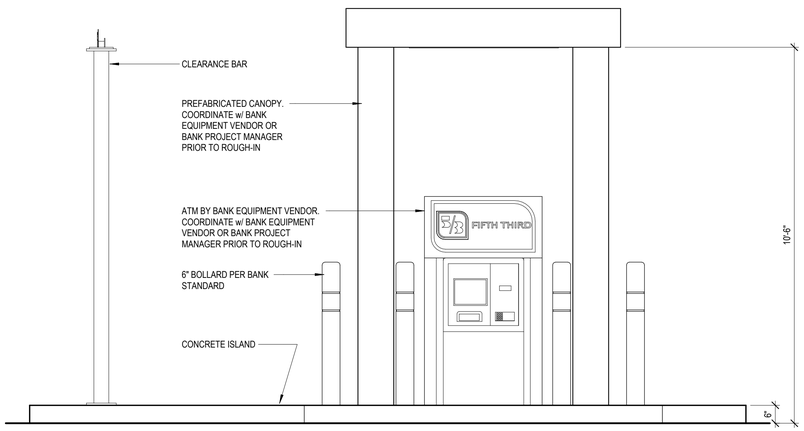


ATM FRONT ELEVATION | 1/2" = 1'-0" | 5

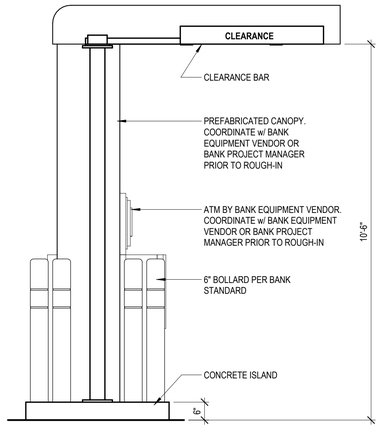

ATM SIDE ELEVATION | 1/2" = 1'-0" | 4

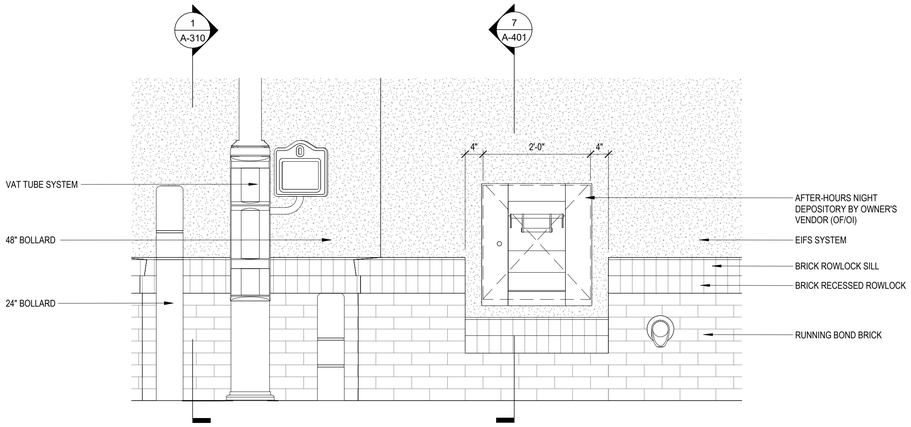

NIGHT DEPOSIT EXTERIOR ELEVATION | 3/4" = 1'-0" | 3

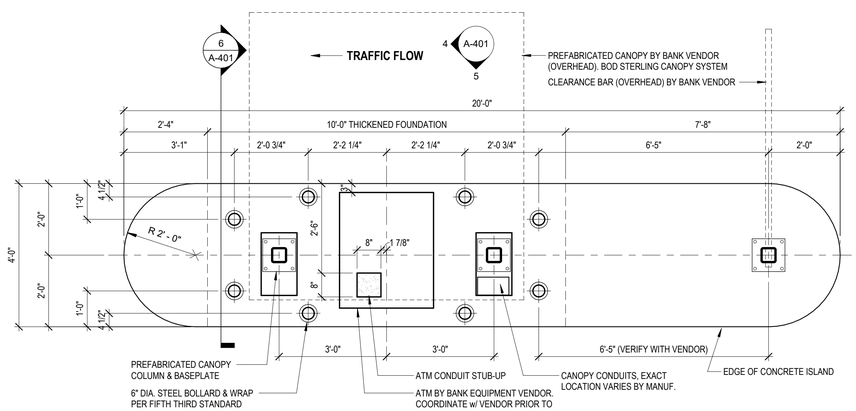


ATM CONDUIT STUB-UP REQUIREMENTS : COORDINATE FINAL LOCATION WITH MANUFACTURER AND ELECTRICAL REQUIREMENTS PRIOR TO ROUGH-IN
- PROVIDE ONE (1) 3/4" CONDUIT FOR POWER.
- ONE (1) 2" CONDUIT w/ TWO (2) PULL STRINGS FOR DATA & SECURITY CABLING.
- STUB-UP CONDUIT AT BOTTOM OF HAND HOLE WITH 120V/30 AMP FOR ATM & 120V/20 AMP FOR TOPPER.
- COIL FLEX CONDUITS IN HAND HOLE FOR FEED THRU HOLES IN BOTTOM OF ATM.
- 6" DEEP WELL OPEN TO GRAVEL FOR STUB UPS.

CANOPY STUB-UP REQUIREMENTS:
- COORDINATE PROJECT-SPECIFIC CANOPY MANUFACTURER STUB-UP LOCATION WITH CBRE PRIOR TO ROUGH-IN
- PROVIDE 3/4" CONDUIT FOR POWER,
- 3/4" CONDUIT w/ ONE (1) PULL STRING FOR SECURITY CABLING

BOLLARD PLACEMENT DRAWN FOR REFERENCE. GC TO COORDINATE W/ ATM GROUP & OWNER'S VENDOR FOR ATM & VAT BOLLARD LOCATION

ENLARGED DRIVE-THRU ISLAND | 1/2" = 1'-0" | 2

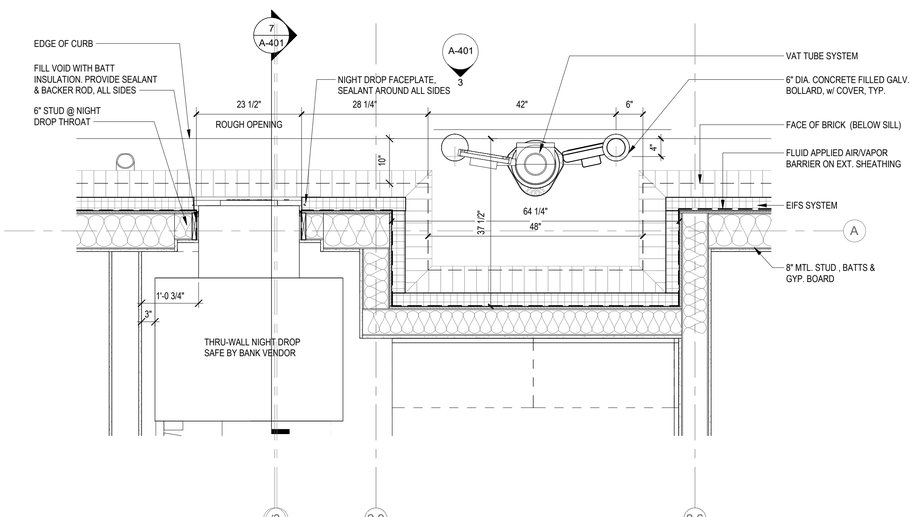

ENLARGED PLAN @ VAT NICHE | 3/4" = 1'-0" | 1

PRAXIS3
100 Peachtree St NW
Suite 1450
Atlanta, GA 30303
404-875-4500 tel
www.praxis3.com

STATE OF GEORGIA
STUART M. ROMM
07/02/26
CERTIFICATE NO. 3457
REGISTERED ARCHITECT

Copyright (c) 2026 Praxis3, LLC

All reports, plans, specifications, computer files, field data, notes and other documents and instruments prepared by Praxis3 shall retain all common law, statutory and other reserved rights, including copyright thereto.

This drawing may not be reproduced in whole or in part without written permission of Praxis3. It is to be returned upon request. Scales as stated are valid on the original drawings.

Rev	Date	Comments
	07/02/2026	PERMIT SET

Client:
FIFTH THIRD BANK

Project Number: 26302
Project Name:
WATSON BLVD.

2711 WATSON BOULEVARD
WARNER ROBINS, GA 31093

Key Plan:

Sheet Title:
BANK EQUIPMENT PLANS & DETAILS

Sheet Number:
A-401

7/8/2026 2:38:33 PM