
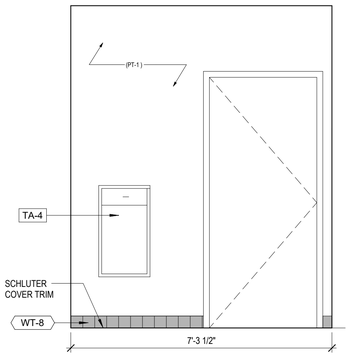



SEE 1/A-410 FOR TYPICAL MOUNTING HEIGHTS FOR TOILET ACCESSORIES

RESTROOM ELEVATION - A | 1/2" = 1'-0" | 10

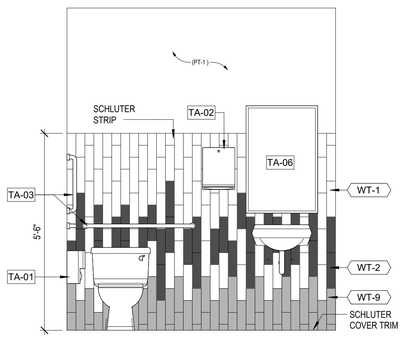


SEE 1/A-410 FOR TYPICAL MOUNTING HEIGHTS FOR TOILET ACCESSORIES

RESTROOM ELEVATION - B | 1/2" = 1'-0" | 9

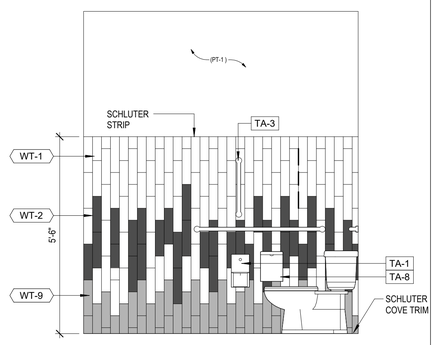

SEE 1/A-410 FOR TYPICAL MOUNTING HEIGHTS FOR TOILET ACCESSORIES

RESTROOM ELEVATION - C | 1/2" = 1'-0" | 8

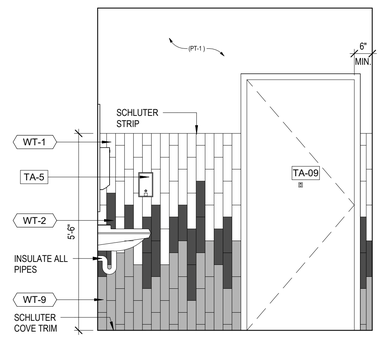

SEE 1/A-410 FOR TYPICAL MOUNTING HEIGHTS FOR TOILET ACCESSORIES


RESTROOM ELEVATION - D | 1/2" = 1'-0" | 7

TOILET ACCESSORY SCHEDULE


ITEM NO	DESCRIPTION	MODEL
TA-01	TOILET TISSUE DISPENSER	OWNER VENDOR PROVIDED, GC TO INSTALL, GC TO ORDER
TA-02	PAPER TOWEL DISPENSER	OWNER VENDOR PROVIDED, GC TO INSTALL, GC TO ORDER
TA-03	GRAB BARS	BRADLEY 1-1/4" STAINLESS STEEL GRAB BAR W/ CONCEALED MOUNTING
TA-04	WASTE RECEPTACLE	BOBRICK B-3644 RECESSED WASTE RECEPTACLE (FOR 4" WALLS)
TA-05	SOAP DISPENSER	OWNER VENDOR PROVIDED, GC TO INSTALL, GC TO ORDER
TA-06	MIRROR	BOBRICK B-290 GLASS MIRROR WITH STAINLESS STEEL ANGLE FRAME
TA-08	SANITARY NAPKIN DISPOSAL	BOBRICK B-270 SURFACE MOUNTED SANITARY NAPKIN DISPOSAL
TA-09	COAT HOOK	REFERENCE DOOR HW SCHEDULE
TA-10	SURFACE MOUNTED MOP HOLDER	BOBRICK B-223 x 24, SATIN FINISH

GC: SCAN QR CODE FOR LINK TO ORDER TOILET ACCESSORIES
"BY OWNER VENDOR, GC INSTALL"
https://app.smartsheet.com/b/form/d7330a3854794f519c389721265979be


NOTE:
MENS INTERIOR ELEVATIONS ARE SIMILAR TO WOMENS INTERIOR ELEVATIONS

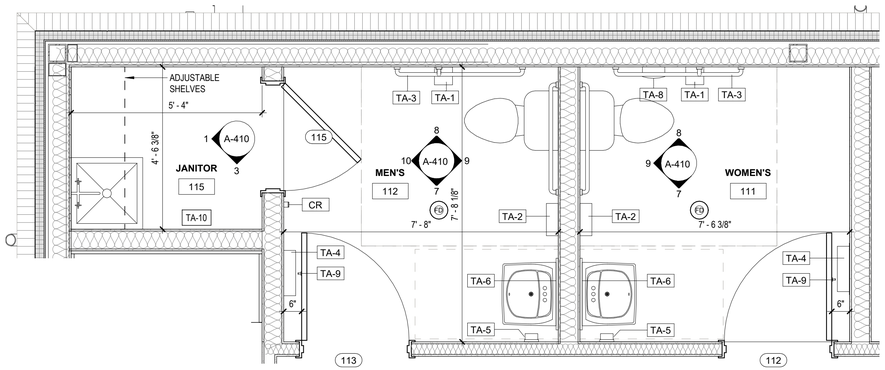


ENLARGED RESTROOM PLAN | 1/2" = 1'-0" | 6

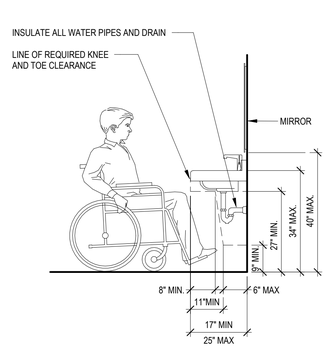


ACCESSIBLE - LAV | 1/2" = 1'-0" | 5

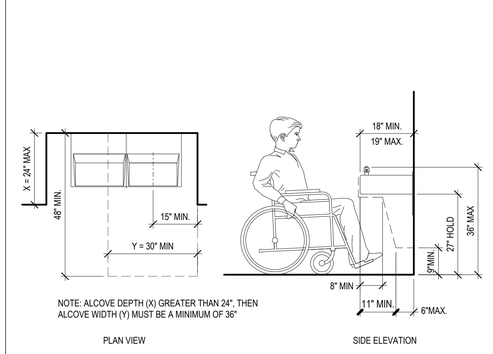


ACCESSIBLE - DRINKING FOUNTAINS | 1/2" = 1'-0" | 4

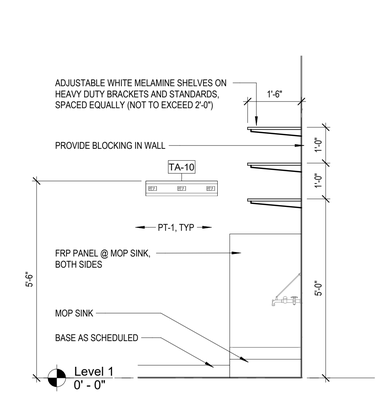


JANITOR CLOSET ELEVATION | 1/2" = 1'-0" | 3

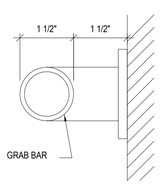


PROVIDE FASTENERS AND WALL REINFORCEMENT TO SUPPORT A 250# MIN. POINT LOAD.

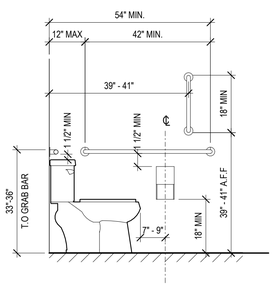


ACCESSIBLE WATER CLOSET

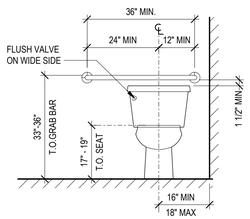


ACCESSIBLE WATER CLOSET

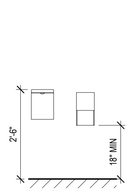


SANITARY NAPKIN RECEPTACLE
TOILET PAPER DISPENSER

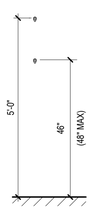


COAT HOOK

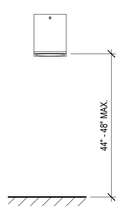


PAPER TOWEL DISPENSER

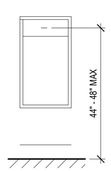

PAPER TOWEL DISPENSER & WASTE RECEPTACLE

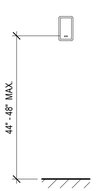


SOAP DISPENSER

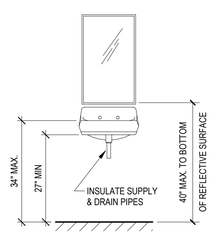

WALL-MOUNTED LAVATORY

TYPICAL ACCESSIBLE ACCESSORY HEIGHTS | 1/2" = 1'-0" | 2

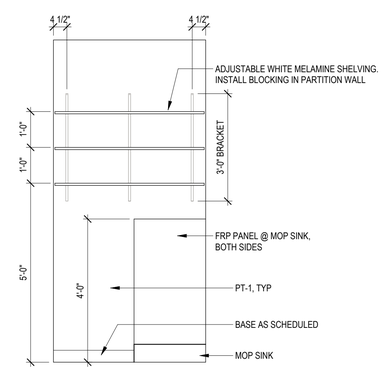

JANITOR CLOSET ELEVATION | 1/2" = 1'-0" | 1

PRAXIS3

100 Peachtree St NW
Suite 1450
Atlanta, GA 30303
404-875-4500 tel
www.praxis3.com

STATE OF GEORGIA
STUART M. ROMM
07/02/26
CERTIFICATE NO. 34511
REGISTERED ARCHITECT

Copyright (c) 2026 Praxis3, LLC

All reports, plans, specifications, computer files, field data, notes and other documents and instruments prepared by Praxis3 shall retain all common law, statutory and other reserved rights, including copyright thereto.

This drawing may not be reproduced in whole or in part without written permission of Praxis3. It is to be returned upon request. Scales as stated are valid on the original drawings.

Rev	Date	Comments
	07/02/2026	PERMIT SET

Client:
FIFTH THIRD BANK

Project Number: 26302
Project Name:
WATSON BLVD.

2711 WATSON BOULEVARD
WARNER ROBINS, GA 31093

Key Plan:

Sheet Title:
ENLARGED RESTROOM PLANS & ELEVATIONS

Sheet Number:
A-410

7/8/2026 2:38:37 PM