

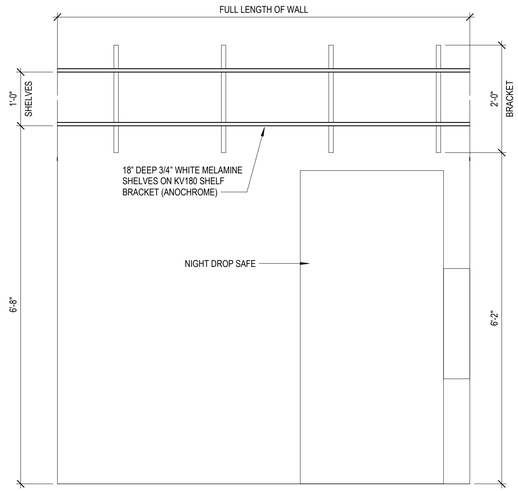



SHELF AT NIGHT DROP ELEVATION | 3/4" = 1'-0" | 12

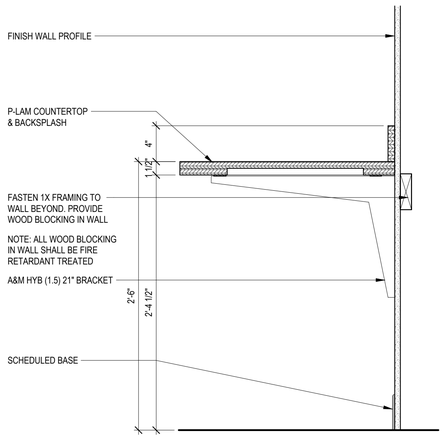


PHONE ROOM COUNTERTOP | 1 1/2" = 1'-0" | 11

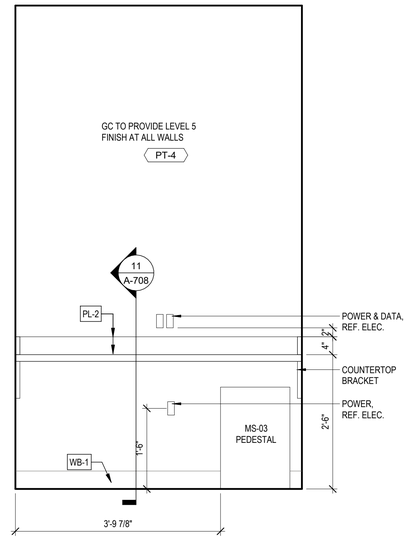


PHONE ROOM ELEVATION | 3/4" = 1'-0" | 10

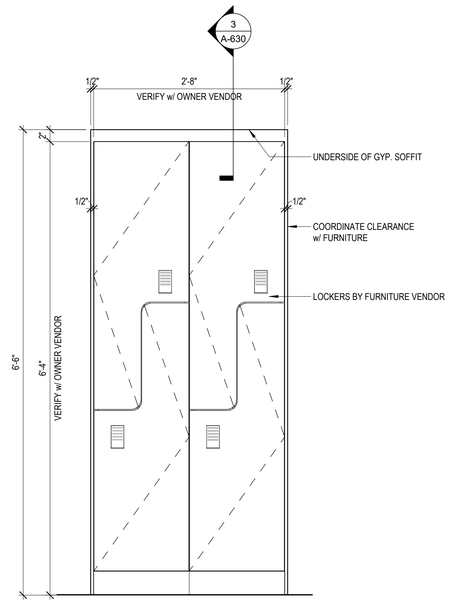


LOCKER ELEVATION | 1" = 1'-0" | 9

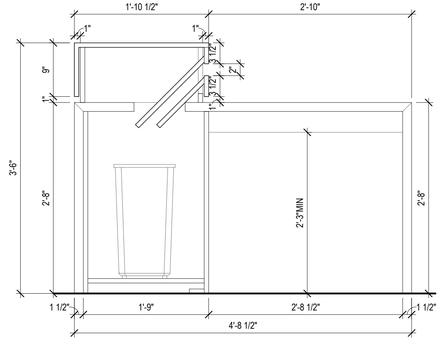


CHECK DESK - SECTION | 1" = 1'-0" | 8

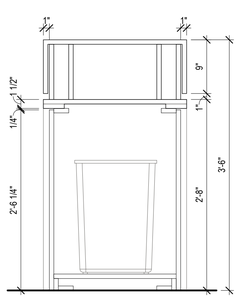


CHECK DESK - SECTION | 1" = 1'-0" | 7

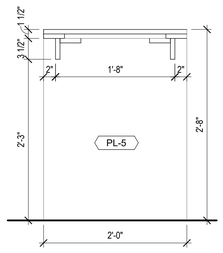


CHECK DESK - SECTION | 1" = 1'-0" | 6

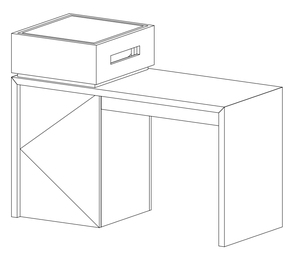


CHECK DESK | NTS | 5

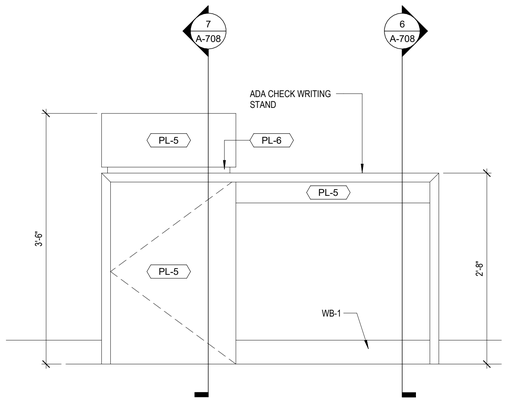


CHECK DESK - ELEVATION | 1" = 1'-0" | 4

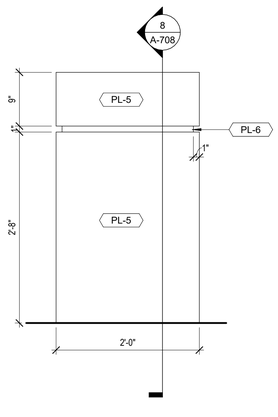

CHECK DESK - ELEVATION | 1" = 1'-0" | 3

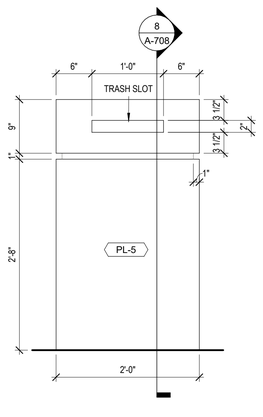

CHECK DESK - ELEVATION | 1" = 1'-0" | 2

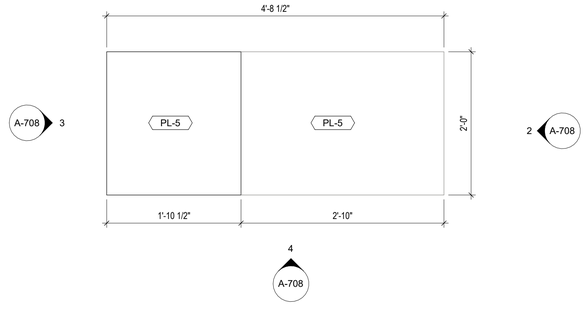

CHECK DESK - ENLARGED PLAN | 1" = 1'-0" | 1

PRAXIS3
100 Peachtree St NW
Suite 1450
Atlanta, GA 30303
404-875-4500 tel
www.praxis3.com

STATE OF GEORGIA
STUART M. ROMM
07/02/26
CERTIFICATE NO. 34511
REGISTERED ARCHITECT

Copyright (c) 2026 Praxis3, LLC

All reports, plans, specifications, computer files, field data, notes and other documents and instruments prepared by Praxis3 shall retain all common law, statutory and other reserved rights, including copyright thereto.

This drawing may not be reproduced in whole or in part without written permission of Praxis3. It is to be returned upon request. Scales as stated are valid on the original drawings.

Rev	Date	Comments
	07/02/2026	PERMIT SET

Client:
FIFTH THIRD BANK

Project Number: 26302
Project Name:
WATSON BLVD.

2711 WATSON BOULEVARD
WARNER ROBINS, GA 31093

Key Plan:

Sheet Title:
CHECK DESK - ENLARGED PLAN & DETAILS

Sheet Number:
A-708

7/8/2026 2:39:10 PM