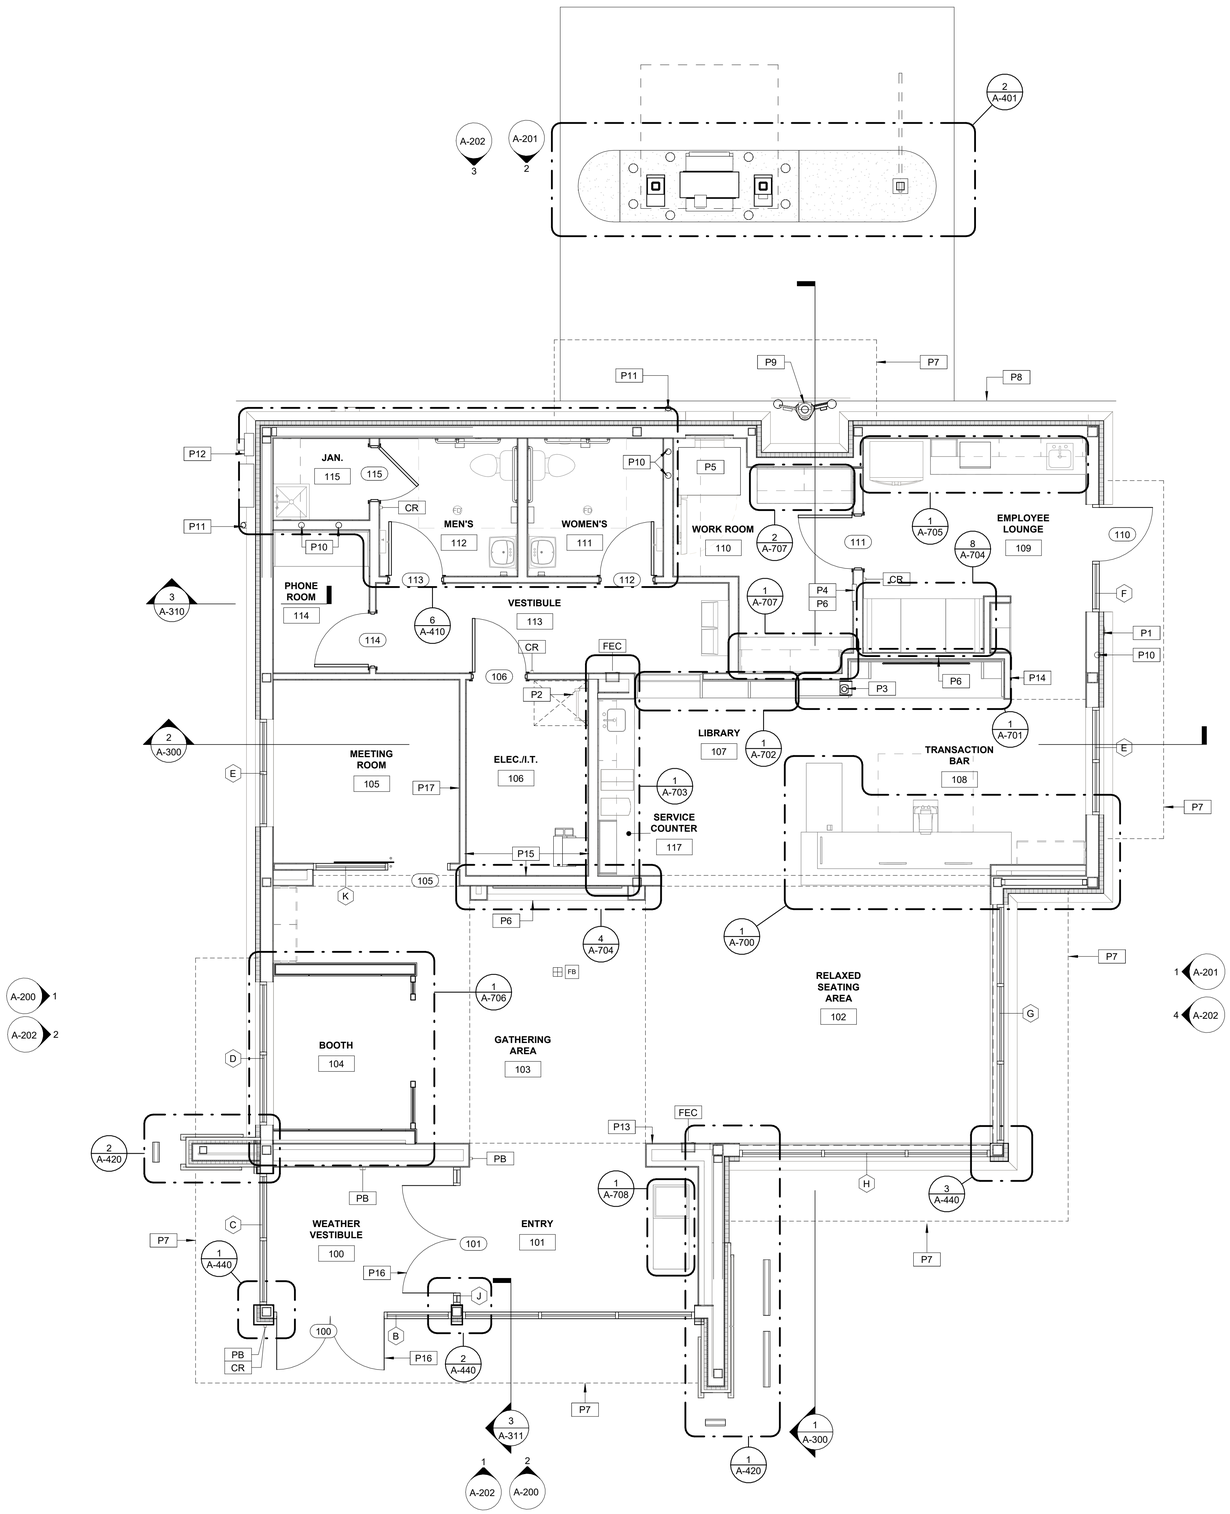


NOTE: PROJECT NORTH IS FOR CONSTRUCTION PURPOSES ONLY. REFER TO CIVIL DRAWING FOR TRUE NORTH AND CORRECT BUILDING ORIENTATION AS IT RELATES TO THE SITE.

A110 FLOOR PLAN | 1/4" = 1'-0" | 1

GENERAL NOTES - FLOOR PLAN

A. ALL PARTITIONS ARE DIMENSIONED FROM FACE OF STUD TO FACE OF STUD, UNLESS OTHERWISE NOTED. ALL DIMENSIONS MARKED "CLEAR" SHALL BE MAINTAINED AND SHALL ALLOW FOR THICKNESS OF ALL FINISHES INCLUDING CARPET, CERAMIC TILE, VCT, ETC.
B. EDGE OF DOOR JAMB SHALL BE MINIMUM 4" FROM INTERSECTING WALL U.N.O. OR AS REQUIRED FOR HARDWARE INSTALLATION
C. SEE SHEET A-620 FOR PARTITION TYPES
D. BANK EQUIPMENT TO BE SUPPLIED AND INSTALLED BY VENDOR
E. CONTRACTOR SHALL PROVIDE BLOCKING FOR ALL WALL-MOUNTED EQUIPMENT AND ACCESSORIES.
F. CONTRACTOR SHALL COORDINATE ALL WOOD BLOCKING, STEEL SUPPORTS, AND ANY OTHER ITEMS WHICH ARE IMBEDDED IN DRYWALL PARTITIONS OR ENCLOSURES, WHICH RELATE TO THEIR WORK OR THE WORK OF ANY SEPARATE CONTRACTORS. ALL WOOD BLOCKING, BRIDGING, BRACING, FRAMING, ETC., SHALL BE FIRE RETARDANT TREATED AS CALLED FOR BY THE GOVERNING BUILDING CODE AND THE CONTRACTOR MUST SUBMIT AFFIDAVITS OF SUCH FIRE TREATMENT TO THE OWNER.
G. ALL INTERIOR FINISHES ARE TO COMPLY WITH THE REQUIREMENTS AS SET FORTH IN THE CURRENT STANDARD EDITIONS OF ALL GOVERNING CODES, REGULATIONS, AND ORDINANCES HAVING JURISDICTION OVER THE SCOPE OF WORK.
H. CONTRACTOR WILL SECURE ALL BUILDING PERMITS & INSPECTIONS NECESSARY FOR THE CONSTRUCTION OF THE PROJECT.
I. DRAWINGS ARE NOT TO BE SCALED
J. LOCATION AND NUMBER OF FIRE EXTINGUISHERS ARE TO BE INSTALLED PER THE DIRECTION OF THE LOCAL AUTHORITIES AND NFPA 13
K. FURNITURE AND MILLWORK TO BE PROVIDED BY OWNER VENDOR. G.C. TO COORDINATE LOCATION OF BLOCKING, PLUMBING, ELECTRICAL AND ALL OTHER REQUIREMENTS
L. REFERENCE ENGINEERING PLANS FOR PLUMBING, ELECTRICAL EQUIPMENT, AND SYSTEMS. CONTRACTOR TO VERIFY AND COORDINATE PLUMBING ROUGH-IN DIMENSIONS WITH PLUMBER. (TO BE PROVIDED BY CONTRACTOR)
M. CONTRACTOR TO SET BANKING EQUIPMENT TEMPLATES. EQUIPMENT VENDOR TO VERIFY CORRECT PLACEMENT AND TO COORDINATE WITH CONTRACTOR FOR PROPER PLACEMENT
N. NO ADJUSTMENT TO THE CONTRACT AMOUNT WILL BE GIVEN FOR THE CONTRACTOR NOT FULLY ACQUAINTING THEMSELVES WITH EQUIPMENT VENDOR REQUIREMENTS.
O. PINK NOISE IS TO BE PROVIDED BY THE CONTRACTOR. COORDINATE PINK NOISE LOCATION WITH MOOD MEDIA VENDOR. REFER TO ELECTRICAL DRAWINGS.
P. REFER TO SHEET A-600 FOR DOOR AND WINDOW SCHEDULE
Q. APPLIANCES PROVIDED AND INSTALLED BY G.C. U.N.O
R. REFER TO SPECS FOR ATTIC STOCK QUANTITIES

FLOOR PLAN SYMBOLS

PARTITION AS SCHEDULED

DOOR AS SCHEDULED

FEC — FIRE EXTINGUISHER CABINET

CR — WALL-MOUNTED CARD READER AS PER DOOR HARDWARE SCHEDULE

PB — ADA DOOR OPERATOR PUSH PADDLE AS PER DOOR HARDWARE SCHEDULE

FB — FLOOR BOX RECEPTACLE WITH BLACK COVER PLATE TRIM FINISH

FD — FLOOR DRAIN

KEY NOTES - FLOOR PLAN

P1	RECESSED KNOX BOX WITH TAMPER SWITCH MOUNTED AT 48" TO THE CENTER OF BOX A.F.F., MODEL # 3200R VERIFY LOCATION WITH LOCAL MUNICIPALITY TO INSURE COMPLIANCE
P2	ROOF ACCESS LADDER. REFER TO SECTION 1/A-312
P3	SINGLE SIDED VAT TUBES BY BANK VENDOR G.C. TO PROVIDE MITERED BLACK ANGLED ALUMINUM FRAME (BOTH SIDES) AROUND VAT TERMINAL. G.C. TO COORDINATE OPENING SIZE AND LOCATION WITH BANK VENDOR
P4	DUAL CONTROL KEY BOX
P5	COMBO NIGHT DEPOSIT BOX / CASH VAULT. FURNISHED BY NATIONAL VENDOR AND INSTALLED BY NATIONAL VENDOR. PREPARATION BY G.C. G.C. TO PROVIDE INSULATION AND WOOD TRIM ON INTERIOR UPON COMPLETION OF ALL ELECTRIC & ALARM WIRING. G.C. TO PROVIDE WOOD BLOCKING BETWEEN BASE OF UNIT AND FLOOR. G.C. TO CONFIRM AND COORDINATE EQUIPMENT CUT SHEETS WITH BANK AND EQUIPMENT VENDOR PRIOR TO INSTALLATION OF WALL OPENING
P6	WALL MOUNTED MONITOR BY BANK VENDOR. COORDINATE W/ OWNER'S VENDOR AND MEP DRAWINGS
P7	LINE OF CANOPY ABOVE
P8	EDGE OF CONCRETE CURB, REF. CIVIL
P9	REMOTE TELLER TERMINAL
P10	ROOF LEADER. REFER TO PLUMBING DRAWINGS
P11	OVERFLOW DOWNSPOUT NOZZLE. REFER TO PLUMBING DRAWINGS
P12	ELECTRICAL METER. REFER TO ELECTRICAL DRAWINGS
P13	DRIVE-THRU INDICATOR LIGHT, INSTALLED AT 8'-0" AFF
P14	LOCATION OF MOOD MEDIA AND MECHOSHADE CONTROLS
P15	INSTALL FIRE RETARDANT PLYWOOD ON ALL WALLS WITHIN IT/ELEC ROOM. PLYWOOD TO BE 8' TALL AND PAINTED TO MATCH ADJACENT WALL. G.C. TO MAINTAIN VISIBILITY OF PLYWOOD LABEL
P16	ACTIVE OPERABLE DOOR LEAF
P17	<varies>

GENERAL NOTES - TERMITE PROTECTION

A. SOIL TREATMENT FOR SUBTERRANEAN TERMITE PREVENTION INSIDE THE FOUNDATION PERIMETER SHALL BE DONE AFTER ALL EXCAVATION, BACKFILLING AND COMPACTION IS COMPLETE.
B. SOIL AREA DISTURBED AFTER INITIAL CHEMICAL SOIL TREATMENT SHALL BE TREATED WITH A CHEMICAL SOIL TREATMENT, INCLUDING SPACES BOXED OR FORMED.
C. SPACE IN CONCRETE FLOORS BOXED OUT OR FORMED FOR THE SUBSEQUENT INSTALLATION OF PLUMBING TRAPS, DRAINS, OR ANY OTHER PURPOSE, SHALL BE CREATED BY USING PLASTIC OR METAL PERMANENTLY PLACED FORMS OF SUFFICIENT DEPTH TO ELIMINATE ANY PLANNED SOIL DISTURBANCE AFTER INITIAL CHEMICAL SOIL TREATMENT.
D. CHEMICALLY TREATED SOIL SHALL BE PROTECTED WITH A MINIMUM 10 MIL VAPOR RETARDER TO PROTECT AGAINST RAINFALL DILUTION. IF RAINFALL OCCURS BEFORE VAPOR RETARDER PLACEMENT, RE-TREATMENT IS REQUIRED. ANY WORK, INCLUDING PLACEMENT OF REINFORCING STEEL, DONE AFTER CHEMICAL TREATMENT UNTIL THE CONCRETE FLOOR IS POURED, SHALL BE DONE IN SUCH A MANNER AS TO AVOID PENETRATING OR DISTURBING TREATED SOIL.
E. CONCRETE OVER-POUR OR MORTAR ACCUMULATED ALONG THE EXTERIOR FOUNDATION PERIMETER SHALL BE REMOVED PRIOR TO EXTERIOR CHEMICAL SOIL TREATMENT, TO ENHANCE VERTICAL PENETRATION OF THE CHEMICALS.
F. CHEMICAL SOIL TREATMENTS SHALL ALSO BE APPLIED UNDER ALL EXTERIOR CONCRETE OF GRADE WITHIN ONE (1) FOOT OF PRIMARY STRUCTURE SIDEWALLS. ALSO A VERTICAL CHEMICAL BARRIER SHALL BE APPLIED PROMPTLY AFTER CONSTRUCTION IS COMPLETED, INCLUDING INITIAL LANDSCAPING AND IRRIGATION/SPRINKLER INSTALLATION. ANY SOIL DISTURBED AFTER THE CHEMICAL VERTICAL BARRIER IS APPLIED SHALL BE PROMPTLY RE-TREATED.
G. THE RULES AND LAWS AS ESTABLISHED BY THE STATE DEPARTMENT OF AGRICULTURE AND CONSUMER SERVICES SHALL BE DEEMED AS APPROVED WITH RESPECT TO PRE-CONSTRUCTION SOIL TREATMENT FOR PROTECTION AGAINST SUBTERRANEAN TERMITES.
H. A 'CERTIFICATE OF COMPLIANCE' SHALL BE ISSUED TO THE BUILDING DEPARTMENT BY THE LICENSED PEST CONTROL COMPANY THAT CONTAINS THE FOLLOWING STATEMENT: 'THE BUILDING HAS RECEIVED A COMPLETE TREATMENT FOR THE PREVENTION OF SUBTERRANEAN TERMITES. TREATMENT IS IN ACCORDANCE WITH RULES AND LAWS ESTABLISHED BY THE STATE DEPARTMENT OF AGRICULTURE AND CONSUMER SERVICES'.

PRAXIS3

100 Peachtree St NW
Suite 1450
Atlanta, GA 30303
404-875-4500 tel
www.praxis3.com

STATE OF GEORGIA
STUART M. ROMM
07/02/26
CERTIFICATE NO. 3457
REGISTERED ARCHITECT

Copyright (c) 2026 Praxis3, LLC

All reports, plans, specifications, computer files, field data, notes and other documents and instruments prepared by Praxis3 shall retain all common law, statutory and other reserved rights, including copyright thereto.

This drawing may not be reproduced in whole or in part without written permission of Praxis3. It is to be returned upon request. Scales as stated are valid on the original drawings.

Rev	Date	Comments
	07/02/2026	PERMIT SET

Client:
FIFTH THIRD BANK

Project Number: 26302
Project Name:
WATSON BLVD.


2711 WATSON BOULEVARD
WARNER ROBINS, GA 31093

Key Plan:

Sheet Title:
FLOOR PLAN

Sheet Number:
A-110

7/8/2026 2:37:42 PM

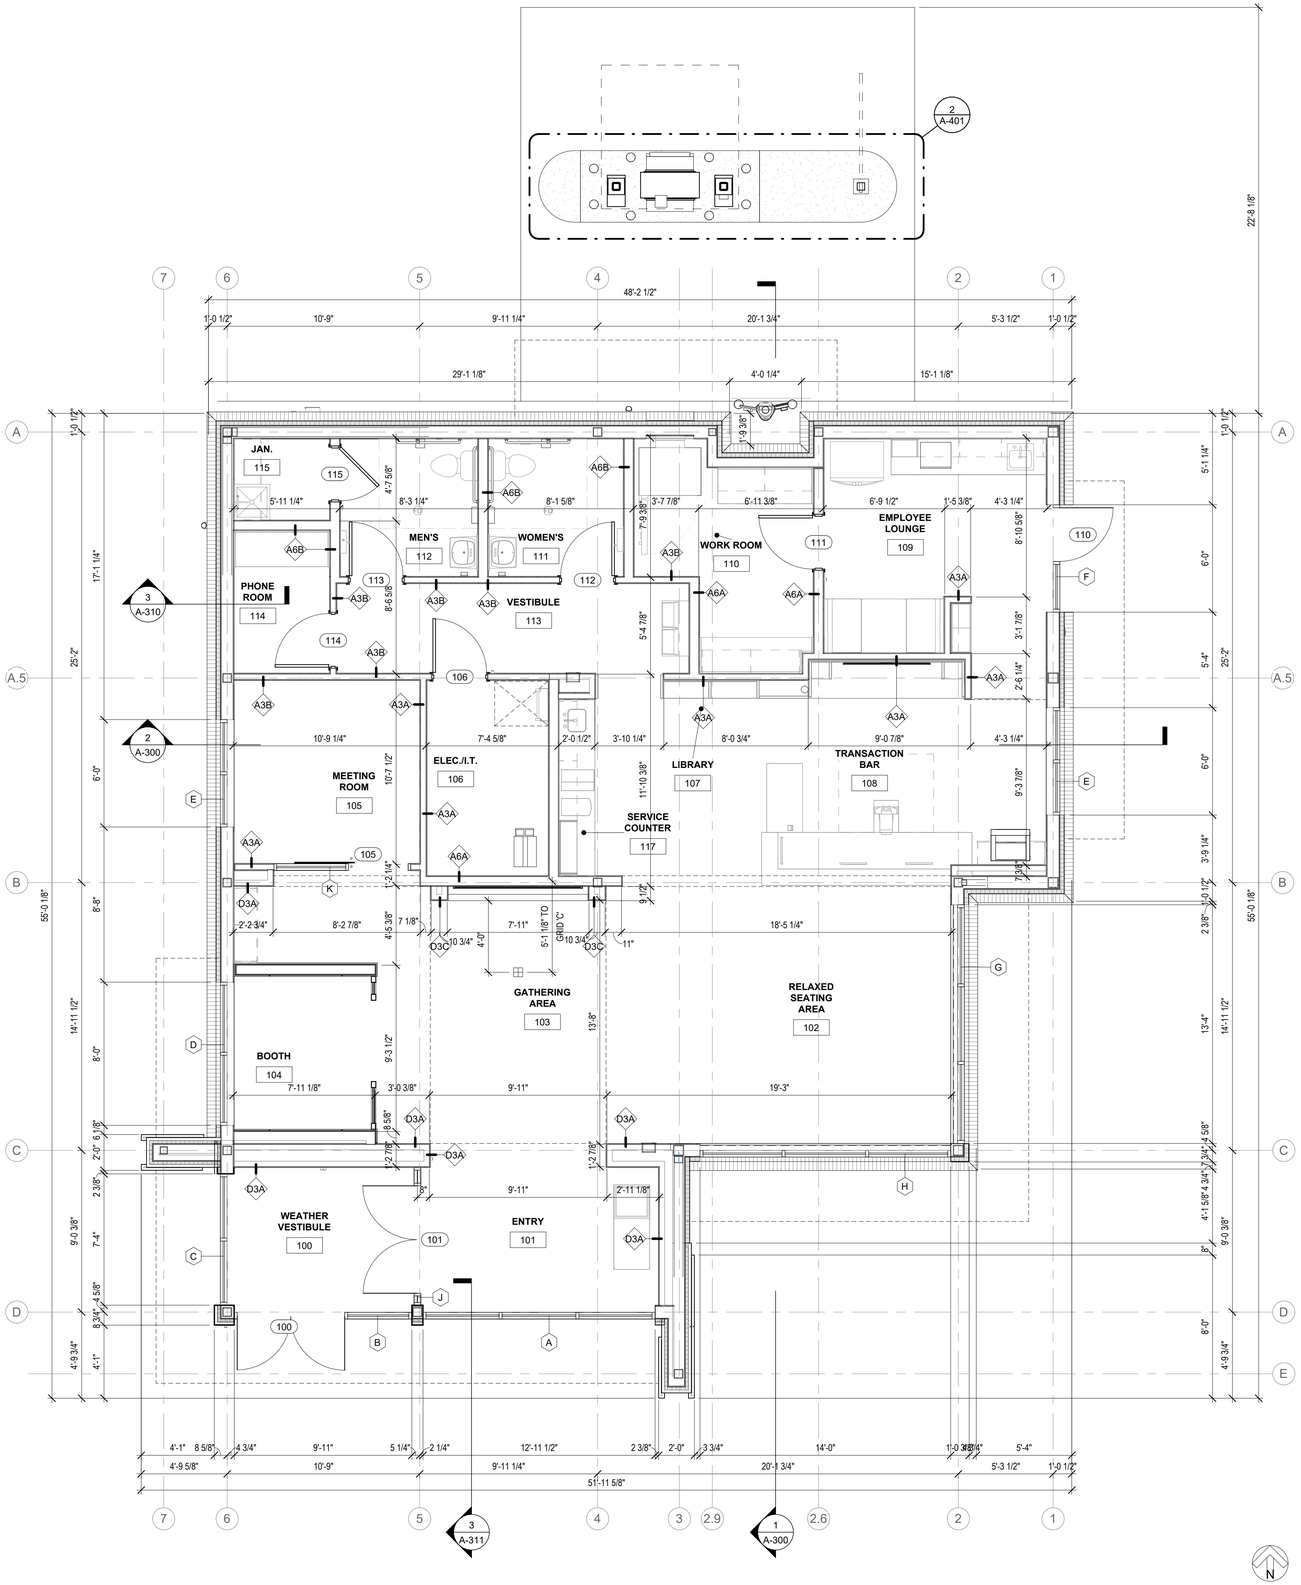

NOTE: PROJECT NORTH IS FOR CONSTRUCTION PURPOSES ONLY. REFER TO CIVIL DRAWING FOR TRUE NORTH AND CORRECT BUILDING ORIENTATION AS IT RELATES TO THE SITE.

DIMENSIONAL FLOOR PLAN | 1/4" = 1'-0" | 1

GENERAL NOTES - FLOOR PLAN

A. ALL PARTITIONS ARE DIMENSIONED FROM FACE OF STUD TO FACE OF STUD, UNLESS OTHERWISE NOTED. ALL DIMENSIONS MARKED "CLEAR" SHALL BE MAINTAINED AND SHALL ALLOW FOR THICKNESS OF ALL FINISHES INCLUDING CARPET, CERAMIC TILE, VCT, ETC.
B. EDGE OF DOOR JAMB SHALL BE MINIMUM 4" FROM INTERSECTING WALL U.N.O. OR AS REQUIRED FOR HARDWARE INSTALLATION
C. SEE SHEET A-620 FOR PARTITION TYPES
D. BANK EQUIPMENT TO BE SUPPLIED AND INSTALLED BY VENDOR
E. CONTRACTOR SHALL PROVIDE BLOCKING FOR ALL WALL-MOUNTED EQUIPMENT AND ACCESSORIES.
F. CONTRACTOR SHALL COORDINATE ALL WOOD BLOCKING, STEEL SUPPORTS, AND ANY OTHER ITEMS WHICH ARE IMBEDDED IN DRYWALL PARTITIONS OR ENCLOSURES, WHICH RELATE TO THEIR WORK OR THE WORK OF ANY SEPARATE CONTRACTORS. ALL WOOD BLOCKING, BRIDGING, BRACING, FRAMING, ETC., SHALL BE FIRE RETARDANT TREATED AS CALLED FOR BY THE GOVERNING BUILDING CODE AND THE CONTRACTOR MUST SUBMIT AFFIDAVITS OF SUCH FIRE TREATMENT TO THE OWNER
G. ALL INTERIOR FINISHES ARE TO COMPLY WITH THE REQUIREMENTS AS SET FORTH IN THE CURRENT STANDARD EDITIONS OF ALL GOVERNING CODES, REGULATIONS, AND ORDINANCES HAVING JURISDICTION OVER THE SCOPE OF WORK.
H. CONTRACTOR WILL SECURE ALL BUILDING PERMITS & INSPECTIONS NECESSARY FOR THE CONSTRUCTION OF THE PROJECT
I. DRAWINGS ARE NOT TO BE SCALED
J. LOCATION AND NUMBER OF FIRE EXTINGUISHERS ARE TO BE INSTALLED PER THE DIRECTION OF THE LOCAL AUTHORITIES AND NFPA 13
K. FURNITURE AND MILLWORK TO BE PROVIDED BY OWNER VENDOR. G.C. TO COORDINATE LOCATION OF BLOCKING, PLUMBING, ELECTRICAL AND ALL OTHER REQUIREMENTS
L. REFERENCE ENGINEERING PLANS FOR PLUMBING, ELECTRICAL EQUIPMENT, AND SYSTEMS. CONTRACTOR TO VERIFY AND COORDINATE PLUMBING ROUGH-IN DIMENSIONS WITH PLUMBER. (TO BE PROVIDED BY CONTRACTOR)
M. CONTRACTOR TO SET BANKING EQUIPMENT TEMPLATES. EQUIPMENT VENDOR TO VERIFY CORRECT PLACEMENT AND TO COORDINATE WITH CONTRACTOR FOR PROPER PLACEMENT
N. NO ADJUSTMENT TO THE CONTRACT AMOUNT WILL BE GIVEN FOR THE CONTRACTOR NOT FULLY ACQUAINTING THEMSELVES WITH EQUIPMENT VENDOR REQUIREMENTS.
O. PINK NOISE IS TO BE PROVIDED BY THE CONTRACTOR. COORDINATE PINK NOISE LOCATION WITH MOOD MEDIA VENDOR. REFER TO ELECTRICAL DRAWINGS.
P. REFER TO SHEET A-600 FOR DOOR AND WINDOW SCHEDULE
Q. APPLIANCES PROVIDED AND INSTALLED BY G.C. U.N.O
R. REFER TO SPECS FOR ATTIC STOCK QUANTITIES

GENERAL NOTES - ACCESSIBILITY

1. ALL CONTROLS FOR USE BY CUSTOMERS MUST BE MOUNTED BETWEEN 15" AND 48" ABOVE FINISHED FLOOR AND MUST HAVE 30" X 48" MINIMUM CLEAR FLOOR SPACE FOR A FORWARD OR PARALLEL APPROACH. CONTROLS MOUNTED OVER AN OBSTRUCTION THAT IS BETWEEN 10" AND 24" DEEP MAY BE NO HIGHER THAN 46" AFF. IF A PARALLEL APPROACH IS PROVIDED; OR WHERE OBSTRUCTIONS ARE BETWEEN 20" AND 25' DEEP WITH A FORWARD APPROACH. CONTROLS MUST NOT REQUIRE TIGHT GRASPING OR TWISTING OF THE WRIST.

2. COMMON EMPLOYEE AREAS SUCH AS BREAK ROOMS, LOCKERS, AND TOILET ROOMS MUST BE ACCESSIBLE AND HAVE ACCESSIBLE FEATURES AND FIXTURES. EMPLOYEE WORK AREAS LESS THAN 1,000 SF AS DEFINED BY PERMANENTLY INSTALLED PARTITIONS, COUNTERS, CASEWORK OR FURNISHINGS ARE NOT REQUIRED TO HAVE AN ACCESSIBLE PATH OF CIRCULATION THROUGHOUT THE SPACE BUT ARE REQUIRED TO BE CONSTRUCTED SO AN INDIVIDUAL CAN APPROACH, ENTER AND EXIT THE SPACE.

3. IN COMMON SPACES WITHIN EMPLOYEE AREAS, AT LEAST ONE OF EACH TYPE OF STORAGE WORK COUNTER, 5% OF LOCKERS AND CONTROLS (EMERGENCY PHONES, CARD READERS ETC.) MUST BE ON AN ACCESSIBLE ROUTE, WITHIN REACH RANGE AND MUST COMPLY WITH STANDARDS FOR CONTROLS AS DEFINED IN THE GOVERNING ACCESSIBILITY STANDARDS OR LOCAL CODES, WHICHEVER IS STRICTER.

4. FIRE ALARM SYSTEM SHALL HAVE PERMANENTLY INSTALLED AUDIBLE AND VISIBLE ALARMS COMPLYING WITH NFPA 72 (1999 OR 2010 EDITION) AND AS REQUIRED BY LOCAL AUTHORITIES. ALARMS MUST BE LOCATED IN PUBLIC AND COMMON USE AREAS. WHERE EMPLOYEES HAVE AUDIBLE ALARMS, THE WIRING SHALL BE DESIGNED SO VISIBLE ALARMS CAN BE INTEGRATED INTO THE SYSTEM, UNLESS GREATER STANDARDS ARE REQUIRED BY LOCAL AUTHORITIES.

5. OPERABLE PORTION OF CARD READER TO BE MOUNTED AT 48" OR BELOW WITH CLEAR FLOOR SPACE FOR FRONT OR PARALLEL APPROACH.

6. ALL SIGNS IDENTIFYING PERMANENT ROOMS OR SPACES ARE REQUIRED TO HAVE VISUAL AND RAISED CHARACTERS AND BRAILLE. SIGNAGE TO BE MOUNTED ON LATCH SIDE OF DOOR WITH THE BOTTOM OF THE BRAILLE NO LOWER THAN 48" AND THE BOTTOM OF THE HIGHEST TACTILE CHARACTER NO HIGHER THAN 60" AFF.

7. IN PUBLIC AREAS PROVIDED WITH WORK SURFACES ARE COUNTERS INTENDED FOR DINING/DRINKING, AT LEAST 5% OF THE TABLES MUST BE ACCESSIBLE WITH COMPLIANT KNEE AND TOE CLEARANCE IN AN ACCESSIBLE ROUTE AND DISTRIBUTED THROUGHOUT THE SPACE. ALL EQUIPMENT, FURNITURE AND MILLWORK INTENDED FOR CUSTOMER USE MUST MEET ALL CLEARANCES AND 2. 6.

8. REACH RANGES AS DEFINED BY GOVERNING ACCESSIBILITY CODE OR LOCAL CODE; WHICHEVER IS STRICTER.

9. PROVIDE ACCESSIBLE FLOOR TRANSITIONS AT ALL LOCATIONS WHERE THERE IS A CHANGE IN FLOORING MATERIAL OR AT DOOR THRESHOLDS. THE CHANGE OF LEVEL BETWEEN MATERIALS MUST BE NO MORE THAN ¾" OR UP TO ½" IF SLOPED NO MORE THAN 1:2.

10. ALL DATA AND POWER RECEPTACLES INTENDED FOR CUSTOMER ACCESS/USE MUST BE INSTALLED WITHIN ACCESSIBLE REACH RANGES-SEE PLAN GENERAL NOTE 1.

11. WALL MOUNTED EQUIPMENT, FIXTURES, LIGHTING, ETC. BETWEEN 27" AND 80" AFF. SHALL NOT PROTRUDE MORE THAN 4" FROM THE WALL PER ACCESSIBILITY REQUIREMENTS.

12. ALL EQUIPMENT (INCLUDING COFFEE MACHINES, ATM MACHINES, ETC.), FURNITURE, AND MILLWORK INTENDED FOR CUSTOMER USE MUST BE ON AN ACCESSIBLE ROUTE AND MUST MEET ACCESSIBILITY STANDARDS FOR CLEAR FLOOR SPACE, REACH RANGE, OPERATING PARTS, AND KNEE AND TOE SPACE AS DEFINED BY ACCESSIBILITY REQUIREMENTS OR APPLICABLE LOCAL CODES, WHICHEVER IS STRICTER.

13. ALL EQUIPMENT INTENDED FOR CUSTOMER USE MUST BE PLACED SO THAT CONTROLS REQUIRED FAR USE ARE WITHIN ACCESSIBLE REACH RANGE. OWNER MUST VERIFY THAT ALL EQUIPMENT MEETS THESE REQUIREMENTS PRIOR TO INSTALLATION.

FLOOR PLAN SYMBOLS

- PARTITION AS SCHEDULED
- DOOR AS SCHEDULED
- FEC — FIRE EXTINGUISHER CABINET
- CR — WALL-MOUNTED CARD READER AS PER DOOR HARDWARE SCHEDULE
- PB — ADA DOOR OPERATOR PUSH PADDLE AS PER DOOR HARDWARE SCHEDULE
- FB — FLOOR BOX RECEPTACLE WITH BLACK COVER PLATE TRIM FINISH
- FD — FLOOR DRAIN

PRAXIS3
100 Peachtree St NW
Suite 1450
Atlanta, GA 30303
404-875-4500 tel
www.praxis3.com

STATE OF GEORGIA
STUART M. ROMM
07/02/26
CERTIFICATE NO. 36511
REGISTERED ARCHITECT

Copyright (c) 2026 Praxis3, LLC

All reports, plans, specifications, computer files, field data, notes and other documents and instruments prepared by Praxis3 shall retain all common law, statutory and other reserved rights, including copyright thereto.

This drawing may not be reproduced in whole or in part without written permission of Praxis3. It is to be returned upon request. Scales as stated are valid on the original drawings.

Rev	Date	Comments
	07/02/2026	PERMIT SET

Client:
FIFTH THIRD BANK

Project Number: 26302
Project Name:
WATSON BLVD.


2711 WATSON BOULEVARD
WARNER ROBINS, GA 31093

Key Plan:

Sheet Title:
DIMENSIONAL FLOOR PLAN

Sheet Number:
A-120

7/8/2026 2:37:44 PM

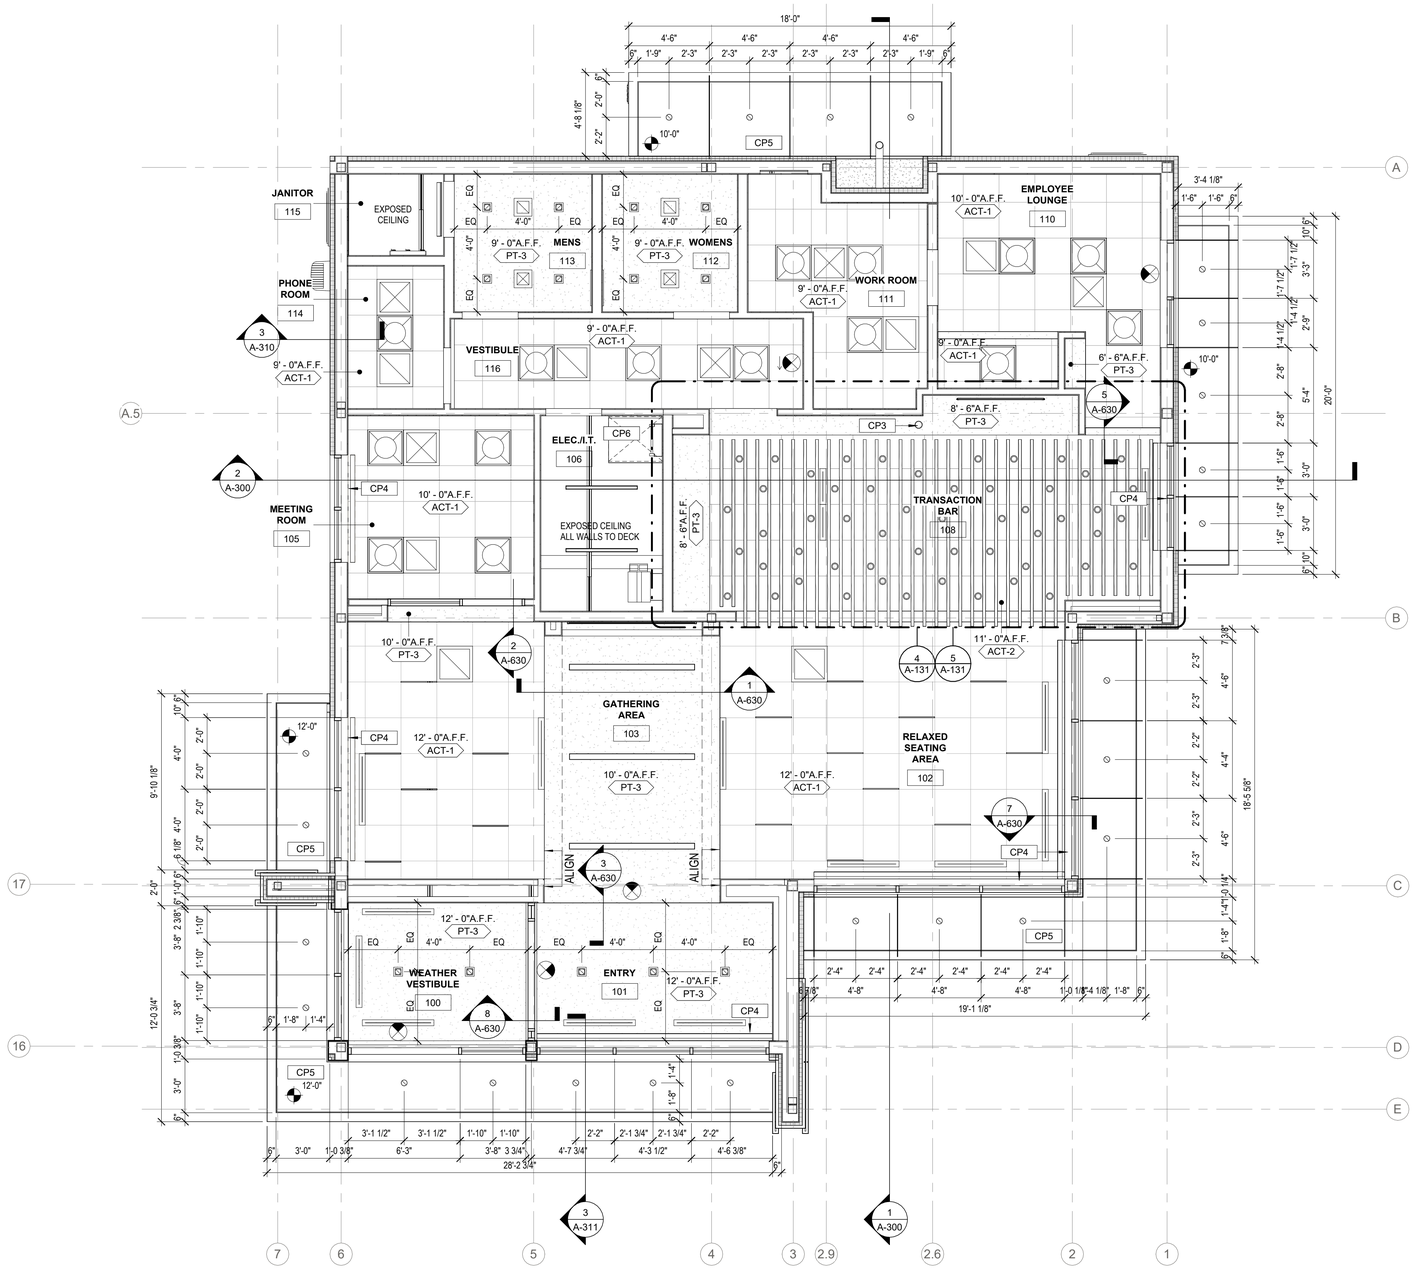

GENERAL NOTES - RCP

A. REFLECTED CEILING PLAN IS SHOWN FOR GENERAL LAYOUT PURPOSES ONLY. REFER TO MECHANICAL AND ELECTRICAL PLANS FOR ALL FIXTURES, DIFFUSERS, AND ANY OTHER REQUIREMENTS

B. REFER TO SECURITY PLAN FOR REQUIRED LIGHTING LEVELS

C. COORDINATE LENGTHS OF UNDER CABINET FIXTURES WITH SCHEDULED MILLWORK CABINETS.

D. MECHANICAL REGISTERS IN FUR DOWN ARE TO ALIGN WITH GRID

E. ALL GYPSUM BOARD CEILING PAINTED AND SUSPENDED GYPSUM BOARD ELEMENTS ARE TO BE PT-1, EXCEPT FOR THE CEILING OVER THE TRANSACTION BAR

F. CONTRACTOR TO INSTALL HVAC DUCTWORK AS HIGH AS POSSIBLE AND COORDINATE LIGHT FIXTURE LOCATIONS IN ORDER TO MAINTAIN DESIGN AT INTENDED CEILING HEIGHTS

G. GC TO PROVIDE, INSTALL AND COORDINATE PROGRAMMING OF MOTORIZED MECHOSHADES.

H. CEILING GRID MAIN TEE MUST BE PERPENDICULAR TO DIRECTION OF LINER GRID LIGHTING. G.C. TO COORDINATE.

KEY NOTES - RCP

CP1	SURFACE MOUNTED SIGN CABINET. COORDINATE SIGNAGE SIZE WITH VENDOR.
CP2	HEADACHE BAR BY BANK VENDOR
CP3	VAT TUBE - COORDINATE WITH BANK EQUIPMENT VENDOR
CP4	MOTORIZED MECHOSHADE, SEE RCP PLAN LEGEND
CP5	RECESSED CANOPY LIGHT TO BE CENTERED IN ACM, UNLESS NOTED OTHERWISE
CP6	ROOF ACCESS LADDER. REFER TO SECTION 1/A-312

LEGEND - RCP

- 2'X2' - ACOUSTIC CEILING TILE & GRID
- EXPOSED CEILING
- PAINTED GYP. CEILING
- PLASTIC LAMINATED PANEL, PL-1
- EXTERIOR GYP. CEILING
- BAR-1 BEAM BAFFLE SYSTEM
- AIR RETURN VENTS
- AIR SUPPLY VENTS
- 30" X 24" ACCESS PANEL PAINT TO MATCH CEILING
- LINEAR AIR DIFFUSER
- MOTORIZED MECHOSHADE
- EF — EXHAUST FAN
- PENDANT LIGHT
- LINEAR LIGHT
- INTEGRAL LINEAR CEILING GRID FIXTURE
- TROFFER LIGHT
- 4" RECESSED CAN DOWNLIGHT
- 6" SQUARE RECESSED CAN LIGHT
- EXIT SIGN
- SUSPENDED LINEAR STRIP LIGHT
- EXTERIOR WALL MOUNTED FIXTURE

NOTE: PROJECT NORTH IS FOR CONSTRUCTION PURPOSES ONLY. REFER TO CIVIL DRAWING FOR TRUE NORTH AND CORRECT BUILDING ORIENTATION AS IT RELATES TO THE SITE.

REFLECTED CEILING PLAN | 1/4" = 1'-0" | 1

PRAXIS3
100 Peachtree St NW
Suite 1450
Atlanta, GA 30303
404-875-4500 tel
www.praxis3.com

STATE OF GEORGIA
STUART M. ROMM
07/02/26
CERTIFICATE NO. 3457
REGISTERED ARCHITECT

Copyright (c) 2026 Praxis3, LLC

All reports, plans, specifications, computer files, field data, notes and other documents and instruments prepared by Praxis3 shall retain all common law, statutory and other reserved rights, including copyright thereto.

This drawing may not be reproduced in whole or in part without written permission of Praxis3. It is to be returned upon request. Scales as stated are valid on the original drawings.

Rev	Date	Comments
	07/02/2026	PERMIT SET

Client:
FIFTH THIRD BANK

Project Number: 26302
Project Name:
WATSON BLVD.


2711 WATSON BOULEVARD
WARNER ROBINS, GA 31093

Key Plan:


Sheet Title:
REFLECTED CEILING PLAN

Sheet Number:
A-130

7/8/2026 2:37:46 PM

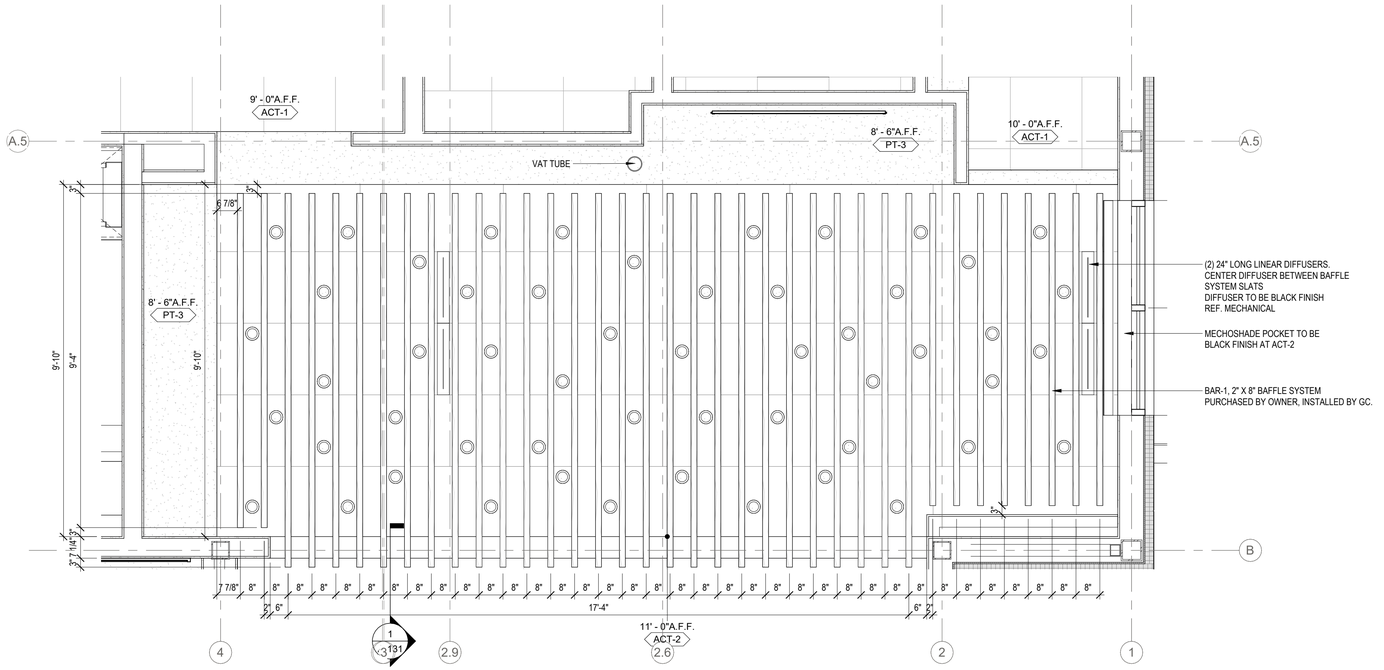

ENLARGED RCP @ TRANSACTION BAFFLES | 1/2" = 1'-0" | 5

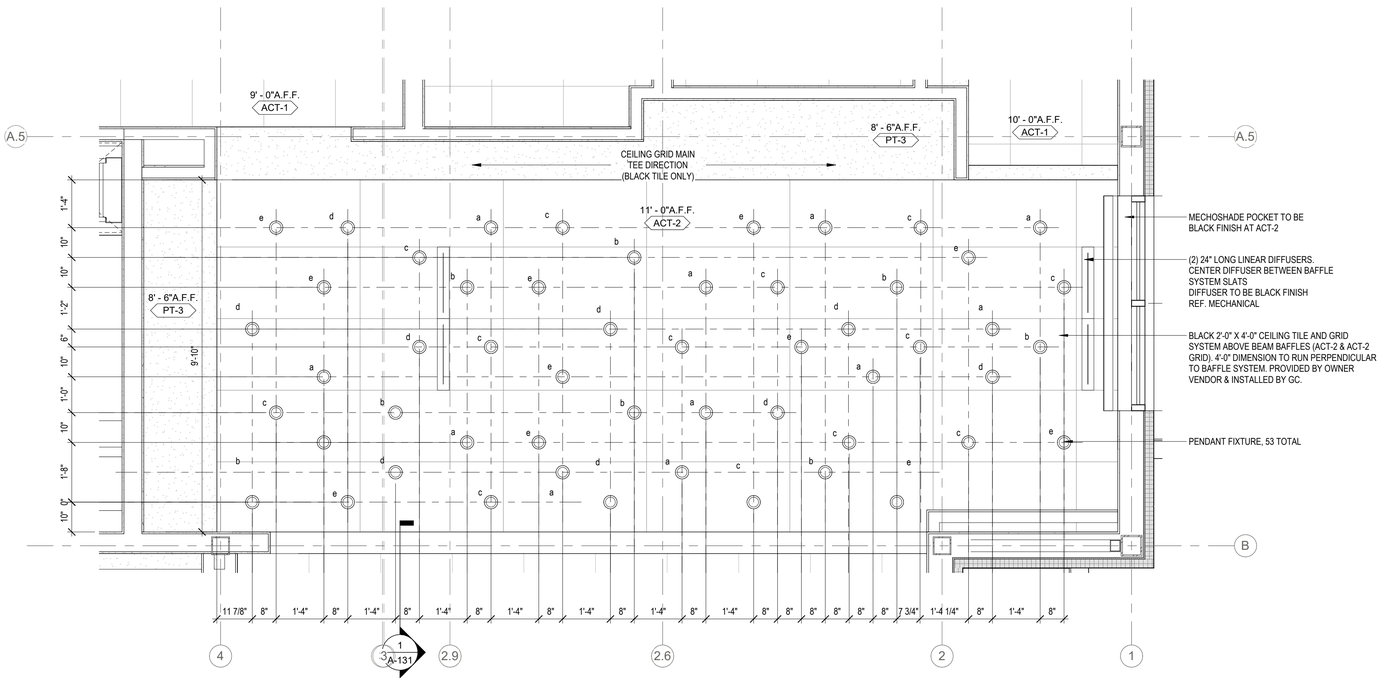


ENLARGED RCP @ TRANSACTION PENDANTS | 1/2" = 1'-0" | 4


INDICATES HEIGHT OF PENDANT FIXTURES ABOVE FINISH FLOOR
(DIMENSIONED TO TOP OF PENDANT)

a. 9'-1"
b. 9'-3"
c. 9'-5"
d. 9'-7"
e. 9'-9"


NOTE: PENDANT FIXTURE INSTALLED CENTERED BETWEEN BEAM BAFFLE SLATS, TYPICAL. SEE ELECTRICAL

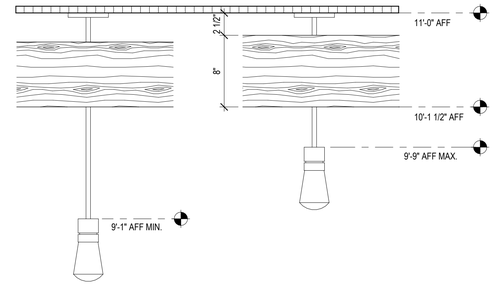

PENDANT HEIGHTS @ BAFFLE | 1 1/2" = 1'-0" | 3

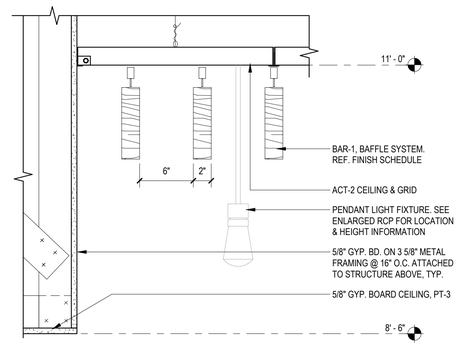

BAFFLE CEILING DETAIL | 1 1/2" = 1'-0" | 2

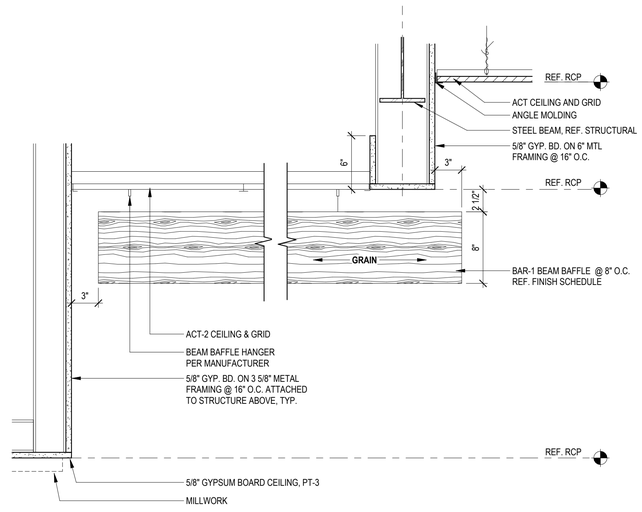

BAFFLE CEILING AT BULKHEAD | 1 1/2" = 1'-0" | 1

PRAXIS3

100 Peachtree St NW
Suite 1450
Atlanta, GA 30303
404-875-4500 tel
www.praxis3.com

STATE OF GEORGIA
STUART M. ROMM
07/02/26
CERTIFICATE NO. 3457
REGISTERED ARCHITECT

Copyright (c) 2026 Praxis3, LLC

All reports, plans, specifications, computer files, field data, notes and other documents and instruments prepared by Praxis3 shall retain all common law, statutory and other reserved rights, including copyright thereto.

This drawing may not be reproduced in whole or in part without written permission of Praxis3. It is to be returned upon request. Scales as stated are valid on the original drawings.

Rev	Date	Comments
	07/02/2026	PERMIT SET

Client:
FIFTH THIRD BANK

Project Number: 26302
Project Name:
WATSON BLVD.


2711 WATSON BOULEVARD
WARNER ROBINS, GA 31093

Key Plan:

Sheet Title:
ENLARGED REFLECTED CEILING PLAN

Sheet Number:
A-131

7/8/2026 2:37:48 PM

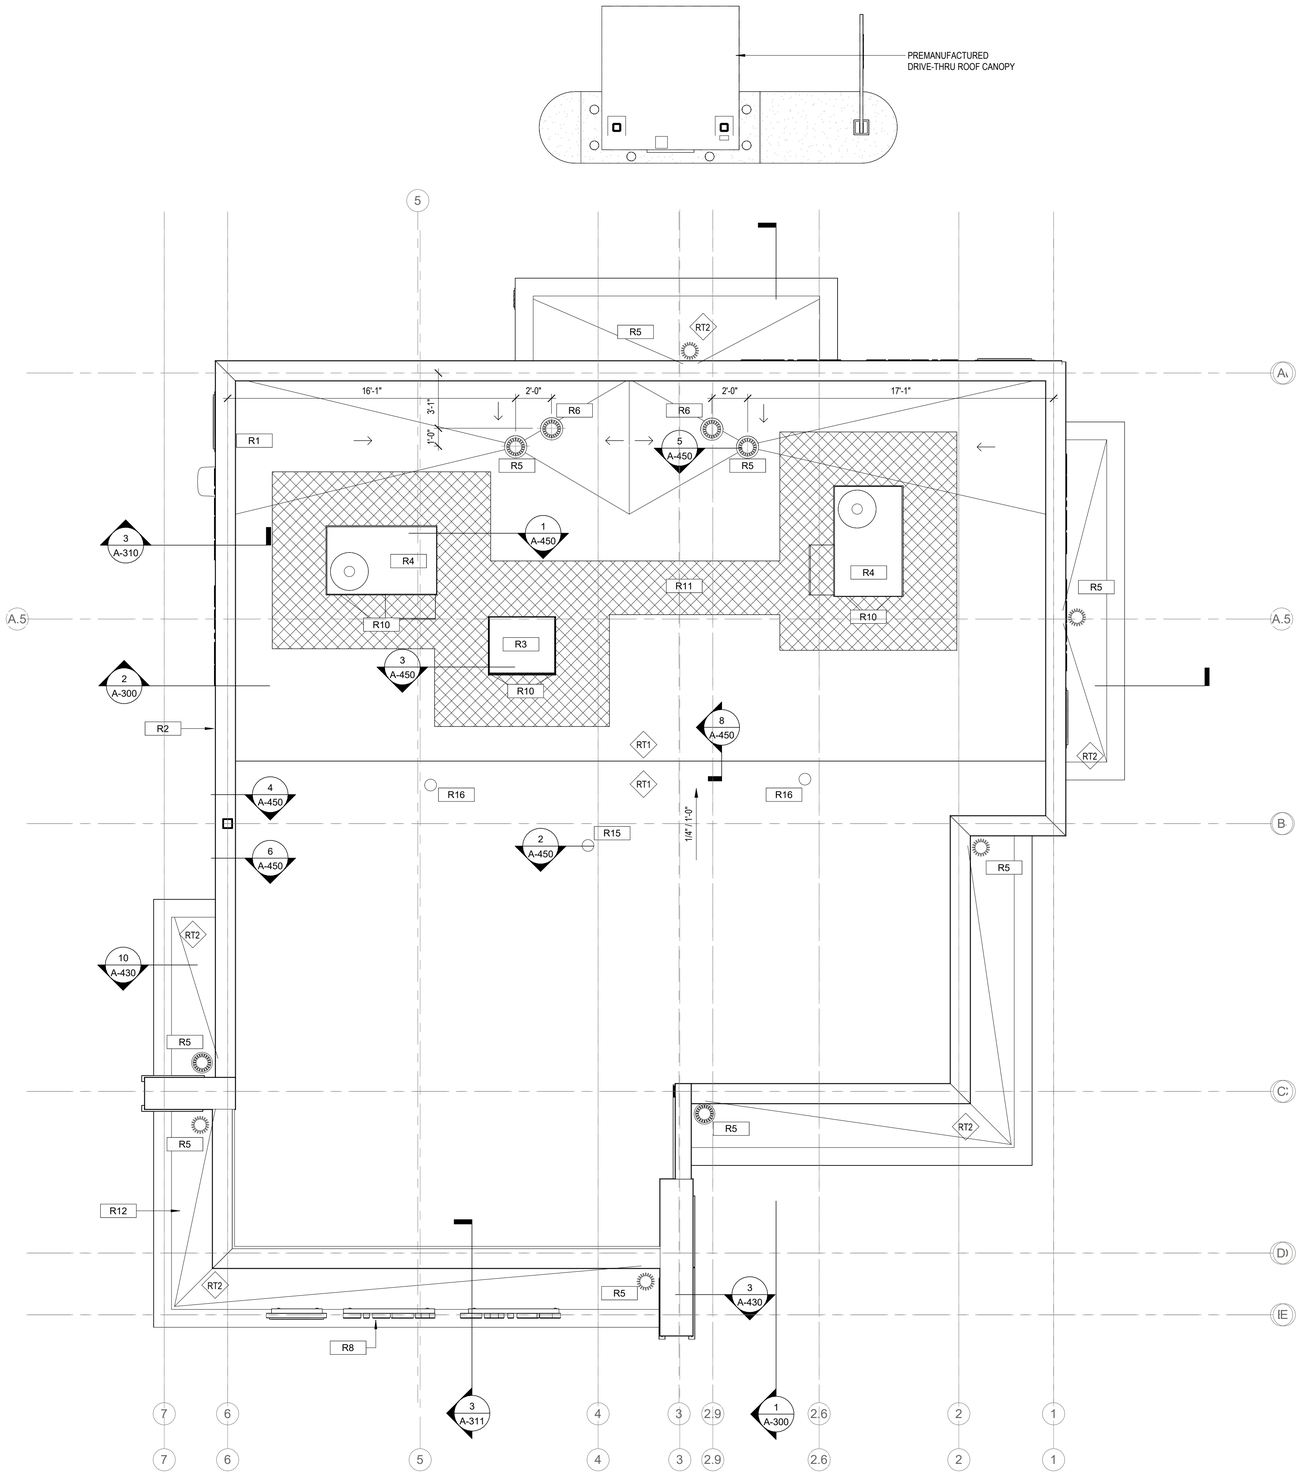


GENERAL NOTES - ROOF PLAN

1. ROOF CRICKETS 1/4" PER FOOT MINIMUM, FULLY TAPERED POLYISOCYANURATE INSULATION
2. INSTALL ALL ROOF SYSTEMS AND RELATED COMPONENTS IN STRICT ACCORDANCE WITH MANUFACTURER'S SPECIFICATIONS AND INSTALLATION INSTRUCTIONS
3. VERIFY AND COORDINATE LOCATION OF ALL ROOF PENETRATIONS WITH STRUCTURAL, MECHANICAL, ELECTRICAL, AND PLUMBING.
4. ALL ROOF PENETRATIONS REQUIRE PRESSURE TREATED 2x6 BLOCKING AT INSULATION AROUND ENTIRE PERIMETER FOR FLASHING ATTACHMENT.
5. OMISSION OF ANY ACCESSORY FROM THE ROOF PLAN SHALL NOT RELIEVE THE CONTRACTOR FROM THE RESPONSIBILITY FOR SUCH ITEMS.


KEY NOTES - ROOF PLAN

R1	WEATHER SENSOR, REF. LANDSCAPE
R2	CONT. METAL COPING TO COVER ENTIRE TOP OF PARAPET
R3	30" x 36" ROOF ACCESS HATCH
R4	MECHANICAL ROOF TOP UNIT
R5	ROOF DRAIN
R6	OVERFLOW ROOF DRAI
R7	RESERVED
R8	MAIN ENTRY CANOPY MOUNTED SIGNAGE
R9	RESERVED
R10	TAPERED INSULATION / ROOF CRICKETS POSITIVE SLOPE TOWARDS DRAIN
R11	HATCH INDICATES TPO WALKWAY PAD MEMBRANE
R12	PRE-FINISHED ALUMINUM COMPOSITE CLAD AWNING, ACM-3
R15	VENT STACK. REFER TO PLUMBING DRAWINGS FOR LOCATION
R16	NO VENT STACK SHALL BE LOCATED WITHIN 10'-0" RADIUS OF AN RTU INTAKE. COORDINATE WITH MECHANICAL.

ROOF TYPES

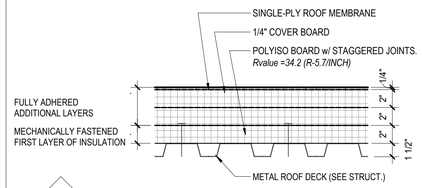

RT1 — ROOF MEMBRANE SYSTEM OVER SLOPED METAL ROOF DECK (SEE STRUCT)
(6" MIN INSULATION THICKNESS) R-VALUE = 34
NOTE: SEE ROOF PLAN FOR TAPERED INSULATION LOCATIONS

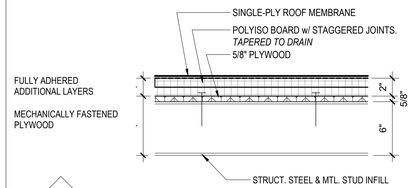

RT2 — ROOF MEMBRANE SYSTEM OVER FLAT ROOF DECK (SEE STRUCT)
NOTE: TAPER INSULATION TO ROOF DRAIN, 1" MIN. INSULATION THICKNESS

NOTE: PROJECT NORTH IS FOR CONSTRUCTION PURPOSES ONLY. REFER TO CIVIL DRAWING FOR TRUE NORTH AND CORRECT BUILDING ORIENTATION AS IT RELATES TO THE SITE.

ROOF PLAN | 1/4" = 1'-0" | 1

PRAXIS3
100 Peachtree St NW
Suite 1450
Atlanta, GA 30303
404-875-4500 tel
www.praxis3.com

STATE OF GEORGIA
STUART M. ROMM
07/02/26
CERTIFICATE NO. 3457
REGISTERED ARCHITECT

Copyright (c) 2026 Praxis3, LLC

All reports, plans, specifications, computer files, field data, notes and other documents and instruments prepared by Praxis3 shall retain all common law, statutory and other reserved rights, including copyright thereto.

This drawing may not be reproduced in whole or in part without written permission of Praxis3. It is to be returned upon request. Scales as stated are valid on the original drawings.

Rev	Date	Comments
	07/02/2026	PERMIT SET

Client:
FIFTH THIRD BANK

Project Number: 26302
Project Name:
WATSON BLVD.


2711 WATSON BOULEVARD
WARNER ROBINS, GA 31093

Key Plan:

Sheet Title:
ROOF PLAN

Sheet Number:
A-140

7/8/2026 2:37:50 PM

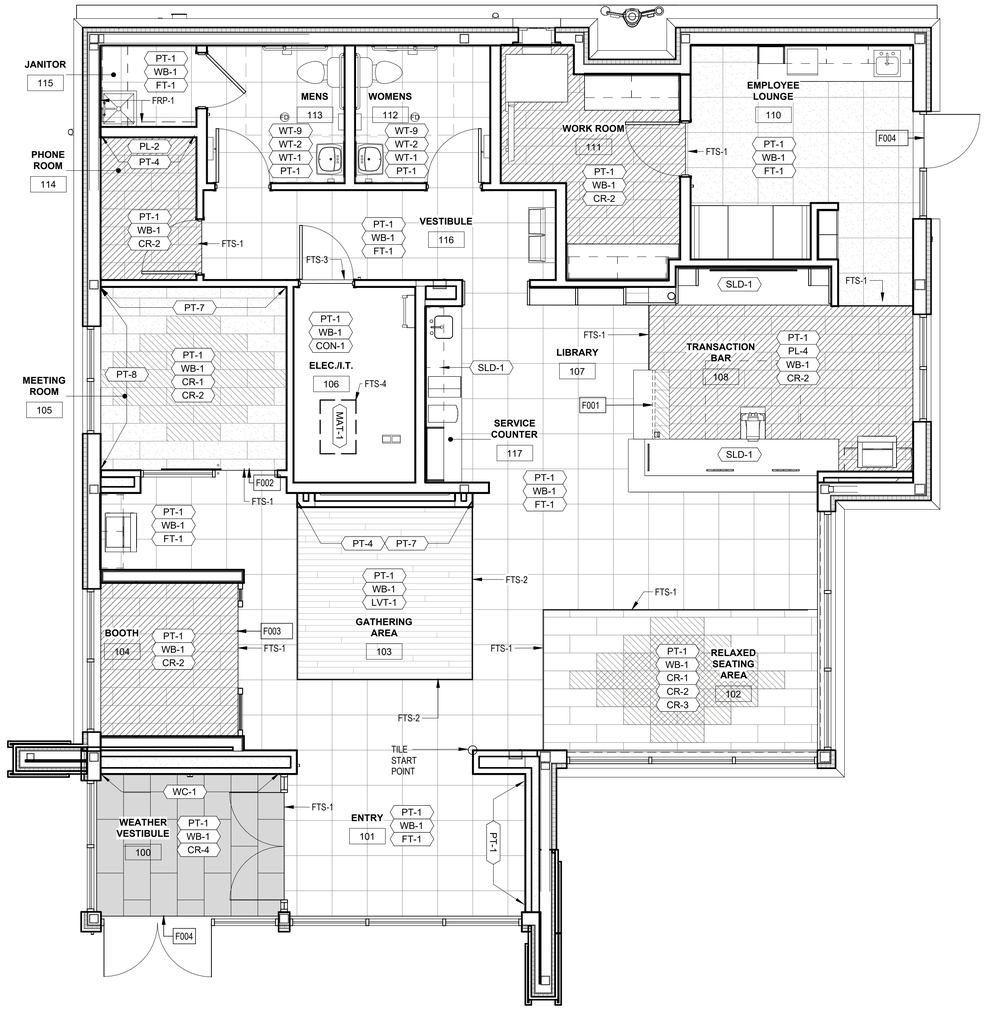

FINISH PLAN | 1/4" = 1'-0" | 6

GENERAL NOTES - FINISH PLAN

A. CONTRACTOR TO PHYSICALLY RECHECK ALL MEASUREMENTS PROVIDED IN DRAWINGS.

B. FIELD VERIFICATION IS REQUIRED FOR QUANTITIES OF ALL MATERIALS PRIOR TO ORDERING AND INSTALLING. (DO NOT SCALE DRAWINGS).

C. WHEN A CHANGE IN FLOOR FINISH OCCURS AT DOORWAY, THE SEAM IS TO BE CENTERED UNDER THE DOOR UNLESS OTHERWISE INDICATED.

D. THRESHOLDS/TRANSITION STRIPS MUST BE PROVIDED BETWEEN DIFFERING FLOORING MATERIALS. SAMPLES MUST BE PROVIDED TO DESIGNER FOR APPROVAL PRIOR TO ORDERING AND INSTALLING.

E. CONTRACTOR TO ENSURE ALL EXISTING WALLS AND FLOORS ARE PROPERLY PREPARED FOR INSTALLATION OF SPECIFIED MATERIALS. PATCH AND REPAIR AS NECESSARY, READY TO RECEIVE NEW FINISH (CARPET, PAINT LAMINATE, RESILIENT FLOORING, ETC.)

F. ALL FLOORING TO HAVE MANUFACTURER'S RECOMMENDED FINISH APPLIED AFTER INSTALLATION AND PROPER CARE AND MAINTENANCE INSTRUCTIONS TO BE ISSUED TO THE CLIENT.

G. PAINTING: ALL SURFACES TO RECEIVE ONE COAT PRIMER, TWO COATS PAINT. PROVIDE SAMPLES TO DESIGNER FOR APPROVAL FOR COLOR VERIFICATION PRIOR TO PROCEEDING WITH WORK. ALL PAINT TO BE BENJAMIN MOORE OR EQUAL: ALL DOORS AND FRAMES, TRIM TO BE LATEX SEMI-GLOSS, ALL CEILINGS TO BE FLAT, ALL WALLS TO BE EGGSHELL.

H. ENSURE SURFACES TO RECEIVE FINISHES ARE CLEAN, TRUE AND FREE OF IRREGULARITIES. DO NOT PROCEED WITH WORK UNTIL SATISFACTORY CONDITIONS HAVE BEEN CONFIRMED.

I. CONTRACTOR TO USE THIS PLAN IN CONJUNCTION WITH ALL OTHER PLANS AND ELEVATIONS TO DETERMINE LOCATIONS OF DIFFERENT MATERIALS AND FINISHES. ALL FINISHES TO MEET LOCAL BUILDING CODE REQUIREMENTS.

J. PROVIDE 1 PRIMER COAT AND 2 FINISH COATS MINIMUM.

K. THERE ARE TO BE NO SUBSTITUTIONS OF ANY SPECIFIED MATERIALS/FINISHES WITHOUT THE WRITTEN APPROVAL OF BDG ARCHITECTS, LLP. ANY UNAUTHORIZED CHANGES WILL BE REFINISHED AS SPECIFIED AT CONTRACTOR'S EXPENSE.

L. ALL MATERIALS INDICATED ON THIS CHART WERE AVAILABLE AT TIME OF SPECIFYING, BDG ARCHITECTS, LLP DOES NOT GUARANTEE SUPPLY IF NOT ORDERED IMMEDIATELY UPON AWARD OF CONTRACT BY THE GENERAL CONTRACTOR AND/OR SUBCONTRACTORS. DELAYS RESULTING FROM FAILURE TO DO SO WILL BE THE RESPONSIBILITY AND AT THE EXPENSE OF THE SAID TRADE. IT IS THE RESPONSIBILITY OF THE CONTRACTOR TO ENSURE THAT ALL INSTALLED/APPLIED MATERIALS CORRESPOND WITH THE DESIGNER'S SAMPLES AND ARE CONSISTENT IN SHAPE AND COLOR AS APPROVED. CONSULT DESIGNER FOR CLARIFICATION.

M. ALL FABRICS AND MATERIALS MUST HAVE APPROPRIATE FLAME SPREAD RATINGS AS PER OBC REQUIREMENTS. GENERAL CONTRACTOR IS RESPONSIBLE FOR OBTAINING ALL CERTIFICATES OF COMPLIANCE AND SUBMITTING THEM TO LOCAL BUILDING AUTHORITIES AND COPY TO CLIENT.

N. PROVIDE LEVEL 5 FINISH WHERE FILM IS APPLIED TO WALL. COORDINATE WITH VENDOR ON CURING TIME PRIOR TO APPLICATION OF FILM.

O. CONTRACTOR IS RESPONSIBLE TO OBTAIN MANUFACTURER'S WRITTEN SPECIFICATIONS AND/OR DESIGNER'S SPECIAL INSTRUCTIONS PRIOR TO INSTALLATION. APPLICATIONS OF MATERIALS AND TO INSTALL/APPLY THEM ACCORDINGLY IS THE CONTRACTOR'S RESPONSIBILITY. ONLY MATERIALS APPROVED IN WRITING BY THE DESIGNER ARE ALLOWED ON SITE


P. ANY SUBSTITUTION OF MATERIALS TO ACCELERATE THE WORK DURING CONSTRUCTION REQUIRES PRIOR WRITTEN APPROVAL OF BOTH THE OWNER AND THE DESIGNER


Q. BDG ARCHITECTS, LLP CANNOT BE HELD RESPONSIBLE FOR THE MANNER OF SUPPLY AND INSTALLATION/APPLICATION OF MATERIALS IF OTHER THAN SPECIFIED BY SAME AND/OR MANUFACTURER

KEY NOTES - FINISH PLAN


F001	FLOOR TRANSITION BETWEEN CARPET AND TILE. TRANSITION TO ALIGN TO VERTICAL PANEL OF ADA LOCATION OF TRANSACTION BAR.
F002	FLOOR TRANSITION AT MEETING ROOM CARPET TO FLOOR TILE. REFER TO THRESHOLD DETAIL @ DIRTT DOOR
F003	FLOOR TRANSITION BETWEEN BOOTH CARPET AND FIELD TILE. FLOORING TRANSITION TO ALIGN TO INTERIOR FACE OF MILLWORK PANEL IN THE BOOTH.
F004	GC TO PROVIDE FLOORING TRANSITIONS TO CONFORM TO CHANGES IN LEVEL BETWEEN 1/4 INCH AND 1/2 INCH MUST BE BEVELED AT 1:2 OR LESS. 1/4 INCH IS THE MAXIMUM VERTICAL RISE.

LEGEND - FINISH PLAN

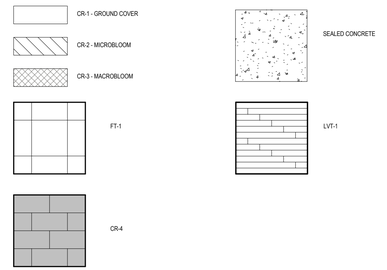

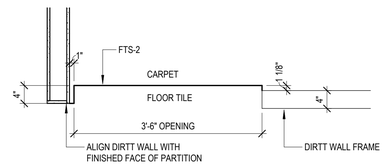


THRESHOLD DETAIL @ DIRTT DOOR | 3/4" = 1'-0" | 5

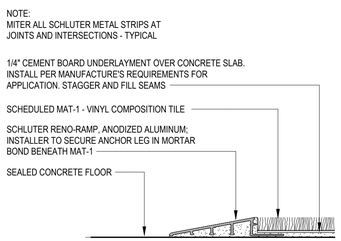


FTS 4 - SEALED CONCRETE TO CARPET

FLOOR TRANSITION: FTS-4 | 6" = 1'-0" | 4

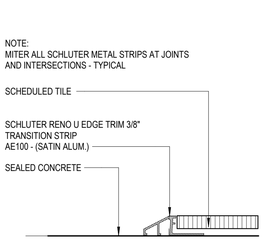


FTS 3 - CONCRETE TO TILE TRANSITION

FLOOR TRANSITION: FTS-3 | 6" = 1'-0" | 3

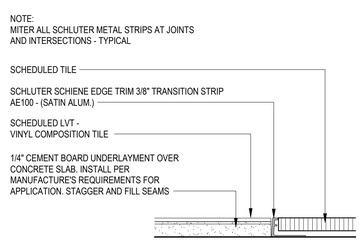

FTS 2 - VINYL TILE PLANK TO TILE

FLOOR TRANSITION - FTS-2 | 6" = 1'-0" | 2

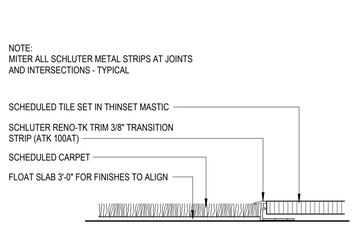

FTS 1 - CARPET TO TILE

FLOOR TRANSITION: FTS-1 | 6" = 1'-0" | 1

PRAXIS3
100 Peachtree St NW
Suite 1450
Atlanta, GA 30303
404-875-4500 tel
www.praxis3.com

STATE OF GEORGIA
STUART M. ROMM
07/02/26
CERTIFICATE NO. 3457
REGISTERED ARCHITECT

Copyright (c) 2026 Praxis3, LLC

All reports, plans, specifications, computer files, field data, notes and other documents and instruments prepared by Praxis3 shall retain all common law, statutory and other reserved rights, including copyright thereto.

This drawing may not be reproduced in whole or in part without written permission of Praxis3. It is to be returned upon request. Scales as stated are valid on the original drawings.

Rev	Date	Comments
	07/02/2026	PERMIT SET

Client:
FIFTH THIRD BANK

Project Number: 26302
Project Name:
WATSON BLVD.

2711 WATSON BOULEVARD
WARNER ROBINS, GA 31093

Key Plan:

Sheet Title:
FINISH PLAN

Sheet Number:
A-150

7/8/2026 2:37:53 PM



FURNITURE & EQUIPMENT PLAN | 1/4" = 1'-0" | 1

7/8/2026 2:37:54 PM

PRAXIS3

100 Peachtree St NW
Suite 1450
Atlanta, GA 30303

404-875-4500 tel
www.praxis3.com

STATE OF GEORGIA
STUART M. ROMM
07/02/26
CERTIFICATE NO. 34521
REGISTERED ARCHITECT

Copyright (c) 2026 Praxis3, LLC

All reports, plans, specifications, computer files, field data, notes and other documents and instruments prepared by Praxis3 shall retain all common law, statutory and other reserved rights, including copyright thereto.

This drawing may not be reproduced in whole or in part without written permission of Praxis3. It is to be returned upon request. Scales as stated are valid on the original drawings.

Rev	Date	Comments
	07/02/2026	PERMIT SET

Client:
FIFTH THIRD BANK

Project Number: 26302
Project Name:
WATSON BLVD.

2711 WATSON BOULEVARD
WARNER ROBINS, GA 31093

Key Plan:

Sheet Title:
FURNITURE & EQUIPMENT

Sheet Number:
A-160

APPLIANCE SCHEDULE

ITEM #	DESCRIPTION	MFR	MODEL #	PROV. BY	INST. BY	LOCATION	COMMENTS
AE-01	MICROWAVE DRAWER	SHARP	SMD3070ASY	GC	GC	EMPLOYEE LOUNGE	
AE-02	MICROWAVE	GE	GCST11X1WSS	GC	GC	EMPLOYEE LOUNGE	1.1 Cu. Ft. CAPACITY COUNTERTOP, STAINLESS STEEL
AE-03	REFRIGERATOR	WHIRLPOOL	WRFC2036RZ	GC	GC	EMPLOYEE LOUNGE	COUNTER-DEPTH FRENCH DOOR BOTTOM MOUNT, STAINLESS STEEL, INTERIOR WATER DISPENSER. ALT: KITCHENAID KRFC300ESS
AE-04	DISHWASHER	GE	PDT145SGL/SS	GC	GC	EMPLOYEE LOUNGE	18" ADA COMPLIANT, SS FINISH. HAIER QDT125SSL ACCEPTABLE SUB.
AE-06	QUENCH	QUENCH	Q8CT	GC	GC	SERVICE	TOUCHLESS BOTTLELESS WATER COOLER
AE-07	COFFEE MAKER	KEURIG	K4500	VENDOR	GC	SERVICE	
AE-09	TV	NEC	V984Q-C981Q 98" DISPLAY	VENDOR	VENDOR	TECH WALL	
AE-10	TV	NEC	V654Q 65"	VENDOR	VENDOR	BACK COUNTER	
AE-11	TV WALL MOUNT	PEERLESS	DS-VW795-QR	VENDOR	VENDOR	TECH WALL	
AE-12	TV WALL MOUNT			VENDOR	VENDOR	BACK COUNTER	
AE-13	SECURITY MONITOR			VENDOR	VENDOR	WORKROOM	
AE-14	IPAD CHARGING CABINET	BELKIN	B2B074	VENDOR	VENDOR	WORKROOM	18" x14" x 7". PROVIDE POWER IN BASE CABINET
AE-15	MULTI-FUNCTION PRINTER (MFP)	HP	J8A13A	VENDOR	VENDOR	VARIES	HP COLOR LASERJET ENTERPRISE FLOW MFP M681Z (PRODUCT #J8A13A)

BANK EQUIPMENT SCHEDULE

ITEM #	DESCRIPTION	MFR	MODEL #	PROV. BY	INST. BY	LOCATION	COMMENTS
BE-01	CASH CHEST/ND COMBO	HAMILTON	20-132L OR 20-132R	VENDOR	VENDOR	WORKROOM	PROVIDE HOUSEKEEPING PAD AT WALK-UP LOCATIONS
BE-02	CASH CHEST	HAMILTON	20-113R OR 20-113L	VENDOR	VENDOR	WORKROOOM	
BE-03	WALK-UP NIGHT DEPOSIT	HAMILTON	17-014 L	VENDOR	VENDOR	VARIES	
BE-03a	DRIVE-UP NIGHT DEPOSIT	HAMILTON	16-098R OR 16-098L	VENDOR	VENDOR	VARIES	
BE-04	THRU-WALL VAT	HAMILTON	PER VENDOR	VENDOR	VENDOR	VARIES	
BE-05	WALK-UP THRU WALL ATM	DIEBOLD / NIXDORF	DN SERIES 450	VENDOR	VENDOR	VARIES	
BE-06a	CASH RECYCLER	NAUTILUS HYOSUNG	MS500	VENDOR	VENDOR	TRANSACTION	
BE-6b	CASH RECYCLER	ARCA	VERO	VENDOR	VENDOR	TRANSACTION	
BE-6c	CASH RECYCLER	GLORY GLR	GLR100	VENDOR	VENDOR	TRANSACTION	
BE-07	PHONE	CISCO	7841	VENDOR	VENDOR	TRANSACTION	
BE-08	UNDERCOUNTER STEEL	CONVERGINT	FENCO #212	VENDOR	VENDOR	TRANSACTION	
BE-09	UNDERCOUNTER STEEL	CONVERGINT	FENCO S-222 OR S-622	VENDOR	VENDOR	WORKROOM	
BE-10	VAT TUBE SYSTEM	HAMILTON	HA1000-XLR	VENDOR	VENDOR	EXTERIOR	
BE-11	DRIVE-UP ATM	DIEBOLD / NIXDORF	SERIES 490	VENDOR	VENDOR	EXTERIOR	

FURNITURE SCHEDULE

ITEM #	DESCRIPTION	MANUFACTURER	DIMENSIONS	MODEL	COLOR
CH-01	TOTO CHAIR	BOSS DESIGN	23.5"W x 23"D x 32"H x 18.25"SH	TOT/3/HB	OAK LEGS ON WHITE CHASSIS
CH-02	BOMBOM	BERNHARDT	34.25"W x 30.25"D x 30"H x 19.25"H	1076K	BASE: MATTE BLACK
CH-03	MERANO CHAIR ARMLESS	GRAND RAPIDS	17"W x 17"D x 31"H x 18"SH	W400SC	ACORN WOOD FINISH ON BEECH
CH-04	LAVA	BERNHARDT	27.25"W x 22"D x 33.25"-37.25"H x 17.75-22"SH	594	SHEL: MIST
CH-05	TOTO CHAIR	BOSS DESIGN	23.5"W x 23"D x 32"H x 18.25"SH	TOT/3/HB	AMERICAN BLACK WALNUT. LEGS ON BLACK CHASSIS
CH-06	TBD	TBD			
CH-07	TOTO CHAIR	BOSS DESIGN	23.5"W x 23"D x 32"H x 18.25"SH	TOT/3/HB	OAK LEGS ON WHITE CHASSIS
CH-08	MAVIC	SITONIT	23.5"W x 23.5"D x 35.4"D x 17.5"-21.5"SH	1113.T	FRAME/BASE: FOG
CH-09	BAHKITA	GLOBAL	18"W x 21"D x 35.4" x 17.5"-21.5"SH	6751	PLASTIC: ALLOY
CH-10	MOVI STOOL	SITONIT	26"W x 26"D x 37.75"H x 21.5"-28.5"SH	1062 FT3 S21	FRAME/BASE: FOG
CH-11	MERANO	GRAND RAPIDS	17"W x 14"D x 29"H x 30"SH	W400BS	ACORN WOOD FINISH ON BEECH
CS-01	CHARGE STATION	GLOBAL INDUSTRIAL	17.5"W x 20"D x 13.5"H	WBB1963653	BLACK
LK-01	LOCKERS	GREAT OPENINGS	16"W x 12"D x 72"H	C100077	WILSONART LINEN LAM
MS-01	PHONE ROOM PEDESTAL	STEELCASE	22.75"H x 15.5"W x 22.5"D	18-0101712	CUSHION COLOR: TBD
MS-03	PLANTER	THE CHANDLER COMPANY	48"L x 12"W x 30"H	CN481830	WHITE: SMOOTH FINISH
PD-01	PENCIL - ACCY	GREAT OPENINGS	21.75"W x 17.25"D x 2.125"H	NFC7657889	BLACK
PL-01	ROO	OFS	17.5"D x 29"H	RO-29PS	ROOT
PL-02	PLANTER	THE PLANT TROLLEY	48"W x 12"D x 28"H (CAN VARY)	LARGE PLANTER	CHARCOAL GREY STAIN. SEMI-GLOSS
PT-01	THREAD	STEELCASE	30"H	PFLHUB	MERLE
PW-01	BOOTH PILLOW; BEDFORD	PALLAS TEXTILES	18" x 18"	PILLOW	JENS
PW-02	BOOTH PILLOWS; DBL STITCH	HBF	18" x 18"	PILLOW	VERT
PW-03	BOOTH PILLOWS; HERITAGE	ARCHITEX	18" x 18"	PILLOW	ROYAL
SH-03	CRATE DIVIDE 3 BAY	ALLERMUIR	53"W x 18"D x 70.5"H	CRT2H3BS	FRAME: BLACK. BASE/SHELVES: BLACK
SH-04	CRATE DIVIDE 4 BAY	ALLERMUIR	70.25"W x 18"D x 70.5"H	CRT2H4BS	FRAME: BLACK. BASE/SHELVES: BLACK
SH-06	CRATE DIVIDE 6 BAY	ALLERMUIR	106"W x 18"D x 70.5"H	DQ-CRT2H6BS	FRAME: BLACK. BASE/SHELVES: BLACK
SH-08	CRATE DIVIDE 8 BAY	ALLERMUIR	142"W x 18"D x 70.5"H	DQ-CRT2H8BS	FRAME: BLACK. BASE/SHELVES: BLACK
SS-01	RAFT SOFA	BOSS DESIGN	26.25"D x 26.25"W x 20.25"-29"H	RAFT 1 FB	LEGS: POLISHED METAL
SS-02L	LUCA 45 LEFT ARM	BERNHARDT	86.25" x 44.5"D x 29.5"H x 16.5' SH	8D33L	BASE: BLACK
SS-02R	LUCA 45 RIGHT ARM	BERNHARDT	86.25" x 44.5"D x 29.5"H x 16.5' SH	8D33R	BASE: BLACK
SS-03A	LUCA 2 SEAT	BERNHARDT	66.5"W x 33.25"D x 29.5"H x 16.5"SH	8D25N	BASE: MATTE BLACK
SS-03B	LUCA 3 SEAT	BERNHARDT	95.75"W x 33.25"D x 29.5"H x 16.5"SH	8D27N	BASE: MATTE BLACK
SS-04L	LUCA LEFT ARM W/TABLE	BERNHARDT	90.25"W x 33.25"D x 29.5"H x 16.5"SH	8D26L	BASE: MATTE BLACK. TABLE: 861 WALNUT
SS-04R	LUCA RIGHT ARM W/TABLE	BERNHARDT	90.25"W x 33.25"D x 29.5"H x 16.5"SH	8D26R	BASE: MATTE BLACK. TABLE: 861 WALNUT
SS-05	TBD	TBD			
SS-06	ORAI	ALLERMUIR	101.5"W x 33.5"D x 27"H x 17"SH	OR1300	FRAME: BLACK POWDER COAT
SS-07A	RAFT SOFA	BOSS DESIGN	26.25"D x 26.25"W x 29"H x 18"SH	RAFT 1 FB	LEGS: POLISHED METAL
SS-07B	RAFT SOFA	BOSS DESIGN	26.25"D x 52.75"W x 29"H x 18"SH	RAFT 2 RB	LEGS: POLISHED METAL
ST-01	TRACE	GREAT OPENINGS	36"W x 18.25"D x 51.5"H (CAN VARY)	RG-D103 (VARIES)	PAINT: MILK
ST-02	SLIM PED W/ CUSHION	GREAT OPENINGS	12"W x 18 7/8"D x 21"H	STU 5640C	PAINT: MILK
ST-03	STAKS	OFS	36"W x 16.5"D x 27.875"H (CAN VARY)	6-NW3617MPD2 (VARIES)	CREDENZA: STEEL LAMINATE
ST-04	YAHEETECH	AMAZON	12.6"W x 11.8"D x 34.25"H	YAHEETECH	WHITE
TB-01	INTERMIX/STAKS	OFS	72"W x 36"D x 1"H	VARIES	LAMINATE: FROSTY WHITE. COLUMN PAINT: LUSTER GREY
TB-02	LUCA	BERNHARDT	18" DIA x 23"H	LUS-LDT-BK-WLT	TOP: WALNUT 861. BASE: MATTE BLACK PAINT
TB-03A	LUCA	BERNHARDT	30" DIA x 16"H	LUS-XDM-BK-WLT	TOP: WALNUT 861. BASE: MATTE BLACK PAINT
TB-03B	LUCA	BERNHARDT	36" DIA x 16"H	LUS-ADM-BK-WLT	TOP: WALNUT 861. BASE: MATTE BLACK PAINT
TB-03C	LUCA SMALL CLUSTER	BERNHARDT	36" DIA x 16"H + 30" DIA 18"H	VARIES	TOP: WALNUT 861. BASE: MATTE BLACK PAINT
TB-03D	LUCA LARGE CLUSTER	BERNHARDT	22"DIA x 14"H	30"DIA x 14"H & 42" DIA x 16"H	VARIES
TB-04A	ROUND TOP/J87 BASE	FALCON	30" DIA	1333/J87	TOP: DESIGNER WHITE LAM. BASE SILVERSTONE
TB-04B	ROUND TOP/J87 BASE	FALCON	36" DIA	1333/J87	TOP: DESIGNER WHITE LAM. BASE SILVERSTONE
TB-05A	BLUEPRINT 1900N	BERNHARDT	66"W x 30"D x 42"H	BPX-01FNW-CCSQXXX	TOP: FROSTY WHITE LAM. BASE: PAINTED VENEER
TB-05B	BLUEPRINT 1900S	BERNHARDT	72"W x 36"D x 42"H	BPX-01BOM-CCSQXXX	TOP: FROSTY WHITE LAM. BASE: PAINTED VENEER
TB-05C	BLUEPRINT TABLE	BERNHARDT	84"W x 36"D x 42"H		TOP: FROSTY WHITE LAM. BASE: PAINTED VENEER
TB-05D	BLUEPRINT 2400+	BERNHARDT	108"W x 36"D x 42"H	BPX-01BEL-CCSQZ02	TOP: FROSTY WHITE LAM. BASE: PAINTED VENEER
TB-06	SWAP TOP / ZOLA TOP	GLOBAL + MOCKETT LEG	24"x30"	GSBTP2430 / TL53 94	TOP: DESIGNER WHITE LAM. BASE: SATIN ALUMINUM
TB-07	SWAP TOP / ZOLA TOP	GLOBAL + MOCKETT LEG	30"x48"	EX200268 / TL53 94	TOP: DESIGNER WHITE LAM. BASE: SATIN ALUMINUM
TB-08	CHECK WRITING STAND	MILLWORKER			SEE SHEET A-708 FOR DETAILS
WD-01	CONNECT X2	CLARIDGE	36"x48" (CAN VARY)	MULTIPLE	GLASS: WHITE. CORKBOARD: BLUEBERRY & GRAPHITE
WS-01	WORKSTATION	OFS	OVAL TOP: 42"D x 9'W OR 10'W (VARIES)	VARIES	TOP: FROSTY WHITE
WS-02	FLEX DESKS	STEELCASE	58"W x 29"D x 22.75"-48.5"H	FLXERQ	LAMINATE: MILK

FINISHES SCHEDULE

ITEM	DESCRIPTION	MANUF.	SIZE	SERIES	COLOR	REMARKS
CEILINGS						
ACT-1	ACOUSTICAL CEILING TILE	USG	24" x 24" x 7/8"	88135 - MARS HIGH NRC	FLAT WHITE 050	SLT EDGE, 0.85 NRC / 35 CAC
ACT-1 GRID	ACOUSTICAL CEILING GRID	USG	DX 15/16"	DONN BRAND DX/DXL	FLAT WHITE 050	
ACT-2	ACOUSTICAL CEILING TILE	ARMSTRONG	24" x 48" x 5/8"	1729 - FINE FISSURED	TECH BLACK (BL)	SQUARE LAY-IN 15/16", 0.55 NRC / 35 CAC
ACT-2 GRID	ACOUSTICAL CEILING GRID	GORDON	2" x 15/16"	ENVIRONMENTAL GRID MT-7/CT-7 GRID WA-2 WALL ANGLE	POWDER COATED PDR60403 NIGHTSHADE BLACK	PROVIDED BY SOUTHEASTERN ARCHITECTURAL SYSTEMS (SEAS). SEAS CONTACT: AUSTIN CLAYTOR, 704.896.5805 austin@seas-tr.com
BAR-1	BEAM BAFFLE	SEAS	2" x 8"	.040" ALUMINUM BEAMS	DARK WOOD II	
GWB-1	PAINTED GYP.	-	-	-	PT-3	
MECHO	MOTORIZED MECHOSHADE	MECHOSHADE		THERMOVEIL DENSE BASKET WEAVE 1300 SERIES	1319: SILVER BIRCH	5% OPEN, CONTACT LOCAL REP: WHITLIE NOCK EMAIL: WHITLIE.NOCK@MECHOSHADE.COM
DOOR FINISHES						
SCW	STAINED DOOR	OSHKOSH	-	DESIGNER COLOR SERIES	SLICED WHITE BIRCH; FINISH: AWI TR8:600 COLOR: 9133D	OSHKOSH PLATINUM PARTNER *NO SUBSTITUTIONS* CONTACT: VICKY TREU-CRAM, EMAIL: VTREUCRAM@OSHKOSHDOOR.COM
FLOOR FINISHES						
CR-1	CARPET	MOHAWK	12" x 36"	LICHEN COLLECTION	STONE COMMUNITY (GT472) 949 STONE	INTALLATION: HALF LAP
CR-2	CARPET	MOHAWK	12" x 36"	LICHEN COLLECTION	MICRO BLOOM II (GT475) 975 FELTED FRINGE STONE FINISH	INTALLATION: HALF LAP
CR-3	CARPET	MOHAWK	12" x 36"	LICHEN COLLECTION	MACRO BLOOM II (GT474) 975 FELTED FRINGE FINISH	INTALLATION: HALF LAP
CR-4	WALK-OFF CARPET	MANNINGTON COMMERCIAL	18" x 36"	CHARGE	STYLE: CHARGE, COLOR: FLUID (32367)	INSTALLATION: HORIZONTAL BRICK ASHLAR
FT-1	CERAMIC TILE	FLORIDA TILE	24" x 24"	AVENTIS	VELVET	UNPOLISHED. GR-1 GROUT. CONTACT: FLORIDA TILE EMAIL: ERLANGER.ORDERS@FLORIDATILE.COM and AUSTIN.KLEIN@FLORIDATILE.COM
LVT-1	LUXURY VINYL TILE	INTERFACE	25cm x 1m	ON GRAIN 4.5mm	EARTHEN FORMS, COLOR: A03305 BESPOKE TIMBER	INSTALL PATTERN: ASHLAR w/ GLUED PERIMETER
LVT-2	LUXURY VINYL TILE	MOHAWK	12" x 24"	C0135 MATAYO PLUS STONE	COLOR: 972A SONIC SILVER STONE	
CON-1	SEALED CONCRETE	BENJAMIN MOORE	-	COROTECH HIGH PERFORMANCE	CLEAR ACRYLIC	
MT-1	ANTI-STATIC MAT	MATS INC.	36" x 48"	-	BLACK	ANTI STATIC/ANTI FATIGUE, COLOR: BLACK
TRANSITION STRIP						
FTS-1	TRANSITION STRIP	SCHLUTER	-	SCHIENE AE100	SATIN ALUMINUM	CARPET TO TILE
FTS-2	TRANSITION STRIP	SCHLUTER	-	SCHIENE AE100	SATIN ALUMINUM	VINYL TILE TO CERAMIC TILE
FTS-3	TRANSITION STRIP	SCHLUTER	-	RENO U AE100	SATIN ALUMINUM	TILE TO SEALED CONCRETE
FTS-4	TRANSITION STRIP	SCHLUTER	-	RENO-RAMP AERP	SATIN ALUMINUM	SEALED CONCRETE TO MAT
GROUT						
GR-1	GROUT	CUSTOM BUILDING		EPOXY	335 WINTER GRAY	TRANSACTION BAR & FLOOR TILE
GR-3	GROUT	CUSTOM BUILDING		EPOXY	543 DRIFTWOOD	SERVICE AREA, EMPLOYEE LOUNGE, RESTROOM WALLS
MILLWORK						
PL-1	PLASTIC LAMINATE	WILSONART	-	STANDARD LAMINATE	FLORENCE WALNUT 7993-38	FINE VELVET FINISH
PL-2	PLASTIC LAMINATE	WILSONART	-	STANDARD LAMINATE	MAGNOLIA 5012-60	MATTE FINISH FOR HORIZONTAL APPLICATION
PL-3	PLASTIC LAMINATE	WILSONART	-	STANDARD LAMINATE	MAGNOLIA 5012-19	LENO WEAVE FOR VERTICAL APPLICATION
PL-4	PLASTIC LAMINATE	NEVAMAR	-	STANDARD LAMINATE	WROUGHT IRON S6054	ARP(T-) FINISH
PL-5	PLASTIC LAMINATE	WILSONART	-	STANDARD LAMINATE	CRYSTAL D388-60	MATTE
PL-6	PLASTIC LAMINATE	WILSONART		STANDARD LAMINATE	LAPIS BLUE D417-60	LOCATED AT CHECK DESK
SLD-1	SOLID SURFACE	WILSONART	-	QUARTZ	NIWA Q1002	TRANSACTION BAR COUNTERTOP. CONTACT: AMANDA FORBES (205) 532-9500
PAINT						
PT-1	PAINT	SHERWIN WILLIAMS	-	PROMAR 200 HP ZERO VOC	SW9166 DRIFT OF MIST	EGGSHELL
PT-2	PAINT	SHERWIN WILLIAMS	-	PROMAR 200 HP ZERO VOC	SW9166 DRIFT OF MIST	SEMI-GLOSS
PT-3	PAINT	SHERWIN WILLIAMS	-	PROMAR 200 HP ZERO VOC	SW9166 DRIFT OF MIST	FLAT
PT-4	PAINT	BENJAMIN MOORE	-	REGAL SELECT	2066-10 BLUE	(TECH WALL) EGGSHELL, LEVEL 5 WALL FINISH
PT-5	PAINT	BENJAMIN MOORE	-	REGAL SELECT	2037-30 KELLY GREEN	SEMI-GLOSS
PT-6	PAINT	BENJAMIN MOORE	-	REGAL SELECT	1603 GRAPHITE	EGGSHELL
PT-7	PRIMER	SHIELDZ	-	UNIVERSAL WALLCOVERING	ROMAN PRO - 999 ULTRA PRIME	PRIMER (DRIES CLEAR), COORDINATE w/ OWNER VENDOR
PT-8	PAINT	BENJAMIN MOORE	-	REGAL SELECT INTERIOR PAINT	797 ATHENS BLUE	EGGSHELL
WALL TILE / COVERING						
WT-1	WALL TILE	ROCA	3" x 12"	FLOW	WHITE (FLOWH17-312)	GLOSS FINISH, MIX 60% TOP TRIM: SCHLUTER JOLLY J AE WITH INSIDE & OUTSIDE CORNER TRIM ACCESSORIES
WT-2	WALL TILE	ROCA	3" x 12"	FLOW	COSMIC SAPPHIRE (FLOCB09-312)	GLOSS FINISH, MIX 20%
WT-3	WALL TILE	MOSA	6" x 12"	MURALS	DARK ANTHRACITE #2 (30610-1530)	GLOSS FINISH
WT-8	BULLNOSE	ROCA	3" x 12"	FLOW	TENDER GRAY (FLOTG10-S4312)	BULLNOSE AS BASE
WT-9	WALL TILE	ROCA	3" x 12"	FLOW	TENDER GRAY (FLOTG10-312)	GLOSS FINISH, MIX 20%. COVE TRIM: SCHLUTER DILEX-AHK 1S AE WITH INSIDE & OUTSIDE TRIM ACCESSORIES
WT-10	WALL TILE	SOUTH CYPRESS		PICKET	MIX BLUE	FLAGSHIP BRANCH ONLY Contact: Karen Royal 205.402.8130
WC-1	WALL COVERING	FORMULA	VARIES	VARIES BY FOCUS MARKET		Contact: Tyler Gilbert (205) 278-9622
FRP-1	FIBERGLASS REINFORCED PLASTIC	MARLITE	48" H	PEBBLED	P100 CLASSIC WHITE	JANITOR CLOSET WET WALLS
WALL BASE & TRIM						
WB-1	RUBBER BASE	JOHNSONITE	4"	TRADITIONAL WALL BASE	#48 GREY	CONTACT: KAREN ROYAL (205) 402-8130
PANEL SYSTEM						
PNL-1	BOOTH SCREEN	BIG APPLE VISUAL GROUP	SEE PLAN	-	PANEL SYSTEM	SIRAJ SAYEED siraj@bigapplegroup.com, (631) 881-5006

PRAXIS3

100 Peachtree St NW
Suite 1450
Atlanta, GA 30303
404-875-4500 tel
www.praxis3.com

STATE OF GEORGIA
STUART M. ROMM
07/02/26
CERTIFICATE NO. 34857
REGISTERED ARCHITECT

Copyright (c) 2026 Praxis3, LLC

All reports, plans, specifications, computer files, field data, notes and other documents and instruments prepared by Praxis3 shall retain all common law, statutory and other reserved rights, including copyright thereto.

This drawing may not be reproduced in whole or in part without written permission of Praxis3. It is to be returned upon request. Scales as stated are valid on the original drawings.

Rev	Date	Comments
	07/02/2026	PERMIT SET

Client:
FIFTH THIRD BANK

Project Number: 26302
Project Name:
WATSON BLVD.


2711 WATSON BOULEVARD
WARNER ROBINS, GA 31093

Key Plan:

Sheet Title:
SCHEDULES

Sheet Number:
A-170


7/8/2026 2:37:56 PM

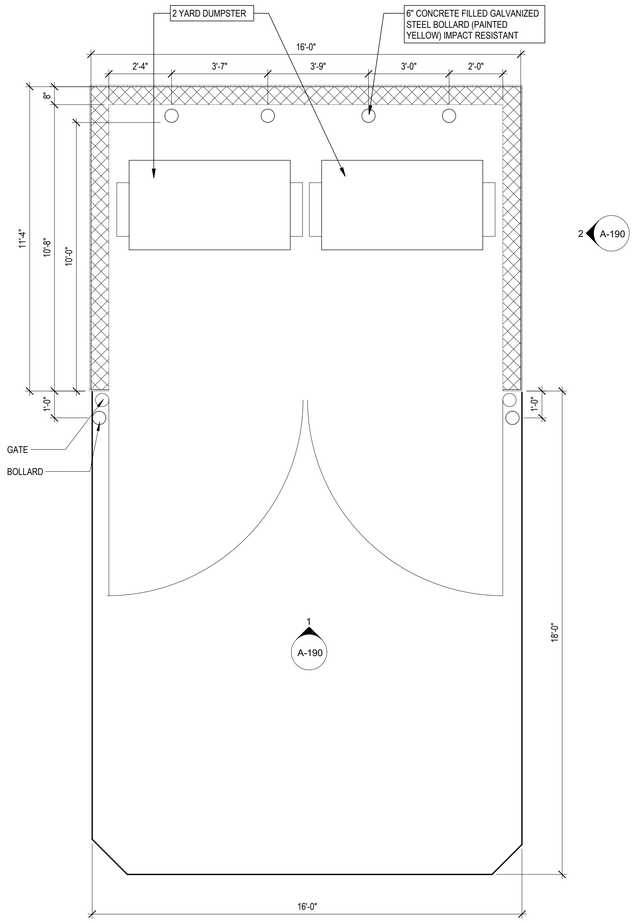


FLOOR PLAN @ TRASH ENCLOSURE | 3/8" = 1'-0" | 4

EXTERIOR FINISH SCHEDULE

ITEM	EXTERIOR FINISH	MANUFACTURER	COLOR	COMMENTS
ACM-1	ALUMINUM COMPOSITE METAL PANEL	ALCOA ARCHITECTURAL REYNOBOND	CUSTOM FIFTH THIRD BLUE	4MM FR CORE ALUM. COMPOSITE PANEL, DURAGLOSS 3000
ACM-2	ALUMINUM COMPOSITE METAL PANEL	ALCOA ARCHITECTURAL REYNOBOND	CUSTOM FIFTH THIRD GREEN	4MM FR CORE ALUM. COMPOSITE PANEL, DURAGLOSS 3000
ACM-3	ALUMINUM COMPOSITE METAL PANEL	ALCOA ARCHITECTURAL REYNOBOND	ANODIC CLEAR	4MM FR CORE ALUM. COMPOSITE PANEL, COLORWELD 500
AL-1	ANODIZED ALUMINUM	YKK	CLEAR ANODIZED	BASIS OF DESIGN: 2" X 4 1/2" YKK YES45 TU CENTER SET STOREFRONT
EIFS-1	EIFS BARRIER SYSTEM	DRYVIT OUTSULATION PLUS MD	DOVER SKY	3" EIFS SYSTEM - TYP., SANDBLAST FINISH
EIFS-2	EIFS BARRIER SYSTEM	DRYVIT OUTSULATION PLUS MD	DOVER SKY	5" EIFS SYSTEM @ VESTIBULE PARAPET, SANDBLAST FINISH
EPT-1	PAINTED GALVANIZED STEEL GATE	BENJAMIN MOORE	BALBOA MIST - OC27	SEMI-GLOSS @ STEEL, SATIN FINISH @ WALLS
EXT-1	STANDARD MODULAR BRICK VENEER	ACME BRICK	SLATE GRAY	MORTAR MANUFACTURER: COOSA , MORTAR COLOR: OLD LIME PUTTY
GL-1	EXTERIOR GLAZING	VITRO	SOLARBAN 90 ACUITY + ACUITY	ARGON U-0.24, SHCC=0.23
M-1	PREFINISHED METAL COPING	PAC-CLAD	MATCH ACM-3	

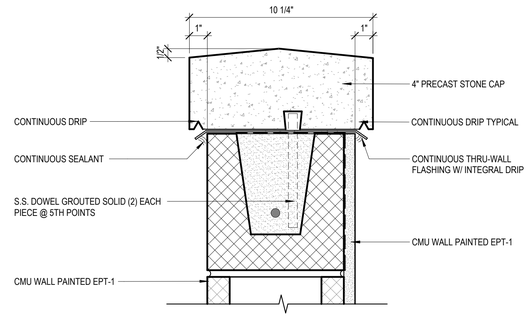

WALL CAP DETAIL | 3" = 1'-0" | 5

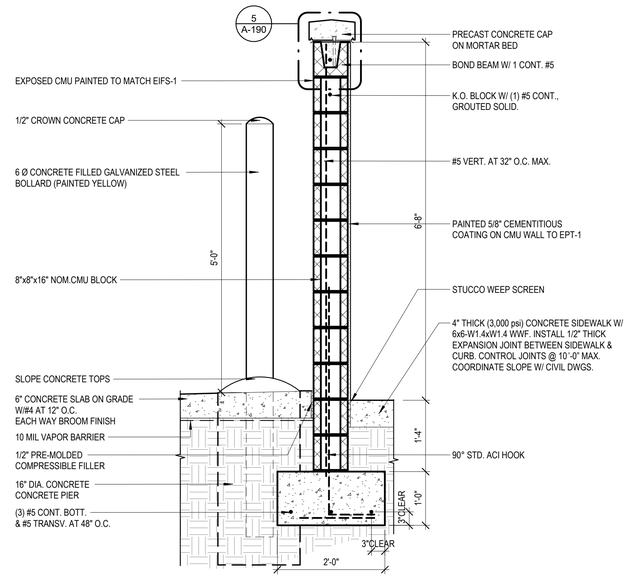


WALL SECTION @ TRASH ENCLOSURE | 3/4" = 1'-0" | 3

GENERAL NOTES


1. ALL DIMENSIONS ARE FROM EXTERIOR FACE OF SHEATHING U.N.O.
2. REFER TO CIVIL PLAN FOR NORTH ORIENTATION
3. EDGE OF DOOR JAMB SHALL BE MINIMUM 4" FROM INTERSECTING WALL UNLESS OTHERWISE NOTED OR AS REQUIRED FOR HARDWARE INSTALLATION.
4. SEE SHEET A-620 FOR PARTITION TYPES.
5. LOCATION AND NUMBER OF FIRE EXTINGUISHERS ARE TO BE INSTALLED PER THE DIRECTION OF THE LOCAL AUTHORITIES AND NFPA 13.
6. ALL INTERIOR FINISHES ARE TO COMPLY WITH THE REQUIREMENTS AS SET FORTH IN THE CURRENT STANDARD EDITION OF ALL GOVERNING CODES, REGULATIONS AND ORDINANCES HAVING JURISDICTION OVER THE SCOPE OF WORK.
7. CONTRACTOR WILL SECURE ALL BUILDING PERMITS & INSPECTIONS NECESSARY FOR THE CONSTRUCTION OF THE PACE.
8. DRAWINGS ARE NOT TO BE SCALED FOR INFORMATION.
9. CONTRACTOR SHALL COORDINATE ALL WOOD BLOCKING, STEEL SUPPORTS AND ANY OTHER ITEMS WHICH ARE IMBEDDED IN DRYWALL PARTITIONS OR ENCLOSURES WHICH RELATE TO HIS WORK OR THE WORK OF ANY SEPARATE CONTRACTORS.ALL WOOD BLOCKING, BRIDGING, BRACING, FRAMING, ETC., SHALL BE FIRE RETARDANT TREATED AS CALLED FOR BY THE GOVERNING BUILDING CODE AND THE CONTRACTOR MUST SUBMIT AFFIDAVITS OF SUCH FIRE TREATMENT TO THE OWNERSHIP.
10. REFER TO EXTERIOR ELEVATIONS AND WINDOW / DOOR SCHEDULE FOR ADDITIONAL STOREFRONT INFORMATION
11. REFERENCE ENGINEERING PLANS FOR PLUMBING, ELECTRICAL EQUIPMENT AND SYSTEMS. CONTRACTOR TO VERIFY AND COORDINATE PLUMBING ROUGH-IN DIMENSIONS WITH PLUMBER.
12. CONTRACTOR TO VERIFY SIZE AND LOCATION OF DRIVE-UP BANKING EQUIPMENT WITH EQUIPMENT VENDOR PRIOR TO CONSTRUCTION
13. CONTRACTOR TO VERIFY SIZE AND LOCATION OF ALL STEEL PIPE BOLLARDS AROUND DRIVE-UP BANKING MACHINES WITH EQUIPMENT VENDOR PRIOR TO CONSTRUCTION
14. CONTRACTOR TO VERIFY ALL ELECTRICAL REQUIREMENTS OF DRIVE-UP BANKING MACHINES PRIOR TO CONSTRUCTION
15. CONTRACTOR TO COORDINATE MAXIMUM EXTERIOR WALL THICKNESS AT NIGHT DROP WITH EQUIPMENT VENDOR
16. CONTRACTOR TO VERIFY ALL REQUIREMENTS, SIZE AND LOCATION OF NIGHT DEPOSIT WITH BANKING EQUIPMENT WITH EQUIPMENT VENDOR PRIOR TO CONSTRUCTION
17. CONTRACTOR TO FRAME FOR DRIVE-UP OPEN / CLOSE RECESSED SIGNAGE. VERIFY SIZE AND REQUIREMENTS WITH OWNER FURNISHED VENDOR.
18. CONTRACTOR TO SET BANKING EQUIPMENT TEMPLATES. EQUIPMENT VENDOR TO VERIFY CORRECT PLACEMENT AND TO COORDINATE WITH CONTRACTOR FOR PROPER PLACEMENT
19. NO ADJUSTMENT TO THE CONTRACT AMOUNT WILL BE GIVEN FOR THE CONTRACTOR NOT FULLY ACQUITTING HIMSELF WITH EQUIPMENT VENDOR REQUIREMENTS.
20. COORDINATE PINK NOISE LOCATION WITH VENDOR. REFER TO ELECTRICAL DRAWINGS.
21. ALL PAINTED STEEL PIPE BOLLARDS ARE TO RECEIVE A BOLLARD COVER TYPICAL
22. ALL INTERIOR DIMENSIONS ARE FROM FINISHED FACE UNLESS INDICATED OTHERWISE.
23. REFER TO SHEET A-600 SERIES FOR DOOR AND WINDOW SCHEDULE ALL DIMENSIONS ARE FROM FINISHED FACE UNLESS INDICATED OTHERWISE.
24. ALL PLYWOOD SHEATHING SHALL BE FRT.

FT_TRASH ENCLOSURE KEY NOTES

TAG	DESCRIPTION
TE1	6" DIA. CONCRETE FILLED GALVANIZED STEEL BOLLARD (PAINTED YELLOW)
TE2	6" DIA. STEEL GATE POST WITH SELF CLOSING HINGE (PAINTED TO MATCH PREFINISHED PANEL)
TE3	SIGNAGE "NO PARKING" SHALL MEET SOLID WASTE ORDINANCE
TE4	STEEL CANE BOLT ONE PER GATE (BASIS OF DESIGN: STANLEY HARDWARE #1010) WELD TO STEEL PLATE (4"x14"x1/4") ON GATE
TE5	SUPPORT WHEEL ONE PER GATE BASIS OF DESIGN: GRAINGER #1VJD5 WHEEL

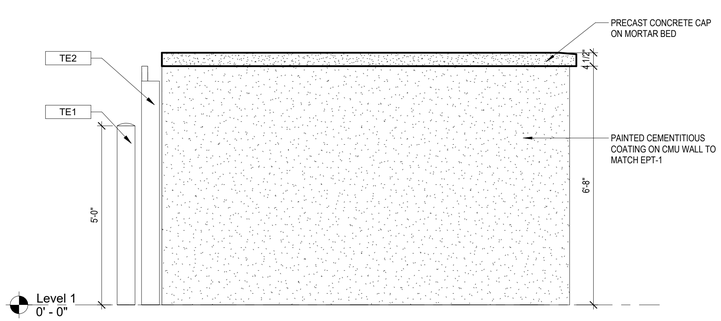

SIDE ELEVATION @ TRASH ENCLOSURE | 1/2" = 1'-0" | 2

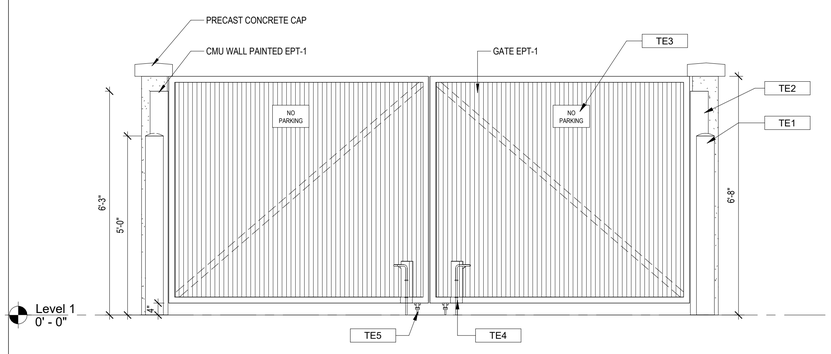

FRONT ELEVATION @ TRASH ENCLOSURE | 1/2" = 1'-0" | 1

NOTE: PROJECT NORTH IS FOR CONSTRUCTION PURPOSES ONLY. REFER TO CIVIL DRAWING FOR TRUE NORTH AND CORRECT BUILDING ORIENTATION AS IT RELATES TO THE SITE.

PRAXIS3
100 Peachtree St NW
Suite 1450
Atlanta, GA 30303
404-875-4500 tel
www.praxis3.com

STATE OF GEORGIA
STUART M. ROMM
07/02/26
CERTIFICATE NO. 3457
REGISTERED ARCHITECT

Copyright (c) 2026 Praxis3, LLC

All reports, plans, specifications, computer files, field data, notes and other documents and instruments prepared by Praxis3 shall retain all common law, statutory and other reserved rights, including copyright thereto.

This drawing may not be reproduced in whole or in part without written permission of Praxis3. It is to be returned upon request. Scales as stated are valid on the original drawings.

Rev	Date	Comments
	07/02/2026	PERMIT SET

Client:
FIFTH THIRD BANK

Project Number: 26302
Project Name:
WATSON BLVD.

2711 WATSON BOULEVARD
WARNER ROBINS, GA 31093

Key Plan:

Sheet Title:
TRASH ENCLOSURE AND DETAILS

Sheet Number:
A-190

7/8/2026 2:37:58 PM

EXTERIOR FINISH SCHEDULE

ITEM	EXTERIOR FINISH	MANUFACTURER	COLOR	COMMENTS
ACM-1	ALUMINUM COMPOSITE METAL PANEL	ALCOA ARCHITECTURAL REYNOBOND	CUSTOM FIFTH THIRD BLUE	4MM FR CORE ALUM. COMPOSITE PANEL, DURAGLOSS 3000
ACM-2	ALUMINUM COMPOSITE METAL PANEL	ALCOA ARCHITECTURAL REYNOBOND	CUSTOM FIFTH THIRD GREEN	4MM FR CORE ALUM. COMPOSITE PANEL, DURAGLOSS 3000
ACM-3	ALUMINUM COMPOSITE METAL PANEL	ALCOA ARCHITECTURAL REYNOBOND	ANODIC CLEAR	4MM FR CORE ALUM. COMPOSITE PANEL, COLORWELD 500
AL-1	ANODIZED ALUMINUM	YKK	CLEAR ANODIZED	BASIS OF DESIGN: 2" X 4 1/2" YKK YES45 TU CENTER SET STOREFRONT
EIFS-1	EIFS BARRIER SYSTEM	DRYVIT OUTSULATION PLUS MD	DOVER SKY	3" EIFS SYSTEM - TYP., SANDBLAST FINISH
EIFS-2	EIFS BARRIER SYSTEM	DRYVIT OUTSULATION PLUS MD	DOVER SKY	5" EIFS SYSTEM @ VESTIBULE PARAPET, SANDBLAST FINISH
EPT-1	PAINTED GALVANIZED STEEL GATE	BENJAMIN MOORE	BALBOA MIST - OC27	SEMI-GLOSS @ STEEL, SATIN FINISH @ WALLS
EXT-1	STANDARD MODULAR BRICK VENEER	ACME BRICK	SLATE GRAY	MORTAR MANUFACTURER: COOSA , MORTAR COLOR: OLD LIME PUTTY
GL-1	EXTERIOR GLAZING	VITRO	SOLARBAN 90 ACUITY + ACUITY	ARGON U-0.24, SHCC=0.23
M-1	PREFINISHED METAL COPING	PAC-CLAD	MATCH ACM-3	

GLAZING - GENERAL NOTES

EXTERIOR GLAZING BASIS OF DESIGN:

REGULAR EXTERIOR STOREFRONT:
YKK YES45 TU - CENTER SET THERMALLY BROKEN STOREFRONT, 1" PANEL INFILL
2" X 4 1/2" MULLION

EXTERIOR INSULATED GLASS UNIT:
VITRO SOLARBAN 90 (2) ACUITY + ACUITY
OVERALL THICKNESS: 1 INCH
VLT: 53%
EXT. REFLECTANCE: 12%
INT. REFLECTANCE: 19%
U-VALUE (ARGON): 0.24
SHGC: 0.23
LSG: 2.30
PROVIDE SAFETY GLAZING LABELING

INTERIOR GLAZING BASIS OF DESIGN:
YKK YES45 FS - CENTER SET, 1/4" PANEL INFILL
1 3/4" X 4 1/2" MULLION

INTERIOR GLASS UNIT:
CLEAR FLOAT GLASS, FULLY TEMPERED
OVERALL THICKNESS: 6mm (1/4")
PROVIDE SAFETY GLAZING LABELING

ACM PANEL - GENERAL NOTES

A. ALL ACM PANELS MUST BE ANCHORED TO MINIMUM 16 GA METAL STUD FRAMING. REFER TO STRUCTURAL. METAL STUD FRAMING NOT BY CA SYSTEMS.

B. METAL STUDS MUST ALIGN WITH PANEL JOINTS AS REQUIRED FOR METAL COMPOSITE PANEL ATTACHMENT.

C. FIXED STUDS MAY BE USED TO SUPPORT METAL COMPOSITE PANELS (G.C. TO COORDINATE)

D. 5/8" GYP. BD SHEATHING AND/OR GLASS MAT SHEATHING WILL NOT SUPPORT METAL COMPOSITE PANEL ATTACHMENT (SHEATHING NOT BY CA SYSTEMS)


E. ALL FLATSTOCK FABRICATED FLASHING REQUIRED FOR METAL COMPOSITE PANEL DETAILS TO BE PREFINISHED ALUMINUM. COLOR TO MATCH U.N.O.

F. ALL DIMENSIONS AND QUANTITIES ARE TO BE FIELD VERIFIED PRIOR TO THE FABRICATION (RELEASE) OF ANY & ALL METAL COMPOSITE PANEL AND ASSOCIATED FLASHINGS.


G. ALL SKYWARD ACM PANEL JOINTS TO HAVE BACKER ROD AND CAULK. APPLY DOWN PAST WOOD BLOCKING, TYP.

H. USE BACKER ROD AND CAULK AT ALL VERTICAL PANEL END (JAMB) CONDITIONS AT DISSIMILAR MATERIALS (IE, STUCCO, WINDOW MULLIONS)


I. ALL SKYWARD ACM PANEL JOINTS TO HAVE BACKER ROD AND CAULK. APPLY DOWN PAST WOOD BLOCKING, TYP. USE BACKER ROD AND CAULK AT ALL VERTICAL PANEL END (JAMB) JOINT CONDITIONS AT DISSIMILAR MATERIALS (IE STUCCO, WINDOW MULLION)

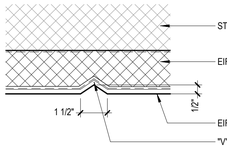


EIFS REVEAL | 3" = 1'-0" | R1

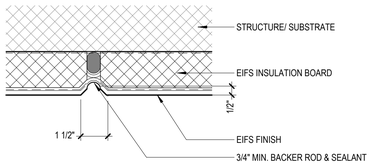


EIFS CONTROL JOINT | 3" = 1'-0" | CJ

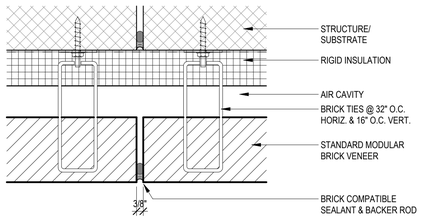

BRICK CONTROL JOINT | 3" = 1'-0" | CJ

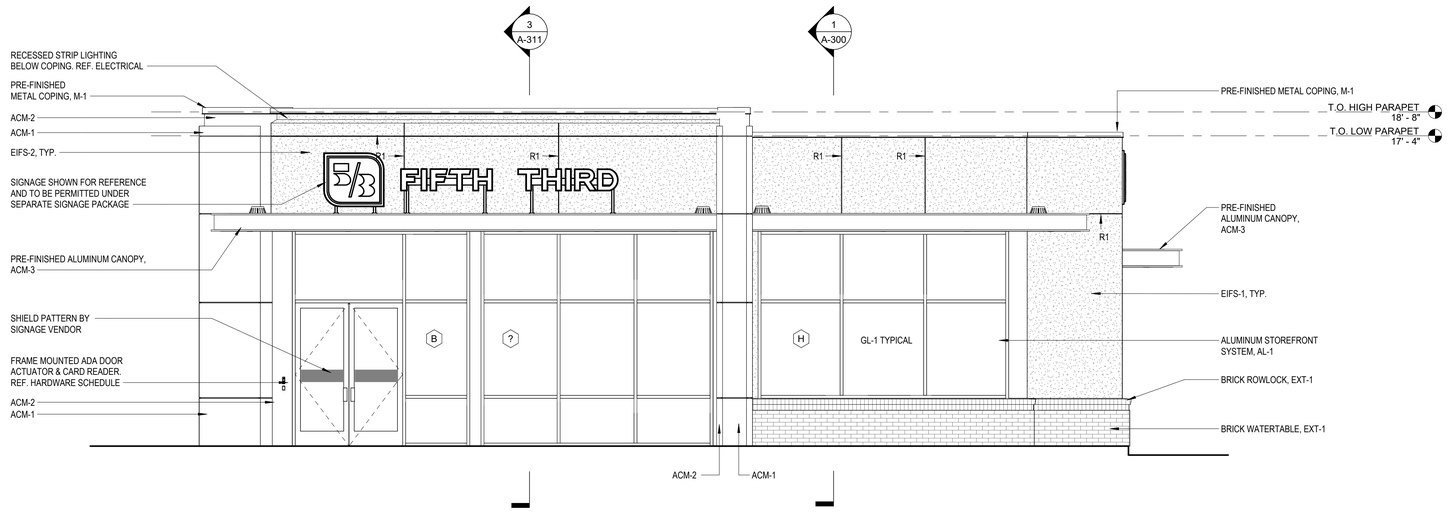

WEST ELEVATION | 1/4" = 1'-0" | 2

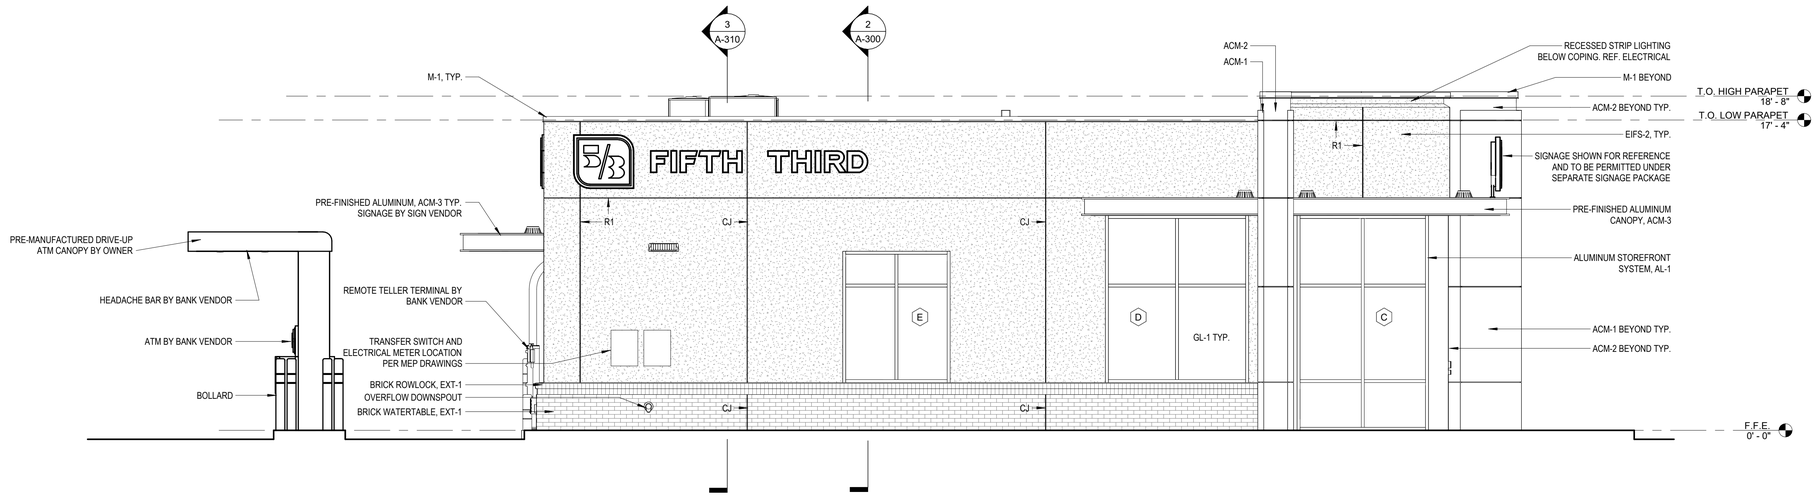

NORTH ELEVATION | 1/4" = 1'-0" | 1

PRAXIS3
100 Peachtree St NW
Suite 1450
Atlanta, GA 30303
404-875-4500 tel
www.praxis3.com

STATE OF GEORGIA
STUART M. ROMM
07/02/26
CERTIFICATE NO. 3457
REGISTERED ARCHITECT

Copyright (c) 2026 Praxis3, LLC

All reports, plans, specifications, computer files, field data, notes and other documents and instruments prepared by Praxis3 shall retain all common law, statutory and other reserved rights, including copyright thereto.

This drawing may not be reproduced in whole or in part without written permission of Praxis3. It is to be returned upon request. Scales as stated are valid on the original drawings.

Rev	Date	Comments
	07/02/2026	PERMIT SET

Client:
FIFTH THIRD BANK

Project Number: 26302
Project Name:
WATSON BLVD.

2711 WATSON BOULEVARD
WARNER ROBINS, GA 31093

Key Plan:

Sheet Title:
EXTERIOR ELEVATIONS

Sheet Number:
A-200

7/8/2026 2:38:02 PM

EXTERIOR FINISH SCHEDULE

ITEM	EXTERIOR FINISH	MANUFACTURER	COLOR	COMMENTS
ACM-1	ALUMINUM COMPOSITE METAL PANEL	ALCOA ARCHITECTURAL REYNOBOND	CUSTOM FIFTH THIRD BLUE	4MM FR CORE ALUM. COMPOSITE PANEL, DURAGLOSS 3000
ACM-2	ALUMINUM COMPOSITE METAL PANEL	ALCOA ARCHITECTURAL REYNOBOND	CUSTOM FIFTH THIRD GREEN	4MM FR CORE ALUM. COMPOSITE PANEL, DURAGLOSS 3000
ACM-3	ALUMINUM COMPOSITE METAL PANEL	ALCOA ARCHITECTURAL REYNOBOND	ANODIC CLEAR	4MM FR CORE ALUM. COMPOSITE PANEL, COLORWELD 500
AL-1	ANODIZED ALUMINUM	YKK	CLEAR ANODIZED	BASIS OF DESIGN: 2" X 4 1/2" YKK YES45 TU CENTER SET STOREFRONT
EIFS-1	EIFS BARRIER SYSTEM	DRYVIT OUTSULATION PLUS MD	DOVER SKY	3" EIFS SYSTEM - TYP., SANDBLAST FINISH
EIFS-2	EIFS BARRIER SYSTEM	DRYVIT OUTSULATION PLUS MD	DOVER SKY	5" EIFS SYSTEM @ VESTIBULE PARAPET, SANDBLAST FINISH
EPT-1	PAINTED GALVANIZED STEEL GATE	BENJAMIN MOORE	BALBOA MIST - OC27	SEMI-GLOSS @ STEEL, SATIN FINISH @ WALLS
EXT-1	STANDARD MODULAR BRICK VENEER	ACME BRICK	SLATE GRAY	MORTAR MANUFACTURER: COOSA , MORTAR COLOR: OLD LIME PUTTY
GL-1	EXTERIOR GLAZING	VITRO	SOLARBAN 90 ACUITY + ACUITY	ARGON U-0.24, SHCC=0.23
M-1	PREFINISHED METAL COPING	PAC-CLAD	MATCH ACM-3	

GLAZING - GENERAL NOTES

EXTERIOR GLAZING BASIS OF DESIGN:

REGULAR EXTERIOR STOREFRONT:
YKK YES45 TU - CENTER SET THERMALLY BROKEN STOREFRONT, 1" PANEL INFILL
2" X 4 1/2" MULLION

EXTERIOR INSULATED GLASS UNIT:
VITRO SOLARBAN 90 (2) ACUITY + ACUITY
OVERALL THICKNESS: 1 INCH
VLT: 53%
EXT. REFLECTANCE: 12%
INT. REFLECTANCE: 19%
U-VALUE (ARGON): 0.24
SHGC: 0.23
LSG: 2.30
PROVIDE SAFETY GLAZING LABELING

INTERIOR GLAZING BASIS OF DESIGN:
YKK YES45 FS - CENTER SET, 1/4" PANEL INFILL
1 3/4" X 4 1/2" MULLION

INTERIOR GLASS UNIT:
CLEAR FLOAT GLASS, FULLY TEMPERED
OVERALL THICKNESS: 6mm (1/4")
PROVIDE SAFETY GLAZING LABELING

ACM PANEL - GENERAL NOTES

A. ALL ACM PANELS MUST BE ANCHORED TO MINIMUM 16 GA METAL STUD FRAMING. REFER TO STRUCTURAL. METAL STUD FRAMING NOT BY CA SYSTEMS.

B. METAL STUDS MUST ALIGN WITH PANEL JOINTS AS REQUIRED FOR METAL COMPOSITE PANEL ATTACHMENT.

C. FIXED STUDS MAY BE USED TO SUPPORT METAL COMPOSITE PANELS (G.C. TO COORDINATE)

D. 5/8" GYP. BD SHEATHING AND/OR GLASS MAT SHEATHING WILL NOT SUPPORT METAL COMPOSITE PANEL ATTACHMENT (SHEATHING NOT BY CA SYSTEMS)


E. ALL FLATSTOCK FABRICATED FLASHING REQUIRED FOR METAL COMPOSITE PANEL DETAILS TO BE PREFINISHED ALUMINUM. COLOR TO MATCH U.N.O.

F. ALL DIMENSIONS AND QUANTITIES ARE TO BE FIELD VERIFIED PRIOR TO THE FABRICATION (RELEASE) OF ANY & ALL METAL COMPOSITE PANEL AND ASSOCIATED FLASHINGS.


G. ALL SKYWARD ACM PANEL JOINTS TO HAVE BACKER ROD AND CAULK. APPLY DOWN PAST WOOD BLOCKING, TYP.

H. USE BACKER ROD AND CAULK AT ALL VERTICAL PANEL END (JAMB) CONDITIONS AT DISSIMILAR MATERIALS (IE, STUCCO, WINDOW MULLIONS)


I. ALL SKYWARD ACM PANEL JOINTS TO HAVE BACKER ROD AND CAULK. APPLY DOWN PAST WOOD BLOCKING, TYP. USE BACKER ROD AND CAULK AT ALL VERTICAL PANEL END (JAMB) JOINT CONDITIONS AT DISSIMILAR MATERIALS (IE STUCCO, WINDOW MULLION)

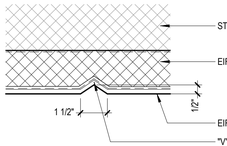


EIFS REVEAL | 3" = 1'-0" | R1

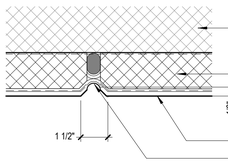


EIFS CONTROL JOINT | 3" = 1'-0" | CJ

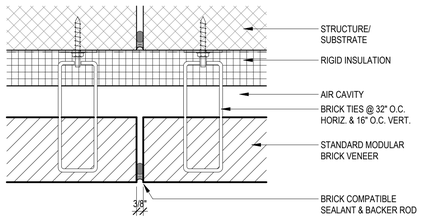

BRICK CONTROL JOINT | 3" = 1'-0" | CJ

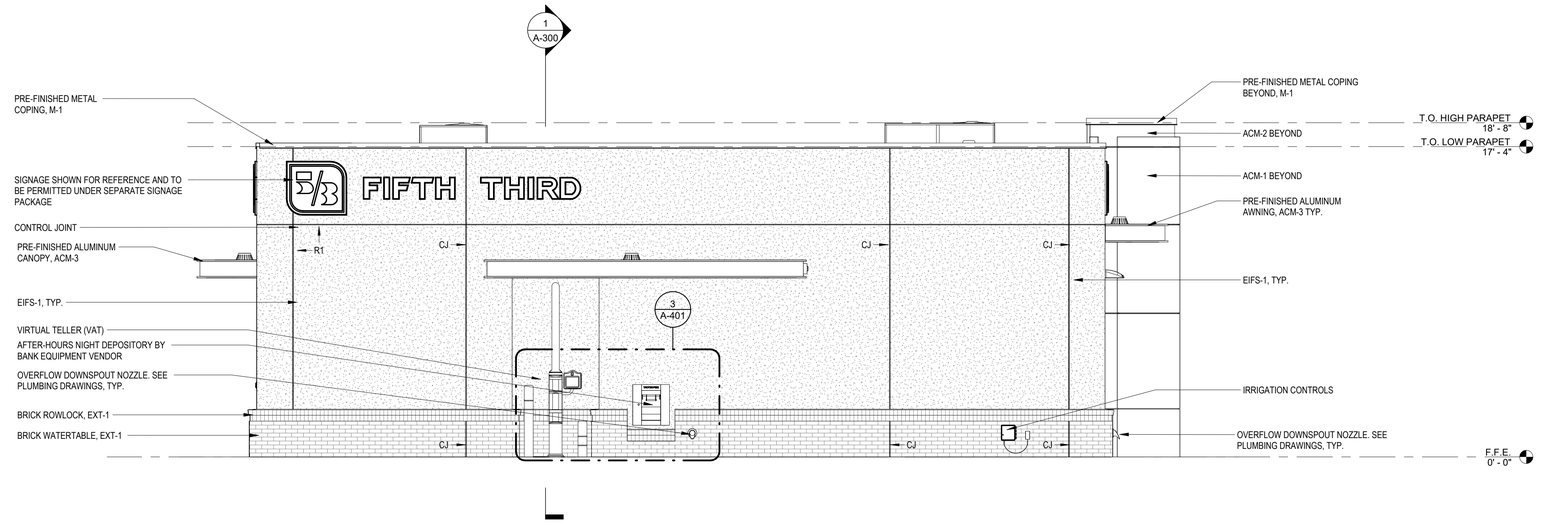

EAST ELEVATION | 1/4" = 1'-0" | 2

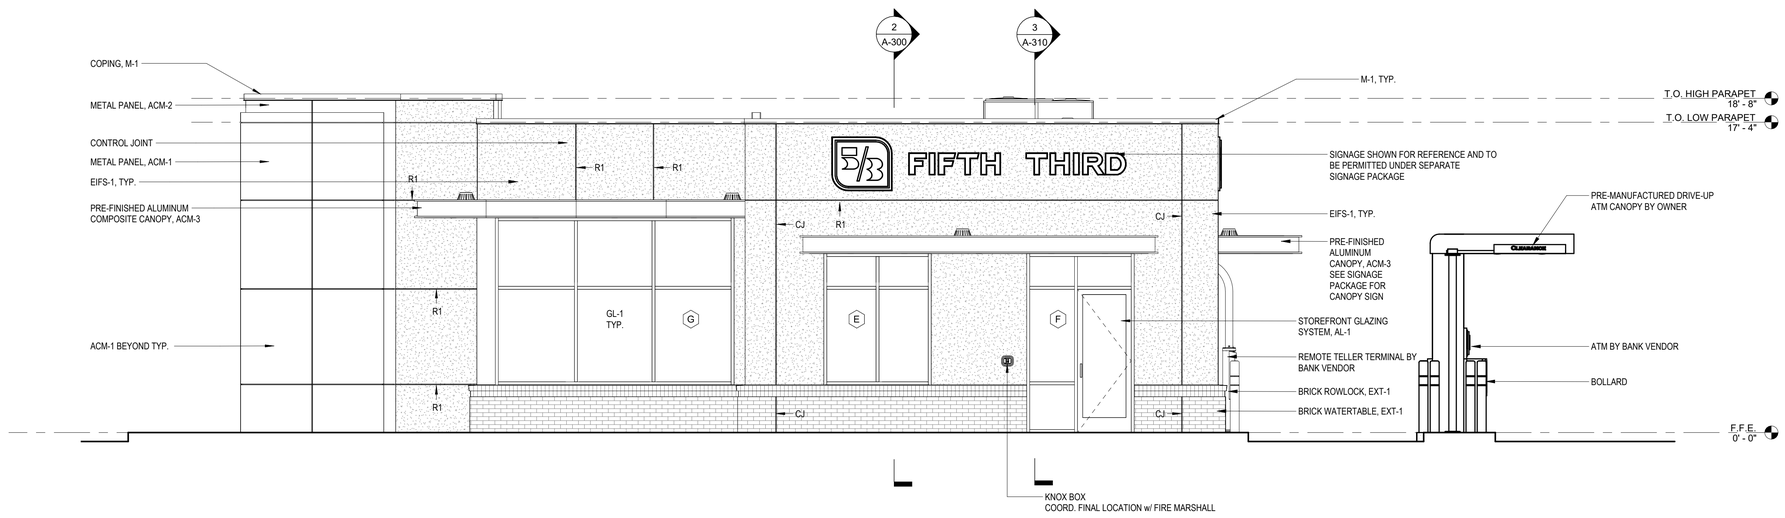

SOUTH ELEVATION | 1/4" = 1'-0" | 1

PRAXIS3
100 Peachtree St NW
Suite 1450
Atlanta, GA 30303
404-875-4500 tel
www.praxis3.com

STATE OF GEORGIA
STUART M. ROMM
07/02/26
CERTIFICATE NO. 3457
REGISTERED ARCHITECT

Copyright (c) 2026 Praxis3, LLC

All reports, plans, specifications, computer files, field data, notes and other documents and instruments prepared by Praxis3 shall retain all common law, statutory and other reserved rights, including copyright thereto.

This drawing may not be reproduced in whole or in part without written permission of Praxis3. It is to be returned upon request. Scales as stated are valid on the original drawings.

Rev	Date	Comments
	07/02/2026	PERMIT SET

Client:
FIFTH THIRD BANK

Project Number: 26302
Project Name:
WATSON BLVD.

2711 WATSON BOULEVARD
WARNER ROBINS, GA 31093

Key Plan:

Sheet Title:
EXTERIOR ELEVATIONS

Sheet Number:
A-201

7/8/2026 2:38:07 PM

SWATCHES

ACM-1

ACM-2

ACM-3
M-1
AL-1
AL-2

EIFS-1

EXT-1
EXT-2


GL-1

EXTERIOR FINISH SCHEDULE


ITEM	EXTERIOR FINISH	MANUFACTURER	COLOR	COMMENTS
ACM-1	ALUMINUM COMPOSITE METAL PANEL	ALCOA ARCHITECTURAL REYNOBOND	CUSTOM FIFTH THIRD BLUE	4MM FR CORE ALUM. COMPOSITE PANEL, DURAGLOSS 3000
ACM-2	ALUMINUM COMPOSITE METAL PANEL	ALCOA ARCHITECTURAL REYNOBOND	CUSTOM FIFTH THIRD GREEN	4MM FR CORE ALUM. COMPOSITE PANEL, DURAGLOSS 3000
ACM-3	ALUMINUM COMPOSITE METAL PANEL	ALCOA ARCHITECTURAL REYNOBOND	ANODIC CLEAR	4MM FR CORE ALUM. COMPOSITE PANEL, COLORWELD 500
AL-1	ANODIZED ALUMINUM	YKK	CLEAR ANODIZED	BASIS OF DESIGN: 2" X 4 1/2" YKK YES45 TU CENTER SET STOREFRONT
EIFS-1	EIFS BARRIER SYSTEM	DRYVIT OUTSULATION PLUS MD	DOVER SKY	3" EIFS SYSTEM - TYP., SANDBLAST FINISH
EIFS-2	EIFS BARRIER SYSTEM	DRYVIT OUTSULATION PLUS MD	DOVER SKY	5" EIFS SYSTEM @ VESTIBULE PARAPET, SANDBLAST FINISH
EPT-1	PAINTED GALVANIZED STEEL GATE	BENJAMIN MOORE	BALBOA MIST - OC27	SEMI-GLOSS @ STEEL, SATIN FINISH @ WALLS
EXT-1	STANDARD MODULAR BRICK VENEER	ACME BRICK	SLATE GRAY	MORTAR MANUFACTURER: COOSA , MORTAR COLOR: OLD LIME PUTTY
GL-1	EXTERIOR GLAZING	VITRO	SOLARBAN 90 ACUITY + ACUITY	ARGON U-0.24, SHCC=0.23
M-1	PREFINISHED METAL COPING	PAC-CLAD	MATCH ACM-3	




SOUTH ELEVATION | 3/16" = 1'-0" | 4

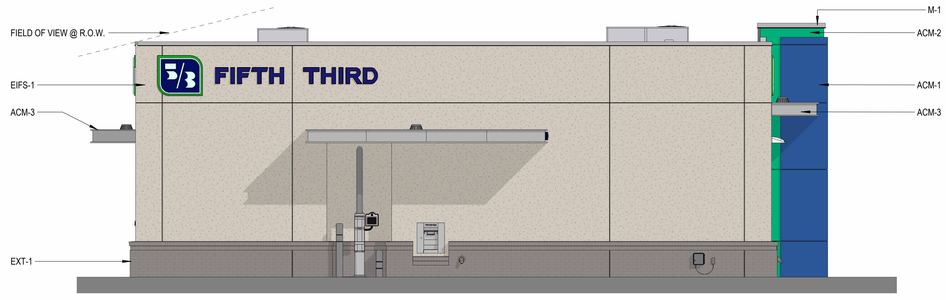

EAST ELEVATION | 3/16" = 1'-0" | 3

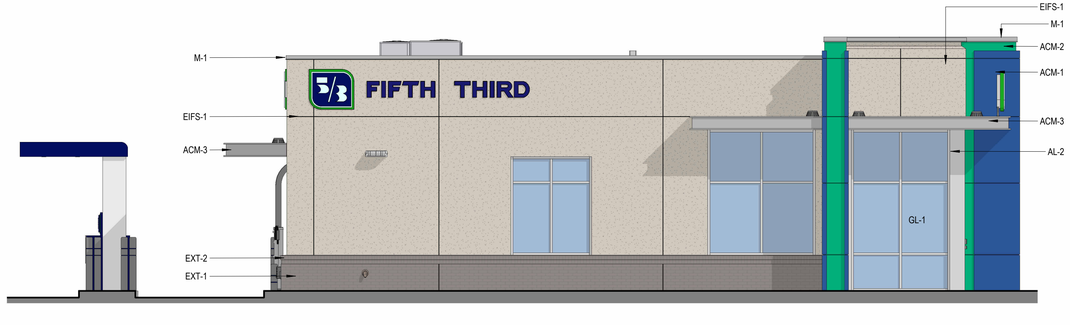

NORTH ELEVATION | 3/16" = 1'-0" | 2

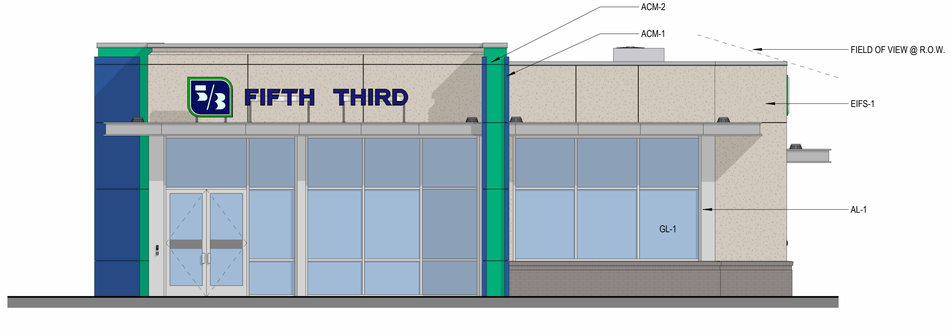

WEST ELEVATION | 3/16" = 1'-0" | 1

7/8/2026 2:38:22 PM

PRAXIS3

100 Peachtree St NW
Suite 1450
Atlanta, GA 30303

404-875-4500 tel
www.praxis3.com

STATE OF GEORGIA
STUART M. ROMM
07/02/26
CERTIFICATE NO. 34521
REGISTERED ARCHITECT

Copyright (c) 2026 Praxis3, LLC

All reports, plans, specifications, computer files, field data, notes and other documents and instruments prepared by Praxis3 shall retain all common law, statutory and other reserved rights, including copyright thereto.

This drawing may not be reproduced in whole or in part without written permission of Praxis3. It is to be returned upon request. Scales as stated are valid on the original drawings.

Rev	Date	Comments
	07/02/2026	PERMIT SET

Client:
FIFTH THIRD BANK


Project Number: 26302
Project Name:
WATSON BLVD.

2711 WATSON BOULEVARD
WARNER ROBINS, GA 31093


Key Plan:

Sheet Title:
COLOR EXTERIOR ELEVATIONS

Sheet Number:
A-202

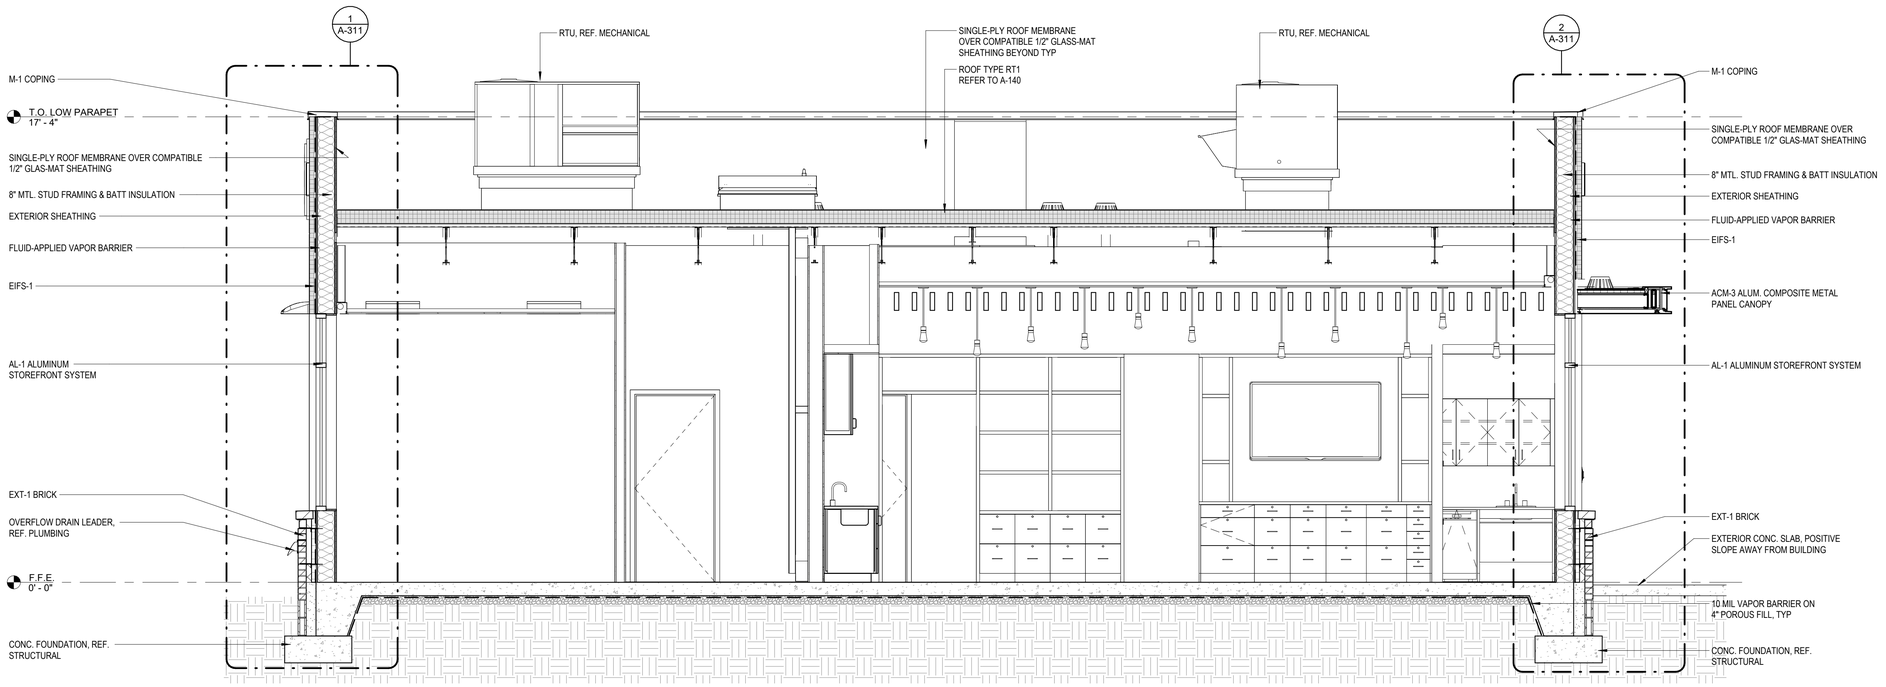

BUILDING SECTION | 3/8" = 1'-0" | 2

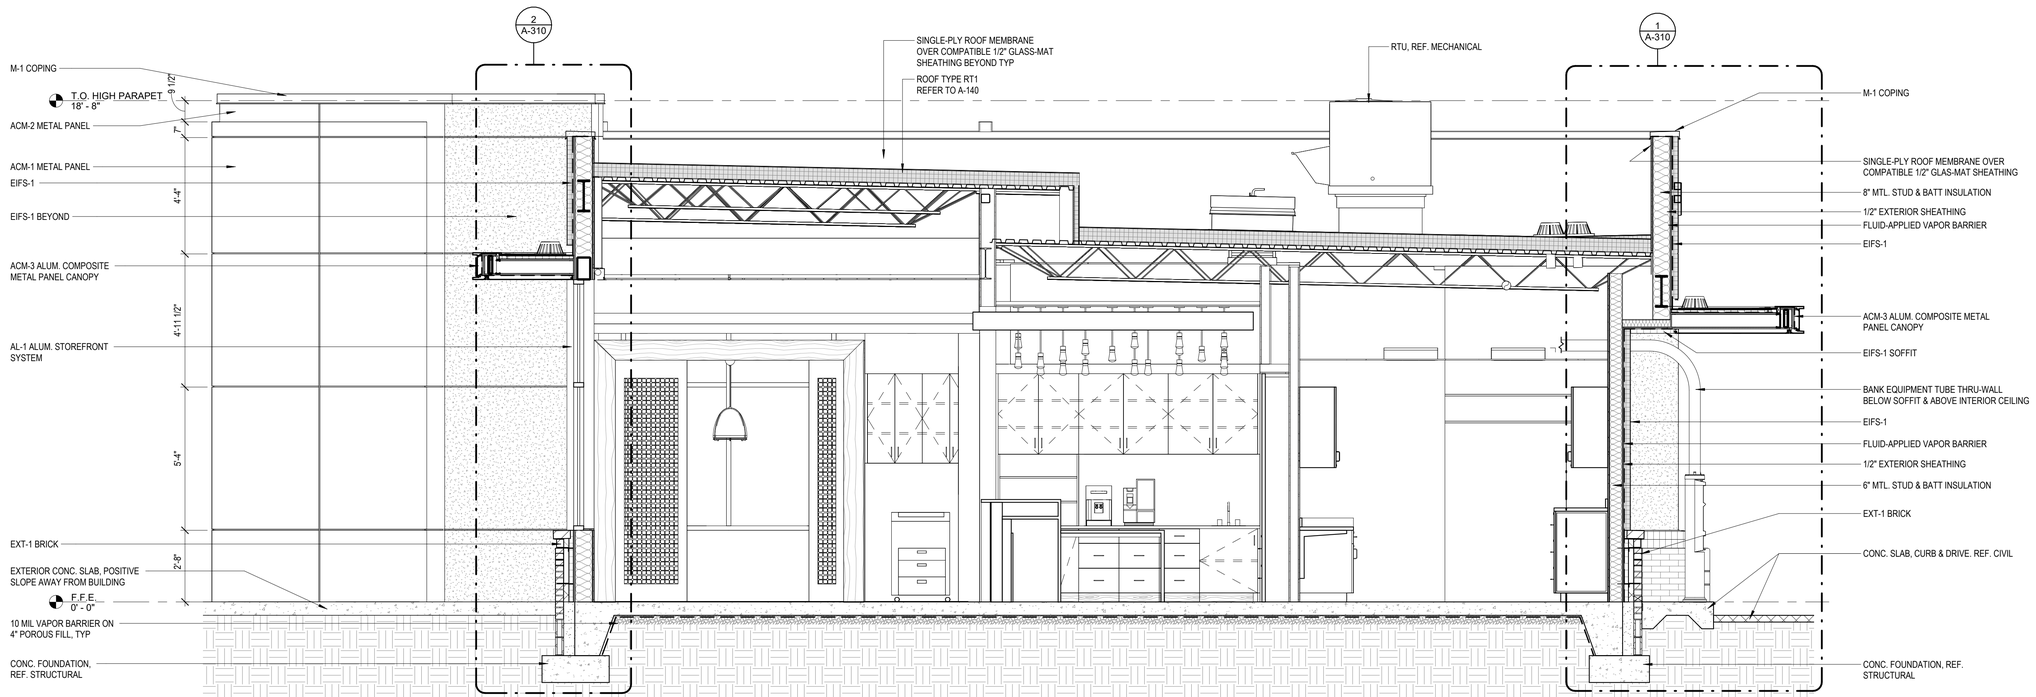

BUILDING SECTION | 3/8" = 1'-0" | 1

7/8/2026 2:38:27 PM

PRAXIS3

100 Peachtree St NW
Suite 1450
Atlanta, GA 30303
404-875-4500 tel
www.praxis3.com

STATE OF GEORGIA
STUART M. ROMM
07/02/26
CERTIFICATE NO. 3457
REGISTERED ARCHITECT

Copyright (c) 2026 Praxis3, LLC

All reports, plans, specifications, computer files, field data, notes and other documents and instruments prepared by Praxis3 shall retain all common law, statutory and other reserved rights, including copyright thereto.

This drawing may not be reproduced in whole or in part without written permission of Praxis3. It is to be returned upon request. Scales as stated are valid on the original drawings.

Rev	Date	Comments
	07/02/2026	PERMIT SET

Client:
FIFTH THIRD BANK


Project Number: 26302
Project Name:
WATSON BLVD.

2711 WATSON BOULEVARD
WARNER ROBINS, GA 31093


Key Plan:

Sheet Title:
BUILDING SECTIONS


Sheet Number:
A-300

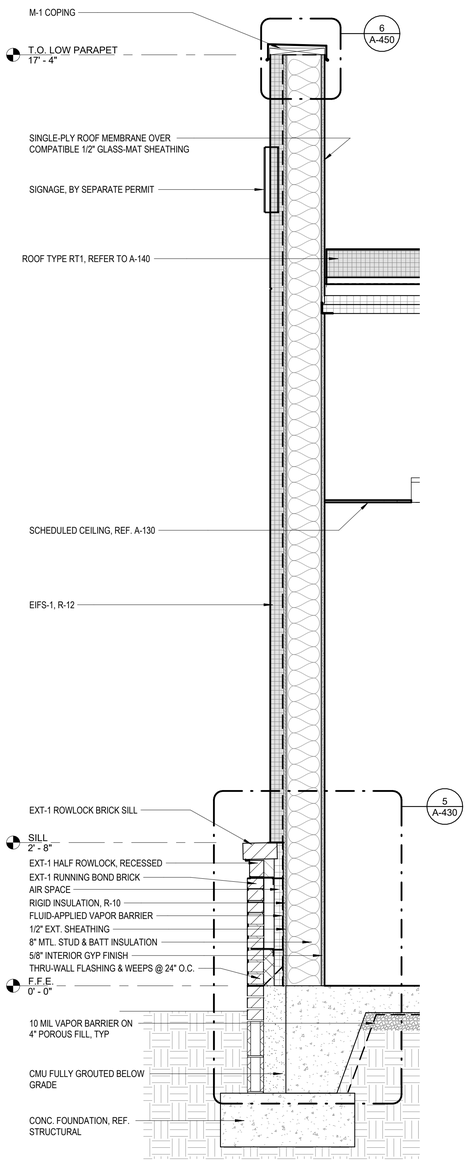

TYPICAL EXTERIOR WALL SECTION | 3/4" = 1'-0" | 3

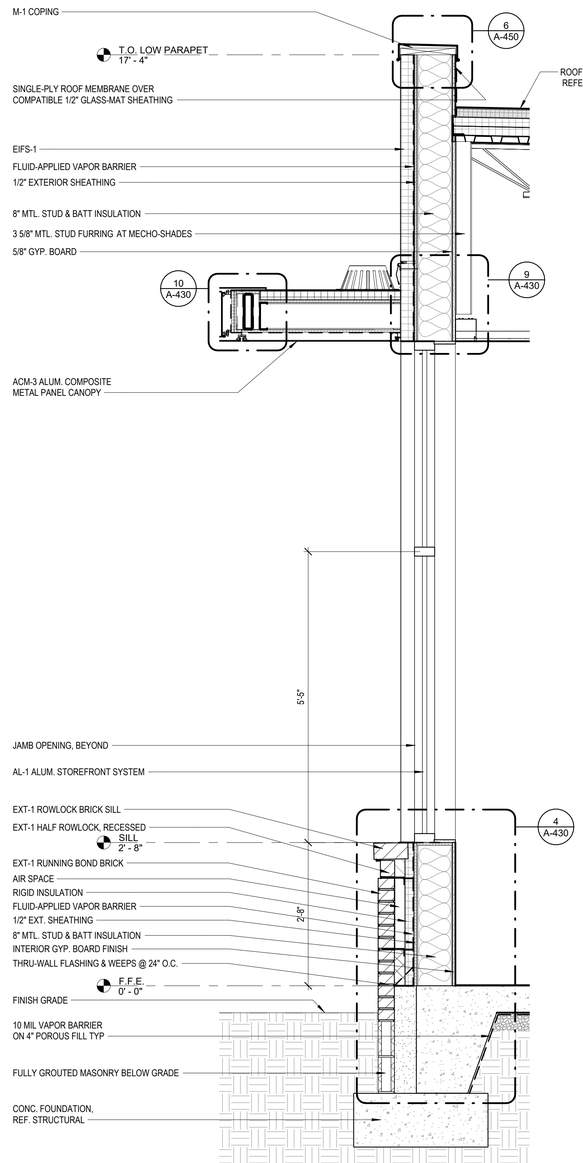

WALL SECTION AT HIGH CANOPY | 3/4" = 1'-0" | 2

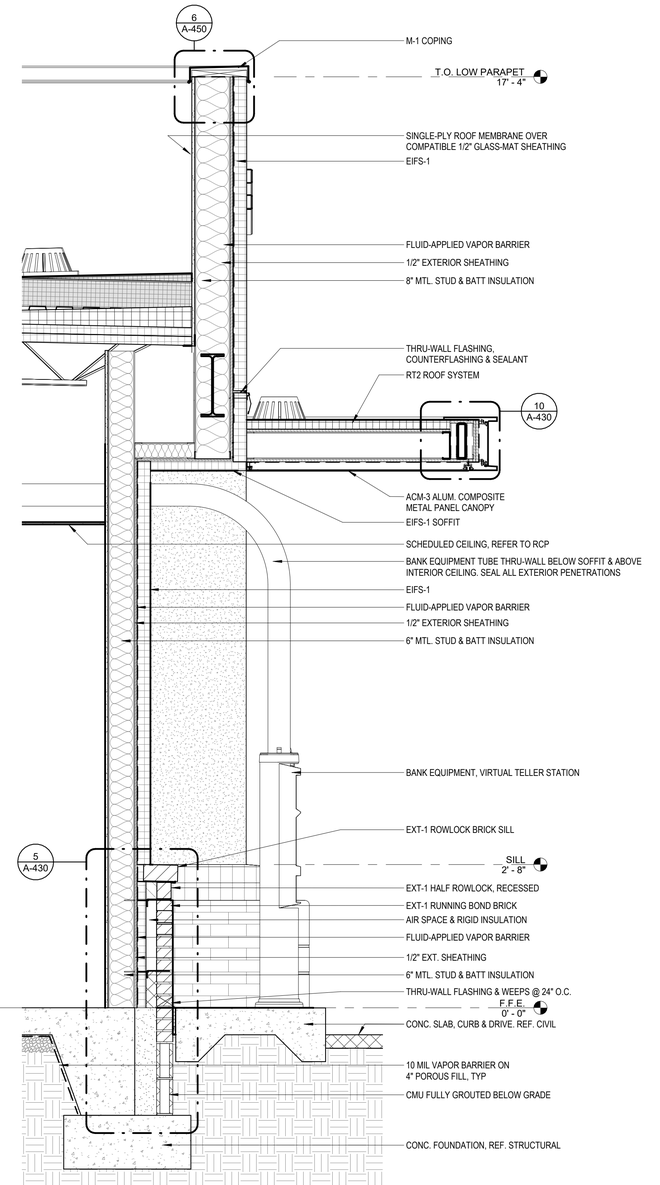

WALL SECTION @ VAT | 3/4" = 1'-0" | 1

7/8/2026 2:38:29 PM

PRAXIS3

100 Peachtree St NW
Suite 1450
Atlanta, GA 30303

404-875-4500 tel
www.praxis3.com

STATE OF GEORGIA
STUART M. ROMM
07/02/26
CERTIFICATE NO. 36511
REGISTERED ARCHITECT

Copyright (c) 2026 Praxis3, LLC

All reports, plans, specifications, computer files, field data, notes and other documents and instruments prepared by Praxis3 shall retain all common law, statutory and other reserved rights, including copyright thereto.

This drawing may not be reproduced in whole or in part without written permission of Praxis3. It is to be returned upon request. Scales as stated are valid on the original drawings.

Rev	Date	Comments
	07/02/2026	PERMIT SET

Client:

FIFTH THIRD BANK

Project Number: 26302
Project Name:

WATSON BLVD.

2711 WATSON BOULEVARD
WARNER ROBINS, GA 31093


Key Plan:

Sheet Title:


EXTERIOR WALL SECTIONS

Sheet Number:


A-310

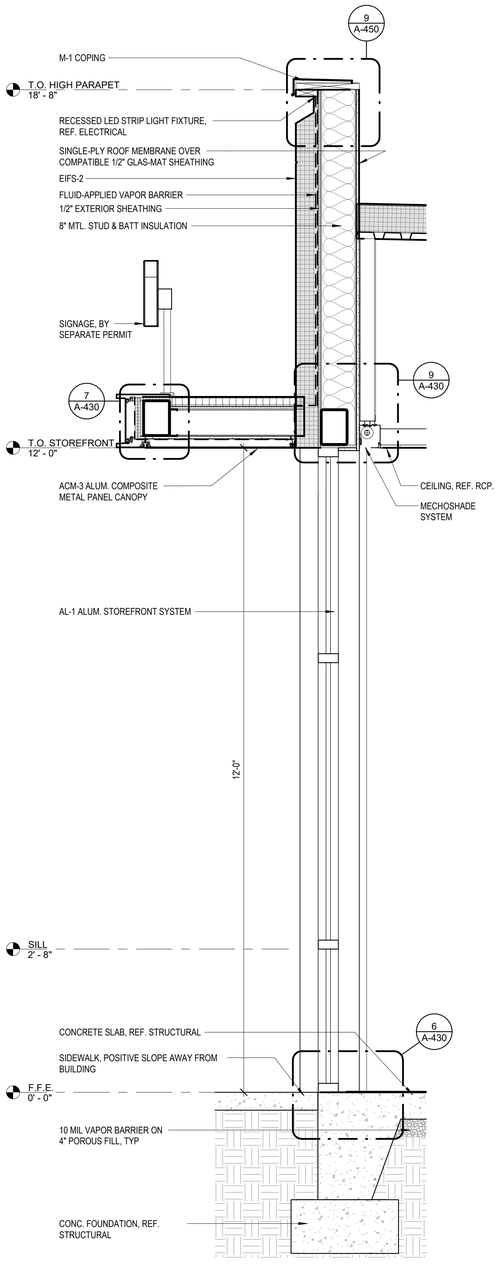

WALL SECTION AT ENTRY VESTIBULE | 3/4" = 1'-0" | 3

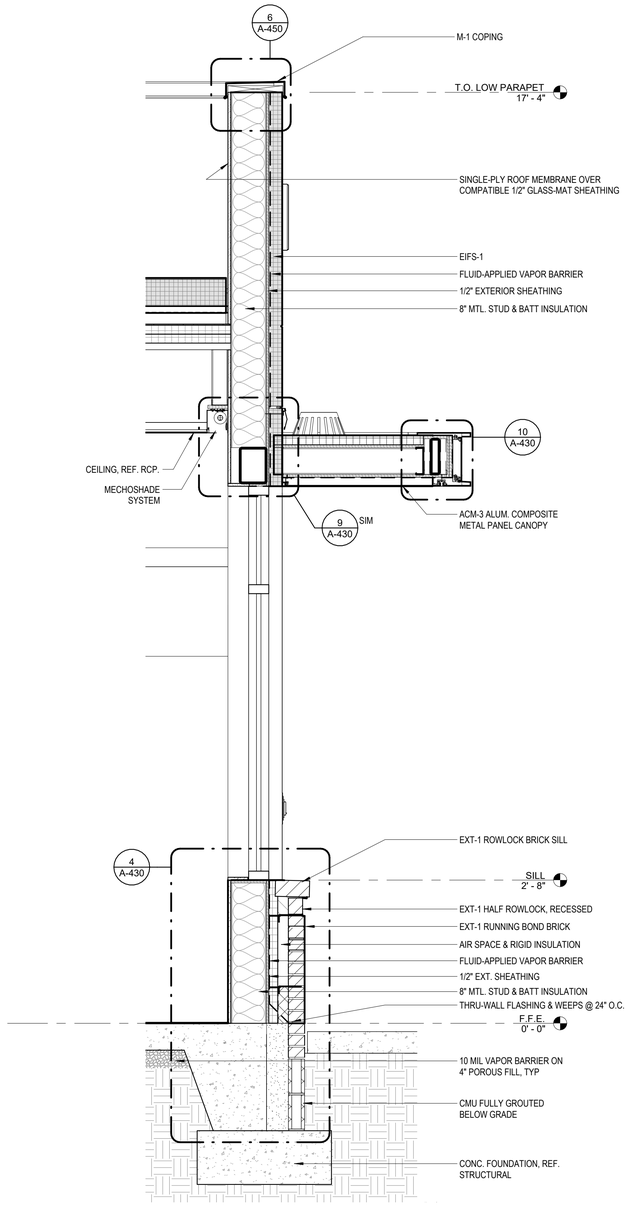

WALL SECTION AT LOW CANOPY | 3/4" = 1'-0" | 2

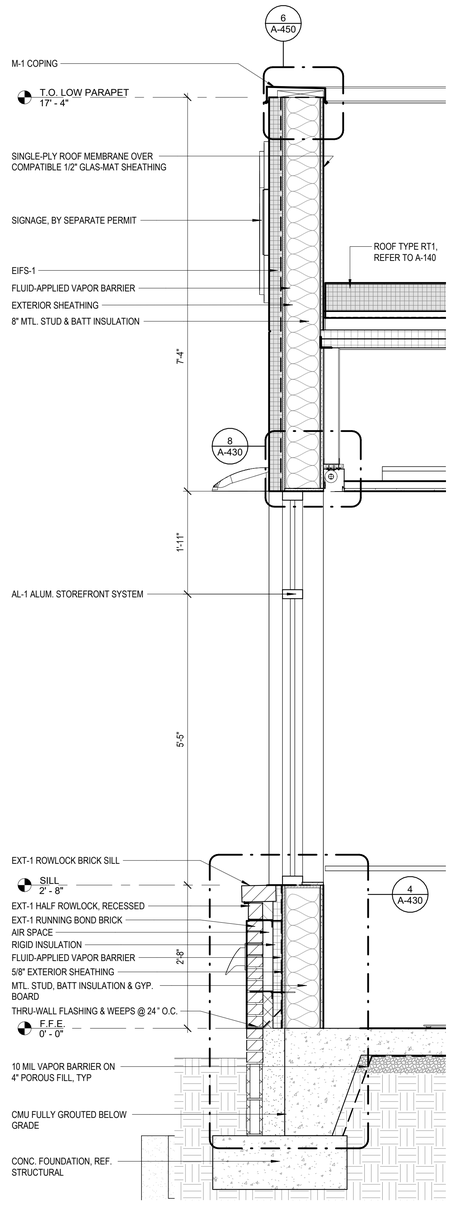

WALL SECTION AT STOREFRONT | 3/4" = 1'-0" | 1

7/8/2026 2:38:31 PM

PRAXIS3

100 Peachtree St NW
Suite 1450
Atlanta, GA 30303

404-875-4500 tel
www.praxis3.com

STATE OF GEORGIA
STUART M. ROMM
07/02/26
CERTIFICATE NO. 3457
REGISTERED ARCHITECT

Copyright (c) 2026 Praxis3, LLC

All reports, plans, specifications, computer files, field data, notes and other documents and instruments prepared by Praxis3 shall retain all common law, statutory and other reserved rights, including copyright thereto.

This drawing may not be reproduced in whole or in part without written permission of Praxis3. It is to be returned upon request. Scales as stated are valid on the original drawings.

Rev	Date	Comments
	07/02/2026	PERMIT SET

Client:
FIFTH THIRD BANK


Project Number: 26302
Project Name:
WATSON BLVD.

2711 WATSON BOULEVARD
WARNER ROBINS, GA 31093


Key Plan:

Sheet Title:
EXTERIOR WALL SECTIONS


Sheet Number:
A-311

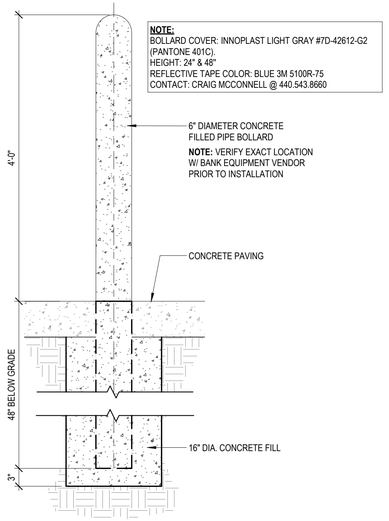


TYPICAL BOLLARD | 1" = 1'-0" | 8

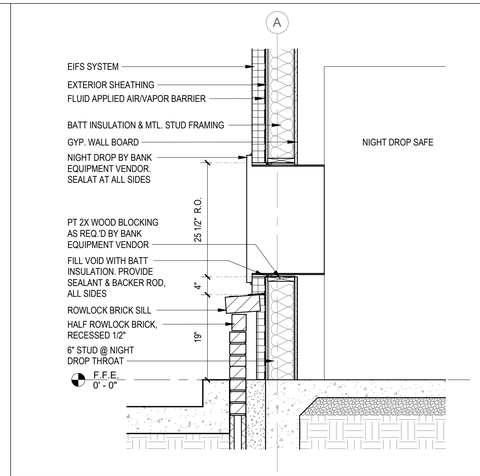


SECTION AT NIGHT DROP | 3/4" = 1'-0" | 7

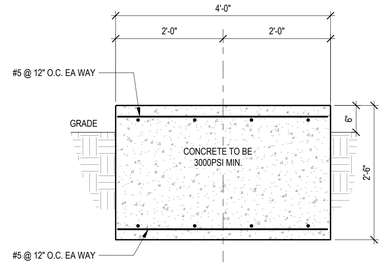


DRIVE-THRU FOUNDATION | 3/4" = 1'-0" | 6

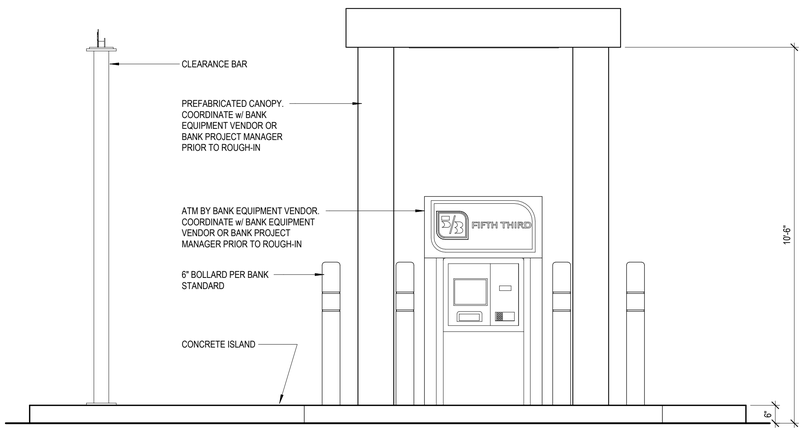


ATM FRONT ELEVATION | 1/2" = 1'-0" | 5

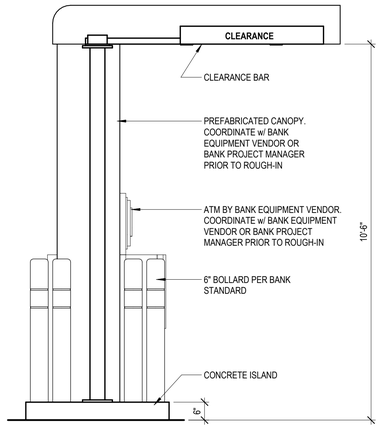

ATM SIDE ELEVATION | 1/2" = 1'-0" | 4

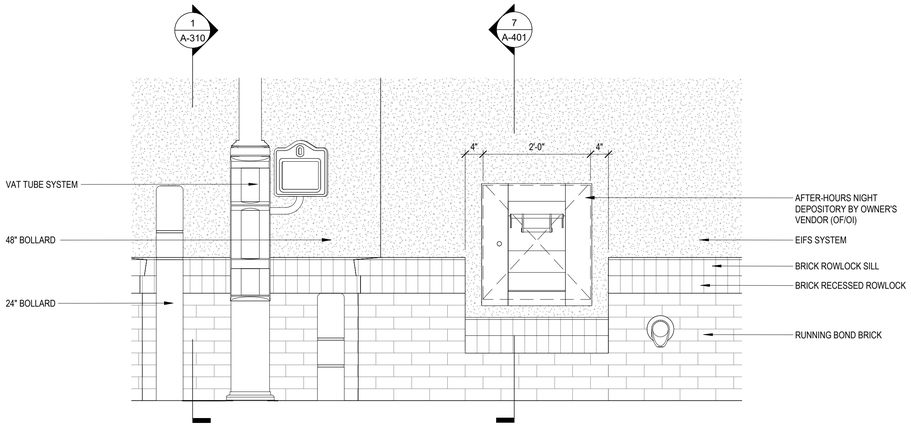

NIGHT DEPOSIT EXTERIOR ELEVATION | 3/4" = 1'-0" | 3

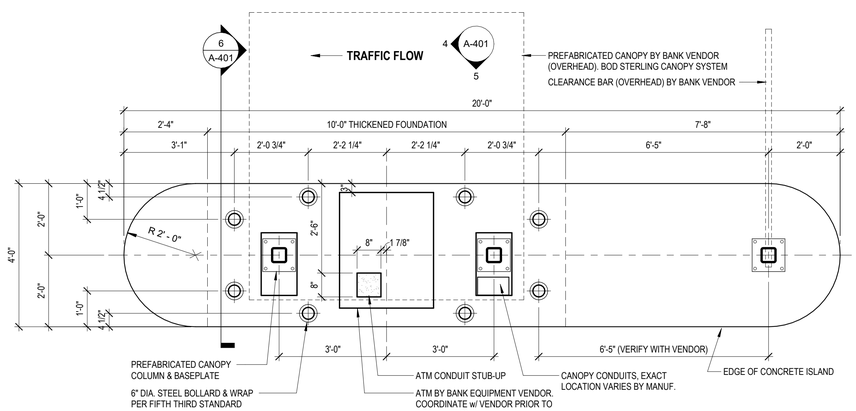


ATM CONDUIT STUB-UP REQUIREMENTS : COORDINATE FINAL LOCATION WITH MANUFACTURER AND ELECTRICAL REQUIREMENTS PRIOR TO ROUGH-IN
- PROVIDE ONE (1) 3/4" CONDUIT FOR POWER.
- ONE (1) 2" CONDUIT w/ TWO (2) PULL STRINGS FOR DATA & SECURITY CABLING.
- STUB-UP CONDUIT AT BOTTOM OF HAND HOLE WITH 120V/30 AMP FOR ATM & 120V/20 AMP FOR TOPPER.
- COIL FLEX CONDUITS IN HAND HOLE FOR FEED THRU HOLES IN BOTTOM OF ATM.
- 6" DEEP WELL OPEN TO GRAVEL FOR STUB UPS.

CANOPY STUB-UP REQUIREMENTS:
- COORDINATE PROJECT-SPECIFIC CANOPY MANUFACTURER STUB-UP LOCATION WITH CBRE PRIOR TO ROUGH-IN
- PROVIDE 3/4" CONDUIT FOR POWER,
- 3/4" CONDUIT w/ ONE (1) PULL STRING FOR SECURITY CABLING

BOLLARD PLACEMENT DRAWN FOR REFERENCE. GC TO COORDINATE W/ ATM GROUP & OWNER'S VENDOR FOR ATM & VAT BOLLARD LOCATION

ENLARGED DRIVE-THRU ISLAND | 1/2" = 1'-0" | 2

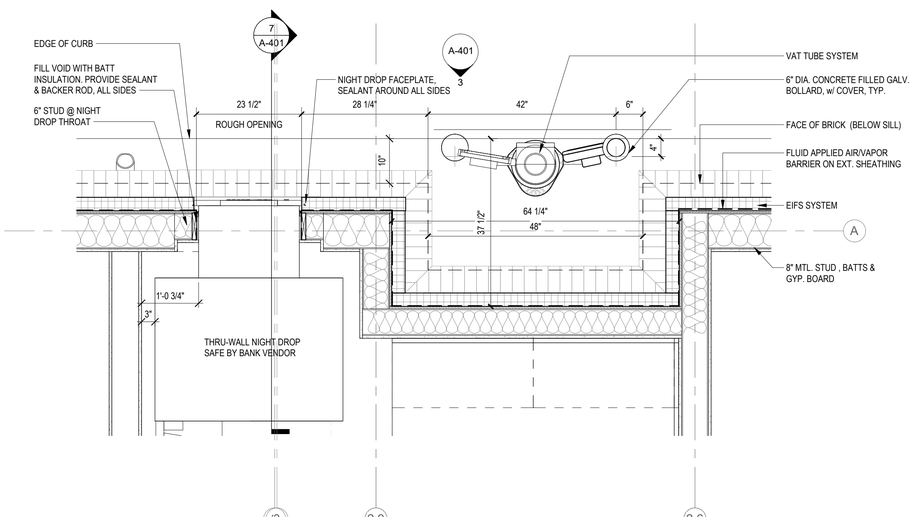

ENLARGED PLAN @ VAT NICHE | 3/4" = 1'-0" | 1

PRAXIS3
100 Peachtree St NW
Suite 1450
Atlanta, GA 30303
404-875-4500 tel
www.praxis3.com

STATE OF GEORGIA
STUART M. ROMM
07/02/26
CERTIFICATE NO. 3457
REGISTERED ARCHITECT

Copyright (c) 2026 Praxis3, LLC

All reports, plans, specifications, computer files, field data, notes and other documents and instruments prepared by Praxis3 shall retain all common law, statutory and other reserved rights, including copyright thereto.

This drawing may not be reproduced in whole or in part without written permission of Praxis3. It is to be returned upon request. Scales as stated are valid on the original drawings.

Rev	Date	Comments
	07/02/2026	PERMIT SET

Client:
FIFTH THIRD BANK

Project Number: 26302
Project Name:
WATSON BLVD.

2711 WATSON BOULEVARD
WARNER ROBINS, GA 31093

Key Plan:

Sheet Title:
BANK EQUIPMENT PLANS & DETAILS

Sheet Number:
A-401

7/8/2026 2:38:33 PM

Composite Chest:
-70H X 42W X 32D
-Left Swing
-TL-30

Color:
-Black

Lock(s):
-1: Prep for and Install Dealer Supplied LaGard 39E

Alarm Options:
-Alarm Holes
- Timelock
  - 3 Movement - 144 HR UL Listed
- Heat Sensor and Door Contact
- Seismic Detector

Safe Options:
- DoorStop
  - Internal Hinge Stop
- Anchor Holes
  - 2 In the Front


Depository Head:
- Oakley UL Listed Night Depository Head
- Secure Housing (Bolt On)
- 24 Additional Head Keys
- Electronic Fire Chute Closure Device
- Chute Closure Retainer Kit (HS-SCD-CCR)
- Covert Camera Kit

Est. Weight of Unit: 4404 LBS

**LaGard 39E lock(s) warranty is the customer's responsibility

**Tech support of the LaGard 39E lock(s) is the customer's responsibility

**Installation of the LaGard 39E lock(s) does not void the warranty
on the safe or locker

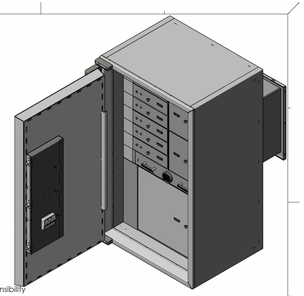

REV.	DESCRIPTION	DATE	APPROVED
A	Corrected Camera Kit	9/25/2020	AH
B	Replaced LaGards with HamiltonPIN. Locks	5/4/2021	TD
C	Added chute closure retainer kit	9/12/2022	AH
D	Changed to Oakley head	9/12/2023	AH

HAMILTON
A FERGUSON WILLIAMS FAMILY BRAND

PROPRIETARY AND CONFIDENTIAL
THIS DRAWING AND THE INFORMATION CONTAINED HEREIN IS THE PROPERTY OF HAMILTON SAFE CO. AND SHALL NOT BE REPRODUCED OR COPIED OR USED AS THE BASIS FOR THE MANUFACTURE OR SALE OF APPARATUS WITHOUT PERMISSION.

CUSTOMER:
DRAWN BY: Premier
SCALE: 1/2"=1'-0"
DESIGN BY: Katie Morris
P.O. NUMBER:
QUOTE NUMBER: 20-1325
ORDER ENTRY NUMBER: 52370588

9 - Decorative Number Plate(s)

9 - Chrome Pull Knob(s)


1 - B5709 Currency Drawer(s)

6 - Single Nose Lock(s)
-1A 2A 3A 4A 5A 6A

4 - Prep for and Install Dealer Supplied LaGard 39E
-7A 1B 2B 8L

1 - Adjustable Shelf in 1B
1 - Adjustable Shelf in 2B

If Utilizing Adjustable Shelves Weight Limit Should Not Exceed 60LBS

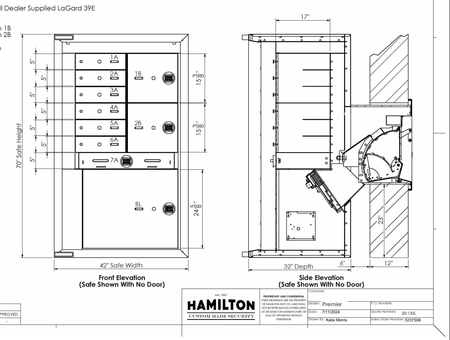

Front Elevation
(Safe Shown With No Door)


Side Elevation
(Safe Shown With No Door)

REV.	DESCRIPTION	DATE	APPROVED
-	See Cover Sheet	-	-

HAMILTON
A FERGUSON WILLIAMS FAMILY BRAND

PROPRIETARY AND CONFIDENTIAL
THIS DRAWING AND THE INFORMATION CONTAINED HEREIN IS THE PROPERTY OF HAMILTON SAFE CO. AND SHALL NOT BE REPRODUCED OR COPIED OR USED AS THE BASIS FOR THE MANUFACTURE OR SALE OF APPARATUS WITHOUT PERMISSION.

CUSTOMER:
DRAWN BY: Premier
SCALE: 1/2"=1'-0"
DESIGN BY: Katie Morris
P.O. NUMBER:
QUOTE NUMBER: 20-1325
ORDER ENTRY NUMBER: 52370588

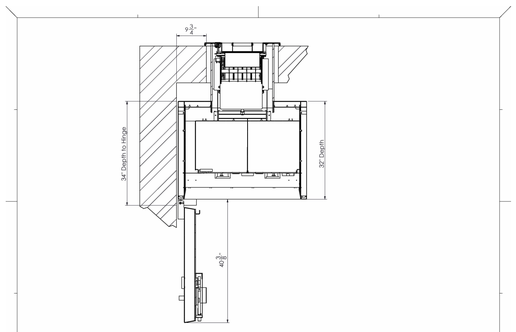

Plan View

Note:
- If safe is placed against the wall on the hinge side space safe 1/2" off the wall for clearance

REV.	DESCRIPTION	DATE	APPROVED
-	See Cover Sheet	-	-

HAMILTON
A FERGUSON WILLIAMS FAMILY BRAND

PROPRIETARY AND CONFIDENTIAL
THIS DRAWING AND THE INFORMATION CONTAINED HEREIN IS THE PROPERTY OF HAMILTON SAFE CO. AND SHALL NOT BE REPRODUCED OR COPIED OR USED AS THE BASIS FOR THE MANUFACTURE OR SALE OF APPARATUS WITHOUT PERMISSION.

CUSTOMER:
DRAWN BY: Premier
SCALE: 1/2"=1'-0"
DESIGN BY: Katie Morris
P.O. NUMBER:
QUOTE NUMBER: 20-1325
ORDER ENTRY NUMBER: 52370588


Exterior Elevation

REV.	DESCRIPTION	DATE	APPROVED
-	See Cover Sheet	-	-

HAMILTON
A FERGUSON WILLIAMS FAMILY BRAND

PROPRIETARY AND CONFIDENTIAL
THIS DRAWING AND THE INFORMATION CONTAINED HEREIN IS THE PROPERTY OF HAMILTON SAFE CO. AND SHALL NOT BE REPRODUCED OR COPIED OR USED AS THE BASIS FOR THE MANUFACTURE OR SALE OF APPARATUS WITHOUT PERMISSION.


CUSTOMER:
DRAWN BY: Premier
SCALE: 1/2"=1'-0"
DESIGN BY: Katie Morris
P.O. NUMBER:
QUOTE NUMBER: 20-1325
ORDER ENTRY NUMBER: 52370588

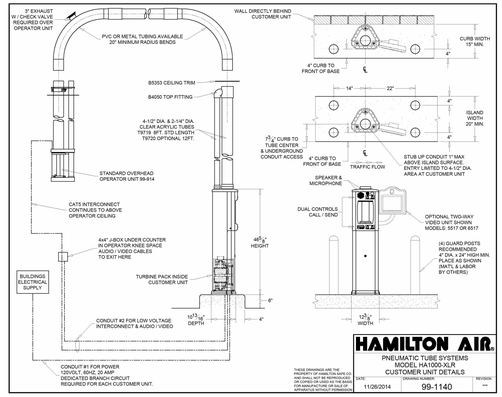

HAMILTON AIR.
PNEUMATIC TUBE SYSTEMS
MODEL HA1000-XLR
CUSTOMER UNIT DETAILS

DATE	DRAWING NUMBER	REVISION
11/26/2014	99-1140	--


THESE DRAWINGS ARE THE PROPRIETARY PROPERTY OF HAMILTON CO. AND SHALL NOT BE REPRODUCED OR COPIED OR USED AS THE BASIS FOR THE MANUFACTURE OR SALE OF APPARATUS WITHOUT PERMISSION.

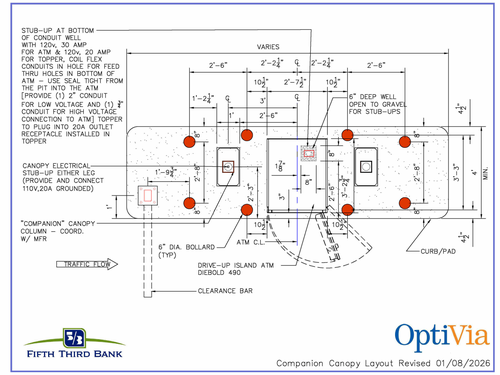

FIFTH THIRD BANK

OptiVia

Companion Canopy Layout Revised 01/08/2026

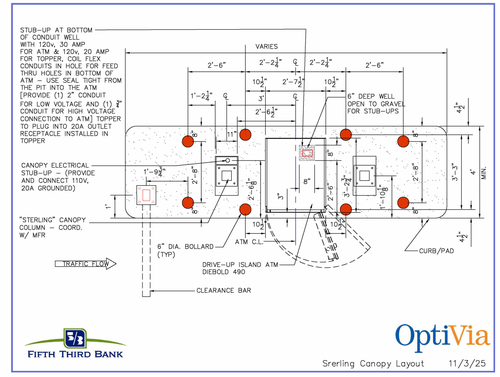

FIFTH THIRD BANK

OptiVia

Srerling Canopy Layout 11/3/25

7/8/2026 2:38:35 PM

PRAXIS3

100 Peachtree St NW
Suite 1450
Atlanta, GA 30303

404-875-4500 tel
www.praxis3.com

STATE OF GEORGIA
STUART M. ROMM
07/02/26
CERTIFICATE NO. 36511
REGISTERED ARCHITECT

Copyright (c) 2026 Praxis3, LLC

All reports, plans, specifications, computer files, field data, notes and other documents and instruments prepared by Praxis3 shall retain all common law, statutory and other reserved rights, including copyright thereto.

This drawing may not be reproduced in whole or in part without written permission of Praxis3. It is to be returned upon request. Scales as stated are valid on the original drawings.

Rev	Date	Comments
	07/02/2026	PERMIT SET

Client:
FIFTH THIRD BANK


Project Number: 26302
Project Name:
WATSON BLVD.

2711 WATSON BOULEVARD
WARNER ROBINS, GA 31093

Key Plan:


Sheet Title:
BANK EQUIPMENT CUT SHEETS

Sheet Number:
A-402

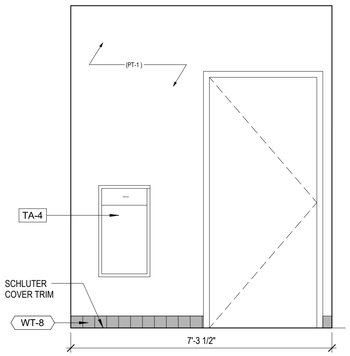


SEE 1/A-410 FOR TYPICAL MOUNTING HEIGHTS FOR TOILET ACCESSORIES

RESTROOM ELEVATION - A | 1/2" = 1'-0" | 10

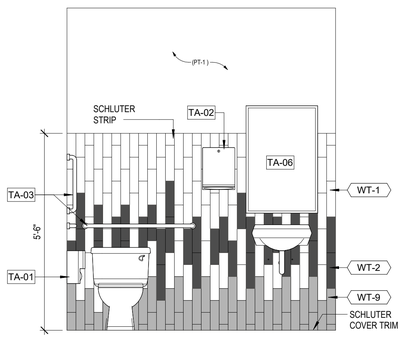


SEE 1/A-410 FOR TYPICAL MOUNTING HEIGHTS FOR TOILET ACCESSORIES

RESTROOM ELEVATION - B | 1/2" = 1'-0" | 9

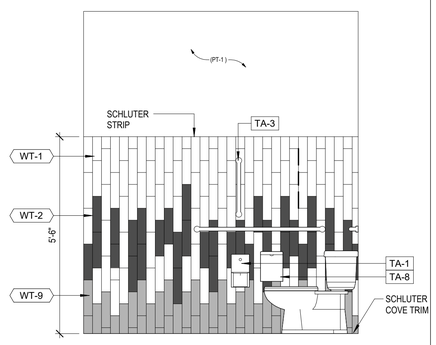

SEE 1/A-410 FOR TYPICAL MOUNTING HEIGHTS FOR TOILET ACCESSORIES

RESTROOM ELEVATION - C | 1/2" = 1'-0" | 8

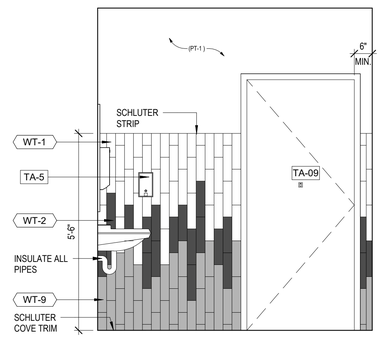

SEE 1/A-410 FOR TYPICAL MOUNTING HEIGHTS FOR TOILET ACCESSORIES


RESTROOM ELEVATION - D | 1/2" = 1'-0" | 7

TOILET ACCESSORY SCHEDULE


ITEM NO	DESCRIPTION	MODEL
TA-01	TOILET TISSUE DISPENSER	OWNER VENDOR PROVIDED, GC TO INSTALL, GC TO ORDER
TA-02	PAPER TOWEL DISPENSER	OWNER VENDOR PROVIDED, GC TO INSTALL, GC TO ORDER
TA-03	GRAB BARS	BRADLEY 1-1/4" STAINLESS STEEL GRAB BAR W/ CONCEALED MOUNTING
TA-04	WASTE RECEPTACLE	BOBRICK B-3644 RECESSED WASTE RECEPTACLE (FOR 4" WALLS)
TA-05	SOAP DISPENSER	OWNER VENDOR PROVIDED, GC TO INSTALL, GC TO ORDER
TA-06	MIRROR	BOBRICK B-290 GLASS MIRROR WITH STAINLESS STEEL ANGLE FRAME
TA-08	SANITARY NAPKIN DISPOSAL	BOBRICK B-270 SURFACE MOUNTED SANITARY NAPKIN DISPOSAL
TA-09	COAT HOOK	REFERENCE DOOR HW SCHEDULE
TA-10	SURFACE MOUNTED MOP HOLDER	BOBRICK B-223 x 24, SATIN FINISH

GC: SCAN QR CODE FOR LINK TO ORDER TOILET ACCESSORIES
"BY OWNER VENDOR, GC INSTALL"
https://app.smartsheet.com/b/form/d7330a3854794f519c389721265979be


NOTE:
MENS INTERIOR ELEVATIONS ARE SIMILAR TO WOMENS INTERIOR ELEVATIONS

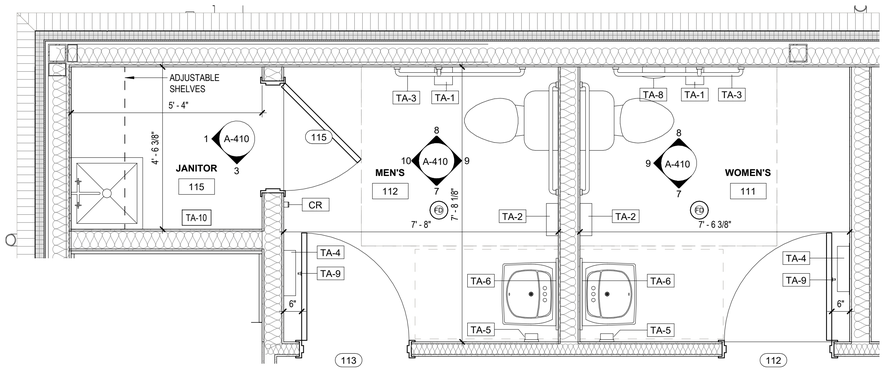

ENLARGED RESTROOM PLAN | 1/2" = 1'-0" | 6

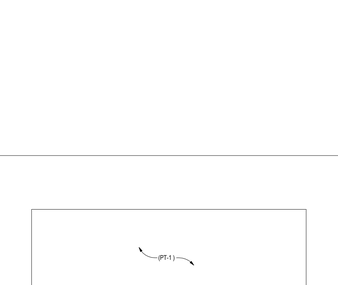


ACCESSIBLE - LAV | 1/2" = 1'-0" | 5

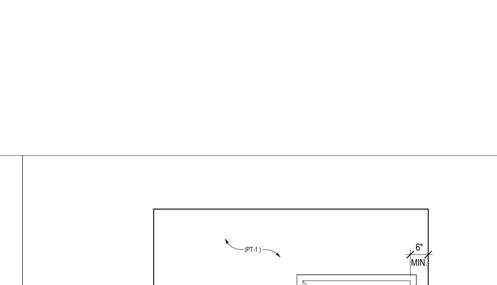


ACCESSIBLE - DRINKING FOUNTAINS | 1/2" = 1'-0" | 4




JANITOR CLOSET ELEVATION | 1/2" = 1'-0" | 3

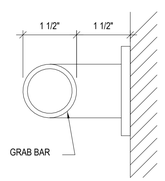


PROVIDE FASTENERS AND WALL REINFORCEMENT TO SUPPORT A 250# MIN. POINT LOAD.

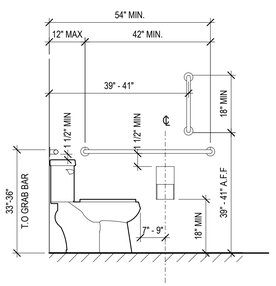


ACCESSIBLE WATER CLOSET

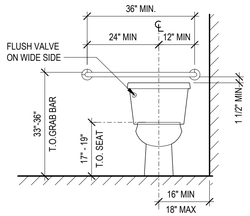


ACCESSIBLE WATER CLOSET

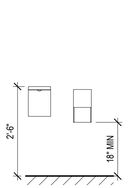


SANITARY NAPKIN RECEPTACLE
TOILET PAPER DISPENSER

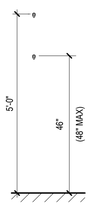

COAT HOOK

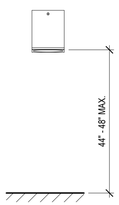


PAPER TOWEL DISPENSER

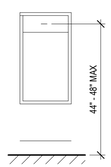

PAPER TOWEL DISPENSER & WASTE RECEPTACLE




SOAP DISPENSER

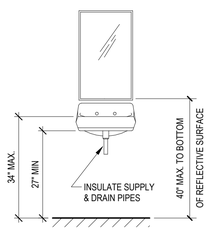

WALL-MOUNTED LAVATORY

TYPICAL ACCESSIBLE ACCESSORY HEIGHTS | 1/2" = 1'-0" | 2

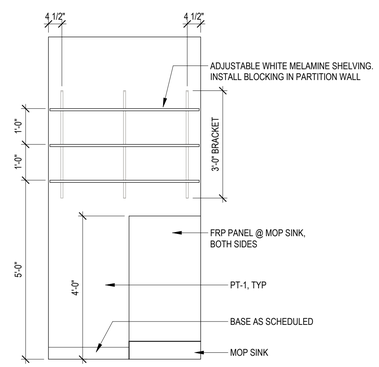

JANITOR CLOSET ELEVATION | 1/2" = 1'-0" | 1

7/8/2026 2:38:37 PM

PRAXIS3

100 Peachtree St NW
Suite 1450
Atlanta, GA 30303
404-875-4500 tel
www.praxis3.com

STATE OF GEORGIA
STUART M. ROMM
07/02/26
CERTIFICATE NO. 34511
REGISTERED ARCHITECT

Copyright (c) 2026 Praxis3, LLC

All reports, plans, specifications, computer files, field data, notes and other documents and instruments prepared by Praxis3 shall retain all common law, statutory and other reserved rights, including copyright thereto.

This drawing may not be reproduced in whole or in part without written permission of Praxis3. It is to be returned upon request. Scales as stated are valid on the original drawings.

Rev	Date	Comments
	07/02/2026	PERMIT SET

Client:
FIFTH THIRD BANK


Project Number: 26302
Project Name:
WATSON BLVD.

2711 WATSON BOULEVARD
WARNER ROBINS, GA 31093


Key Plan:

Sheet Title:
ENLARGED RESTROOM PLANS & ELEVATIONS


Sheet Number:
A-410

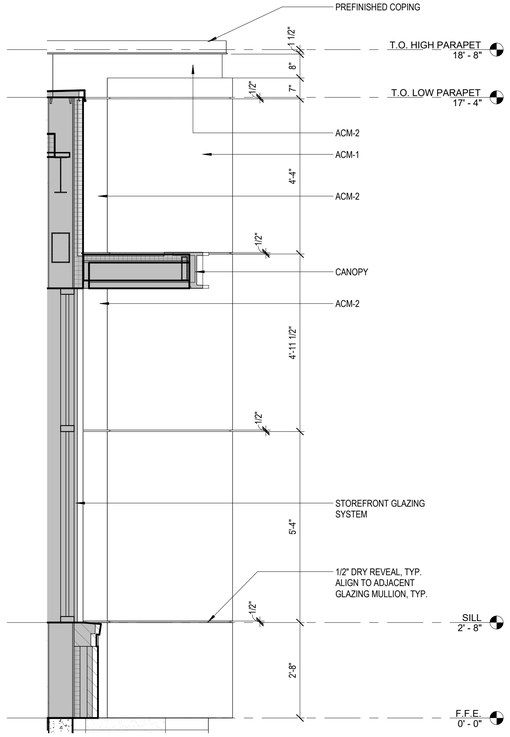


WING WALL ELEVATION | 1/2" = 1'-0" | 6

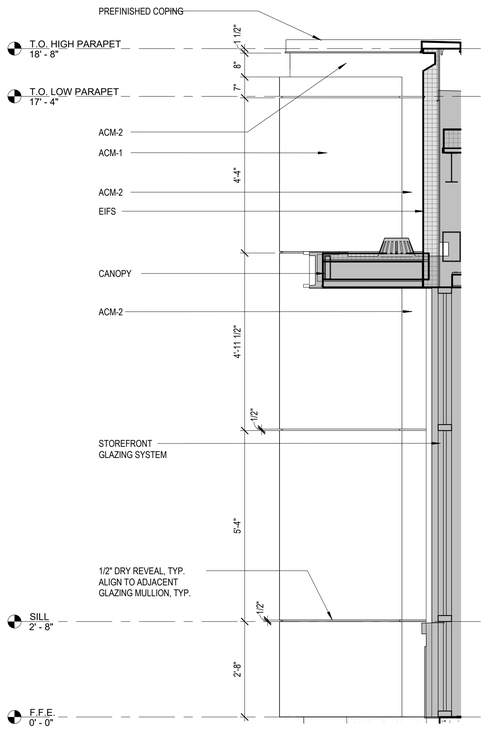


WING WALL ELEVATION | 1/2" = 1'-0" | 5

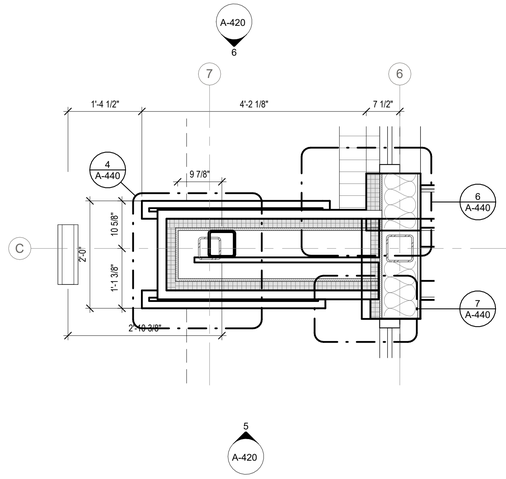


WING WALL ENLARGED PLAN | 3/4" = 1'-0" | 2

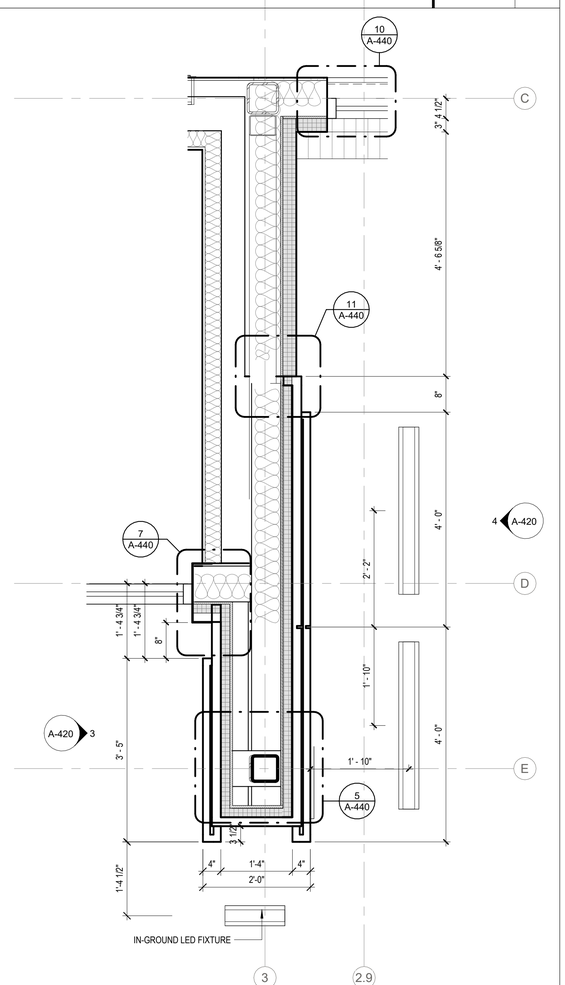

WING WALL ENLARGED PLAN | 3/4" = 1'-0" | 1

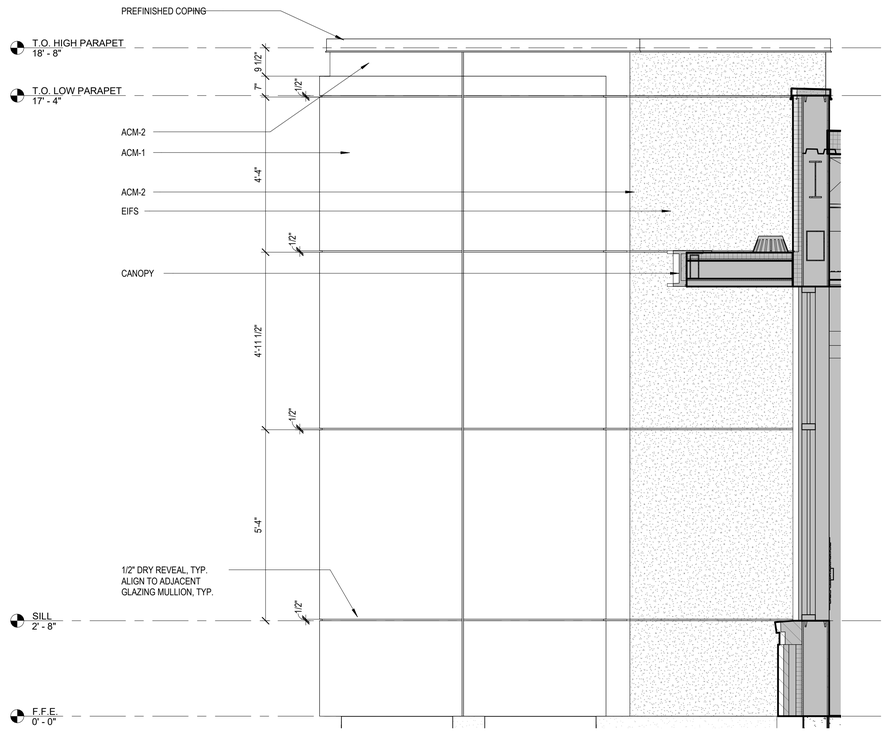

WING WALL ELEVATION | 1/2" = 1'-0" | 4

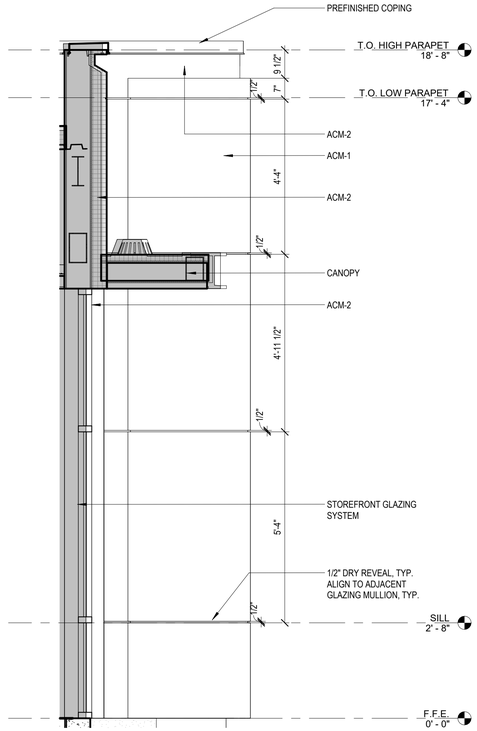

WING WALL ELEVATION | 1/2" = 1'-0" | 3

PRAXIS3

100 Peachtree St NW
Suite 1450
Atlanta, GA 30303

404-875-4500 tel
www.praxis3.com

STATE OF GEORGIA
STUART M. ROMM
07/02/26
CERTIFICATE NO. 34511
REGISTERED ARCHITECT

Copyright (c) 2026 Praxis3, LLC

All reports, plans, specifications, computer files, field data, notes and other documents and instruments prepared by Praxis3 shall retain all common law, statutory and other reserved rights, including copyright thereto.

This drawing may not be reproduced in whole or in part without written permission of Praxis3. It is to be returned upon request. Scales as stated are valid on the original drawings.

Rev	Date	Comments
	07/02/2026	PERMIT SET

Client:
FIFTH THIRD BANK

Project Number: 26302
Project Name:
WATSON BLVD.


2711 WATSON BOULEVARD
WARNER ROBINS, GA 31093

Key Plan:


Sheet Title:
ENLARGED WING WALL PLANS & ELEVATIONS

Sheet Number:
A-420


7/8/2026 2:38:39 PM

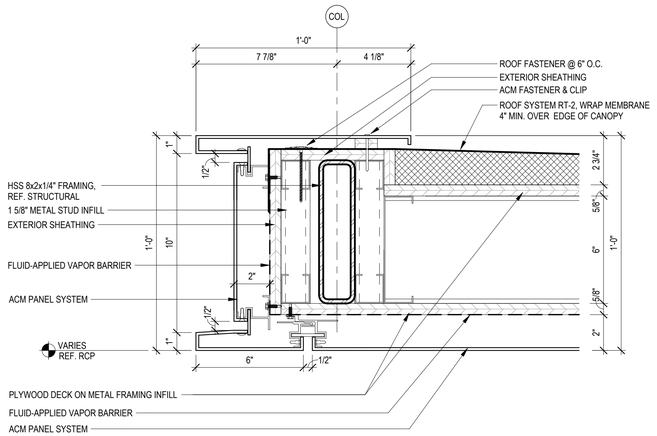


CANOPY EDGE DETAIL | 3" = 1'-0" | 10

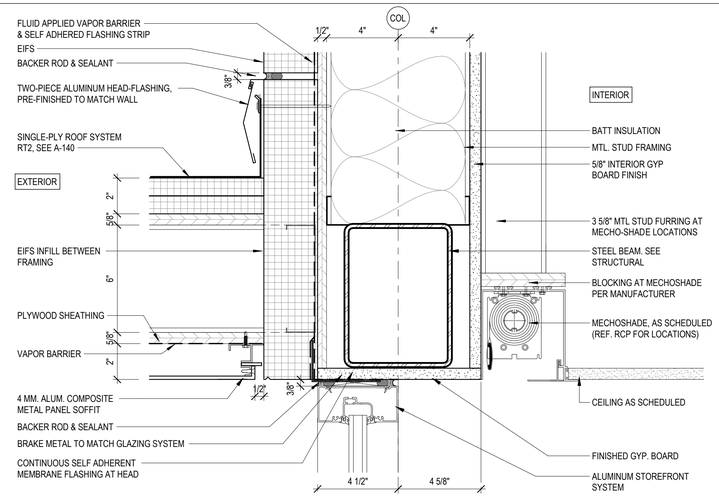


STOREFRONT HEAD @ CANOPY | 3" = 1'-0" | 9

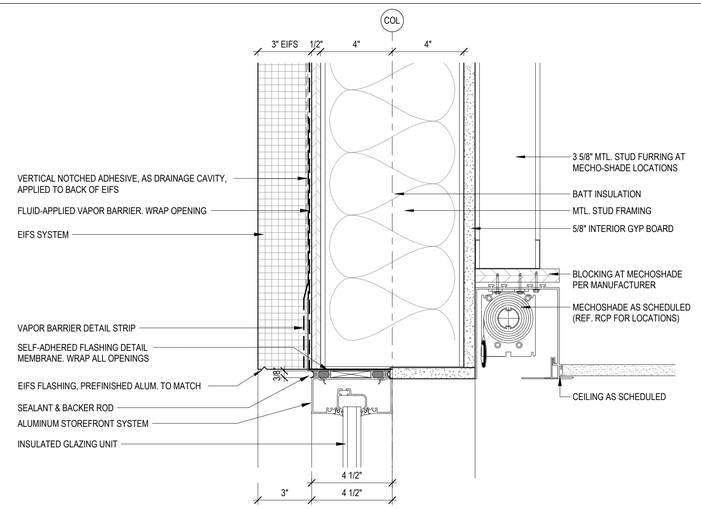


STOREFRONT HEAD @ TYP. EIFS | 3" = 1'-0" | 8

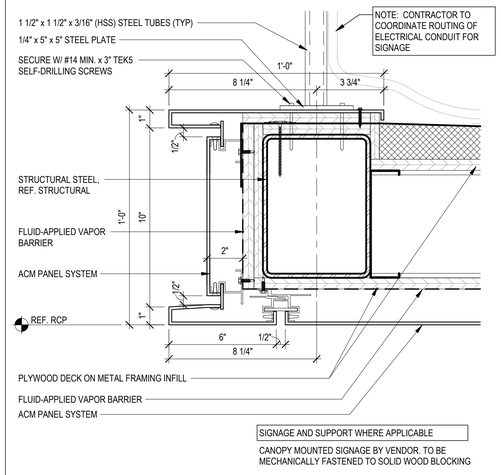


CANOPY EDGE DETAIL AT SIGNAGE | 3" = 1'-0" | 7

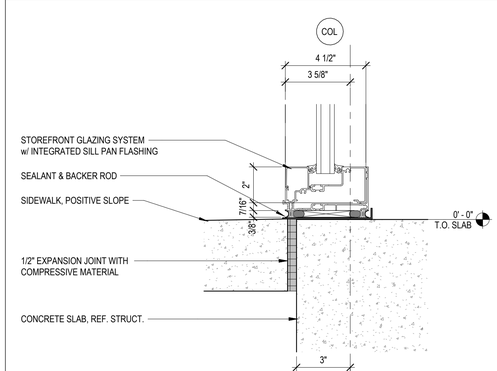


STOREFRONT SILL @ SLAB EDGE | 3" = 1'-0" | 6

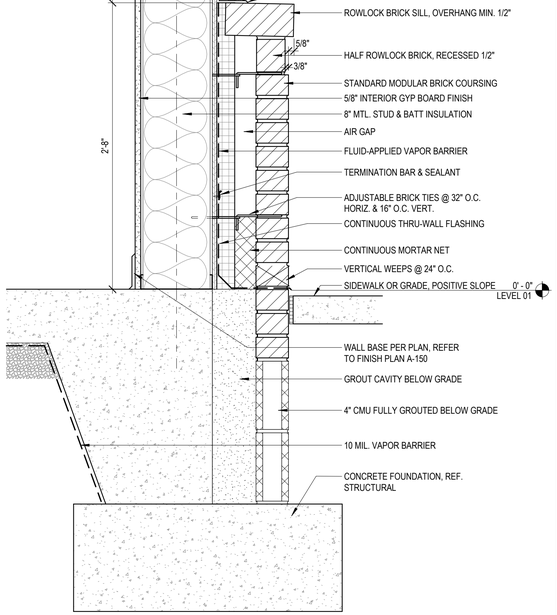


MASONRY SILL TO EIFS | 1 1/2" = 1'-0" | 5

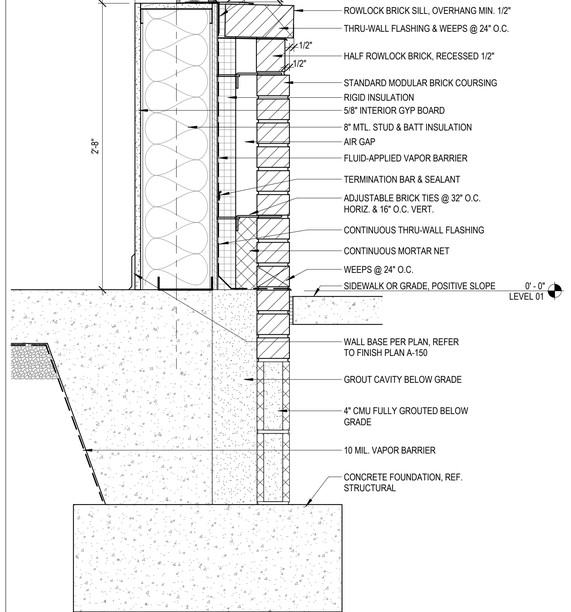


SECTION DETAIL @ MASONRY BASE | 1 1/2" = 1'-0" | 4

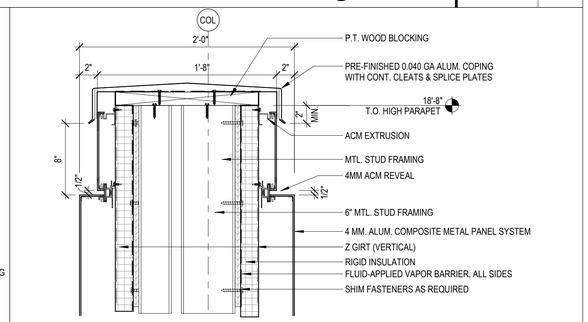

COPING DETAIL @ WING WALL | 1 1/2" = 1'-0" | 3

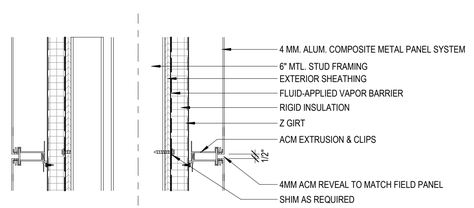

SECTION DETAIL @ ACM HORIZONTAL JOINT | 1 1/2" = 1'-0" | 2

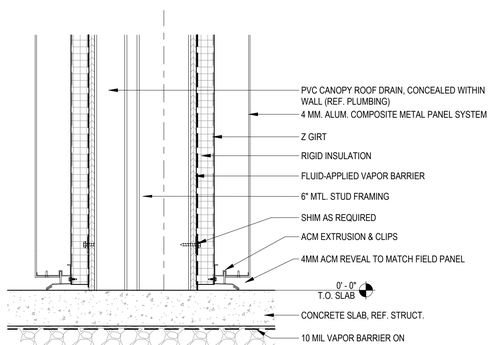

SECTION DETAIL @ ACM WALL | 1 1/2" = 1'-0" | 1

PRAXIS3

100 Peachtree St NW
Suite 1450
Atlanta, GA 30303
404-875-4500 tel
www.praxis3.com

STATE OF GEORGIA
STUART M. ROMM
07/02/26
CERTIFICATE NO. 3457
REGISTERED ARCHITECT

Copyright (c) 2026 Praxis3, LLC

All reports, plans, specifications, computer files, field data, notes and other documents and instruments prepared by Praxis3 shall retain all common law, statutory and other reserved rights, including copyright thereto.

This drawing may not be reproduced in whole or in part without written permission of Praxis3. It is to be returned upon request. Scales as stated are valid on the original drawings.

Rev	Date	Comments
	07/02/2026	PERMIT SET

Client:
FIFTH THIRD BANK

Project Number: 26302
Project Name:
WATSON BLVD.


2711 WATSON BOULEVARD
WARNER ROBINS, GA 31093

Key Plan:


Sheet Title:
SECTION DETAILS

Sheet Number:
A-430


7/8/2026 2:38:41 PM

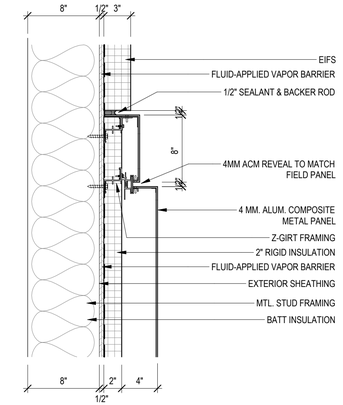

WING WALL JOINT @ EIFS | 1 1/2" = 1'-0" | 11

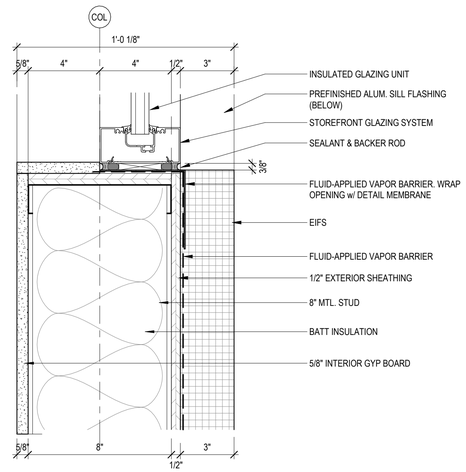


STOREFRONT JAMB @ TYP. EIFS | 3" = 1'-0" | 10

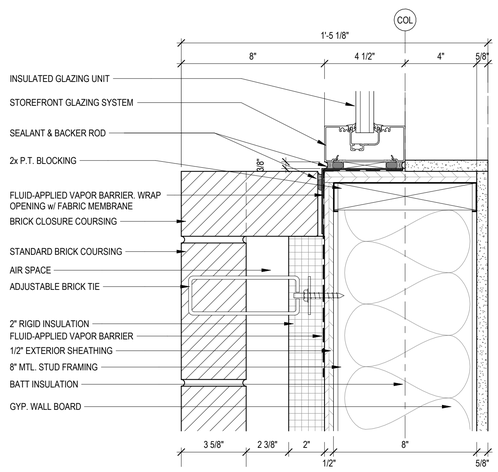


STOREFRONT JAMB @ TYP. BRICK | 3" = 1'-0" | 9

VAPOR BARRIER FLASHING SEQUENCE:
1. INSTALL FLUID-APPLIED AIR BARRIER TO ENTIRE FACADE AND TAKE MATERIAL TO EDGE OF ALL OPENINGS
2. INSTALL FLASHING TAPE AT SILL
3. INSTALL CORNER FLASHING OVER TAPE
4. INSTALL SELF-ADHERING METAL CLAD FLASHING TO SILL
5. INSTALL FLASHING TAPE AT JAMBS
6. INSTALL FLASHING TAPE AT HEAD
7. INSTALL SELF-ADHERING METAL CLAD FLASHING AT HEAD
8. INSTALL TERMINATION BAR AND SEALANT AT TOP OF HEAD FLASHING


NOTE:
-NO REVERSE LAPS
-INTERIOR AND EXTERIOR LAPS TO BE 4" MIN.

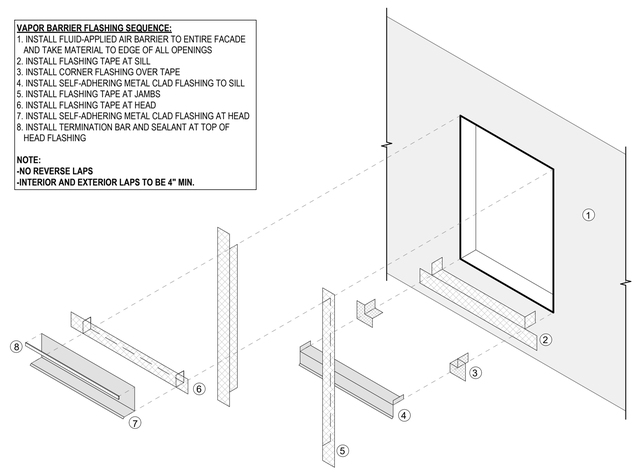


VAPOR BARRIER FLASHING SEQUENCE | 1/2" = 1'-0" | 8

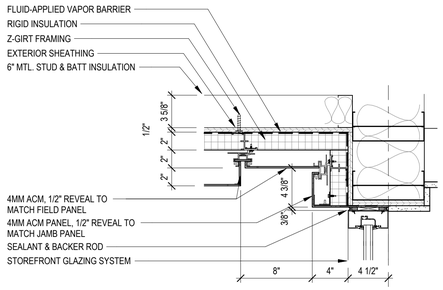


STOREFRONT JAMB @ WING WALL | 1 1/2" = 1'-0" | 7

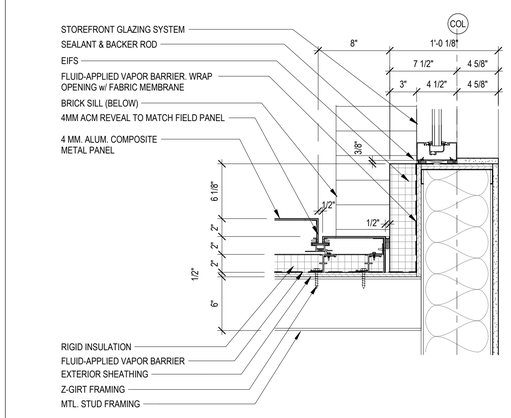


STOREFRONT JAMB @ WING WALL | 1 1/2" = 1'-0" | 6

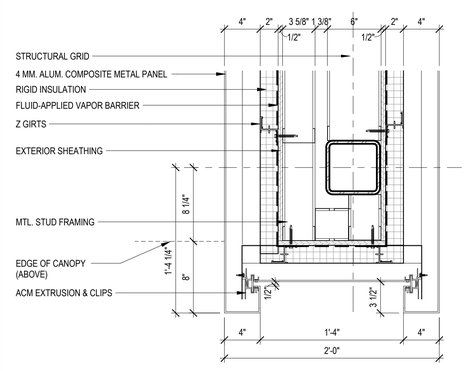


WING WALL (LONG) PLAN DETAIL | 1 1/2" = 1'-0" | 5

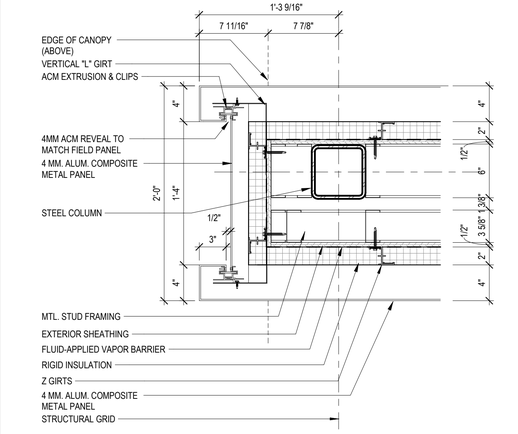


WING WALL (SHORT) PLAN DETAIL | 1 1/2" = 1'-0" | 4

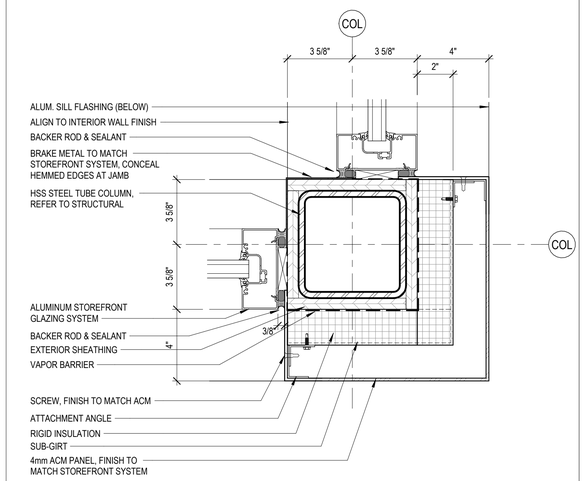

STOREFRONT JAMB @ CORNER | 3" = 1'-0" | 3

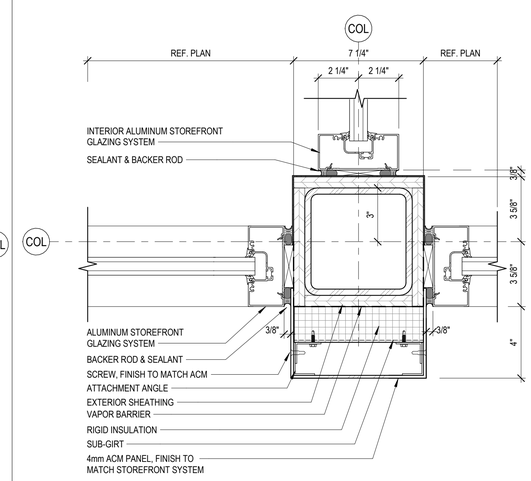

STOREFRONT JAMB @ VESTIBULE CORNER | 3" = 1'-0" | 2

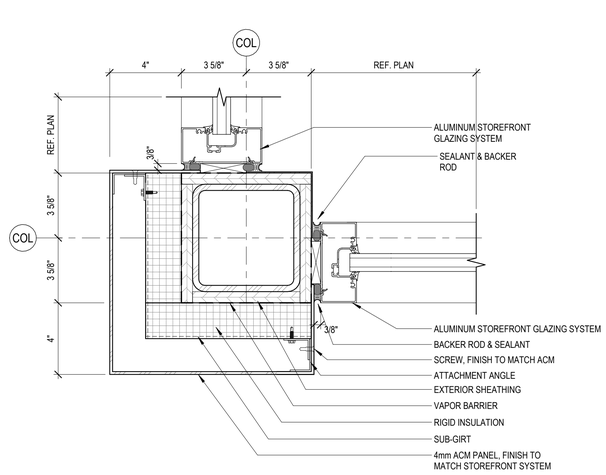

STOREFRONT JAMB @ VESTIBULE COLUMN | 3" = 1'-0" | 1

PRAXIS3
100 Peachtree St NW
Suite 1450
Atlanta, GA 30303
404-875-4500 tel
www.praxis3.com

STATE OF GEORGIA
STUART M. ROMM
07/02/26
CERTIFICATE NO. 3457
REGISTERED ARCHITECT

Copyright (c) 2026 Praxis3, LLC

All reports, plans, specifications, computer files, field data, notes and other documents and instruments prepared by Praxis3 shall retain all common law, statutory and other reserved rights, including copyright thereto.

This drawing may not be reproduced in whole or in part without written permission of Praxis3. It is to be returned upon request. Scales as stated are valid on the original drawings.

Rev	Date	Comments
	07/02/2026	PERMIT SET

Client:
FIFTH THIRD BANK

Project Number: 26302
Project Name:
WATSON BLVD.


2711 WATSON BOULEVARD
WARNER ROBINS, GA 31093

Key Plan:


Sheet Title:
PLAN DETAILS

Sheet Number:
A-440


7/8/2026 2:38:42 PM

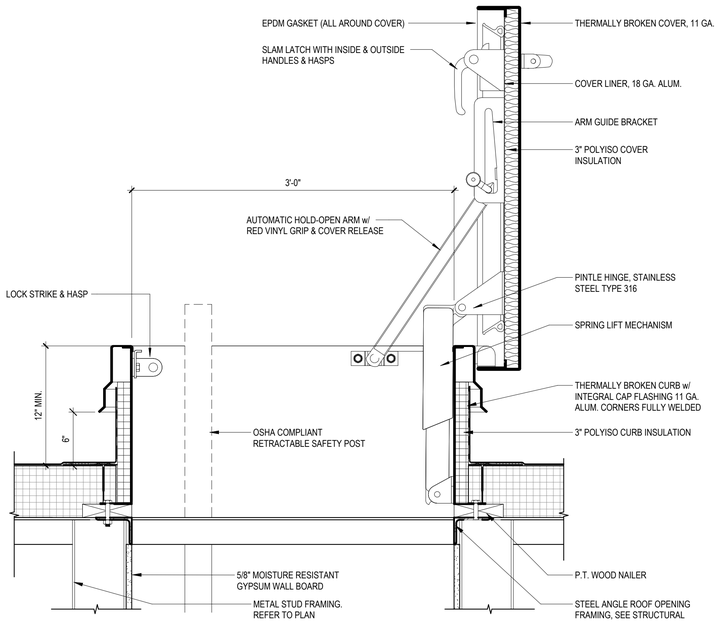


ENLARGED ROOF HATCH DETAIL | 1 1/2" = 1'-0" | 11

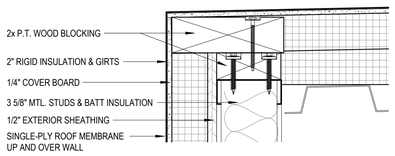


ROOF TRANSITION DETAIL | 3" = 1'-0" | 10

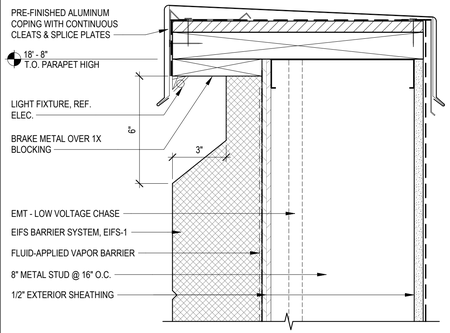


COPING DETAIL | 3" = 1'-0" | 9

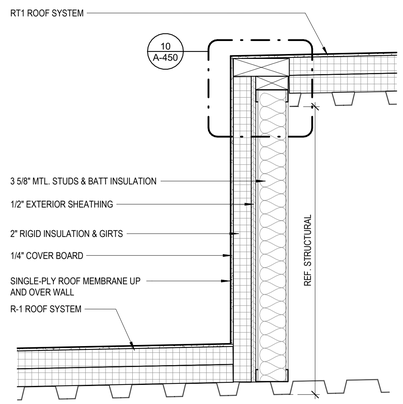


HIGH-LOW ROOF DETAIL | 1 1/2" = 1'-0" | 8

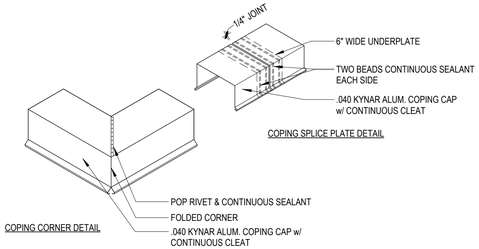


ROOF COPING SPLICE DETAIL | 1 1/2" = 1'-0" | 7

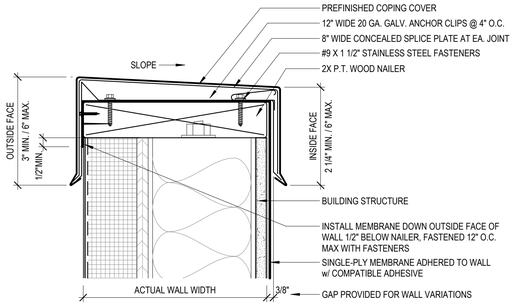


ROOF COPING DETAIL | 3" = 1'-0" | 6

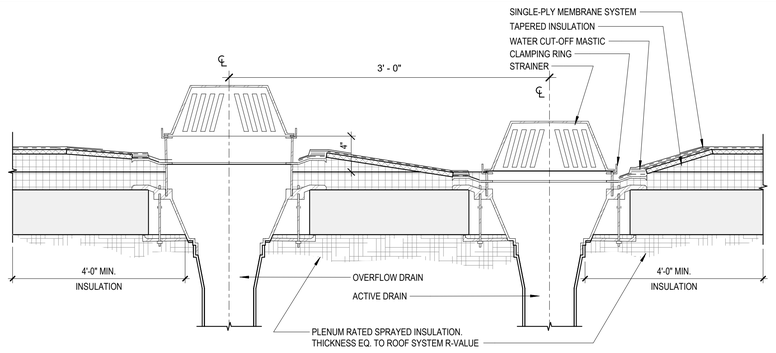


PRIMARY & SECONDARY DRAIN DETAIL | 1 1/2" = 1'-0" | 5

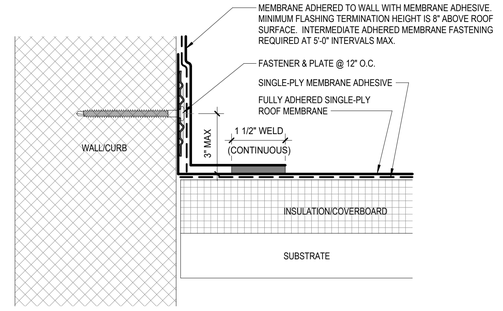


BASE TIE-IN FLASHING DETAIL | 6" = 1'-0" | 4

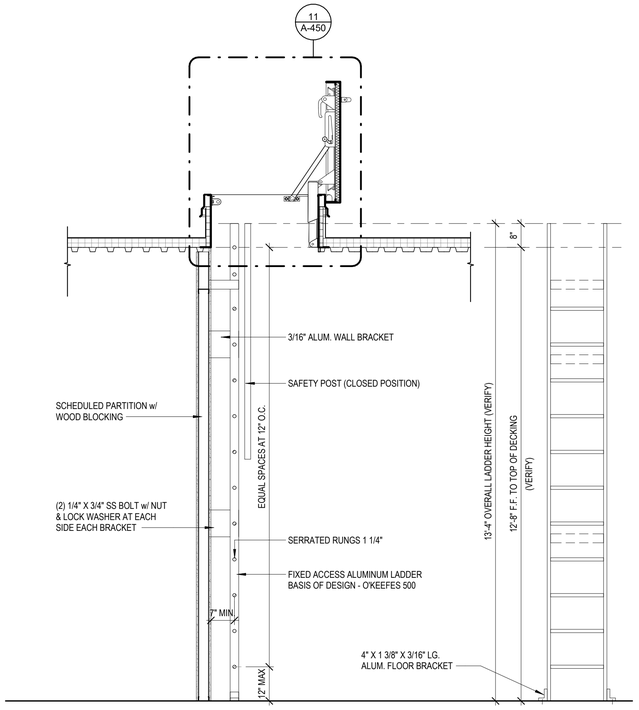

ROOF HATCH & LADDER DETAIL | 1/2" = 1'-0" | 3

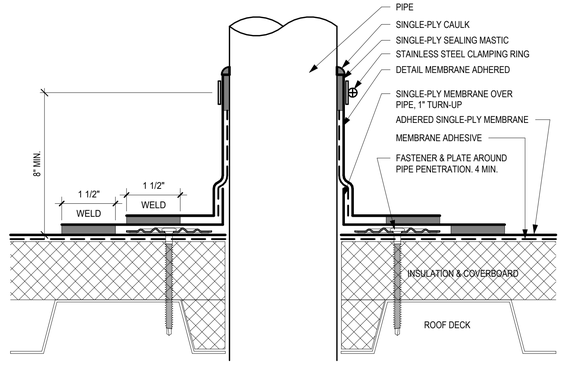

ROOF PIPE PENETRATION DETAIL | 6" = 1'-0" | 2

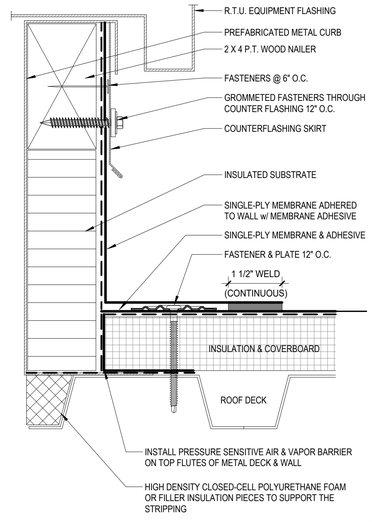

EQUIPMENT CURB DETAIL | 6" = 1'-0" | 1

PRAXIS3
100 Peachtree St NW
Suite 1450
Atlanta, GA 30303
404-875-4500 tel
www.praxis3.com

STATE OF GEORGIA
STUART M. ROMM
07/02/26
CERTIFICATE NO. 34511
REGISTERED ARCHITECT

Copyright (c) 2026 Praxis3, LLC

All reports, plans, specifications, computer files, field data, notes and other documents and instruments prepared by Praxis3 shall retain all common law, statutory and other reserved rights, including copyright thereto.

This drawing may not be reproduced in whole or in part without written permission of Praxis3. It is to be returned upon request. Scales as stated are valid on the original drawings.

Rev	Date	Comments
	07/02/2026	PERMIT SET

Client:
FIFTH THIRD BANK

Project Number: 26302
Project Name:
WATSON BLVD.

2711 WATSON BOULEVARD
WARNER ROBINS, GA 31093

Key Plan:

Sheet Title:
ROOF DETAILS


Sheet Number:
A-450

7/8/2026 2:38:44 PM

DOOR SCHEDULE

MARK	ROOM NAME	DOOR TYPE	DOORS SIZES WIDTH	DOORS SIZES HEIGHT	THICKNESS	DOOR MATERIAL	FRAME MATERIAL	HRDW SET NO.	COMMENTS
100	WEATHER VESTIBULE	D	6' - 0"	8' - 0"		GLASS	ALUM	1	CARD READER AND POWER ASSIST BUTTON
101	ENTRY	D	6' - 0"	8' - 0"		GLASS	ALUM	4	AUTO OPERATOR BUTTON
105	MEETING ROOM	F	3' - 4"	7' - 0"		GLASS	ALUM	14	32.34" CLEAR OPENING. GC PURCHASE AND COORDINATE WITH FIFTHTHIRDSUPPORT@DIRTT.COM
106	ELEC./I.T.	B	3' - 0"	7' - 0"		SCW	HM	7	CARD READER
110	EMPLOYEE LOUNGE	E	3' - 0"	8' - 0"		GLASS	ALUM	3	CARD READER
111	WORK ROOM	C	3' - 0"	7' - 0"		SCW	HM	6	CARD READER, KNOCK DOWN FRAME
112	WOMENS	B	3' - 0"	7' - 0"		SCW	HM	11	1" UNDERCUT
113	MENS	B	3' - 0"	7' - 0"		SCW	HM	11	1" UNDERCUT
114	PHONE ROOM	B	3' - 0"	7' - 0"		SCW	HM	10	
115	JANITOR	B	3' - 0"	7' - 0"		SCW	HM	9	CARD READER, 1" UNDERCUT
xxx		H	3' - 0"	1' - 0 5/8"					

DOOR TYPES

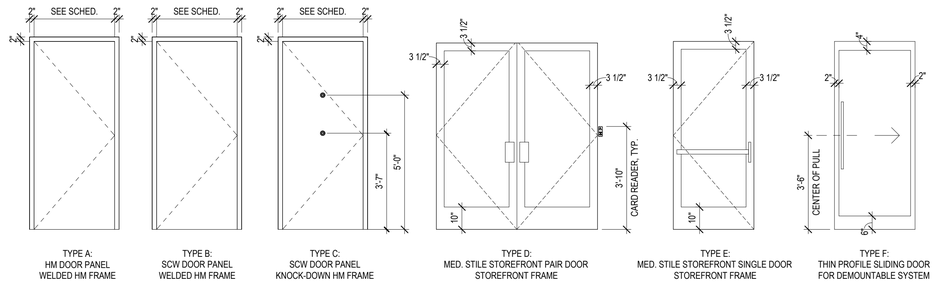

TYPE A: HM DOOR PANEL WELDED HM FRAME

TYPE B: SCW DOOR PANEL WELDED HM FRAME

TYPE C: SCW DOOR PANEL KNOCK-DOWN HM FRAME

TYPE D: MED. STILE STOREFRONT PAIR DOOR STOREFRONT FRAME

TYPE E: MED. STILE STOREFRONT SINGLE DOOR STOREFRONT FRAME

TYPE F: THIN PROFILE SLIDING DOOR FOR DEMOUNTABLE SYSTEM

GENERAL NOTES - DOORS & FRAMES

1. WOOD DOOR FINISH AS SCHEDULED ON FINISH PLAN
2. CAULK DOOR JAMBS AND HEADS AT ALL DOORS LOCATED IN WALLS TO BE SOUND INSULATED AND ANYWHERE THAT GAPS BETWEEN WALL AND FRAME EXCEEDS 1/16"
3. HOLLOW METAL DOOR FRAMES TO BE FULLY WELDED FRAMES UNLESS NOTED OTHERWISE.
4. EXTERIOR HOLLOW METAL DOORS AND FRAMES SHALL BE GALVANIZED AND PAINTED.
5. PROVIDE ANCHORS AND ACCESSORIES AS REQ'D FOR CONDITIONS AS RECOMMENDED BY THE MANUFACTURER. MINIMUM TYPICAL INSTALLATION REQUIRES THREE (3) JAMB ANCHORS AND ONE (1) BASE ANCHOR PER JAMB AT GYP. BOARD PARTITIONS.
6. DOORS SHALL OPERATE FREELY WITHOUT BINDING.
7. FRAME ROUGH OPENINGS AS RECOMMENDED BY METAL STUD MFR. AND DOOR FRAME MFR.
8. DOOR FRAMES SHALL BE SECURED RIGIDLY IN PLACE AND BRACED TO FLOOR AND STRUCTURE ABOVE TO PREVENT BREAK OUT TO PARTITIONS.
9. DOORS TO BE LOCATED 6" FROM FACE OF WALL INCLUDING DOOR FRAME, UNLESS NOTED OTHERWISE.
10. ERECT ALL DOOR FRAMES AND ADJACENT WALLS TO CONFORM TO THE APPLICABLE PLAN CONFIGURATION. NOTIFY ARCHITECT OF ANY CONFLICTS PRIOR TO INSTALLATION OF DOOR FRAMES AND ADJACENT WALLS DURING TRACK LAYOUT.
11. COORDINATE WITH SECURITY SYSTEM, SECURITY RISER DIAGRAM AND FIRE ALARM SYSTEM.
12. CONFIGURE CURTAIN WALL / STOREFRONT SYSTEM TO ACCOMMODATE CONDUIT FOR SECURITY DEVICES.
13. DOOR UNDERCUTS SHALL BE KEPT TO A MINIMAL DIMENSION AND SHALL BE UNIFORM THROUGHOUT PROJECT, UNLESS NOTED OTHERWISE.
14. BOTH SIDES OF ALL EXTERIOR DOORS SHALL HAVE THE SAME ELEVATION WITH NO MORE THAN 1/2" DIFFERENCE ON EITHER SIDE.
15. INSTALLATION OF ALL DOORS AND HARDWARE SHALL MEET MINIMUM ADA REQUIREMENTS.

GENERAL NOTES - HARDWARE

1. CONTINUOUS HINGES ARE LISTED IN THE HW SETS; STAINLESS STEEL BUTT HINGES/OFFSET PIVOTS ARE ACCEPTABLE ON INTERIOR DOORS ONLY.
2. FLORIDA PROJECTS: PANIC EXIT HARDWARE ON EXTERIOR ALUMINUM DOORS SUBJECT TO CHANGE BASED ON DOOR SYSTEM MANUFACTURER 'S REQUIREMENTS. HARDWARE MUST BE REVIEWED BY ARCHITECT PRIOR TO ORDER.

ALL DOOR HARDWARE TO BE PURCHASED FROM LOCKNET OR ALARM DETECTION SYSTEMS, BASED ON PROJECT LOCATION. GC TO FURNISH FOR INSTALLATION

- COVERAGE AREAS:
  a. ALL OF ILLINOIS AND NW INDIANA: ALARM DETECTION SYSTEM: dsirek@adsalarm.com
  b. ALL PROJECTS OUTSIDE OF ILLINOIS AND NW INDIANA: LOCKNET: 53Retail@LockNet.com

CYLINDERS AND KEYING

- Permanent KIL, Mortise & Rim Lock Cylinders: Proprietary Medeco cylinders furnished by Owner, installed by Contractor at later date.
- Temporary Cylinders: Manufacturers' standard cylinders / keyway to match across all cylinder types.
- Bored locks: Standard KIL cylinders in keyway to match Rim & Mortise cylinders.
- Rim & Mortise cylinders: Complete fixed core cylinders in keyway to match bored locks.
- Keyway: Supply locks complete with manufacturers standard cylinders, construction keyed.
- Key Quantity: Provide the following minimum number of keys:
  - Construction Keys (where required): Ten (10).
  - Construction Keying: Provide manufacturers standard keyed cylinders, bitted for construction keying.

ACCEPTABLE MFRS


- Locksets: Sargent – "L" Lever – No Substitutions
- Exit Devices: Sargent 8000 Series – No Substitutions
- Door Closers: Sargent 281 Series – No Substitutions
- Automatic Operators – Norton 6000 – No Substitutions
- Electric Strikes: HES 1500 / 5000 / 5200 / 9000 Series – No Substitutions

ABBREVIATION LEGEND


PE	Pemko
SA	Sargent
MC	Medeco Cylinder
RO	Rockwood
RF	Rixson
NO	Norton
BEA	BEA
SU	Securitron
VD	Von Duprin
HS	HES
MK	McKinney
DT	DIRTT
OT	by Others

GENERAL NOTES - ADA

1. DOOR THRESHOLD SHALL BE 1/2"" HIGH MAX WITH SLOPE 1:2 MAX. RAISED THRESHOLDS TO COMPLY WITH 302 AND 303 (404.2.5, 302, 303)
2. DOUBLE DOORS - AT LEAST (1) ACTIVE LEAF OF A DOORWAY TO PROVIDE 32"" MIN CLEAR OPENING WIDTH. (402.2.2, 403.2.3)
3. SWINGING DOOR SURFACES WITHIN 10"" FROM FINISH FLOOR MEASURED VERTICALLY TO HAVE A SMOOTH SURFACE ON THE PUSH SIDE EXTENDING THE FULL WIDTH OF THE DOOR. PARTS CREATING HORIZONTAL OR VERTICAL JOINTS IN THESE SURFACES TO BE WITHIN 1/16" OF THE SAME PLANE AS THE OTHER. CAVITIES CREATED BY ADDED KICK PLATES SHALL BE CAPPED. EXCEPTIONS: 1) SLIDING DOORS ARE NOT REQUIRED TO COMPLY WITH 404.2.10; 2) TEMPERED GLASS DOORS WITHOUT STILES AND HAVING A BOTTOM RAIL OR SHOE WITH THE TOP LEADING EDGE TAPERED AT 60 DEGREES MINIMUM FROM THE HORIZONTAL SHALL NOT BE REQUIRED TO MEET THE 10"" BOTTOM SMOOTH SURFACE HEIGHT REQUIREMENT (ADA 404.2.10)
4. DOOR HARDWARE TO BE OPERABLE WITH ONE HAND AND SHALL NOT REQUIRE TIGHT GRASPING, PINCHING, OR TWISTING OF THE WRIST (309.4)
5. OPERABLE PARTS SUCH AS DOOR HARDWARE TO BE MOUNTED 34" MIN AND 48" MAX AFF. WHERE SLIDING DOORS ARE IN THE FULLY OPEN POSITION, OPERATING HARDWARE SHALL BE EXPOSED AND USABLE FROM BOTH SIDES (404.2.7)
6. DOOR CLOSERS TO BE ADJUSTED SO THAT FROM THE OPEN POSITION OF 90 DEGREES, THE TIME REQUIRED TO MOVE THE DOOR TO A POSITION OF 12 DEGREES FROM THE LATCH IS 5 SECONDS MIN (404.2.8)
7. THE FORCE FOR PUSHING OR PULLING OPEN A DOOR OR GATE OTHER THAN FIRE DOORS ARE AS FOLLOWS: A) INTERIOR HINGED DOORS AND GATES REQUIRE 5 LBS MAXIMUM FORCE TO OPEN. B) SLIDING AND FOLDING DOORS REQUIRE 5 LBS MAXIMUM FORCE TO OPEN. THESE FORCES DO NOT APPLY TO THE FORCE REQUIRED TO RETRACT LATCH BOLTS OR DISENGAGE OTHER DEVICES THAT HOLD THE DOOR IN A CLOSED POSITION. (ADA 404.2.9)

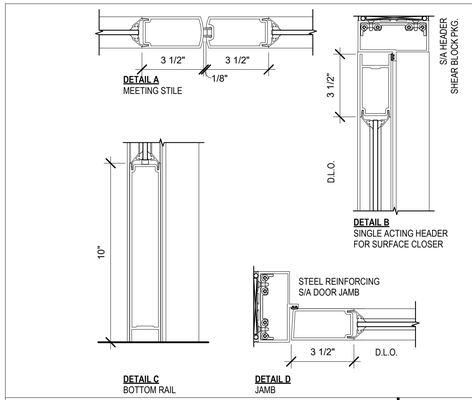


DOORS - STORFRONT DETAILS | 3" = 1'-0" | 8

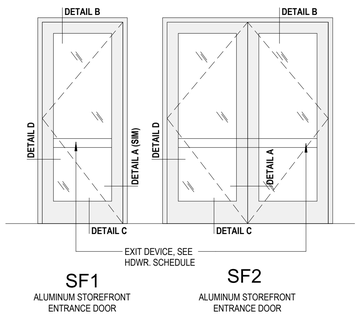

SF1
ALUMINUM STOREFRONT ENTRANCE DOOR

SF2
ALUMINUM STOREFRONT ENTRANCE DOOR

ELEVATION - STOREFRONT ENTRANCES | 3/8" = 1'-0" | 7

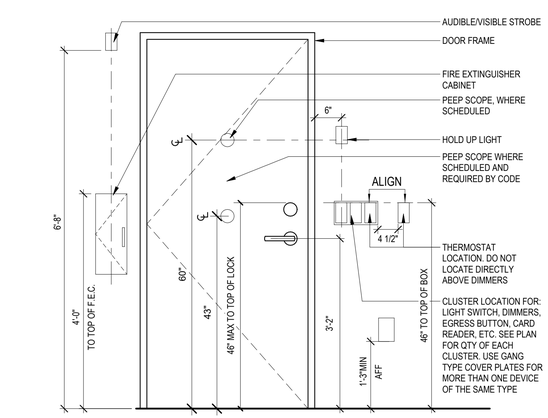


DEVICES AT DOOR IN CLOSED POSITION


DEVICES AT DOOR IN OPEN POSITION

NOTE: ALL DIMENSIONS TO CENTER LINE OF DEVICES U.N.O.; INTERCOM TO BE MOUNTED AT 3'-9" AFF U.N.O.; CENTER ALL DEVICES BELOW SWITCH. ALL OPERABLE PARTS SHALL BE OPERABLE WITH ONE HAND AND SHALL NOT REQUIRE TIGHT GRASPING, PINCHING, OR TWISTING OF THE WRIST WITH A MAX OF 5 LBS. OF FORCE TO OPERATE. A CLEAR SPACE TO BE PROVIDED OF 30" MIN. X 48" MIN.


TYPICAL MOUNTING HEIGHTS | 3/4" = 1'-0" | 6

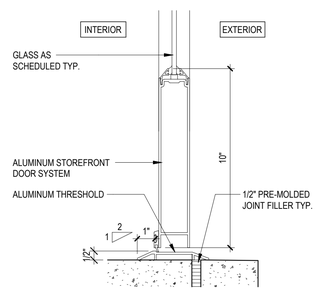


STOREFRONT THRESHOLD | 3" = 1'-0" | 5

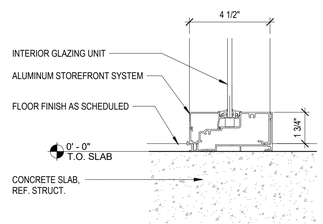


INT. ALUM. SILL | 3" = 1'-0" | 4

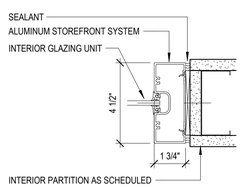

INT. ALUM. JAMB/HEAD | 3" = 1'-0" | 3

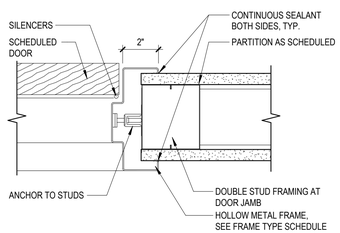

INTERIOR HM JAMB | 3" = 1'-0" | 2

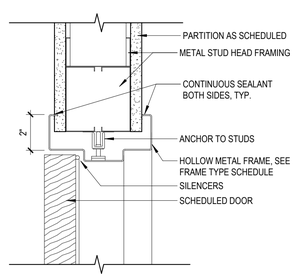

INTERIOR HM HEAD | 3" = 1'-0" | 1

PRAXIS3

100 Peachtree St NW
Suite 1450
Atlanta, GA 30303
404-875-4500 tel
www.praxis3.com

STATE OF GEORGIA
STUART M. ROMM
07/02/26
CERTIFICATE NO. 3457
REGISTERED ARCHITECT

Copyright (c) 2026 Praxis3, LLC

All reports, plans, specifications, computer files, field data, notes and other documents and instruments prepared by Praxis3 shall retain all common law, statutory and other reserved rights, including copyright thereto.

This drawing may not be reproduced in whole or in part without written permission of Praxis3. It is to be returned upon request. Scales as stated are valid on the original drawings.

Rev	Date	Comments
	07/02/2026	PERMIT SET

Client:
FIFTH THIRD BANK

Project Number: 26302
Project Name:
WATSON BLVD.

2711 WATSON BOULEVARD
WARNER ROBINS, GA 31093

Key Plan:

Sheet Title:
DOOR SCHEDULE & DETAILS

Sheet Number:
A-600

7/8/2026 2:38:47 PM

HARDWARE SCHEDULE

Set 1.0
Doors: 100 (Weather Vestibule)
Description: Standard - Exterior Aluminum Storefront Pair - Access Control - Panic Egress - Auto-Door

2 Continuous Hinge x EPT prep	CFM__HD1 PT		PE
1 Elec CVR Exit Device (Nightlatch)	53 55 56-HK AD8410 106 x less pull (24V)	US32D	SA
1 Elec CVR Exit Device (Exit Only)	53 55 56-HK AD8410 EO (24V)	US32D	SA
1 Mortise Cylinder	41 series as req'd	US32D	SA
1 Permanent Medeco Cylinder	By Owner (installed by Contractor – coordinate / verify keying with owner)	24	MC
2 Offset Pull	RM201	US32D316	RO
1 Conc Overhead Stop	6-X36	630	RF
1 Door Closer W/ Stop	281 CPS	EN	SA
1 Blade Stop Spacer	581 as req'd	EN	SA
1 Closer Mtg Plate	281D as req'd	EN	SA
1 Automatic Opener	6061 (D) - Push Side	689	NO
1 Threshold	253x3AFG FHSL14SS		PE
1 Credential Reader	By Div 28 (12V)		OT
1 ADA Switch – Flush Mount Box	10BOXJAMBFM		BEA
1 ADA Switch - Jamb Mount	503		NO
2 Power Supply Battery (24V)	B-24-5		SU
2 Position Switch	DPS-M		SU
2 Shared Power Supply (24V)	AQD2-8F8R2 24V-2 AMP		SU
2 Electric Power Transfer	EPT10		VD
1 Seals, Sweeps & Astragals	By Aluminum Door Mfr.		OT

Notes:
Entry by valid credential at reader to retract latches (both leafs) or manual key (active leaf) when locked.
Free egress (both leafs) at all times. Push / Pull operation as required by electronic dogging of exit devices, either timed unlock via access control system or by Hex Key dogging
Door position switches to monitor opening status. Exit devices have integral RX feature to signal egress.
Auto-Door operator and ADA switches must be integrated with electronic exit devices.
Exterior ADA switch is controlled by exit device latch monitor in active door leaf. Switch active only when latch is in retracted position.
Vestibule ADA switch always active and will unlock door for egress.
See plan sheet for locations of automated door leafs and switch locations.
Coordinate with electrical and security contractors.

Set 3.0
Doors: 110 (Employee Lounge)
Description: Standard - Exterior Aluminum Storefront Single - Access Control Function

1 Continuous Hinge	CFM__HD1		PE
1 Rim Exit Device (NL x less dogging)	43 AD8504 Less Pull	US32D	SA
1 Rim Cylinder	34 series as req'd	US32D	SA
1 Permanent Medeco Cylinder	By Owner (installed by Contractor – coordinate keying with owner)	24	MC
1 Electric Strike w/ Latch Monitor	9500-LBM (12V)	630	HS
1 Offset Pull	RM201 Mtg-Type 12XHD	US32D316	RO
1 Door Closer w/ Stop	281 CPS	EN	SA
1 Blade Stop Spacer	581 as req'd	EN	SA
1 Closer Mtg Plate 281D as req'd EN SA			
1 Threshold	253x3AFG FHSL14S		PE
1 Access Control Reader	By Div 28 (12V)		OT
1 Power Supply	By Div 28 (12V)		OT
1 Seals, Sweeps & Astragals	By Aluminum Door Mfr.		OT

Notes:
Entry by valid input at exterior reader to release electric strike and shunt alarm or manual key.
Free egress by manual push bar operation to retract latch
LBM feature in electric strike to monitor opening status, shunted by valid input at exterior reader.
Coordinate with electrical and security contractors.

Set 4.0
Doors: 101 (Entry)
Description: Double Interior Aluminum Storefront Pair – Push / Pull Function - Auto-Door

2 Continuous Hinge	CFM__HD1		PE
2 Push / Pull Set	RM251 Mtg-Type 12XHD	US32D	RO
1 Conc Overhead Stop	6-X36	630	RF
1 Door Closer W/ Stop	281 CPS	EN	SA
1 Blade Stop Spacer	581 as req'd	EN	SA
1 Closer Mtg Plate	281D as req'd	EN	SA
1 Automatic Opener	6061 (D) - Push Side	689	NO
1 ADA Switch - Jamb Mount	503		NO
1 ADA Switch Mounting Box	10BOXJAMBFM		BEA
1 ADA Switch – Vestibule Button	10PBDGP1		BEA
1 ADA Switch Mounting Box	10BOX475SQFM		BEA
1 Seals, Sweeps & Astragals	By Aluminum Door Mfr.		OT

Notes:
Auto door operation by Interior & Vestibule ADA switches at all times.
See plan sheet for locations of automated door leafs and switch locations.
Coordinate with electrical and security contractors.

Set 5.0 (1900 Narrow)
Doors: 101 (Entry)
Description: Interior Aluminum Storefront Single - Push / Pull Function - Auto-Door

1 Continuous Hinge	CFM__HD1		PE
1 Push Pull Set	RM251 Mtg-Type 12XHD	US32D	RO
1 Conc Overhead Stop	6-X36	630	RF
1 Automatic Opener	6061 (D) - Push Side	689	NO
1 ADA Switch	503 (jamb)		NO
1 ADA Switch Mounting Box	10BOXJAMBFM		BEA
1 ADA Switch – Vestibule Button	10PBDGP1		BEA
1 ADA Switch Mounting Box	10BOX475SQFM		BEA
1 Seals, Sweeps & Astragals	By Aluminum Door Mfr.		OT

Notes:
Auto door operation by Interior & Vestibule ADA switches at all times.
See plan sheet for locations of automated door leaf and switch locations.
Coordinate with electrical and security contractors.

Set 6.0
Doors: 111 (Work Room)
Description: Access Control Function x Door Closer x Viewers

3 Hinge, Full Mortise	TA2714 NRP (outswing) / TA2714 (inswing)	US26D	MK
1 Storeroom Lock	10XG04 LL (w/ std cyl)	US26D	SA
1 Permanent Medeco KIL Cylinder	By Owner (installed by Contractor – coordinate keying with owner)	24	MC
1 Electric Strike w/ Latch Monitor	5200C-LBM (12V)	630	HS
1 Door Stop	441CU floor stop (Use Rixson 10-x36 overhead stop as req'd if floor stop is not feasible	US26D	RO
1 Door Closer	281 O / P10 as req'd	EN	SA
1 Kick Plate	K1050 10" HGT x CSK x BEV	US32D	RO
3 Silencer	608/609 as req'd		RO
1 Access Control Reader	By Div 28 (12V)		OT
1 Wiring Harness (frame)	QC-C3000P		MK
1 RX Motion Sensor	By Div 28 (12V)		SU
1 Power Supply	By Div 28 (12V)		OT
2 Door Scope / Viewer	DS1000	626	OT

Notes:
Entry by valid input at reader or manual key. Free egress at all times.
LBM in electric strike to monitor opening status, shunted by RX motion sensor if required.
Coordinate with electrical and security contractors.
Mount door scopes according to typical mounting height diagram

Set 7.0
Doors: 106 (Electrical/IT Room)
Description: Access Control Function x Closer w/ Stop

3 Hinge, Full Mortise	TA2714 NRP (outswing) / TA2714 (inswing)	US26D	MK
1 Storeroom Lock	10XG04 LL (w/ std cyl)	US26D	SA
1 Permanent Medeco KIL Cylinder	By Owner (installed by Contractor – coordinate keying with owner)	24	MC
1 Electric Strike w/ Latch Monitor	5200C-LBM (12V)	630	HS
1 Door Closer W/ Stop	281 CPS	EN	SA
3 Silencer	608/609 as req'd		RO
1 Credential Reader	By Div 28 (12V)		OT
1 Wiring Harness (frame)	QC-C3000P		MK
1 RX Motion Sensor	By Div 28 (12V)		SU

Notes:
Entry by valid input at reader or manual key. Free egress at all times.
LBM feature in electric strike to monitor opening status, shunted by RX motion sensor if required.
Coordinate with electrical and security contractors.

Set 8.0
Doors: (Storage Rooms) (1900N IT ROOM)
Description: Access Control Function x Door Closer

3 Hinge, Full Mortise	TA2714 NRP (outswing) / TA2714 (inswing)	US26D	MK
1 Storeroom Lock	10XG04 LL (w/ std cyl)	US26D	SA
1 Permanent Medeco KIL Cylinder	By Owner (installed by Contractor – coordinate keying with owner)	24	MC
1 Electric Strike w/ Latch Monitor	5200C-LBM (12V)	630	HS
1 Door Stop	441CU floor stop (Use Rixson 10-x36 overhead stop as req'd if floor stop is not feasible	US26D	RO
1 Door Closer	281 O / P10 as req'd	EN	SA
3 Silencer	608/609 as req'd		RO
1 Access Control Reader	By Div 28 (12V)		OT
1 Wiring Harness (frame)	QC-C3000P		MK
1 RX Motion Sensor	By Div 28 (12V)		SU
1 Power Supply	By Div 28 (12V)		OT

Notes:
Entry by valid input at reader or manual key. Free egress at all times.
LBM in electric strike to monitor opening status, shunted by RX motion sensor if required.
Coordinate with electrical and security contractors.

Set 9.0
Doors: 115 (Janitor)
Description: Access Control Function x Kickplate (Janitor Closet)

3 Hinge, Full Mortise	TA2714 NRP (outswing) / TA2714 (inswing)	US26D	MK
1 Storeroom Lock	10XG04 LL (w/ std cyl)	US26D	SA
1 Permanent Medeco KIL Cylinder	By Owner (installed by Contractor – coordinate keying with owner	24	MC
1 Electric Strike w/ Latch Monitor	5200C-LBM (12V)	630	HS
1 Kick Plate	K1050 10" HGT x CSK x BEV	US32D	RO
1 Door Stop	441CU floor stop (Use Rixson 10-x36 overhead stop as req'd if floor stop is not feasible	US26D	RO
3 Silencer	608/609 as req'd		RO
1 Wiring Harness (frame)	QC-C3000P		MK
1 Access Control Reader	By Div. 28 (12V)		OT
1 Power Supply (12V)	By Div 28		OT

Notes:
Entry by valid input at reader or manual key. Free egress at all times.
LBM in electric strike to monitor opening status if required.
Coordinate with electrical and security contractors.

Set 10.0
Doors: 114 (Phone Room)
Description: Privacy Function - Occupancy Indicator (Phone Room)

3 Hinge, Full Mortise	TA2714 4.5" x 4.5"	US26D	MK
1 Privacy Lock w/ Indicator	LB V20 8265 LNL	US26D	SA
1 Door Stop	441CU floor stop (Use Rixson 10-x36 overhead stop as req'd if floor stop is not feasible	US26D	RO
3 Silencers	608/609 as req'd		PE
2 Coat Hook	RM817	US26D	RO

Set 11.0
Doors:112 (Womens), 113 (Mens)
Description: Privacy Function w/ Occupancy Indicator x Door Closer (Restroom)

3 Hinge, Full Mortise	TA2314 4.5" x 4.5"	US26D	MK
1 Privacy Lock w/ Indicator	LB V20 8265 LNL	US26D	SA
1 Door Stop	441CU floor stop (Use Rixson 10-x36 overhead stop as req'd if floor stop is not feasible	US26D	RO
1 Door Closer	281 O / P10 as req'd	EN	SA
1 Kick Plate	K1050 10" HGT x CSK x BEV	US32D	RO
3 Silencer	608/609 as req'd		RO
2 Coat Hook	RM817	US26D	RO

Set 14.0
Doors: 105 (Meeting Room)
Description: DIRTT Doors

1 Concealed Overhead Slider Hardware	By DIRTT	US26D	DT
1 Back-to-Back Pull	30"/24" CTC	630	DT

PRAXIS3
100 Peachtree St NW
Suite 1450
Atlanta, GA 30303
404-875-4500 tel
www.praxis3.com

STATE OF GEORGIA
STUART M. ROMM
07/02/26
CERTIFICATE NO. 3457
REGISTERED ARCHITECT

Copyright (c) 2026 Praxis3, LLC

All reports, plans, specifications, computer files, field data, notes and other documents and instruments prepared by Praxis3 shall retain all common law, statutory and other reserved rights, including copyright thereto.

This drawing may not be reproduced in whole or in part without written permission of Praxis3. It is to be returned upon request. Scales as stated are valid on the original drawings.

Rev	Date	Comments
	07/02/2026	PERMIT SET

Client:
FIFTH THIRD BANK

Project Number: 26302
Project Name:
WATSON BLVD.

2711 WATSON BOULEVARD
WARNER ROBINS, GA 31093

Key Plan:

Sheet Title:
HARDWARE SCHEDULES

Sheet Number:
A-601

7/8/2026 2:38:49 PM

ACM PANEL - GENERAL NOTES


EXTERIOR GLAZING BASIS OF DESIGN:

REGULAR EXTERIOR STOREFRONT:
YKK YES45 TU - CENTER SET THERMALLY BROKEN STOREFRONT, 1" PANEL INFILL
2" X 4 1/2" MULLION

EXTERIOR INSULATED GLASS UNIT:
VITRO SOLARBAN 90 (2) ACUITY + ACUITY
OVERALL THICKNESS: 1 INCH
VLT: 53%
EXT. REFLECTANCE: 12%
INT. REFLECTANCE: 19%
U-VALUE (ARGON): 0.24
SHGC: 0.23
LSG: 2.30
PROVIDE SAFETY GLAZING LABELING


INTERIOR GLAZING BASIS OF DESIGN:
YKK YES45 FS - CENTER SET, 1/4" PANEL INFILL
1 3/4" X 4 1/2" MULLION

INTERIOR GLASS UNIT:
CLEAR FLOAT GLASS, FULLY TEMPERED
OVERALL THICKNESS: 6mm (1/4")
PROVIDE SAFETY GLAZING LABELING

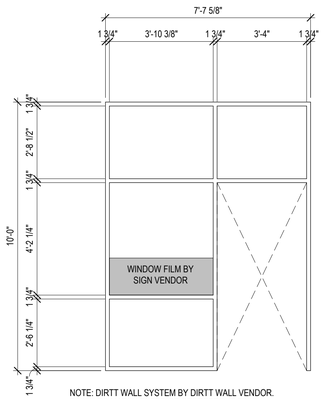


NOTE: DIRTT WALL SYSTEM BY DIRTT WALL VENDOR.
FINISH TO MATCH EXTERIOR STOREFRONT FINISH.


WINDOW K | 3/8" = 1'-0" | 10

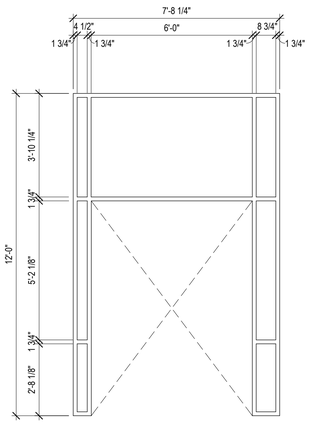


WINDOW J | 3/8" = 1'-0" | 9

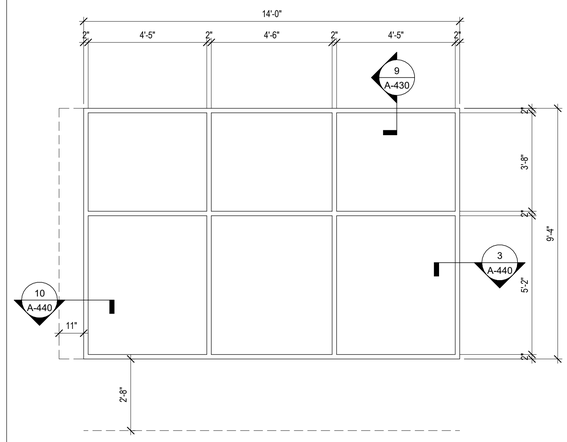


WINDOW H | 3/8" = 1'-0" | 8

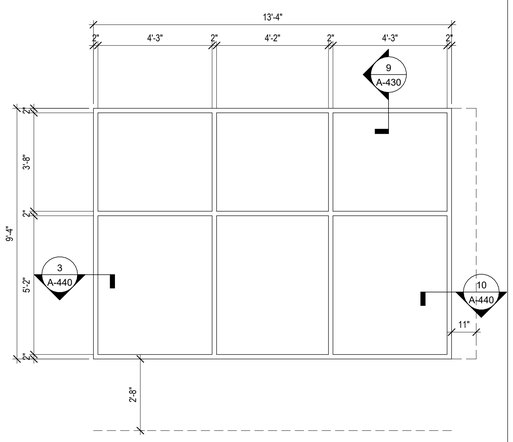


WINDOW G | 3/8" = 1'-0" | 7

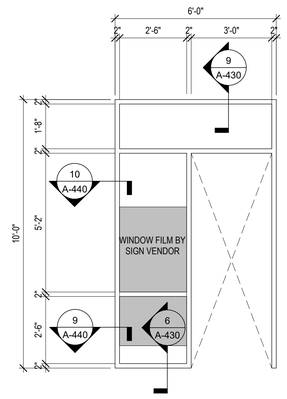


WINDOW F | 3/8" = 1'-0" | 6

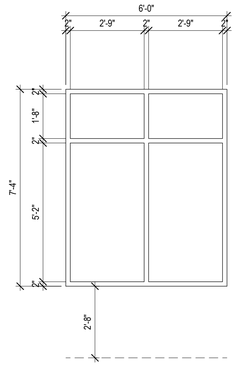


WINDOW E | 3/8" = 1'-0" | 5

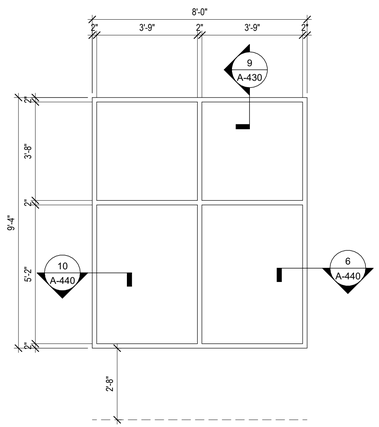


WINDOW D | 3/8" = 1'-0" | 4

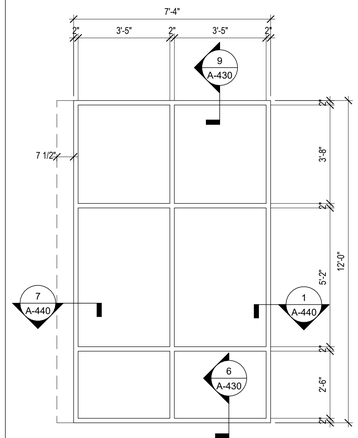

WINDOW C | 3/8" = 1'-0" | 3

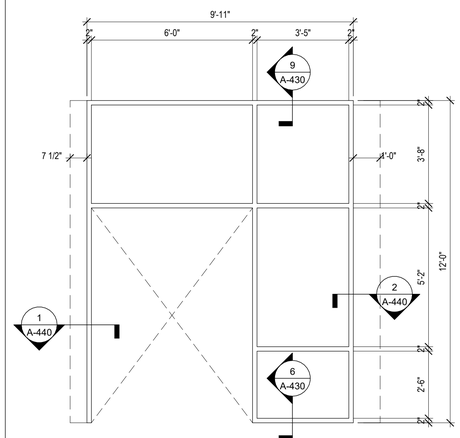

WINDOW B | 3/8" = 1'-0" | 2

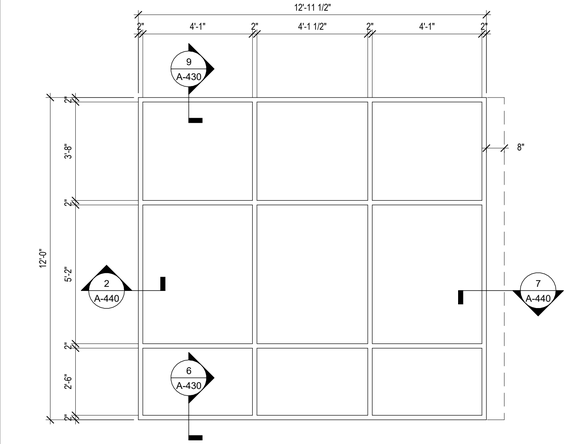

WINDOW A | 3/8" = 1'-0" | 1

PRAXIS3

100 Peachtree St NW
Suite 1450
Atlanta, GA 30303

404-875-4500 tel
www.praxis3.com

STATE OF GEORGIA
STUART M. ROMM
07/02/26
CERTIFICATE NO. 34521
REGISTERED ARCHITECT

Copyright (c) 2026 Praxis3, LLC

All reports, plans, specifications, computer files, field data, notes and other documents and instruments prepared by Praxis3 shall retain all common law, statutory and other reserved rights, including copyright thereto.

This drawing may not be reproduced in whole or in part without written permission of Praxis3. It is to be returned upon request. Scales as stated are valid on the original drawings.

Rev	Date	Comments
	07/02/2026	PERMIT SET

Client:
FIFTH THIRD BANK

Project Number: 26302
Project Name:
WATSON BLVD.

2711 WATSON BOULEVARD
WARNER ROBINS, GA 31093


Key Plan:

Sheet Title:
WINDOW ELEVATIONS


Sheet Number:
A-610

7/8/2026 2:38:50 PM


PARTITION HEAD DETAILS

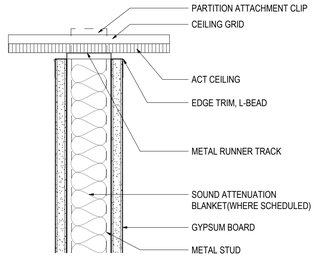

A-T03

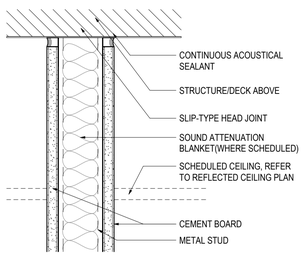


B-T01

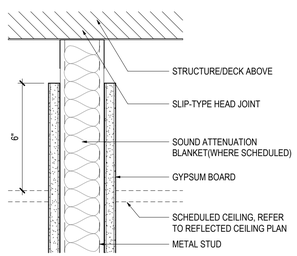


A-T02

PARTITION BASE DETAILS

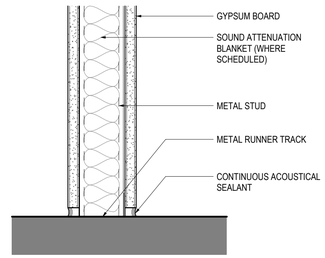


A-B01

PARTITION SERIES - A

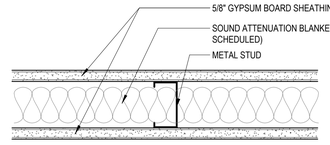

PARTITION TYPE	FRAMING			DETAILS		ATTEN THK	FIRE RTG	UL LISTING	STC RTG
	THK (IN)	DEPTH	SPACING	TOP	BOT				

PARTITION LEGEND

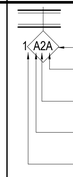

PARTITION TAG
PARTITION HEIGHT DESIGNATOR (SEE **TABLE D** BELOW)
FRAMING MEMBER DEPTH (SEE **TABLE B** OR **TABLE C** - BELOW
PARTITION SERIES (SEE **TABLE A** - BELOW)
FIRE RATING (IF APPLICABLE)

TABLE A- PARTITION SERIES CONSTRUCTION ASSEMBLY

SERIES	SHEATHING	FRAMING	SHEATHING
A	1-LAYER	MTL STUD	1-LAYER
B	1-LAYER	MTL STUD	1-LAYER
C	1-LAYER	MTL STUD	1-LAYER
D	1-LAYER	MTL STUD	NONE
E	1-LAYER (PLY.WD)	MTL STUD	NONE
F	1-LAYER	MTL STUD	NONE
G	1-LAYER	NONE	NONE
H	1-LAYER	MTL STUD	NONE
J	2-LAYERS	MTL STUD	LINER PANEL
K	1-LAYER	(2) MTL STUDS	1-LAYER
L	2-LAYERS	(2) MTL STUDS	2-LAYERS

TABLE B- FRAMING DEPTH SCHEDULE

TAG NUMBER DESIGNATION	MTL STUD DEPTH	MTL C-H STUD DEPTH	WOOD STUD DEPTH
-	NO FRAMING		
0	7/8" FURRING CHANNEL		N/A
1	1 5/8"	N/A	N/A
2	2 1/2"	2 1/2"	N/A
3	3 5/8"	N/A	N/A
4	4"	4"	3 1/2"
6	6"	6"	5 1/2"
8	8"	N/A	N/A
10	10"	N/A	N/A

TABLE C- MASONRY WIDTH SCHEDULE

TAG NUMBER DESIGNATION	CMU WIDTH
4	3 5/8"
6	5 5/8"
8	7 5/8"
10	9 5/8"
12	11 5/8"

TABLE D - PARTITION HEIGHT DESIGNATOR

TAG NUMBER DESIGNATION	PARTITION HEIGHT
A	FROM SLAB TO STRUCTURE ABOVE
B	FROM SLAB TO STRUCTURE ABOVE W/ BATT
C	FROM SLAB TO 6" ABOVE SCHEDULED CEILING
D	FROM SLAB TO 6" ABOVE SCHEDULED CEILING W/ BATT
E	FROM SLAB TO SCHEDULED CEILING
F	FROM SLAB TO SCHEDULED CEILING W/ BATT
G	PARTIAL HEIGHT REFER TO DETAILS

STEEL SHEET THICKNESS FOR STUDS AND RUNNERS


GUAGE*	MIN. STEEL BASE METAL THICKNESS (UNCOATED)		
	INCH	MILS	MM
12	0.1017	97	X
14	0.0713	68	X
16	0.0566	54	1.34
18	0.0451	43	1.09
20	0.0312	30	0.84
22	0.0270	27	0.68
25	0.0179	18	0.45

*GUAGE 16,18 USED FOR STRUCTURAL FRAMING; 20, 22, AND 25 USED FOR NON-STRUCTURAL FRAMING
*USE OF DIMPLED STEEL STUDS ACCEPTABLE PROVIDED CONTRACTOR SUPPLIES DOCUMENTATION PROVING THE EQUIVALENT MINIMUM BASE METAL THICKNESS IS ACHIEVED

GENERAL NOTES - PARTITIONS


A. REFERENCE SPECIFICATIONS FOR ALL STUD GAUGES AND LIMITING HEIGHTS
B. ALL PARTITIONS CONTAINING PLUMBING OR HAVING AN EXT. FACE SHALL BE INSULATED.
C. ALL ELEC /MECH ROOMS AND A/V EQUIPMENT / LIGHTING ROOMS, SHALL HAVE THEIR PERIMETER PARTITIONS INSULATED USING MINERAL WOOL
D. ALL OFFICES AND TOILET ROOMS SHALL HAVE THEIR PERIMETER PARTITIONS INSULATED WITH SOUND ATTENUATION BATTS AS SPECIFIED.
E. ALL RATED PARTITIONS TO EXTEND FROM TOP OF SLAB TO UNDERSIDE OF STRUCTURE. SEAL TOP AND BOTTOM, TYP.
F. ALL INT. ROOF DRAINS AND OVERFLOW DRAINS TO BE WRAPPED CONTINUOUSLY WITH SOUND ATTEN. BATT
G. 'UNDERSIDE OF STRUCTURE' INDICATED AT HEAD CONDITION DETAIL IS DIAGRAMMATIC ONLY, AND DOES NOT INDICATE EXACT CONSTRUCTION CONDITIONS.
H. INSTALL FRAMING AND GYPSUM BOARD TO OFFSET AROUND STRUCTURAL MEMBERS OR OTHER OBSTRUCTIONS TO MAINTAIN FIRE RESISTIVE RATINGS.
I. WHERE GYPSUM BOARD EXTENDS TO THE UNDERSIDE OF STRUCTURE, STOP GYPSUM BOARD 1/2" BELOW THE LINE OF STRUCTURE AND SEAL AS REQUIRED.
J. FIRE RESISTANT, RATED PARTITIONS TO BE INSTALLED WITH FIRESTOP SEALANT, U.N.O.
K. NON-RATED PARTITIONS TO BE INSTALLED WITH ACOUSTICAL SEALANT, U.N.O.
L. REFER TO MECHANICAL DRAWINGS FOR DETAILS ON PIPE PENETRATIONS THROUGH ACOUSTICAL PARTITIONS AS WELL AS RATED PARTITIONS.
M. INSTALL FIRE RETARDANT, TREATED BLOCKING IN PARTITIONS AS REQD ON DRAWINGS.
N. ALL PARTITIONS SCHEDULED TO RECEIVE TILE OR FRP, SHALL BE CONSTRUCTED OF WATER-RESISTANT CORE GYPSUM WALL BOARD.
O. PER MOLD PREVENTION GUIDELINES, DO NOT INSTALL GYP. BD IN DIRECT CONTACT WITH THE FLOOR. ALL PARTITIONS SHALL BE SHIMMED 1/2" OFF THE FLOOR WITH PLASTIC NON-POROUS SHIMS. GYP. BD WALL SHIMS ARE NOT ACCEPTABLE.

PARTITION HEAD DETAILS

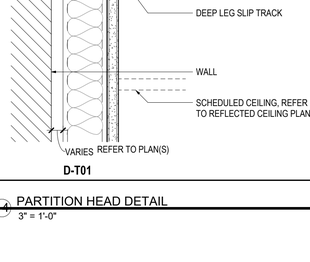


A-T01

PARTITION BASE DETAILS

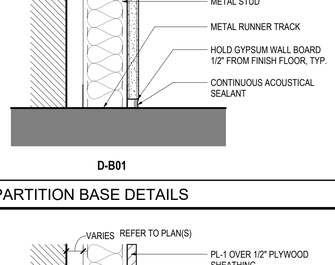

B-B01

PARTITION SERIES - B

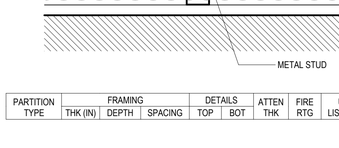

PARTITION TYPE	FRAMING			DETAILS		ATTEN THK	FIRE RTG	UL LISTING	STC RTG
	THK (IN)	DEPTH	SPACING	TOP	BOT				

PARTITION HEAD DETAILS

C-T01

PARTITION BASE DETAILS

C-B01

PARTITION SERIES - C

PARTITION TYPE	FRAMING			DETAILS		ATTEN THK	FIRE RTG	UL LISTING	STC RTG
	THK (IN)	DEPTH	SPACING	TOP	BOT				

PARTITION HEAD DETAILS

D-T02

D-T01

PARTITION BASE DETAILS

D-B01

PARTITION SERIES - D

PARTITION TYPE	FRAMING			DETAILS		ATTEN THK	FIRE RTG	UL LISTING	STC RTG
	THK (IN)	DEPTH	SPACING	TOP	BOT				

PARTITION HEAD DETAILS

15 PARTITION HEAD DETAIL
3" = 1'-0"

14 PARTITION HEAD DETAIL
3" = 1'-0"

PARTITION BASE DETAILS

E-B01

PARTITION SERIES - E

PARTITION TYPE	FRAMING			DETAILS		ATTEN THK	FIRE RTG	UL LISTING	STC RTG
	THK (IN)	DEPTH	SPACING	TOP	BOT				

PRAXIS3
100 Peachtree St NW
Suite 1450
Atlanta, GA 30303
404-875-4500 tel
www.praxis3.com

STATE OF GEORGIA
STUART M. ROMM
07/02/26
CERTIFICATE NO. 3457
REGISTERED ARCHITECT

Copyright (c) 2026 Praxis3, LLC

All reports, plans, specifications, computer files, field data, notes and other documents and instruments prepared by Praxis3 shall retain all common law, statutory and other reserved rights, including copyright thereto.

This drawing may not be reproduced in whole or in part without written permission of Praxis3. It is to be returned upon request. Scales as stated are valid on the original drawings.

Rev	Date	Comments
	07/02/2026	PERMIT SET

Client:
FIFTH THIRD BANK

Project Number: 26302
Project Name:
WATSON BLVD.


2711 WATSON BOULEVARD
WARNER ROBINS, GA 31093

Key Plan:


Sheet Title:
INTERIOR PARTITION SCHEDULE & DETAILS

Sheet Number:
A-620

7/8/2026 2:38:52 PM

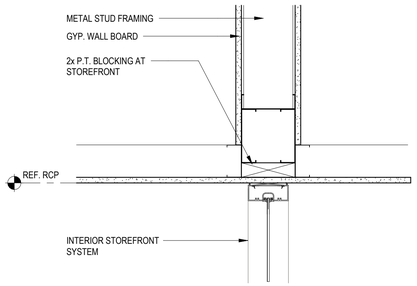


CEILING DETAIL AT INTERIOR STOREFRONT | 1 1/2" = 1'-0" | 8

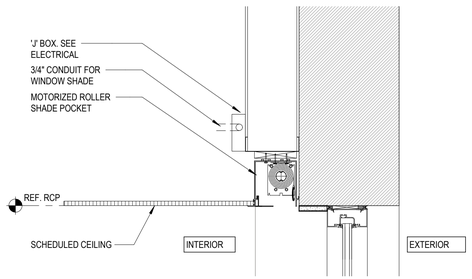


NOTE: STANDARD MECHOSHADE MOTOR (3 WIRE, 120Vac UP / 120Vav DOWN / NEUTRAL FLOATING CONTROL SHADE MOTOR). GC COORDINATE CONTROL REQUIREMENTS WITH OWNER IOT VENDOR

TYPICAL MECHOSHADE DETAIL | 1 1/2" = 1'-0" | 7

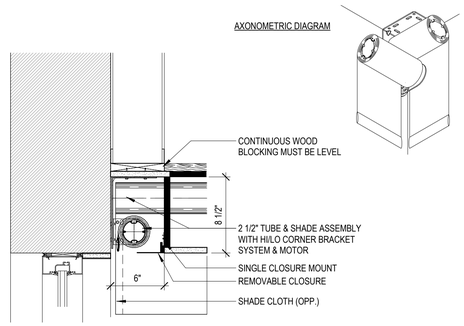


NOTE: STANDARD MECHOSHADE MOTOR (3 WIRE, 120vac UP / 120Vav DOWN / NEUTRAL FLOATING CONTROL SHADE MOTOR). GC COORDINATE CONTROL REQUIREMENTS WITH OWNER IOT VENDOR


MECHOSHADE CORNER DETAIL | 1 1/2" = 1'-0" | 6

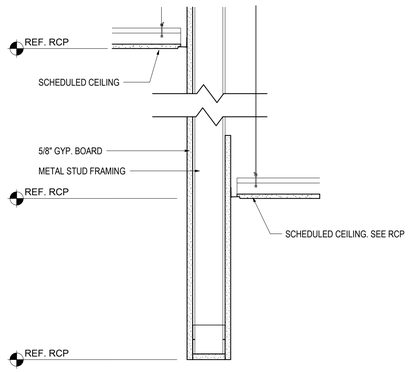


TYPICAL BULKHEAD DETAIL | 1 1/2" = 1'-0" | 5

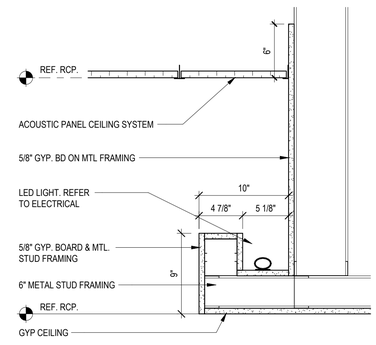


CEILING DETAIL | 1 1/2" = 1'-0" | 4

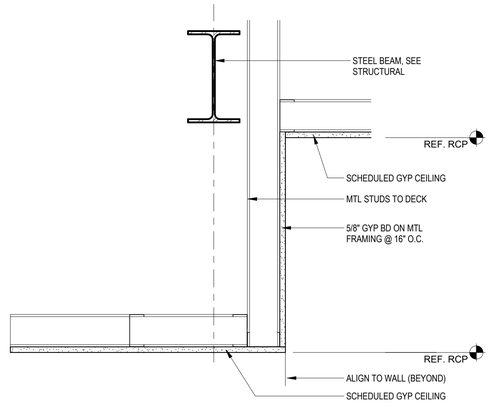

CLOUD CEILING SECTION | 1 1/2" = 1'-0" | 3

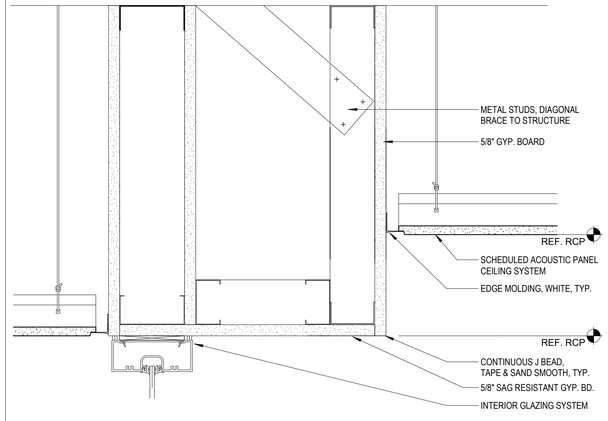

CEILING TILE TO GYP. SOFFIT | 3" = 1'-0" | 2

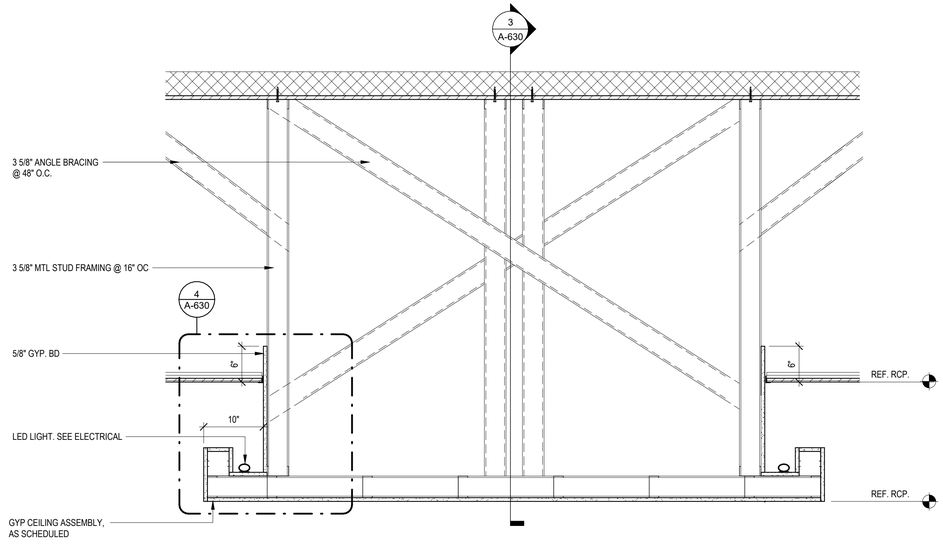

CLOUD CEILING SECTION | 1" = 1'-0" | 1

PRAXIS3

100 Peachtree St NW
Suite 1450
Atlanta, GA 30303
404-875-4500 tel
www.praxis3.com

STATE OF GEORGIA
STUART M. ROMM
07/02/26
CERTIFICATE NO. 34511
REGISTERED ARCHITECT

Copyright (c) 2026 Praxis3, LLC

All reports, plans, specifications, computer files, field data, notes and other documents and instruments prepared by Praxis3 shall retain all common law, statutory and other reserved rights, including copyright thereto.

This drawing may not be reproduced in whole or in part without written permission of Praxis3. It is to be returned upon request. Scales as stated are valid on the original drawings.

Rev	Date	Comments
	07/02/2026	PERMIT SET

Client:
FIFTH THIRD BANK

Project Number: 26302
Project Name:
WATSON BLVD.


2711 WATSON BOULEVARD
WARNER ROBINS, GA 31093

Key Plan:


Sheet Title:
CEILING DETAILS

Sheet Number:
A-630


7/8/2026 2:38:53 PM

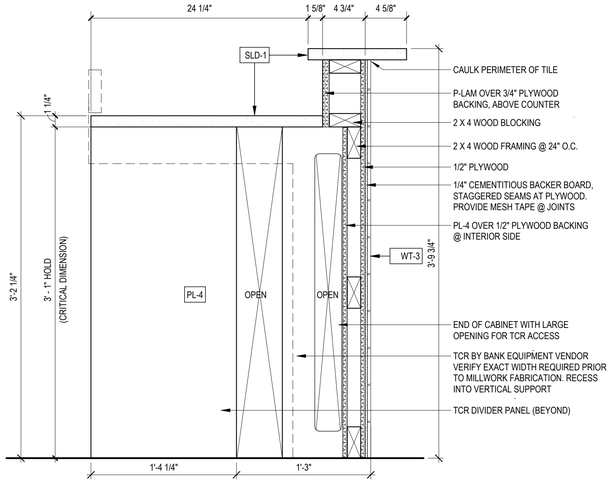


TRANSACTION BAR MILLWORK DETAIL | 1 1/2" = 1'-0" | 9

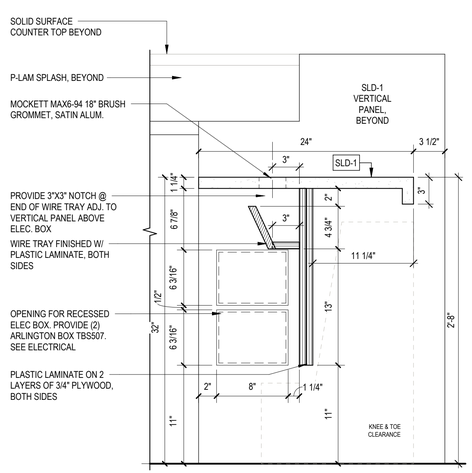


MILLWORK DETAIL | 1 1/2" = 1'-0" | 8

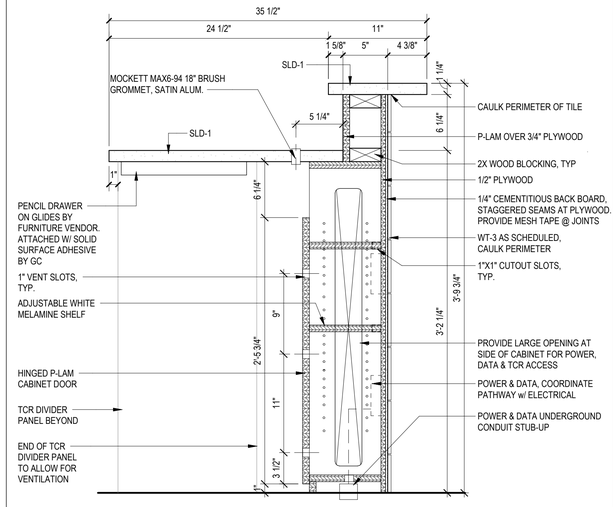


TRANSACTION BAR MILLWORK DETAIL | 1 1/2" = 1'-0" | 7

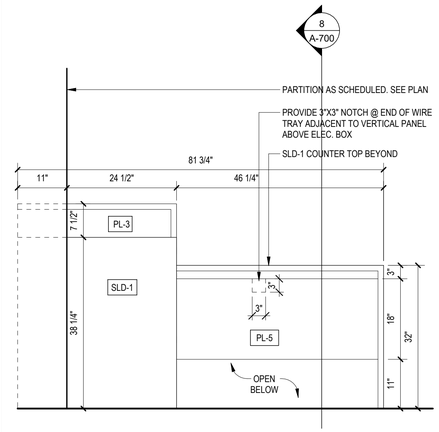


TRANSACTION BAR - ELEVATION | 3/4" = 1'-0" | 6

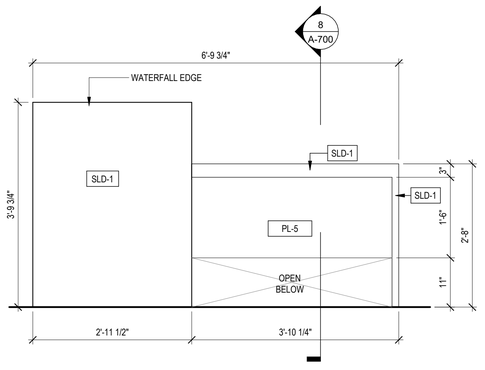


TRANSACTION BAR - SIDE ELEV | 3/4" = 1'-0" | 5

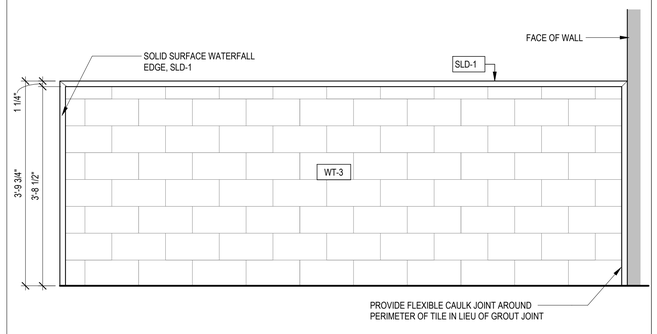


TRANSACTION BAR - FRONT ELEVATION | 3/4" = 1'-0" | 4

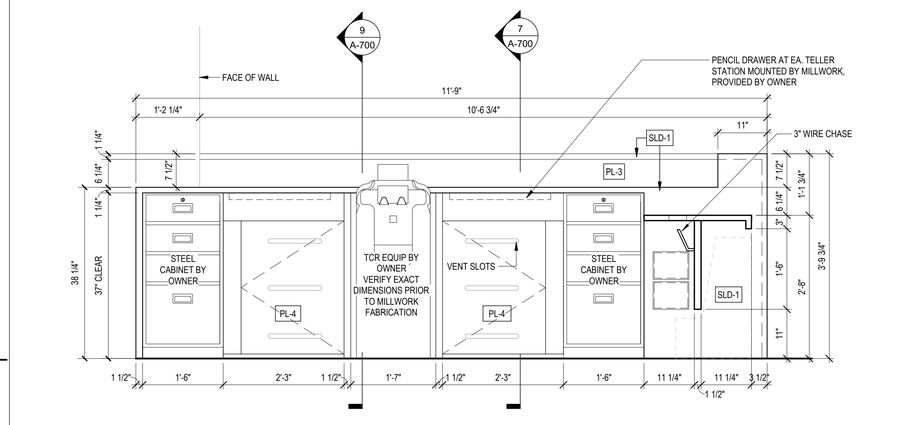

TRANSACTION BAR - BACK ELEVATION | 3/4" = 1'-0" | 3

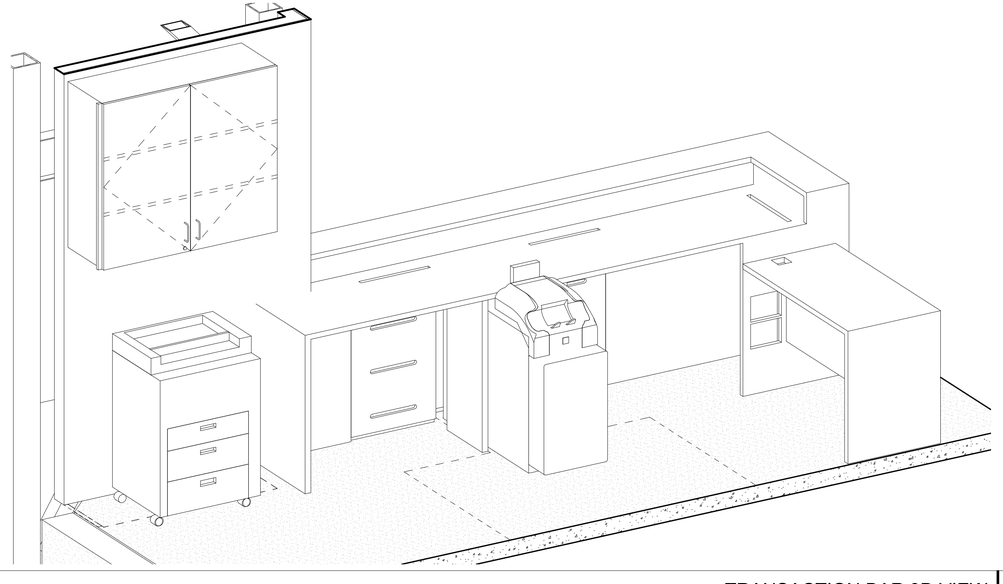

TRANSACTION BAR 3D VIEW | NTS | 2

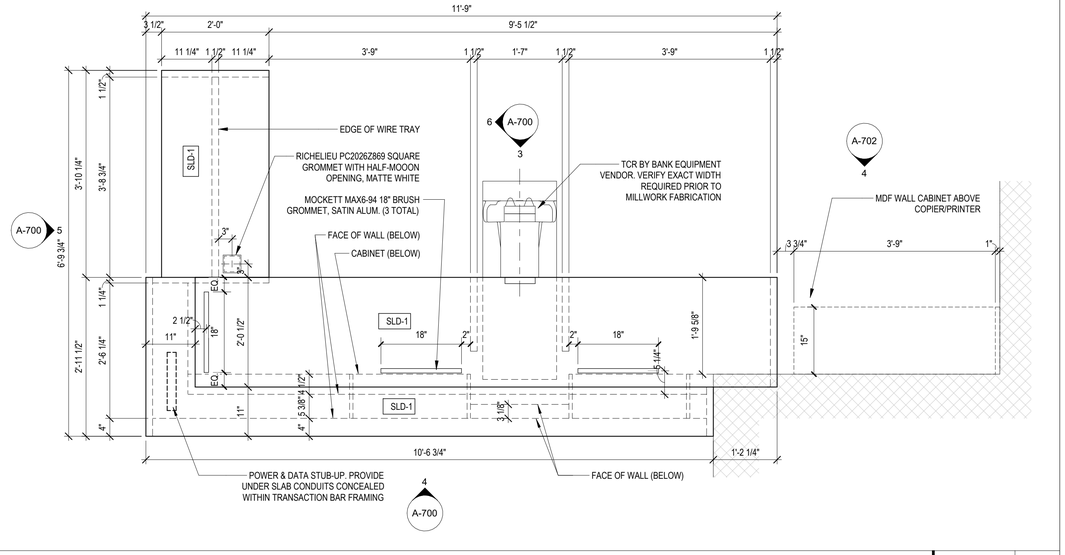

TRANSACTION BAR PLAN | 3/4" = 1'-0" | 1

7/8/2026 2:38:54 PM

PRAXIS3

100 Peachtree St NW
Suite 1450
Atlanta, GA 30303
404-875-4500 tel
www.praxis3.com

STATE OF GEORGIA
STUART M. ROMM
07/02/26
CERTIFICATE NO. 3457
REGISTERED ARCHITECT

Copyright (c) 2026 Praxis3, LLC

All reports, plans, specifications, computer files, field data, notes and other documents and instruments prepared by Praxis3 shall retain all common law, statutory and other reserved rights, including copyright thereto.

This drawing may not be reproduced in whole or in part without written permission of Praxis3. It is to be returned upon request. Scales as stated are valid on the original drawings.

Rev	Date	Comments
	07/02/2026	PERMIT SET

Client:
FIFTH THIRD BANK


Project Number: 26302
Project Name:
WATSON BLVD.

2711 WATSON BOULEVARD
WARNER ROBINS, GA 31093


Key Plan:

Sheet Title:
TRANSACTION BAR - ENLARGED PLAN & DETAILS


Sheet Number:
A-700

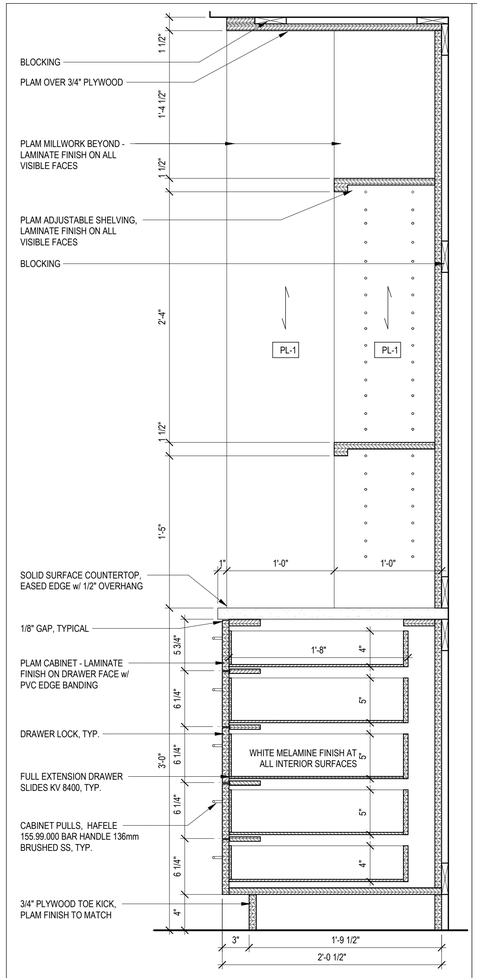


MILLWORK SECTION | 1 1/2" = 1'-0" | 9

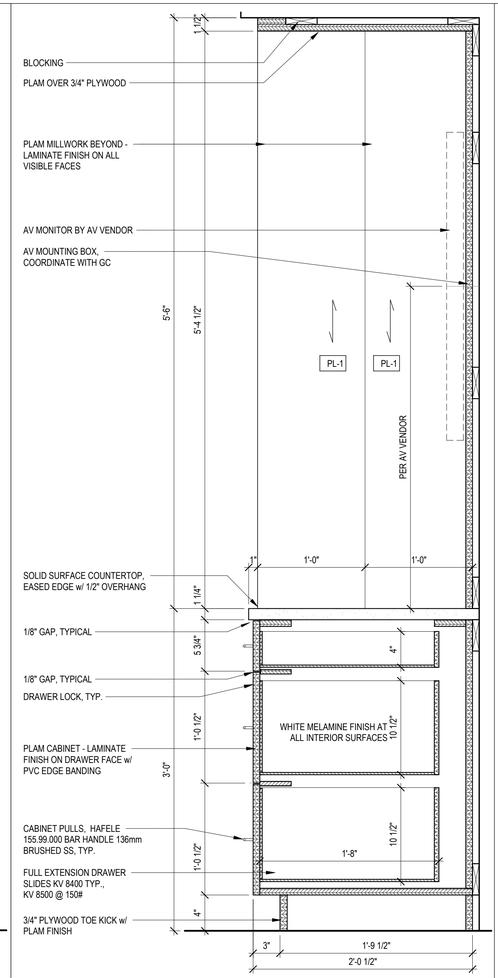


MILLWORK SECTION | 1 1/2" = 1'-0" | 7

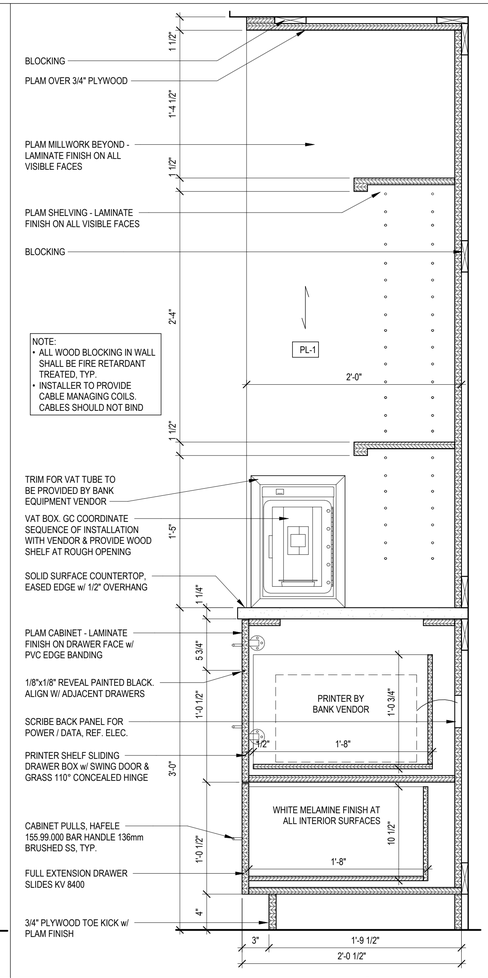


MILLWORK SECTION | 1 1/2" = 1'-0" | 5

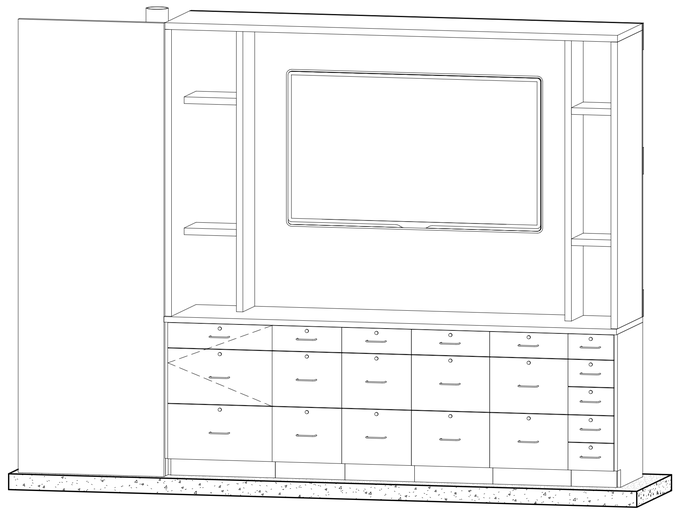


BACK COUNTER AXONOMETRIC VIEW | NTS | 3

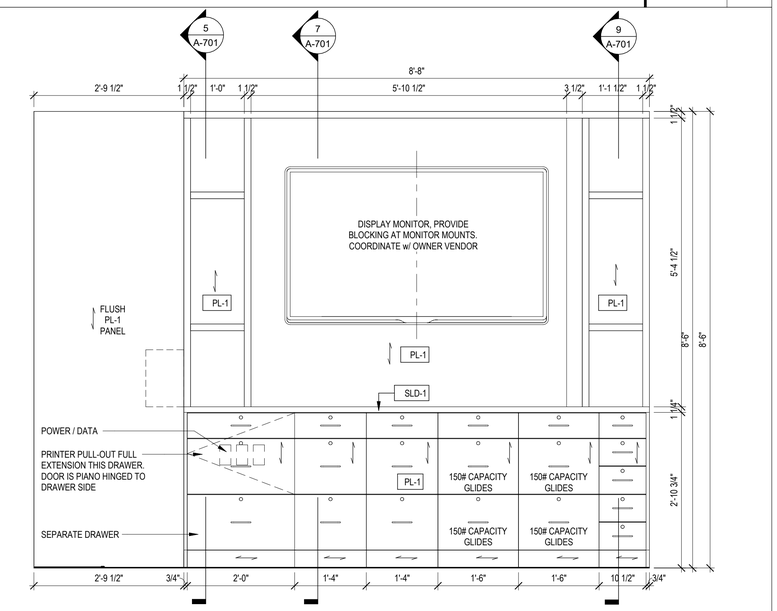


BACK COUNTER - MILLWORK ELEVATION | 3/4" = 1'-0" | 2

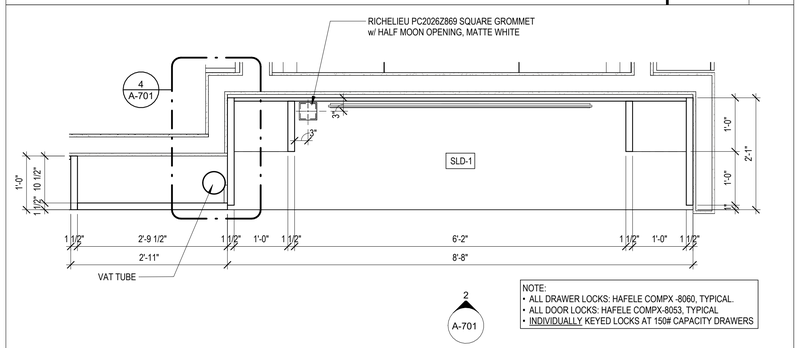

BACK COUNTER - MILLWORK PLAN | 3/4" = 1'-0" | 1

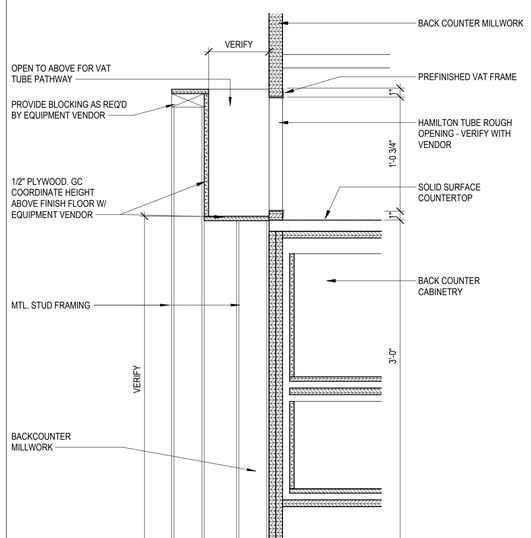


SECTION AT VAT | 1 1/2" = 1'-0" | 8

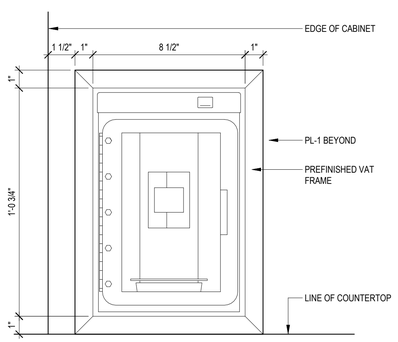

NOTE: SINGLE SIDED VAT TUBE BY BANK VENDOR.
G.C. FURNISH - PREFINISHED, MITERED BLACK ANGLED ALUMINUM VAT FRAME AROUND VAT TERMINAL OPENING.
G.C. COORDINATE OPENING SIZE & LOCATION W/ BANK VENDOR

VAT ACCESS ELEVATION | 3" = 1'-0" | 6

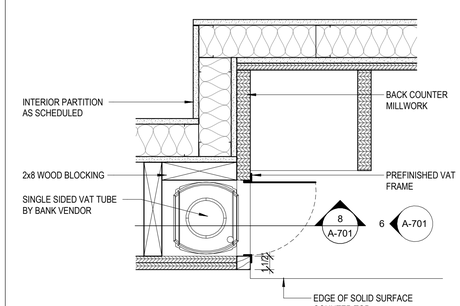

PLAN DETAIL AT VAT TUBE | 1 1/2" = 1'-0" | 4

PRAXIS3
100 Peachtree St NW
Suite 1450
Atlanta, GA 30303
404-875-4500 tel
www.praxis3.com

STATE OF GEORGIA
STUART M. ROMM
07/02/26
CERTIFICATE NO. 3457
REGISTERED ARCHITECT

Copyright (c) 2026 Praxis3, LLC

All reports, plans, specifications, computer files, field data, notes and other documents and instruments prepared by Praxis3 shall retain all common law, statutory and other reserved rights, including copyright thereto.

This drawing may not be reproduced in whole or in part without written permission of Praxis3. It is to be returned upon request. Scales as stated are valid on the original drawings.

Rev	Date	Comments
	07/02/2026	PERMIT SET

Client:
FIFTH THIRD BANK

Project Number: 26302
Project Name:
WATSON BLVD.


2711 WATSON BOULEVARD
WARNER ROBINS, GA 31093

Key Plan:


Sheet Title:
BACK COUNTER - ENLARGED PLAN & DETAILS

Sheet Number:
A-701


7/8/2026 2:38:56 PM

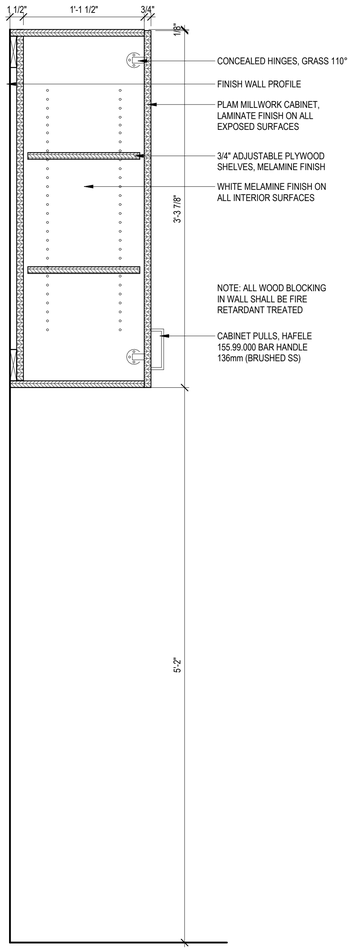

MFD SECTION | 1 1/2" = 1'-0" | 8

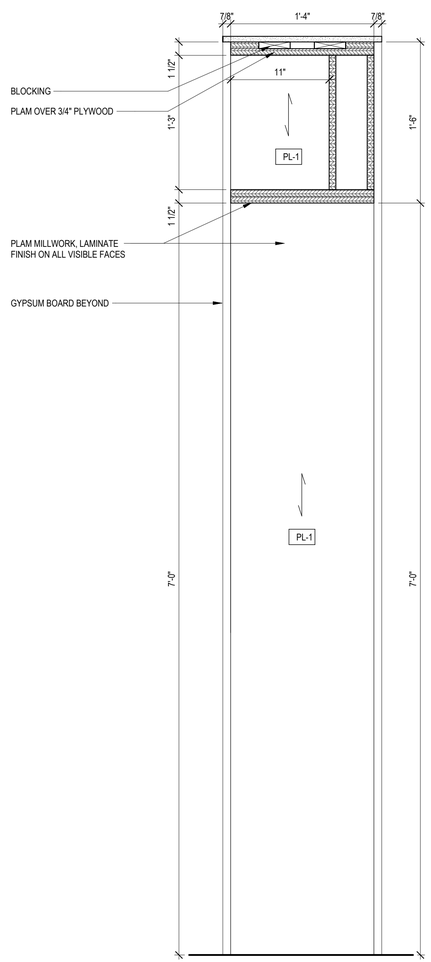

MILLWORK DETAIL | 1 1/2" = 1'-0" | 7

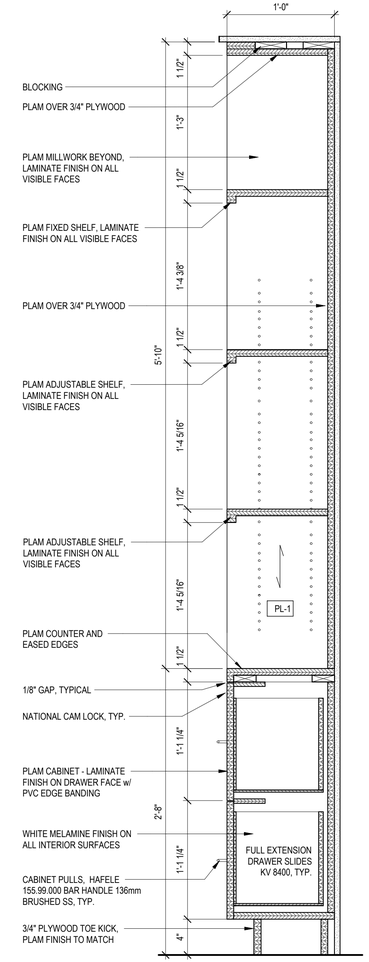


MILLWORK DETAIL | 1 1/2" = 1'-0" | 5




LIBRARY | NTS | 3


NOTE:
PROVIDE LOCKS ON ALL CABINETS.
ALL LOCKS TO BE KEYED THE SAME

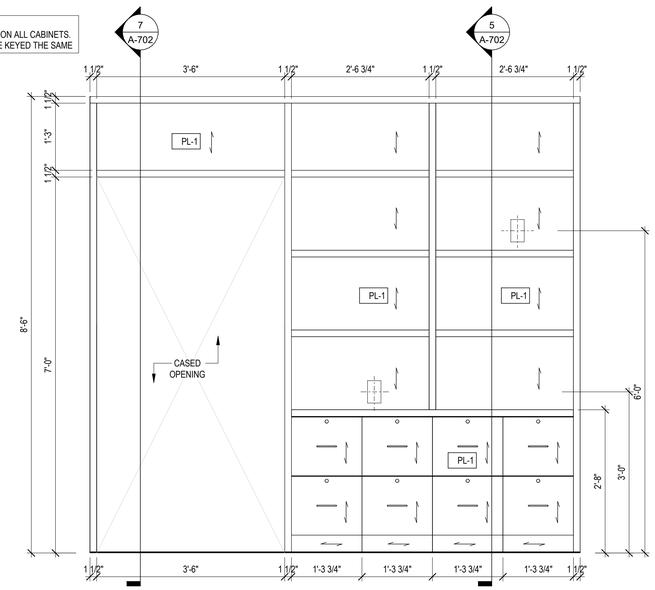


FT_A702_LIBRARY - MILLWORK ELEVATION | 3/4" = 1'-0" | 2

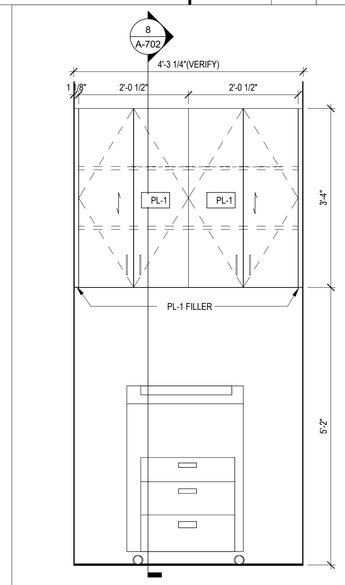

CABINET @ BOOTH | 3/4" = 1'-0" | 6

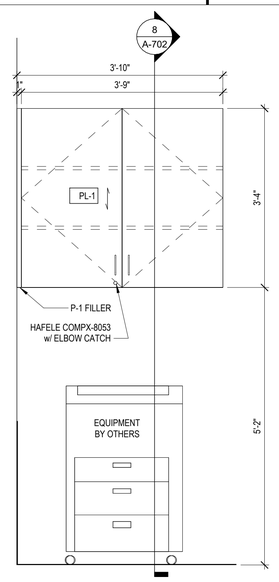

CABINET @ TRANSACTION | 3/4" = 1'-0" | 4

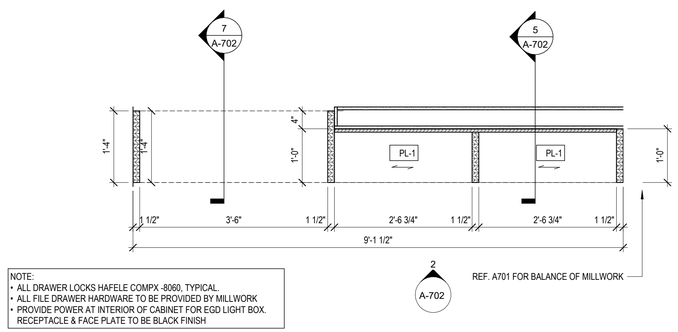

NOTE:
- ALL DRAWER LOCKS HAFELE COMPX -8060, TYPICAL.
- ALL FILE DRAWER HARDWARE TO BE PROVIDED BY MILLWORK
- PROVIDE POWER AT INTERIOR OF CABINET FOR EGD LIGHT BOX. RECEPTACLE & FACE PLATE TO BE BLACK FINISH

INDICATES GRAIN DIRECTION

LIBRARY - MILLWORK PLAN | 3/4" = 1'-0" | 1

PRAXIS3

100 Peachtree St NW
Suite 1450
Atlanta, GA 30303
404-875-4500 tel
www.praxis3.com

STATE OF GEORGIA
STUART M. ROMM
07/02/26
CERTIFICATE NO. 34521
REGISTERED ARCHITECT

Copyright (c) 2026 Praxis3, LLC

All reports, plans, specifications, computer files, field data, notes and other documents and instruments prepared by Praxis3 shall retain all common law, statutory and other reserved rights, including copyright thereto.

This drawing may not be reproduced in whole or in part without written permission of Praxis3. It is to be returned upon request. Scales as stated are valid on the original drawings.

Rev	Date	Comments
	07/02/2026	PERMIT SET

Client:
FIFTH THIRD BANK

Project Number: 26302
Project Name:
WATSON BLVD.


2711 WATSON BOULEVARD
WARNER ROBINS, GA 31093

Key Plan:


Sheet Title:
LIBRARY - ENLARGED PLAN & DETAILS

Sheet Number:
A-702


7/8/2026 2:38:58 PM

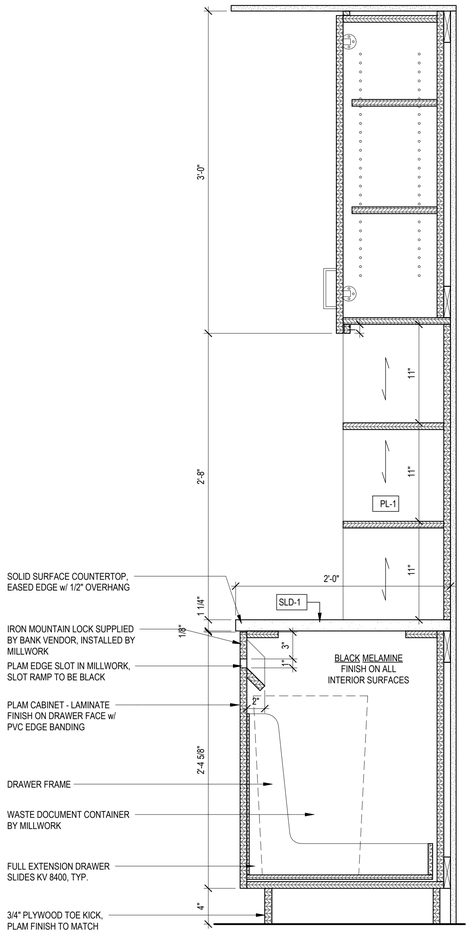


MILLWORK DETAIL | 1 1/2" = 1'-0" | 6

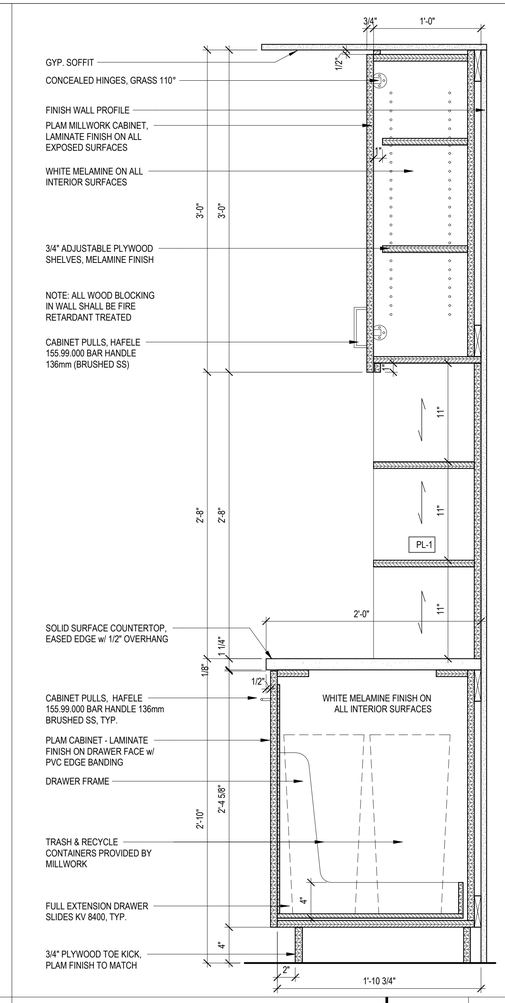


MILLWORK DETAIL | 1 1/2" = 1'-0" | 5

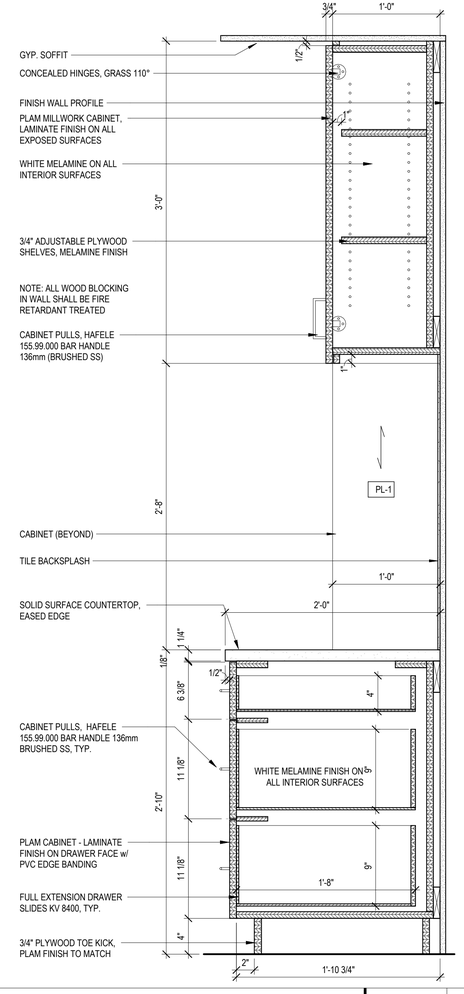


MILLWORK DETAIL | 1 1/2" = 1'-0" | 4

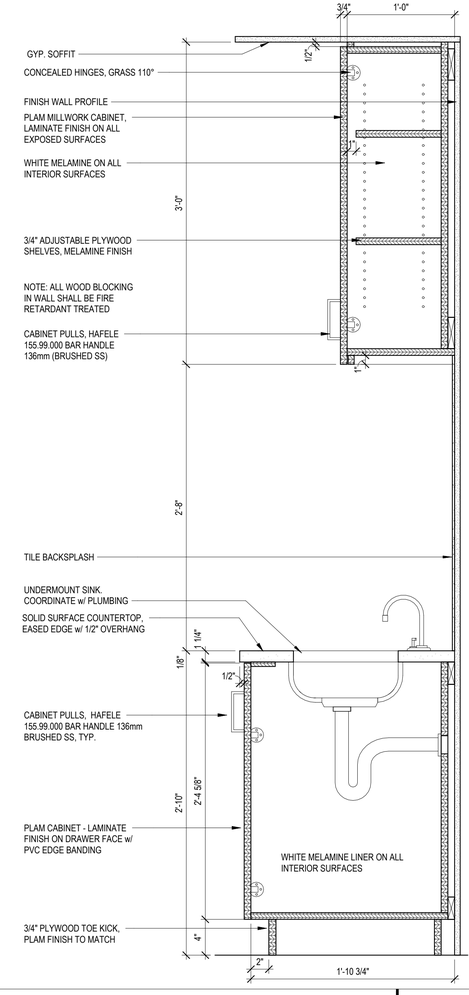


MILLWORK DETAIL | 1 1/2" = 1'-0" | 3

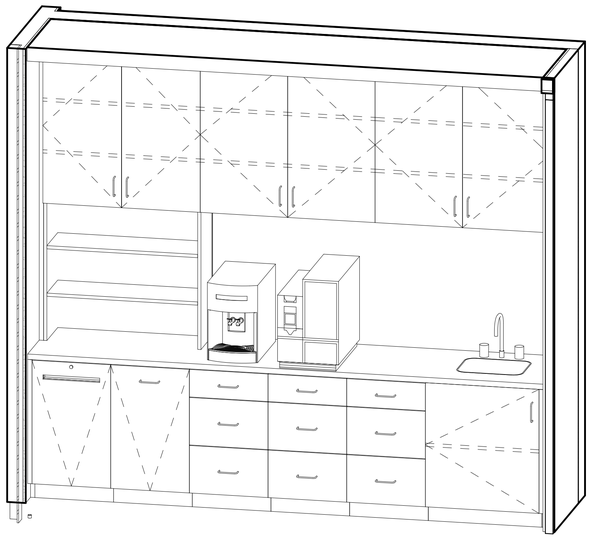

SERVICE COUNTER AXONOMETRIC VIEW | NTS | 7

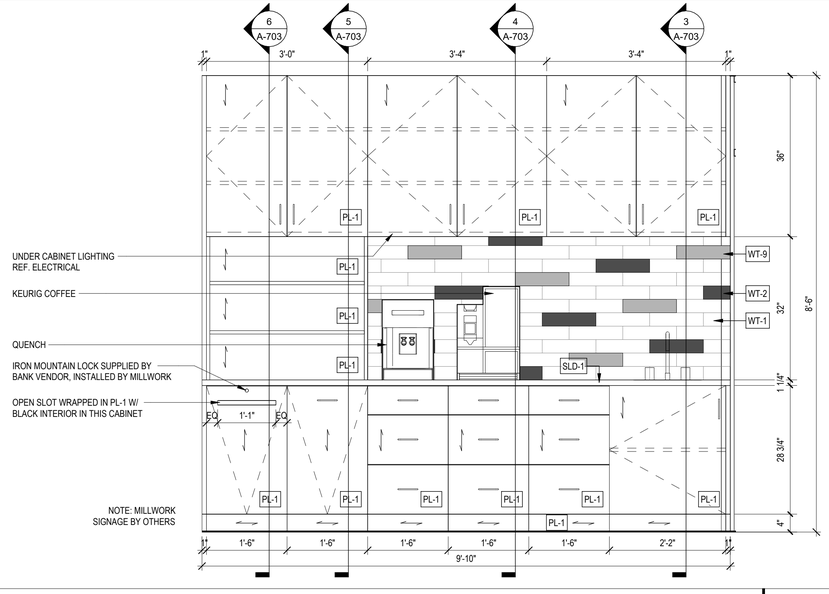

SERVICE COUNTER - MILLWORK ELEVATION | 3/4" = 1'-0" | 2

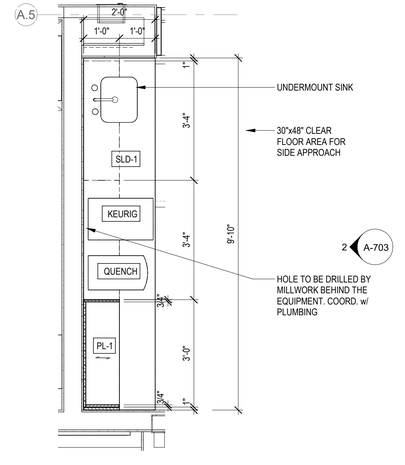

SERVICE COUNTER PLAN | 1/2" = 1'-0" | 1

7/8/2026 2:39:00 PM

PRAXIS3

100 Peachtree St NW
Suite 1450
Atlanta, GA 30303
404-875-4500 tel
www.praxis3.com

STATE OF GEORGIA
STUART M. ROMM
07/02/26
CERTIFICATE NO. 34511
REGISTERED ARCHITECT

Copyright (c) 2026 Praxis3, LLC

All reports, plans, specifications, computer files, field data, notes and other documents and instruments prepared by Praxis3 shall retain all common law, statutory and other reserved rights, including copyright thereto.

This drawing may not be reproduced in whole or in part without written permission of Praxis3. It is to be returned upon request. Scales as stated are valid on the original drawings.

Rev	Date	Comments
	07/02/2026	PERMIT SET

Client:
FIFTH THIRD BANK


Project Number: 26302
Project Name:
WATSON BLVD.

2711 WATSON BOULEVARD
WARNER ROBINS, GA 31093


Key Plan:

Sheet Title:
SERVICE COUNTER - ENLARGED PLAN & DETAILS


Sheet Number:
A-703

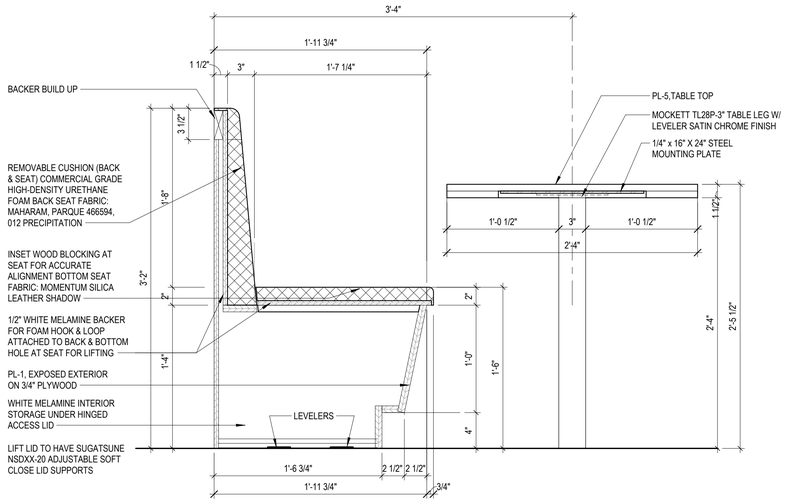


SECTION @ LOUNGE SEATING | 1 1/2" = 1'-0" | 6

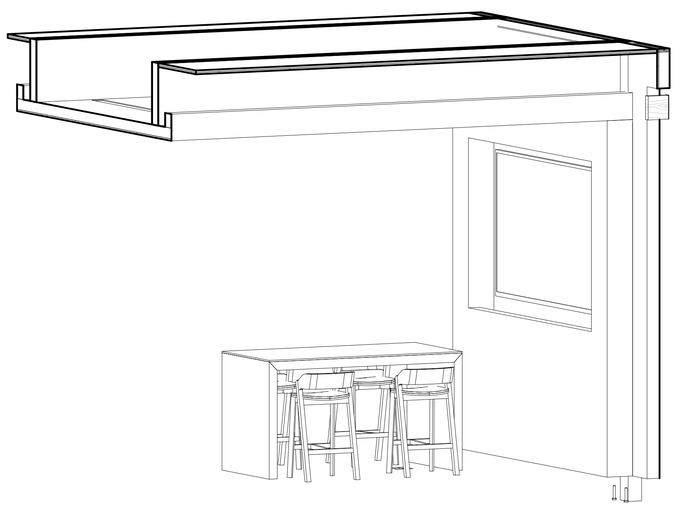


TECH WALL 3D VIEW | NTS | 3

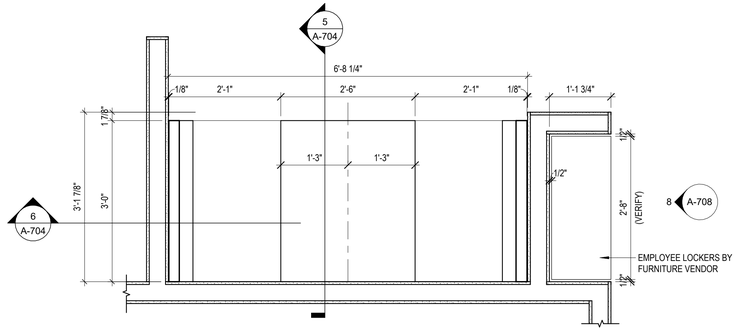


LOUNGE BOOTH PLAN | 3/4" = 1'-0" | 8

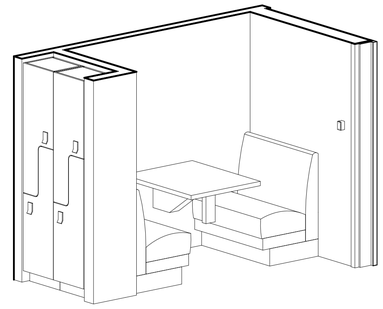


LOUNGE BOOTH 3D VIEW | NTS | 7

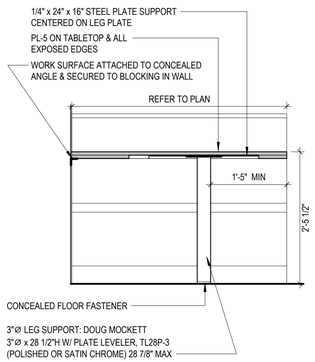


LOUNGE ELEVATION | 3/4" = 1'-0" | 5

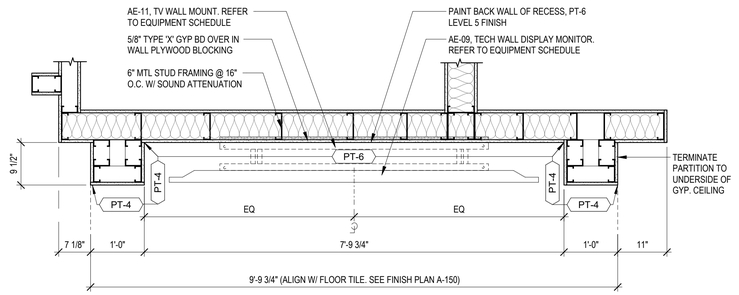

TECH WALL ENLARGED PLAN | 3/4" = 1'-0" | 4

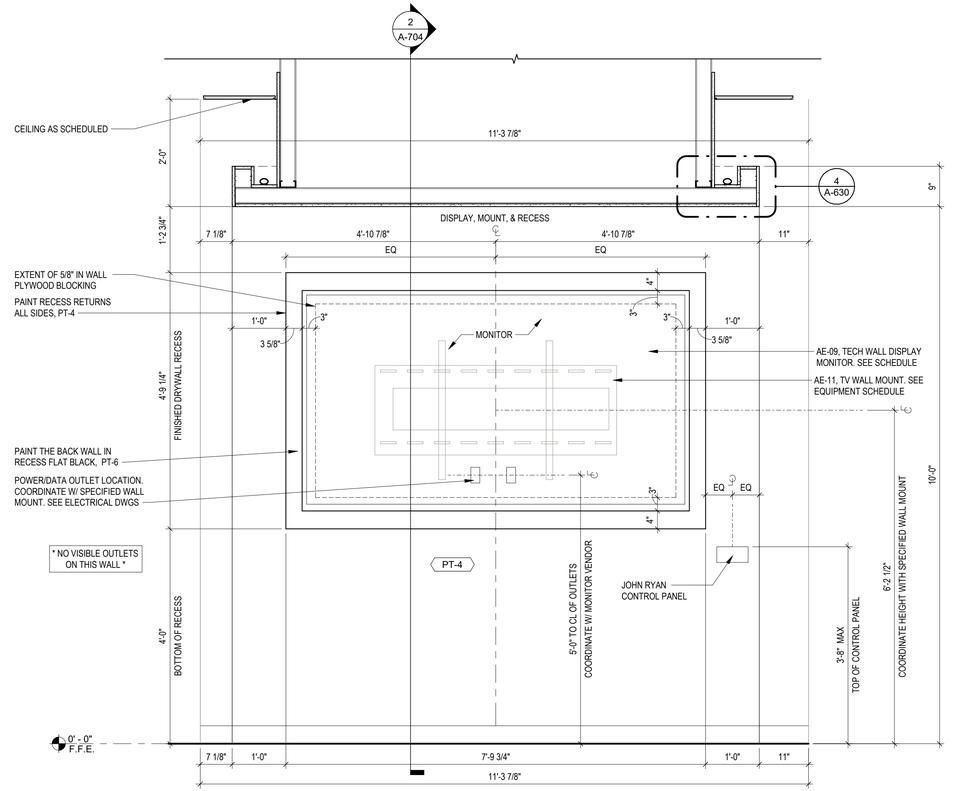

TECH WALL ELEVATION | 3/4" = 1'-0" | 1

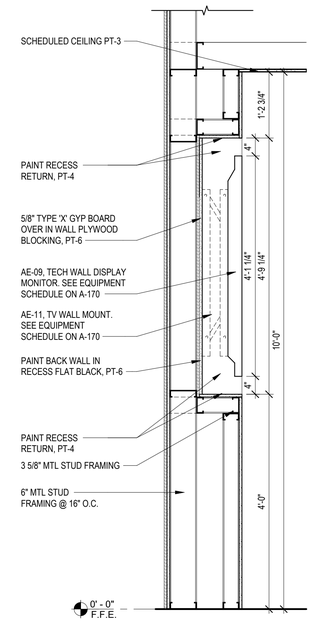

TECH WALL SECTION | 3/4" = 1'-0" | 2

PRAXIS3

100 Peachtree St NW
Suite 1450
Atlanta, GA 30303

404-875-4500 tel
www.praxis3.com

STATE OF GEORGIA
STUART M. ROMM
07/02/26
CERTIFICATE NO. 34511
REGISTERED ARCHITECT

Copyright (c) 2026 Praxis3, LLC

All reports, plans, specifications, computer files, field data, notes and other documents and instruments prepared by Praxis3 shall retain all common law, statutory and other reserved rights, including copyright thereto.

This drawing may not be reproduced in whole or in part without written permission of Praxis3. It is to be returned upon request. Scales as stated are valid on the original drawings.

Rev	Date	Comments
	07/02/2026	PERMIT SET

Client:

FIFTH THIRD BANK

Project Number: 26302
Project Name:

WATSON BLVD.

2711 WATSON BOULEVARD
WARNER ROBINS, GA 31093

Key Plan:


Sheet Title:

TECH WALL & LOUNGE BOOTH - ENLARGED PLAN & DETAILS


Sheet Number:

A-704


7/8/2026 2:39:02 PM

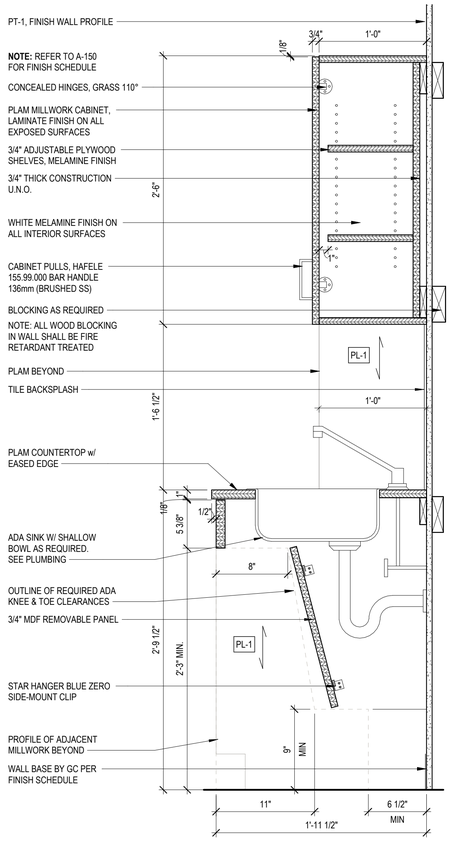


MILLWORK SECTION @ SINK | 1 1/2" = 1'-0" | 7

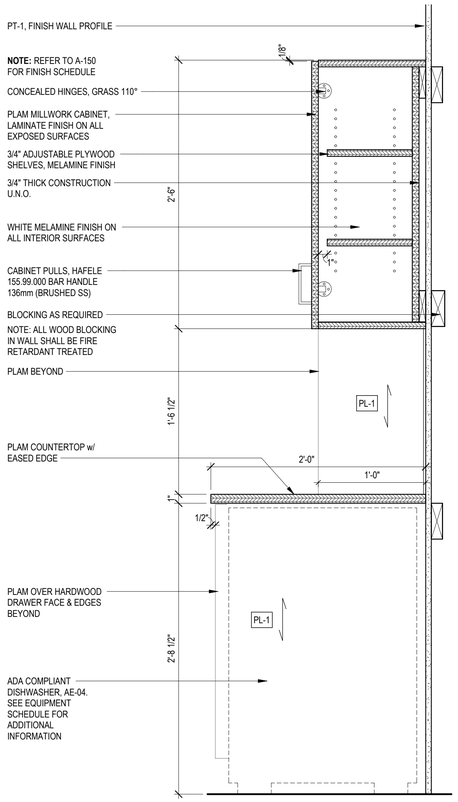


MILLWORK SECT. @ DISHWASHER | 1 1/2" = 1'-0" | 6

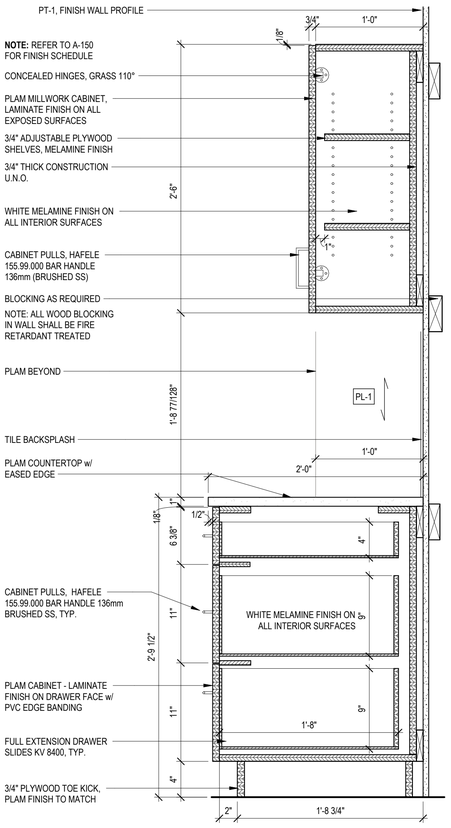


MILLWORK SECTION @ DRAWERS | 1 1/2" = 1'-0" | 5

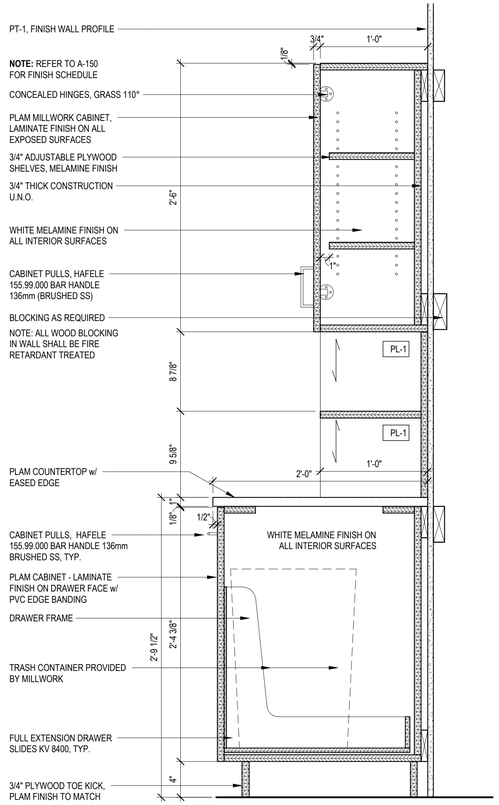


MILLWORK SECTION @ TRASH | 1 1/2" = 1'-0" | 4

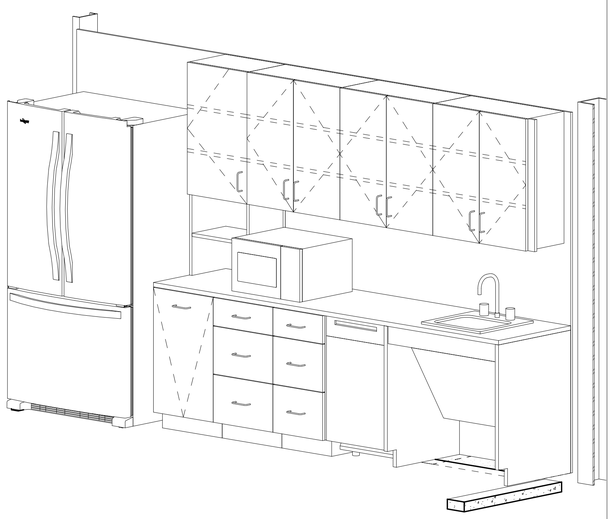

EMPLOYEE LOUNGE 3D VIEW | NTS | 3

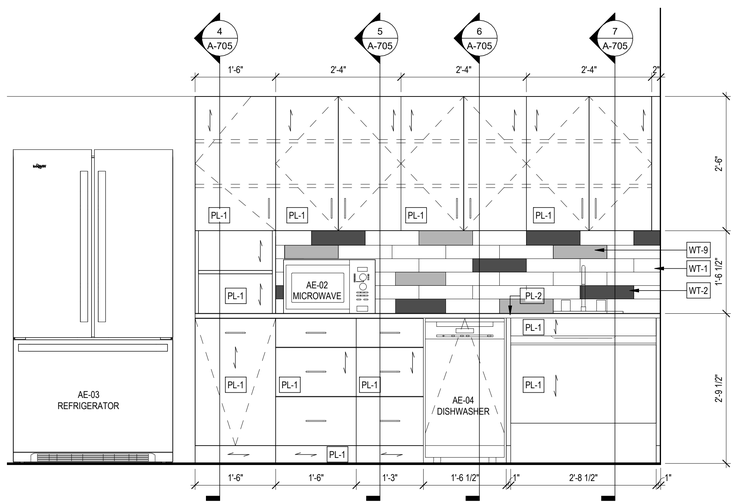

EMPLOYEE LOUNGE ELEVATION | 3/4" = 1'-0" | 2

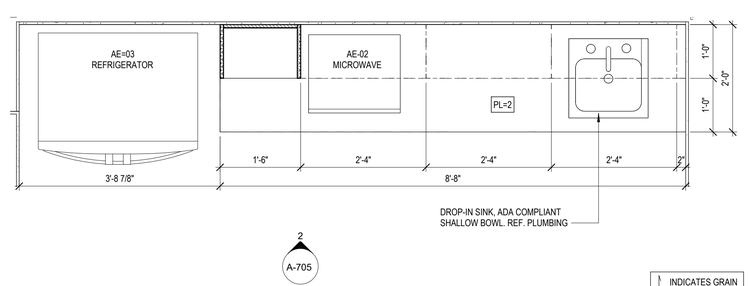

EMPLOYEE LOUNGE PLAN | 3/4" = 1'-0" | 1

7/8/2026 2:39:04 PM

PRAXIS3

100 Peachtree St NW
Suite 1450
Atlanta, GA 30303
404-875-4500 tel
www.praxis3.com

STATE OF GEORGIA
STUART M. ROMM
07/02/26
CERTIFICATE NO. 36511
REGISTERED ARCHITECT

Copyright (c) 2026 Praxis3, LLC

All reports, plans, specifications, computer files, field data, notes and other documents and instruments prepared by Praxis3 shall retain all common law, statutory and other reserved rights, including copyright thereto.

This drawing may not be reproduced in whole or in part without written permission of Praxis3. It is to be returned upon request. Scales as stated are valid on the original drawings.

Rev	Date	Comments
	07/02/2026	PERMIT SET

Client:
FIFTH THIRD BANK


Project Number: 26302
Project Name:
WATSON BLVD.

2711 WATSON BOULEVARD
WARNER ROBINS, GA 31093


Key Plan:

Sheet Title:
EMPLOYEE LOUNGE - ENLARGED PLAN & DETAILS


Sheet Number:
A-705

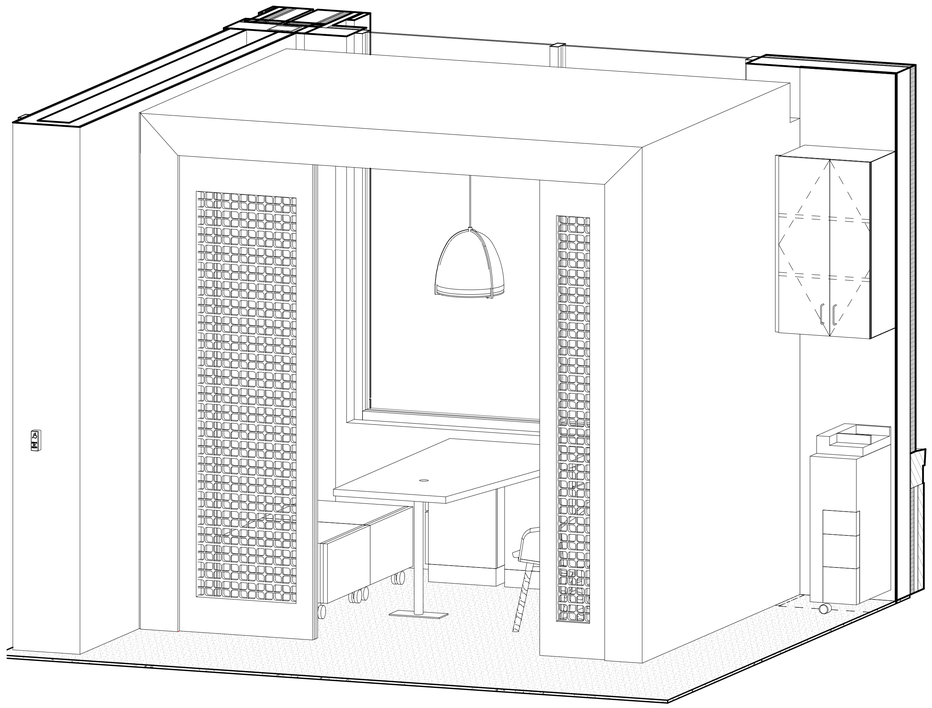


BOOTH 3D VIEW | NTS | 10

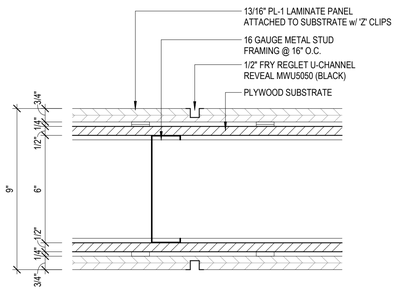


ENLARGED BOOTH DETAIL | 3" = 1'-0" | 9

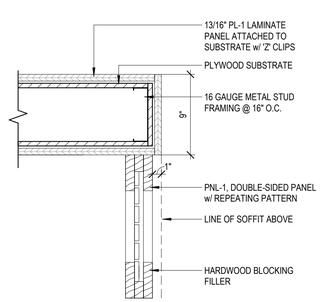


BOOTH - DETAIL | 1 1/2" = 1'-0" | 8

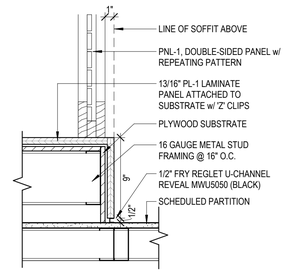

BOOTH - DETAIL | 1 1/2" = 1'-0" | 7

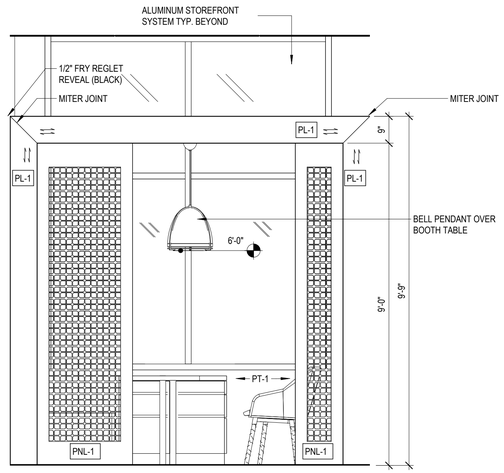


INTERIOR ELEVATION - BOOTH | 1/2" = 1'-0" | 6

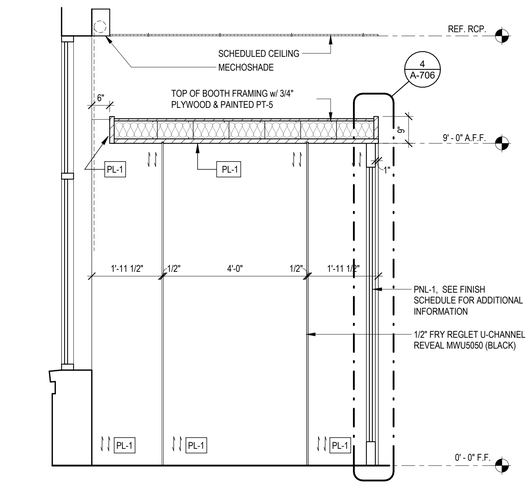


NOTE: ALL SWITCHES & COVER PLATES MOUNTED TO LAMINATE WALL TO BE BLACK FINISH


BOOTH - SECTION | 1/2" = 1'-0" | 5

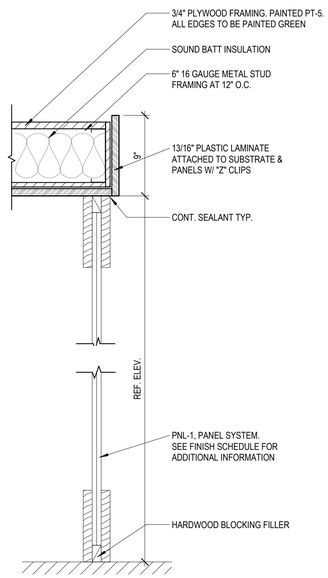


BOOTH - HEAD AND SILL | 1 1/2" = 1'-0" | 4

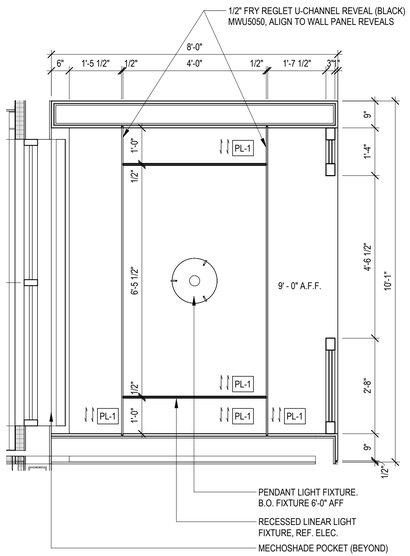

ENLARGED BOOTH CEILING PLAN | 1/2" = 1'-0" | 11

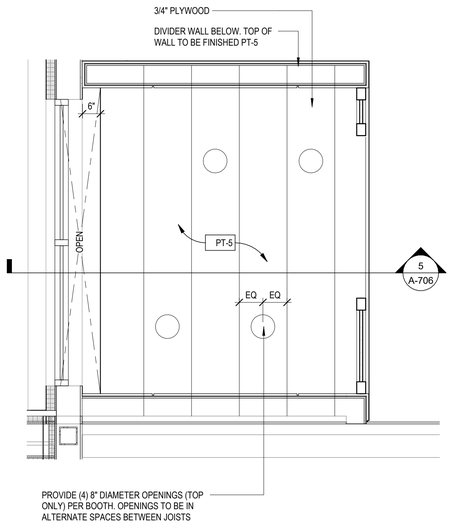

BOOTH ROOF FRAMING PLAN | 1/2" = 1'-0" | 2

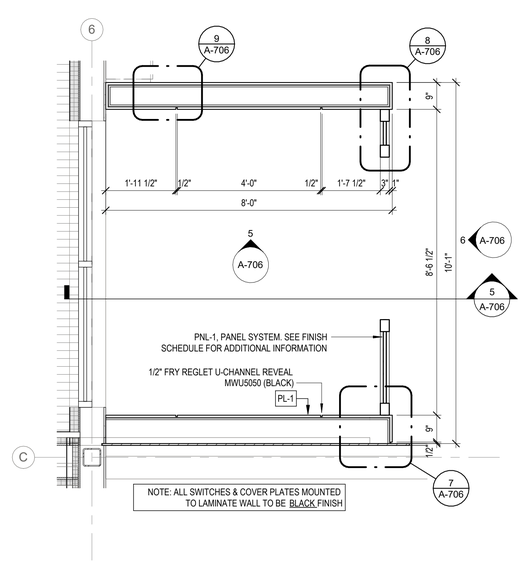

NOTE: ALL SWITCHES & COVER PLATES MOUNTED TO LAMINATE WALL TO BE BLACK FINISH

INDICATES GRAIN DIRECTION

FURNITURE AND EQUIPMENT PLAN | 1/2" = 1'-0" | 1

7/8/2026 2:39:07 PM

PRAXIS3
100 Peachtree St NW
Suite 1450
Atlanta, GA 30303
404-875-4500 tel
www.praxis3.com

STATE OF GEORGIA
STUART M. ROMM
07/02/26
CERTIFICATE NO. 3457
REGISTERED ARCHITECT

Copyright (c) 2026 Praxis3, LLC

All reports, plans, specifications, computer files, field data, notes and other documents and instruments prepared by Praxis3 shall retain all common law, statutory and other reserved rights, including copyright thereto.

This drawing may not be reproduced in whole or in part without written permission of Praxis3. It is to be returned upon request. Scales as stated are valid on the original drawings.

Rev	Date	Comments
	07/02/2026	PERMIT SET

Client:
FIFTH THIRD BANK


Project Number: 26302
Project Name:
WATSON BLVD.

2711 WATSON BOULEVARD
WARNER ROBINS, GA 31093


Key Plan:

Sheet Title:
BOOTH - ENLARGED PLAN & DETAILS


Sheet Number:
A-706

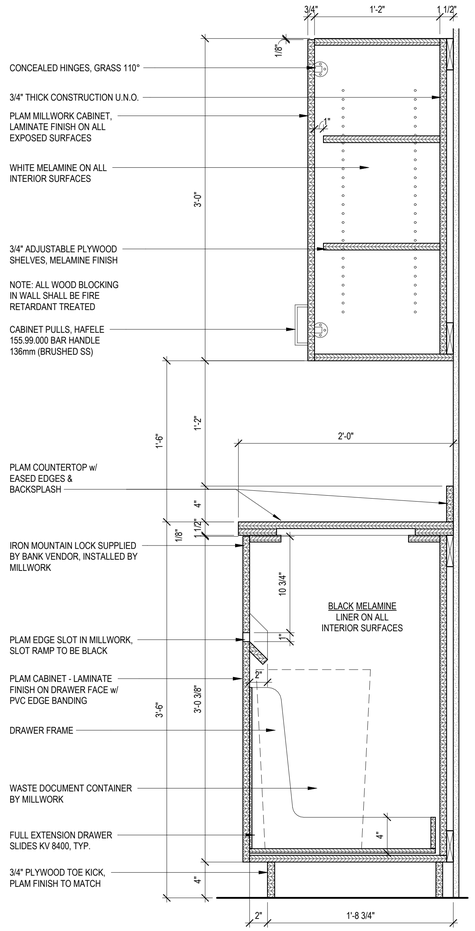


MILLWORK SECTION | 1 1/2" = 1'-0" | 9

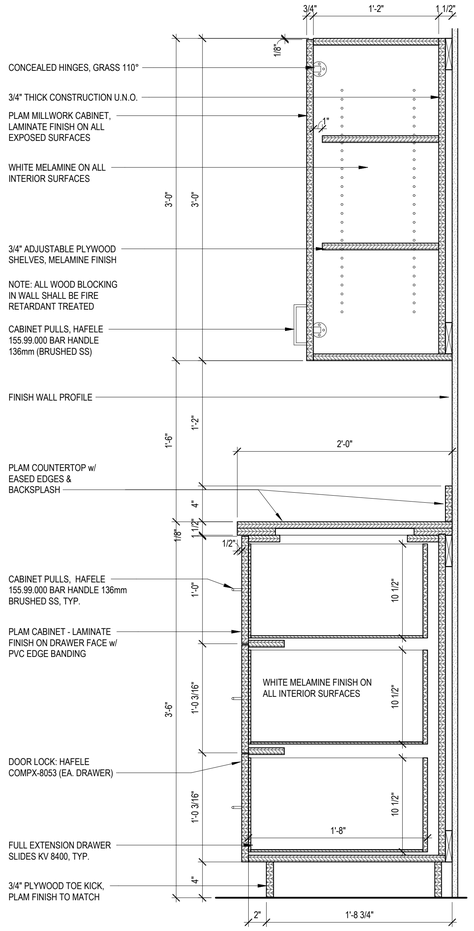


MILLWORK SECTION | 1 1/2" = 1'-0" | 8

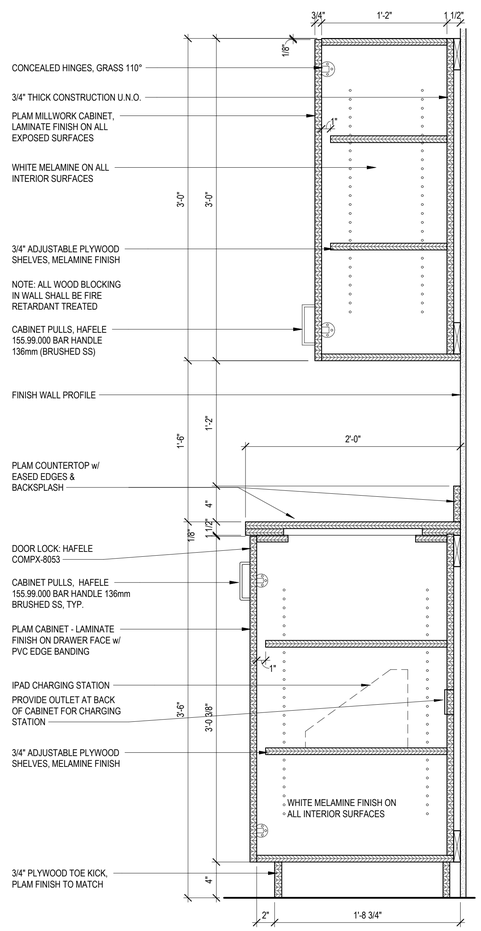


MILLWORK SECTION | 1 1/2" = 1'-0" | 7

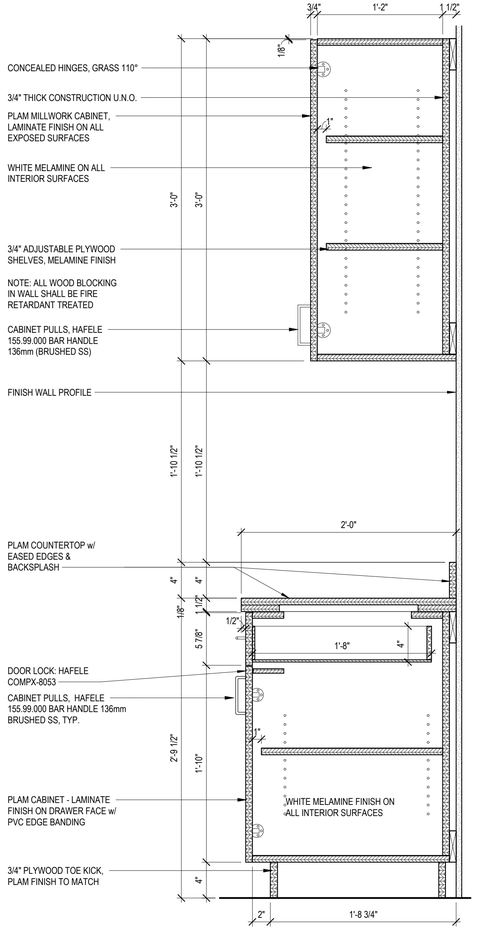


MILLWORK SECTION | 1 1/2" = 1'-0" | 6

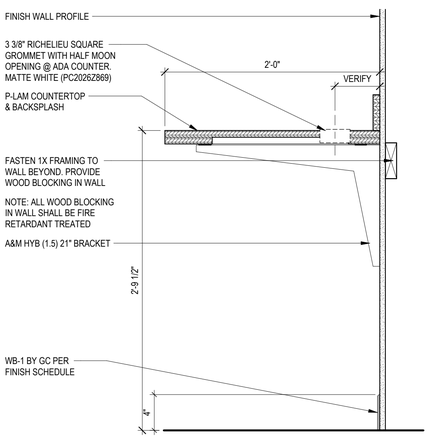


COUNTERTOP GROMMET | 1 1/2" = 1'-0" | 5

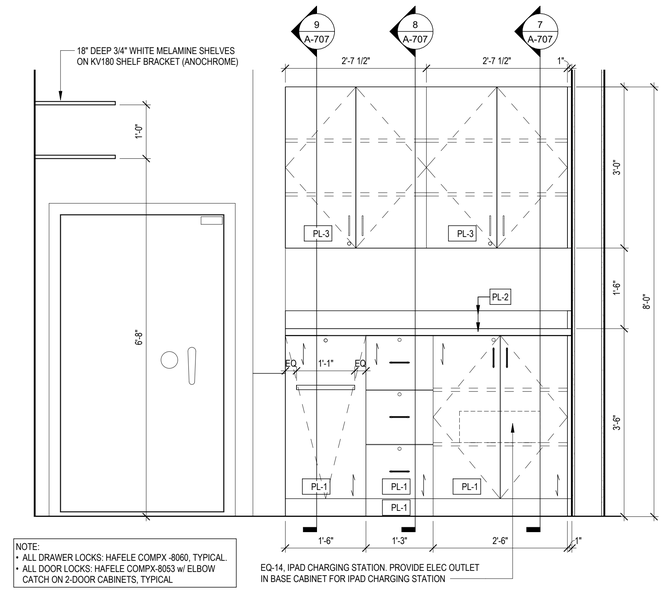


WORK ROOM - MILWORK ELEVATON | 3/4" = 1'-0" | 4

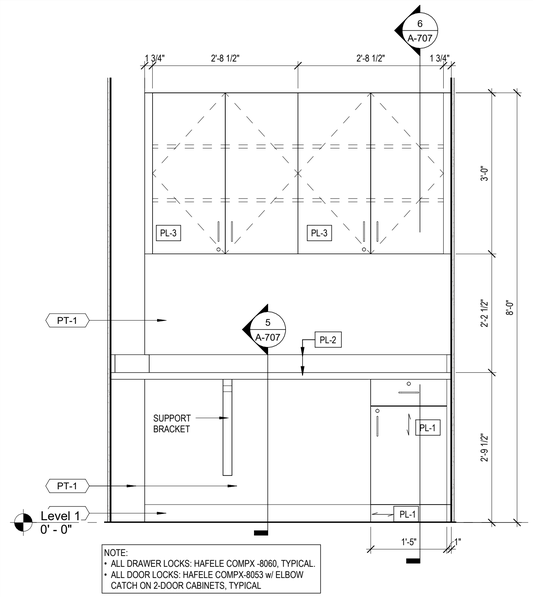

WORK ROOM - MILWORK ELEVATON | 3/4" = 1'-0" | 3

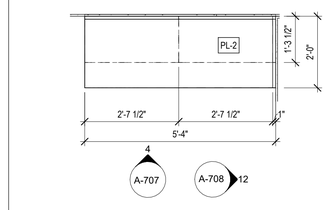

MILLWORK PLAN | 1/2" = 1'-0" | 2

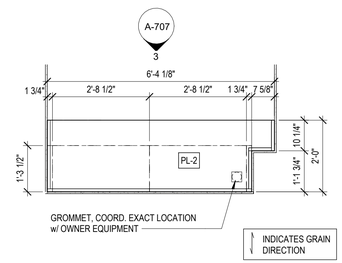

MILLWORK PLAN | 1/2" = 1'-0" | 1

7/8/2026 2:39:09 PM

PRAXIS3

100 Peachtree St NW
Suite 1450
Atlanta, GA 30303
404-875-4500 tel
www.praxis3.com

STATE OF GEORGIA
STUART M. ROMM
07/02/26
CERTIFICATE NO. 34511
REGISTERED ARCHITECT

Copyright (c) 2026 Praxis3, LLC

All reports, plans, specifications, computer files, field data, notes and other documents and instruments prepared by Praxis3 shall retain all common law, statutory and other reserved rights, including copyright thereto.

This drawing may not be reproduced in whole or in part without written permission of Praxis3. It is to be returned upon request. Scales as stated are valid on the original drawings.

Rev	Date	Comments
	07/02/2026	PERMIT SET

Client:
FIFTH THIRD BANK


Project Number: 26302
Project Name:
WATSON BLVD.

2711 WATSON BOULEVARD
WARNER ROBINS, GA 31093


Key Plan:

Sheet Title:
WORK ROOM - ENLARGED PLAN & DETAILS


Sheet Number:
A-707

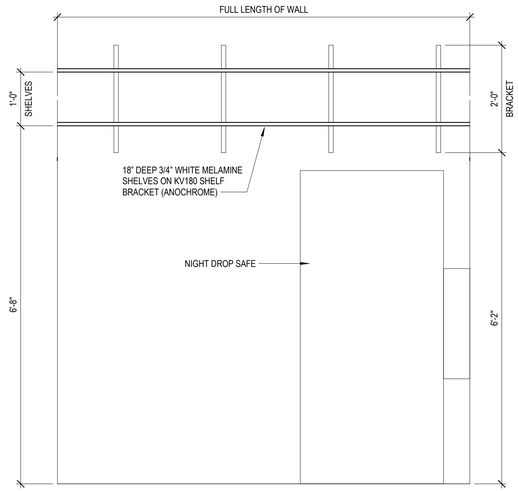


SHELF AT NIGHT DROP ELEVATION | 3/4" = 1'-0" | 12

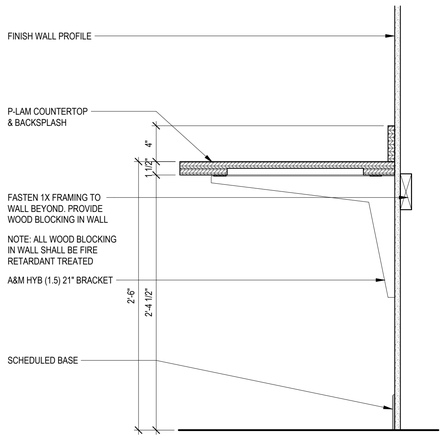


PHONE ROOM COUNTERTOP | 1 1/2" = 1'-0" | 11

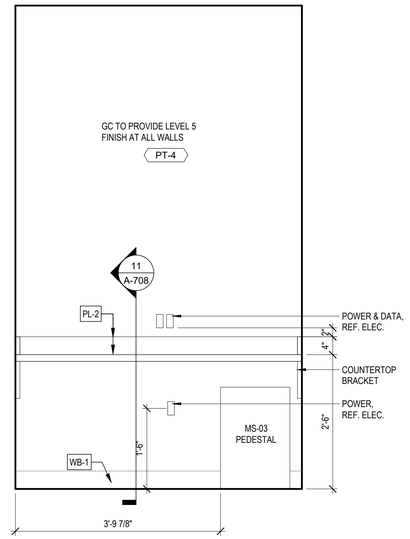


PHONE ROOM ELEVATION | 3/4" = 1'-0" | 10

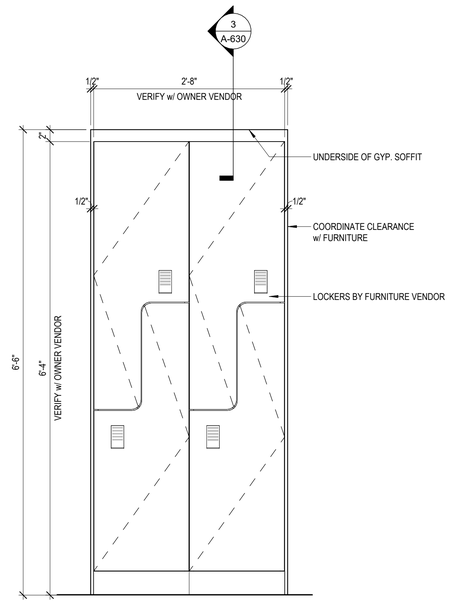


LOCKER ELEVATION | 1" = 1'-0" | 9

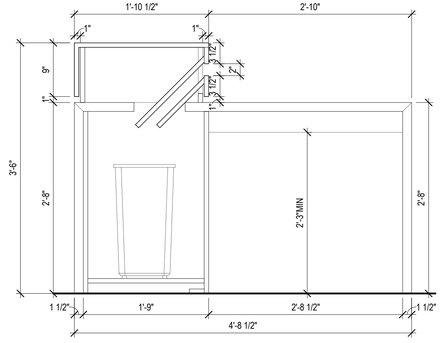


CHECK DESK - SECTION | 1" = 1'-0" | 8

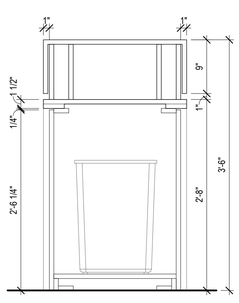


CHECK DESK - SECTION | 1" = 1'-0" | 7

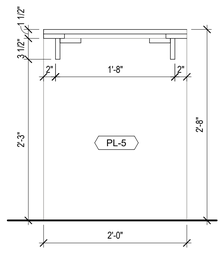


CHECK DESK - SECTION | 1" = 1'-0" | 6

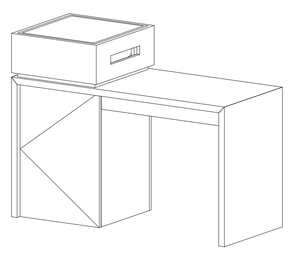


CHECK DESK | NTS | 5

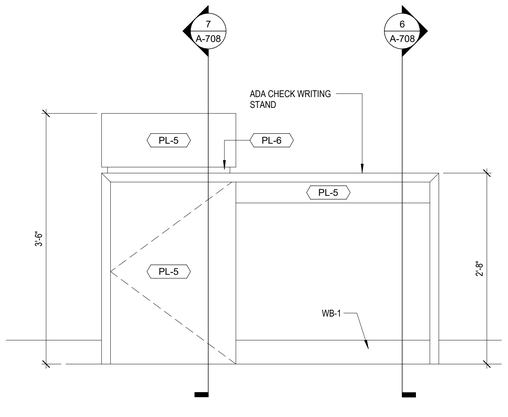


CHECK DESK - ELEVATION | 1" = 1'-0" | 4

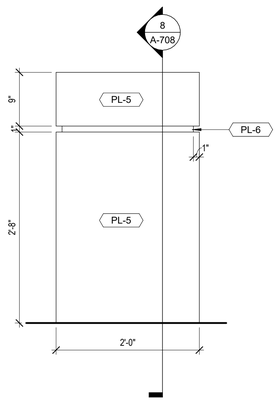

CHECK DESK - ELEVATION | 1" = 1'-0" | 3

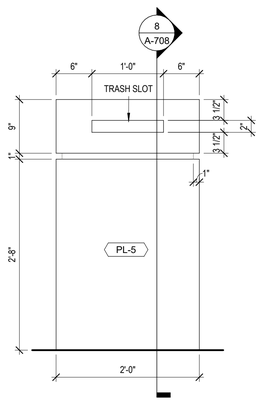

CHECK DESK - ELEVATION | 1" = 1'-0" | 2

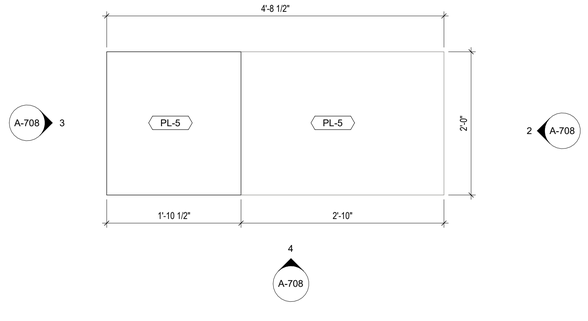

CHECK DESK - ENLARGED PLAN | 1" = 1'-0" | 1

PRAXIS3
100 Peachtree St NW
Suite 1450
Atlanta, GA 30303
404-875-4500 tel
www.praxis3.com

STATE OF GEORGIA
STUART M. ROMM
07/02/26
CERTIFICATE NO. 34511
REGISTERED ARCHITECT

Copyright (c) 2026 Praxis3, LLC

All reports, plans, specifications, computer files, field data, notes and other documents and instruments prepared by Praxis3 shall retain all common law, statutory and other reserved rights, including copyright thereto.

This drawing may not be reproduced in whole or in part without written permission of Praxis3. It is to be returned upon request. Scales as stated are valid on the original drawings.

Rev	Date	Comments
	07/02/2026	PERMIT SET

Client:
FIFTH THIRD BANK

Project Number: 26302
Project Name:
WATSON BLVD.

2711 WATSON BOULEVARD
WARNER ROBINS, GA 31093

Key Plan:

Sheet Title:
CHECK DESK - ENLARGED PLAN & DETAILS

Sheet Number:
A-708

7/8/2026 2:39:10 PM