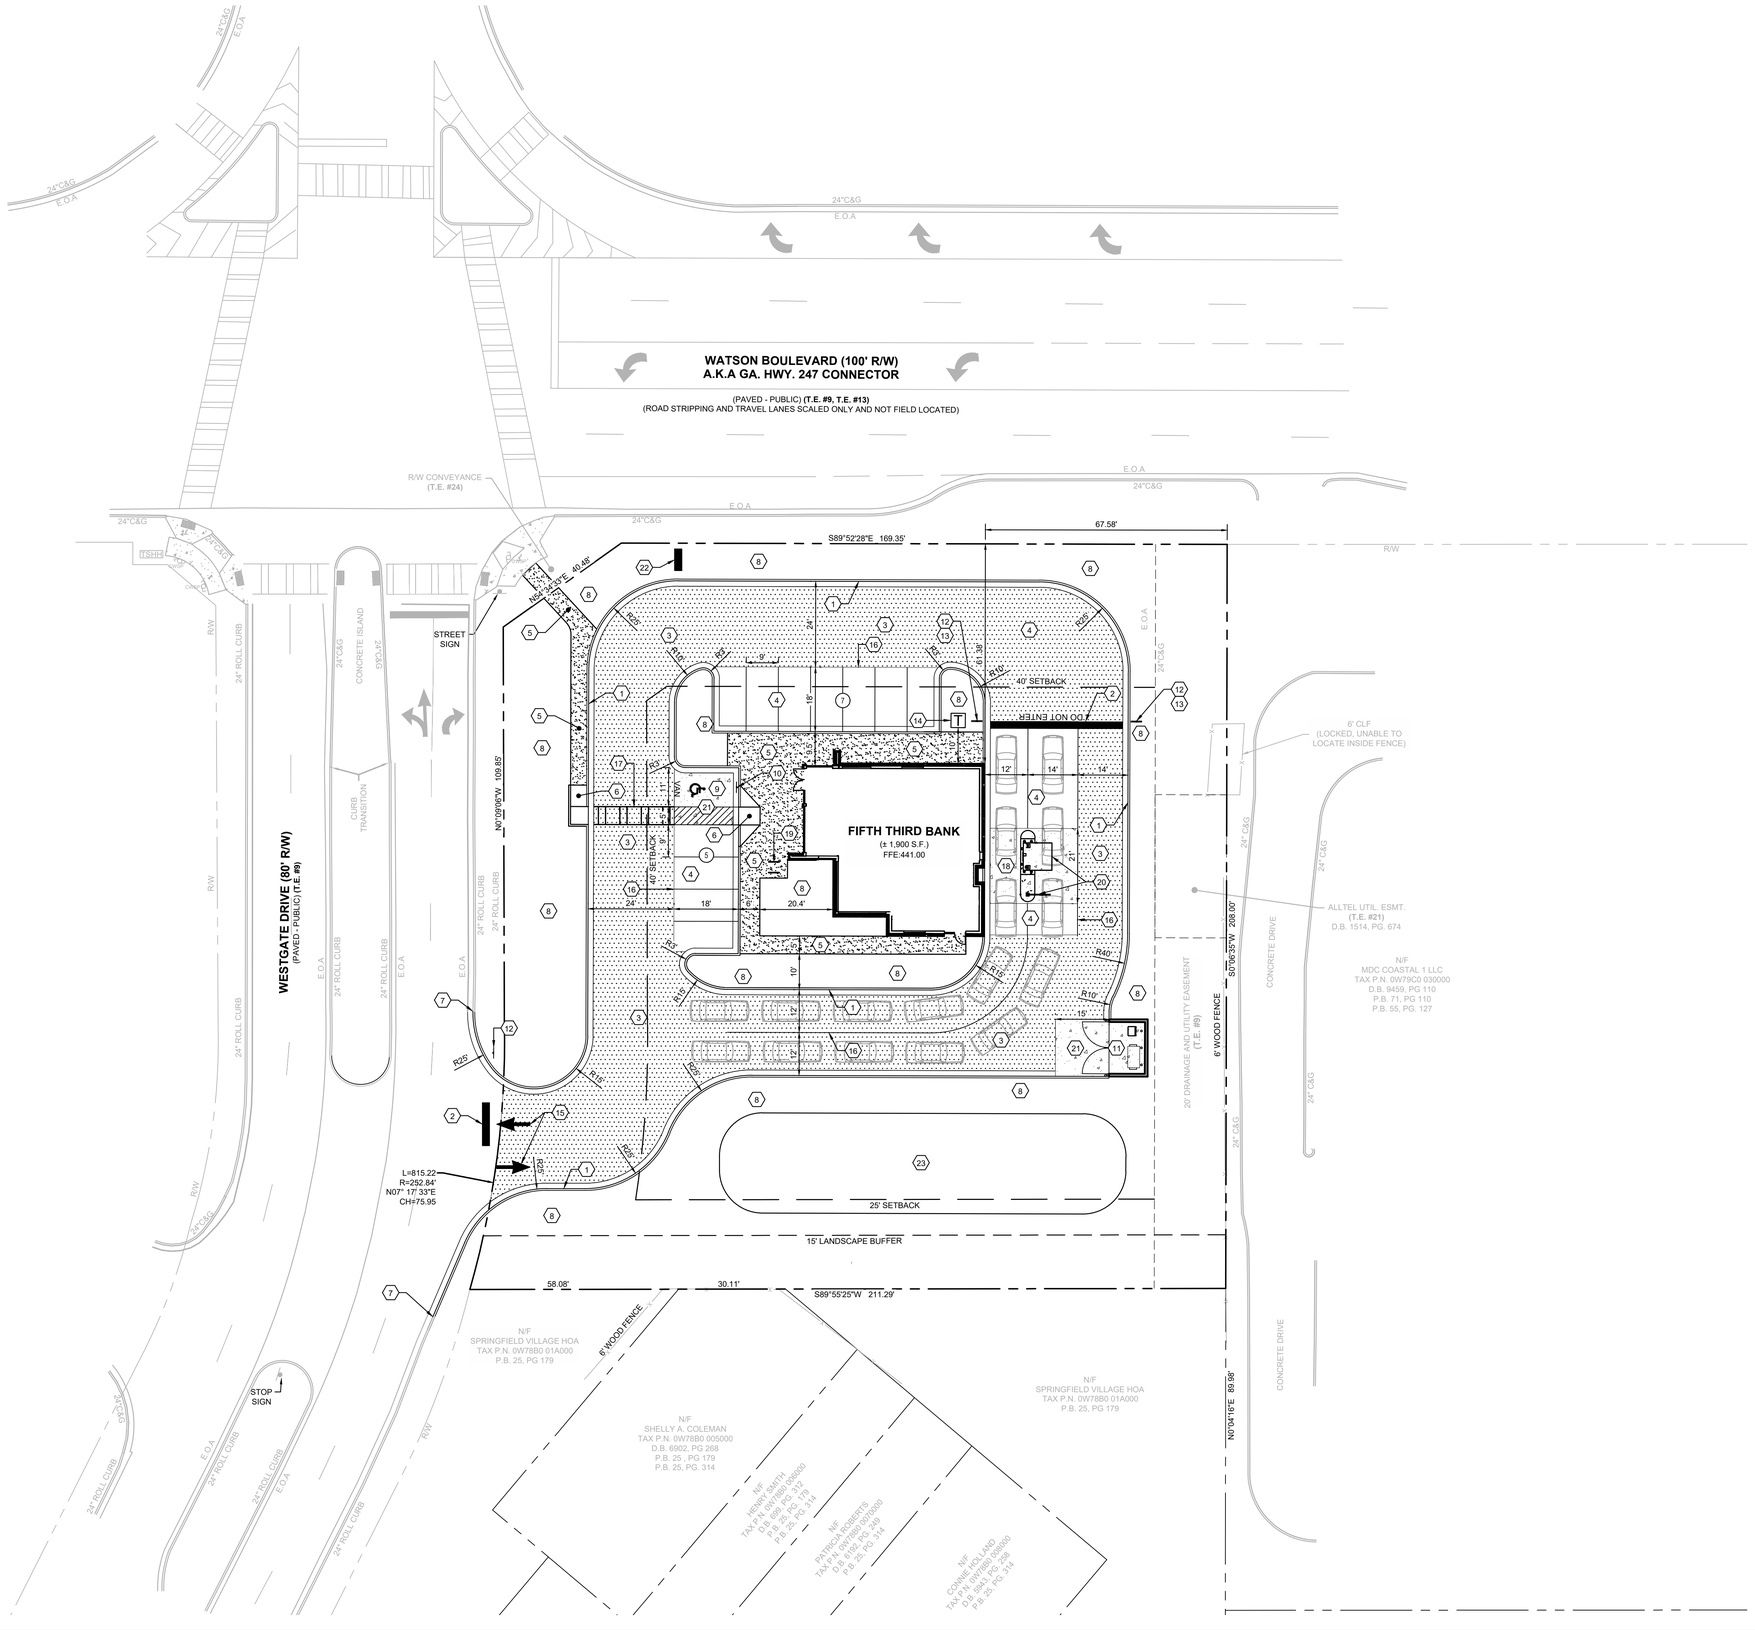


GENERAL SITE NOTES

1) ALL DIMENSIONS ARE TO THE FACE OF CURB UNLESS SPECIFIED OTHERWISE.

2) ALL TREES SHALL HAVE PROPER PROTECTION DURING CONSTRUCTION UNLESS APPROVED PLANS INDICATE OTHERWISE.

3) BOUNDARY & TOPOGRAPHIC SURVEY BY GASKINS+LECRAW, A PAPE DAWSON COMPANY, DATED 05.08.2026. BENCHMARK IS NOTED ON SURVEY.

4) FLOOD PLAIN IS NOT PRESENT ON THIS SITE AS SHOWN ON THE FEMA FIRM MAP NUMBER 13153C0085E, DATED 09.28.2007.

5) 1 HANDICAP SPACE IS REQUIRED TO BE VAN ACCESSIBLE WITH A MINIMUM 96" WIDE ACCESS AREA.

6) ACCESSIBLE PARKING AREAS, INCLUDING AISLES, SHALL SLOPE NO MORE THAN 2% IN ANY DIRECTION.

7) THE OWNER IS RESPONSIBLE FOR OBTAINING ANY NECESSARY AGREEMENTS FROM ADJACENT PROPERTY OWNERS IN ORDER TO PERFORM THE REQUIRED OFFSITE WORK, INCLUDING, STORM DRAINAGE, CURB AND GUTTER AND PAVEMENT TIE-INS AND GRADING.

8) REFERENCE ARCH PLANS FOR DIRECTIONAL SIGNAGE, SITE SIGNAGE, BUILDING DIMENSIONS, ETC.

9) ALL NEW PAVEMENT SHALL MEET OR EXCEED GEOTECHNICAL SPECIFICATION. SEE REPORT PREPARED BY TERRACON, DATED 05.04.2026.

SITE SUMMARY

SITE AREA		
	SITE AREA:	0.96 ACRES (41,909 S.F.)
	IMPERVIOUS AREA:	21,033 S.F. (50.2%)
	PERVIOUS AREA:	20,876 S.F. (49.8%)
ZONING CLASSIFICATION		
	JURISDICTION:	CITY OF WARNER ROBINS
	ZONING:	C-2 (GENERAL COMMERCIAL DISTRICT)
	ADJACENT ZONING:	C-2 / R-3
BUILDING SETBACKS		
	FRONT:	40'
	SIDE:	0'
	REAR:	25'
BUILDING SUMMARY		
	BUILDING AREA:	1,900 S.F.
	BUILDING COVERAGE:	4.5%
PARKING SUMMARY		
	PARKING REQ.:	1 SPACE / 300 S.F.
		7 SPACES
	PARKING PROV.:	11 SPACES
	STANDARD STALL DIMENSIONS:	9' x 18'
	MIN. DRIVE WIDTH:	24'

KEY NOTES

1	24" CURB & GUTTER, SEE SHEET C-6.0 FOR DETAIL
2	24" WHITE STOP BAR, SEE SHEET C-6.0 FOR DETAIL
3	HEAVY DUTY ASPHALT PAVEMENT, SEE SHEET C-6.2 FOR PAVEMENT SPECIFICATIONS
4	STANDARD DUTY ASPHALT PAVEMENT, SEE SHEET C-6.2 FOR PAVEMENT SPECIFICATIONS
5	CONCRETE SIDEWALK, SEE SHEET C-6.0 FOR DETAIL
6	GDOT STANDARD ADA RAMP WITH DETECTABLE WARNING, SEE SHEET C-6.1 FOR DETAIL
7	CONTRACTOR TO TIE INTO AND MATCH EXISTING CURB & GUTTER IN BOTH GRADE AND ALIGNMENT
8	LANDSCAPE AREA, SEE SHEET L-1.0 FOR LANDSCAPE PLANTING DESIGN
9	ADA PARKING AREA, SEE SHEET C-6.0 FOR DETAIL(S)
10	ADA PARKING SIGN, SEE SHEET C-6.0 FOR DETAIL
11	DUMPSTER ENCLOSURE, REFER TO ARCHITECTURAL PLANS FOR DETAILS
12	STOP SIGN (R1-1), SEE SHEET C-6.0 FOR MOUNTING DETAIL
13	DO NOT ENTER SIGN (R5-1), SEE SHEET C-6.0 FOR MOUNTING DETAIL
14	CONCRETE TRANSFORMER PAD PER UTILITY OWNER'S REQUIREMENTS
15	TYPICAL PAVEMENT MARKINGS, SEE SHEET C-6.0 FOR DETAILS
16	4" WIDE SINGLE SOLID WHITE LINE (SSWL)
17	5' WIDE, WHITE STRIPED PEDESTRIAN CROSSING/CROSSWALK
18	HEAVY DUTY CONCRETE PAVEMENT, SEE SHEET C-6.2 FOR PAVEMENT SPECIFICATIONS
19	BIKE RACK(S), SEE SHEET C-6.0 FOR DETAILS
20	DRIVE THRU EQUIPMENT / SIGNAGE, REFER TO ARCH PLANS FOR DETAILS
21	HEAVY DUTY CONCRETE PAVEMENT, SEE SHEET C-6.2 FOR PAVEMENT SPECIFICATIONS
22	PROPOSED MONUMENT SIGN, DESIGNED AND PERMITTED BY OTHERS
23	PROPOSED STORMWATER POND

IMPERVIOUS CALCULATIONS

	PERVIOUS (SF)	IMPERVIOUS (SF)
EXISTING CONDITION:	13,601 (32.5%)	28,308 (67.5%)
PROPOSED CONDITION:	20,876 (49.8%)	21,033 (50.2%)

NET DECREASE OF 7,275 SF OF IMPERVIOUS AREA

PAVEMENT LEGEND

*CONTRACTOR TO SUBMIT JOINT PLAN TO GEOTECH FOR REVIEW/APPROVAL PRIOR TO PAVING

CONCRETE PAVEMENT
(SEE GEOTECH REPORT BY TERRACON, DATED 05.04.2026)

HEAVY DUTY PAVEMENT
(SEE GEOTECH REPORT BY TERRACON, DATED 05.04.2026)

PREPARED IN THE OFFICE OF:
GASKINS +LECRAW
a PAPE-DAWSON company

© 2026 GASKINS + LECRAW

3475 CORPORATE WAY
SUITE A
DULUTH, GA 30096
PHONE - 678.546.8100
www.gaskinslecraw.com
PEF008127

REVISIONS:

REV.#	DATE	DRAWN BY:	CHECKED BY:

CLIENT
PRAXIS3
100 PEACHTREE STREET NW, SUITE 1450, ATLANTA, GEORGIA 30303

PROJECT
FIFTH THIRD BANK - WARNER ROBINS, GA
2711 WATSON BLVD
PARCEL ID: 0W0780-005000
WARNER ROBINS, HOUSTON COUNTY, GEORGIA

SEAL:
GEORGIA REGISTERED No. PE036681 PROFESSIONAL ENGINEER * TIMOTHY KYLE SHARPE *
7/9/2026

CALL BEFORE YOU DIG
811
Know what's below. Call before you dig.

SCALE & NORTH ARROW:
NORTH ARROW
0' 10' 20' 40'
SCALE: 1" = 20'

DESIGN INFO:

DRAWN BY:	JOA
DESIGNED BY:	MAT
REVIEWED BY:	TKS
JOB #:	75670007
DATE:	JULY 9, 2026

SITE PLAN

C-3.0

Drawing name: C:\Users\ckientz\Gaskins+LeCraw Dropbox\Shared Folders\Engineering\75670007 - Praxis3 - Fifth Third - Warner Robins_GA\CADD\CONSTR\75670007 - 06 - SITE.dwg SITE PLAN Jul 09, 2026 10:51am by ckientz

This document, together with the concepts and designs presented herein, as an instrument of service, is intended only for the specific purpose and client for which it was prepared. Reuse of and improper reliance on this document without written authorization and adaptation by Gaskins + LeCraw, a Pape-Dawson Company shall be without liability to Gaskins + LeCraw, a Pape-Dawson Company, Copyright Gaskins + LeCraw, a Pape-Dawson Company, 2026