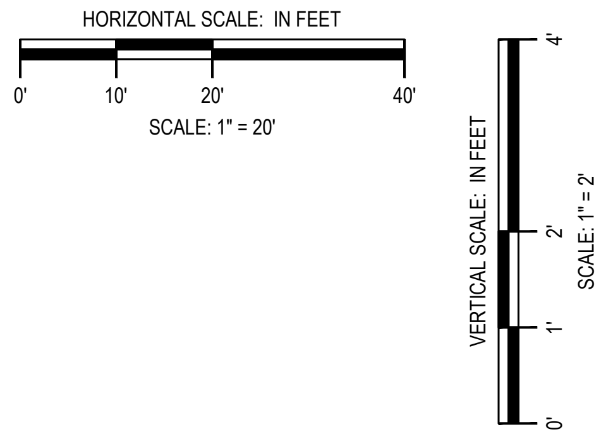

STRUCTURE TYPES

SSCO:	CLEANOUT	SSDD:	DUMPSTER DRAIN
SSMH:	MANHOLE	SSGT:	GREASE TRAP
SSBC:	BUILDING CONNECTION	SSSW:	SAMPLING WELL

PROFILE LEGEND

EXISTING GRADE: – – – – – –
PROPOSED GRADE: ————————

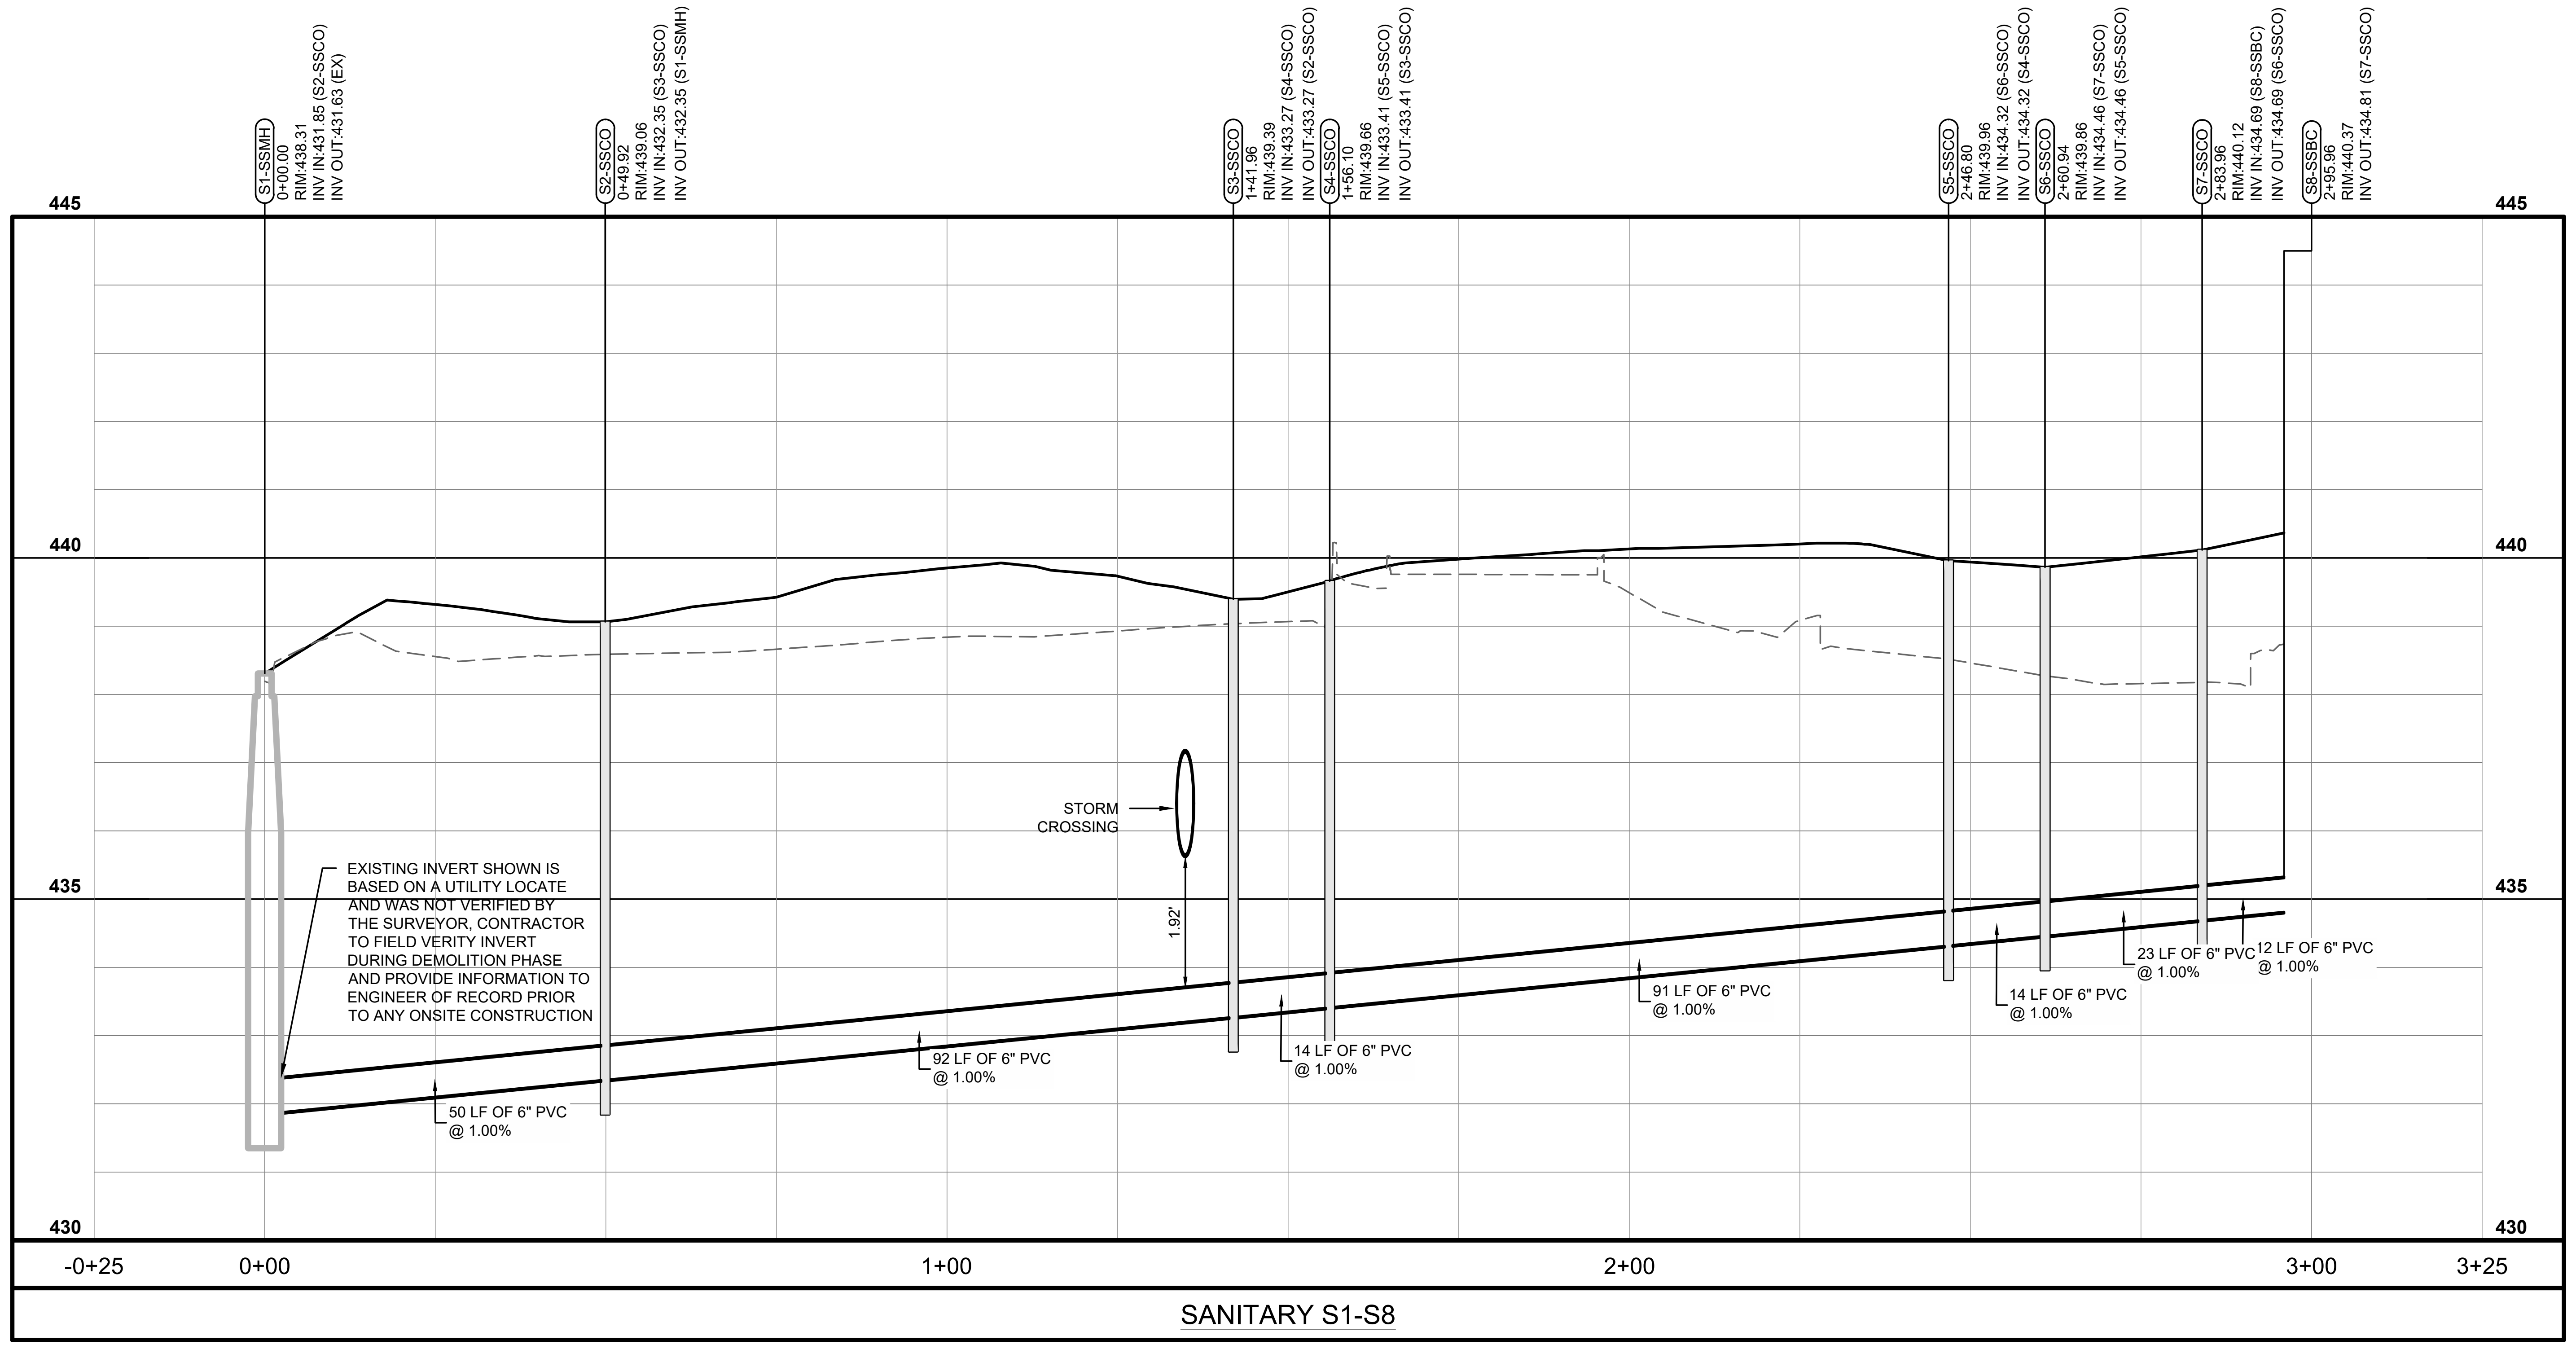

EXISTING INVERT SHOWN IS BASED ON A UTILITY LOCATE AND WAS NOT VERIFIED BY THE SURVEYOR, CONTRACTOR TO FIELD VERITY INVERT DURING DEMOLITION PHASE AND PROVIDE INFORMATION TO ENGINEER OF RECORD PRIOR TO ANY ONSITE CONSTRUCTION

SANITARY S1-S8

Drawing name: C:\Users\cklentz\Gaskins+LeCraw Dropbox\Shared Folders\Engineering\75670007 - Praxis3 - Fifth Third - Warner Robins_GA\CADD\CONSTR\75670007 - 09 - PROFILES.dwg SANITARY PROFILES Jul 09, 2026 10:53am by: cklentz

PREPARED IN THE OFFICE OF:

GASKINS
+LECRAW
a PAPE-DAWSON company
© 2026 GASKINS + LECRAW
3475 CORPORATE WAY
SUITE A
DULUTH, GA 30096
PHONE - 678.546.8100
www.gaskinslecraw.com
PEF008127

REVISIONS:

REV. #		DATE	DRAWN BY:	CHECKED BY:
--	--	--	--	--

CLIENT
PRAXIS3
100 PEACHTREE STREET NW, SUITE 1450, ATLANTA, GEORGIA 30303

PROJECT
FIFTH THIRD BANK - WARNER ROBINS, GA
2711 WATSON BLVD
PARCEL ID: 0W0780-005000
WARNER ROBINS, HOUSTON COUNTY, GEORGIA

SEAL:

No. PE036681
PROFESSIONAL
TIMOTHY KYLE SHARPE
7/9/2026

CALL BEFORE YOU DIG

811
Know what's below.
Call before you dig.

SCALE & NORTH ARROW:

DESIGN INFO:

DRAWN BY:	JOA
DESIGNED BY:	MAT
REVIEWED BY:	TKS
JOB #:	75670007
DATE:	JULY 9, 2026

SANITARY PROFILES

C-5.1

This document, together with the concepts and designs presented herein, as an instrument of service, is intended only for the specific purpose and client for which it was prepared. Reuse of and improper reliance on this document without written authorization and adaptation by Gaskins + LeCraw, a Pape-Dawson Company shall be without liability to Gaskins + LeCraw, a Pape-Dawson Company, Copyright Gaskins + LeCraw, a Pape-Dawson Company, 2026