POWER SYMBOLS:

NOTE: A COMPLETE LIST OF RECEPTACLE SYMBOLS IS SHOWN FOR THE DUPLEX RECEPTACLE ONLY. OTHER RECEPTACLE SYMBOLS WILL FOLLOW THE SAME SHADING CONVENTION AS THE DUPLEX RECEPTACLE, UNO.

CENTER HATCH: ISOLATED GROUND RECEPTACLE
OUTER HATCH: GFCI RECEPTACLE
RIGHT HATCH: CONTROLLED RECEPTACLE

20A, 125V, RECEPTACLE
(NEMA 520R), WALL MTD
(SIMPLEX LEFT, DUPLEX CENTER, QUAD RIGHT)
D= DUAL SWITCHED
H = HALF SWITCHED
TR = TAMPER RESISTANT
U= USB OUTLET
WP = WEATHERPROOF
WR = WEATHER RESISTANT
SP = SURGE PROTECTIVE
(LEVITON T5380W OR EQUAL)

20A, 125V, IG DUPLEX RECEPTACLE
(NEMA 520R), WALL MTD

20A, 125V, GFCI DUPLEX RECEPTACLE
(NEMA 520R), WALL MTD

20A, 125V, GFCI DUPLEX RECEPTACLE
(NEMA 520R), WALL MTD

20A, 125V, RECEPTACLE ON EMERGENCY
CIRCUIT (NEMA 520R), WALL MTD
(SIMPLEX LEFT, DUPLEX CENTER, QUAD RIGHT)

20A, 125V, RECEPTACLE
(NEMA 520R), FLOOR MTD
(SIMPLEX LEFT, DUPLEX CENTER, QUAD RIGHT)

20A, 125V, RECEPTACLE ON EMERGENCY
CIRCUIT (NEMA 520R), FLOOR MTD
(SIMPLEX LEFT, DUPLEX CENTER, QUAD RIGHT)

20A, 125V, RECEPTACLE
(NEMA 520R), CEILING MTD
(SIMPLEX LEFT, DUPLEX CENTER, QUAD RIGHT)

20A, 125V, RECEPTACLE ON EMERGENCY
CIRCUIT (NEMA 520R), CEILING MTD
(SIMPLEX LEFT, DUPLEX CENTER, QUAD RIGHT)

FB — MULTISERVICE, FLOOR BOX, FLUSH MNT
(SEE SPECS OR NOTES)
FB = FLOOR BOX
FF = FURNITURE FEED

PT — MULTISERVICE, POKE-
THRU, 2 HR. FIRERATED, FLUSH MNT (SEE SPECS OR NOTES)
PT = POKETHRU
FF = FURNITURE FEED

PT — MULTISERVICE, CEILING BOX WITH PROJECTOR MOUNT (SEE SPECS OR NOTES)

WB — MULTISERVICE, WALL BOX, RECESSED MNT
(SEE SPECS OR NOTES)

SPECIAL PURPOSE RECEPTACLE
(SEE EQUIPMENT SCHEDULE OR NOTES)
(WALL MNT LEFT, FLOOR MTD RIGHT)

SPECIAL PURPOSE RECEPTACLE ON
EMERGENCY CIRCUIT
(SEE EQUIPMENT SCHEDULE OR NOTES)
(WALL MNT LEFT, FLOOR MTD RIGHT

60A — 60A, 480V, 3PH, WELDING RECEPTACLE, WALL MTD

DROP CORD (SEE SPECS OR NOTES)

POWER POLE (SEE SPECS OR NOTES)

RECEPTACLE RACEWAY / PLUG MOLD

J — JUNCTION BOX, WALL MTD

WP — JUNCTION BOX
WP = WEATHERPROOF

J — JUNCTION BOX, FLOOR MTD

J — JUNCTION BOX, EXPLOSION PROOF

30/NF — SAFETY SWITCH, 30A, 3POLE, NONFUSED
(FBO - FURNISHED BY OTHERS)

30/20 — SAFETY SWITCH, 30A, 3POLE, FUSED @ 20A
(FBO - FURNISHED BY OTHERS)

STARTER OR MOTOR CONTROLLER

T — STARTER, COMBINATION W/ DISC. SWITCH

TRANSFORMER

ELECTRICAL PANEL / ENCLOSURE AS NOTED ON
PLAN DRAWINGS
(SURFACE MTD LEFT, RECESSED MTD RIGHT)

ELECTRIC UTILITY METER

GROUNDING BUSBAR (SEE SPECS OR NOTES)

PP — UTILITY POWER POLE

LIGHTING SYMBOLS:

NOTE: REFER TO LIGHTING FIXTURE SCHEDULE FOR FIXTURE TYPES AND SENSOR SCHEDULE FOR SENSOR TYPES. REFER TO PLAN DRAWINGS FOR ADDITIONAL SYMBOLS.

A: — CAPITAL LETTER ADJACENT TO FIXTURE = TYPE

a: — LOWERCASE LETTER = SWITCHING GROUP

EM: — EMERGENCY LIGHTING IS DESIGNATED BY AN "EM" ADJACENT TO THE FIXTURE AND/OR A "HALF SHADED" OR "FULL SHADED" FIXTURE SYMBOL

NL: — NIGHT LIGHTING (UNSWITCHED FIXTURE)

$^{x}_{xx} — SWITCH, 20A, 120/277V, TOGGLE TYPE, U.N.O.
a,b,c,... =SWITCHING GROUP
BLANK =SINGLE POLE
2 =DOUBLE POLE
3 =THREEWAY
4 =FOURWAY
D =DIMMER SWITCH
K =SINGLE POLE KEY OPERATED
M =MOTOR RATED
MA =MAINTAINED CONTACT
MO =MOMENTARY CONTACT
P =SINGLE POLE W/ PILOT LIGHT
P2 =DOUBLE POLE W/ PILOT LIGHT
RC =REMOTE CONTROL
T =TIMER OPERATED SWITCH
WP =WEATHERPROOF
2HR =2HOUR OVERRIDE SWITCH

B — BLANK PLATE

O — OCCUPANCY SENSOR, WALL MTD

D^{x}_{xx} — LOW VOLTAGE DIGITAL SWITCH, WALL MTD

DP — LIGHTING CONTROL DEVICE
DP =DIMMABLE POWER PACK (ON/OFF WITH DIMMING)
PP =POWER PACK (ON/OFF)
RP =AUX. RELAY PACK (ON/OFF)
GW =GATEWAY
PS =POWER SUPPLY
BR =BRIDGE
LC =LIGHTING CONTACTOR
TC =TIME CLOCK
MS =MOTION SENSOR
PC =PHOTOCELL

PL — PLUG LOAD CONTROLLER (ON/OFF)

EPC — EMERGENCY POWER CONTROLLER

OCCUPANCY SENSOR, CORNER MTD

OS — OCCUPANCY SENSOR, CEILING MTD

DS — DAYLIGHT SENSOR, CEILING MTD

OS/DS — COMBINATION OCCUPANCY / DAYLIGHT SENSOR, CEILING MTD

2'X4' LAYIN TROFFER

2'X2' LAYIN TROFFER

1'X4' LAYIN TROFFER

STRIP/CHANNEL FIXTURE

DOWNLIGHT, CEILING MTD

WALL WASHER, CEILING MTD

LIGHT FIXTURE, CEILING MTD

LIGHT FIXTURE, WALL MTD

WALL PACK

EMERGENCY WALL PACK (BUG EYE)
(WALL MTD LEFT, CEILING MTD RIGHT)

EXIT SIGN, SINGLE FACE
(ARROW INDICATES DIRECTION OF EGRESS)
(WALL MTD LEFT, CEILING MTD RIGHT)

EXIT SIGN, DOUBLE FACE
(ARROW INDICATES DIRECTION OF EGRESS)
(WALL MTD LEFT, CEILING MTD RIGHT)

EXIT SIGN W/ COMBINATION EMERGENCY LIGHT, SINGLE FACE
(ARROW INDICATES DIRECTION OF EGRESS)
(WALL MTD LEFT, CEILING MTD RIGHT)

SPECIAL SYSTEMS SYMBOLS:

NOTE: UNLESS NOTED OTHERWISE, PROVIDE OVERSIZED JUNCTION BOX AND 1" EMPTY CONDUIT WITH PLASTIC INSULATING BUSHINGS AND PULL STRING STUBBED MIN. 6" INTO ACCESSIBLE CEILING SPACE. COORDINATE WITH LV CONTRACTOR FOR FINAL REQUIREMENTS.

TELEPHONE OUTLET, WALL MTD
1 TELE OUTLET, U.N.O.

COMBINATION TELE/DATA OUTLET, WALL MTD
1 TELE / 1 DATA OUTLET, U.N.O.

COMBINATION TELE/DATA OUTLET, WALL MTD
1 TELE / 2 DATA OUTLETS, U.N.O.

TELEPHONE OUTLET
1 TELE OUTLET, U.N.O.
(FLOOR MTD LEFT, CEILING MTD RIGHT)

COMBINATION TELE/DATA OUTLET
1 TELE / 1 DATA OUTLET, U.N.O.
(FLOOR MTD LEFT, CEILING MTD RIGHT)

COMBINATION TELE/DATA OUTLET
1 TELE / 2 DATA OUTLETS, U.N.O.
(FLOOR MTD LEFT, CEILING MTD RIGHT

TELEPHONE BACKBOARD (TBB)

INTERCOM OUTLET

M / I — INTERCOM STATION
BLANK = REMOTE
M = MASTER

AV AV — AUDIO / VIDEO DEVICE
(WALL MTD LEFT, CEILING MTD RIGHT)
AV = AUDIO / VIDEO OUTLET
M = MICROPHONE OUTLET
SM = SECURITY MONITOR OUTLET
TV = TELEVISION OUTLET
V=VOLUME CONTROL

AMP — SOUND SYSTEM AMPLIFIER

S S — SPEAKER
(WALL MTD LEFT, CEILING MTD RIGHT)

B — AUDIBLE NOTIFICATION DEVICE
B= BELL
C= CHIME
G= GONG

B — BUZZER

B — BELL & BUZZER COMBINATION

H — AUDIBLE NOTIFICATION DEVICE
H= HORN
S= SIREN

BT — AUXILIARY SYSTEM DEVICE
BT= BELL RINGING TRANSFORMER
R= RELAY
D= ELECTRIC DOOR OPENER
LV= LOW VOLTAGE TRANSFORMER

ANNUNCIATOR

BL BL — INDICATOR LIGHT
(WALL MTD LEFT, CEILING MTD RIGHT)
BL = BURGLAR ALARM LIGHT

M — CLOCK
M = MASTER
DF = DOUBLE FACE
S = COMBINATION SPEAKER

DC PVM — SECURITY DEVICES
DC = DOOR CONTACT
GB = GLASS BREAK DETECTOR
HD = HEAT DETECTOR
HU = HOLDUP BUTTON
KP = KEY PAD
MD = MOTION DETECTOR
PB = PANIC BUTTON
PVM = PUBLIC VIEW MONITOR
SD = SOUND DETECTOR
SEC = SECURITY CONTROL PANEL
VS = VIBRATION SENSOR
WC = WINDOW CONTACT

CR ACP — ACCESS CONTROL DEVICE
ACP = ACCESS CONTROL PANEL
CR = CARD READER
ES = ELECTRIC STRIKE
ML = MAGNETIC LOCK
PS = PROXIMITY SENSOR
PWR = POWER SUPPLY
RX = REQUEST EXIT PUSH BUTTON

XX XX — SECURITY CAMERA
(WALL MTD LEFT, CEILING MTD RIGHT)
PTZ = PAN/TILT/ZOOM
BX = BOX
D=MINI DOME
BL = BULLET
WP = WEATHERPROOF

PUSHBUTTON STATION
(BUTTONS REPRESENTED BY SOLID DOTS

NORMAL / EMERGENCY CALL BUTTON

PUSH BUTTON

RACEWAY SYMBOLS:

HOMERUN CIRCUIT TO PANELBOARD

LOW VOLTAGE CABLE

CONDUIT BURIED

CONDUIT CONCEALED

CONDUIT EXPOSED

FLEXIBLE CONDUIT

CONDUIT UP

CONDUIT DOWN

CONDUIT SEALOFF

CONDUIT TEE BODY

CONDUIT EL BODY

CONDUIT CAP

CONDUIT SLEEVE WITH BUSHINGS

PB — PULL BOX

HH — HAND HOLE

FIRE ALARM SYMBOL LEGEND

SYMBOL	DESCRIPTION
F	FIRE ALARM ADA APPROVED WALL MOUNTED HORN/STROBE ALARM. ENTIRE LENS SHALL NOT BE LESS THAN 80" AND NOT GREATER THAN 96" AFF.
V	FIRE ALARM ADA APPROVED WALL MOUNTED VISUAL ALARM. ENTIRE LENS SHALL NOT BE LESS THAN 80" AND NOT GREATER THAN 96" AFF.
FACP	FIRE ALARM CONTROL PANEL
FAA	FIRE ALARM ANNUNCIATOR
D D	FIRE ALARM SMOKE DETECTOR - WALL MTD., CEILING MTD.
F	FIRE ALARM PULL STATION
D	DUCT MOUNTED SMOKE DETECTOR

CODE IN EFFECT(GA):

ALL WORK SHALL BE IN STRICT ACCORDANCE WITH:

- NATIONAL ELECTRICAL CODE - 2020
- GEORGIA BUILDING CODE - 2015 IECC

WORK AND EQUIPMENT UNDER THIS DIVISION SHALL BE IN STRICT COMPLIANCE WITH THE CODES, STANDARDS, AND PRACTICES LISTED HEREIN. THEIR RESPECTIVE DATES ARE FURNISHED AS THE MINIMUM REQUIREMENTS (UNLESS OTHERWISE DETERMINED BY THE LOCAL AUTHORITIES HAVING JURISDICTION).

ABBREVIATIONS:

A	AMPERE
AFC	AVAILABLE FAULT CURRENT
AFCI	ARC FAULT CIRCUIT INTERRUPTER
AFF	ABOVE FINISHED FLOOR
AFG	ABOVE FINISHED GRADE
AHJ	AUTHORITY HAVING JURISDICTION
AIC	AMPERE INTERRUPTING CAPACITY
ATS	AUTOMATIC TRANSFER SWITCH
BLDG	BUILDING
BRKR	BREAKER
C	CONDUIT
CKT	CIRCUIT
CLG	CEILING
CPT	CONTROL POWER TRANSFORMER
CT	CURRENT TRANSFORMER
CU	COPPER
CTR	CENTER
EA	EACH
EG	EQUIPMENT GROUND
EGC	EQUIPMENT GROUNDING CONDUCTOR
EM	EMERGENCY
EOL	ELECTRONIC OVERLOAD
FDR	FEEDER
FLA	FULL LOAD AMPS
GEC	GROUNDING ELECTRODE CONDUCTOR
GFI	GROUND FAULT INTERRUPTER
GFCI	GROUND FAULT CIRCUIT INTERRUPTER
GND	GROUND
GRS	GALVANIZED RIGID STEEL
HTD	HEATED
HOA	HANDOFFAUTO
IG	ISOLATED GROUND
JB	JUNCTION BOX
KVA	KILOVOLTAMPERE
KW	KILOWATT
L.S.I.G.	LONG, SHORT, INSTANTANEOUS, GROUND FAULT TRIP
LTG	LIGHTING
MCA	MINIMUM CIRCUIT AMPS
MCB	MAIN CIRCUIT BREAKER
MCC	MOTOR CONTROL CENTER
MCCB	MOLDED CASE CIRCUIT BREAKER
MCP	MOTOR CIRCUIT PROTECTOR
MDP	MAIN DISTRIBUTION PANEL
MFS	MAXIMUM FUSE SIZE
MGB	MAIN GROUNDING BUSBAR
MLO	MAIN LUG ONLY
MOCP	MAXIMUM OVERCURRENT PROTECTION
MTD	MOUNTED
MTS	MANUAL TRANSFER SWITCH
N.C.	NORMALLY CLOSED
N.O.	NORMALLY OPEN
NL	NIGHT LIGHT
NTS	NOT TO SCALE
OCPD	OVERCURRENT PROTECTION DEVICE
OH	OVERHEAD
P	POLE
PH	PHASE
PNL	PANEL
PWR	POWER
RECEP	RECEPTACLE
RI	REACHIN
RM	ROOM
SC	SECONTAINED
SCCR	SHORT CIRCUIT CURRENT RATING
SOL	SOLENOID
SW	SWITCH
SWBR	SWITCHBOARD
SWGR	SWITCHGEAR
TBB	TELEPHONE BACKBOARD
TD	TIME DELAY
TELCO	TELEPHONE COMPANY
TELE	TELEPHONE
TGB	TELECOMMUNICATIONS GROUNDING BUSBAR
TMGB	TELECOMMUNICATIONS MAIN GROUNDING BUSBAR
TYP	TYPICAL
UG	UNDERGROUND
UNO	UNLESS NOTED OTHERWISE
UPS	UNINTERRUPTIBLE POWER SUPPLY
V	VOLT
VIF	VERIFY IN FIELD
W/	WITH
W	WIRE
WP	WEATHERPROOF
WR	WEATHER RESISTANT
WTOP	WORKTOP
XFMR	TRANSFORMER

ELECTRICAL SHEET INDEX:

E-001	ELECTRICAL LEGEND AND ABBREVIATION
E-002	ELECTRICAL GENERAL NOTES
E-003	ELECTRICAL SPECIFICATIONS
E-004	COMCHECK
E-010	ELECTRICAL SITE PLAN AND REMOTE DRIVE THRU
E-011	ELECTRICAL PHOTOMETRIC SITE PLAN
E-012	ELECTRICAL SITE DETAILS
E-100	ELECTRICAL POWER & AUXILIARY PLAN
E-101	ELECTRICAL POWER ROOF PLAN
E-130	ELECTRICAL LIGHTING PLAN
E-150	ELECTRICAL SECURITY PLAN
E-500	ELECTRICAL DETAILS
E-600	LUMINAIRE AND SENSOR SCHEDULES AND DETAILS
E-601	EXTERIOR LIGHTING CUTSHEETS
E-602	EXTERIOR LIGHTING CUTSHEETS
E-603	EXTERIOR LIGHTING CUTSHEETS
E-610	ELECTRICAL PANEL SCHEDULES
E-700	ELECTRICAL DEVICE PLAN
E-701	ELECTRICAL ELEVATIONS
E-702	ELECTRICAL ELEVATIONS
E-703	ELECTRICAL ELEVATIONS
E-704	ELECTRICAL ELEVATIONS
E-800	ELECTRICAL RISER DIAGRAM

PRAXIS3
100 Peachtree St NW
Suite 1450
Atlanta, GA 30303
404-875-4500 tel
www.praxis3.com

GEORGIA REGISTERED No. 041560 PROFESSIONAL ENGINEER RAHN ONEAL WILLIAMS

Copyright (c) 2024 Praxis3, LLC

All reports, plans, specifications, computer files, field data, notes and other documents and instruments prepared by Praxis3 shall retain all common law, statutory and other reserved rights, including copyright thereto.

This drawing may not be reproduced in whole or in part without written permission of Praxis3. It is to be returned upon request. Scales as stated are valid on the original drawings.

Rev	Date	Comments
	07/02/2026	PERMIT SET

Client:
FIFTH THIRD BANK

Project Number: 26032
Project Name:
FIFTH THIRD BANK WATSON
1,900 SF

2711 WATSON BOULEVARD
WARNER ROBBINS, GA 31093

Key Plan:

Sheet Title:
ELECTRICAL LEGEND AND ABBREVIATION

Sheet Number:
E-001

6/30/2026 2:31:56 PM

GENERAL NOTES:

1. PRE-BID SITE VISIT: CONTRACTOR PROPOSING TO UNDERTAKE WORK UNDER THIS DIVISION SHALL VISIT THE SITE OF THE WORK AND FULLY INFORM THEMSELVES OF ALL CONDITIONS THAT EFFECT THE WORK AND COST THEREOF AND EXAMINE THE DRAWINGS AS RELATED TO THE SITE CONDITIONS. BIDDERS WHO DO NOT VISIT THE SITE MAY BE UNILATERALLY NOT PERMITTED TO SUBMIT A BID IF THE OWNER SO DESIGNATES.
2. BID TERMS AND CONDITIONS: THE ELECTRICAL CONTRACTOR SHALL OBTAIN A FULL SET OF PLANS AND SPECIFICATIONS FROM THE GENERAL CONTRACTOR PRIOR TO BID. CONSIDERATION WILL NOT BE GRANTED FOR ANY ALLEGED MISUNDERSTANDINGS OF THE AMOUNT OF WORK TO BE PERFORMED. TENDER OF PROPOSAL SHALL CONVEY FULL AGREEMENT TO THE ITEMS AND CONDITIONS INDICATED IN THE PLANS AND SPECIFICATIONS. ANY DISCREPANCIES OR OMISSIONS FOUND IN THE CONTRACT DOCUMENTS OR DOUBT AS TO THE INTENT THEREOF, SHALL BE IMMEDIATELY BROUGHT TO THE ATTENTION OF THE ARCHITECT IN WRITING TO OBTAIN CLARIFICATION FROM THE ENGINEER AND/OR OWNER'S REPRESENTATIVE PRIOR TO SUBMITTING PROPOSAL FOR WORK. WHERE CLARIFICATION CANNOT BE PROVIDED PRIOR TO BID, THE CONTRACTOR SHALL ASSUME THE MORE EXPENSIVE METHOD FOR THE BID. WITHOUT FORMAL AUTHORIZATION, THE ARCHITECT AND OWNER RESERVE THE RIGHT TO REQUIRE THE MORE RESTRICTIVE SPECIFICATION.
3. EXCLUSIONS: MATERIAL AND LABOR EXCLUDED BY THE ELECTRICAL CONTRACTOR SHALL NOT RELIEVE THE GENERAL CONTRACTOR FROM PROVIDING SAME.
4. COMPLETE SYSTEM: FURNISH ALL LABOR, MATERIALS, EQUIPMENT, TOOLS, TRANSPORTATION, SUPERINTENDENTS AND SERVICES REQUIRED TO CONSTRUCT, INSTALL, AND MODIFY THE ELECTRICAL SYSTEMS AS HEREIN SPECIFIED AND SHOWN ON THESE DRAWINGS FOR A COMPLETE AND FULLY OPERATIONAL SYSTEM. COORDINATE WORK TO BE PERFORMED OR INSTALLED BY OTHERS AFFECTING THE ELECTRICAL WORK AND FURNISH AND INSTALL ALL NECESSARY STEEL SHAPES, BLOCKING, ANCHORS, SLEEVES, HANGERS, ETC. FOR ATTACHING OR CONNECTING ELECTRICAL WORK TO RELATED WORK OF OTHER TRADES. ALL ITEMS NOT SPECIFICALLY MENTIONED HEREIN OR NOT INDICATED IN THE DRAWINGS, WHICH ARE NECESSARY TO MAKE A COMPLETE WORKING INSTALLATION, SHALL BE PROVIDED WITHOUT ADDITIONAL EXPENSE TO THE OWNER. DRAWINGS AND SPECIFICATIONS DO NOT UNDERTAKE TO INDICATE EVERY ITEM OF MATERIAL, EQUIPMENT, OR LABOR REQUIRED TO PRODUCE A COMPLETE AND PROPERLY OPERATING INSTALLATION.
5. PERMITS: OBTAIN ALL NECESSARY PERMITS, LICENSES, AND INSPECTIONS AS REQUIRED BY ANY OF THE FOREGOING AUTHORITIES AND PAY FOR ALL OTHER COSTS IN CONNECTION WITH THE WORK.
6. INSPECTIONS: CONTRACTOR SHALL NOT CONCEAL ANY WORK UNTIL INSPECTED AND APPROVED BY ELECTRICAL INSPECTOR AND/OR ARCHITECT/ENGINEER.
7. REGULATIONS: ALL ELECTRICAL WORK SHALL BE PERFORMED IN STRICT ACCORDANCE WITH THE LATEST ADOPTED NATIONAL ELECTRICAL CODE (NEC) AND ALL OTHER APPLICABLE FEDERAL, STATE, AND LOCAL BUILDING CODES, RULES, REGULATIONS AND AUTHORITIES HAVING JURISDICTION. WORKMANSHIP: ALL WORK SHALL BE INSTALLED IN A NEAT AND WORKMANLIKE MANNER IN ACCORDANCE WITH APPLICABLE NECA STANDARDS SUBJECT TO THE APPROVAL OF THE OWNER OR OWNER'S AUTHORIZED REPRESENTATIVE. RACEWAY, FIXTURES, AND WIRING DEVICES SHALL BE PROPERLY ALIGNED, LEVELED, PLUMBED AND SUPPORTED. RACEWAY SHALL BE GROUPED AND INSTALLED IN RUNS WHICH ARE PARALLEL AND PERPENDICULAR WITH BUILDING LINES.
8. COORDINATION: PRIOR TO COMMENCEMENT OF WORK, EXAMINE ALL CONSTRUCTION DRAWINGS AND SPECIFICATIONS AND COORDINATE WITH ALL OTHER TRADES INCLUDING GENERAL CONTRACTOR, MECHANICAL CONTRACTOR, LOW VOLTAGE CONTRACTOR, AND SECURITY CONTRACTOR IN ORDER TO BECOME FAMILIAR WITH ALL ASPECTS OF THE DESIGN AFFECTING THE ELECTRICAL WORK AND TO CONFIRM SITE SPECIFIC INSTALLATION REQUIREMENTS. REFER TO ARCHITECTURAL DRAWINGS AND EQUIPMENT CUT SHEETS FOR EQUIPMENT POWER/CONTROL REQUIREMENTS, CONNECTIONS, WIRING DEVICE TYPE, MOUNTING HEIGHTS, MEANS OF ATTACHMENT, AND LOCATIONS OF ALL NEW EQUIPMENT AND ELECTRICAL DEVICES. FIELD VERIFY EXACT NAMEPLATE DATA ON ALL EQUIPMENT FURNISHED UNDER OTHER DIVISIONS AND/OR BY THE OWNER PRIOR TO THE INSTALLATION OF ELECTRICAL WORK AND MAKE ANY ADJUSTMENTS TO OUTLETS, CONDUITS, WIRE, AND/OR CIRCUIT BREAKER/FUSE RATINGS AS REQUIRED TO MATCH EQUIPMENT ACTUALLY FURNISHED.
9. EQUIPMENT AND DEVICE LOCATIONS: LOCATIONS ON THE ELECTRICAL PLANS ARE APPROXIMATE. EXACT LOCATIONS SHALL BE DETERMINED FROM ARCHITECTURAL PLANS, SECTIONS, AND ELEVATIONS. FINAL LOCATION OF EQUIPMENT AND DEVICES TO BE COORDINATED WITH ARCHITECT, OWNER, AND/OR OWNER'S REPRESENTATIVE. VERIFY STUB-UP LOCATION FOR ALL UNDER SLAB CONDUITS PRIOR TO ROUGH-IN.
10. UTILITIES: UTILITY COORDINATION INFORMATION SHOWN ON THE DRAWINGS SHALL BE CONSIDERED PRELIMINARY. COORDINATE WITH LOCAL POWER COMPANY AND TELCO (TELEPHONE/CABLE/INTERNET) PROVIDERS FOR SERVICE REQUIREMENTS AND VERIFY FINAL POINT OF CONNECTION PRIOR TO MOBILIZATION IN THE FIELD. NOTIFY UTILITIES OF COMMENCEMENT OF WORK AND MAKE ALL ARRANGEMENTS FOR TEMPORARY AND PERMANENT SERVICES. PROVIDE ALL EQUIPMENT, MATERIAL, AND LABOR TO MEET UTILITY REQUIREMENTS. INCLUDE ALL ASSOCIATED COSTS TO SET-UP AND COORDINATE TEMPORARY AND PERMANENT ELECTRIC AND TELCO SERVICES IN BID. ALL MATERIALS MUST BE APPROVED BY THE LOCAL UTILITY. IF REQUIRED, THE ELECTRICAL CONTRACTOR SHALL PROVIDE CONDUIT SYSTEMS FOR UTILITY MEDIUM VOLTAGE FROM UTILITY PRIMARY TO POINT OF INTERCEPTION AT EDGE OF PROPERTY LINE.
11. TEMPORARY POWER: PROVIDE TEMPORARY SERVICE FOR LIGHTING, POWER EQUIPMENT (DRILLS, SAWS, ETC.), AND CONTRACTOR MOBILIZED WORK TRAILERS. VERIFY TEMPORARY SERVICE REQUIREMENTS WITH GENERAL CONTRACTOR. TEMPORARY LIGHTING AND POWER SHALL MEET OSHA REQUIREMENTS AND LOCAL CODE.
12. INTERRUPTION OF SERVICE: COORDINATE ALL WORK REQUIRING INTERRUPTION OF SERVICE (POWER, SECURITY, DATA, FIRE ALARM, ETC) WITH ALL AFFECTED PARTIES, INCLUDING BUT NOT LIMITED TO GENERAL CONTRACTOR, BUILDING OWNER AND/OR LANDLORD, TENANT(S), AND OWNER AND/OR OWNER'S REPRESENTATIVE AND OBTAIN WRITTEN PERMISSION FROM SAID PARTIES AT LEAST 48 HOURS PRIOR TO SHUT DOWN. PROVIDE NOTICE TO ALL OTHER TRADES OF ALL SCHEDULED INTERRUPTIONS. ALL OUTAGES OR INTERRUPTIONS SHALL BE KEPT TO MINIMUM DURATION. PROVIDE TEMPORARY SERVICE DURING OUTAGE WHEN REQUIRED BY AFFECTED PARTIES. CONTRACTOR SHALL BE RESPONSIBLE TO PROVIDE PERSONNEL FOR FIRE AND SECURITY WATCH DURING OUTAGES TO FIRE AND SECURITY SYSTEMS.
13. PRODUCTS: ALL ELECTRICAL MATERIALS SHALL BE NEW EXCEPT WHERE SPECIFICALLY NOTED AS EXISTING TO BE REUSED. MATERIAL AND METHODS OF INSTALLATION SHALL CONFORM TO THE STANDARDS OF UNDERWRITERS LABORATORIES, INC. (UL), ANSI, NFPA, ADA, AND ALL OTHER APPLICABLE LOCAL ORDINANCES. DEFECTIVE EQUIPMENT AND/OR EQUIPMENT DAMAGED DURING INSTALLATION AND/OR TESTING SHALL BE REPLACED OR REPAIRED IN A MANNER MEETING THE APPROVAL OF THE ARCHITECT AND THE ENGINEER. PROPOSED EQUIPMENT SHALL BE NRTL LISTED, LABELED, OR APPROVED.
14. SHOP DRAWINGS AND SUBMITTALS: SUBMIT MANUFACTURER'S STANDARD PRODUCT INFORMATION, PERFORMANCE SPECIFICATIONS, ELECTRICAL RATINGS, PHYSICAL DIMENSIONS, AND OTHER INFORMATION NECESSARY FOR ENGINEER TO ENSURE COMPLIANCE WITH SPECIFICATIONS. SHOP DRAWINGS SHALL BE SUBMITTED FOR APPROVAL PRIOR TO ORDERING AND INSTALLING ANY EQUIPMENT. SUBMITTALS AND SHOP DRAWINGS SHALL CLEARLY INDICATE ITEMS TO BE REVIEWED BY HIGHLIGHTING, AND ITEMS NOT TO BE REVIEWED SHALL BE CROSSED OUT. SUBMITTALS WITHOUT HIGHLIGHTING AND CROSSED OUT ITEMS SHALL NOT BE REVIEWED. ALL SUBMITTALS MUST BE RECEIVED BY THE ENGINEER WITHIN 30 DAYS OF CONTRACT AWARD TO THE GENERAL CONTRACTOR; NO EXCEPTIONS. EQUIPMENT ORDERED OR INSTALLED WITHOUT A FAVORABLY REVIEWED SUBMITTAL IS DONE AT THE CONTRACTOR'S OWN RISK.
15. VALUE ENGINEERING SUBMITTALS: VALUE ENGINEERING SUBMITTALS SHALL BE LABELED AS SUCH AND INDICATE A 'DEDUCT' OR CREDIT BACK TO THE OWNER. VE SUBMITTALS NOT CLEARLY LABELED OR NOT INCLUDING A DEDUCT SHALL BE REJECTED.
16. SUBSTITUTION AND ALTERATIONS: THERE SHALL BE NO DEVIATION FROM THE REQUIREMENTS HEREIN WITHOUT THE WRITTEN APPROVAL OF THE ENGINEER. CONTRACTOR SHALL ASSUME RESPONSIBILITY FOR ALL COSTS INCURRED RESULTING FROM SUBSTITUTION OF EQUIPMENT AS WELL AS THE PERFORMANCE AND SPACE REQUIREMENTS OF SUCH EQUIPMENT.
    SUBSTITUTIONS AND ALTERATIONS OF OTHER DISCIPLINE'S EQUIPMENT: SUBSTITUTED AND ALTERED EQUIPMENT BY OTHER DISCIPLINES SHALL INCLUDE ALL MATERIAL AND LABOR COSTS FOR ELECTRICAL CONTRACTOR TO PROVIDE COMPLETE AND FULLY FUNCTIONAL SYSTEMS TO ACCOMMODATE THESE SUBSTITUTED AND ALTERED EQUIPMENT. THESE ADDITIONAL ELECTRICAL COSTS MUST BE ABSORBED BY THE OTHER DISCIPLINE'S CONTRACTOR IN ORDER FOR THE SUBSTITUTED OR ALTERED GEAR TO BE ACCEPTED.
17. FAULT CURRENT PROTECTION: ALL EQUIPMENT SHORT CIRCUIT CURRENT RATINGS (SCCR) AND OVERCURRENT PROTECTIVE DEVICE AMPERE INTERRUPTING CAPACITY (AIC) RATINGS SHALL BE GREATER THAN THE AVAILABLE FAULT CURRENT AT EACH RESPECTIVE PIECE OF EQUIPMENT. COORDINATE EQUIPMENT SCCR AND OVERCURRENT PROTECTIVE DEVICE AIC RATINGS WITH POWER COMPANY. OBTAIN THE AVAILABLE FAULT CURRENT AT TRANSFORMER SECONDARY FROM THE POWER COMPANY AND PROVIDE PROPOSED EQUIPMENT SCCR AND OVERCURRENT PROTECTIVE DEVICE AIC RATINGS FOR ENGINEER APPROVAL. OVERCURRENT PROTECTIVE DEVICES AIC RATINGS SHALL BE FULLY RATED WITH A MINIMUM 10% MARGIN BETWEEN THE CALCULATED FAULT LEVEL AND THE SPECIFIED SHORT CIRCUIT RATING OF THE EQUIPMENT UNO ON PLANS.
18. VOLTAGE DROP: WIRE SIZES SPECIFIED IN THESE PLANS ARE MINIMUM WIRE SIZES. THE ELECTRICAL CONTRACTOR IS RESPONSIBLE FOR INCREASING WIRE SIZES BASED ON ACTUAL CIRCUIT LENGTH TO MAINTAIN VOLTAGE DROP AT A MAXIMUM OF 3% FOR BRANCH CIRCUITS AND 2% FOR FEEDERS. THE CUMULATIVE VOLTAGE DROP FROM THE SOURCE TO THE END DEVICE SHALL NOT EXCEED 5% OF NOMINAL SYSTEM VOLTAGE.
19. WIRING: ALL CONDUCTORS CARRYING 50 VOLTS OR MORE SHALL BE MINIMUM #12 AWG, CU, UNO. PROVIDE DUAL RATED TYPE THHN-THWN FOR ABOVE GROUND AND TYPE THWN OR XHHW FOR BELOW GROUND, COORDINATE INSULATION TYPES WITH ENVIRONMENTAL CONDITIONS, NEC REQUIREMENTS, AND CONDUIT FILL REQUIREMENTS. CONDUCTORS #12 AND #10 SHALL BE SOLID, CONDUCTORS #8 AND LARGER SHALL BE STRANDED. ALL CONDUCTOR SIZES ARE BASED ON COPPER WITH 60°C INSULATION FOR CIRCUITS RATED 100A OR LESS AND 75°C FOR CIRCUITS RATED MORE THAN 100A
22. LOW VOLTAGE WIRING: LOW VOLTAGE WIRING FOR SPECIAL SYSTEMS IS PERMITTED TO BE FREE-WIRED ONLY ABOVE ACCESSIBLE CEILINGS AND BELOW RAISED FLOOR SYSTEMS, UNO. FREE-WIRED CABLE SHALL BE UL LISTED, PLENUM RATED. LOW VOLTAGE WIRING IN OPEN CEILINGS, HARD CEILINGS, WALLS, PASSING THROUGH ADJACENT TENANT SPACES, OR ROUTED UNDERGROUND OR BELOW SLAB SHALL BE INSTALLED IN CONDUIT. LOW VOLTAGE WIRING IS NOT SHOWN ON PLANS, UNLESS SPECIFICALLY CALLED OUT.
23. COLOR CODING: FOR EXISTING WIRING SYSTEMS, COLOR CODING SHALL FOLLOW EXISTING SITE REQUIREMENTS. FOR NEW INSTALLATIONS OR WHERE EXISTING INSTALLATIONS DO NOT HAVE A COLOR CODING CONVENTION, THE FOLLOWING SYSTEMS OF COLOR CODING SHALL BE STRICTLY ADHERED TO AND FOLLOWED THROUGHOUT:

CONDUCTOR	480Y/277V, 3-PH	208Y/120V, 3-PH	240D/120V, 3-PH	240/120V, 1-PH
PHASE A:	BROWN	BLACK	BLACK	BLACK
PHASE B:	ORANGE	RED	ORANGE	RED
PHASE C:	YELLOW	BLUE	BLUE	-
NEUTRAL:	GRAY	WHITE	WHITE	WHITE
EQUIPMENT GROUND:	GREEN	GREEN	GREEN	GREEN
ISOLATED GROUND:	---	GREEN/YELLOW	GREEN/YELLOW	GREEN/YELLOW

24. SHARED CIRCUIT NEUTRALS: SHARED CIRCUIT NEUTRALS SHALL NOT BE USED UNLESS INDICATED OTHERWISE ON PANEL SCHEDULE. WHERE USED, CIRCUIT BREAKER HANDLE TIES SHALL BE PROVIDED TO DISCONNECT POWER TO EACH PHASE CONDUCTOR OF THE SHARED NEUTRAL CIRCUIT.
25. GROUNDING: ALL CIRCUITS SHALL BE PROVIDED WITH AN INSULATED GREEN COPPER EQUIPMENT GROUND CONDUCTOR SIZED PER NEC. THE EQUIPMENT GROUND CONDUCTOR SHALL BE INCREASED IN SIZE BY EQUAL PROPORTION TO THE PHASE CONDUCTORS WHENEVER THE PHASE CONDUCTORS HAVE BEEN UPSIZED TO MAINTAIN ACCEPTABLE VOLTAGE DROP LEVELS. EQUIPMENT GROUNDS SHALL BE BONDED TO ALL EQUIPMENT AND DEVICES. USE OF METALLIC CONDUIT SHALL NOT TAKE THE PLACE OF AN EQUIPMENT GROUND CONDUCTOR.
26. CONDUIT: ALL WIRING SHALL BE INSTALLED IN CONDUIT, MINIMUM 1/2" FOR INDOOR AND 3/4" FOR OUTDOOR AND UNDER SLAB. EMT IS ACCEPTABLE WITH COMPRESSION FITTINGS ONLY. ALL HOMERUNS SHALL BE HARD PIPED. MC IS ACCEPTABLE FOR FIXTURE WHIPS ONLY. ALL CONDUIT AND WIRING SHALL BE CONCEALED IN FLOORS, WALLS, AND/OR CEILINGS UNLESS SPECIFICALLY NOTED OTHERWISE. CHANNEL EXISTING WALLS WHERE REQUIRED. WHERE CONDUITS ARE UNABLE TO BE CONCEALED, HARD PIPED CONDUIT SHALL BE USED AND PAINTED TO MATCH ADJOINING SURFACE.
27. UNDERGROUND CONDUITS: MINIMUM BURIAL DEPTH SHALL BE 24" TO TOP OF CONDUIT. PROVIDE DETECTABLE WARNING TAPE WHERE REQUIRED BY AHJ OR CODE.
28. ROUTING: FOR CLARITY, CONDUIT ROUTING SHOWN IS SYMBOLIC AND DIAGRAMMATIC. INSTALL CONDUIT TO FIT ACTUAL FIELD CONDITIONS.
29. OPEN CEILINGS: IN AREAS WITHOUT CEILINGS OR WHERE ANY CONDUITS, CONDUCTORS, FEEDERS, OR LOW VOLTAGE CABLING IS VISIBLE, ALL WIRING SHALL BE HARD PIPED IN CONDUIT. BX, AC, AND MC CABLE OR FLEX CONDUIT ARE NOT PERMITTED. CONDUITS SHALL BE ROUTED TIGHT TO DECK EITHER PARALLEL OR PERPENDICULAR TO BUILDING LINES, GROUPED ALONG STRUCTURAL MEMBERS, AND DROP AT POINT OF CONNECTION. MAINTAIN 1-1/2" CLEARANCE FROM ROOF DECK PER NEC 300.4(E). WHERE EXPOSED TO VIEW, ALL MATERIALS (CONDUIT, JUNCTION BOXES, ETC.) SHALL BE INSTALLED IN AN ORDERLY FASHION AND SHALL BE CLEAN, FREE FROM ALL VISIBLE MARKINGS, AND PAINTED TO MATCH ADJOINING SURFACE. JUNCTION BOXES SHALL HAVE CIRCUIT NUMBERS WRITTEN ON THE INSIDE OF THE JUNCTION BOX COVER.
30. PENETRATIONS: CONTRACTOR SHALL INSPECT AREA OF WORK AND PERFORM GROUND PENETRATING RADAR (GPR) SCAN OR X-RAY ALL PROPOSED PENETRATIONS PRIOR TO WORK TO DETERMINE EXACT LOCATIONS OF STRUCTURAL REINFORCEMENT OR EMBEDDED SYSTEMS. COORDINATE FLOOR AND WALL PENETRATIONS WITH STRUCTURAL ENGINEER. ALL PENETRATIONS SHALL BE SEALED BY APPROVED MEANS TO PREVENT ENERGY LOSS AND MOISTURE AND RODENT INTRUSION.
31. FIRE-RATED PENETRATIONS: ALL PENETRATIONS THROUGH FIRE-RATED SLABS AND/OR PARTITIONS SHALL BE SEALED WITH A UL LISTED FIRE-RATED ASSEMBLY OF EQUAL OR GREATER RATING THAN THAT OF THE EXISTING SLAB OR PARTITION.
32. TRENCHING: FIELD VERIFY UNDERGROUND UTILITIES PRIOR TO TRENCHING. ALL PROPOSED EXCAVATION IN THE VICINITY OF EXISTING UTILITIES, PIPING SYSTEMS, OR SIMILAR SHALL BE HAND EXCAVATED. HAND EXCAVATE IN THE VICINITY OF EXISTING TREES WHERE TRENCHING MAY ENCOUNTER TREE ROOT SYSTEM.
33. SLEEVES: SLEEVES AND SLEEVE SEALS SHALL BE PROVIDED AT PENETRATIONS OF WALL ASSEMBLIES.
34. SUPPORTS: ALL CONDUIT AND CABLING SHALL BE PROPERLY SUPPORTED AS REQUIRED BY CODE.
35. REPAIRS: THE CONTRACTOR SHALL REPAIR ALL WALL, CEILING, FLOOR, OR ROOF OPENINGS WHICH ARE CREATED BY DEMOLITION OR PENETRATION. THE REPAIRS SHALL BE WITH MATERIAL AND FINISHES TO MATCH EXISTING ADJACENT UNDISTURBED FINISHED SURFACES.
36. IDENTIFICATION: ALL ELECTRICAL DISTRIBUTION EQUIPMENT, TRANSFORMERS, PANELBOARDS, AND OTHER ENCLOSED EQUIPMENT SHALL BE IDENTIFIED AS INDICATED IN THE CONTRACT DOCUMENTS. SAID IDENTIFICATION SHALL CONSIST OF PERMANENTLY ATTACHED ENGRAVED LAMINATED PLASTIC NAMEPLATES. EACH BRANCH CIRCUIT OVERCURRENT PROTECTION DEVICE SHALL BE IDENTIFIED BY CIRCUIT NUMBER AND SCHEDULED INSIDE PANEL DOOR WITH A TYPEWRITTEN CIRCUIT DIRECTORY. EACH BRANCH CIRCUIT SPLICE OR TERMINATION SHALL BE IDENTIFIED BY PANEL AND CIRCUIT DESIGNATION SHOWN ON THE JUNCTION OR OUTLET BOX, OR UPON INDIVIDUAL WIRES IN CASES WHERE MORE THAN ONE OF EACH PHASE CONDUCTOR OCCUR. RECEPTACLES AND SWITCH COVER PLATES SHALL BE LABELED WITH PANEL AND CIRCUIT DESIGNATION USING TYPEWRITTEN CHARACTERS OF CONTRASTING COLOR (BLACK OR WHITE) ON CLEAR ADHESIVE BACKED LABELS OR FACTORY ENGRAVED COVER PLATES.
37. PANEL CLEARANCE: MAINTAIN ALL WORKING SPACE AND DEDICATED EQUIPMENT SPACE CLEARANCES AS REQUIRED BY ARTICLE 110 OF THE NEC. GENERAL CONTRACTOR SHALL COORDINATE BETWEEN TRADES SO THAT NO FOREIGN SYSTEMS ARE LOCATED IN THE DEDICATED EQUIPMENT SPACE. IN THE EVENT THAT FOREIGN SYSTEMS ARE INSTALLED ABOVE A PANEL'S DEDICATED EQUIPMENT SPACE, THE GENERAL CONTRACTOR SHALL ABSORB THE COST TO RELOCATE THE FOREIGN SYSTEMS.
38. WIRING DEVICES: WIRING DEVICES AND COVER PLATES SHALL BE DECORA STYLE OF COLORS SELECTED BY THE ARCHITECT OR INTERIOR DESIGNER. GANG ADJACENT DEVICES WITH A SINGLE ONE-PIECE COVER PLATE, UNO. FOR REMODELS, ALL DEVICES AND COVER PLATES WITHIN THE CONTRACT AREA SHALL BE REPLACED WITH NEW DECORA STYLE DEVICES AND COVER PLATES, UNO.
39. CLEANING: UPON COMPLETION OF WORK, THE CONTRACTOR SHALL THOROUGHLY CLEAN THE CONTRACT AREA AND ALL OTHER AREAS USED FOR STORAGE, STAGING, ETC. ALL EQUIPMENT AND DEVICES SHALL BE CLEANED AND POLISHED IN ACCORDANCE WITH MANUFACTURER'S RECOMMENDATIONS. SOAP AND WATER CLEANING OR OTHER METHODS THAT LEAVE A FILM SHALL BE CORRECTED UPON REQUEST BY THE ENGINEER OR ARCHITECT.
40. TESTING: THE CONTRACTOR SHALL TEST ALL EQUIPMENT INSTALLED UNDER THIS CONTRACT AND DEMONSTRATE TO THE OWNER ITS PROPER OPERATION. AT THE TIME OF FINAL INSPECTION AND TESTS, ALL CONNECTIONS AT PANELBOARDS, CONTROL PANELS, DEVICES, AND EQUIPMENT AND ALL SPLICES MUST BE COMPLETED. EACH BRANCH CIRCUIT AND ITS RESPECTIVE CONNECTED EQUIPMENT MUST TEST FREE OF SHORT CIRCUITS.
41. TRAINING: OWNER AND/OR OWNER'S REPRESENTATIVE SHALL BE TRAINED ON THE USE OF ANY NEW ELECTRICAL EQUIPMENT AND LIGHTING CONTROLS PRIOR TO FINAL ACCEPTANCE.
42. FINAL ACCEPTANCE: AT THE END OF CONSTRUCTION, A FINAL WALK-THROUGH SHALL BE PERFORMED. ALL DEFICIENCIES IDENTIFIED DURING FINAL INSPECTION SHALL BE CORRECTED.
43. CERTIFICATES OF APPROVAL: ALL CERTIFICATES OF APPROVAL SHALL BE IN DUPLICATE, DELIVERED TO THE ARCHITECT, AND BECOME THE PROPERTY OF THE OWNER.
44. PROJECT RECORD DOCUMENTS: THE ELECTRICAL CONTRACTOR SHALL MAINTAIN AT THE SITE, FOR THE OWNER, ONE COPY OF ALL DRAWINGS, ADDENDA, APPROVED SHOP DRAWINGS, REVISIONS AND OTHER MODIFICATIONS IN GOOD ORDER AND MARKED TO RECORD ALL CHANGES MADE DURING CONSTRUCTION. THE SET OF DRAWINGS AND OTHER INFORMATION SHALL BE DELIVERED TO THE OWNER WITHIN 30 DAYS AFTER THE DATE OF SYSTEM ACCEPTANCE AND ONE COPY GIVEN TO THE ENGINEER UPON COMPLETION OF WORK. DRAWINGS SHALL INCLUDE AT A MINIMUM:
    A. SINGLE-LINE DIAGRAM OF THE BUILDING ELECTRICAL DISTRIBUTION SYSTEM AND
    B. FLOOR PLANS INDICATING LOCATION AND AREA SERVED FOR ALL DISTRIBUTION.
45. OPERATIONS AND MAINTENANCE (O&M) MANUALS: PROVIDE TWO COPIES OF OPERATIONS AND MAINTENANCE MANUALS TO THE BUILDING OWNER IN HARD COPY AND ELECTRONIC FORMAT. HARD COPIES SHALL BE COMPILED AND ORGANIZED IN A BINDER. THE MANUALS SHALL INCLUDE, AT A MINIMUM, THE FOLLOWING:
    A. SUBMITTAL DATA STATING EQUIPMENT RATING AND SELECTED OPTIONS FOR EACH PIECE OF EQUIPMENT REQUIRING MAINTENANCE.
    B. OPERATING AND MAINTENANCE MANUALS FOR EACH PIECE OF EQUIPMENT REQUIRING MAINTENANCE. REQUIRED ROUTINE MAINTENANCE ACTIONS SHALL BE CLEARLY IDENTIFIED.
    C. NAMES AND ADDRESSES OF AT LEAST ONE QUALIFIED SERVICE AGENCY.
    D. WARRANTY INFORMATION.
46. WARRANTY: THE ENTIRE ELECTRICAL SYSTEM INSTALLED UNDER THIS CONTRACT SHALL BE HANDED OVER IN PROPER WORKING ORDER. ANY WORK OR MATERIALS WHICH DEVELOP DEFECTS, EXCEPT FROM ORDINARY WEAR AND TEAR, WITHIN ONE YEAR FROM THE DATE OF FINAL ACCEPTANCE SHALL BE REPLACED WITHOUT CHARGE. IF MATERIALS HAVE A STANDARD WARRANTY GREATER THAN ONE YEAR, THE MANUFACTURER'S STANDARD WARRANTY SHALL APPLY. BENEFICIAL USE SHALL NOT BE CONSTRUED AS FINAL ACCEPTANCE. THE ELECTRICAL CONTRACTOR SHALL, DURING THE ONE YEAR GUARANTEE PERIOD, BE RESPONSIBLE FOR THE PROPER REPAIR AND ADJUSTMENTS OF ALL ELECTRICAL SYSTEMS AND EQUIPMENT, APPARATUS, DEVICES, ETC. INSTALLED BY HIM, AND DO ALL WORK NECESSARY TO ENSURE

PRAXIS3

100 Peachtree St NW
Suite 1450
Atlanta, GA 30303

404-875-4500 tel
www.praxis3.com

GEORGIA REGISTERED No. 041568 PROFESSIONAL ENGINEER RAHN ONEAL WILLIAMS

Copyright (c) 2024 Praxis3, LLC

All reports, plans, specifications, computer files, field data, notes and other documents and instruments prepared by Praxis3 shall retain all common law, statutory and other reserved rights, including copyright thereto.

This drawing may not be reproduced in whole or in part without written permission of Praxis3. It is to be returned upon request. Scales as stated are valid on the original drawings.

Rev	Date	Comments
	07/02/2026	PERMIT SET

Client:

FIFTH THIRD BANK

Project Number: 26032
Project Name:

FIFTH THIRD BANK WATSON 1,900 SF

2711 WATSON BOULEVARD
WARNER ROBBINS, GA 31093

Key Plan:

Sheet Title:

ELECTRICAL GENERAL NOTES

Sheet Number:

E-002

6/30/2026 2:31:56 PM

PART 1 - GENERAL

1.01 RELATED DOCUMENTS
A. The general provisions of the contract including General and Special Conditions and General Requirements shall apply to all work under this Section.

1.02 REQUIREMENTS OF REGULATORY AGENCIES AND STANDARDS
A. Equipment, fixtures, material and installation shall conform to the requirements of the local Building Department, the serving utility companies, the National Electrical Code, National Electrical Safety Code, Life Safety Code, Occupational Safety and Health Act, and applicable national, state and local codes, ordinances and regulations.
B. All equipment shall be equal to or exceed the minimum requirements of NEMA, IEEE, and UL.
C. Should any change in Drawings or Specifications be required to comply with governmental regulations, the Contractor shall notify Architect/Engineer prior to execution of the Work. The work shall be carried out according to the requirements of such code in accordance with the instruction of the Architect/Engineer and at no additional cost to the Owner.
D. The provisions of Standards, Codes, Laws, Ordinances, etc., shall be considered minimum requirements. In case of conflict between their published requirements, the Owner's Representative shall determine which is to be followed and his decision shall be binding. Specific requirements of this specification or the drawings, which exceed the published requirements, shall take precedence over them.

1.03 FEES
A. All local fees, permits, and services of inspection authorities shall be obtained and paid for by the Contractor. The Contractor shall
B. cooperate fully with local companies with respect to their services. Contractor shall include in his bid any costs to be incurred
C. relative to power service (primary and/or secondary) and telephone service.

1.04 SCOPE OF WORK
A. This division of the specifications covers the electrical systems of the project. It includes work performed by the electrical trades as well as trades not normally considered as electrical trades.
B. Provide all incidentals, equipment, appliances, services, hoisting, scaffolding, supports, tools, supervision, labor consumable items, fees, licenses, etc., necessary to provide complete systems. Perform start-up and checkout on each item and system to provide fully operable systems.
C. Examine and compare the Electrical Drawings with these specifications, and report any discrepancies between them to the Architect/Engineer and obtain from him written instructions for changes necessary in the work. At time of bid the most stringent requirements must be included in the bid.
D. Examine and compare the Electrical Drawings and Specifications with the Drawings and Specifications of other trades, and report any discrepancies between them to the Architect/Engineer and obtain from him written instructions for changes necessary in the work. At time of bid, the most stringent requirements must be included in said bid.
E. Install and coordinate the electrical work in cooperation with other trades installing interrelated work. Before installation, make proper provisions to avoid interferences in a manner approved by the Architect/Engineer. All changes required in the work of the Contractor, caused by his neglect to do so, shall be made by him at his own expense.
F. It is the intent of the Drawings and Specifications to provide a complete workable system ready for the Owner's operation. Any item not specifically shown on the Drawings or called for in the Specifications, but normally required to conform with the intent, are to be considered a part of the Contract.
G. All materials furnished by the Contractor shall be new and unused (temporary lighting and power products are excluded) and free from defects. All materials used shall bear the Underwriter's Laboratory, Inc. label provided a standard has been established for the material in question.
H. Except for conduit, conduit fittings, outlet boxes, wire and cable, all items of equipment or material shall be the product of one manufacturer throughout the entire project. Multiple manufacturers will not be permitted.

1.05 REFERENCES
A. Utilize the following abbreviations and definitions for discernment within the Drawings and Specifications.
1. Abbreviations
- NEC National Electrical Code.
- OSHA Occupational Safety and Health Act.
- ANSI American National Standards Institute.
- NFPA National Fire Protection Association.
- ASA American Standards Association.
- IEEE Institute of Electrical and Electronics Engineers.
- NEMA National Electrical Manufacturers Association.
- UL Underwriters' Laboratories, Inc.
- IES Illuminating Engineering Society.
- ICEA Insulated Cable Engineers Association.
- ASTM American Society of Testing Materials.
- ETL Electrical Testing Laboratories, Inc.
- CBM Certified Ballast Manufacturers.
- EIA Electronic Industries Association.
- LED Light Emitting Diode.
- OEM Original Equipment Manufacturer.

1.06 DEFINITIONS
A. "PROVIDE" means to supply, purchase, transport, place, erect, connect, test, and turn over to Owner, complete and ready for regular operation, the particular Work referred to.
B. "INSTALL" means to join, unite, fasten, link, attach, set up, or otherwise connect together before testing and turning over to Owner, complete and ready for regular operation, the particular Work referred to.
C. "FURNISH" means to supply all materials, labor, equipment, testing apparatus, controls, tests, accessories, and all other items customarily required for the proper and complete application for the particular Work referred to.
D. "WIRING" means the inclusion of all raceways, fittings, conductors, connectors, tape, junction and outlet boxes, connections, splices, and all other items necessary and/or required in connection with such Work.
E. "CONDUIT" means the inclusion of all fittings, hangers, supports, sleeves, etc.
F. "AS DIRECTED" means as directed by the Architect/Engineer, or his representative.
G. "CONCEALED" means embedded in masonry or other construction, installed behind wall furring or within double partitions, or installed above hung ceilings.

1.07 COORDINATION OF THE WORK

A. Certain materials will be provided by other trades. Examine the Contract Documents to ascertain these requirements.
B. Carefully check space requirements with other trades and the physical confines of the area to insure that all material can be installed in the spaces allotted thereto including finished suspended ceilings and the spaces within the existing building. Make modifications thereto as required and approved.
C. Transmit to other trades all information required for work to be provided under their respective Sections in ample time for installation.
D. Wherever work interconnects with work of other trades, coordinate with other trades to insure that all trades have the information necessary so that they may properly install all the necessary connections and equipment. Identify all items of work that require access so that the ceiling trade will know where to install access doors and panels.
E. Coordinate, project and schedule work with other trades in accordance with the construction sequence.
F. The Drawings show only the general run of raceways and approximate location of outlets. Any significant changes in location of outlets, cabinets, etc., necessary in order to meet field conditions shall be brought to the immediate attention of the Architect/Engineer and receive his approval before such alterations are made. All such modifications shall be made without additional cost to the Owner.
G. Obtain from the Architect/Engineer in the field the location of such outlets or equipment not definitely located on the Drawings.
H. Circuit "tags" in the form of arrows are used where shown to indicate the home runs of raceways to electrical distribution points. These tags show the circuits in each home run and the panel designation. Show the actual circuits numbers on the finished record drawings and on panel directory card. Where circuiting is not indicated, Electrical Subcontractor must provide required circuiting in accordance with the loading indicated on the drawings and/or as directed.
I. Adjust location of conduits, panels, equipment, pull boxes, fixtures, etc. to accommodate the work to prevent interferences, both anticipated and encountered. Determine the exact route and location of each raceway prior to fabrication.
1. Right-of-Way:
a. Lines that pitch have the right-of-way over those that do not pitch. For example: steam, condensate, and plumbing drains normally have right-of-way. Lines whose elevations cannot be changed to have right-of-way over lines whose elevations can be changed.
b. Make offsets, transitions and changes in direction in raceways as required to maintain proper headroom in pitch of sloping lines whether or not indicated on the Drawings.
J. Wherever the work is of sufficient complexity, prepare additional Detail Drawings to scale similar to that of the bidding Drawings, prepared on tracing medium of the same size as Contract Drawings. With these layouts, coordinate the work with the work of other trades. Such detailed work to be clearly identified on the Drawings as to the area to which it applies. Submit for review Drawings clearly showing the work and its relation to the work of other trades before commencing shop fabrication or erection in the field.
K. Coordinate with the local Electric Utility Company and the local Telephone Company as to their requirements for service connections and provide all necessary materials, labor and testing.
L. Coordinate with contractors for work under other Divisions of this specification for all work necessary to accomplish this contractor's work.

1.08 EXAMINATION OF SITE
A. Prior to the submitting of bids, the Contractor shall visit the site of the job and shall familiarize himself with all conditions affecting the proposed installation and shall make provisions as to the cost thereof. Failure to comply with the intent of this paragraph will in no way relieve the contractor of performing all necessary work shown on the Drawings.

1.09 PROGRESS OF WORK
A. The Contractor shall order the progress of his work to conform to the progress of the work of other trades and shall complete the entire installation as soon as the conditions of the building will permit. Any cost resulting from the defective or ill-timed work performed under this section shall be borne by the Contractor.

1.10 DELIVERY, STORAGE, AND HANDLING
A. Ship and store all products and materials in a manner that will protect them from damage, weather and entry of debris. If items are damaged, do not install, but take immediate steps to obtain replacement or repair. Any such repairs shall be subject to review and acceptance of the Architect/Engineer.
B. Deliver materials in manufacturer's unopened container fully identified with manufacturer's name, trade name, type, class, grade, size and color.
C. Store materials suitably sheltered from the elements, but readily accessibly for inspection by the Architect/Engineer until installed. Store all items subject to moisture damage in dry, heated spaces.

1.11 EQUIPMENT ACCESSORIES
A. Provide supports, hangers and auxiliary structural members required for support of the work.
B. Furnish and set all sleeves for passage of raceways through structural, masonry and concrete walls of floors and elsewhere as will be required for the proper protection of each raceway passing through building surfaces.
C. Wall mounted equipment may be directly secured to wall by means of steel bolts. Maintain at least 1" air space between equipment and supporting wall. Groups or arrays of equipment may be mounted on adequately sized steel angles, channels, or bars. Prefabricated steel channels providing a high degree of mounting flexibility, such as those manufactured by Kindorf, Glob-Strutt and Unistrut, may be used for mounting arrays of equipment.

1.12 OPERATIONS AND MAINTENANCE MANUALS
General: Provide operations & maintenance (O&M) manuals in accordance with the Contract Documents.
1. Provide two (2) copies of each manual.
2. Manuals shall be 8-1/2 inches X 11 inches in hard cover 3-ring loose-leaf binders.
3. Manuals shall be complete and in Owner's hands prior to turning building over to Owner and at least 10 days prior to instruction to operating personnel.
B. Provide manufacturer's literature as regularly published by the respective manufacturers for proper preventative and comprehensive maintenance.
C. Provide O&M manuals including but not limited to the following.
1. Alphabetical list of all system components, with the name, address, and 24-hour phone number of the company responsible for servicing each item during the first year of operation.
Operating instructions for complete system including:
a. Normal starting, operating, and shut-down.
b. Emergency procedures for fire or failure of major equipment.
c. Summer and winter special procedures, if any.
d. Day and night special procedures, if any.
2. Maintenance instruction including:
a. Proper lubricants and lubricating instructions for each piece of equipment, and date when lubricated.
b. Necessary cleaning, replacement and/or adjustment schedule.
3. Manufacturer's data for each piece of equipment including:
a. Installation instructions.
b. Drawings and specifications.
c. Parts list, including recommended items to be stocked.
d. Complete wiring diagrams.
e. Marked or changed prints locating all concealed parts and all variations from the original system design.
f. Test and inspection certificates.
D. Refer to individual specification sections for additional O&M requirements.

1.13 RECORD DOCUMENTS
A. During construction, keep an accurate record of all deviations between the work as shown on Drawings and that which is actually installed. Keep this record set of prints at the job site for review by the Architect/Engineer.
B. Upon completion of the installation and acceptance by the owner, transfer all record drawing information to one neat and legible set of prints. Then deliver them to the Architect/Engineer for transmittal to the Owner.
C. Provide in each main electrical switchboard room a framed copy under glass of the appropriate Single Line Riser Diagram as reviewed by the electrical engineer. Media shall be a high quality presentation type paper. Blueprints or other media which fade shall not be used.

1.14 GUARANTEE
A. Guarantee all material and workmanship for a period of one (1) year from date of final acceptance by the Owner, except that where guarantees or warranties for longer terms are specified herein, such longer term to apply. Within 24 hours after notification, correct any deficiencies that occur during the guarantee period at no additional cost to the Owner, all to the satisfaction of the Owner and Architect/Engineer. Obtain similar guarantees from subcontractors, manufacturers, suppliers and subtrade specialists.

PART 2 - PRODUCTS

2.01 MATERIALS
A. Applicable equipment and materials shall be listed by Underwriters' Laboratories and Manufactured in accordance with ASME, NEMA, ANSI or IEEE standards, and as approved by local authorities having jurisdiction as mentioned in Division 1.
B. If products and materials are specified or indicated on the Drawings for a specific item or system, use those products or materials. If products and materials are not listed in either of the above, use first class products and materials, subject to approval of Shop Drawings where Shop Drawings are required or as approved in writing where Shop Drawings are not required.
C. All equipment capacities, etc. are listed for job site operating conditions. All equipment sensitive to altitudes or ambient temperatures to be derated and method of derating shown on Shop Drawings. Where operating conditions shown differ from the laboratory test conditions, the equipment to be derated and the method of derating shown on Shop Drawings.

2.02 SUBSTITUTION OF MATERIALS OR EQUIPMENT
A. All requests for substitution of materials or equipment shall be made in writing by the Contractor. The request must be in the Engineers office not less than 10 days prior to the bid date. Samples of proposed substitute materials or equipment shall be submitted to the Engineer for review whenever they are requested. Bids shall be based only upon the specified materials and equipment, or substitutes that have received written acceptance from the Engineer prior to the bid.
B. Wherever the words "for approval" or "approved" are used in regard to manufactured specialties, or wherever it is desired to substitute a different make or type of apparatus for that specified, submit all information pertinent to the adequacy and adaptability of the proposed apparatus, and secure Architect/Engineer's acceptance before apparatus is ordered.
C. Wherever quantities or a definite make and size of apparatus is specified, the make and size of apparatus which is proposed must conform substantially (in regard to the operating results) to that specified or implied. Same shall apply to important dimensions relating to operation of apparatus in coordination with the rest of the system, or to properly fitting it into available space conditions. Any substitution of equipment or apparatus shall include all necessary revisions, as required to complete the installation.
D. Acceptance of substitutions, for equipment specified herein, will not be given merely upon submission of manufacturer's names and will be given only after receipt of complete and satisfactory performance data covering the complete range of operating conditions in tabular and graphical form. Furnish complete and satisfactory information relative to equipment dimensions, weight, etc. Acceptance of all equipment specified or shown on the Drawings, or substitutions submitted for that specified or shown on the Drawings, will be granted if such equipment, in the opinion of the Architect/Engineer, conforms to the performance requirements, space conditions, weight requirements and quality requirements. Any additional construction and design costs incurred as a result of any accepted substitution shall be borne by the Contractor. The opinion and judgement of the Architect/Engineer shall be final, conclusive, and binding.

2.03 SHOP DRAWINGS
A. Prepare and submit detailed Shop Drawings for materials, systems, and equipment as listed herein, including locations and sizes of all openings in floor decks, walls, and floors.
B. The Work described in any Shop Drawing submission shall be carefully checked for all clearances (including those required for maintenance and servicing), field conditions, maintenance of architectural conditions, and proper coordination with all trades on the job. Each submitted Shop Drawing shall include a certification that all related job conditions have been checked and that no conflict exists.
C. All drawings shall be submitted sufficiently in advance of field requirements to allow ample time for checking and resubmittal as may be required. All submittals shall be complete and contain all required and detailed information.
D. Acceptance of any submitted data or Shop Drawings for material, equipment apparatus, devices, arrangements, and layout shall not relieve Contractor from responsibility of furnishing same of proper dimensions and weight, capacities, sizes, quantity, quality and installation details, to efficiently perform the requirements and intent of the Contract. Such acceptance shall not relieve Contractor from responsibility for errors, omissions, or inadequacies of any sort on submitted data or Shop Drawings.
E. Each Shop Drawing shall contain the following information.
1. Provide general information on each copy of the submittal.
a. Project title.
Reference to the applicable drawing and specification article.
Contractor and supplier identification, addresses and telephone numbers.
Submittal Date.
2. Certification that the contractor has reviewed the submittal.
3. Refer to individual specification sections for additional information requirements.
F. Shop Drawing submittals shall be provided for each specific material, system, or equipment as identified herein.
1. As a minimum, make submittals on the following items.
a. Raceways, conduit & wire
b. Wiring devices and plates
c. Switchboards
d. Transformers
e. Panelboards
f. Fuses
g. Disconnect switches
h. Motor control centers
i. Motor controllers, starters, and contactors
j. Lighting fixtures, lamps
k. Instrumentation, metering equipment
l. Special systems - fire alarm, security, CCTV, intercom, etc.
2. Refer to individual specification sections for additional submittal requirements.

PART 3 - EXECUTION

3.01 INSTALLATION
A. Follow manufacturer's instructions for installing, connecting, and adjusting all equipment. Provide one copy of such instructions to the Architect/Engineer before installing any equipment. Provide a copy of such instructions at the equipment during any work on the equipment. Provide all special supports, connections, wiring, accessories, etc.
B. Use mechanics skilled in their trade for all work.
C. Keep all items protected before and after installation. Clean up all debris.
D. Before commencing Work, examine all adjoining, underlying, etc., Work on which this Work is in any way dependent for perfect workmanship and report any condition which prevents performance of first class work. Become thoroughly familiar with actual existing conditions to which connections must be made or which must be changed or altered.

3.02 PREMIUM TIME WORK
A. The following Work shall be performed at night or weekend other than holiday weekends as directed and coordinated with the Owner.
1. All tie-in, cut-over and modifications to the existing electrical system and other existing system requiring tie-ins or modifications shall be arranged and scheduled with the Owner to be done at a time as to maintain continuity of the service and not interfere with normal building operations.

3.03 EXCAVATION, TRENCHING AND BACKFILL
A. Provide excavation for the Work. Excavate all material encountered, to the depths indicated on the drawings or required. Remove from the site, excavated materials not required or suitable for backfill. Provide grading, as may be necessary, to prevent surface water from flowing into trenches or other excavations. Remove any water accumulating therein. Provide sheeting and shoring as may be necessary for the protection of the Work and for the safety of personnel.
B. Provide trenches of widths necessary for the proper execution of the Work. Grade bottom of the trenches accurately to provide uniform bearing and support the Work on undisturbed soil at every point along its entire length. Except where rock is encountered, do not excavate below the depths indicated. Where rock excavations are required, excavate rock to a minimum overdepth of four (4") inches below the trench depths indicated on the Drawings or required. Backfill overdepths in the rock excavation and unauthorized overdepths with loose granular, moist earth, thoroughly machine tamped, to a compaction level of at least 95 percent to standard protector density or 75 percent relative density or as specified by the Architect. Where unstable soil that is incapable of properly supporting the Work, as determined by Architect/Engineer, is encountered in the bottom of the trench, remove soil to a depth required and backfill the trench to the proper grade with coarse sand, fine gravel, or other suitable material.
C. Excavate trenches for utilities to a depth that will provide the following minimum depths of cover from existing grade or from indicated finished grade, whichever is lower, unless otherwise specifically shown.
1. Primary electric service: four (4) feet (minimum)
2. Secondary electric service: two (2) feet (minimum)
3. Telephone service: two (2) feet (minimum)
D. Trenches shall not be placed within ten (10) feet of foundation or soil surfaces which must resist horizontal forces.
E. Do not backfill trenches until all required tests have been preformed and the installation observed by the Engineer. Comply with the requirements of other sections of these specifications. Backfill shall consist of non-expansive soil with limited porosity. Deposit in six (6") inch layers and thoroughly and carefully tamp until the Work has a cover of not less than one (1) foot. Backfill and tamp remainder of trench at twelve (12") inch intervals until complete. Uniformly grade the finished surface. Backfill and tamp with compaction at least equal to the surrounding area.

3.04 CUTTING, PATCHING AND REPAIRING
A. The work shall be carefully laid out in advance. Where cutting, channeling, chasing or drilling of floors, walls, partitions, ceilings or other surfaces is necessary for the proper installation, support or anchorage of raceway, outlets or other equipment, the work shall be carefully done. Any damage to the building, piping, equipment or defaced finish plaster, woodwork, metalwork, etc. shall be repaired by skilled mechanics of the trades involved at no additional cost to the Owner.
B. Where conduits, mounting channels, outlet, junction, or pull boxes are mounted on a painted surface, or a surface to be painted, they shall be painted to match the surface. Whenever support channels are cut, the bare metal shall be cold galvanized.

3.05 DEMOLITION AND CONTINUANCE OF EXISTING SERVICES
A. All existing electrical services not specifically indicated to be removed or altered shall remain as they presently exist.
B. Should any existing services interfere with new construction, the Contractor shall (after obtaining written approval from the Architect/Engineer) alter or reroute such existing equipment to facilitate new construction.
C. Under no circumstances shall existing services be terminated or altered unless deemed necessary by the Architect/Engineer or specified herein; also, prior to altering any existing situation, the Contractor shall notify the Owner in writing giving two (2) weeks advance notice of planned alteration.
D. It shall be solely the Contractor's responsibility to guarantee continuity of present facilities (with respect to damage or alteration due to new construction) and any unauthorized alteration to existing equipment shall be corrected by the Contractor to the Architect/Engineer's satisfaction at the Contractor's expense.

3.06 CLEANING UP
A. A Contractor shall take care to avoid accumulation of debris, boxes, crates, etc., resulting from the installation of his work. Contractor shall remove from the premises each day all debris, boxes, etc., and keep the premises clean.
B. Contractor shall clean up all fixtures and equipment at the completion of the project.
C. All switchboards, panelboards, wireways, trench ducts, cabinets and enclosures shall be thoroughly vacuumed clean prior to energizing equipment and at the completion of the project. Equipment shall be opened for observation by the Architect/Engineer as required.

3.07 WATERPROOFING
A. Avoid, if possible, the penetration of any waterproof membranes such as roofs, machine room floors, basement walls, and the like. If such penetration is necessary, perform it prior to the waterproofing and furnish all sleeves or pitch-pockets required. Advise the Architect/Engineer and obtain written permission before penetrating any waterproof membrane, even where such penetration is shown on the Drawings.
B. If Contractor penetrates any walls or surfaces after they have been waterproofed, he shall restore the waterproof integrity of that surface as directed by the Architect/Engineer at his own expense.

3.08 SUPPORTS
A. Support work in accordance with the best industry practice and the following.
B. Include supporting frames or racks extending from building structure for work indicated as being supported from walls where the walls are incapable of supporting the weight. In particular, provide such frames or racks in electric closets.
C. Include supporting frames or racks for equipment, intended for vertical surface mounting, which is required in a free standing position.
D. Supporting frames or racks shall be of standard angle, standard channel or specialty support system steel members. They shall be rigidly bolted or welded together and adequately braced to form a substantial structure. Racks shall be of ample size to assure a workmanlike arrangement of all equipment mounted on them.
E. Nothing, (including outlet, pull and junction boxes and fittings) shall depend on electric conduits, raceways, or cables for support, except that threaded hub type fittings having a gross volume not in excess of 100 cubic inches may be supported from heavy wall conduit, where the conduit is securely supported from the structure within five inches of the fitting on two opposite sides.
F. Nothing shall rest on, or depend for support on, suspended ceilings media (tiles, lath, plaster, as well as splines, runners, bars and the like in the plane of the ceiling).
G. Provide required supports and hangers for conduit, equipment, etc., so that loading will not exceed allowable loadings of structure.

3.09 FASTENINGS
A. Fasten electric work to building structure in accordance with the best industry practice and the following.
B. Floor or pad mounted equipment shall not be held in place solely by its own dead weight. Include anchor fastening in all cases.
C. For items which are shown as being ceiling mounted at locations where fastening to the building construction element above is not possible, provide suitable auxiliary channel or angle iron bridging, tying to the building structural elements.

3.10 TESTING EQUIPMENT AND MATERIALS
A. The Contractor shall provide all testing instruments, equipment and all materials, connections, labor, etc., required to perform tests.
B. Test all circuits, fixtures, equipment, and systems for proper operation and freedom from grounds, shorts and open circuits before acceptance is requested.
C. Measure voltage at panelboards and outlets after the building is fully occupied. Make final transformer tap adjustments based on these measurements.
D. Perform all tests required by local authorities, such as tests of life safety systems, in addition to tests specified herein.
E. Perform tests required by other specification sections.

PRAXIS3
100 Peachtree St NW
Suite 1450
Atlanta, GA 30303
404-875-4500 tel
www.praxis3.com

GEORGIA REGISTERED No. 041508 PROFESSIONAL ENGINEER RAHN ONEAL WILLIAMS

Copyright (c) 2024 Praxis3, LLC

All reports, plans, specifications, computer files, field data, notes and other documents and instruments prepared by Praxis3 shall retain all common law, statutory and other reserved rights, including copyright thereto.

This drawing may not be reproduced in whole or in part without written permission of Praxis3. It is to be returned upon request. Scales as stated are valid on the original drawings.

Rev	Date	Comments
	07/02/2026	PERMIT SET

Client:
FIFTH THIRD BANK

Project Number: 26032
Project Name:
FIFTH THIRD BANK WATSON
1,900 SF

2711 WATSON BOULEVARD
WARNER ROBBINS, GA 31093

Key Plan:

Sheet Title:
ELECTRICAL SPECIFICATIONS

Sheet Number:
E-003

6/30/2026 2:31:56 PM

COMcheck Software Version 4.1.5.5

Interior Lighting Compliance Certificate

Project Information

Energy Code: 2015 IECC
Project Title: FIFTH THIRD BANK WATSON
Project Type: New Construction

Construction Site:
2711 WATSON BOULEVARD
WARNER ROBBINS, GA 31093

Owner/Agent:

Designer/Contractor:

Additional Efficiency Package(s)

Credits: 1.0 Required 1.0 Proposed
Reduced Lighting Power, 1.0 credit

Allowed Interior Lighting Power

A Area Category	B Floor Area (ft2)	C Allowed Watts / ft2	D Allowed Watts (B X C)
1-Retail	2798	1.13	3173
		Total Allowed Watts =	3173

Proposed Interior Lighting Power

A Fixture ID : Description / Lamp / Wattage Per Lamp / Ballast	B Lamps/ Fixture	C # of Fixtures	D Fixture Watt.	E (C X D)
1-Retail				
LED 1: A/AE: Other:	1	29	15	435
LED 1 copy 1: B: Other:	1	40	3	120
LED 1 copy 1: C: Other:	1	9	52	468
LED 1 copy 2: F3: Other:	1	27	1	27
LED 1 copy 3: FEM: Other:	1	30	2	60
LED 1 copy 4: G: Other:	1	50	2	100
LED 1 copy 5: J/JE: Other:	1	19	8	152
LED 1 copy 6: PB: Other:	1	17	1	17
LED 1 copy 7: S: Other:	1	27	2	54
LED 1 copy 8: T: Other:	1	16	19	304
		Total Proposed Watts =		1737

Interior Lighting PASSES: Design 45% better than code

Interior Lighting Compliance Statement

Compliance Statement: The proposed interior lighting design represented in this document is consistent with the building plans, specifications, and other calculations submitted with this permit application. The proposed interior lighting systems have been designed to meet the 2015 IECC requirements in COMcheck Version 4.1.5.5 and to comply with any applicable mandatory requirements listed in the Inspection Checklist.

Travis Apperson — Digitally signed by Travis Apperson; DN: C=US, E=tapperson@praxis3designgroup.com, CN=Travis Apperson; Date: 2026.06.30 14:15:33-04'00' — 07/02/2026

Name - Title | Signature | Date

COMcheck Software Version 4.1.5.5

Exterior Lighting Compliance Certificate

Project Information

Energy Code: 2015 IECC
Project Title: FIFTH THIRD BANK WATSON
Project Type: New Construction
Exterior Lighting Zone 4 (High activity metropolitan commercial district (LZ4))

Construction Site:
2711 WATSON BOULEVARD
WARNER ROBBINS, GA 31093

Owner/Agent:

Designer/Contractor:

Allowed Exterior Lighting Power

A Area/Surface Category	B Quantity	C Allowed Watts / Unit	D Tradable Wattage	E Allowed Watts (B X C)
Parking area	6873 ft2	0.13	Yes	893
Entry canopy	43 ft2	0.4	Yes	17
Entry canopy	237 ft2	0.4	Yes	95
Entry canopy	379 ft2	0.4	Yes	152
			Total Tradable Watts (a) =	1157
			Total Allowed Watts =	1157
			Total Allowed Supplemental Watts (b) =	1300

(a) Wattage tradeoffs are only allowed between tradable areas/surfaces.
(b) A supplemental allowance equal to 1300 watts may be applied toward compliance of both non-tradable and tradable areas/surfaces.

Proposed Exterior Lighting Power

A Fixture ID : Description / Lamp / Wattage Per Lamp / Ballast	B Lamps/ Fixture	C # of Fixtures	D Fixture Watt.	E (C X D)
Parking area (6873 ft2): Tradable Wattage				
LED 1: 1P4F: Other:	1	140	1	140
LED 1 copy 1: SP4DA: Other:	1	140	4	560
Entry canopy (43 ft2): Tradable Wattage				
LED 1 copy 2: G1/GEM: Other:	1	21	4	84
Entry canopy (237 ft2): Tradable Wattage				
LED 1 copy 6: G1/GEM: Other:	1	21	10	210
Entry canopy (379 ft2): Tradable Wattage				
LED 1 copy 7: G1/GEM: Other:	1	21	8	168
LED 1 copy 5: L: Other:	1	180	2	360
LED 1 copy 4: U1: Other:	1	9	2	18
LED 1 copy 3: U3: Other:	1	26	4	104
			Total Tradable Proposed Watts =	1644

Exterior Lighting PASSES: Design 33% better than code

Exterior Lighting Compliance Statement

Compliance Statement: The proposed exterior lighting design represented in this document is consistent with the building plans, specifications, and other calculations submitted with this permit application. The proposed exterior lighting systems have been designed to meet the 2015 IECC requirements in COMcheck Version 4.1.5.5 and to comply with any applicable mandatory requirements listed in the Inspection Checklist.

Travis Apperson — Digitally signed by Travis Apperson; DN: C=US, E=tapperson@praxis3designgroup.com, CN=Travis Apperson; Date: 2026.06.30 14:15:33-04'00' — 07/02/2026

Name - Title | Signature | Date

PRAXIS3
100 Peachtree St NW
Suite 1450
Atlanta, GA 30303
404-875-4500 tel
www.praxis3.com

GEORGIA REGISTERED No. 041460 PROFESSIONAL ENGINEER RAHN ONEAL WILLIAMS

Copyright (c) 2024 Praxis3, LLC

All reports, plans, specifications, computer files, field data, notes and other documents and instruments prepared by Praxis3 shall retain all common law, statutory and other reserved rights, including copyright thereto.

This drawing may not be reproduced in whole or in part without written permission of Praxis3. It is to be returned upon request. Scales as stated are valid on the original drawings.

Rev	Date	Comments
	07/02/2026	PERMIT SET

Client:
FIFTH THIRD BANK

Project Number: 26032
Project Name:
FIFTH THIRD BANK WATSON 1,900 SF


2711 WATSON BOULEVARD
WARNER ROBBINS, GA 31093

Key Plan:


Sheet Title:
COMCHECK

Sheet Number:
E-004

6/30/2026 2:31:58 PM

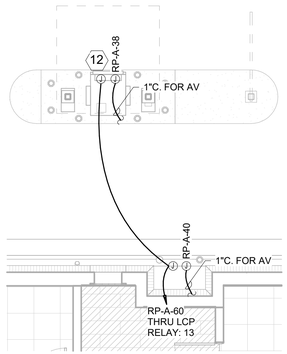

2 E-010 ELECTRICAL POWER & AUXILIARY RDT PLAN
3/16" = 1'-0"

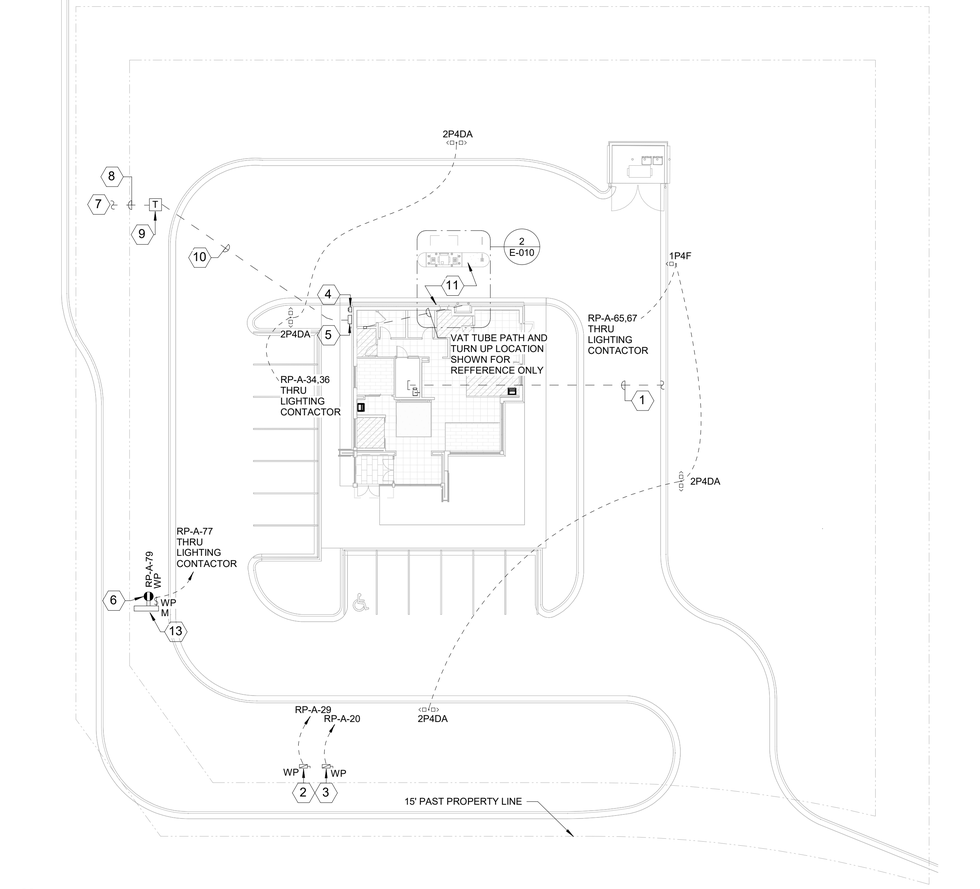

1 E-010 ELECTRICAL SITE PLAN
1" = 20'-0"

SHEET NOTES:

1. COORDINATE ALL SITE CONDUIT ROUTINGS WITH GENERAL CONTRACTOR.
2. REFER TO CIVIL PLANS FOR FINAL LOCATION AND ELECTRICAL REQUIREMENTS OF ALL SIGNAGE, UTILITY CONNECTION POINTS, AND SITE UTILITIES/EQUIPMENT SUCH AS LIFT STATIONS, IRRIGATION PUMPS/CONTROLLERS, HOT BOXES, ETC.
3. ALL UNDERGROUND WIRING SHALL BE LOCATED WITHIN 12" OF BACK OF CURB IN ALL LOCATIONS.
4. BACKFILL, TAMP, AND RESURFACE ALL EXISTING PAVEMENT/ASPHALT AND RESTORE ALL EXISTING LANDSCAPING DISTURBED AS A RESULT OF TRENCHING AND/OR DIRECTIONAL BORING TO ITS ORIGINAL CONDITION.
5. ALL UTILITY SERVICE SHALL BE VERIFIED WITH THE UTILITY COMPANIES PRIOR TO BIDDING AND ALL RESULTING COSTS SHALL BE INCLUDED IN BID
6. ACTUAL INSTALLATION OF ALL UTILITY SERVICES SHALL BE ACCORDING TO FINAL UTILITY COMPANY PLANS.
7. PROVIDE PULLWIRE IN ALL EMPTY CONDUITS.
8. USE JOINT TRENCHING WHEREVER POSSIBLE

KEYED NOTES:

1. ROUTE (2)4"C TO MAIN TELEPHONE SERVICE ENTRANCE. ROUTE TO CLEAR STRUCTURAL FOOTING. CONDUITS SHALL BE STUBBED UP AND CAPPED 12" A.F.F. IN BUILDING. ASBUILT DRAWINGS MUST SHOW CONDUIT LENGTH AND ROUTE
2. IRRIGATION BACKFLOW. VERIFY LOCATION DISCONNECT SHALL BE NEMA 3R.
3. DDCV HOTBOX. VERIFY LOCATION DISCONNECT SHALL BE NEMA 3R.
4. ELECTRIC UTILITY METER. PROVIDE ELECTRIC UTILITY METER PER POWER COMPANY REQUIREMENTS. REFER TO ELECTRICAL RISER DIAGRAM FOR ADDITIONAL INFORMATION. EXACT LOCATION TO BE DETERMINED BY UTILITY COMPANY REPRESENTATIVE IN FIELD.
5. SERVICE DISCONNECT. PROPOSED ELECTRICAL SERVICE DISCONNECT MOUNTED ON BUILDING EXTERIOR. REFER TO ELECTRICAL RISER DIAGRAM FOR ADDITIONAL INFORMATION.
6. MAINTENANCE RECEPTACLE: PROVIDE 120V, 20A, GFCI WEATHER-RESISTANT DUPLEX RECEPTACLE IN WEATHERPROOF SURFACE MOUNTED BELL BOX WITH "EXTRA DUTY WHILE-IN-USE" METALLIC COVER.
7. STUBOUT AND TERMINATE PER UTILITY COMPANY REQUIREMENTS. VERIFY LOCATION OF HIGH VOLTAGE SERVICE POINT PRIOR TO BIDDING AND INCLUDE ALL COST IN BID.
8. (2)5"C FOR HIGH VOLTAGE SERVICE FROM PROPERTY LINE TO TRANSFORMER SLABS VERIFY LOCATION AND ROUTING. HIGH VOLTAGE CONDUIT SHALL BE 48" DEEP. TERMINATE IN ACCORDANCE WITH UTILITY COMPANY REQUIREMENTS INCLUDING TRENCHING AND BACKFILL TO 90% COMPACTION.
9. TRANSFORMER SLABBOX WITH TRAFFIC GUARDS PER UTILITY COMPANY REQUIREMENTS. VERIFY SIZE, LOCATION AND ORIENTATION WITH UTILITY COMPANY. CONTRACTOR WILL PROVIDE TRANSFORMER SLABS INSTALLED COMPLETE IN ACCORDANCE WITH UTILITY COMPANY REQUIREMENTS. PROVIDE ADEQUATE GUARD RAILING AROUND POWER TRANSFORMERS IN PARKING AREAS.
10. SECONDARY FROM TRANSFORMER TO MAIN DISCONNECT. VERIFY ROUTING WITH UTILITY COMPANY AND ROUTE TO CLEAR STRUCTURAL FOOTING. SEE RISER DIAGRAM. TERMINATE IN ACCORDANCE WITH PLANS AND SPECIFICATIONS.
11. CANOPY LIGHT FIXTURE: FACTORY INSTALLED CANOPY LIGHT PROVIDED BY KIOSK MANUFACTURER. EC TO COORDINATE WITH THE MANUFACTURER AND MAKE FINAL CONNECTION.
12. DRIVE-THRU ATM: PROVIDE CONDUIT AND WIRING FOR ATM. REFER TO ELECTRICAL FLOOR PLAN ON SHEET E-500 FOR ADDITIONAL INFORMATION.
13. MONUMENT SIGN POWER: COORDINATE EXACT LOCATION OF SIGNAGE STUB-UP WITH SIGN VENDOR AND MAKE FINAL ELECTRICAL CONNECTIONS. PROVIDE 120V, 20A, TOGGLE SWITCH IN METALLIC BELL BOX WITH METALLIC WEATHERPROOF COVER IF DISCONNECT IS NOT FURNISHED WITH MONUMENT SIGN. COORDINATE EXACT LOCATION WITH CIVIL DRAWINGS.

PRAXIS3
100 Peachtree St NW
Suite 1450
Atlanta, GA 30303
404-875-4500 tel
www.praxis3.com

GEORGIA REGISTERED No. 041604 PROFESSIONAL ENGINEER RAHN ONEAL WILLIAMS

Copyright (c) 2024 Praxis3, LLC

All reports, plans, specifications, computer files, field data, notes and other documents and instruments prepared by Praxis3 shall retain all common law, statutory and other reserved rights, including copyright thereto.

This drawing may not be reproduced in whole or in part without written permission of Praxis3. It is to be returned upon request. Scales as stated are valid on the original drawings.

Rev	Date	Comments
	07/02/2026	PERMIT SET

Client:
FIFTH THIRD BANK

Project Number: 26032
Project Name:
FIFTH THIRD BANK WATSON 1,900 SF


2711 WATSON BOULEVARD
WARNER ROBBINS, GA 31093

Key Plan:


Sheet Title:
ELECTRICAL SITE PLAN AND REMOTE DRIVE THRU

Sheet Number:
E-010

6/30/2026 2:31:58 PM

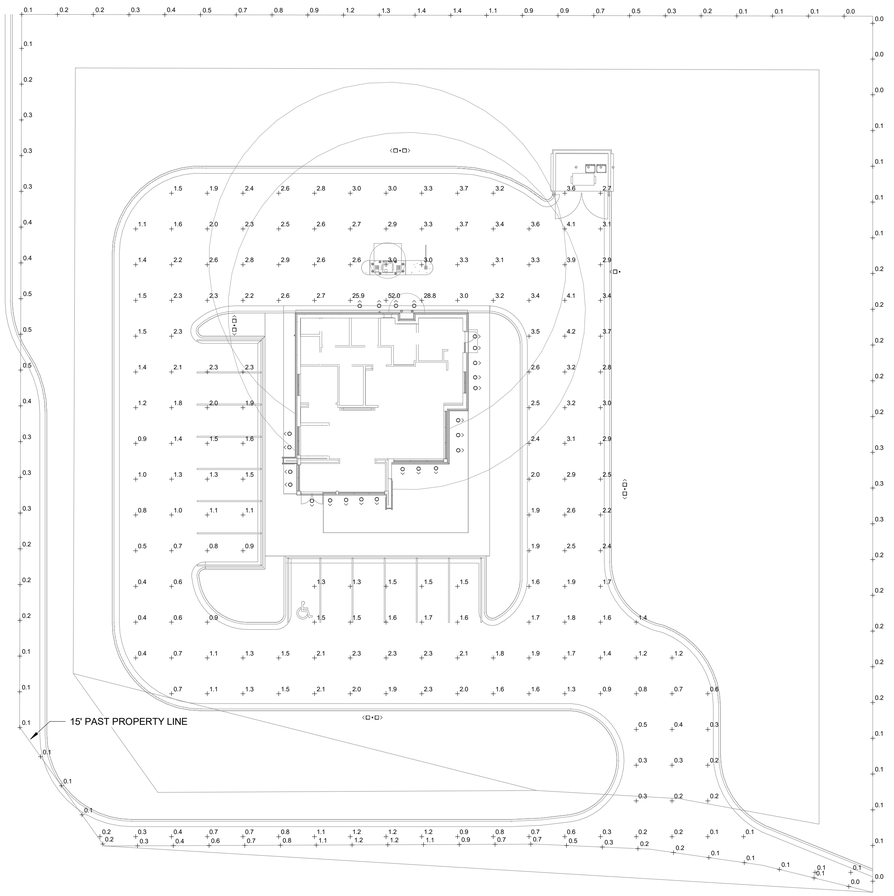

1 E-011 ELECTRICAL PHOTOMETRIC SITE PLAN AT GRADE
1" = 20'-0"

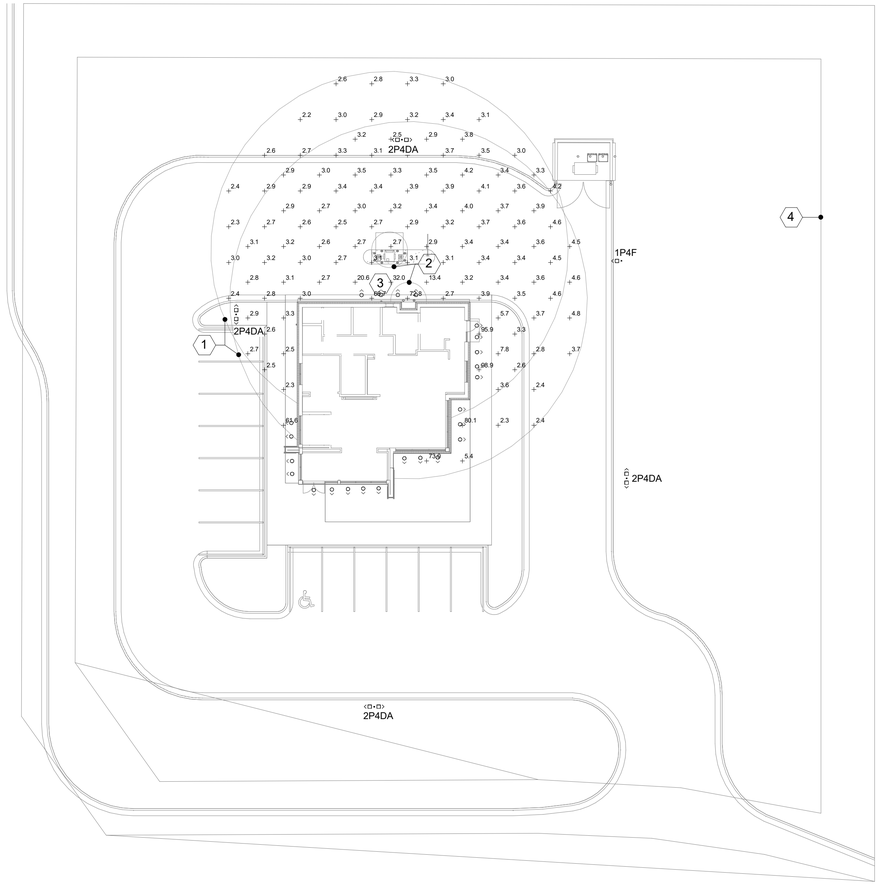

2 E-011 ELECTRICAL PHOTOMETRIC SITE PLAN AT 3'-0"
1" = 20'-0"

LIGHTING STANDARD:

MINIMUM STANDARD

REGULATED STATES: ALABAMA, CALIFORNIA, CONNECTICUT, DISTRICT OF COLUMBIA, FLORIDA, GEORGIA, ILLINOIS, KANSAS, KENTUCKY, LOUISIANA, MARYLAND, MASSACHUSETTS, MISSOURI, MONTANA, NEVADA, NEW HAMPSHIRE, NEW JERSEY, NEW YORK, OREGON, RHODE ISLAND, TEXAS, VIRGINIA, WASHINGTON, VIRGINIA**.

A. BANKING CENTERS IN VIRGINIA MUST COMPLY WITH ALL HOME STATE LAWS AND IS CONSIDERED REGULATED IF THE BANK HEADQUARTERS ARE LOCATED IN A REGULATED STATE.

- A MINIMUM OF TEN (10) FOOT CANDLE POWER AT THE FACE OF THE ATM OR AFTERHOUR DEPOSITORY EXTENDING OUTWARD FIVE (5) FEET IN ALL UNOBSTRUCTED DIRECTIONS.
- A MINIMUM OF TWO (2) FOOT CANDLE POWER EXTENDING OUTWARDS IN ALL UNOBSTRUCTED DIRECTIONS FIFTY (50) FEET FROM THE FACE OF THE ATM AND AFTERHOUR DEPOSITORY.
- A MINIMUM OF TWO (2) FOOT CANDLE POWER IN DEFINED PARKING AREAS WITHIN SIXTY (60) FEET OF THE ATM AND AFTERHOUR DEPOSITORY. IN THE EVENT THE ATM OR AFTERHOUR DEPOSITORY IS LOCATED WITHIN TEN (10) FEET OF THE CORNER OF THE BUILDING AND IS GENERALLY ACCESSIBLE FROM THE ADJACENT SIDE, THERE SHALL BE A MINIMUM OF TWO (2) FOOT CANDLE POWER ALONG THE FIRST FORTY (40) UNOBSTRUCTED FEET OF THE ADJACENT SIDE OF THE BUILDING.
- IF THE ATM OR AFTERHOUR DEPOSITORY IS LOCATED INSIDE A ACCESSIBLE VESTIBULE DURING ANY HOURS OF DARKNESS, A MINIMUM OF 10 FOOT CANDLE POWER AT THE FACE OF THE ATM OR AFTERHOUR DEPOSITORY EXTENDING OUTWARD FIVE (5) FEET IN ALL UNOBSTRUCTED DIRECTIONS. THERE WILL BE A MINIMUM OF TWO (2) FOOT CANDLE POWER AT THE INSIDE OF THE VESTIBULE ENTRY/EXIT DOOR(S). A MINIMUM OF TWO (2) FOOT CANDLE POWER EXTENDING OUTWARDS IN ALL UNOBSTRUCTED DIRECTIONS FIFTY (50) FEET FROM THE VESTIBULE ENTRY/EXIT DOOR. A MINIMUM OF TWO (2) FOOT CANDLE POWER IN DEFINED PARKING AREAS WITHIN SIXTY (60) FEET OF THE VESTIBULE ENTRY/EXIT DOOR. IN THE EVENT THE VESTIBULE ENTRY/EXIT DOOR IS LOCATED WITHIN TEN (10) FEET OF THE CORNER OF THE BUILDING AND IS GENERALLY ACCESSIBLE FROM THE ADJACENT SIDE, THERE SHALL BE A MINIMUM OF TWO (2) FOOT CANDLE POWER ALONG THE FIRST FORTY (40) UNOBSTRUCTED FEET OF THE ADJACENT SIDE OF THE BUILDING. IN URBAN SETTINGS FOR WHICH THERE IS NO DEFINED BANK PARKING AND THE ONLY ACCESS AREA IS A PUBLIC SIDEWALK, A MINIMUM 2 FOOT CANDLE POWER SHALL BE FOR THE FIRST 5 UNOBSTRUCTED FEET FROM THE DOOR. THE MINIMUM FOOT CANDLE READING WILL ALSO BE LIMITED TO BANK CONTROLLED PROPERTY LINES.
- A MINIMUM OF TWO (2) FOOT CANDLE POWER IN THE IMMEDIATE AREA OF THE DESIGNATED ASSOCIATE ENTRANCE/EXIT TO THE FACILITY.
- ALL LIGHTING MEASUREMENTS ARE TO BE TAKEN AT 36 INCHES ABOVE THE GROUND ON A HORIZONTAL PLANE, UNLESS OTHERWISE SPECIFIED BY STATE LAW OR REGULATION (3/07).
- CORPORATE WORKPLACE HAS OVERALL RESPONSIBILITY OF ENSURING THAT BANK PROPERTIES REMAINS IN COMPLIANCE.
- THE MINIMUM STANDARD SHALL APPLY UNLESS A GREATER STANDARD IS REQUIRED BY AN APPLICABLE LAW FOR A PARTICULAR FACILITY LOCATION.

CALCULATION SUMMARY AT 36" AFG

LABEL	CALCTYPE	UNIT	AVG	MAX	MIN	AVG/MIN	MAX/MIN
DRIVEUP VAT 5FT COMPLIANCE	LUMINANCE	FC	PROVIDE BY OTHERS				
DRIVEUP VAT 50FT COMPLIANCE	LUMINANCE	FC	7.8	52.0	2.3	34.8:1	34.8:1
DRIVEUP ATM 5FT COMPLIANCE	LUMINANCE	FC	PROVIDE BY OTHERS				
DRIVEUP ATM 50FT COMPLIANCE	LUMINANCE	FC	8.3	98.9	2.2	3.8:1	45.0:1

SHEET NOTES:

1. PHOTOMETRY CALCULATION:PHOTOMETRIC VALUES SHOWN HEREIN ARE INTENDED FOR DESIGN AND EVALUATION PURPOSES ONLY.THE CALCULATED POINT BY POINT VALUES SHOWN ON THIS SHEET ARE BASED ON A COMPUTER LIGHTING PROGRAM WITH APPROXIMATED PARAMETERS. AS A RESULT, PHOTOMETRIC VALUES MAY VARY FROM ACTUAL FIELD MEASUREMENTS.

KEYED NOTES:

1 ATM/VTM FIVE FOOT COMPLIANCE AREA: A MINIMUM OF TEN (10) FOOT CANDLE POWER AT THE FACE OF THE ATM/AFTERHOUR DEPOSITORY EXTENDING OUTWARD FIVE (5) FEET IN ALL UNOBSTRUCTED DIRECTIONS TO BE PROVIDED BY OWNER'S PREMANUFACTURED ATM CANOPY.

2 ATM/VTM FIFTY FOOT COMPLIANCE AREA: A MINIMUM OF TWO (2) FOOT CANDLE POWER EXTENDING OUTWARD IN ALL UNOBSTRUCTED DIRECTIONS FIFTY (50) FEET FROM THE FACE OF THE ATM AND AFTERHOUR DEPOSITORY.

3 AFTERHOUR DEPOSITORY SIXTY FOOT COMPLIANCE AREA: A MINIMUM OF TWO (2) FOOT CANDLE POWER EXTENDING OUTWARD IN ALL UNOBSTRUCTED DIRECTIONS SIXTY (60) FEET FROM THE FACE OF THE ATM AND AFTERHOURDEPOSITORY.

4 BANK CONTROLLED PROPERTY LINES: THE MINIMUM FOOT CANDLE READING WILL BE LIMITED TO BANK CONTROLLED PROPERTY LINES.

LIGHTING FIXTURE SCHEDULE (EXTERIOR)

LABEL	DESCRIPTION	LIGHT FIXTURE		MOUNTING	QTY. OF LAMPS	VOLTS	WATTS
		MFG.	MODEL NUMBER				
1P4F	LED FULL CUTOFF AREA LUMINAIRE, 15000 LU MENS.FORWARD DISTRIBUTION, ALUMINUM HOUSING, UL LISTED FOR WET LOCATION. 1HEAD	GE/LSI (POLE)	FIXTURE: EALS 04 2 F4 AF 7 40 X D D 1 DKBZ POLE: 4SQB5 S07G ** S BRZ 4BC 27'-6"	POLE MOUNT, **SEE DETAIL FOR POLE HEIGHT	LED	120-277	116
2P4DA	LED FULL CUTOFF AREA LUMINAIRE, 10000 LU MENS.FORWARD DISTRIBUTION, ALUMINUM HOUSING, UL LISTED FOR WET LOCATION. 2HEAD, 180° CONFIGURATION	GE/LSI (POLE)	FIXTURE: EALS 04 2 D4 AF 7 40 X D D1 DKBZ POLE: 4SQB5 S07G ** D180 BRZ 4BC 27'-6"	POLE MOUNT, **SEE DETAIL FOR POLE HEIGHT	LED	120-277	140

PRAXIS3
100 Peachtree St NW
Suite 1450
Atlanta, GA 30303
404-875-4500 tel
www.praxis3.com

GEORGIA REGISTERED No. 041508 PROFESSIONAL ENGINEER RAHN ONEAL WILLIAMS

Copyright (c) 2024 Praxis3, LLC

All reports, plans, specifications, computer files, field data, notes and other documents and instruments prepared by Praxis3 shall retain all common law, statutory and other reserved rights, including copyright thereto.

This drawing may not be reproduced in whole or in part without written permission of Praxis3. It is to be returned upon request. Scales as stated are valid on the original drawings.

Rev	Date	Comments
	07/02/2026	PERMIT SET

Client:
FIFTH THIRD BANK

Project Number: 26032
Project Name:
FIFTH THIRD BANK WATSON 1,900 SF


2711 WATSON BOULEVARD
WARNER ROBBINS, GA 31093

Key Plan:

Sheet Title:
ELECTRICAL PHOTOMETRIC SITE PLAN


Sheet Number:
E-011

6/30/2026 2:31:58 PM

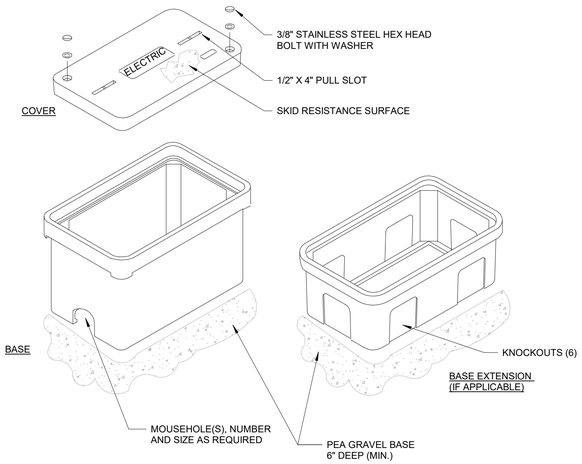


NOTES:

1. PROVIDE STANDARD POLYMER CONCRETE HAND HOLE SIZED PER NEC. COVER COLOR SHALL MATCH EXISTING.
2. PROVIDE 1" X 3/8" BELL PULL SLOT FOR EACH HAND HOLE.
3. COVER, RING, BASE, AND BASE EXTENSION SHALL BE MADE OF SAME MATERIAL.
4. PROVIDE IMPRINTED 'ELECTRIC' ON COVER.
5. HAND HOLE SHALL BE INSTALLED IN LANDSCAPE AREAS NOT SUBJECT TO VEHICULAR TRAFFIC.
6. HAND HOLE SHALL BE MIN. TIER 8 RATED.
7. ALL TERMINATIONS SHALL BE MADE USING UNITAP TAP CONNECTORS OR COMPRESSION SPLICE KITS LISTED FOR WET LOCATIONS. TWIST ON WIRE CONNECTORS ARE NOT ACCEPTABLE.
8. ALL DISTURBED SOIL SHALL BE WELL COMPACTED.
9. EACH END OF PULL STRING SHALL BE LABELED TO INDICATE ORIGIN/DESTINATION OF CONDUIT.

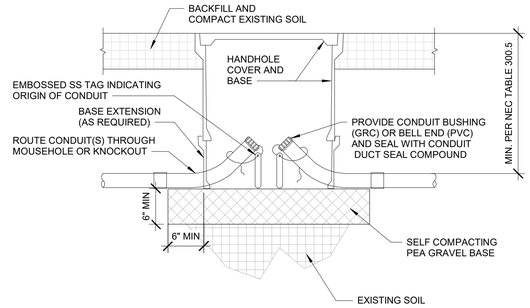


SECTION VIEW OF HAND HOLE

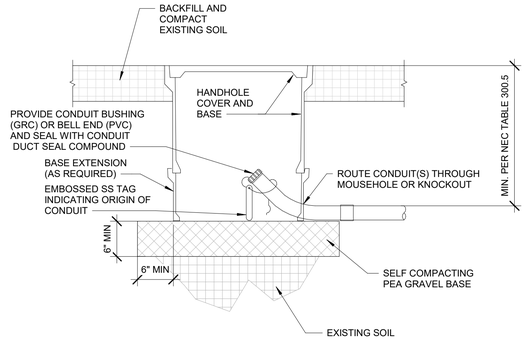


SECTION VIEW OF HAND HOLE (CAPPED SPARE CONDUIT)

1 E-012 HAND HOLE INSTALLED IN LANDSCAPE AREA DETAIL
N.T.S.

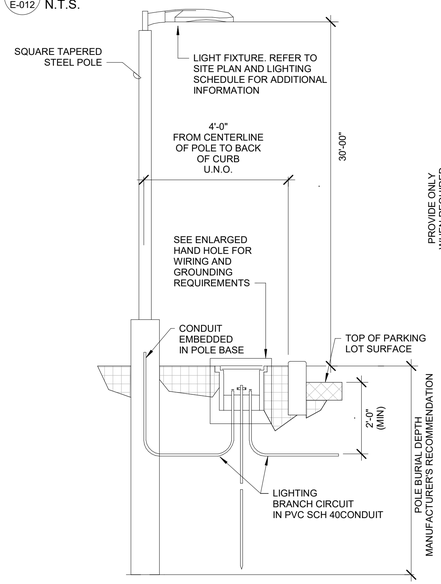


2 E-012 SITE POLE LIGHT DETAIL DIRECT BURIAL - CONCRETE
N.T.S.

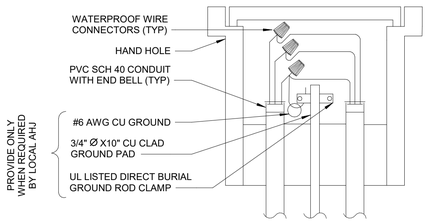

ENLARGED HAND HOLE

HAND HOLE:
1. REFER TO ENLARGED HAND HOLE DETAIL ON THIS SHEET FOR HAND HOLE SPECIFICATION AND INSTALLATION REQUIREMENTS
2. ALL TERMINATIONS WITHIN HAND HOLE SHALL BE MADE USING UNITAP TAP CONNECTORS OR COMPRESSION SPLICE KITS LISTED FOR WET LOCATIONS.TWIST ON WIRE CONNECTORS ARE NOT ACCEPTABLE.

POLE BASE:
1. REFER TO POLE BASE DETAIL 3/E-012 FOR MORE INFORMATION.

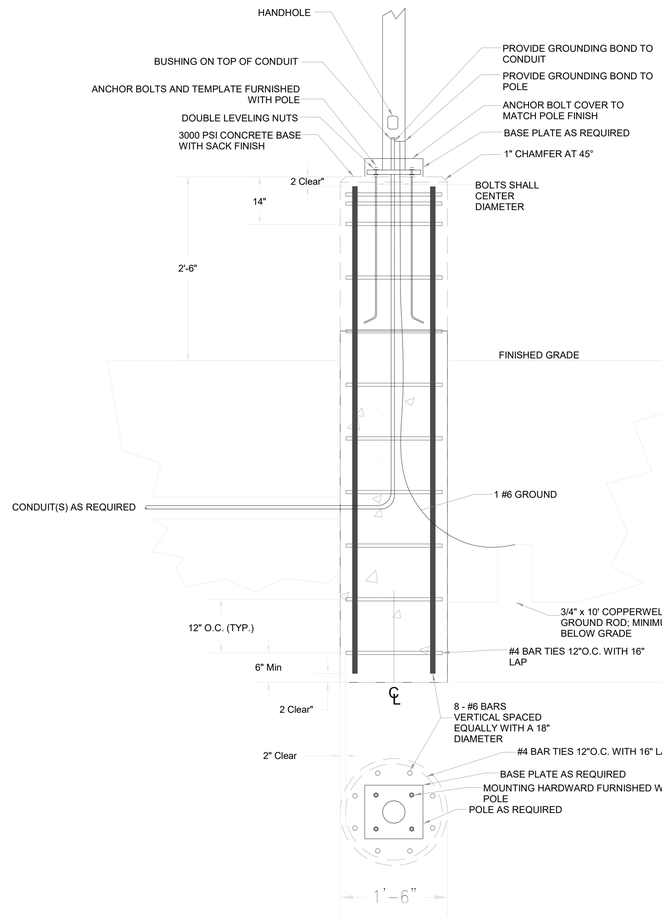

3 E-012 POLE BASE DETAIL
12" = 1'-0"

PRAXIS3
100 Peachtree St NW
Suite 1450
Atlanta, GA 30303
404-875-4500 tel
www.praxis3.com

GEORGIA REGISTERED No. 041508 PROFESSIONAL ENGINEER RAHN ONEAL WILLIAMS

Copyright (c) 2024 Praxis3, LLC

All reports, plans, specifications, computer files, field data, notes and other documents and instruments prepared by Praxis3 shall retain all common law, statutory and other reserved rights, including copyright thereto.

This drawing may not be reproduced in whole or in part without written permission of Praxis3. It is to be returned upon request. Scales as stated are valid on the original drawings.

Rev	Date	Comments
	07/02/2026	PERMIT SET

Client:
FIFTH THIRD BANK

Project Number: 26032
Project Name:
FIFTH THIRD BANK WATSON 1,900 SF


2711 WATSON BOULEVARD
WARNER ROBBINS, GA 31093

Key Plan:

Sheet Title:
ELECTRICAL SITE DETAILS

Sheet Number:
E-012

6/30/2026 2:31:59 PM

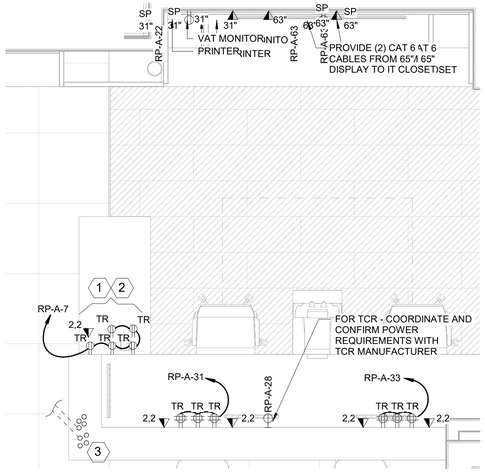


NOTE:

COORDINATE LOCATION OF ALL ELECTRICAL DEVICES WITH ARCHITECTURAL MILLWORK.

2 E-100 ELECTRICAL - POWER ENLARGED PLAN - TRANSACTION BAR1
1/2" = 1'-0"

TRANSACTION BAR KEYED NOTES:

1. ALL RECEPTACLES AND DATA AT TRANSACTION BAR, BELOW COUNTERHEIGHT, SHALL HAVE BLACK COVER PLATES AND OUTLETS U.O.N. COORDINATE DEVICE LOCATIONS WITH MILLWORK PROVIDER AND ARCHITECT. BOX ROUGH OPENINGS SHALL BE CUT BY THE MILLWORK PROVIDER.
2. E.C. TO COORDINATE WITH MILLWORK PROVIDER FOR EXACT LOCATIONS. PROVIDE OUTLETS WITHIN MILLWORK POCKET.
3. TRANSACTION BAR CONDUITS: PROVIDE FOUR (4) 3/4" CONDUITS FOR POWER AND (4) FOUR 2" CONDUITS FOR TELE/DATA FROM UNDER SLAB WITH CONDUIT BUSHINGS AND PULL STRINGS. COORDINATE WITH ARCHITECT AND MILLWORK VENDOR FOR EXACT STUB-UP LOCATIONS PRIOR TO ROUGH-IN. CONDUITS SHALL BE SEALED TO PREVENT RODENT INTRUSION.

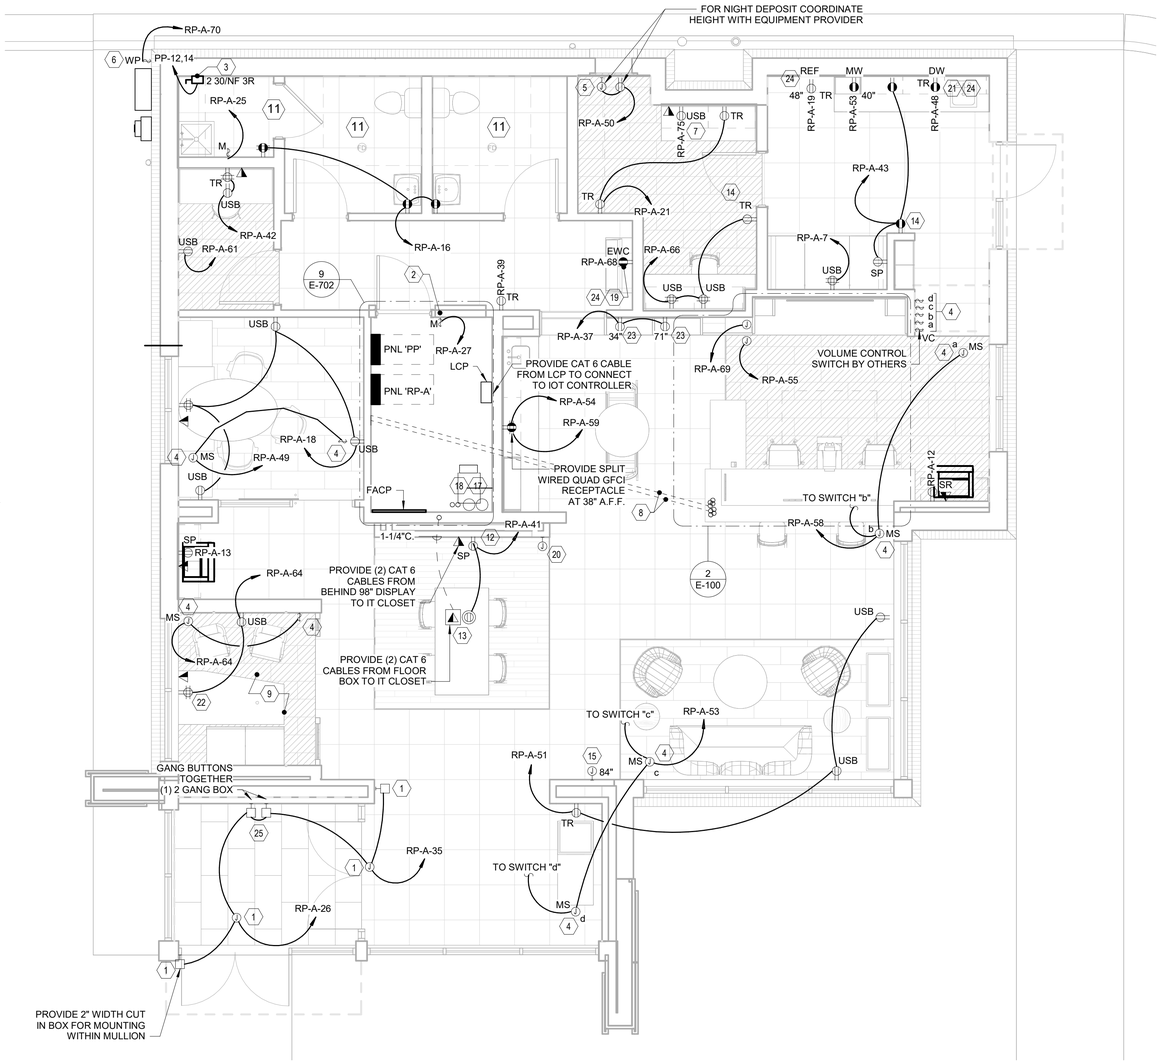

1 E-100 ELECTRICAL POWER & AUXILIARY PLAN
1/4" = 1'-0"

AUXILIARY - GENERAL NOTES:

1. ALL LOW VOLTAGE CONDUITS AND CABLING INCLUDING TELEPHONE, DATA, FIRE ALARM, AUXILIARY, ETC. SHOWN ON THESE PLANS ARE BY THE CONTRACTOR. SEE SHEET E001 "TELDATA" FOR ALL REQUIREMENTS.
2. ALL LOW VOLTAGE CABLES ABOVE ACCESSIBLE CEILING SHALL BE SUPPORTED WITH METALLIC JHOOKS FROM DEVICE LOCATIONS BACK TO THE TBB. WHERE CABLES ARE NOT ACCESSIBLE OR CONCEALED IN WALLS, THEY SHALL BE RUN IN EMT CONDUIT. JHOOKS SHALL BE SPACED SO THAT NO CABLE IS UNSUPPORTED FOR MORE THAN 5'0".

KEYED NOTES:

1. FOR POWER TO DOOR MOTOR AND DOOR PUSH PLATE. COORDINATE LOCATION OF DOOR POWER. PROVIDE 2" WIDTH CUTIN BOX FOR ALL PUSH PLATE MOUNTING WITHIN MULLION. VERIFY ALL REQUIRED CONNECTIONS PRIOR TO ROUGHIN.
2. FOR CONDENSATE PUMP.
3. 30/2 NF DISCONNECT FOR 2KW WATER HEATER, SEE RISER DIAGRAM.
4. RAISE/LOWER SWITCH FOR MECHOSHADES - COORDINATE LOCATION WITH ARCHITECT. THE INTERNET OF TEAM, LLC (IOT) WILL PROVIDE LOW VOLTAGE RAISE/LOWER SWITCHES, LINE VOLTAGE RELAY / MOTOR CONTROLLERS, THE SHADE SOLAR CONTROLLER (INTEGRAL AND PRE-INSTALLED INSIDE LCP) FOR THE ELECTRICAL CONTRACTOR (EC) TO INSTALL. IOT WILL PROVIDE MULTI GANG SWITCH OVER PLATES WHERE SHOWN AS GANGED SWITCH AND COVER PLATE SHALL BE BLACK WITHIN THE BOOTHS. EC SHALL PROVIDE WIRE, CONDUIT, AND ANCILLARY ITEMS NECESSARY TO INSTALL THE SYSTEM. TO COMPLETE THE SHADE CONTROL SYSTEM THE EC MUST PARTICIPATE IN POINT-TO-POINT COMMISSIONING AND RECEIVE SIGN-OFF WITH AN AGENT FROM IOT. REFERENCE IOT SHOP DRAWINGS FOR REQUIRED WIRE SPECIFICATIONS. REFERENCE IOT SHOP DRAWINGS FOR SHADE SYSTEM CONTROL DESIGN DETAILS AND INSTALLATION PROCEDURES. REFERENCE NEC AND LOCAL REQUIREMENTS FOR CONDUIT, FITTINGS, AND FIXTURES FOR CODE COMPLIANCE. COORDINATE ALL REQUIREMENTS WITH ARCHITECT, MECHOSHADE VENDOR, AND THE INTERNET OF TEAM, LLC
5. 4" SQUARE JUNCTION BOX MOUNTED ABOVE NIGHT DEPOSITORY WITH 3/4"C STUBBED ABOVE ACCESSIBLE CEILING FOR ALARM CONNECTION. ELECTRICALCONTRACTOR SHALL MAKE FINAL CONNECTION FROM JBOX TO NIGHT-DEPOSITORY. COORDINATE LOCATION WITH EQUIPMENT VENDOR PRIOR TO ROUGHIN.
6. WP SWITCH FOR DISCONNECTING MEANS OF IRRIGATION CONTROL VERIFY LOCATION PRIOR TO ROUGHIN. SWITCH AND CONTROLLER SHALL BE MOUNTED NEXT TO THE UTILITY METER.
7. USB OUTLET. PROVIDE USB TYPE-A & TYPE-C OUTLET, LEGRAND R26USBACWCCV6, OR EQUAL.
8. TRANSACTION BAR POWER AND DATA STUB-UP. PROVIDE UNDER SLAB CONDUITS AS FOLLOWS: (4) 3/4" IMC FOR POWER AND (4) 2" IMC WITH STRING FOR TELE/DATA TO ELEC/IT ROOM. SEE ENLARGED PLAN FOR DETAILS. ELECTRICAL CONTRACTOR SHALL COORDINATE EXACT LOCATION AND CONNECTION REQUIREMENTS WITH FURNITURE VENDOR AND ARCHITECT PRIOR TO ROUGH-IN.
9. ALL RECEPTACLES AND DATA OUTLETS AT BOOTHS, SHALL HAVE BLACK DEVICES AND COVER PLATES.
10. POWER FOR INDOOR HEAT PUMP UNITS IS DERIVED FROM OUTDOOR HEAT PUMP. ELECTRICAL CONTRACTOR SHALL PROVIDE AND INSTALL CONNECTIONBETWEEN EACH INDOOR AND OUTDOOR UNIT. ELECTRICAL CONTRACTOR SHALL CONNECT DISCONNECT SWITCH PROVIDED BY MECHANICAL FOR EACH UNIT.
11. CONNECT EXHAUST FAN TO LIGHTING CIRCUIT SERVING ROOM. FAN SHALL BE CONTROLLED BY ROOM LIGHT SWITCH.
12. FOR CONNECTION TO VIDEO SIGNAGE DISPLAY MONITORS IN TECH WALL. INDICATED JUNCTION BOXES SHALL BE DOUBLEGANG, DEEP JBOX, EACH WITH 2" EMT STUBBED ABOVE ACCESSIBLE CEILING, PROVIDE BUSHING AND LABELED. CONTRACTOR SHALL COORDINATE EXACT CABLING AND TERMINATIONS WITH VIDEO SIGNAGE PROVIDER AND ARCHITECT. COORDINATE LOCATION OF SIGNAGE PLAYER BOX WITH SIGNAGE PROVIDER. PROVIDE CABLING FROM PLAYER BOX TO DISPLAY MONITORS. VERIFY THATALL CONNECTIONS CAN REACH THE BOXES WHERE THEY ARE TERMINATED AND FED FROM WITHOUT INTERFERING WITH MONITORS. SEE DETAIL 6, SHEET E501 FOR ELEVATIONS.
13. FLOOR BOX - PWR & DATA (RECESSED): PROVIDE RECESSED FLOOR BOX LEGRAND WIREMOLD #RFBA4C30OG, RFBADP, RFBA24C4EXT, 2 HUB, RFBA6A, RFBAMAAP, 6CTC2GY (FLANGED COVER FOR CONCRETE FLOORS) WITH 3/4" IMC FOR POWER AND 1-1/4" IMC WITH PULL STRING FOR TELE/DATA TO ELECIT ROOM. ELECTRICAL CONTRACTOR SHALL COORDINATE EXACT LOCATION AND CONNECTION REQUIREMENTS WITH FURNITURE VENDOR AND ARCHITECT PRIOR TO ROUGH-IN.
14. FOR MONITOR. COORDINATE EXACT LOCATION, MOUNTING HEIGHT AND CONNECTIVITY WITH ARCHITECT PRIOR TO ROUGHIN. VERIFY MOUNTING WITH ARCHITECT.
15. PROVIDE DRIVE THRU ALERT LIGHT WHERE NOTED. COORDINATE ROUGH-IN REQUIREMENTS AND WIRING.
16. NOT USED.
17. STUB UP (2) 2" CONDUITS FROM VTM/ATM DRIVE THROUGH FOR EQUIPMENT DATA CONNECTION.
18. STUB UP (2) 4" CONDUITS FOR TELEPHONE SERVICE ENTRANCE. SEE SITE PLAN.
19. FOR E.W.C. COORDINATE MOUNTING HEIGHT AND EXACT ROUGH-IN LOCATION WITH PLUMBING FIXTURE SUBMITTAL.
20. PROVIDE RECESSED DOUBLE GANG BOX AND (1) CAT 6 CABLE FROM 7" TOUCHPANEL TO IT CLOSET MOUNT AT 44" TO THE CENTER OF THE BOX A.F.F.CONFIRM TOP OF PANEL IS NOT HIGHER THAN 46" A.F.F. TO THE TOP. THE RECESSED DOUBLE GANG BOX SHALL BE MOUNTED VERTICALLY U.O.N.
21. FOR DISHWASHER MOUNT OUTLET IN THE SPACE ADJACENT TO THE SPACE OCCUPIED BY THE DISHWASHER SO THAT THE FLEXIBLE CORD CAN PASS THROUGH THE OPENING. COORDINATE WITH GC FOR OPENING PLACEMENT
22. INSTALL POWER/DATA RECEPTACLE PER ARCHITECTURAL ELEVATIONS TO AVOID FURNITURE PLACEMENT.
23. RECEPTACLES AND COVER PLATES AT LIBRARY WALL SHALL BE BROWN. INSTALL HORIZONTAL AND COORDINATE WITH ARCHITECT AND REFERENCE ARCHITECTURAL ELEVATION DRAWINGS FOR MORE DETAIL.
24. GFCI PROTECTED CONTROLLED RECEPTACLE: CONTROLLED RECEPTACLE SHALL BE FED FROM A GFCI PROTECTED CIRCUIT BREAKER. PROVIDE FACTORY ENGRAVED COVER PLATE WITH 'GFCI PROTECTED' LABEL
25. 2-GANG DOOR PUSH PLATES. EC SHALL INSTALL AND POWER THE POWER SUPPLY (SUPPLIED BY DOOR COMPANY) ABOVE CEILING AND COORDINATE LOCATION OF DOOR POWER. PROVIDE 2-GANG ELECTRICAL BOX FOR PUSH PLATE. VERIFY ALL REQUIRED CONNECTIONS PRIOR TO ROUGH-IN.

PRAXIS3
100 Peachtree St NW
Suite 1450
Atlanta, GA 30303
404-875-4500 tel
www.praxis3.com

GEORGIA REGISTERED No. 041408 PROFESSIONAL ENGINEER RAHN ONEAL WILLIAMS

Copyright (c) 2024 Praxis3, LLC

All reports, plans, specifications, computer files, field data, notes and other documents and instruments prepared by Praxis3 shall retain all common law, statutory and other reserved rights, including copyright thereto.

This drawing may not be reproduced in whole or in part without written permission of Praxis3. It is to be returned upon request. Scales as stated are valid on the original drawings.

Rev	Date	Comments
	07/02/2026	PERMIT SET

Client:
FIFTH THIRD BANK

Project Number: 26032
Project Name:
FIFTH THIRD BANK WATSON 1,900 SF


2711 WATSON BOULEVARD
WARNER ROBBINS, GA 31093

Key Plan:

Sheet Title:
ELECTRICAL POWER & AUXILIARY PLAN

Sheet Number:
E-100


6/30/2026 2:32:01 PM

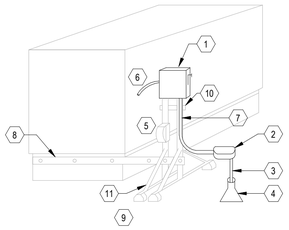

2 / E-101 ROOF DISCONNECT MOUNTING DETAIL
N.T.S.

ROOF DISCONNECT MOUNTING DETAILS KEYNOTES:

1. DISCONNECT SWITCH SHALL BE LOCATED ADJACENT TO (NOT ATTACHED TO) EQUIPMENT AND MEET WORKING CLEARANCES.
2. WEATHERPROOF "LB" CONDUIT TO TRANSITION TO LMFC.
3. HVAC EQUIPMENT FEEDER IN IMC CONDUIT.
4. PROVIDE PITCH POCKET FOR ALL CONDUIT PENETRATIONS.
5. WHERE A RECEPTACLE IS SHOWN ON A UNIT, RECEPTACLE OUTLET WITHIN 25 FT. OF EQUIPMENT WITH AN OUTLET BOX HOOD. RECEPTACLE TO BE GFCI PROTECTED.
6. LFMC PER SPECS WITHIN 12" OR LESS OF THE CONNECTION POINT OF THE UNIT.
7. SUPPORT RACEWAY WITH GALVANIZED MULTISTRUT PIPE CLAMP WHERE RUN UP THE UNITSTRUT.
8. ATTACH UNISTRUT TO CURB (NOT EQUIPMENT AND FLASHING). SEAL ALL PENETRATIONS.
9. UV RESISTANT UNISTRUT SUPPORT BASE. TYPICAL.
10. ADDITIONAL UNITSTRUT SUPPORT PERPENDICULAR TO THE UNISTRUT THAT THE DISCONNECT IS ATTACHED TO.
11. UNISTRUT SUPPORT ADDED AT 45 DEGREE ANGLE FOR ADDITIONAL SUPPORT.

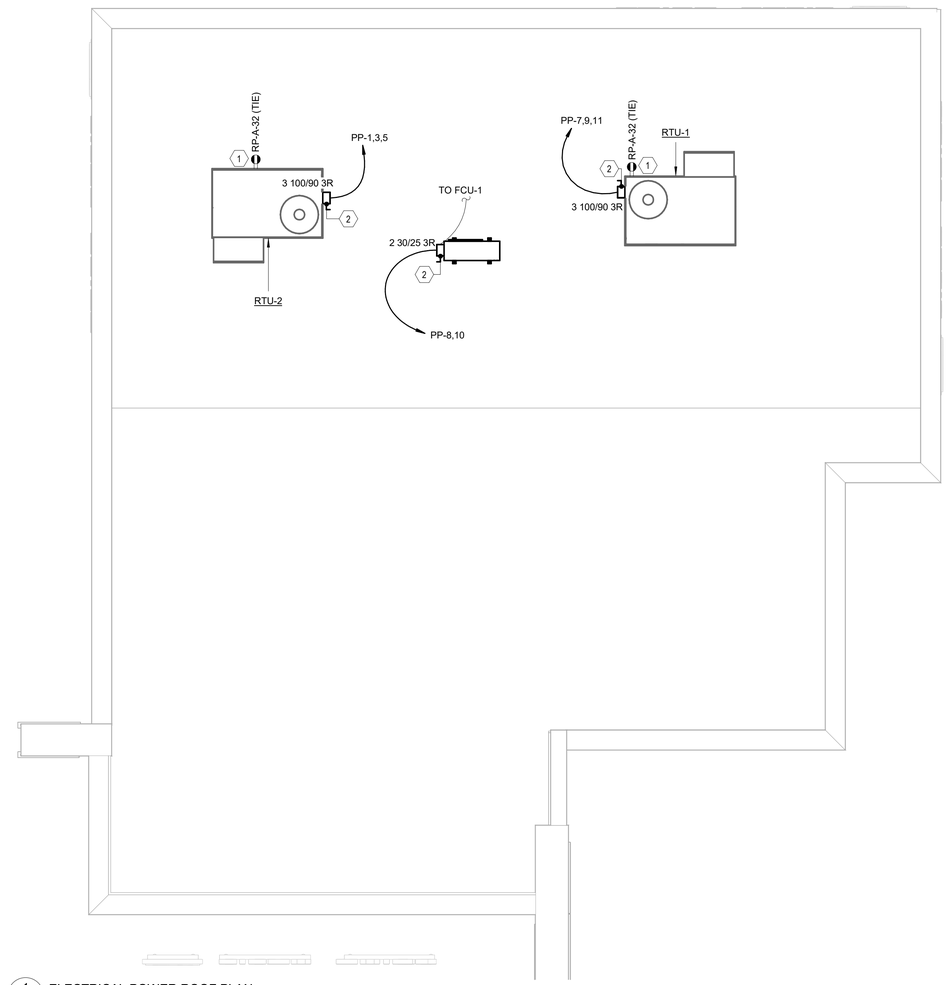

1 / E-101 ELECTRICAL POWER ROOF PLAN
1/4" = 1'-0"

SHEET NOTES:

1. EXACT LOCATIONS OF MECHANICAL EQUIPMENT AND THEIR ELECTRICAL CONNECTIONS SHALL BE COORDINATED WITH MECHANICAL CONTRACTOR. ELECTRICAL CONNECTIONS TO ROOF TOP EQUIPMENT SHALL BE ROUTED WITHIN ROOF CURB
2. COORDINATE WITH MECHANICAL CONTRACTOR FOR MECHANICAL EQUIPMENT DISCONNECT SWITCH RESPONSIBILITIES. FINAL ELECTRICAL INSTALLATION AND CONNECTIONS BY ELECTRICAL CONTRACTOR.
3. PROVIDE APPROPRIATE TRIM RING AND 3/4" CONDUIT WITH INSULATED CONDUIT BUSHINGS AND PULL STRING TO ACCESSIBLE CEILING FOR EACH THERMOSTAT. REFER TO MECHANICAL PLAN FOR THERMOSTAT QUANTITIES AND LOCATIONS. IN AREAS WITH OPEN CEILINGS, A COMPLETE CONDUIT SYSTEM SHALL BE PROVIDED FROM THE THERMOSTAT TO THE MECHANICAL UNIT; FREE WIRING IS NOT ACCEPTABLE.
4. ELECTRICAL CONTRACTOR'S BID SHALL INCLUDE POWER TO ALL MISCELLANEOUS MECHANICAL AND PLUMBING EQUIPMENT ACCESSORIES AND AUXILIARY LOADS WHICH MAY NOT BE REFLECTED IN THE ELECTRICAL PLANS BUT NECESSARY FOR A COMPLETE AND FULLY FUNCTIONING SYSTEM. NO CHANGE ORDERS WILL BE CONSIDERED.

KEYED NOTES:

1. MAINTENANCE RECEPTACLE: PROVIDE 20A, 120V GFCI WEATHERPROOF/WEATHER-RESISTANT RECEPTACLE WITH METALLIC WHILE-IN-USE COVER IF NOT PROVIDED BY RTU MANUFACTURER. PROVIDE POWER CONNECTIONS AS REQUIRED BY RTU MANUFACTURER
2. MECHANICAL UNIT DISCONNECT SWITCH: PROVIDE NEMA 3R FUSIBLE DISCONNECT SWITCH. REFER TO "ROOF DISCONNECT MOUNTING DETAIL" ON THIS SHEET FOR MORE DETAILS.

PRAXIS3
100 Peachtree St NW
Suite 1450
Atlanta, GA 30303
404-875-4500 tel
www.praxis3.com



Copyright (c) 2024 Praxis3, LLC

All reports, plans, specifications, computer files, field data, notes and other documents and instruments prepared by Praxis3 shall retain all common law, statutory and other reserved rights, including copyright thereto.

This drawing may not be reproduced in whole or in part without written permission of Praxis3. It is to be returned upon request. Scales as stated are valid on the original drawings.

Rev	Date	Comments
	07/02/2026	PERMIT SET

Client:
FIFTH THIRD BANK

Project Number: 26032
Project Name:
FIFTH THIRD BANK
WATSON
1,900 SF


2711 WATSON BOULEVARD
WARNER ROBBINS, GA 31093

Key Plan:

Sheet Title:
ELECTRICAL POWER ROOF PLAN

Sheet Number:
E-101


6/30/2026 2:32:02 PM

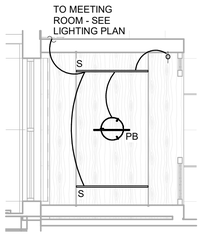

2 E-130 ELECTRICAL LIGHTING PLAN - BOOTH
1/4" = 1'-0"


LCP SCHEDULE

RELAY NUMBER	PANEL	CIRCUIT NUMBER	DESCRIPTION OF AREA	LOCAL CONTROL
1	RPA	47	CRITICAL LTG CONTACTOR	EXTERIOR OVERRIDE SWITCH
2	RPA	57	NONCRITICAL LTG CONTACTOR	EXTERIOR OVERRIDE SWITCH
3	RPA	44	EXTERIOR SIGNAGE	EXTERIOR OVERRIDE SWITCH
4	RPA	11	EXTERIOR SIGNAGE	EXTERIOR OVERRIDE SWITCH
5	RPA	5	WEATHER VESTIBULE/ENTRY	OVERRIDE SWITCH "a"
6	RPA	8	LIBRARY/TRANSACTION BAR	OVERRIDE SWITCH "b" & ELV DIMMER "b"
7	RPA	8	LIBRARY/TRANSACTION BAR	OVERRIDE SWITCH "i" & ELV DIMMER "i"
8	RPA	9	BANKING LOBBY	OVERRIDE SWITCH "c"
9	RPA	10	VESTIBULE 116 LOCAL	OVERRIDE SWITCH "d"
10	RPA	24	GATHERING AREA	OVERRIDE SWITCH "e"
11	RPA	8	UNDERCOUNTER SERVICE BAR	EXTERIOR OVERRIDE SWITCH "h"
12	RPA	6	EXTERIOR SIGNAGE	EXTERIOR OVERRIDE SWITCH
13	RPA	60	ATM TOPPER LIGHTING	EXTERIOR OVERRIDE SWITCH
14	RPA	3	UPLIGHTS AND PARAPET LIGHTING	EXTERIOR OVERRIDE SWITCH
15	RPA	4	EXTERIOR CANOPY LIGHTING	EXTERIOR OVERRIDE SWITCH

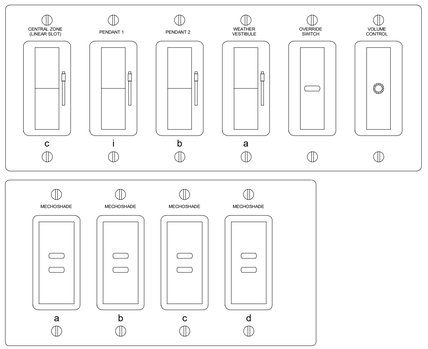

NOTES:
1. PROVIDE LABELED COVER PLATE WITH DESCRIPTION OF LOAD ABOVE EACH SWITCH. PROVIDE SUBMITTAL WITH LEGEND PRIOR TO ORDERING FOR ENGINEER APPROVAL.
2. COORDINATE WITH ARCHITECT FOR EXACT LOCATION AND MOUNTING HEIGHT PRIOR TO ROUGH-IN.
3. SWITCHES SHALL BE GROUPED AS SHOWN WITH SINGLE GANGED COVER PLATE.
4. LINE VOLTAGE ON/OFF TOGGLE AND DECORA ROCKER SWITCHES SHALL BE PROVIDED WITH A PILOT LIGHT TO INDICATE WHEN LIGHTS ARE 'ON'.

3 E-130 SWITCH BANK DETAIL
N.T.S.

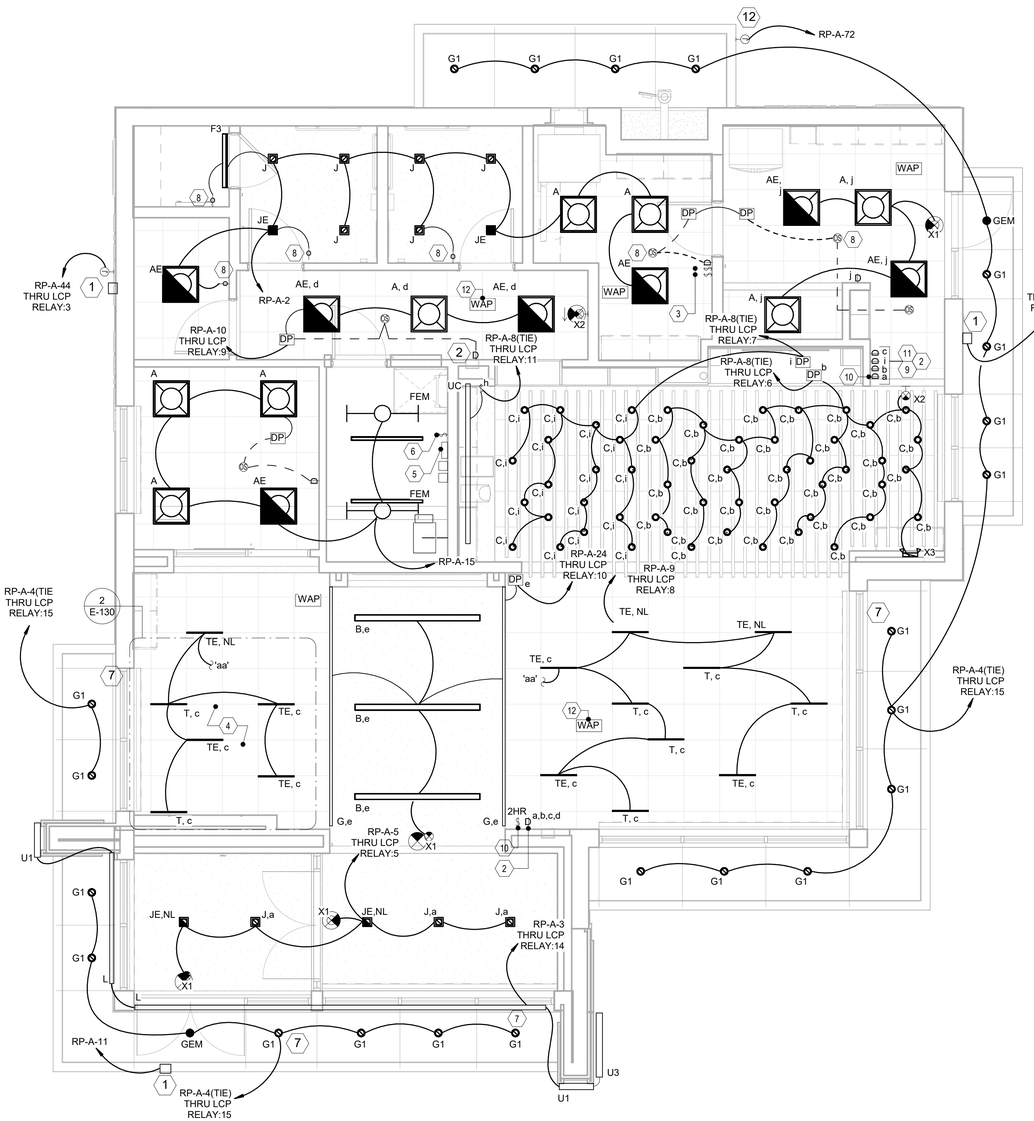

1 E-130 ELECTRICAL POWER & AUXILIARY PLAN
1/4" = 1'-0"

SHEET NOTES:

1. HALF SHADED OR FULLY SHADED LUMINAIRES SHALL BE PROVIDED WITH SELFCONTAINED 90MINUTE BACKUP BATTERY PACKS.
2. EMERGENCY LIGHTING FIXTURES SHALL SWITCH WITH LOCAL NORMAL LIGHTING UNLESS INDICATED AS "EM/NL" OR "NL" (NIGHT LIGHT).
3. EMERGENCY FIXTURES WITH INTEGRAL 90MINUTE BATTERY PACKS SHALL BE PROVIDED WITH AN UNSWITCHED HOT CONDUCTOR SO THAT EMERGENCY BATTERY PACK CAN CHARGE WHEN POWER TO THE LIGHT FIXTURES IS SWITCHED OFF.
4. EXIT AND NIGHT LIGHT FIXTURES SHALL BE CONNECTED TO UNSWITCHE D CIRCUIT AHEAD OF LIGHTING CONTROLLER.
5. THE CIRCUIT NEUTRAL CONDUCTOR SHALL BE ROUTED TO EACH LINE VOLTAGE WALL SWITCH. WHERE THE WIRING DEVICE DOES NOT REQUIRE THE USE OF A NEUTRAL CONDUCTOR, CAP FOR FUTURE USE.
6. LOW VOLTAGE CIRCUITRY IS NOT SHOWN ON THE FLOOR PLANS FOR CLARITY. LOW VOLTAGE CIRCUITRY SHALL BE PROVIDED AND INSTALLED IN ACCORDANCE WITH THE LIGHTING CONTROL VENDOR'S INSTRUCTIONS AND AS REQUIRED BETWEEN ALL LOW VOLTAGE CONTROLS AND FIXTURES.
7. LIGHTING CONTROLS VENDOR SHALL PRODUCE AND SUBMIT JOB SPECIFIC SHOP DRAWINGS SHOWING ALL DEVICE LOCATIONS, SENSOR COVERAGE, AND TERMINALTOTERMINAL WIRING DIAGRAMS SPECIFIC TO THIS PROJECT.

KEYED NOTES:

1. DISCONNECT SWITCH FOR BANK LOGO SIGN. ROUTE 1" C TO PANEL RPA THRU LIGHTING CONTROL PANEL. ELECTRICAL CONTRACTOR SHALL COORDINATE WITH ARCHITECTURAL ELEVATIONS AND SIGNAGE PROVIDER FOR EXACT LOCATION, QUANTITIES AND MOUNTING HEIGHT PRIOR TO ROUGHIN.
2. LOW VOLTAGE ON/OFF/DIMMING OVERRIDE SWITCHES FOR INTERIOR LIGHTING. SWITCH SHALL HAVE THE ABILITY TO TURN THE ZONE ON/OFF DURING PROGRAM "ON" HOURS, HAVE THE ABILITY TO MANUALLY OVERRIDE THE LIGHTS TO BE "ON" FOR TWO HOURS DURING "OFF HOURS",AND HAVE THE ABILITY TO DIM THE LIGHTS.
3. DRIVE THROUGH LANE OPEN/CLOSE GANG SWITCHES. SEE DETAIL 9 ON E-500. COORDINATE PLACEMENT WITH ARCHITECT PRIOR TO ROUGH-IN.
4. FIXTURES "PB" AND "S" SHALL BE MOUNTED AT BOOTH CEILING HEIGHT (SEE BOOTH ENLARGED PLAN). FIXTURES "T" SHALL BE MOUNTED ABOVE BOOTH. SEE ARCHITECTURAL RCP.
5. INTERNET OF TEAM BMS LCP-SA LIGHTING CONTROL PANEL. PANEL HARDWARE IS BY INTERNET OF TEAM AND SHALL BE PREPROGRAMMED PER LCP SCHEDULE. PROVIDE FOUR HOURS FOR INSTALLATION AND COMMISSIONING. PROVIDE AND INSTALL SECONDARY PANEL AS NEED FOR THE NUMBER OF RELAY SPACES.PANEL SHALL HAVE ABILITY TO CONNECT TO BUILDING AUTOMATION SYSTEM.
6. PROVIDE AN OVERRIDE SWITCH FOR TESTING OF EXTERIOR AND SITE LIGHTING. SEE LIGHTING CONTROL SCHEDULE.
7. PROVIDE PHOTOSENSOR TO INTERFACE WITH LCP AND BMS FOR EXTERIOR LIGHTING CONTROL. INSTALL PHOTOSENSOR TO WHERE THE EYE OF THE PHOTOSENSOR FACES DUE NORTH. LOCATE PHOTOSENSOR SOMEWHERE THAT IS EXPOSED TO FULL DAYLIGHT AND IS NOT SHADOWED OR DIRECTLY EXPOSED TO ANY NIGHTTIME ILLUMINATION OR ANY OTHER OBSTRUCTIONS.
8. SET LIGHT CONTROLS FOR "OCCUPANCY SENSOR" MODE, TO TURN LIGHTS ON WHEN OCCUPANCY DETECTED.
9. LOW VOLTAGE ON/OFF OVERRIDE SWITCHES FOR TRANSACTION BAR/ LIBRARYLIGHTING. SWITCH SHALL HAVE THE ABILITY TO TURN THE ZONE ON/O FF DURING PROGRAM "ON" HOURS AND HAVE THE ABILITY TO MANUALLY OVERRIDE THE LIGHTS TO BE "ON" FOR TWO HOURS DURING "OFF HOURS". PROVIDE LINE VOLTAGE ELV DIMMER SEPARATELY AS SHOWN.
10. LOW VOLTAGE 2HOUR MANUAL OVERRIDE SWITCH FOR MULTIZONES. LABEL EACH BUTTON WITH ITS RESPECTIVE ROOM/AREA. SWITCH SHALL HAVE ABILITY MANUALLY OVERRIDE THE LIGHTS TO BE "ON" FOR TWO HOURS DURING "OFF HOURS".
11. SWITCH BANK: REFER TO SWITCH BANK DETAIL THIS SHEET AND ELEVATION #3 ON SHEET E-703
12. PROVIDE WEATHER PROOF JUNCTION BOX FOR OPEN/CLOSE SIGN. COORDINATE FINAL LOCATION WITH ARCHITECT.

PRAXIS3
100 Peachtree St NW
Suite 1450
Atlanta, GA 30303
404-875-4500 tel
www.praxis3.com

GEORGIA REGISTERED No. 041508 PROFESSIONAL ENGINEER RAHN ONEAL WILLIAMS

Copyright (c) 2024 Praxis3, LLC

All reports, plans, specifications, computer files, field data, notes and other documents and instruments prepared by Praxis3 shall retain all common law, statutory and other reserved rights, including copyright thereto.

This drawing may not be reproduced in whole or in part without written permission of Praxis3. It is to be returned upon request. Scales as stated are valid on the original drawings.

Rev	Date	Comments
	07/02/2026	PERMIT SET

Client:
FIFTH THIRD BANK

Project Number: 26032
Project Name:
FIFTH THIRD BANK WATSON 1,900 SF

2711 WATSON BOULEVARD
WARNER ROBBINS, GA 31093

Key Plan:

Sheet Title:
ELECTRICAL LIGHTING PLAN

Sheet Number:
E-130

6/30/2026 2:32:04 PM

POWER SYMBOLS:

NOTE: A COMPLETE LIST OF RECEPTACLE SYMBOLS IS SHOWN FOR THE DUPLEX RECEPTACLE ONLY. OTHER RECEPTACLE SYMBOLS WILL FOLLOW THE SAME SHADING CONVENTION AS THE DUPLEX RECEPTACLE, UNO.

CENTER HATCH: ISOLATED GROUND RECEPTACLE
OUTER HATCH: GFCI RECEPTACLE
RIGHT HATCH: CONTROLLED RECEPTACLE

20A, 125V, RECEPTACLE
(NEMA 520R), WALL MTD
(SIMPLEX LEFT, DUPLEX CENTER, QUAD RIGHT)
D= DUAL SWITCHED
H = HALF SWITCHED
TR = TAMPER RESISTANT
U= USB OUTLET
WP = WEATHERPROOF
WR = WEATHER RESISTANT
SP = SURGE PROTECTIVE
(LEVITON T5380W OR EQUAL)

20A, 125V, IG DUPLEX RECEPTACLE
(NEMA 520R), WALL MTD

20A, 125V, GFCI DUPLEX RECEPTACLE
(NEMA 520R), WALL MTD

20A, 125V, GFCI DUPLEX RECEPTACLE
(NEMA 520R), WALL MTD

20A, 125V, RECEPTACLE ON EMERGENCY
CIRCUIT (NEMA 520R), WALL MTD
(SIMPLEX LEFT, DUPLEX CENTER, QUAD RIGHT)

20A, 125V, RECEPTACLE
(NEMA 520R), FLOOR MTD
(SIMPLEX LEFT, DUPLEX CENTER, QUAD RIGHT)

20A, 125V, RECEPTACLE ON EMERGENCY
CIRCUIT (NEMA 520R), FLOOR MTD
(SIMPLEX LEFT, DUPLEX CENTER, QUAD RIGHT)

20A, 125V, RECEPTACLE
(NEMA 520R), CEILING MTD
(SIMPLEX LEFT, DUPLEX CENTER, QUAD RIGHT)

20A, 125V, RECEPTACLE ON EMERGENCY
CIRCUIT (NEMA 520R), CEILING MTD
(SIMPLEX LEFT, DUPLEX CENTER, QUAD RIGHT)

FB — MULTISERVICE, FLOOR BOX, FLUSH MNT
(SEE SPECS OR NOTES)
FB = FLOOR BOX
FF = FURNITURE FEED

PT — MULTISERVICE, POKE-
THRU, 2 HR. FIRERATED, FLUSH MNT (SEE SPECS OR NOTES)
PT = POKETHRU
FF = FURNITURE FEED

PT — MULTISERVICE, CEILING BOX WITH PROJECTOR MOUNT (SEE SPECS OR NOTES)

WB — MULTISERVICE, WALL BOX, RECESSED MNT
(SEE SPECS OR NOTES)

SPECIAL PURPOSE RECEPTACLE
(SEE EQUIPMENT SCHEDULE OR NOTES)
(WALL MNT LEFT, FLOOR MTD RIGHT)

SPECIAL PURPOSE RECEPTACLE ON
EMERGENCY CIRCUIT
(SEE EQUIPMENT SCHEDULE OR NOTES)
(WALL MNT LEFT, FLOOR MTD RIGHT

60A — 60A, 480V, 3PH, WELDING RECEPTACLE, WALL MTD

DROP CORD (SEE SPECS OR NOTES)

POWER POLE (SEE SPECS OR NOTES)

RECEPTACLE RACEWAY / PLUG MOLD

J — JUNCTION BOX, WALL MTD

WP — JUNCTION BOX
WP = WEATHERPROOF

J — JUNCTION BOX, FLOOR MTD

J — JUNCTION BOX, EXPLOSION PROOF

30/NF — SAFETY SWITCH, 30A, 3POLE, NONFUSED
(FBO - FURNISHED BY OTHERS)

30/20 — SAFETY SWITCH, 30A, 3POLE, FUSED @ 20A
(FBO - FURNISHED BY OTHERS)

STARTER OR MOTOR CONTROLLER

T — STARTER, COMBINATION W/ DISC. SWITCH

TRANSFORMER

ELECTRICAL PANEL / ENCLOSURE AS NOTED ON
PLAN DRAWINGS
(SURFACE MTD LEFT, RECESSED MTD RIGHT)

ELECTRIC UTILITY METER

GROUNDING BUSBAR (SEE SPECS OR NOTES)

PP — UTILITY POWER POLE

LIGHTING SYMBOLS:

NOTE: REFER TO LIGHTING FIXTURE SCHEDULE FOR FIXTURE TYPES AND SENSOR SCHEDULE FOR SENSOR TYPES. REFER TO PLAN DRAWINGS FOR ADDITIONAL SYMBOLS.

A: — CAPITAL LETTER ADJACENT TO FIXTURE = TYPE

a: — LOWERCASE LETTER = SWITCHING GROUP

EM: — EMERGENCY LIGHTING IS DESIGNATED BY AN "EM" ADJACENT TO THE FIXTURE AND/OR A "HALF SHADED" OR "FULL SHADED" FIXTURE SYMBOL

NL: — NIGHT LIGHTING (UNSWITCHED FIXTURE)

$^{x}_{xx} — SWITCH, 20A, 120/277V, TOGGLE TYPE, U.N.O.
a,b,c,... =SWITCHING GROUP
BLANK =SINGLE POLE
2 =DOUBLE POLE
3 =THREEWAY
4 =FOURWAY
D =DIMMER SWITCH
K =SINGLE POLE KEY OPERATED
M =MOTOR RATED
MA =MAINTAINED CONTACT
MO =MOMENTARY CONTACT
P =SINGLE POLE W/ PILOT LIGHT
P2 =DOUBLE POLE W/ PILOT LIGHT
RC =REMOTE CONTROL
T =TIMER OPERATED SWITCH
WP =WEATHERPROOF
2HR =2HOUR OVERRIDE SWITCH

B — BLANK PLATE

O — OCCUPANCY SENSOR, WALL MTD

D^{x}_{xx} — LOW VOLTAGE DIGITAL SWITCH, WALL MTD

DP — LIGHTING CONTROL DEVICE
DP =DIMMABLE POWER PACK (ON/OFF WITH DIMMING)
PP =POWER PACK (ON/OFF)
RP =AUX. RELAY PACK (ON/OFF)
GW =GATEWAY
PS =POWER SUPPLY
BR =BRIDGE
LC =LIGHTING CONTACTOR
TC =TIME CLOCK
MS =MOTION SENSOR
PC =PHOTOCELL

PL — PLUG LOAD CONTROLLER (ON/OFF)

EPC — EMERGENCY POWER CONTROLLER

OCCUPANCY SENSOR, CORNER MTD

OS — OCCUPANCY SENSOR, CEILING MTD

DS — DAYLIGHT SENSOR, CEILING MTD

OS/DS — COMBINATION OCCUPANCY / DAYLIGHT SENSOR, CEILING MTD

2'X4' LAYIN TROFFER

2'X2' LAYIN TROFFER

1'X4' LAYIN TROFFER

STRIP/CHANNEL FIXTURE

DOWNLIGHT, CEILING MTD

WALL WASHER, CEILING MTD

LIGHT FIXTURE, CEILING MTD

LIGHT FIXTURE, WALL MTD

WALL PACK

EMERGENCY WALL PACK (BUG EYE)
(WALL MTD LEFT, CEILING MTD RIGHT)

EXIT SIGN, SINGLE FACE
(ARROW INDICATES DIRECTION OF EGRESS)
(WALL MTD LEFT, CEILING MTD RIGHT)

EXIT SIGN, DOUBLE FACE
(ARROW INDICATES DIRECTION OF EGRESS)
(WALL MTD LEFT, CEILING MTD RIGHT)

EXIT SIGN W/ COMBINATION EMERGENCY LIGHT, SINGLE FACE
(ARROW INDICATES DIRECTION OF EGRESS)
(WALL MTD LEFT, CEILING MTD RIGHT)

SPECIAL SYSTEMS SYMBOLS:

NOTE: UNLESS NOTED OTHERWISE, PROVIDE OVERSIZED JUNCTION BOX AND 1" EMPTY CONDUIT WITH PLASTIC INSULATING BUSHINGS AND PULL STRING STUBBED MIN. 6" INTO ACCESSIBLE CEILING SPACE. COORDINATE WITH LV CONTRACTOR FOR FINAL REQUIREMENTS.

TELEPHONE OUTLET, WALL MTD
1 TELE OUTLET, U.N.O.

COMBINATION TELE/DATA OUTLET, WALL MTD
1 TELE / 1 DATA OUTLET, U.N.O.

COMBINATION TELE/DATA OUTLET, WALL MTD
1 TELE / 2 DATA OUTLETS, U.N.O.

TELEPHONE OUTLET
1 TELE OUTLET, U.N.O.
(FLOOR MTD LEFT, CEILING MTD RIGHT)

COMBINATION TELE/DATA OUTLET
1 TELE / 1 DATA OUTLET, U.N.O.
(FLOOR MTD LEFT, CEILING MTD RIGHT)

COMBINATION TELE/DATA OUTLET
1 TELE / 2 DATA OUTLETS, U.N.O.
(FLOOR MTD LEFT, CEILING MTD RIGHT

TELEPHONE BACKBOARD (TBB)

INTERCOM OUTLET

M / I — INTERCOM STATION
BLANK = REMOTE
M = MASTER

AV AV — AUDIO / VIDEO DEVICE
(WALL MTD LEFT, CEILING MTD RIGHT)
AV = AUDIO / VIDEO OUTLET
M = MICROPHONE OUTLET
SM = SECURITY MONITOR OUTLET
TV = TELEVISION OUTLET
V=VOLUME CONTROL

AMP — SOUND SYSTEM AMPLIFIER

S S — SPEAKER
(WALL MTD LEFT, CEILING MTD RIGHT)

B — AUDIBLE NOTIFICATION DEVICE
B= BELL
C= CHIME
G= GONG

B — BUZZER

B — BELL & BUZZER COMBINATION

H — AUDIBLE NOTIFICATION DEVICE
H= HORN
S= SIREN

BT — AUXILIARY SYSTEM DEVICE
BT= BELL RINGING TRANSFORMER
R= RELAY
D= ELECTRIC DOOR OPENER
LV= LOW VOLTAGE TRANSFORMER

ANNUNCIATOR

BL BL — INDICATOR LIGHT
(WALL MTD LEFT, CEILING MTD RIGHT)
BL = BURGLAR ALARM LIGHT

M — CLOCK
M = MASTER
DF = DOUBLE FACE
S = COMBINATION SPEAKER

DC PVM — SECURITY DEVICES
DC = DOOR CONTACT
GB = GLASS BREAK DETECTOR
HD = HEAT DETECTOR
HU = HOLDUP BUTTON
KP = KEY PAD
MD = MOTION DETECTOR
PB = PANIC BUTTON
PVM = PUBLIC VIEW MONITOR
SD = SOUND DETECTOR
SEC = SECURITY CONTROL PANEL
VS = VIBRATION SENSOR
WC = WINDOW CONTACT

CR ACP — ACCESS CONTROL DEVICE
ACP = ACCESS CONTROL PANEL
CR = CARD READER
ES = ELECTRIC STRIKE
ML = MAGNETIC LOCK
PS = PROXIMITY SENSOR
PWR = POWER SUPPLY
RX = REQUEST EXIT PUSH BUTTON

XX XX — SECURITY CAMERA
(WALL MTD LEFT, CEILING MTD RIGHT)
PTZ = PAN/TILT/ZOOM
BX = BOX
D=MINI DOME
BL = BULLET
WP = WEATHERPROOF

PUSHBUTTON STATION
(BUTTONS REPRESENTED BY SOLID DOTS

NORMAL / EMERGENCY CALL BUTTON

PUSH BUTTON

RACEWAY SYMBOLS:

HOMERUN CIRCUIT TO PANELBOARD

LOW VOLTAGE CABLE

CONDUIT BURIED

CONDUIT CONCEALED

CONDUIT EXPOSED

FLEXIBLE CONDUIT

CONDUIT UP

CONDUIT DOWN

CONDUIT SEALOFF

CONDUIT TEE BODY

CONDUIT EL BODY

CONDUIT CAP

CONDUIT SLEEVE WITH BUSHINGS

PB — PULL BOX

HH — HAND HOLE

FIRE ALARM SYMBOL LEGEND

SYMBOL	DESCRIPTION
F	FIRE ALARM ADA APPROVED WALL MOUNTED HORN/STROBE ALARM. ENTIRE LENS SHALL NOT BE LESS THAN 80" AND NOT GREATER THAN 96" AFF.
V	FIRE ALARM ADA APPROVED WALL MOUNTED VISUAL ALARM. ENTIRE LENS SHALL NOT BE LESS THAN 80" AND NOT GREATER THAN 96" AFF.
FACP	FIRE ALARM CONTROL PANEL
FAA	FIRE ALARM ANNUNCIATOR
D D	FIRE ALARM SMOKE DETECTOR - WALL MTD., CEILING MTD.
F	FIRE ALARM PULL STATION
D	DUCT MOUNTED SMOKE DETECTOR

CODE IN EFFECT(GA):

ALL WORK SHALL BE IN STRICT ACCORDANCE WITH:

- NATIONAL ELECTRICAL CODE - 2020
- GEORGIA BUILDING CODE - 2015 IECC

WORK AND EQUIPMENT UNDER THIS DIVISION SHALL BE IN STRICT COMPLIANCE WITH THE CODES, STANDARDS, AND PRACTICES LISTED HEREIN. THEIR RESPECTIVE DATES ARE FURNISHED AS THE MINIMUM REQUIREMENTS (UNLESS OTHERWISE DETERMINED BY THE LOCAL AUTHORITIES HAVING JURISDICTION).

ABBREVIATIONS:

A	AMPERE
AFC	AVAILABLE FAULT CURRENT
AFCI	ARC FAULT CIRCUIT INTERRUPTER
AFF	ABOVE FINISHED FLOOR
AFG	ABOVE FINISHED GRADE
AHJ	AUTHORITY HAVING JURISDICTION
AIC	AMPERE INTERRUPTING CAPACITY
ATS	AUTOMATIC TRANSFER SWITCH
BLDG	BUILDING
BRKR	BREAKER
C	CONDUIT
CKT	CIRCUIT
CLG	CEILING
CPT	CONTROL POWER TRANSFORMER
CT	CURRENT TRANSFORMER
CU	COPPER
CTR	CENTER
EA	EACH
EG	EQUIPMENT GROUND
EGC	EQUIPMENT GROUNDING CONDUCTOR
EM	EMERGENCY
EOL	ELECTRONIC OVERLOAD
FDR	FEEDER
FLA	FULL LOAD AMPS
GEC	GROUNDING ELECTRODE CONDUCTOR
GFI	GROUND FAULT INTERRUPTER
GFCI	GROUND FAULT CIRCUIT INTERRUPTER
GND	GROUND
GRS	GALVANIZED RIGID STEEL
HTD	HEATED
HOA	HANDOFFAUTO
IG	ISOLATED GROUND
JB	JUNCTION BOX
KVA	KILOVOLTAMPERE
KW	KILOWATT
L.S.I.G.	LONG, SHORT, INSTANTANEOUS, GROUND FAULT TRIP
LTG	LIGHTING
MCA	MINIMUM CIRCUIT AMPS
MCB	MAIN CIRCUIT BREAKER
MCC	MOTOR CONTROL CENTER
MCCB	MOLDED CASE CIRCUIT BREAKER
MCP	MOTOR CIRCUIT PROTECTOR
MDP	MAIN DISTRIBUTION PANEL
MFS	MAXIMUM FUSE SIZE
MGB	MAIN GROUNDING BUSBAR
MLO	MAIN LUG ONLY
MOCP	MAXIMUM OVERCURRENT PROTECTION
MTD	MOUNTED
MTS	MANUAL TRANSFER SWITCH
N.C.	NORMALLY CLOSED
N.O.	NORMALLY OPEN
NL	NIGHT LIGHT
NTS	NOT TO SCALE
OCPD	OVERCURRENT PROTECTION DEVICE
OH	OVERHEAD
P	POLE
PH	PHASE
PNL	PANEL
PWR	POWER
RECEP	RECEPTACLE
RI	REACHIN
RM	ROOM
SC	SECONTAINED
SCCR	SHORT CIRCUIT CURRENT RATING
SOL	SOLENOID
SW	SWITCH
SWBR	SWITCHBOARD
SWGR	SWITCHGEAR
TBB	TELEPHONE BACKBOARD
TD	TIME DELAY
TELCO	TELEPHONE COMPANY
TELE	TELEPHONE
TGB	TELECOMMUNICATIONS GROUNDING BUSBAR
TMGB	TELECOMMUNICATIONS MAIN GROUNDING BUSBAR
TYP	TYPICAL
UG	UNDERGROUND
UNO	UNLESS NOTED OTHERWISE
UPS	UNINTERRUPTIBLE POWER SUPPLY
V	VOLT
VIF	VERIFY IN FIELD
W/	WITH
W	WIRE
WP	WEATHERPROOF
WR	WEATHER RESISTANT
WTOP	WORKTOP
XFMR	TRANSFORMER

ELECTRICAL SHEET INDEX:

E-001	ELECTRICAL LEGEND AND ABBREVIATION
E-002	ELECTRICAL GENERAL NOTES
E-003	ELECTRICAL SPECIFICATIONS
E-004	COMCHECK
E-010	ELECTRICAL SITE PLAN AND REMOTE DRIVE THRU
E-011	ELECTRICAL PHOTOMETRIC SITE PLAN
E-012	ELECTRICAL SITE DETAILS
E-100	ELECTRICAL POWER & AUXILIARY PLAN
E-101	ELECTRICAL POWER ROOF PLAN
E-130	ELECTRICAL LIGHTING PLAN
E-150	ELECTRICAL SECURITY PLAN
E-500	ELECTRICAL DETAILS
E-600	LUMINAIRE AND SENSOR SCHEDULES AND DETAILS
E-601	EXTERIOR LIGHTING CUTSHEETS
E-602	EXTERIOR LIGHTING CUTSHEETS
E-603	EXTERIOR LIGHTING CUTSHEETS
E-610	ELECTRICAL PANEL SCHEDULES
E-700	ELECTRICAL DEVICE PLAN
E-701	ELECTRICAL ELEVATIONS
E-702	ELECTRICAL ELEVATIONS
E-703	ELECTRICAL ELEVATIONS
E-704	ELECTRICAL ELEVATIONS
E-800	ELECTRICAL RISER DIAGRAM

PRAXIS3
100 Peachtree St NW
Suite 1450
Atlanta, GA 30303
404-875-4500 tel
www.praxis3.com

GEORGIA REGISTERED No. 041560 PROFESSIONAL ENGINEER RAHN ONEAL WILLIAMS

Copyright (c) 2024 Praxis3, LLC

All reports, plans, specifications, computer files, field data, notes and other documents and instruments prepared by Praxis3 shall retain all common law, statutory and other reserved rights, including copyright thereto.

This drawing may not be reproduced in whole or in part without written permission of Praxis3. It is to be returned upon request. Scales as stated are valid on the original drawings.

Rev	Date	Comments
	07/02/2026	PERMIT SET

Client:
FIFTH THIRD BANK

Project Number: 26032
Project Name:
FIFTH THIRD BANK WATSON
1,900 SF

2711 WATSON BOULEVARD
WARNER ROBBINS, GA 31093

Key Plan:

Sheet Title:
ELECTRICAL LEGEND AND ABBREVIATION

Sheet Number:
E-001

6/30/2026 2:31:56 PM

GENERAL NOTES:

1. PRE-BID SITE VISIT: CONTRACTOR PROPOSING TO UNDERTAKE WORK UNDER THIS DIVISION SHALL VISIT THE SITE OF THE WORK AND FULLY INFORM THEMSELVES OF ALL CONDITIONS THAT EFFECT THE WORK AND COST THEREOF AND EXAMINE THE DRAWINGS AS RELATED TO THE SITE CONDITIONS. BIDDERS WHO DO NOT VISIT THE SITE MAY BE UNILATERALLY NOT PERMITTED TO SUBMIT A BID IF THE OWNER SO DESIGNATES.
2. BID TERMS AND CONDITIONS: THE ELECTRICAL CONTRACTOR SHALL OBTAIN A FULL SET OF PLANS AND SPECIFICATIONS FROM THE GENERAL CONTRACTOR PRIOR TO BID. CONSIDERATION WILL NOT BE GRANTED FOR ANY ALLEGED MISUNDERSTANDINGS OF THE AMOUNT OF WORK TO BE PERFORMED. TENDER OF PROPOSAL SHALL CONVEY FULL AGREEMENT TO THE ITEMS AND CONDITIONS INDICATED IN THE PLANS AND SPECIFICATIONS. ANY DISCREPANCIES OR OMISSIONS FOUND IN THE CONTRACT DOCUMENTS OR DOUBT AS TO THE INTENT THEREOF, SHALL BE IMMEDIATELY BROUGHT TO THE ATTENTION OF THE ARCHITECT IN WRITING TO OBTAIN CLARIFICATION FROM THE ENGINEER AND/OR OWNER'S REPRESENTATIVE PRIOR TO SUBMITTING PROPOSAL FOR WORK. WHERE CLARIFICATION CANNOT BE PROVIDED PRIOR TO BID, THE CONTRACTOR SHALL ASSUME THE MORE EXPENSIVE METHOD FOR THE BID. WITHOUT FORMAL AUTHORIZATION, THE ARCHITECT AND OWNER RESERVE THE RIGHT TO REQUIRE THE MORE RESTRICTIVE SPECIFICATION.
3. EXCLUSIONS: MATERIAL AND LABOR EXCLUDED BY THE ELECTRICAL CONTRACTOR SHALL NOT RELIEVE THE GENERAL CONTRACTOR FROM PROVIDING SAME.
4. COMPLETE SYSTEM: FURNISH ALL LABOR, MATERIALS, EQUIPMENT, TOOLS, TRANSPORTATION, SUPERINTENDENTS AND SERVICES REQUIRED TO CONSTRUCT, INSTALL, AND MODIFY THE ELECTRICAL SYSTEMS AS HEREIN SPECIFIED AND SHOWN ON THESE DRAWINGS FOR A COMPLETE AND FULLY OPERATIONAL SYSTEM. COORDINATE WORK TO BE PERFORMED OR INSTALLED BY OTHERS AFFECTING THE ELECTRICAL WORK AND FURNISH AND INSTALL ALL NECESSARY STEEL SHAPES, BLOCKING, ANCHORS, SLEEVES, HANGERS, ETC. FOR ATTACHING OR CONNECTING ELECTRICAL WORK TO RELATED WORK OF OTHER TRADES. ALL ITEMS NOT SPECIFICALLY MENTIONED HEREIN OR NOT INDICATED IN THE DRAWINGS, WHICH ARE NECESSARY TO MAKE A COMPLETE WORKING INSTALLATION, SHALL BE PROVIDED WITHOUT ADDITIONAL EXPENSE TO THE OWNER. DRAWINGS AND SPECIFICATIONS DO NOT UNDERTAKE TO INDICATE EVERY ITEM OF MATERIAL, EQUIPMENT, OR LABOR REQUIRED TO PRODUCE A COMPLETE AND PROPERLY OPERATING INSTALLATION.
5. PERMITS: OBTAIN ALL NECESSARY PERMITS, LICENSES, AND INSPECTIONS AS REQUIRED BY ANY OF THE FOREGOING AUTHORITIES AND PAY FOR ALL OTHER COSTS IN CONNECTION WITH THE WORK.
6. INSPECTIONS: CONTRACTOR SHALL NOT CONCEAL ANY WORK UNTIL INSPECTED AND APPROVED BY ELECTRICAL INSPECTOR AND/OR ARCHITECT/ENGINEER.
7. REGULATIONS: ALL ELECTRICAL WORK SHALL BE PERFORMED IN STRICT ACCORDANCE WITH THE LATEST ADOPTED NATIONAL ELECTRICAL CODE (NEC) AND ALL OTHER APPLICABLE FEDERAL, STATE, AND LOCAL BUILDING CODES, RULES, REGULATIONS AND AUTHORITIES HAVING JURISDICTION. WORKMANSHIP: ALL WORK SHALL BE INSTALLED IN A NEAT AND WORKMANLIKE MANNER IN ACCORDANCE WITH APPLICABLE NECA STANDARDS SUBJECT TO THE APPROVAL OF THE OWNER OR OWNER'S AUTHORIZED REPRESENTATIVE. RACEWAY, FIXTURES, AND WIRING DEVICES SHALL BE PROPERLY ALIGNED, LEVELED, PLUMBED AND SUPPORTED. RACEWAY SHALL BE GROUPED AND INSTALLED IN RUNS WHICH ARE PARALLEL AND PERPENDICULAR WITH BUILDING LINES.
8. COORDINATION: PRIOR TO COMMENCEMENT OF WORK, EXAMINE ALL CONSTRUCTION DRAWINGS AND SPECIFICATIONS AND COORDINATE WITH ALL OTHER TRADES INCLUDING GENERAL CONTRACTOR, MECHANICAL CONTRACTOR, LOW VOLTAGE CONTRACTOR, AND SECURITY CONTRACTOR IN ORDER TO BECOME FAMILIAR WITH ALL ASPECTS OF THE DESIGN AFFECTING THE ELECTRICAL WORK AND TO CONFIRM SITE SPECIFIC INSTALLATION REQUIREMENTS. REFER TO ARCHITECTURAL DRAWINGS AND EQUIPMENT CUT SHEETS FOR EQUIPMENT POWER/CONTROL REQUIREMENTS, CONNECTIONS, WIRING DEVICE TYPE, MOUNTING HEIGHTS, MEANS OF ATTACHMENT, AND LOCATIONS OF ALL NEW EQUIPMENT AND ELECTRICAL DEVICES. FIELD VERIFY EXACT NAMEPLATE DATA ON ALL EQUIPMENT FURNISHED UNDER OTHER DIVISIONS AND/OR BY THE OWNER PRIOR TO THE INSTALLATION OF ELECTRICAL WORK AND MAKE ANY ADJUSTMENTS TO OUTLETS, CONDUITS, WIRE, AND/OR CIRCUIT BREAKER/FUSE RATINGS AS REQUIRED TO MATCH EQUIPMENT ACTUALLY FURNISHED.
9. EQUIPMENT AND DEVICE LOCATIONS: LOCATIONS ON THE ELECTRICAL PLANS ARE APPROXIMATE. EXACT LOCATIONS SHALL BE DETERMINED FROM ARCHITECTURAL PLANS, SECTIONS, AND ELEVATIONS. FINAL LOCATION OF EQUIPMENT AND DEVICES TO BE COORDINATED WITH ARCHITECT, OWNER, AND/OR OWNER'S REPRESENTATIVE. VERIFY STUB-UP LOCATION FOR ALL UNDER SLAB CONDUITS PRIOR TO ROUGH-IN.
10. UTILITIES: UTILITY COORDINATION INFORMATION SHOWN ON THE DRAWINGS SHALL BE CONSIDERED PRELIMINARY. COORDINATE WITH LOCAL POWER COMPANY AND TELCO (TELEPHONE/CABLE/INTERNET) PROVIDERS FOR SERVICE REQUIREMENTS AND VERIFY FINAL POINT OF CONNECTION PRIOR TO MOBILIZATION IN THE FIELD. NOTIFY UTILITIES OF COMMENCEMENT OF WORK AND MAKE ALL ARRANGEMENTS FOR TEMPORARY AND PERMANENT SERVICES. PROVIDE ALL EQUIPMENT, MATERIAL, AND LABOR TO MEET UTILITY REQUIREMENTS. INCLUDE ALL ASSOCIATED COSTS TO SET-UP AND COORDINATE TEMPORARY AND PERMANENT ELECTRIC AND TELCO SERVICES IN BID. ALL MATERIALS MUST BE APPROVED BY THE LOCAL UTILITY. IF REQUIRED, THE ELECTRICAL CONTRACTOR SHALL PROVIDE CONDUIT SYSTEMS FOR UTILITY MEDIUM VOLTAGE FROM UTILITY PRIMARY TO POINT OF INTERCEPTION AT EDGE OF PROPERTY LINE.
11. TEMPORARY POWER: PROVIDE TEMPORARY SERVICE FOR LIGHTING, POWER EQUIPMENT (DRILLS, SAWS, ETC.), AND CONTRACTOR MOBILIZED WORK TRAILERS. VERIFY TEMPORARY SERVICE REQUIREMENTS WITH GENERAL CONTRACTOR. TEMPORARY LIGHTING AND POWER SHALL MEET OSHA REQUIREMENTS AND LOCAL CODE.
12. INTERRUPTION OF SERVICE: COORDINATE ALL WORK REQUIRING INTERRUPTION OF SERVICE (POWER, SECURITY, DATA, FIRE ALARM, ETC) WITH ALL AFFECTED PARTIES, INCLUDING BUT NOT LIMITED TO GENERAL CONTRACTOR, BUILDING OWNER AND/OR LANDLORD, TENANT(S), AND OWNER AND/OR OWNER'S REPRESENTATIVE AND OBTAIN WRITTEN PERMISSION FROM SAID PARTIES AT LEAST 48 HOURS PRIOR TO SHUT DOWN. PROVIDE NOTICE TO ALL OTHER TRADES OF ALL SCHEDULED INTERRUPTIONS. ALL OUTAGES OR INTERRUPTIONS SHALL BE KEPT TO MINIMUM DURATION. PROVIDE TEMPORARY SERVICE DURING OUTAGE WHEN REQUIRED BY AFFECTED PARTIES. CONTRACTOR SHALL BE RESPONSIBLE TO PROVIDE PERSONNEL FOR FIRE AND SECURITY WATCH DURING OUTAGES TO FIRE AND SECURITY SYSTEMS.
13. PRODUCTS: ALL ELECTRICAL MATERIALS SHALL BE NEW EXCEPT WHERE SPECIFICALLY NOTED AS EXISTING TO BE REUSED. MATERIAL AND METHODS OF INSTALLATION SHALL CONFORM TO THE STANDARDS OF UNDERWRITERS LABORATORIES, INC. (UL), ANSI, NFPA, ADA, AND ALL OTHER APPLICABLE LOCAL ORDINANCES. DEFECTIVE EQUIPMENT AND/OR EQUIPMENT DAMAGED DURING INSTALLATION AND/OR TESTING SHALL BE REPLACED OR REPAIRED IN A MANNER MEETING THE APPROVAL OF THE ARCHITECT AND THE ENGINEER. PROPOSED EQUIPMENT SHALL BE NRTL LISTED, LABELED, OR APPROVED.
14. SHOP DRAWINGS AND SUBMITTALS: SUBMIT MANUFACTURER'S STANDARD PRODUCT INFORMATION, PERFORMANCE SPECIFICATIONS, ELECTRICAL RATINGS, PHYSICAL DIMENSIONS, AND OTHER INFORMATION NECESSARY FOR ENGINEER TO ENSURE COMPLIANCE WITH SPECIFICATIONS. SHOP DRAWINGS SHALL BE SUBMITTED FOR APPROVAL PRIOR TO ORDERING AND INSTALLING ANY EQUIPMENT. SUBMITTALS AND SHOP DRAWINGS SHALL CLEARLY INDICATE ITEMS TO BE REVIEWED BY HIGHLIGHTING, AND ITEMS NOT TO BE REVIEWED SHALL BE CROSSED OUT. SUBMITTALS WITHOUT HIGHLIGHTING AND CROSSED OUT ITEMS SHALL NOT BE REVIEWED. ALL SUBMITTALS MUST BE RECEIVED BY THE ENGINEER WITHIN 30 DAYS OF CONTRACT AWARD TO THE GENERAL CONTRACTOR; NO EXCEPTIONS. EQUIPMENT ORDERED OR INSTALLED WITHOUT A FAVORABLY REVIEWED SUBMITTAL IS DONE AT THE CONTRACTOR'S OWN RISK.
15. VALUE ENGINEERING SUBMITTALS: VALUE ENGINEERING SUBMITTALS SHALL BE LABELED AS SUCH AND INDICATE A 'DEDUCT' OR CREDIT BACK TO THE OWNER. VE SUBMITTALS NOT CLEARLY LABELED OR NOT INCLUDING A DEDUCT SHALL BE REJECTED.
16. SUBSTITUTION AND ALTERATIONS: THERE SHALL BE NO DEVIATION FROM THE REQUIREMENTS HEREIN WITHOUT THE WRITTEN APPROVAL OF THE ENGINEER. CONTRACTOR SHALL ASSUME RESPONSIBILITY FOR ALL COSTS INCURRED RESULTING FROM SUBSTITUTION OF EQUIPMENT AS WELL AS THE PERFORMANCE AND SPACE REQUIREMENTS OF SUCH EQUIPMENT.
    SUBSTITUTIONS AND ALTERATIONS OF OTHER DISCIPLINE'S EQUIPMENT: SUBSTITUTED AND ALTERED EQUIPMENT BY OTHER DISCIPLINES SHALL INCLUDE ALL MATERIAL AND LABOR COSTS FOR ELECTRICAL CONTRACTOR TO PROVIDE COMPLETE AND FULLY FUNCTIONAL SYSTEMS TO ACCOMMODATE THESE SUBSTITUTED AND ALTERED EQUIPMENT. THESE ADDITIONAL ELECTRICAL COSTS MUST BE ABSORBED BY THE OTHER DISCIPLINE'S CONTRACTOR IN ORDER FOR THE SUBSTITUTED OR ALTERED GEAR TO BE ACCEPTED.
17. FAULT CURRENT PROTECTION: ALL EQUIPMENT SHORT CIRCUIT CURRENT RATINGS (SCCR) AND OVERCURRENT PROTECTIVE DEVICE AMPERE INTERRUPTING CAPACITY (AIC) RATINGS SHALL BE GREATER THAN THE AVAILABLE FAULT CURRENT AT EACH RESPECTIVE PIECE OF EQUIPMENT. COORDINATE EQUIPMENT SCCR AND OVERCURRENT PROTECTIVE DEVICE AIC RATINGS WITH POWER COMPANY. OBTAIN THE AVAILABLE FAULT CURRENT AT TRANSFORMER SECONDARY FROM THE POWER COMPANY AND PROVIDE PROPOSED EQUIPMENT SCCR AND OVERCURRENT PROTECTIVE DEVICE AIC RATINGS FOR ENGINEER APPROVAL. OVERCURRENT PROTECTIVE DEVICES AIC RATINGS SHALL BE FULLY RATED WITH A MINIMUM 10% MARGIN BETWEEN THE CALCULATED FAULT LEVEL AND THE SPECIFIED SHORT CIRCUIT RATING OF THE EQUIPMENT UNO ON PLANS.
18. VOLTAGE DROP: WIRE SIZES SPECIFIED IN THESE PLANS ARE MINIMUM WIRE SIZES. THE ELECTRICAL CONTRACTOR IS RESPONSIBLE FOR INCREASING WIRE SIZES BASED ON ACTUAL CIRCUIT LENGTH TO MAINTAIN VOLTAGE DROP AT A MAXIMUM OF 3% FOR BRANCH CIRCUITS AND 2% FOR FEEDERS. THE CUMULATIVE VOLTAGE DROP FROM THE SOURCE TO THE END DEVICE SHALL NOT EXCEED 5% OF NOMINAL SYSTEM VOLTAGE.
19. WIRING: ALL CONDUCTORS CARRYING 50 VOLTS OR MORE SHALL BE MINIMUM #12 AWG, CU, UNO. PROVIDE DUAL RATED TYPE THHN-THWN FOR ABOVE GROUND AND TYPE THWN OR XHHW FOR BELOW GROUND, COORDINATE INSULATION TYPES WITH ENVIRONMENTAL CONDITIONS, NEC REQUIREMENTS, AND CONDUIT FILL REQUIREMENTS. CONDUCTORS #12 AND #10 SHALL BE SOLID, CONDUCTORS #8 AND LARGER SHALL BE STRANDED. ALL CONDUCTOR SIZES ARE BASED ON COPPER WITH 60°C INSULATION FOR CIRCUITS RATED 100A OR LESS AND 75°C FOR CIRCUITS RATED MORE THAN 100A
22. LOW VOLTAGE WIRING: LOW VOLTAGE WIRING FOR SPECIAL SYSTEMS IS PERMITTED TO BE FREE-WIRED ONLY ABOVE ACCESSIBLE CEILINGS AND BELOW RAISED FLOOR SYSTEMS, UNO. FREE-WIRED CABLE SHALL BE UL LISTED, PLENUM RATED. LOW VOLTAGE WIRING IN OPEN CEILINGS, HARD CEILINGS, WALLS, PASSING THROUGH ADJACENT TENANT SPACES, OR ROUTED UNDERGROUND OR BELOW SLAB SHALL BE INSTALLED IN CONDUIT. LOW VOLTAGE WIRING IS NOT SHOWN ON PLANS, UNLESS SPECIFICALLY CALLED OUT.
23. COLOR CODING: FOR EXISTING WIRING SYSTEMS, COLOR CODING SHALL FOLLOW EXISTING SITE REQUIREMENTS. FOR NEW INSTALLATIONS OR WHERE EXISTING INSTALLATIONS DO NOT HAVE A COLOR CODING CONVENTION, THE FOLLOWING SYSTEMS OF COLOR CODING SHALL BE STRICTLY ADHERED TO AND FOLLOWED THROUGHOUT:

CONDUCTOR	480Y/277V, 3-PH	208Y/120V, 3-PH	240D/120V, 3-PH	240/120V, 1-PH
PHASE A:	BROWN	BLACK	BLACK	BLACK
PHASE B:	ORANGE	RED	ORANGE	RED
PHASE C:	YELLOW	BLUE	BLUE	-
NEUTRAL:	GRAY	WHITE	WHITE	WHITE
EQUIPMENT GROUND:	GREEN	GREEN	GREEN	GREEN
ISOLATED GROUND:	---	GREEN/YELLOW	GREEN/YELLOW	GREEN/YELLOW

24. SHARED CIRCUIT NEUTRALS: SHARED CIRCUIT NEUTRALS SHALL NOT BE USED UNLESS INDICATED OTHERWISE ON PANEL SCHEDULE. WHERE USED, CIRCUIT BREAKER HANDLE TIES SHALL BE PROVIDED TO DISCONNECT POWER TO EACH PHASE CONDUCTOR OF THE SHARED NEUTRAL CIRCUIT.
25. GROUNDING: ALL CIRCUITS SHALL BE PROVIDED WITH AN INSULATED GREEN COPPER EQUIPMENT GROUND CONDUCTOR SIZED PER NEC. THE EQUIPMENT GROUND CONDUCTOR SHALL BE INCREASED IN SIZE BY EQUAL PROPORTION TO THE PHASE CONDUCTORS WHENEVER THE PHASE CONDUCTORS HAVE BEEN UPSIZED TO MAINTAIN ACCEPTABLE VOLTAGE DROP LEVELS. EQUIPMENT GROUNDS SHALL BE BONDED TO ALL EQUIPMENT AND DEVICES. USE OF METALLIC CONDUIT SHALL NOT TAKE THE PLACE OF AN EQUIPMENT GROUND CONDUCTOR.
26. CONDUIT: ALL WIRING SHALL BE INSTALLED IN CONDUIT, MINIMUM 1/2" FOR INDOOR AND 3/4" FOR OUTDOOR AND UNDER SLAB. EMT IS ACCEPTABLE WITH COMPRESSION FITTINGS ONLY. ALL HOMERUNS SHALL BE HARD PIPED. MC IS ACCEPTABLE FOR FIXTURE WHIPS ONLY. ALL CONDUIT AND WIRING SHALL BE CONCEALED IN FLOORS, WALLS, AND/OR CEILINGS UNLESS SPECIFICALLY NOTED OTHERWISE. CHANNEL EXISTING WALLS WHERE REQUIRED. WHERE CONDUITS ARE UNABLE TO BE CONCEALED, HARD PIPED CONDUIT SHALL BE USED AND PAINTED TO MATCH ADJOINING SURFACE.
27. UNDERGROUND CONDUITS: MINIMUM BURIAL DEPTH SHALL BE 24" TO TOP OF CONDUIT. PROVIDE DETECTABLE WARNING TAPE WHERE REQUIRED BY AHJ OR CODE.
28. ROUTING: FOR CLARITY, CONDUIT ROUTING SHOWN IS SYMBOLIC AND DIAGRAMMATIC. INSTALL CONDUIT TO FIT ACTUAL FIELD CONDITIONS.
29. OPEN CEILINGS: IN AREAS WITHOUT CEILINGS OR WHERE ANY CONDUITS, CONDUCTORS, FEEDERS, OR LOW VOLTAGE CABLING IS VISIBLE, ALL WIRING SHALL BE HARD PIPED IN CONDUIT. BX, AC, AND MC CABLE OR FLEX CONDUIT ARE NOT PERMITTED. CONDUITS SHALL BE ROUTED TIGHT TO DECK EITHER PARALLEL OR PERPENDICULAR TO BUILDING LINES, GROUPED ALONG STRUCTURAL MEMBERS, AND DROP AT POINT OF CONNECTION. MAINTAIN 1-1/2" CLEARANCE FROM ROOF DECK PER NEC 300.4(E). WHERE EXPOSED TO VIEW, ALL MATERIALS (CONDUIT, JUNCTION BOXES, ETC.) SHALL BE INSTALLED IN AN ORDERLY FASHION AND SHALL BE CLEAN, FREE FROM ALL VISIBLE MARKINGS, AND PAINTED TO MATCH ADJOINING SURFACE. JUNCTION BOXES SHALL HAVE CIRCUIT NUMBERS WRITTEN ON THE INSIDE OF THE JUNCTION BOX COVER.
30. PENETRATIONS: CONTRACTOR SHALL INSPECT AREA OF WORK AND PERFORM GROUND PENETRATING RADAR (GPR) SCAN OR X-RAY ALL PROPOSED PENETRATIONS PRIOR TO WORK TO DETERMINE EXACT LOCATIONS OF STRUCTURAL REINFORCEMENT OR EMBEDDED SYSTEMS. COORDINATE FLOOR AND WALL PENETRATIONS WITH STRUCTURAL ENGINEER. ALL PENETRATIONS SHALL BE SEALED BY APPROVED MEANS TO PREVENT ENERGY LOSS AND MOISTURE AND RODENT INTRUSION.
31. FIRE-RATED PENETRATIONS: ALL PENETRATIONS THROUGH FIRE-RATED SLABS AND/OR PARTITIONS SHALL BE SEALED WITH A UL LISTED FIRE-RATED ASSEMBLY OF EQUAL OR GREATER RATING THAN THAT OF THE EXISTING SLAB OR PARTITION.
32. TRENCHING: FIELD VERIFY UNDERGROUND UTILITIES PRIOR TO TRENCHING. ALL PROPOSED EXCAVATION IN THE VICINITY OF EXISTING UTILITIES, PIPING SYSTEMS, OR SIMILAR SHALL BE HAND EXCAVATED. HAND EXCAVATE IN THE VICINITY OF EXISTING TREES WHERE TRENCHING MAY ENCOUNTER TREE ROOT SYSTEM.
33. SLEEVES: SLEEVES AND SLEEVE SEALS SHALL BE PROVIDED AT PENETRATIONS OF WALL ASSEMBLIES.
34. SUPPORTS: ALL CONDUIT AND CABLING SHALL BE PROPERLY SUPPORTED AS REQUIRED BY CODE.
35. REPAIRS: THE CONTRACTOR SHALL REPAIR ALL WALL, CEILING, FLOOR, OR ROOF OPENINGS WHICH ARE CREATED BY DEMOLITION OR PENETRATION. THE REPAIRS SHALL BE WITH MATERIAL AND FINISHES TO MATCH EXISTING ADJACENT UNDISTURBED FINISHED SURFACES.
36. IDENTIFICATION: ALL ELECTRICAL DISTRIBUTION EQUIPMENT, TRANSFORMERS, PANELBOARDS, AND OTHER ENCLOSED EQUIPMENT SHALL BE IDENTIFIED AS INDICATED IN THE CONTRACT DOCUMENTS. SAID IDENTIFICATION SHALL CONSIST OF PERMANENTLY ATTACHED ENGRAVED LAMINATED PLASTIC NAMEPLATES. EACH BRANCH CIRCUIT OVERCURRENT PROTECTION DEVICE SHALL BE IDENTIFIED BY CIRCUIT NUMBER AND SCHEDULED INSIDE PANEL DOOR WITH A TYPEWRITTEN CIRCUIT DIRECTORY. EACH BRANCH CIRCUIT SPLICE OR TERMINATION SHALL BE IDENTIFIED BY PANEL AND CIRCUIT DESIGNATION SHOWN ON THE JUNCTION OR OUTLET BOX, OR UPON INDIVIDUAL WIRES IN CASES WHERE MORE THAN ONE OF EACH PHASE CONDUCTOR OCCUR. RECEPTACLES AND SWITCH COVER PLATES SHALL BE LABELED WITH PANEL AND CIRCUIT DESIGNATION USING TYPEWRITTEN CHARACTERS OF CONTRASTING COLOR (BLACK OR WHITE) ON CLEAR ADHESIVE BACKED LABELS OR FACTORY ENGRAVED COVER PLATES.
37. PANEL CLEARANCE: MAINTAIN ALL WORKING SPACE AND DEDICATED EQUIPMENT SPACE CLEARANCES AS REQUIRED BY ARTICLE 110 OF THE NEC. GENERAL CONTRACTOR SHALL COORDINATE BETWEEN TRADES SO THAT NO FOREIGN SYSTEMS ARE LOCATED IN THE DEDICATED EQUIPMENT SPACE. IN THE EVENT THAT FOREIGN SYSTEMS ARE INSTALLED ABOVE A PANEL'S DEDICATED EQUIPMENT SPACE, THE GENERAL CONTRACTOR SHALL ABSORB THE COST TO RELOCATE THE FOREIGN SYSTEMS.
38. WIRING DEVICES: WIRING DEVICES AND COVER PLATES SHALL BE DECORA STYLE OF COLORS SELECTED BY THE ARCHITECT OR INTERIOR DESIGNER. GANG ADJACENT DEVICES WITH A SINGLE ONE-PIECE COVER PLATE, UNO. FOR REMODELS, ALL DEVICES AND COVER PLATES WITHIN THE CONTRACT AREA SHALL BE REPLACED WITH NEW DECORA STYLE DEVICES AND COVER PLATES, UNO.
39. CLEANING: UPON COMPLETION OF WORK, THE CONTRACTOR SHALL THOROUGHLY CLEAN THE CONTRACT AREA AND ALL OTHER AREAS USED FOR STORAGE, STAGING, ETC. ALL EQUIPMENT AND DEVICES SHALL BE CLEANED AND POLISHED IN ACCORDANCE WITH MANUFACTURER'S RECOMMENDATIONS. SOAP AND WATER CLEANING OR OTHER METHODS THAT LEAVE A FILM SHALL BE CORRECTED UPON REQUEST BY THE ENGINEER OR ARCHITECT.
40. TESTING: THE CONTRACTOR SHALL TEST ALL EQUIPMENT INSTALLED UNDER THIS CONTRACT AND DEMONSTRATE TO THE OWNER ITS PROPER OPERATION. AT THE TIME OF FINAL INSPECTION AND TESTS, ALL CONNECTIONS AT PANELBOARDS, CONTROL PANELS, DEVICES, AND EQUIPMENT AND ALL SPLICES MUST BE COMPLETED. EACH BRANCH CIRCUIT AND ITS RESPECTIVE CONNECTED EQUIPMENT MUST TEST FREE OF SHORT CIRCUITS.
41. TRAINING: OWNER AND/OR OWNER'S REPRESENTATIVE SHALL BE TRAINED ON THE USE OF ANY NEW ELECTRICAL EQUIPMENT AND LIGHTING CONTROLS PRIOR TO FINAL ACCEPTANCE.
42. FINAL ACCEPTANCE: AT THE END OF CONSTRUCTION, A FINAL WALK-THROUGH SHALL BE PERFORMED. ALL DEFICIENCIES IDENTIFIED DURING FINAL INSPECTION SHALL BE CORRECTED.
43. CERTIFICATES OF APPROVAL: ALL CERTIFICATES OF APPROVAL SHALL BE IN DUPLICATE, DELIVERED TO THE ARCHITECT, AND BECOME THE PROPERTY OF THE OWNER.
44. PROJECT RECORD DOCUMENTS: THE ELECTRICAL CONTRACTOR SHALL MAINTAIN AT THE SITE, FOR THE OWNER, ONE COPY OF ALL DRAWINGS, ADDENDA, APPROVED SHOP DRAWINGS, REVISIONS AND OTHER MODIFICATIONS IN GOOD ORDER AND MARKED TO RECORD ALL CHANGES MADE DURING CONSTRUCTION. THE SET OF DRAWINGS AND OTHER INFORMATION SHALL BE DELIVERED TO THE OWNER WITHIN 30 DAYS AFTER THE DATE OF SYSTEM ACCEPTANCE AND ONE COPY GIVEN TO THE ENGINEER UPON COMPLETION OF WORK. DRAWINGS SHALL INCLUDE AT A MINIMUM:
    A. SINGLE-LINE DIAGRAM OF THE BUILDING ELECTRICAL DISTRIBUTION SYSTEM AND
    B. FLOOR PLANS INDICATING LOCATION AND AREA SERVED FOR ALL DISTRIBUTION.
45. OPERATIONS AND MAINTENANCE (O&M) MANUALS: PROVIDE TWO COPIES OF OPERATIONS AND MAINTENANCE MANUALS TO THE BUILDING OWNER IN HARD COPY AND ELECTRONIC FORMAT. HARD COPIES SHALL BE COMPILED AND ORGANIZED IN A BINDER. THE MANUALS SHALL INCLUDE, AT A MINIMUM, THE FOLLOWING:
    A. SUBMITTAL DATA STATING EQUIPMENT RATING AND SELECTED OPTIONS FOR EACH PIECE OF EQUIPMENT REQUIRING MAINTENANCE.
    B. OPERATING AND MAINTENANCE MANUALS FOR EACH PIECE OF EQUIPMENT REQUIRING MAINTENANCE. REQUIRED ROUTINE MAINTENANCE ACTIONS SHALL BE CLEARLY IDENTIFIED.
    C. NAMES AND ADDRESSES OF AT LEAST ONE QUALIFIED SERVICE AGENCY.
    D. WARRANTY INFORMATION.
46. WARRANTY: THE ENTIRE ELECTRICAL SYSTEM INSTALLED UNDER THIS CONTRACT SHALL BE HANDED OVER IN PROPER WORKING ORDER. ANY WORK OR MATERIALS WHICH DEVELOP DEFECTS, EXCEPT FROM ORDINARY WEAR AND TEAR, WITHIN ONE YEAR FROM THE DATE OF FINAL ACCEPTANCE SHALL BE REPLACED WITHOUT CHARGE. IF MATERIALS HAVE A STANDARD WARRANTY GREATER THAN ONE YEAR, THE MANUFACTURER'S STANDARD WARRANTY SHALL APPLY. BENEFICIAL USE SHALL NOT BE CONSTRUED AS FINAL ACCEPTANCE. THE ELECTRICAL CONTRACTOR SHALL, DURING THE ONE YEAR GUARANTEE PERIOD, BE RESPONSIBLE FOR THE PROPER REPAIR AND ADJUSTMENTS OF ALL ELECTRICAL SYSTEMS AND EQUIPMENT, APPARATUS, DEVICES, ETC. INSTALLED BY HIM, AND DO ALL WORK NECESSARY TO ENSURE

PRAXIS3

100 Peachtree St NW
Suite 1450
Atlanta, GA 30303

404-875-4500 tel
www.praxis3.com

GEORGIA REGISTERED No. 041568 PROFESSIONAL ENGINEER RAHN ONEAL WILLIAMS

Copyright (c) 2024 Praxis3, LLC

All reports, plans, specifications, computer files, field data, notes and other documents and instruments prepared by Praxis3 shall retain all common law, statutory and other reserved rights, including copyright thereto.

This drawing may not be reproduced in whole or in part without written permission of Praxis3. It is to be returned upon request. Scales as stated are valid on the original drawings.

Rev	Date	Comments
	07/02/2026	PERMIT SET

Client:

FIFTH THIRD BANK

Project Number: 26032
Project Name:

FIFTH THIRD BANK WATSON 1,900 SF

2711 WATSON BOULEVARD
WARNER ROBBINS, GA 31093

Key Plan:

Sheet Title:

ELECTRICAL GENERAL NOTES

Sheet Number:

E-002

6/30/2026 2:31:56 PM

PART 1 - GENERAL

1.01 RELATED DOCUMENTS
A. The general provisions of the contract including General and Special Conditions and General Requirements shall apply to all work under this Section.

1.02 REQUIREMENTS OF REGULATORY AGENCIES AND STANDARDS
A. Equipment, fixtures, material and installation shall conform to the requirements of the local Building Department, the serving utility companies, the National Electrical Code, National Electrical Safety Code, Life Safety Code, Occupational Safety and Health Act, and applicable national, state and local codes, ordinances and regulations.
B. All equipment shall be equal to or exceed the minimum requirements of NEMA, IEEE, and UL.
C. Should any change in Drawings or Specifications be required to comply with governmental regulations, the Contractor shall notify Architect/Engineer prior to execution of the Work. The work shall be carried out according to the requirements of such code in accordance with the instruction of the Architect/Engineer and at no additional cost to the Owner.
D. The provisions of Standards, Codes, Laws, Ordinances, etc., shall be considered minimum requirements. In case of conflict between their published requirements, the Owner's Representative shall determine which is to be followed and his decision shall be binding. Specific requirements of this specification or the drawings, which exceed the published requirements, shall take precedence over them.

1.03 FEES
A. All local fees, permits, and services of inspection authorities shall be obtained and paid for by the Contractor. The Contractor shall
B. cooperate fully with local companies with respect to their services. Contractor shall include in his bid any costs to be incurred
C. relative to power service (primary and/or secondary) and telephone service.

1.04 SCOPE OF WORK
A. This division of the specifications covers the electrical systems of the project. It includes work performed by the electrical trades as well as trades not normally considered as electrical trades.
B. Provide all incidentals, equipment, appliances, services, hoisting, scaffolding, supports, tools, supervision, labor consumable items, fees, licenses, etc., necessary to provide complete systems. Perform start-up and checkout on each item and system to provide fully operable systems.
C. Examine and compare the Electrical Drawings with these specifications, and report any discrepancies between them to the Architect/Engineer and obtain from him written instructions for changes necessary in the work. At time of bid the most stringent requirements must be included in the bid.
D. Examine and compare the Electrical Drawings and Specifications with the Drawings and Specifications of other trades, and report any discrepancies between them to the Architect/Engineer and obtain from him written instructions for changes necessary in the work. At time of bid, the most stringent requirements must be included in said bid.
E. Install and coordinate the electrical work in cooperation with other trades installing interrelated work. Before installation, make proper provisions to avoid interferences in a manner approved by the Architect/Engineer. All changes required in the work of the Contractor, caused by his neglect to do so, shall be made by him at his own expense.
F. It is the intent of the Drawings and Specifications to provide a complete workable system ready for the Owner's operation. Any item not specifically shown on the Drawings or called for in the Specifications, but normally required to conform with the intent, are to be considered a part of the Contract.
G. All materials furnished by the Contractor shall be new and unused (temporary lighting and power products are excluded) and free from defects. All materials used shall bear the Underwriter's Laboratory, Inc. label provided a standard has been established for the material in question.
H. Except for conduit, conduit fittings, outlet boxes, wire and cable, all items of equipment or material shall be the product of one manufacturer throughout the entire project. Multiple manufacturers will not be permitted.

1.05 REFERENCES
A. Utilize the following abbreviations and definitions for discernment within the Drawings and Specifications.
1. Abbreviations
- NEC National Electrical Code.
- OSHA Occupational Safety and Health Act.
- ANSI American National Standards Institute.
- NFPA National Fire Protection Association.
- ASA American Standards Association.
- IEEE Institute of Electrical and Electronics Engineers.
- NEMA National Electrical Manufacturers Association.
- UL Underwriters' Laboratories, Inc.
- IES Illuminating Engineering Society.
- ICEA Insulated Cable Engineers Association.
- ASTM American Society of Testing Materials.
- ETL Electrical Testing Laboratories, Inc.
- CBM Certified Ballast Manufacturers.
- EIA Electronic Industries Association.
- LED Light Emitting Diode.
- OEM Original Equipment Manufacturer.

1.06 DEFINITIONS
A. "PROVIDE" means to supply, purchase, transport, place, erect, connect, test, and turn over to Owner, complete and ready for regular operation, the particular Work referred to.
B. "INSTALL" means to join, unite, fasten, link, attach, set up, or otherwise connect together before testing and turning over to Owner, complete and ready for regular operation, the particular Work referred to.
C. "FURNISH" means to supply all materials, labor, equipment, testing apparatus, controls, tests, accessories, and all other items customarily required for the proper and complete application for the particular Work referred to.
D. "WIRING" means the inclusion of all raceways, fittings, conductors, connectors, tape, junction and outlet boxes, connections, splices, and all other items necessary and/or required in connection with such Work.
E. "CONDUIT" means the inclusion of all fittings, hangers, supports, sleeves, etc.
F. "AS DIRECTED" means as directed by the Architect/Engineer, or his representative.
G. "CONCEALED" means embedded in masonry or other construction, installed behind wall furring or within double partitions, or installed above hung ceilings.

1.07 COORDINATION OF THE WORK

A. Certain materials will be provided by other trades. Examine the Contract Documents to ascertain these requirements.
B. Carefully check space requirements with other trades and the physical confines of the area to insure that all material can be installed in the spaces allotted thereto including finished suspended ceilings and the spaces within the existing building. Make modifications thereto as required and approved.
C. Transmit to other trades all information required for work to be provided under their respective Sections in ample time for installation.
D. Wherever work interconnects with work of other trades, coordinate with other trades to insure that all trades have the information necessary so that they may properly install all the necessary connections and equipment. Identify all items of work that require access so that the ceiling trade will know where to install access doors and panels.
E. Coordinate, project and schedule work with other trades in accordance with the construction sequence.
F. The Drawings show only the general run of raceways and approximate location of outlets. Any significant changes in location of outlets, cabinets, etc., necessary in order to meet field conditions shall be brought to the immediate attention of the Architect/Engineer and receive his approval before such alterations are made. All such modifications shall be made without additional cost to the Owner.
G. Obtain from the Architect/Engineer in the field the location of such outlets or equipment not definitely located on the Drawings.
H. Circuit "tags" in the form of arrows are used where shown to indicate the home runs of raceways to electrical distribution points. These tags show the circuits in each home run and the panel designation. Show the actual circuits numbers on the finished record drawings and on panel directory card. Where circuiting is not indicated, Electrical Subcontractor must provide required circuiting in accordance with the loading indicated on the drawings and/or as directed.
I. Adjust location of conduits, panels, equipment, pull boxes, fixtures, etc. to accommodate the work to prevent interferences, both anticipated and encountered. Determine the exact route and location of each raceway prior to fabrication.
1. Right-of-Way:
a. Lines that pitch have the right-of-way over those that do not pitch. For example: steam, condensate, and plumbing drains normally have right-of-way. Lines whose elevations cannot be changed to have right-of-way over lines whose elevations can be changed.
b. Make offsets, transitions and changes in direction in raceways as required to maintain proper headroom in pitch of sloping lines whether or not indicated on the Drawings.
J. Wherever the work is of sufficient complexity, prepare additional Detail Drawings to scale similar to that of the bidding Drawings, prepared on tracing medium of the same size as Contract Drawings. With these layouts, coordinate the work with the work of other trades. Such detailed work to be clearly identified on the Drawings as to the area to which it applies. Submit for review Drawings clearly showing the work and its relation to the work of other trades before commencing shop fabrication or erection in the field.
K. Coordinate with the local Electric Utility Company and the local Telephone Company as to their requirements for service connections and provide all necessary materials, labor and testing.
L. Coordinate with contractors for work under other Divisions of this specification for all work necessary to accomplish this contractor's work.

1.08 EXAMINATION OF SITE
A. Prior to the submitting of bids, the Contractor shall visit the site of the job and shall familiarize himself with all conditions affecting the proposed installation and shall make provisions as to the cost thereof. Failure to comply with the intent of this paragraph will in no way relieve the contractor of performing all necessary work shown on the Drawings.

1.09 PROGRESS OF WORK
A. The Contractor shall order the progress of his work to conform to the progress of the work of other trades and shall complete the entire installation as soon as the conditions of the building will permit. Any cost resulting from the defective or ill-timed work performed under this section shall be borne by the Contractor.

1.10 DELIVERY, STORAGE, AND HANDLING
A. Ship and store all products and materials in a manner that will protect them from damage, weather and entry of debris. If items are damaged, do not install, but take immediate steps to obtain replacement or repair. Any such repairs shall be subject to review and acceptance of the Architect/Engineer.
B. Deliver materials in manufacturer's unopened container fully identified with manufacturer's name, trade name, type, class, grade, size and color.
C. Store materials suitably sheltered from the elements, but readily accessibly for inspection by the Architect/Engineer until installed. Store all items subject to moisture damage in dry, heated spaces.

1.11 EQUIPMENT ACCESSORIES
A. Provide supports, hangers and auxiliary structural members required for support of the work.
B. Furnish and set all sleeves for passage of raceways through structural, masonry and concrete walls of floors and elsewhere as will be required for the proper protection of each raceway passing through building surfaces.
C. Wall mounted equipment may be directly secured to wall by means of steel bolts. Maintain at least 1" air space between equipment and supporting wall. Groups or arrays of equipment may be mounted on adequately sized steel angles, channels, or bars. Prefabricated steel channels providing a high degree of mounting flexibility, such as those manufactured by Kindorf, Glob-Strutt and Unistrut, may be used for mounting arrays of equipment.

1.12 OPERATIONS AND MAINTENANCE MANUALS
General: Provide operations & maintenance (O&M) manuals in accordance with the Contract Documents.
1. Provide two (2) copies of each manual.
2. Manuals shall be 8-1/2 inches X 11 inches in hard cover 3-ring loose-leaf binders.
3. Manuals shall be complete and in Owner's hands prior to turning building over to Owner and at least 10 days prior to instruction to operating personnel.
B. Provide manufacturer's literature as regularly published by the respective manufacturers for proper preventative and comprehensive maintenance.
C. Provide O&M manuals including but not limited to the following.
1. Alphabetical list of all system components, with the name, address, and 24-hour phone number of the company responsible for servicing each item during the first year of operation.
Operating instructions for complete system including:
a. Normal starting, operating, and shut-down.
b. Emergency procedures for fire or failure of major equipment.
c. Summer and winter special procedures, if any.
d. Day and night special procedures, if any.
2. Maintenance instruction including:
a. Proper lubricants and lubricating instructions for each piece of equipment, and date when lubricated.
b. Necessary cleaning, replacement and/or adjustment schedule.
3. Manufacturer's data for each piece of equipment including:
a. Installation instructions.
b. Drawings and specifications.
c. Parts list, including recommended items to be stocked.
d. Complete wiring diagrams.
e. Marked or changed prints locating all concealed parts and all variations from the original system design.
f. Test and inspection certificates.
D. Refer to individual specification sections for additional O&M requirements.

1.13 RECORD DOCUMENTS
A. During construction, keep an accurate record of all deviations between the work as shown on Drawings and that which is actually installed. Keep this record set of prints at the job site for review by the Architect/Engineer.
B. Upon completion of the installation and acceptance by the owner, transfer all record drawing information to one neat and legible set of prints. Then deliver them to the Architect/Engineer for transmittal to the Owner.
C. Provide in each main electrical switchboard room a framed copy under glass of the appropriate Single Line Riser Diagram as reviewed by the electrical engineer. Media shall be a high quality presentation type paper. Blueprints or other media which fade shall not be used.

1.14 GUARANTEE
A. Guarantee all material and workmanship for a period of one (1) year from date of final acceptance by the Owner, except that where guarantees or warranties for longer terms are specified herein, such longer term to apply. Within 24 hours after notification, correct any deficiencies that occur during the guarantee period at no additional cost to the Owner, all to the satisfaction of the Owner and Architect/Engineer. Obtain similar guarantees from subcontractors, manufacturers, suppliers and subtrade specialists.

PART 2 - PRODUCTS

2.01 MATERIALS
A. Applicable equipment and materials shall be listed by Underwriters' Laboratories and Manufactured in accordance with ASME, NEMA, ANSI or IEEE standards, and as approved by local authorities having jurisdiction as mentioned in Division 1.
B. If products and materials are specified or indicated on the Drawings for a specific item or system, use those products or materials. If products and materials are not listed in either of the above, use first class products and materials, subject to approval of Shop Drawings where Shop Drawings are required or as approved in writing where Shop Drawings are not required.
C. All equipment capacities, etc. are listed for job site operating conditions. All equipment sensitive to altitudes or ambient temperatures to be derated and method of derating shown on Shop Drawings. Where operating conditions shown differ from the laboratory test conditions, the equipment to be derated and the method of derating shown on Shop Drawings.

2.02 SUBSTITUTION OF MATERIALS OR EQUIPMENT
A. All requests for substitution of materials or equipment shall be made in writing by the Contractor. The request must be in the Engineers office not less than 10 days prior to the bid date. Samples of proposed substitute materials or equipment shall be submitted to the Engineer for review whenever they are requested. Bids shall be based only upon the specified materials and equipment, or substitutes that have received written acceptance from the Engineer prior to the bid.
B. Wherever the words "for approval" or "approved" are used in regard to manufactured specialties, or wherever it is desired to substitute a different make or type of apparatus for that specified, submit all information pertinent to the adequacy and adaptability of the proposed apparatus, and secure Architect/Engineer's acceptance before apparatus is ordered.
C. Wherever quantities or a definite make and size of apparatus is specified, the make and size of apparatus which is proposed must conform substantially (in regard to the operating results) to that specified or implied. Same shall apply to important dimensions relating to operation of apparatus in coordination with the rest of the system, or to properly fitting it into available space conditions. Any substitution of equipment or apparatus shall include all necessary revisions, as required to complete the installation.
D. Acceptance of substitutions, for equipment specified herein, will not be given merely upon submission of manufacturer's names and will be given only after receipt of complete and satisfactory performance data covering the complete range of operating conditions in tabular and graphical form. Furnish complete and satisfactory information relative to equipment dimensions, weight, etc. Acceptance of all equipment specified or shown on the Drawings, or substitutions submitted for that specified or shown on the Drawings, will be granted if such equipment, in the opinion of the Architect/Engineer, conforms to the performance requirements, space conditions, weight requirements and quality requirements. Any additional construction and design costs incurred as a result of any accepted substitution shall be borne by the Contractor. The opinion and judgement of the Architect/Engineer shall be final, conclusive, and binding.

2.03 SHOP DRAWINGS
A. Prepare and submit detailed Shop Drawings for materials, systems, and equipment as listed herein, including locations and sizes of all openings in floor decks, walls, and floors.
B. The Work described in any Shop Drawing submission shall be carefully checked for all clearances (including those required for maintenance and servicing), field conditions, maintenance of architectural conditions, and proper coordination with all trades on the job. Each submitted Shop Drawing shall include a certification that all related job conditions have been checked and that no conflict exists.
C. All drawings shall be submitted sufficiently in advance of field requirements to allow ample time for checking and resubmittal as may be required. All submittals shall be complete and contain all required and detailed information.
D. Acceptance of any submitted data or Shop Drawings for material, equipment apparatus, devices, arrangements, and layout shall not relieve Contractor from responsibility of furnishing same of proper dimensions and weight, capacities, sizes, quantity, quality and installation details, to efficiently perform the requirements and intent of the Contract. Such acceptance shall not relieve Contractor from responsibility for errors, omissions, or inadequacies of any sort on submitted data or Shop Drawings.
E. Each Shop Drawing shall contain the following information.
1. Provide general information on each copy of the submittal.
a. Project title.
Reference to the applicable drawing and specification article.
Contractor and supplier identification, addresses and telephone numbers.
Submittal Date.
2. Certification that the contractor has reviewed the submittal.
3. Refer to individual specification sections for additional information requirements.
F. Shop Drawing submittals shall be provided for each specific material, system, or equipment as identified herein.
1. As a minimum, make submittals on the following items.
a. Raceways, conduit & wire
b. Wiring devices and plates
c. Switchboards
d. Transformers
e. Panelboards
f. Fuses
g. Disconnect switches
h. Motor control centers
i. Motor controllers, starters, and contactors
j. Lighting fixtures, lamps
k. Instrumentation, metering equipment
l. Special systems - fire alarm, security, CCTV, intercom, etc.
2. Refer to individual specification sections for additional submittal requirements.

PART 3 - EXECUTION

3.01 INSTALLATION
A. Follow manufacturer's instructions for installing, connecting, and adjusting all equipment. Provide one copy of such instructions to the Architect/Engineer before installing any equipment. Provide a copy of such instructions at the equipment during any work on the equipment. Provide all special supports, connections, wiring, accessories, etc.
B. Use mechanics skilled in their trade for all work.
C. Keep all items protected before and after installation. Clean up all debris.
D. Before commencing Work, examine all adjoining, underlying, etc., Work on which this Work is in any way dependent for perfect workmanship and report any condition which prevents performance of first class work. Become thoroughly familiar with actual existing conditions to which connections must be made or which must be changed or altered.

3.02 PREMIUM TIME WORK
A. The following Work shall be performed at night or weekend other than holiday weekends as directed and coordinated with the Owner.
1. All tie-in, cut-over and modifications to the existing electrical system and other existing system requiring tie-ins or modifications shall be arranged and scheduled with the Owner to be done at a time as to maintain continuity of the service and not interfere with normal building operations.

3.03 EXCAVATION, TRENCHING AND BACKFILL
A. Provide excavation for the Work. Excavate all material encountered, to the depths indicated on the drawings or required. Remove from the site, excavated materials not required or suitable for backfill. Provide grading, as may be necessary, to prevent surface water from flowing into trenches or other excavations. Remove any water accumulating therein. Provide sheeting and shoring as may be necessary for the protection of the Work and for the safety of personnel.
B. Provide trenches of widths necessary for the proper execution of the Work. Grade bottom of the trenches accurately to provide uniform bearing and support the Work on undisturbed soil at every point along its entire length. Except where rock is encountered, do not excavate below the depths indicated. Where rock excavations are required, excavate rock to a minimum overdepth of four (4") inches below the trench depths indicated on the Drawings or required. Backfill overdepths in the rock excavation and unauthorized overdepths with loose granular, moist earth, thoroughly machine tamped, to a compaction level of at least 95 percent to standard protector density or 75 percent relative density or as specified by the Architect. Where unstable soil that is incapable of properly supporting the Work, as determined by Architect/Engineer, is encountered in the bottom of the trench, remove soil to a depth required and backfill the trench to the proper grade with coarse sand, fine gravel, or other suitable material.
C. Excavate trenches for utilities to a depth that will provide the following minimum depths of cover from existing grade or from indicated finished grade, whichever is lower, unless otherwise specifically shown.
1. Primary electric service: four (4) feet (minimum)
2. Secondary electric service: two (2) feet (minimum)
3. Telephone service: two (2) feet (minimum)
D. Trenches shall not be placed within ten (10) feet of foundation or soil surfaces which must resist horizontal forces.
E. Do not backfill trenches until all required tests have been preformed and the installation observed by the Engineer. Comply with the requirements of other sections of these specifications. Backfill shall consist of non-expansive soil with limited porosity. Deposit in six (6") inch layers and thoroughly and carefully tamp until the Work has a cover of not less than one (1) foot. Backfill and tamp remainder of trench at twelve (12") inch intervals until complete. Uniformly grade the finished surface. Backfill and tamp with compaction at least equal to the surrounding area.

3.04 CUTTING, PATCHING AND REPAIRING
A. The work shall be carefully laid out in advance. Where cutting, channeling, chasing or drilling of floors, walls, partitions, ceilings or other surfaces is necessary for the proper installation, support or anchorage of raceway, outlets or other equipment, the work shall be carefully done. Any damage to the building, piping, equipment or defaced finish plaster, woodwork, metalwork, etc. shall be repaired by skilled mechanics of the trades involved at no additional cost to the Owner.
B. Where conduits, mounting channels, outlet, junction, or pull boxes are mounted on a painted surface, or a surface to be painted, they shall be painted to match the surface. Whenever support channels are cut, the bare metal shall be cold galvanized.

3.05 DEMOLITION AND CONTINUANCE OF EXISTING SERVICES
A. All existing electrical services not specifically indicated to be removed or altered shall remain as they presently exist.
B. Should any existing services interfere with new construction, the Contractor shall (after obtaining written approval from the Architect/Engineer) alter or reroute such existing equipment to facilitate new construction.
C. Under no circumstances shall existing services be terminated or altered unless deemed necessary by the Architect/Engineer or specified herein; also, prior to altering any existing situation, the Contractor shall notify the Owner in writing giving two (2) weeks advance notice of planned alteration.
D. It shall be solely the Contractor's responsibility to guarantee continuity of present facilities (with respect to damage or alteration due to new construction) and any unauthorized alteration to existing equipment shall be corrected by the Contractor to the Architect/Engineer's satisfaction at the Contractor's expense.

3.06 CLEANING UP
A. A Contractor shall take care to avoid accumulation of debris, boxes, crates, etc., resulting from the installation of his work. Contractor shall remove from the premises each day all debris, boxes, etc., and keep the premises clean.
B. Contractor shall clean up all fixtures and equipment at the completion of the project.
C. All switchboards, panelboards, wireways, trench ducts, cabinets and enclosures shall be thoroughly vacuumed clean prior to energizing equipment and at the completion of the project. Equipment shall be opened for observation by the Architect/Engineer as required.

3.07 WATERPROOFING
A. Avoid, if possible, the penetration of any waterproof membranes such as roofs, machine room floors, basement walls, and the like. If such penetration is necessary, perform it prior to the waterproofing and furnish all sleeves or pitch-pockets required. Advise the Architect/Engineer and obtain written permission before penetrating any waterproof membrane, even where such penetration is shown on the Drawings.
B. If Contractor penetrates any walls or surfaces after they have been waterproofed, he shall restore the waterproof integrity of that surface as directed by the Architect/Engineer at his own expense.

3.08 SUPPORTS
A. Support work in accordance with the best industry practice and the following.
B. Include supporting frames or racks extending from building structure for work indicated as being supported from walls where the walls are incapable of supporting the weight. In particular, provide such frames or racks in electric closets.
C. Include supporting frames or racks for equipment, intended for vertical surface mounting, which is required in a free standing position.
D. Supporting frames or racks shall be of standard angle, standard channel or specialty support system steel members. They shall be rigidly bolted or welded together and adequately braced to form a substantial structure. Racks shall be of ample size to assure a workmanlike arrangement of all equipment mounted on them.
E. Nothing, (including outlet, pull and junction boxes and fittings) shall depend on electric conduits, raceways, or cables for support, except that threaded hub type fittings having a gross volume not in excess of 100 cubic inches may be supported from heavy wall conduit, where the conduit is securely supported from the structure within five inches of the fitting on two opposite sides.
F. Nothing shall rest on, or depend for support on, suspended ceilings media (tiles, lath, plaster, as well as splines, runners, bars and the like in the plane of the ceiling).
G. Provide required supports and hangers for conduit, equipment, etc., so that loading will not exceed allowable loadings of structure.

3.09 FASTENINGS
A. Fasten electric work to building structure in accordance with the best industry practice and the following.
B. Floor or pad mounted equipment shall not be held in place solely by its own dead weight. Include anchor fastening in all cases.
C. For items which are shown as being ceiling mounted at locations where fastening to the building construction element above is not possible, provide suitable auxiliary channel or angle iron bridging, tying to the building structural elements.

3.10 TESTING EQUIPMENT AND MATERIALS
A. The Contractor shall provide all testing instruments, equipment and all materials, connections, labor, etc., required to perform tests.
B. Test all circuits, fixtures, equipment, and systems for proper operation and freedom from grounds, shorts and open circuits before acceptance is requested.
C. Measure voltage at panelboards and outlets after the building is fully occupied. Make final transformer tap adjustments based on these measurements.
D. Perform all tests required by local authorities, such as tests of life safety systems, in addition to tests specified herein.
E. Perform tests required by other specification sections.

PRAXIS3
100 Peachtree St NW
Suite 1450
Atlanta, GA 30303
404-875-4500 tel
www.praxis3.com

GEORGIA REGISTERED No. 041508 PROFESSIONAL ENGINEER RAHN ONEAL WILLIAMS

Copyright (c) 2024 Praxis3, LLC

All reports, plans, specifications, computer files, field data, notes and other documents and instruments prepared by Praxis3 shall retain all common law, statutory and other reserved rights, including copyright thereto.

This drawing may not be reproduced in whole or in part without written permission of Praxis3. It is to be returned upon request. Scales as stated are valid on the original drawings.

Rev	Date	Comments
	07/02/2026	PERMIT SET

Client:
FIFTH THIRD BANK

Project Number: 26032
Project Name:
FIFTH THIRD BANK WATSON
1,900 SF

2711 WATSON BOULEVARD
WARNER ROBBINS, GA 31093

Key Plan:

Sheet Title:
ELECTRICAL SPECIFICATIONS

Sheet Number:
E-003

6/30/2026 2:31:56 PM

COMcheck Software Version 4.1.5.5

Interior Lighting Compliance Certificate

Project Information

Energy Code: 2015 IECC
Project Title: FIFTH THIRD BANK WATSON
Project Type: New Construction

Construction Site:
2711 WATSON BOULEVARD
WARNER ROBBINS, GA 31093

Owner/Agent:

Designer/Contractor:

Additional Efficiency Package(s)

Credits: 1.0 Required 1.0 Proposed
Reduced Lighting Power, 1.0 credit

Allowed Interior Lighting Power

A Area Category	B Floor Area (ft2)	C Allowed Watts / ft2	D Allowed Watts (B X C)
1-Retail	2798	1.13	3173
		Total Allowed Watts =	3173

Proposed Interior Lighting Power

A Fixture ID : Description / Lamp / Wattage Per Lamp / Ballast	B Lamps/ Fixture	C # of Fixtures	D Fixture Watt.	E (C X D)
1-Retail				
LED 1: A/AE: Other:	1	29	15	435
LED 1 copy 1: B: Other:	1	40	3	120
LED 1 copy 1: C: Other:	1	9	52	468
LED 1 copy 2: F3: Other:	1	27	1	27
LED 1 copy 3: FEM: Other:	1	30	2	60
LED 1 copy 4: G: Other:	1	50	2	100
LED 1 copy 5: J/JE: Other:	1	19	8	152
LED 1 copy 6: PB: Other:	1	17	1	17
LED 1 copy 7: S: Other:	1	27	2	54
LED 1 copy 8: T: Other:	1	16	19	304
		Total Proposed Watts =		1737

Interior Lighting PASSES: Design 45% better than code

Interior Lighting Compliance Statement

Compliance Statement: The proposed interior lighting design represented in this document is consistent with the building plans, specifications, and other calculations submitted with this permit application. The proposed interior lighting systems have been designed to meet the 2015 IECC requirements in COMcheck Version 4.1.5.5 and to comply with any applicable mandatory requirements listed in the Inspection Checklist.

Travis Apperson — Digitally signed by Travis Apperson; DN: C=US, E=tapperson@praxis3designgroup.com, CN=Travis Apperson; Date: 2026.06.30 14:15:33-04'00' — 07/02/2026

Name - Title | Signature | Date

COMcheck Software Version 4.1.5.5

Exterior Lighting Compliance Certificate

Project Information

Energy Code: 2015 IECC
Project Title: FIFTH THIRD BANK WATSON
Project Type: New Construction
Exterior Lighting Zone 4 (High activity metropolitan commercial district (LZ4))

Construction Site:
2711 WATSON BOULEVARD
WARNER ROBBINS, GA 31093

Owner/Agent:

Designer/Contractor:

Allowed Exterior Lighting Power

A Area/Surface Category	B Quantity	C Allowed Watts / Unit	D Tradable Wattage	E Allowed Watts (B X C)
Parking area	6873 ft2	0.13	Yes	893
Entry canopy	43 ft2	0.4	Yes	17
Entry canopy	237 ft2	0.4	Yes	95
Entry canopy	379 ft2	0.4	Yes	152
			Total Tradable Watts (a) =	1157
			Total Allowed Watts =	1157
			Total Allowed Supplemental Watts (b) =	1300

(a) Wattage tradeoffs are only allowed between tradable areas/surfaces.
(b) A supplemental allowance equal to 1300 watts may be applied toward compliance of both non-tradable and tradable areas/surfaces.

Proposed Exterior Lighting Power

A Fixture ID : Description / Lamp / Wattage Per Lamp / Ballast	B Lamps/ Fixture	C # of Fixtures	D Fixture Watt.	E (C X D)
Parking area (6873 ft2): Tradable Wattage				
LED 1: 1P4F: Other:	1	140	1	140
LED 1 copy 1: SP4DA: Other:	1	140	4	560
Entry canopy (43 ft2): Tradable Wattage				
LED 1 copy 2: G1/GEM: Other:	1	21	4	84
Entry canopy (237 ft2): Tradable Wattage				
LED 1 copy 6: G1/GEM: Other:	1	21	10	210
Entry canopy (379 ft2): Tradable Wattage				
LED 1 copy 7: G1/GEM: Other:	1	21	8	168
LED 1 copy 5: L: Other:	1	180	2	360
LED 1 copy 4: U1: Other:	1	9	2	18
LED 1 copy 3: U3: Other:	1	26	4	104
			Total Tradable Proposed Watts =	1644

Exterior Lighting PASSES: Design 33% better than code

Exterior Lighting Compliance Statement

Compliance Statement: The proposed exterior lighting design represented in this document is consistent with the building plans, specifications, and other calculations submitted with this permit application. The proposed exterior lighting systems have been designed to meet the 2015 IECC requirements in COMcheck Version 4.1.5.5 and to comply with any applicable mandatory requirements listed in the Inspection Checklist.

Travis Apperson — Digitally signed by Travis Apperson; DN: C=US, E=tapperson@praxis3designgroup.com, CN=Travis Apperson; Date: 2026.06.30 14:15:33-04'00' — 07/02/2026

Name - Title | Signature | Date

PRAXIS3
100 Peachtree St NW
Suite 1450
Atlanta, GA 30303
404-875-4500 tel
www.praxis3.com

GEORGIA REGISTERED No. 041460 PROFESSIONAL ENGINEER RAHN ONEAL WILLIAMS

Copyright (c) 2024 Praxis3, LLC

All reports, plans, specifications, computer files, field data, notes and other documents and instruments prepared by Praxis3 shall retain all common law, statutory and other reserved rights, including copyright thereto.

This drawing may not be reproduced in whole or in part without written permission of Praxis3. It is to be returned upon request. Scales as stated are valid on the original drawings.

Rev	Date	Comments
	07/02/2026	PERMIT SET

Client:
FIFTH THIRD BANK

Project Number: 26032
Project Name:
FIFTH THIRD BANK WATSON 1,900 SF


2711 WATSON BOULEVARD
WARNER ROBBINS, GA 31093

Key Plan:


Sheet Title:
COMCHECK

Sheet Number:
E-004

6/30/2026 2:31:58 PM

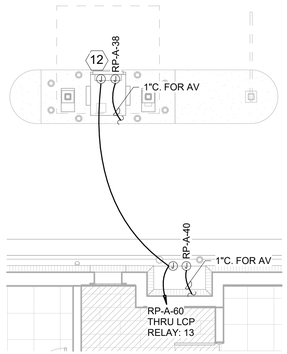

2 E-010 ELECTRICAL POWER & AUXILIARY RDT PLAN
3/16" = 1'-0"

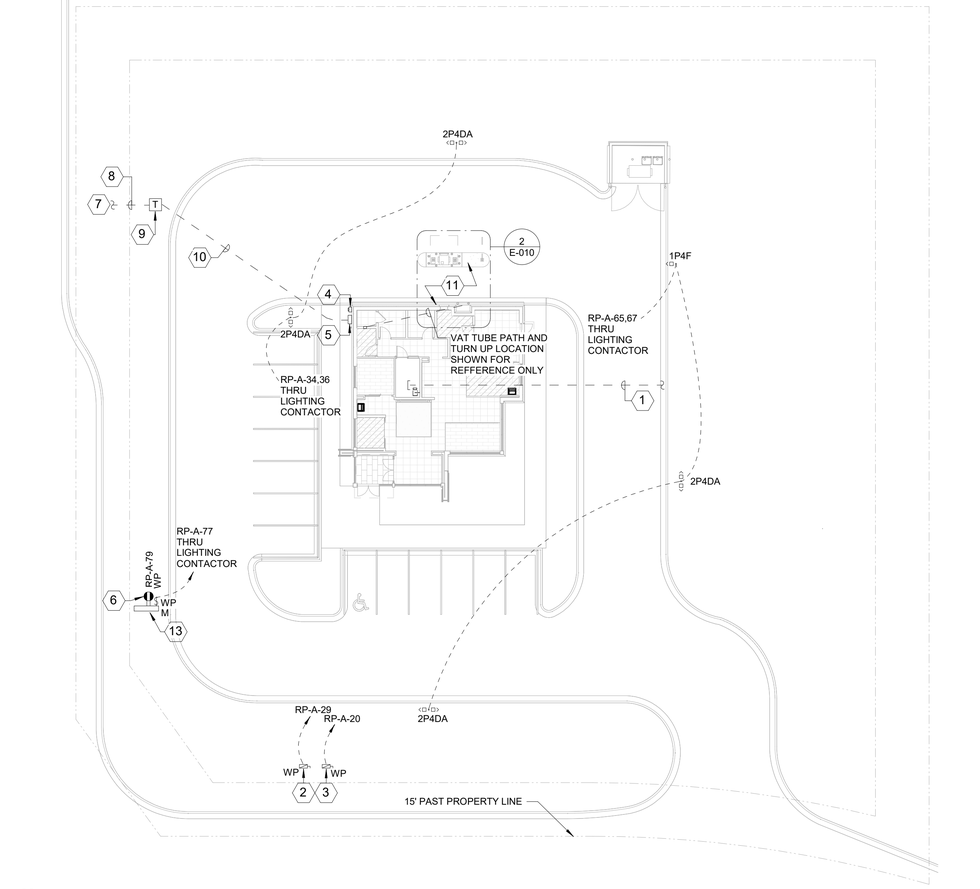

1 E-010 ELECTRICAL SITE PLAN
1" = 20'-0"

SHEET NOTES:

1. COORDINATE ALL SITE CONDUIT ROUTINGS WITH GENERAL CONTRACTOR.
2. REFER TO CIVIL PLANS FOR FINAL LOCATION AND ELECTRICAL REQUIREMENTS OF ALL SIGNAGE, UTILITY CONNECTION POINTS, AND SITE UTILITIES/EQUIPMENT SUCH AS LIFT STATIONS, IRRIGATION PUMPS/CONTROLLERS, HOT BOXES, ETC.
3. ALL UNDERGROUND WIRING SHALL BE LOCATED WITHIN 12" OF BACK OF CURB IN ALL LOCATIONS.
4. BACKFILL, TAMP, AND RESURFACE ALL EXISTING PAVEMENT/ASPHALT AND RESTORE ALL EXISTING LANDSCAPING DISTURBED AS A RESULT OF TRENCHING AND/OR DIRECTIONAL BORING TO ITS ORIGINAL CONDITION.
5. ALL UTILITY SERVICE SHALL BE VERIFIED WITH THE UTILITY COMPANIES PRIOR TO BIDDING AND ALL RESULTING COSTS SHALL BE INCLUDED IN BID
6. ACTUAL INSTALLATION OF ALL UTILITY SERVICES SHALL BE ACCORDING TO FINAL UTILITY COMPANY PLANS.
7. PROVIDE PULLWIRE IN ALL EMPTY CONDUITS.
8. USE JOINT TRENCHING WHEREVER POSSIBLE

KEYED NOTES:

1. ROUTE (2)4"C TO MAIN TELEPHONE SERVICE ENTRANCE. ROUTE TO CLEAR STRUCTURAL FOOTING. CONDUITS SHALL BE STUBBED UP AND CAPPED 12" A.F.F. IN BUILDING. ASBUILT DRAWINGS MUST SHOW CONDUIT LENGTH AND ROUTE
2. IRRIGATION BACKFLOW. VERIFY LOCATION DISCONNECT SHALL BE NEMA 3R.
3. DDCV HOTBOX. VERIFY LOCATION DISCONNECT SHALL BE NEMA 3R.
4. ELECTRIC UTILITY METER. PROVIDE ELECTRIC UTILITY METER PER POWER COMPANY REQUIREMENTS. REFER TO ELECTRICAL RISER DIAGRAM FOR ADDITIONAL INFORMATION. EXACT LOCATION TO BE DETERMINED BY UTILITY COMPANY REPRESENTATIVE IN FIELD.
5. SERVICE DISCONNECT. PROPOSED ELECTRICAL SERVICE DISCONNECT MOUNTED ON BUILDING EXTERIOR. REFER TO ELECTRICAL RISER DIAGRAM FOR ADDITIONAL INFORMATION.
6. MAINTENANCE RECEPTACLE: PROVIDE 120V, 20A, GFCI WEATHER-RESISTANT DUPLEX RECEPTACLE IN WEATHERPROOF SURFACE MOUNTED BELL BOX WITH "EXTRA DUTY WHILE-IN-USE" METALLIC COVER.
7. STUBOUT AND TERMINATE PER UTILITY COMPANY REQUIREMENTS. VERIFY LOCATION OF HIGH VOLTAGE SERVICE POINT PRIOR TO BIDDING AND INCLUDE ALL COST IN BID.
8. (2)5"C FOR HIGH VOLTAGE SERVICE FROM PROPERTY LINE TO TRANSFORMER SLABS VERIFY LOCATION AND ROUTING. HIGH VOLTAGE CONDUIT SHALL BE 48" DEEP. TERMINATE IN ACCORDANCE WITH UTILITY COMPANY REQUIREMENTS INCLUDING TRENCHING AND BACKFILL TO 90% COMPACTION.
9. TRANSFORMER SLABBOX WITH TRAFFIC GUARDS PER UTILITY COMPANY REQUIREMENTS. VERIFY SIZE, LOCATION AND ORIENTATION WITH UTILITY COMPANY. CONTRACTOR WILL PROVIDE TRANSFORMER SLABS INSTALLED COMPLETE IN ACCORDANCE WITH UTILITY COMPANY REQUIREMENTS. PROVIDE ADEQUATE GUARD RAILING AROUND POWER TRANSFORMERS IN PARKING AREAS.
10. SECONDARY FROM TRANSFORMER TO MAIN DISCONNECT. VERIFY ROUTING WITH UTILITY COMPANY AND ROUTE TO CLEAR STRUCTURAL FOOTING. SEE RISER DIAGRAM. TERMINATE IN ACCORDANCE WITH PLANS AND SPECIFICATIONS.
11. CANOPY LIGHT FIXTURE: FACTORY INSTALLED CANOPY LIGHT PROVIDED BY KIOSK MANUFACTURER. EC TO COORDINATE WITH THE MANUFACTURER AND MAKE FINAL CONNECTION.
12. DRIVE-THRU ATM: PROVIDE CONDUIT AND WIRING FOR ATM. REFER TO ELECTRICAL FLOOR PLAN ON SHEET E-500 FOR ADDITIONAL INFORMATION.
13. MONUMENT SIGN POWER: COORDINATE EXACT LOCATION OF SIGNAGE STUB-UP WITH SIGN VENDOR AND MAKE FINAL ELECTRICAL CONNECTIONS. PROVIDE 120V, 20A, TOGGLE SWITCH IN METALLIC BELL BOX WITH METALLIC WEATHERPROOF COVER IF DISCONNECT IS NOT FURNISHED WITH MONUMENT SIGN. COORDINATE EXACT LOCATION WITH CIVIL DRAWINGS.

PRAXIS3
100 Peachtree St NW
Suite 1450
Atlanta, GA 30303
404-875-4500 tel
www.praxis3.com

GEORGIA REGISTERED No. 041604 PROFESSIONAL ENGINEER RAHN ONEAL WILLIAMS

Copyright (c) 2024 Praxis3, LLC

All reports, plans, specifications, computer files, field data, notes and other documents and instruments prepared by Praxis3 shall retain all common law, statutory and other reserved rights, including copyright thereto.

This drawing may not be reproduced in whole or in part without written permission of Praxis3. It is to be returned upon request. Scales as stated are valid on the original drawings.

Rev	Date	Comments
	07/02/2026	PERMIT SET

Client:
FIFTH THIRD BANK

Project Number: 26032
Project Name:
FIFTH THIRD BANK WATSON 1,900 SF


2711 WATSON BOULEVARD
WARNER ROBBINS, GA 31093

Key Plan:


Sheet Title:
ELECTRICAL SITE PLAN AND REMOTE DRIVE THRU

Sheet Number:
E-010

6/30/2026 2:31:58 PM

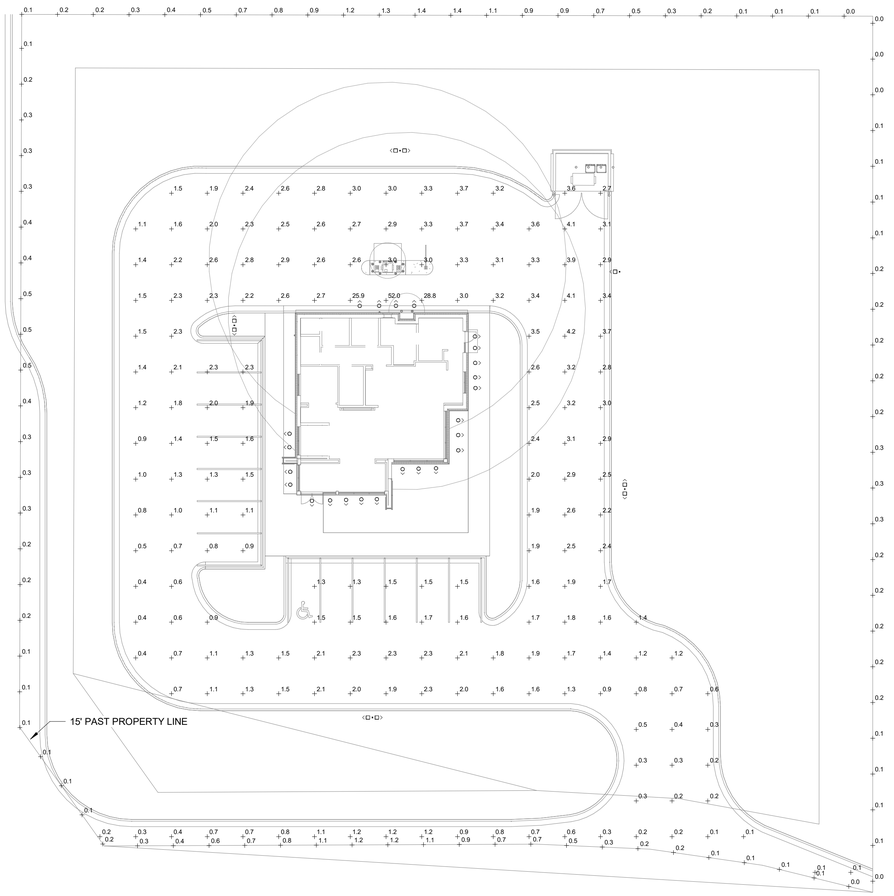

1 E-011 ELECTRICAL PHOTOMETRIC SITE PLAN AT GRADE
1" = 20'-0"

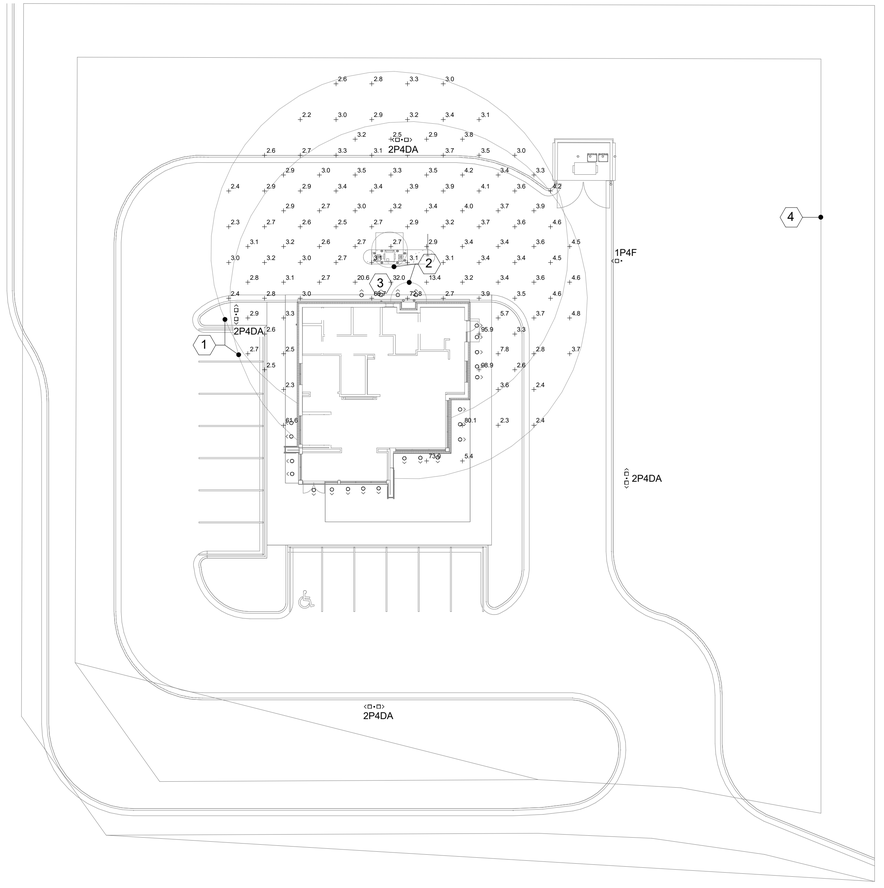

2 E-011 ELECTRICAL PHOTOMETRIC SITE PLAN AT 3'-0"
1" = 20'-0"

LIGHTING STANDARD:

MINIMUM STANDARD

REGULATED STATES: ALABAMA, CALIFORNIA, CONNECTICUT, DISTRICT OF COLUMBIA, FLORIDA, GEORGIA, ILLINOIS, KANSAS, KENTUCKY, LOUISIANA, MARYLAND, MASSACHUSETTS, MISSOURI, MONTANA, NEVADA, NEW HAMPSHIRE, NEW JERSEY, NEW YORK, OREGON, RHODE ISLAND, TEXAS, VIRGINIA, WASHINGTON, VIRGINIA**.

A. BANKING CENTERS IN VIRGINIA MUST COMPLY WITH ALL HOME STATE LAWS AND IS CONSIDERED REGULATED IF THE BANK HEADQUARTERS ARE LOCATED IN A REGULATED STATE.

- A MINIMUM OF TEN (10) FOOT CANDLE POWER AT THE FACE OF THE ATM OR AFTERHOUR DEPOSITORY EXTENDING OUTWARD FIVE (5) FEET IN ALL UNOBSTRUCTED DIRECTIONS.
- A MINIMUM OF TWO (2) FOOT CANDLE POWER EXTENDING OUTWARDS IN ALL UNOBSTRUCTED DIRECTIONS FIFTY (50) FEET FROM THE FACE OF THE ATM AND AFTERHOUR DEPOSITORY.
- A MINIMUM OF TWO (2) FOOT CANDLE POWER IN DEFINED PARKING AREAS WITHIN SIXTY (60) FEET OF THE ATM AND AFTERHOUR DEPOSITORY. IN THE EVENT THE ATM OR AFTERHOUR DEPOSITORY IS LOCATED WITHIN TEN (10) FEET OF THE CORNER OF THE BUILDING AND IS GENERALLY ACCESSIBLE FROM THE ADJACENT SIDE, THERE SHALL BE A MINIMUM OF TWO (2) FOOT CANDLE POWER ALONG THE FIRST FORTY (40) UNOBSTRUCTED FEET OF THE ADJACENT SIDE OF THE BUILDING.
- IF THE ATM OR AFTERHOUR DEPOSITORY IS LOCATED INSIDE A ACCESSIBLE VESTIBULE DURING ANY HOURS OF DARKNESS, A MINIMUM OF 10 FOOT CANDLE POWER AT THE FACE OF THE ATM OR AFTERHOUR DEPOSITORY EXTENDING OUTWARD FIVE (5) FEET IN ALL UNOBSTRUCTED DIRECTIONS. THERE WILL BE A MINIMUM OF TWO (2) FOOT CANDLE POWER AT THE INSIDE OF THE VESTIBULE ENTRY/EXIT DOOR(S). A MINIMUM OF TWO (2) FOOT CANDLE POWER EXTENDING OUTWARDS IN ALL UNOBSTRUCTED DIRECTIONS FIFTY (50) FEET FROM THE VESTIBULE ENTRY/EXIT DOOR. A MINIMUM OF TWO (2) FOOT CANDLE POWER IN DEFINED PARKING AREAS WITHIN SIXTY (60) FEET OF THE VESTIBULE ENTRY/EXIT DOOR. IN THE EVENT THE VESTIBULE ENTRY/EXIT DOOR IS LOCATED WITHIN TEN (10) FEET OF THE CORNER OF THE BUILDING AND IS GENERALLY ACCESSIBLE FROM THE ADJACENT SIDE, THERE SHALL BE A MINIMUM OF TWO (2) FOOT CANDLE POWER ALONG THE FIRST FORTY (40) UNOBSTRUCTED FEET OF THE ADJACENT SIDE OF THE BUILDING. IN URBAN SETTINGS FOR WHICH THERE IS NO DEFINED BANK PARKING AND THE ONLY ACCESS AREA IS A PUBLIC SIDEWALK, A MINIMUM 2 FOOT CANDLE POWER SHALL BE FOR THE FIRST 5 UNOBSTRUCTED FEET FROM THE DOOR. THE MINIMUM FOOT CANDLE READING WILL ALSO BE LIMITED TO BANK CONTROLLED PROPERTY LINES.
- A MINIMUM OF TWO (2) FOOT CANDLE POWER IN THE IMMEDIATE AREA OF THE DESIGNATED ASSOCIATE ENTRANCE/EXIT TO THE FACILITY.
- ALL LIGHTING MEASUREMENTS ARE TO BE TAKEN AT 36 INCHES ABOVE THE GROUND ON A HORIZONTAL PLANE, UNLESS OTHERWISE SPECIFIED BY STATE LAW OR REGULATION (3/07).
- CORPORATE WORKPLACE HAS OVERALL RESPONSIBILITY OF ENSURING THAT BANK PROPERTIES REMAINS IN COMPLIANCE.
- THE MINIMUM STANDARD SHALL APPLY UNLESS A GREATER STANDARD IS REQUIRED BY AN APPLICABLE LAW FOR A PARTICULAR FACILITY LOCATION.

CALCULATION SUMMARY AT 36" AFG

LABEL	CALCTYPE	UNIT	AVG	MAX	MIN	AVG/MIN	MAX/MIN
DRIVEUP VAT 5FT COMPLIANCE	LUMINANCE	FC	PROVIDE BY OTHERS				
DRIVEUP VAT 50FT COMPLIANCE	LUMINANCE	FC	7.8	52.0	2.3	34.8:1	34.8:1
DRIVEUP ATM 5FT COMPLIANCE	LUMINANCE	FC	PROVIDE BY OTHERS				
DRIVEUP ATM 50FT COMPLIANCE	LUMINANCE	FC	8.3	98.9	2.2	3.8:1	45.0:1

SHEET NOTES:

1. PHOTOMETRY CALCULATION:PHOTOMETRIC VALUES SHOWN HEREIN ARE INTENDED FOR DESIGN AND EVALUATION PURPOSES ONLY.THE CALCULATED POINT BY POINT VALUES SHOWN ON THIS SHEET ARE BASED ON A COMPUTER LIGHTING PROGRAM WITH APPROXIMATED PARAMETERS. AS A RESULT, PHOTOMETRIC VALUES MAY VARY FROM ACTUAL FIELD MEASUREMENTS.

KEYED NOTES:

1 ATM/VTM FIVE FOOT COMPLIANCE AREA: A MINIMUM OF TEN (10) FOOT CANDLE POWER AT THE FACE OF THE ATM/AFTERHOUR DEPOSITORY EXTENDING OUTWARD FIVE (5) FEET IN ALL UNOBSTRUCTED DIRECTIONS TO BE PROVIDED BY OWNER'S PREMANUFACTURED ATM CANOPY.

2 ATM/VTM FIFTY FOOT COMPLIANCE AREA: A MINIMUM OF TWO (2) FOOT CANDLE POWER EXTENDING OUTWARD IN ALL UNOBSTRUCTED DIRECTIONS FIFTY (50) FEET FROM THE FACE OF THE ATM AND AFTERHOUR DEPOSITORY.

3 AFTERHOUR DEPOSITORY SIXTY FOOT COMPLIANCE AREA: A MINIMUM OF TWO (2) FOOT CANDLE POWER EXTENDING OUTWARD IN ALL UNOBSTRUCTED DIRECTIONS SIXTY (60) FEET FROM THE FACE OF THE ATM AND AFTERHOURDEPOSITORY.

4 BANK CONTROLLED PROPERTY LINES: THE MINIMUM FOOT CANDLE READING WILL BE LIMITED TO BANK CONTROLLED PROPERTY LINES.

LIGHTING FIXTURE SCHEDULE (EXTERIOR)

LABEL	DESCRIPTION	LIGHT FIXTURE		MOUNTING	QTY. OF LAMPS	VOLTS	WATTS
		MFG.	MODEL NUMBER				
1P4F	LED FULL CUTOFF AREA LUMINAIRE, 15000 LU MENS.FORWARD DISTRIBUTION, ALUMINUM HOUSING, UL LISTED FOR WET LOCATION. 1HEAD	GE/LSI (POLE)	FIXTURE: EALS 04 2 F4 AF 7 40 X D D 1 DKBZ POLE: 4SQB5 S07G ** S BRZ 4BC 27'-6"	POLE MOUNT, **SEE DETAIL FOR POLE HEIGHT	LED	120-277	116
2P4DA	LED FULL CUTOFF AREA LUMINAIRE, 10000 LU MENS.FORWARD DISTRIBUTION, ALUMINUM HOUSING, UL LISTED FOR WET LOCATION. 2HEAD, 180° CONFIGURATION	GE/LSI (POLE)	FIXTURE: EALS 04 2 D4 AF 7 40 X D D1 DKBZ POLE: 4SQB5 S07G ** D180 BRZ 4BC 27'-6"	POLE MOUNT, **SEE DETAIL FOR POLE HEIGHT	LED	120-277	140

PRAXIS3
100 Peachtree St NW
Suite 1450
Atlanta, GA 30303
404-875-4500 tel
www.praxis3.com

GEORGIA REGISTERED No. 041508 PROFESSIONAL ENGINEER RAHN ONEAL WILLIAMS

Copyright (c) 2024 Praxis3, LLC

All reports, plans, specifications, computer files, field data, notes and other documents and instruments prepared by Praxis3 shall retain all common law, statutory and other reserved rights, including copyright thereto.

This drawing may not be reproduced in whole or in part without written permission of Praxis3. It is to be returned upon request. Scales as stated are valid on the original drawings.

Rev	Date	Comments
	07/02/2026	PERMIT SET

Client:
FIFTH THIRD BANK

Project Number: 26032
Project Name:
FIFTH THIRD BANK WATSON 1,900 SF


2711 WATSON BOULEVARD
WARNER ROBBINS, GA 31093

Key Plan:

Sheet Title:
ELECTRICAL PHOTOMETRIC SITE PLAN


Sheet Number:
E-011

6/30/2026 2:31:58 PM

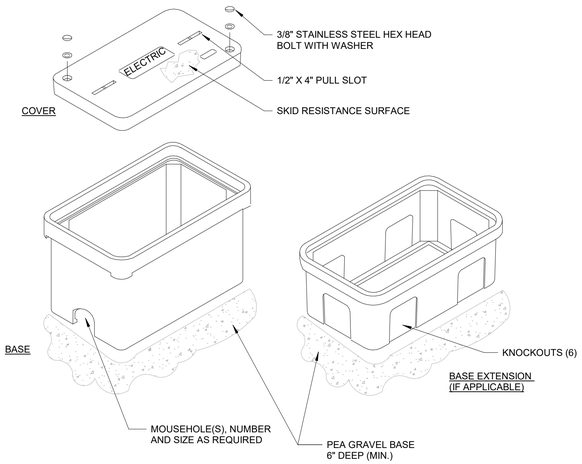


NOTES:

1. PROVIDE STANDARD POLYMER CONCRETE HAND HOLE SIZED PER NEC. COVER COLOR SHALL MATCH EXISTING.
2. PROVIDE 1" X 3/8" BELL PULL SLOT FOR EACH HAND HOLE.
3. COVER, RING, BASE, AND BASE EXTENSION SHALL BE MADE OF SAME MATERIAL.
4. PROVIDE IMPRINTED 'ELECTRIC' ON COVER.
5. HAND HOLE SHALL BE INSTALLED IN LANDSCAPE AREAS NOT SUBJECT TO VEHICULAR TRAFFIC.
6. HAND HOLE SHALL BE MIN. TIER 8 RATED.
7. ALL TERMINATIONS SHALL BE MADE USING UNITAP TAP CONNECTORS OR COMPRESSION SPLICE KITS LISTED FOR WET LOCATIONS. TWIST ON WIRE CONNECTORS ARE NOT ACCEPTABLE.
8. ALL DISTURBED SOIL SHALL BE WELL COMPACTED.
9. EACH END OF PULL STRING SHALL BE LABELED TO INDICATE ORIGIN/DESTINATION OF CONDUIT.

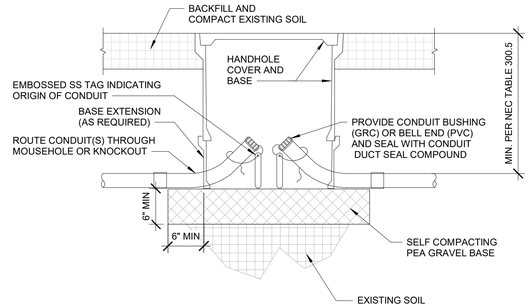


SECTION VIEW OF HAND HOLE

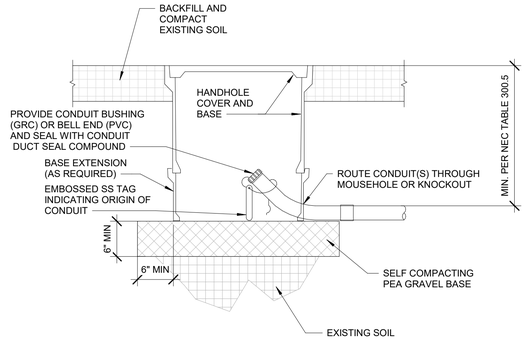


SECTION VIEW OF HAND HOLE (CAPPED SPARE CONDUIT)

1 E-012 HAND HOLE INSTALLED IN LANDSCAPE AREA DETAIL
N.T.S.

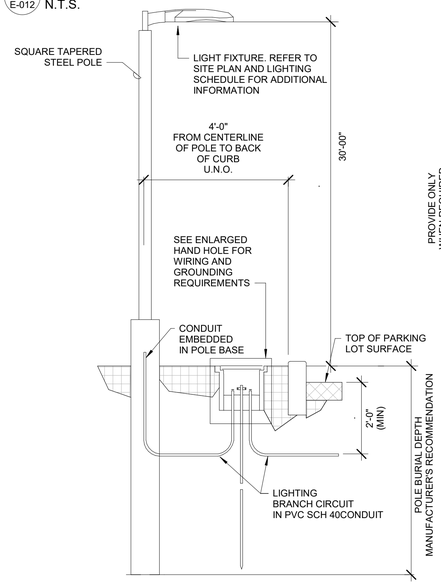


2 E-012 SITE POLE LIGHT DETAIL DIRECT BURIAL - CONCRETE
N.T.S.

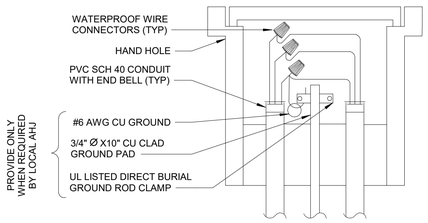

ENLARGED HAND HOLE

HAND HOLE:
1. REFER TO ENLARGED HAND HOLE DETAIL ON THIS SHEET FOR HAND HOLE SPECIFICATION AND INSTALLATION REQUIREMENTS
2. ALL TERMINATIONS WITHIN HAND HOLE SHALL BE MADE USING UNITAP TAP CONNECTORS OR COMPRESSION SPLICE KITS LISTED FOR WET LOCATIONS.TWIST ON WIRE CONNECTORS ARE NOT ACCEPTABLE.

POLE BASE:
1. REFER TO POLE BASE DETAIL 3/E-012 FOR MORE INFORMATION.

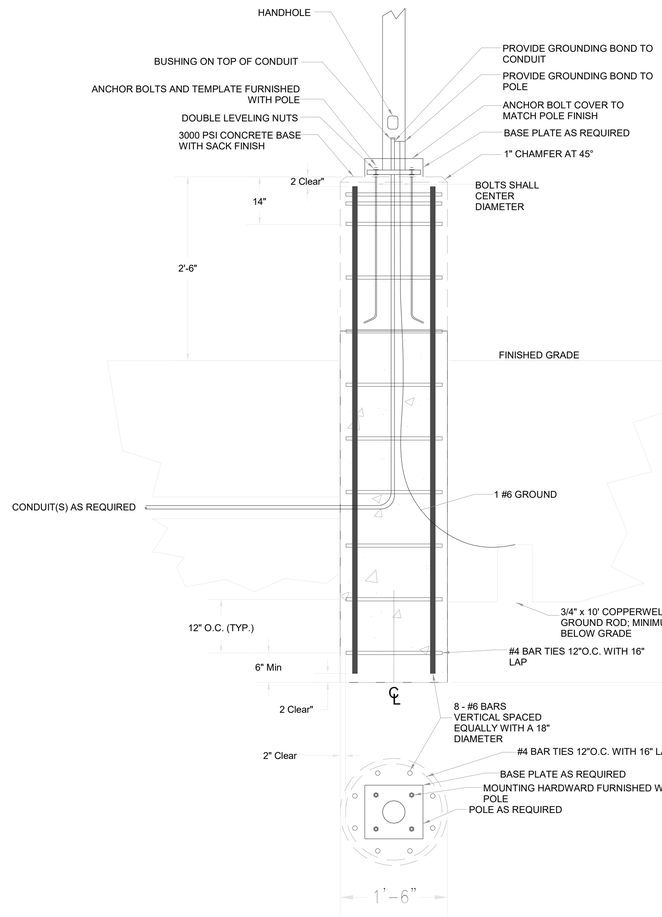

3 E-012 POLE BASE DETAIL
12" = 1'-0"

PRAXIS3
100 Peachtree St NW
Suite 1450
Atlanta, GA 30303
404-875-4500 tel
www.praxis3.com

GEORGIA REGISTERED No. 041508 PROFESSIONAL ENGINEER RAHN ONEAL WILLIAMS

Copyright (c) 2024 Praxis3, LLC

All reports, plans, specifications, computer files, field data, notes and other documents and instruments prepared by Praxis3 shall retain all common law, statutory and other reserved rights, including copyright thereto.

This drawing may not be reproduced in whole or in part without written permission of Praxis3. It is to be returned upon request. Scales as stated are valid on the original drawings.

Rev	Date	Comments
	07/02/2026	PERMIT SET

Client:
FIFTH THIRD BANK

Project Number: 26032
Project Name:
FIFTH THIRD BANK WATSON 1,900 SF


2711 WATSON BOULEVARD
WARNER ROBBINS, GA 31093

Key Plan:

Sheet Title:
ELECTRICAL SITE DETAILS

Sheet Number:
E-012

6/30/2026 2:31:59 PM

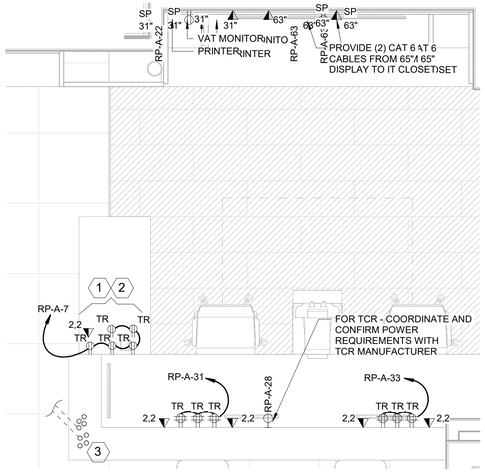


NOTE:

COORDINATE LOCATION OF ALL ELECTRICAL DEVICES WITH ARCHITECTURAL MILLWORK.

2 E-100 ELECTRICAL - POWER ENLARGED PLAN - TRANSACTION BAR1
1/2" = 1'-0"

TRANSACTION BAR KEYED NOTES:

1. ALL RECEPTACLES AND DATA AT TRANSACTION BAR, BELOW COUNTERHEIGHT, SHALL HAVE BLACK COVER PLATES AND OUTLETS U.O.N. COORDINATE DEVICE LOCATIONS WITH MILLWORK PROVIDER AND ARCHITECT. BOX ROUGH OPENINGS SHALL BE CUT BY THE MILLWORK PROVIDER.
2. E.C. TO COORDINATE WITH MILLWORK PROVIDER FOR EXACT LOCATIONS. PROVIDE OUTLETS WITHIN MILLWORK POCKET.
3. TRANSACTION BAR CONDUITS: PROVIDE FOUR (4) 3/4" CONDUITS FOR POWER AND (4) FOUR 2" CONDUITS FOR TELE/DATA FROM UNDER SLAB WITH CONDUIT BUSHINGS AND PULL STRINGS. COORDINATE WITH ARCHITECT AND MILLWORK VENDOR FOR EXACT STUB-UP LOCATIONS PRIOR TO ROUGH-IN. CONDUITS SHALL BE SEALED TO PREVENT RODENT INTRUSION.

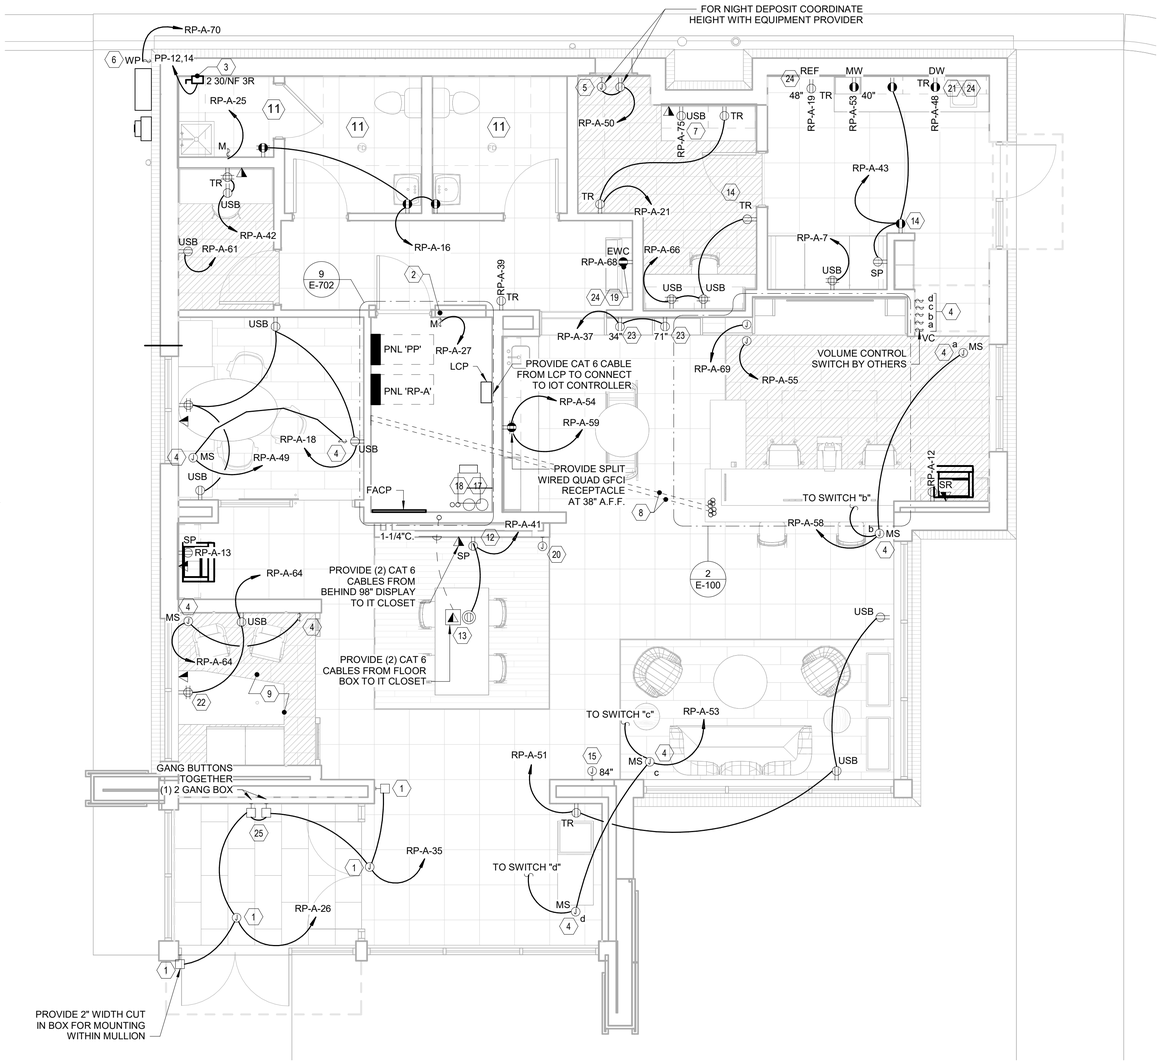

1 E-100 ELECTRICAL POWER & AUXILIARY PLAN
1/4" = 1'-0"

AUXILIARY - GENERAL NOTES:

1. ALL LOW VOLTAGE CONDUITS AND CABLING INCLUDING TELEPHONE, DATA, FIRE ALARM, AUXILIARY, ETC. SHOWN ON THESE PLANS ARE BY THE CONTRACTOR. SEE SHEET E001 "TELDATA" FOR ALL REQUIREMENTS.
2. ALL LOW VOLTAGE CABLES ABOVE ACCESSIBLE CEILING SHALL BE SUPPORTED WITH METALLIC JHOOKS FROM DEVICE LOCATIONS BACK TO THE TBB. WHERE CABLES ARE NOT ACCESSIBLE OR CONCEALED IN WALLS, THEY SHALL BE RUN IN EMT CONDUIT. JHOOKS SHALL BE SPACED SO THAT NO CABLE IS UNSUPPORTED FOR MORE THAN 5'0".

KEYED NOTES:

1. FOR POWER TO DOOR MOTOR AND DOOR PUSH PLATE. COORDINATE LOCATION OF DOOR POWER. PROVIDE 2" WIDTH CUTIN BOX FOR ALL PUSH PLATE MOUNTING WITHIN MULLION. VERIFY ALL REQUIRED CONNECTIONS PRIOR TO ROUGHIN.
2. FOR CONDENSATE PUMP.
3. 30/2 NF DISCONNECT FOR 2KW WATER HEATER, SEE RISER DIAGRAM.
4. RAISE/LOWER SWITCH FOR MECHOSHADES - COORDINATE LOCATION WITH ARCHITECT. THE INTERNET OF TEAM, LLC (IOT) WILL PROVIDE LOW VOLTAGE RAISE/LOWER SWITCHES, LINE VOLTAGE RELAY / MOTOR CONTROLLERS, THE SHADE SOLAR CONTROLLER (INTEGRAL AND PRE-INSTALLED INSIDE LCP) FOR THE ELECTRICAL CONTRACTOR (EC) TO INSTALL. IOT WILL PROVIDE MULTI GANG SWITCH OVER PLATES WHERE SHOWN AS GANGED SWITCH AND COVER PLATE SHALL BE BLACK WITHIN THE BOOTHS. EC SHALL PROVIDE WIRE, CONDUIT, AND ANCILLARY ITEMS NECESSARY TO INSTALL THE SYSTEM. TO COMPLETE THE SHADE CONTROL SYSTEM THE EC MUST PARTICIPATE IN POINT-TO-POINT COMMISSIONING AND RECEIVE SIGN-OFF WITH AN AGENT FROM IOT. REFERENCE IOT SHOP DRAWINGS FOR REQUIRED WIRE SPECIFICATIONS. REFERENCE IOT SHOP DRAWINGS FOR SHADE SYSTEM CONTROL DESIGN DETAILS AND INSTALLATION PROCEDURES. REFERENCE NEC AND LOCAL REQUIREMENTS FOR CONDUIT, FITTINGS, AND FIXTURES FOR CODE COMPLIANCE. COORDINATE ALL REQUIREMENTS WITH ARCHITECT, MECHOSHADE VENDOR, AND THE INTERNET OF TEAM, LLC
5. 4" SQUARE JUNCTION BOX MOUNTED ABOVE NIGHT DEPOSITORY WITH 3/4"C STUBBED ABOVE ACCESSIBLE CEILING FOR ALARM CONNECTION. ELECTRICALCONTRACTOR SHALL MAKE FINAL CONNECTION FROM JBOX TO NIGHT-DEPOSITORY. COORDINATE LOCATION WITH EQUIPMENT VENDOR PRIOR TO ROUGHIN.
6. WP SWITCH FOR DISCONNECTING MEANS OF IRRIGATION CONTROL VERIFY LOCATION PRIOR TO ROUGHIN. SWITCH AND CONTROLLER SHALL BE MOUNTED NEXT TO THE UTILITY METER.
7. USB OUTLET. PROVIDE USB TYPE-A & TYPE-C OUTLET, LEGRAND R26USBACWCCV6, OR EQUAL.
8. TRANSACTION BAR POWER AND DATA STUB-UP. PROVIDE UNDER SLAB CONDUITS AS FOLLOWS: (4) 3/4" IMC FOR POWER AND (4) 2" IMC WITH STRING FOR TELE/DATA TO ELEC/IT ROOM. SEE ENLARGED PLAN FOR DETAILS. ELECTRICAL CONTRACTOR SHALL COORDINATE EXACT LOCATION AND CONNECTION REQUIREMENTS WITH FURNITURE VENDOR AND ARCHITECT PRIOR TO ROUGH-IN.
9. ALL RECEPTACLES AND DATA OUTLETS AT BOOTHS, SHALL HAVE BLACK DEVICES AND COVER PLATES.
10. POWER FOR INDOOR HEAT PUMP UNITS IS DERIVED FROM OUTDOOR HEAT PUMP. ELECTRICAL CONTRACTOR SHALL PROVIDE AND INSTALL CONNECTIONBETWEEN EACH INDOOR AND OUTDOOR UNIT. ELECTRICAL CONTRACTOR SHALL CONNECT DISCONNECT SWITCH PROVIDED BY MECHANICAL FOR EACH UNIT.
11. CONNECT EXHAUST FAN TO LIGHTING CIRCUIT SERVING ROOM. FAN SHALL BE CONTROLLED BY ROOM LIGHT SWITCH.
12. FOR CONNECTION TO VIDEO SIGNAGE DISPLAY MONITORS IN TECH WALL. INDICATED JUNCTION BOXES SHALL BE DOUBLEGANG, DEEP JBOX, EACH WITH 2" EMT STUBBED ABOVE ACCESSIBLE CEILING, PROVIDE BUSHING AND LABELED. CONTRACTOR SHALL COORDINATE EXACT CABLING AND TERMINATIONS WITH VIDEO SIGNAGE PROVIDER AND ARCHITECT. COORDINATE LOCATION OF SIGNAGE PLAYER BOX WITH SIGNAGE PROVIDER. PROVIDE CABLING FROM PLAYER BOX TO DISPLAY MONITORS. VERIFY THATALL CONNECTIONS CAN REACH THE BOXES WHERE THEY ARE TERMINATED AND FED FROM WITHOUT INTERFERING WITH MONITORS. SEE DETAIL 6, SHEET E501 FOR ELEVATIONS.
13. FLOOR BOX - PWR & DATA (RECESSED): PROVIDE RECESSED FLOOR BOX LEGRAND WIREMOLD #RFBA4C30OG, RFBADP, RFBA24C4EXT, 2 HUB, RFBA6A, RFBAMAAP, 6CTC2GY (FLANGED COVER FOR CONCRETE FLOORS) WITH 3/4" IMC FOR POWER AND 1-1/4" IMC WITH PULL STRING FOR TELE/DATA TO ELECIT ROOM. ELECTRICAL CONTRACTOR SHALL COORDINATE EXACT LOCATION AND CONNECTION REQUIREMENTS WITH FURNITURE VENDOR AND ARCHITECT PRIOR TO ROUGH-IN.
14. FOR MONITOR. COORDINATE EXACT LOCATION, MOUNTING HEIGHT AND CONNECTIVITY WITH ARCHITECT PRIOR TO ROUGHIN. VERIFY MOUNTING WITH ARCHITECT.
15. PROVIDE DRIVE THRU ALERT LIGHT WHERE NOTED. COORDINATE ROUGH-IN REQUIREMENTS AND WIRING.
16. NOT USED.
17. STUB UP (2) 2" CONDUITS FROM VTM/ATM DRIVE THROUGH FOR EQUIPMENT DATA CONNECTION.
18. STUB UP (2) 4" CONDUITS FOR TELEPHONE SERVICE ENTRANCE. SEE SITE PLAN.
19. FOR E.W.C. COORDINATE MOUNTING HEIGHT AND EXACT ROUGH-IN LOCATION WITH PLUMBING FIXTURE SUBMITTAL.
20. PROVIDE RECESSED DOUBLE GANG BOX AND (1) CAT 6 CABLE FROM 7" TOUCHPANEL TO IT CLOSET MOUNT AT 44" TO THE CENTER OF THE BOX A.F.F.CONFIRM TOP OF PANEL IS NOT HIGHER THAN 46" A.F.F. TO THE TOP. THE RECESSED DOUBLE GANG BOX SHALL BE MOUNTED VERTICALLY U.O.N.
21. FOR DISHWASHER MOUNT OUTLET IN THE SPACE ADJACENT TO THE SPACE OCCUPIED BY THE DISHWASHER SO THAT THE FLEXIBLE CORD CAN PASS THROUGH THE OPENING. COORDINATE WITH GC FOR OPENING PLACEMENT
22. INSTALL POWER/DATA RECEPTACLE PER ARCHITECTURAL ELEVATIONS TO AVOID FURNITURE PLACEMENT.
23. RECEPTACLES AND COVER PLATES AT LIBRARY WALL SHALL BE BROWN. INSTALL HORIZONTAL AND COORDINATE WITH ARCHITECT AND REFERENCE ARCHITECTURAL ELEVATION DRAWINGS FOR MORE DETAIL.
24. GFCI PROTECTED CONTROLLED RECEPTACLE: CONTROLLED RECEPTACLE SHALL BE FED FROM A GFCI PROTECTED CIRCUIT BREAKER. PROVIDE FACTORY ENGRAVED COVER PLATE WITH 'GFCI PROTECTED' LABEL
25. 2-GANG DOOR PUSH PLATES. EC SHALL INSTALL AND POWER THE POWER SUPPLY (SUPPLIED BY DOOR COMPANY) ABOVE CEILING AND COORDINATE LOCATION OF DOOR POWER. PROVIDE 2-GANG ELECTRICAL BOX FOR PUSH PLATE. VERIFY ALL REQUIRED CONNECTIONS PRIOR TO ROUGH-IN.

PRAXIS3
100 Peachtree St NW
Suite 1450
Atlanta, GA 30303
404-875-4500 tel
www.praxis3.com

GEORGIA REGISTERED No. 041408 PROFESSIONAL ENGINEER RAHN ONEAL WILLIAMS

Copyright (c) 2024 Praxis3, LLC

All reports, plans, specifications, computer files, field data, notes and other documents and instruments prepared by Praxis3 shall retain all common law, statutory and other reserved rights, including copyright thereto.

This drawing may not be reproduced in whole or in part without written permission of Praxis3. It is to be returned upon request. Scales as stated are valid on the original drawings.

Rev	Date	Comments
	07/02/2026	PERMIT SET

Client:
FIFTH THIRD BANK

Project Number: 26032
Project Name:
FIFTH THIRD BANK WATSON 1,900 SF


2711 WATSON BOULEVARD
WARNER ROBBINS, GA 31093

Key Plan:

Sheet Title:
ELECTRICAL POWER & AUXILIARY PLAN

Sheet Number:
E-100


6/30/2026 2:32:01 PM

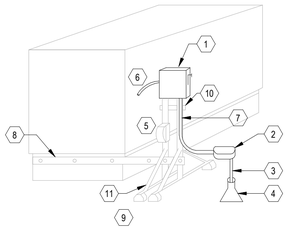

2 / E-101 ROOF DISCONNECT MOUNTING DETAIL
N.T.S.

ROOF DISCONNECT MOUNTING DETAILS KEYNOTES:

1. DISCONNECT SWITCH SHALL BE LOCATED ADJACENT TO (NOT ATTACHED TO) EQUIPMENT AND MEET WORKING CLEARANCES.
2. WEATHERPROOF "LB" CONDUIT TO TRANSITION TO LMFC.
3. HVAC EQUIPMENT FEEDER IN IMC CONDUIT.
4. PROVIDE PITCH POCKET FOR ALL CONDUIT PENETRATIONS.
5. WHERE A RECEPTACLE IS SHOWN ON A UNIT, RECEPTACLE OUTLET WITHIN 25 FT. OF EQUIPMENT WITH AN OUTLET BOX HOOD. RECEPTACLE TO BE GFCI PROTECTED.
6. LFMC PER SPECS WITHIN 12" OR LESS OF THE CONNECTION POINT OF THE UNIT.
7. SUPPORT RACEWAY WITH GALVANIZED MULTISTRUT PIPE CLAMP WHERE RUN UP THE UNITSTRUT.
8. ATTACH UNISTRUT TO CURB (NOT EQUIPMENT AND FLASHING). SEAL ALL PENETRATIONS.
9. UV RESISTANT UNISTRUT SUPPORT BASE. TYPICAL.
10. ADDITIONAL UNITSTRUT SUPPORT PERPENDICULAR TO THE UNISTRUT THAT THE DISCONNECT IS ATTACHED TO.
11. UNISTRUT SUPPORT ADDED AT 45 DEGREE ANGLE FOR ADDITIONAL SUPPORT.

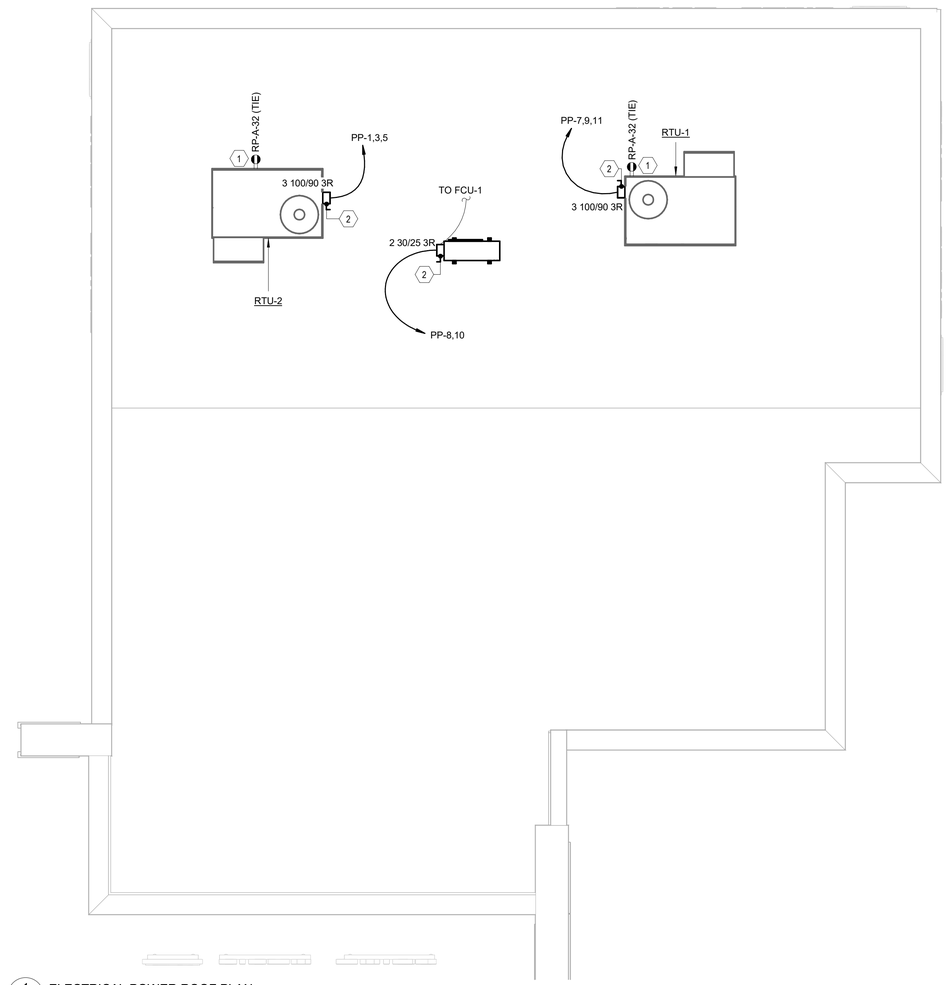

1 / E-101 ELECTRICAL POWER ROOF PLAN
1/4" = 1'-0"

SHEET NOTES:

1. EXACT LOCATIONS OF MECHANICAL EQUIPMENT AND THEIR ELECTRICAL CONNECTIONS SHALL BE COORDINATED WITH MECHANICAL CONTRACTOR. ELECTRICAL CONNECTIONS TO ROOF TOP EQUIPMENT SHALL BE ROUTED WITHIN ROOF CURB
2. COORDINATE WITH MECHANICAL CONTRACTOR FOR MECHANICAL EQUIPMENT DISCONNECT SWITCH RESPONSIBILITIES. FINAL ELECTRICAL INSTALLATION AND CONNECTIONS BY ELECTRICAL CONTRACTOR.
3. PROVIDE APPROPRIATE TRIM RING AND 3/4" CONDUIT WITH INSULATED CONDUIT BUSHINGS AND PULL STRING TO ACCESSIBLE CEILING FOR EACH THERMOSTAT. REFER TO MECHANICAL PLAN FOR THERMOSTAT QUANTITIES AND LOCATIONS. IN AREAS WITH OPEN CEILINGS, A COMPLETE CONDUIT SYSTEM SHALL BE PROVIDED FROM THE THERMOSTAT TO THE MECHANICAL UNIT; FREE WIRING IS NOT ACCEPTABLE.
4. ELECTRICAL CONTRACTOR'S BID SHALL INCLUDE POWER TO ALL MISCELLANEOUS MECHANICAL AND PLUMBING EQUIPMENT ACCESSORIES AND AUXILIARY LOADS WHICH MAY NOT BE REFLECTED IN THE ELECTRICAL PLANS BUT NECESSARY FOR A COMPLETE AND FULLY FUNCTIONING SYSTEM. NO CHANGE ORDERS WILL BE CONSIDERED.

KEYED NOTES:

1. MAINTENANCE RECEPTACLE: PROVIDE 20A, 120V GFCI WEATHERPROOF/WEATHER-RESISTANT RECEPTACLE WITH METALLIC WHILE-IN-USE COVER IF NOT PROVIDED BY RTU MANUFACTURER. PROVIDE POWER CONNECTIONS AS REQUIRED BY RTU MANUFACTURER
2. MECHANICAL UNIT DISCONNECT SWITCH: PROVIDE NEMA 3R FUSIBLE DISCONNECT SWITCH. REFER TO "ROOF DISCONNECT MOUNTING DETAIL" ON THIS SHEET FOR MORE DETAILS.

PRAXIS3
100 Peachtree St NW
Suite 1450
Atlanta, GA 30303
404-875-4500 tel
www.praxis3.com



Copyright (c) 2024 Praxis3, LLC

All reports, plans, specifications, computer files, field data, notes and other documents and instruments prepared by Praxis3 shall retain all common law, statutory and other reserved rights, including copyright thereto.

This drawing may not be reproduced in whole or in part without written permission of Praxis3. It is to be returned upon request. Scales as stated are valid on the original drawings.

Rev	Date	Comments
	07/02/2026	PERMIT SET

Client:
FIFTH THIRD BANK

Project Number: 26032
Project Name:
FIFTH THIRD BANK
WATSON
1,900 SF


2711 WATSON BOULEVARD
WARNER ROBBINS, GA 31093

Key Plan:

Sheet Title:
ELECTRICAL POWER ROOF PLAN

Sheet Number:
E-101


6/30/2026 2:32:02 PM

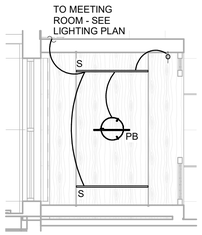

2 E-130 ELECTRICAL LIGHTING PLAN - BOOTH
1/4" = 1'-0"


LCP SCHEDULE

RELAY NUMBER	PANEL	CIRCUIT NUMBER	DESCRIPTION OF AREA	LOCAL CONTROL
1	RPA	47	CRITICAL LTG CONTACTOR	EXTERIOR OVERRIDE SWITCH
2	RPA	57	NONCRITICAL LTG CONTACTOR	EXTERIOR OVERRIDE SWITCH
3	RPA	44	EXTERIOR SIGNAGE	EXTERIOR OVERRIDE SWITCH
4	RPA	11	EXTERIOR SIGNAGE	EXTERIOR OVERRIDE SWITCH
5	RPA	5	WEATHER VESTIBULE/ENTRY	OVERRIDE SWITCH "a"
6	RPA	8	LIBRARY/TRANSACTION BAR	OVERRIDE SWITCH "b" & ELV DIMMER "b"
7	RPA	8	LIBRARY/TRANSACTION BAR	OVERRIDE SWITCH "i" & ELV DIMMER "i"
8	RPA	9	BANKING LOBBY	OVERRIDE SWITCH "c"
9	RPA	10	VESTIBULE 116 LOCAL	OVERRIDE SWITCH "d"
10	RPA	24	GATHERING AREA	OVERRIDE SWITCH "e"
11	RPA	8	UNDERCOUNTER SERVICE BAR	EXTERIOR OVERRIDE SWITCH "h"
12	RPA	6	EXTERIOR SIGNAGE	EXTERIOR OVERRIDE SWITCH
13	RPA	60	ATM TOPPER LIGHTING	EXTERIOR OVERRIDE SWITCH
14	RPA	3	UPLIGHTS AND PARAPET LIGHTING	EXTERIOR OVERRIDE SWITCH
15	RPA	4	EXTERIOR CANOPY LIGHTING	EXTERIOR OVERRIDE SWITCH

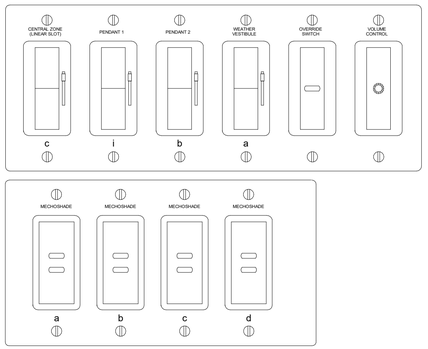

NOTES:
1. PROVIDE LABELED COVER PLATE WITH DESCRIPTION OF LOAD ABOVE EACH SWITCH. PROVIDE SUBMITTAL WITH LEGEND PRIOR TO ORDERING FOR ENGINEER APPROVAL.
2. COORDINATE WITH ARCHITECT FOR EXACT LOCATION AND MOUNTING HEIGHT PRIOR TO ROUGH-IN.
3. SWITCHES SHALL BE GROUPED AS SHOWN WITH SINGLE GANGED COVER PLATE.
4. LINE VOLTAGE ON/OFF TOGGLE AND DECORA ROCKER SWITCHES SHALL BE PROVIDED WITH A PILOT LIGHT TO INDICATE WHEN LIGHTS ARE 'ON'.

3 E-130 SWITCH BANK DETAIL
N.T.S.

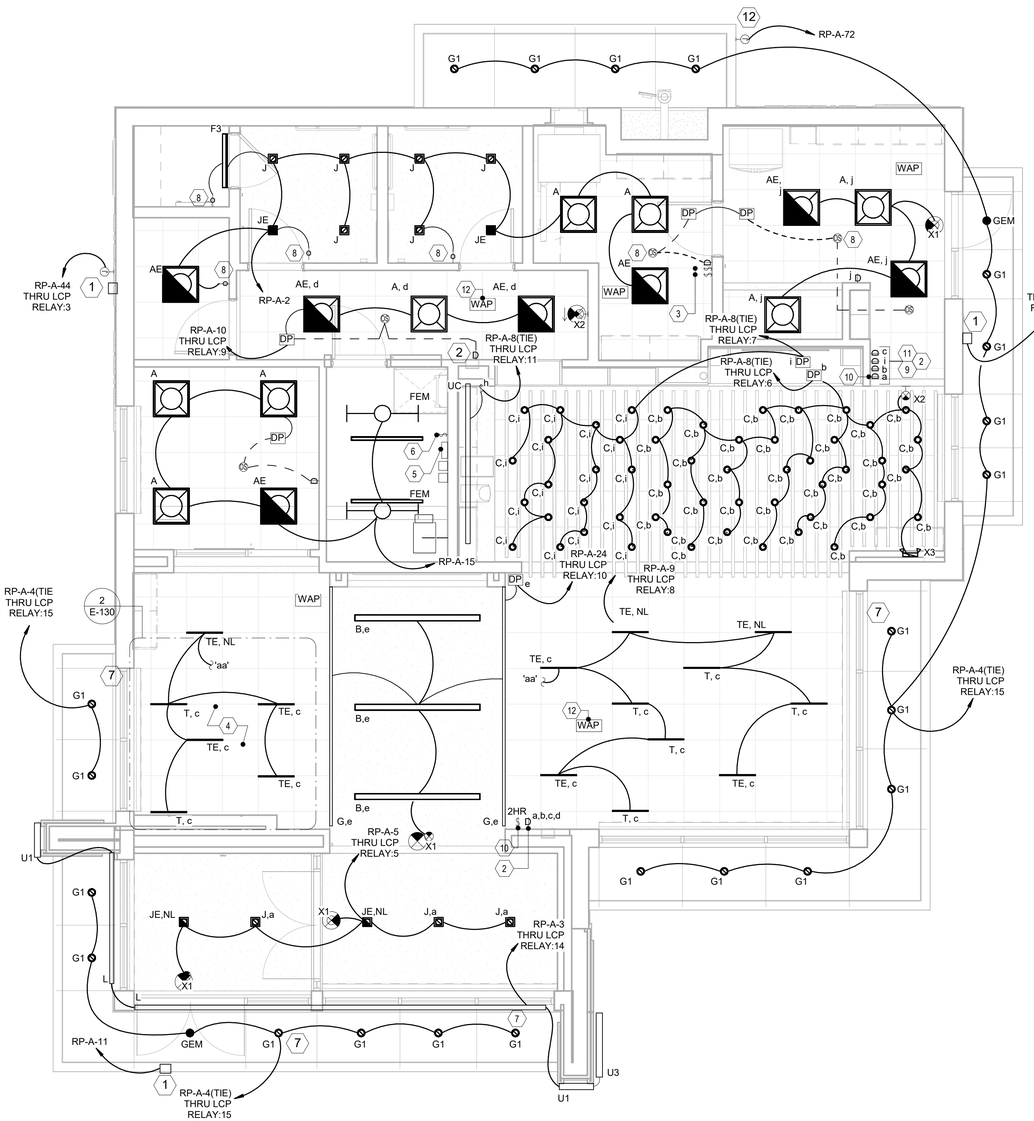

1 E-130 ELECTRICAL POWER & AUXILIARY PLAN
1/4" = 1'-0"

SHEET NOTES:

1. HALF SHADED OR FULLY SHADED LUMINAIRES SHALL BE PROVIDED WITH SELFCONTAINED 90MINUTE BACKUP BATTERY PACKS.
2. EMERGENCY LIGHTING FIXTURES SHALL SWITCH WITH LOCAL NORMAL LIGHTING UNLESS INDICATED AS "EM/NL" OR "NL" (NIGHT LIGHT).
3. EMERGENCY FIXTURES WITH INTEGRAL 90MINUTE BATTERY PACKS SHALL BE PROVIDED WITH AN UNSWITCHED HOT CONDUCTOR SO THAT EMERGENCY BATTERY PACK CAN CHARGE WHEN POWER TO THE LIGHT FIXTURES IS SWITCHED OFF.
4. EXIT AND NIGHT LIGHT FIXTURES SHALL BE CONNECTED TO UNSWITCHE D CIRCUIT AHEAD OF LIGHTING CONTROLLER.
5. THE CIRCUIT NEUTRAL CONDUCTOR SHALL BE ROUTED TO EACH LINE VOLTAGE WALL SWITCH. WHERE THE WIRING DEVICE DOES NOT REQUIRE THE USE OF A NEUTRAL CONDUCTOR, CAP FOR FUTURE USE.
6. LOW VOLTAGE CIRCUITRY IS NOT SHOWN ON THE FLOOR PLANS FOR CLARITY. LOW VOLTAGE CIRCUITRY SHALL BE PROVIDED AND INSTALLED IN ACCORDANCE WITH THE LIGHTING CONTROL VENDOR'S INSTRUCTIONS AND AS REQUIRED BETWEEN ALL LOW VOLTAGE CONTROLS AND FIXTURES.
7. LIGHTING CONTROLS VENDOR SHALL PRODUCE AND SUBMIT JOB SPECIFIC SHOP DRAWINGS SHOWING ALL DEVICE LOCATIONS, SENSOR COVERAGE, AND TERMINALTOTERMINAL WIRING DIAGRAMS SPECIFIC TO THIS PROJECT.

KEYED NOTES:

1. DISCONNECT SWITCH FOR BANK LOGO SIGN. ROUTE 1" C TO PANEL RPA THRU LIGHTING CONTROL PANEL. ELECTRICAL CONTRACTOR SHALL COORDINATE WITH ARCHITECTURAL ELEVATIONS AND SIGNAGE PROVIDER FOR EXACT LOCATION, QUANTITIES AND MOUNTING HEIGHT PRIOR TO ROUGHIN.
2. LOW VOLTAGE ON/OFF/DIMMING OVERRIDE SWITCHES FOR INTERIOR LIGHTING. SWITCH SHALL HAVE THE ABILITY TO TURN THE ZONE ON/OFF DURING PROGRAM "ON" HOURS, HAVE THE ABILITY TO MANUALLY OVERRIDE THE LIGHTS TO BE "ON" FOR TWO HOURS DURING "OFF HOURS",AND HAVE THE ABILITY TO DIM THE LIGHTS.
3. DRIVE THROUGH LANE OPEN/CLOSE GANG SWITCHES. SEE DETAIL 9 ON E-500. COORDINATE PLACEMENT WITH ARCHITECT PRIOR TO ROUGH-IN.
4. FIXTURES "PB" AND "S" SHALL BE MOUNTED AT BOOTH CEILING HEIGHT (SEE BOOTH ENLARGED PLAN). FIXTURES "T" SHALL BE MOUNTED ABOVE BOOTH. SEE ARCHITECTURAL RCP.
5. INTERNET OF TEAM BMS LCP-SA LIGHTING CONTROL PANEL. PANEL HARDWARE IS BY INTERNET OF TEAM AND SHALL BE PREPROGRAMMED PER LCP SCHEDULE. PROVIDE FOUR HOURS FOR INSTALLATION AND COMMISSIONING. PROVIDE AND INSTALL SECONDARY PANEL AS NEED FOR THE NUMBER OF RELAY SPACES.PANEL SHALL HAVE ABILITY TO CONNECT TO BUILDING AUTOMATION SYSTEM.
6. PROVIDE AN OVERRIDE SWITCH FOR TESTING OF EXTERIOR AND SITE LIGHTING. SEE LIGHTING CONTROL SCHEDULE.
7. PROVIDE PHOTOSENSOR TO INTERFACE WITH LCP AND BMS FOR EXTERIOR LIGHTING CONTROL. INSTALL PHOTOSENSOR TO WHERE THE EYE OF THE PHOTOSENSOR FACES DUE NORTH. LOCATE PHOTOSENSOR SOMEWHERE THAT IS EXPOSED TO FULL DAYLIGHT AND IS NOT SHADOWED OR DIRECTLY EXPOSED TO ANY NIGHTTIME ILLUMINATION OR ANY OTHER OBSTRUCTIONS.
8. SET LIGHT CONTROLS FOR "OCCUPANCY SENSOR" MODE, TO TURN LIGHTS ON WHEN OCCUPANCY DETECTED.
9. LOW VOLTAGE ON/OFF OVERRIDE SWITCHES FOR TRANSACTION BAR/ LIBRARYLIGHTING. SWITCH SHALL HAVE THE ABILITY TO TURN THE ZONE ON/O FF DURING PROGRAM "ON" HOURS AND HAVE THE ABILITY TO MANUALLY OVERRIDE THE LIGHTS TO BE "ON" FOR TWO HOURS DURING "OFF HOURS". PROVIDE LINE VOLTAGE ELV DIMMER SEPARATELY AS SHOWN.
10. LOW VOLTAGE 2HOUR MANUAL OVERRIDE SWITCH FOR MULTIZONES. LABEL EACH BUTTON WITH ITS RESPECTIVE ROOM/AREA. SWITCH SHALL HAVE ABILITY MANUALLY OVERRIDE THE LIGHTS TO BE "ON" FOR TWO HOURS DURING "OFF HOURS".
11. SWITCH BANK: REFER TO SWITCH BANK DETAIL THIS SHEET AND ELEVATION #3 ON SHEET E-703
12. PROVIDE WEATHER PROOF JUNCTION BOX FOR OPEN/CLOSE SIGN. COORDINATE FINAL LOCATION WITH ARCHITECT.

PRAXIS3
100 Peachtree St NW
Suite 1450
Atlanta, GA 30303
404-875-4500 tel
www.praxis3.com

GEORGIA REGISTERED No. 041508 PROFESSIONAL ENGINEER RAHN ONEAL WILLIAMS

Copyright (c) 2024 Praxis3, LLC

All reports, plans, specifications, computer files, field data, notes and other documents and instruments prepared by Praxis3 shall retain all common law, statutory and other reserved rights, including copyright thereto.

This drawing may not be reproduced in whole or in part without written permission of Praxis3. It is to be returned upon request. Scales as stated are valid on the original drawings.

Rev	Date	Comments
	07/02/2026	PERMIT SET

Client:
FIFTH THIRD BANK

Project Number: 26032
Project Name:
FIFTH THIRD BANK WATSON 1,900 SF


2711 WATSON BOULEVARD
WARNER ROBBINS, GA 31093

Key Plan:


Sheet Title:
ELECTRICAL LIGHTING PLAN

Sheet Number:
E-130

6/30/2026 2:32:04 PM

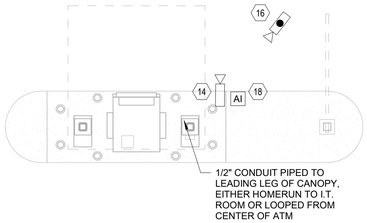

2 E-150 SECURITY PLAN REMOTE DRIVE THRU
1/4" = 1'-0"

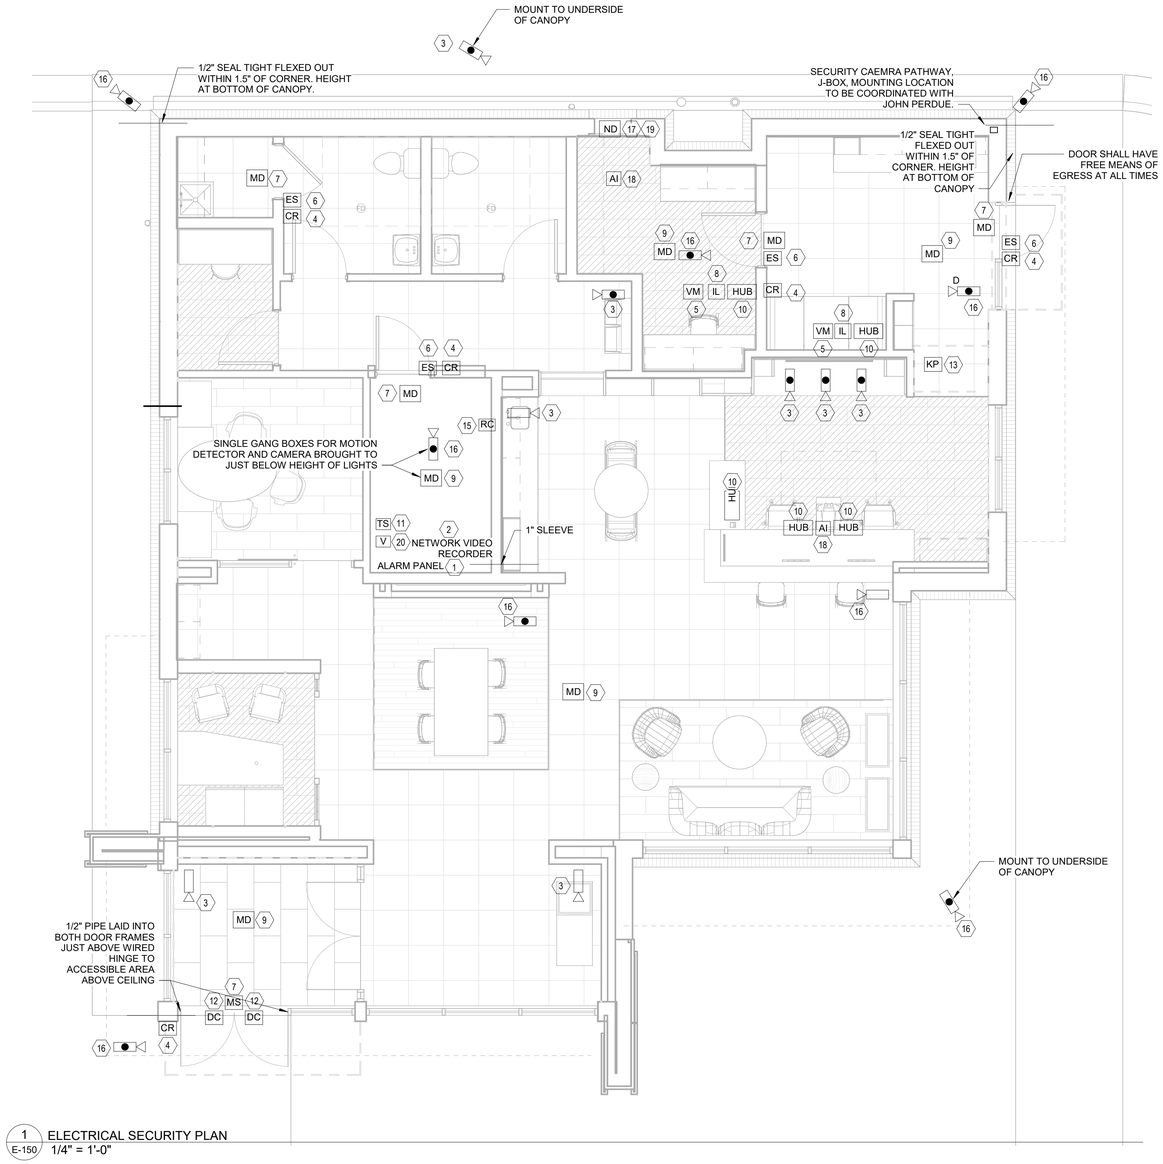

1 E-150 ELECTRICAL SECURITY PLAN
1/4" = 1'-0"

SHEET NOTES:

1. SECURITY DEVICES SHOWING ON THIS SHEET IS FOR COORDINATION PURPOSES ONLY. REFER TO SECURITY DRAWING FOR FINAL LOCATION AND REQUIREMENTS AND PROVIDE ACCORDINGLY.
2. ELECTRICAL CONTRACTOR SHALL PROVIDE ALL RACEWAYS, BOXES, PULLSTRINGS, ETC. SECURITY CABLING SHALL BE BY SECURITY VENDOR.
3. "RED" COLORED WIRE TO BE RESERVED FOR FIRE SYSTEMS AND "YELLOW" WIRES TO BE RESERVED FOR SECURITY SYSTEMS.
4. NOT ALL DEVICES MAY BE USED**
5. ALL CABLES SHALL BE PLENUM RATED
6. SUPPORT DATA / VOICE CABLES ON JHOOKS, 6' O.C., BACK TO THE SECURITY PANEL
7. PROVIDE 3/4" EMT CONDUIT WITH 3/4" BUSHING STUBBED UP TO ACCESSIBLE CEILING AND A 2 GANG BACKBOX FOR THE FOLLOWING: EACH ALARM ACTIVATING DEVICE; EXTERIOR ATM AND / OR NIGHT DEPOSIT; CCTV; CARD READERS; ALL WALL MOUNTED DEVICES.
8. PROVIDE 3/4" C. TO KNOX BOX AND STUB ABOVE TO NEAREST ACCESSIBLE CEILING.
9. ALL EXTERIOR CAMERAS SHALL HAVE A 3/4"C. STUBBED BACK TO THE NEAREST ACCESSIBLE CEILING.
10. ALL EXTERIOR CAMERAS SHALL BE INSTALLED BELOW THE CANOPIES TO MAXIMIZE CAMERA SIGHT LINES CONFIRM FINAL LOCATION WITH SECURITY VENDOR
11. ALL DOORS SHALL HAVE FREE EGRESS. COORDINATE WITH ARCHITECTURAL DOOR HARDWARE.
12. EXTERIOR JUNCTION BOX TO MOUNTED FOR 360 CAMERA TO BE INSTALLED AT CORNERS OF THE BUILDING.

SECURITY DEVICE SCHEDULE

#	DESCRIPTION	WIRE (FOR REFERENCE SEE NOTE A)	INSTALLATION REQUIREMENTS
1	ALARM PANEL	(4) 110VAC DUPLEX	(4) DUPLEX OUTLETS MOUNTED VERTICALLY FROM 6' TO 4' NEXT TO SECURITY PANELS. FIELD VERIFY LOCATION.
2	NETWORK VIDEO RECORDER	(1) 110VAC QUAD	QUAD OUTLET ADJACENT TO DATA RACK. EXACT LOCATION TBD BY SITE.
3	IP DOME CAMERA - INDOOR	CAT6	SINGLE GANG BOX, 2-3/4" ROUND MUD RING, STUB UP INTO ACCESSIBLE AREA ABOVE CEILING. SEE ELEVATION FOR AFF HEIGHT. NO PROVISIONS REQUIRED FOR MOUNTING ON DROP-IN CEILING.
4	CARD READER	22/3 PAIR IN BANANA CABLE	SINGLE GANG BOX, 44" AFF, STUB UP INTO ACCESSIBLE AREA ABOVE CEILING, FLEX FROM BOTTOM OF BOX TO ELECTRIC STRIKE. PROVIDE SLIM/MULLION METAL BACK BOX FOR MOUNTING ON MULLION.
5	VIDEO MONITOR	110VAC OUTLET, RG59 COAX	SINGLE GANG BOX, 86" AFF, SERIALLY PIPED WITH HUB AND IL, STUB UP INTO ACCESSIBLE AREA ABOVE CEILING.
6	ELECTRIC STRIKE WITH LBM	18/4 IN BANANA CABLE	WIRING FROM CARD READER.
7	MOTION DETECTOR (TO SHUNT DOOR CONTACT)	22/4 BANANA CABLE	SINGLE GANG BOX MOUNTED LONG SIDE PARALLEL TO DOOR(S) WITH RING, SEE ELEVATION FOR HEIGHT, NO PROVISIONS REQUIRED FOR MOUNTING ON DROP-IN CEILING TILES.
8	ALARM LAMP/INDICATOR LIGHT	18/2	SINGLE GANG BOX WITH RING, 60" AFF, STUB UP INTO ACCESSIBLE AREA ABOVE CEILING.
9	360 MOTION DETECTOR	22/4	SINGLE GANG BOX WITH ROUND MUD RING IN CEILING, STUB UP INTO ACCESSIBLE AREA ABOVE CEILING, NO PROVISIONS REQUIRED FOR DROP-IN TILE CEILINGS.
10	HOLD UP BUTTON	22/4	FOR TELLER LINE, STUB CONDUIT AT 18" AFF UNDER COUNTERTOP WITH STUB UP INTO ACCESSIBLE AREA ABOVE CEILING. FOR CASH/BREAK ROOMS, SINGLE GANG BOX WITH RING, 44" AFF WITH STUB UP INTO ACCESSIBLE AREA ABOVE CEILING. FOR OFFICE DESK LOCATIONS, SINGLE GANG BOX WITH RING, 18" AFF ON WALL ADJACENT TO DESK WITH STUB UP INTO ACCESSIBLE AREA ABOVE CEILING.
11	TEMPERATURE SENSOR	22/4	FOR ATM ROOM, SINGLE GANG BOX WITH RING, 60" AFF, STUB UP INTO ACCESSIBLE AREA ABOVE CEILING. FOR IT ROOMS, NO PROVISIONS REQUIRED.
12	DOOR CONTACT	22/2 IN BANANA CABLE	1/2" PIPE LAID INTO BOTH DOOR FRAMES JUST ABOVE WIRED HINGE INTO ACCESSIBLE AREA ABOVE CEILING.
13	ALARM KEYPAD	22/4	SINGLE GANG BOX WITH RING, 44" AFF, STUB UP INTO ACCESSIBLE AREA ABOVE CEILING.
14	ANALOG MINIATURE BOARD CAMERA	CAT6	SINGE GANG BOX WITH RING, STUB UP INTO ACCESSIBLE AREA ABOVE CEILING. SEE ELEVATION FOR HEIGHT.
15	ROOF CONTACT	22/4	NO PROVISIONS REQUIRED.
16	360 IP DOME CAMERA	CAT6	SINGLE GANG BOX WITH 2-3/4" ROUND MUD RING, 8'-6" AFF OR TO CEILING FOR CEILING OR CANOPY MOUNT, STUB UP INTO ACCESSIBLE AREA ABOVE CEILING. NO PROVISIONS REQUIRED FOR MOUNTING ON DROP-IN CEILING TILES.
17	IP MINIATURE BOARD CAMERA	CAT6	SINGLE GANG BOX WITH RING, 74" AFF, STUB UP INTO ACCESSIBLE AREA ABOVE CEILING. SEE ELEVATION FOR HEIGHT.
18	ALARM INTERFACE	22/8	SINGLE GANG BOX WITH RING, STUB UP INTO ACCESSIBLE AREA ABOVE CEILING. HEIGHT TO BE DETERMINED BY SHOP PRINTS PER JOB. NO PROVISIONS REQUIRED FOR VAULT.
19	NIGHT DEPOSIT	110VAC	110VAC OUTLET, 74" AFF, ADJACENT TO CAMERA JBOX. SEE POWER PLAN FOR CIRCUIT.
20	VENUS ROUTER		NO PROVISIONS REQUIRED.

PRAXIS3
100 Peachtree St NW
Suite 1450
Atlanta, GA 30303
404-875-4500 tel
www.praxis3.com

GEORGIA REGISTERED No. 041500 PROFESSIONAL ENGINEER RAHN ONEAL WILLIAMS

Copyright (c) 2024 Praxis3, LLC

All reports, plans, specifications, computer files, field data, notes and other documents and instruments prepared by Praxis3 shall retain all common law, statutory and other reserved rights, including copyright thereto.

This drawing may not be reproduced in whole or in part without written permission of Praxis3. It is to be returned upon request. Scales as stated are valid on the original drawings.

Rev	Date	Comments
	07/02/2026	PERMIT SET

Client:
FIFTH THIRD BANK

Project Number: 26032
Project Name:
FIFTH THIRD BANK WATSON 1,900 SF

2711 WATSON BOULEVARD
WARNER ROBBINS, GA 31093

Key Plan:

Sheet Title:
ELECTRICAL SECURITY PLAN

Sheet Number:
E-150

6/30/2026 2:32:05 PM



1 E-160 ELECTRICAL FIRE ALARM PLAN
1/4" = 1'-0"

SHEET NOTES:

1. ALL FIRE ALARM DEVICES, INCLUDING SPEAKERS, VISUALS, SMOKE DETECTORS, ETC. SHALL BE CONNECTED TO THE BASE BUILDING BY A LANDLORD APPROVED, LICENSED FIRE ALARM CONTRACTOR WHO'S BUSINESS IS FIRE ALARM INSTALLATION AND/OR SERVICE.
2. ALL DEVICES ARE TO BE MOUNTED A MINIMUM OF 80" FROM BOTTOM OF STROBE TO FINISHED FLOOR. DEVICES ARE TO BE MOUNTED IN PROPER BOXES (NOT TO BE MOUNTED IN EXTENSION RINGS). JUNCTION BOXES ARE TO BE CLEARLY LABELED "F/A". FLEX CONDUIT WITH INTERNAL CONNECTORS ARE TO BE USED FROM DEVICE BOX TO HOME RUN JUNCTION BOX. IN FULL WALL PENETRATIONS, CONDUIT OR FLEX MUST BE KEPT AT 12" MINIMUM ABOVE THE CEILING.
3. STROBE AND HORN WIRING TO BE 14 AWG THIN STRANDED WIRED, RED/BLACK AND SPEAKER TO BE "BELDON 8760" WITH SHIELD, GRAY JACKET OR EQUIVALENT. FOUR CONDUCTOR OR CABLES ARE NOT TO BE USED ON FIRE ALARM DEVICES. SOLID WIRE IS NOT TO BE USED. SPLICING OF WIRE BETWEEN DEVICES IS PROHIBITED. ALL FIRE ALARM WIRING TO BE PUT IN MINIMUM 1/2" EMT CONDUIT, DEDICATED HANGERS OR STRAPPED, TO BE LOCATED AT THE HIGHEST POINT ABOVE THE CEILING. FIRE ALARM WIRE MUST NOT OCCUPY THE SAME WALL PENETRATION WITH DUCTWORK, PIPING, ELECTRICAL DEVICES OR CIRCUITS. ALL CONDUIT SHALL BE TERMINATED WITH INSULATION BUSHINGS.
4. PROVIDE AND INSTALL POWER SUPPLY FOR NEW STROBES - MATCH BUILDING STANDARD - WITH NECESSARY BATTERIES, BASED ON MAXIMUM OF 20 DEVICES PER POWER SUPPLY. POWER SUPPLY TO BE CONNECTED TO A DEDICATED CIRCUIT AND SUPERVISED FOR FAILURE.
5. WIRING METHOD TO MEET THE ABOVE BUILDING STANDARDS AND COMPLY WITH ARTICLE 760 OF NEC-70 CODE REQUIREMENTS.
6. ALL DEVICES SHALL BE 110 CANDELA UNLESS OTHERWISE NOTED. THE ENTIRE LENS OF VISUAL FIRE ALARM DEVICES SHALL BE MOUNTED AT LEAST 80" AFF.
7. COORDINATE FIRE ALARM SYSTEM SHUTDOWNS AND REPROGRAMMING WITH OWNER.
8. PROVIDE LETTER OF CERTIFICATION FOR NEW FIRE ALARM DEVICES.

PRAXIS3

100 Peachtree St NW
Suite 1450
Atlanta, GA 30303

404-875-4500 tel
www.praxis3.com

GEORGIA REGISTERED No. 041450 PROFESSIONAL ENGINEER RAHN ONEAL WILLIAMS

Copyright (c) 2024 Praxis3, LLC

All reports, plans, specifications, computer files, field data, notes and other documents and instruments prepared by Praxis3 shall retain all common law, statutory and other reserved rights, including copyright thereto.

This drawing may not be reproduced in whole or in part without written permission of Praxis3. It is to be returned upon request. Scales as stated are valid on the original drawings.

Rev	Date	Comments
	07/02/2026	PERMIT SET

Client:
FIFTH THIRD BANK

Project Number: 26032
Project Name:
FIFTH THIRD BANK WATSON 1,900 SF


2711 WATSON BOULEVARD
WARNER ROBBINS, GA 31093

Key Plan:

Sheet Title:
ELECTRICAL FIRE ALARM PLAN

Sheet Number:
E-160


6/30/2026 2:32:06 PM

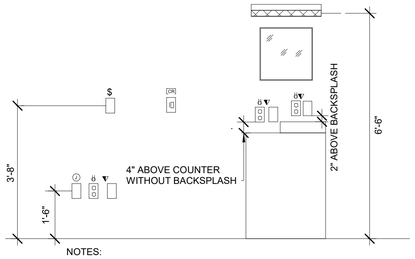

NOTES:

1. MOUNTING HEIGHTS SHOWN ARE FROM FINISHED FLOOR TO CENTERLINE OF OUTLET, UNLESS OTHERWISE NOTED.
2. LOCATIONS OF OUTLETS SHOWN ON ARCHITECTURAL ELEVATIONS SHALL TAKE PRECEDENCE OVER THESE MOUNTING HEIGHTS. FIELD LOCATE OUTLETS WITH ARCHITECT DURING ROUGH-IN.
3. INSTALL OUTLETS THAT ARE IN CLOSE PROXIMITY ON THE SAME CENTERLINE. OUTLETS THAT ARE WITHIN 2'-0" HORIZONTALLY AND WITHIN 1'-0" VERTICALLY SHALL BE INSTALLED ON THE SAME HORIZONTAL CENTERLINE LOCATED HALF WAY BETWEEN THE HEIGHTS SHOWN. OUTLETS THAT ARE MORE THAN 1'-0" APART VERTICALLY SHALL BE INSTALLED ON THE SAME VERTICAL CENTERLINE


6 E-500 STANDARD MOUNTING HEIGHT
N.T.S.

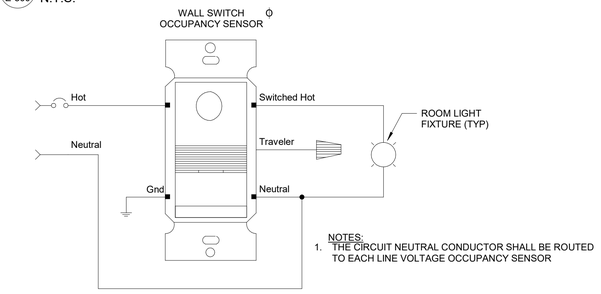

NOTES:

1. THE CIRCUIT NEUTRAL CONDUCTOR SHALL BE ROUTED TO EACH LINE VOLTAGE OCCUPANCY SENSOR


7 E-500 LINE VOLTAGE OCCUPANCY SENSOR WIRING DIAGRAM
N.T.S.

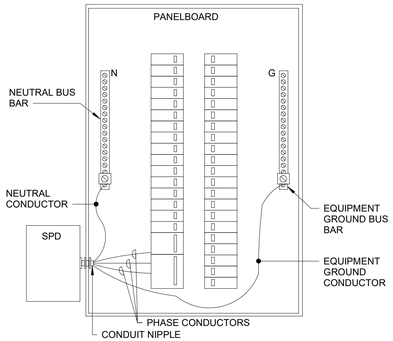


INSTALLATION NOTES:

1. REFER TO SURGE PROTECTION DEVICE (SPD) MANUFACTURER CUTSHEET FOR BREAKER AMPERE RATING. PROVIDE 2P BREAKER FOR 1 PHASE PANELBOARDS AND 3P BREAKER FOR 3 PHASE PANELBOARDS FOR CONNECTING SPD.
2. RELOCATE BREAKER IN PANEL AS NECESSARY TO PROVIDE THE SHORTEST WIRE LENGTH TO SPD.
3. DIRECT CONNECTION TO BUS IS NOT PERMITTED.
4. USE A NIPPLE CONNECTION VIA KNOCKOUT.
5. USE #10 AWG OR LARGER CONDUCTORS AS RECOMMENDED BY SPD MANUFACTURER.
6. LIMIT WIRE LENGTH TO BE AS SHORT AS POSSIBLE, 18" OR LESS.
7. KEEP WIRE FREE OF ANY SHARP BENDS.


8 E-500 SPD PANELBOARD INSTALLATION DETAIL
N.T.S.

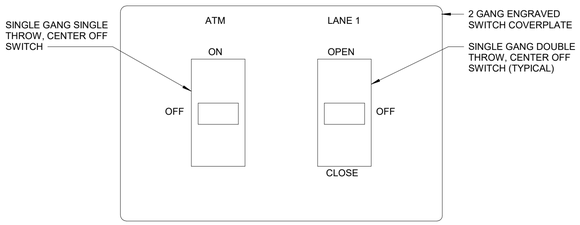


9 E-500 DRIVE THRU LIGHT SWITCH
N.T.S.

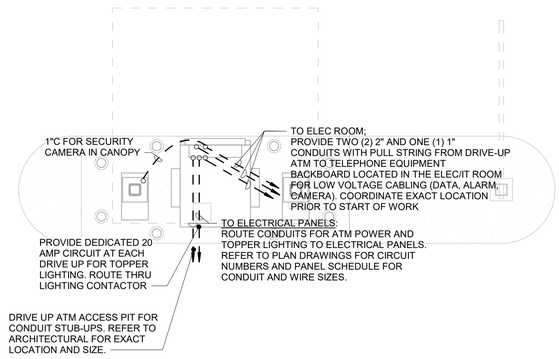

1 E-500 DRIVE-UP ATM DETAIL
N.T.S.

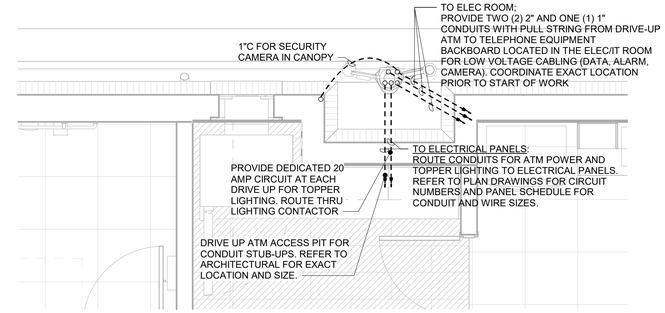


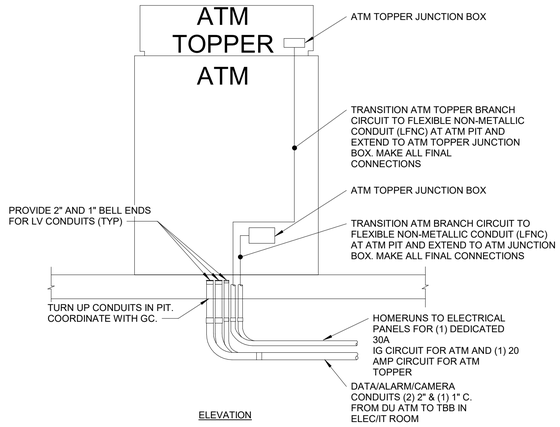

ELEVATION


NOTES:

1. REFER TO ARCHITECTURAL PLANS FOR ATM MODEL NUMBER AND INSTALLATION REQUIREMENTS RELATED TO VEHICULAR AND ANTI-THEFT BOLLARDS, CONDUIT PIT, AND MEDIAN.
2. REFER TO ATM VENDOR CUT SHEETS FOR SPECIFIC REQUIREMENTS PRIOR TO ROUGH-IN.
3. COORDINATE EXACT/FINAL STUB-UP LOCATIONS WITH GC AND ATM CUT SHEETS.
4. EC SHALL BE ON SITE DURING ATM DELIVERY TO MAKE ALL FINAL CONNECTIONS.
5. COORDINATE WITH THE OWNER AND GENERAL CONTRACTOR FOR SCHEDULING WORK.
6. REFER TO ELECTRICAL PANEL SCHEDULES FOR BRANCH CIRCUIT CONDUIT AND WIRE SIZES.
7. REFER TO ELECTRICAL FLOOR PLAN FOR CIRCUIT NUMBERS.
8. CONDUITS SHALL BE SEALED TO PREVENT RODENT INTRUSION.
9. ALL CONDUITS SHALL BE ROUTED CONCEALED.

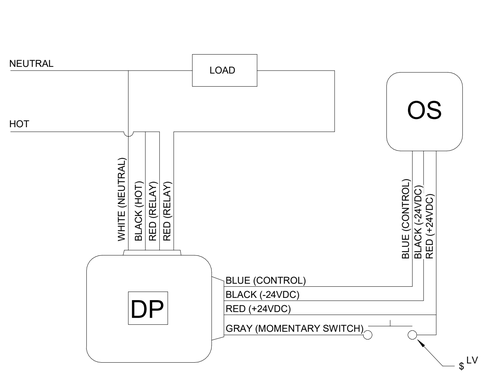


NOTE:
SEE GENERAL NOTES ON THE LIGHTING FLOOR PLANS. LIGHTING CONTROLS SHALL BE INSTALLED AND WIRED PER MANUFACTURER INSTALLATION INSTRUCTIONS. WIRING IN THE DETAIL SHOWN IS FOR REFERENCE AND SHALL BE CONFIRMED WITH THE MANUFACTURER INSTALLATION INSTRUCTIONS

3 E-500 CEILING OCCUPANCY SENSOR NO DIMMING
N.T.S.

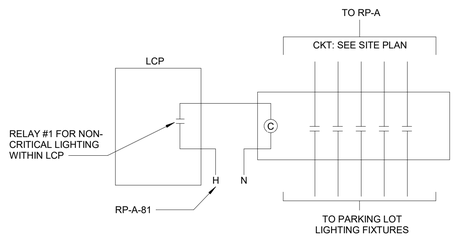


5 E-500 CRITICAL LIGHTING CONTACTOR
N.T.S.

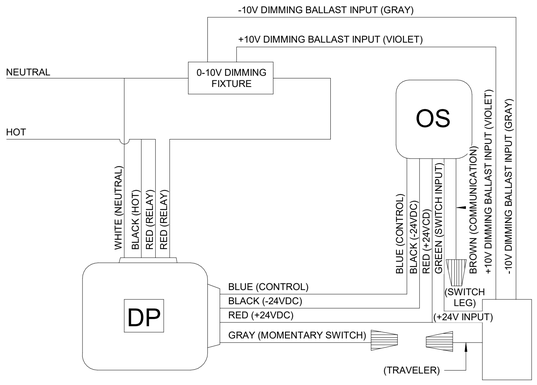

NOTE:
SEE GENERAL NOTES ON THE LIGHTING FLOOR PLANS. LIGHTING CONTROLS SHALL BE INSTALLED AND WIRED PER MANUFACTURER INSTALLATION INSTRUCTIONS. WIRING IN THE DETAIL SHOWN IS FOR REFERENCE AND SHALL BE CONFIRMED WITH THE MANUFACTURER INSTALLATION INSTRUCTIONS.

2 E-500 CEILING OCCUPANCY SENSOR WITH DIMMING
N.T.S.

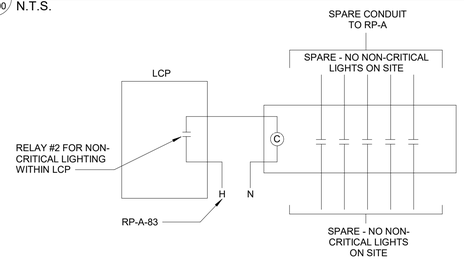

4 E-500 NON-CRITICAL LIGHTING CONTACTOR
N.T.S.

PRAXIS3
100 Peachtree St NW
Suite 1450
Atlanta, GA 30303
404-875-4500 tel
www.praxis3.com

GEORGIA REGISTERED No. 041508 PROFESSIONAL ENGINEER RAHN ONEAL WILLIAMS

Copyright (c) 2024 Praxis3, LLC

All reports, plans, specifications, computer files, field data, notes and other documents and instruments prepared by Praxis3 shall retain all common law, statutory and other reserved rights, including copyright thereto.

This drawing may not be reproduced in whole or in part without written permission of Praxis3. It is to be returned upon request. Scales as stated are valid on the original drawings.

Rev	Date	Comments
	07/02/2026	PERMIT SET

Client:
FIFTH THIRD BANK

Project Number: 26032
Project Name:
FIFTH THIRD BANK WATSON 1,900 SF


2711 WATSON BOULEVARD
WARNER ROBBINS, GA 31093

Key Plan:

Sheet Title:
ELECTRICAL DETAILS

Sheet Number:
E-500

6/30/2026 2:32:06 PM

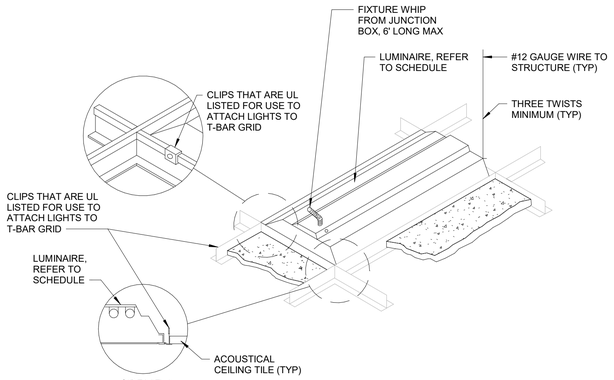


SIDE VIEW:

NOTES:

1. REFER TO ARCHITECTURAL PLANS FOR CEILING GRID SUPPORT REQUIREMENTS. THIS DETAIL SHOWS FIXTURE SUPPORT REQUIREMENTS ONLY.
2. INSTALL IN ACCORDANCE WITH MANUFACTURER'S MOUNTING INSTRUCTIONS AND USING RECOMMENDED MOUNTING HARDWARE.
3. THERMAL INSULATION SHALL NOT BE INSTALLED ABOVE A RECESSED LUMINAIRE OR WITHIN 3" OF THE RECESSED LUMINAIRE'S ENCLOSURES, WIRING COMPARTMENT, BALLAST, TRANSFORMER, LED DRIVER, OR POWER SUPPLY UNLESS THE LUMINAIRE ISIDENTIFIED AS TYPE IC FOR INSULATION CONTACT.


2 E-600 TROFFER MOUNTING - LAY-IN-CEILING
N.T.S.

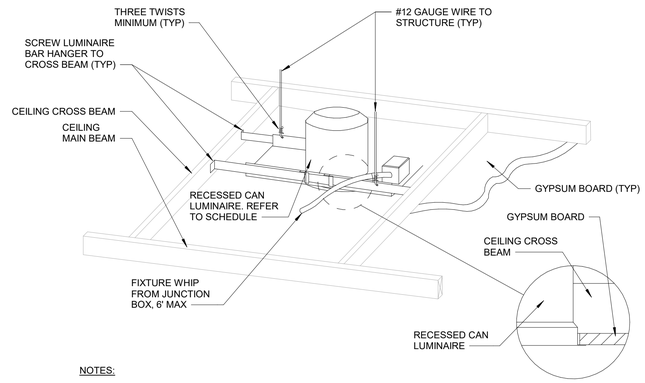

NOTES:

1. INSTALL IN ACCORDANCE WITH MANUFACTURER'S MOUNTING INSTRUCTIONS AND USING RECOMMENDED MOUNTING HARDWARE.
2. THERMAL INSULATION SHALL NOT BE INSTALLED ABOVE A RECESSED LUMINAIRE OR WITHIN 3" OF THE RECESSED LUMINAIRE'S ENCLOSURES, WIRING COMPARTMENT, BALLAST, TRANSFORMER, LED DRIVER, OR POWER SUPPLY UNLESS THE LUMINAIRE IS IDENTIFIED AS TYPE IC FOR INSULATION CONTACT.
3. ALL JUNCTION BOXES SHALL BE ACCESSIBLE.

3 E-600 DOWNLIGHT MOUNTING - GYPBOARD CEILING
N.T.S.

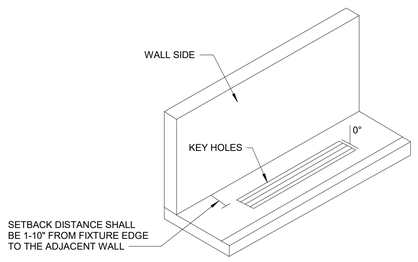

GENERAL NOTES:

1. INGROUND LED, WALK-OVER COMPLIANT, IP68 RATED, ASYMMETRIC WALLWASH WITH ANTI-SLIP LENS.
2. COORDINATE LOCATION WITH ARCHITECT PRIOR TO ROUGH-IN, AIM KEYHOLES AND FROSTED SECTION OF LENS TOWARD THE WALL SIDE.

4 E-600 INGROUND LED INSTALLATION
N.T.S.

LIGHTING FIXTURE SCHEDULE (INTERIOR)

LABEL	DESCRIPTION	LIGHT FIXTURE		MOUNTING	QTY. OF LAMPS	VOLTS	WATTS	NOTES:
		MFG.	MODEL NUMBER					
A	2' X 2' LED RECESSED LUMINAIRE, TRANSMITTANCE DIFFUSER WITH CONCAVE RIBBED REFRACTOR, L90/60,000, STEEL HOUSING, 010V DIMMING DRIVER	GE	LVT-22-B-0-33-MM-835-VQ-LT-WHTE	RECESSED	LED	120	29	
AE	2' X 2' LED RECESSED LUMINAIRE, TRANSMITTANCE DIFFUSER WITH CONCAVE RIBBED REFRACTOR, L90/60,000, STEEL HOUSING, 010V DIMMING DRIVER WITH EMERGENCY BATTERY BACKUP	GE	LVT-22-B-0-33-MM-835-VQ-LT-WHTE-EL	RECESSED	LED	120	29	
B	RECESSED EXTRUDED ALUMINUM, 010V DIMMING STANDARD, LENSED DIFFUSER, STANDARD OUTPUT, HE TECH OPTICS, MUD OVER FLANGE	CORONET	LSR4-8-35-LTG2-UNV-DB-W-NT-SD	RECESSED	LED	120		
C	TACADA PENDANT, BLACK CORD, AGED BRASS HARDWARE SEE REFLECTED CEILING PLANS FOR PENDANT LENGTHS.	MICHAEL OREN	700TDDALVPMC-B-R-LEDWD	PENDANT	LED	120		* VERIFY FINISH WITH ARCHITECT PRIOR TO ORDERING **PROVIDE TEN (10) EXTRA FIXTURES FOR ATTIC STOCK COORDINATE WITH OWNER
F3	WALL MOUNTED 3' LED STRIPLIGHT WITH DIFFUSED LENS AND STEEL HOUSING	LSI	PST-3-3-47L-FAD-UNV-835-GWT	WALL MOUNT (ABOVE DOOR)	LED	120		
FEM	48" SUSPENDED STRIP LIGHT, ACRYLIC DROP LENS, 80 CRI, WHITE FINISH, AIRCRAFT CABLE MOUNTING, WIREGUARD WITH EMERGENCY BATTERY BACKUP	GE	ALV2-0-4T-03-T-C8-1D-S-Q-Q-E-51-A-Q-W	SUSPENDED	LED	120		
G	LINEAR LED COVE WALL WASHER, 5W/ft, MEDIUM OUTPUT, 30 X 80 LENS VIEWING ANGLE, 80CRI	GE	L-LW-SO-B-0-04-CV-8-35-V-Q-TM-WHITE (LENGTH AS SPECIFIED ON PLANS)	COVE	LED	120		
G1	RECESSED LED OPEN ROUND DOWNLIGHT, 5" DIA. APERTURE, WIDE BEAM SPREAD,SEMI-DIFFUSED REFLECTOR FINISH. U.L. LISTED WET LOCATION	CSL	ED5AIC-359050-16-S; ED5-RFWLWT; ED5-TC2	RECESSED	LED	120		
GEM	RECESSED LED OPEN ROUND DOWNLIGHT, 5" DIA. APERTURE, WIDE BEAM SPREAD, SEMI-DIFFUSED REFLECTOR FINISH. U.L. LISTED WET LOCATION WITH EMERGENCY BATTERY BACKUP	CSL	ED5AIC-359050-16-S; ED5-RFWLWT; ED5-TC2; EM-1006	RECESSED	LED	120		
J	6" SQUARE DOWNLIGHT, 010V DIMMING DRIVER, SEMISPECULAR, CLEAR REFLECTOR.	GE	LDX-6S-A-1-15-T-35-VQ / RD-I6S-W-SD-WT	RECESSED	LED	120		
JE	6" SQUARE DOWNLIGHT, 010V DIMMING DRIVER, SEMISPECULAR, CLEAR REFLECTOR WITH EMERGENCY BATTERY BACKUP	GE	LDX-6S-A-1-15-T-35-VQ-EL / RD-I6S-WSD-WT	RECESSED	LED	120		
L	TETRA CONTOUR LS LED LIGHTING SYSTEM, 2W/ft, GREEN LIGHT ENGINE AND GREEN LIGHT GUIDE 180W POWER SUPPLY	GE	GEGNGLE1-A (LENGTH AS SPECIFIED ON PLANS)	RECESSED	LED	120		LOCATE AT PARAPET REVEAL. PROVIDE ALL COMPONENTS AND ACCESSORIES FOR A COMPLETE INSTALLATION
PB	PARAVO PENDANT FIXTURE WHITE FINISH FIBERGLASS SHADE, ALUMINUM EXOSTRUCTURE, FROSTED GLASS PLATE DIFFUSER, MEDIUM BASE LED A21 2700K DIMMABLE LAMP	TECH LIGHTING	700TDPRVP-WW-LED927	PENDANT	LED	120		PROVIDE 4" ROUND BOX
S	STRIP LED, 4' LENGTH, DIFFUSING LENS, MEDIUM WARM CCT, DIMMABLE REMOTE DRIVER. 96W LED DRIVER POWER SUPPLY.	NOVA FLEX	DES-LED-SWH-24-3.0-IP20-35/ CHN-SUR-2217-SL-SOFT-2M/ NF-PS-UNV-80W-24V	RECESSED	LED	120		
T	TBAR LED, 2' LENGTH, DIFFUSING LENS, MEDIUM WARM CCT, DIMMABLE REMOTE DRIVER. 30W POWER SUPPLY	SLG LIGHTING	TG-2-13-W-G1-35K / TG-2-30W	RECESSED	LED	120		COORDINATE AND CONFIRM GRID TYPE WITH ARCHITECTURAL.
TE	TBAR LED, 2' LENGTH, DIFFUSING LENS, MEDIUM WARM CCT, DIMMABLE REMOTE DRIVER. 30W POWER SUPPLY WITH EMERGENCY BATTERY BACKUP	SLG LIGHTING	TG-2-13-W-G1-35K / TG-2-30W-EMH--8	RECESSED	LED	120		COORDINATE AND CONFIRM GRID TYPE WITH ARCHITECTURAL.
U1	INGROUND LED, WALKOVER COMPLIANT, IP68 RATED, ASYMMETRIC WALLWASH WITH ANTISLIP LENS	LUMENFACADE	LOI RO-120-12-35K-WW-NO-ASL	RECESSED	LED	120		COORDINATE LOCATION WITH ARCHITECT PRIOR TO ROUGHIN, AIM KEYHOLES AND FROSTED SECTION OF LENS TOWARD THE WALL SIDE.
U3	INGROUND LED, WALKOVER COMPLIANT, IP68 RATED, ASYMMETRIC WALLWASH WITH ANTISLIP LENS.	LUMENFACADE	LOI RO-120-36-35K-WW-NO-ASL	RECESSED	LED	120		COORDINATE LOCATION WITH ARCHITECT PRIOR TO ROUGHIN, AIM KEYHOLES AND FROSTED SECTION OF LENS TOWARD THE WALL SIDE.
UC	STRIP LED, PERMANENT HOUSING LENGTH WITH LED TAPE THAT SHALL BE FIELD CUT TO THE SIZE OF THE HOUSING, DIFFUSING LENDS, MEDIUM WARM CCT, DIMMABLE REMOTE DRIVER, 80W LED DRIVER POWER SUPPLY.	NOVA FLEX	DES-LED-HO-24V-3.0-IP20-35; NF-CH-1707-SL-SOFT-2M; NF-PS-UNV-80W-24V (LENGTH AS SPECIFIED ON PLANS)	UNDER CABINET	LED	120		* VERIFY FINISH WITH ARCHITECT PRIOR TO ORDERING **PROVIDE TEN (10) EXTRA FIXTURES FOR ATTIC STOCK COORDINATE WITH OWNER
X1	LED EDGE LIT EXIT SIGN, SINGLE FACE, RECESSED IN THE CEILING	EVENLITE	SOVII-EM-R-1M-BA-RC-UC-FP-FT	RECESSED	LED	120		PROVIDE ARROWS AS SHOWN ON FLOOR PLAN
X2	LED EDGE LIT EXIT SIGN, SINGLE FACE, SURFACE WALL MOUNTED	EVENLITE	SOVII-EM-R-1M-BA-SW-UC-FP	RECESSED	LED	120		PROVIDE ARROWS AS SHOWN ON FLOOR PLAN
X3	NORMALLY OFF, EMERGENCY EGRESS CONCEALED WALLPACK	EVENLITE	APLNCUI	RECESSED	LED	120		PROVIDE ALL MOUNTING ACCESSORIES.

LIGHTING FIXTURE SCHEDULE NOTES:

1. MANUFACTURER CATALOG NUMBERS ARE SHOWN FOR GENERAL DESCRIPTIVE PURPOSES AND TO ESTABLISH STANDARD OF QUALITY ONLY. CONTACT CHRIS YOUNG (cyoung@southernlightingsource.com) OR ADAM MAGGIO (amaggio@southernlightingsource.com) (770-242-4000) (53lights@southernlightingsource.com) SOUTHERN LIGHTING SOURCE ON LIGHTING AND LIGHTING CONTROLS. GC/EC SHALL PROVIDE LUMINAIRES COMPLETE WITH ALL OPTIONS AND ACCESSORIES REQUIRED FOR A COMPLETE INSTALLATION. ALL PRODUCTS SHALL BE UL LISTED. POLE MOUNTED LIGHT FIXTURES SHALL MATCH EXISTING DEVELOPMENT AS SPECIFIED. NO EQUALS FOR POLE MOUNTED FIXTURES.
2. REFER TO ELECTRICAL SPECIFICATIONS FOR ADDITIONAL REQUIREMENTS WHICH MAY NOT NECESSARILY BE REFLECTED IN CATALOG NUMBER AND/OR DESCRIPTION IN THIS SCHEDULE
3. PROVIDE FUSES FOR UNGROUNDED CONDUCTORS SUPPLYING LED DRIVERS. PROVIDE FUSE SIZED FOR RATING OF LED DRIVER.
4. VERIFY CONSTRUCTION OF CEILINGS BEING INSTALLED AND PROVIDE THE LUMINAIRES SPECIFIED IN APPROPRIATE CONFIGURATION WITH ALL HARDWARE AND ACCESSORIES REQUIRED FOR A COMPLETE INSTALLATION.
5. PROVIDE LUMINAIRES WITH JOINING PLATES, END CAPS, CANOPIED, MOUNTING HARDWARE, ETC. AS REQUIRED FOR COMPLETE INSTALLATION.
6. EXIT LIGHTS SHALL BE PROVIDED WITH COLOR OF LETTERS REQUIRED BY LOCAL CODE AUTHORITY. FURNISH WITH CHEVRON DIRECTIONAL INDICATORS AS INDICATED AND REQUIRED.
7. PROVIDE DEVICES FOR SECURING LAY-IN TYPE LUMINAIRES TO CEILING GRID TO COMPLY WITH ARTICLE 410 OF THE NATIONAL ELECTRIC CODE.
8. FURNISH LINEAR LUMINAIRES IN CONTINUOUS ROWS OR PATTERNS AS INDICATED ON DRAWINGS. PROVIDE WITH CORNER, ANGLE AND END PIECES AS REQUIRED FOR A COMPLETE INSTALLATION.
9. FURNISH LUMINAIRES IN MECHANICAL SPACES COMPLETE WITH PENDANT STEMS OR CHAIN HANGERS AS REQUIRED TO MOUNT BELOW PIPING, DUCT, CONDUIT, ETC. MAINTAIN UNIFORM MOUNTING HEIGHT FOR ALL LUMINAIRES THROUGHOUT THE MECHANICAL AREA.
10. PENDANT MOUNTED LUMINAIRES WITH AIRCRAFT CABLE SUSPENSION SYSTEMS SHALL BE FURNISHED WITH ADJUSTABLE CABLE GRIP HARDWARE. CABLE SIZE SHALL BE SELECTED MY MANUFACTURER TO PROVIDE ADEQUATE SUPPORT OF LUMINAIRES SPECIFIED.

PRAXIS3
100 Peachtree St NW
Suite 1450
Atlanta, GA 30303
404-875-4500 tel
www.praxis3.com

GEORGIA REGISTERED No. 041500 PROFESSIONAL ENGINEER RAHN ONEAL WILLIAMS

Copyright (c) 2024 Praxis3, LLC

All reports, plans, specifications, computer files, field data, notes and other documents and instruments prepared by Praxis3 shall retain all common law, statutory and other reserved rights, including copyright thereto.

This drawing may not be reproduced in whole or in part without written permission of Praxis3. It is to be returned upon request. Scales as stated are valid on the original drawings.

Rev	Date	Comments
	07/02/2026	PERMIT SET

Client:
FIFTH THIRD BANK

Project Number: 26032
Project Name:
FIFTH THIRD BANK WATSON 1,900 SF

2711 WATSON BOULEVARD
WARNER ROBBINS, GA 31093

Key Plan:

Sheet Title:
LUMINAIRE AND SENSOR SCHEDULE AND DETAILS

Sheet Number:
E-600

6/30/2026 2:32:07 PM

Evolve®



CUSTOMER NAME _____

PROJECT NAME _____

DATE _____ TYPE _____

CATALOG NUMBER _____

EALS Series
LED Outdoor Area Light

The EALS Area Light luminaire offers a wide range of optical patterns, color temperatures, lumen packages and mounting configurations to optimize area light applications, as well as provide versatility in lighting design within one form-factor. They are ideal for commercial property site-lighting applications such as retail and commercial exteriors.

Construction

Housing:	Aluminum die cast enclosure. Integral heat sink for maximum heat transfer
Lens:	Impact resistant tempered glass
Paint:	Corrosion resistant polyester powder paint, minimum 2.0 mil thickness Standard = Black, Dark Bronze Gray, White (RAL & custom colors available) Optional = Coastal Finish
Weight:	27 lbs

Optical System

Lumens:	7,000 - 50,000
Photometry:	Type II, III, IV & V
Efficacy:	118-177LPW
CCT:	2700K, 3000K, 4000K, 5000K
CRI:	≥70
Upward Light Output Ratio (ULOR):	0 Horizontal Orientation

Electrical

Input Voltage:	120-277V, 277-480V & 347-480V
Input Frequency:	50/60 Hz
Power Factor (PH):	≥ 0.9 at rated watts
Total Harmonic Distortion (THD):	≤ 20% at rated watts

Surge Protection

☐ 6kV/3kA ☐ 10kV/5kA ☐ 20kV/10kA

Per ANSI C136.2-2023

Lumen Maintenance

Projected Lxx per IES TM-21-11 at 25°C

OPTICS	LXX/50K) @ HOURS		
	25,000 HR	50,000 HR	60,000 HR
C2, C3, C4, C5 D2, D3, D4, D5 F2, F3, F4, F5	L99	L97	L96
H2, H3, H4, H5 J2, J3, J4, J5 K2, K3, K4, K5	L98	L96	L96
L2, L3, L4, L5 M2, M3, M4, M5	L96	L93	L91
N2, N3, N4, N5	L94	L85	L82

Note: Projected Lxx based on LM80 (> 17,000 hour testing). Accepted industry tolerances apply to initial luminous flux and lumen maintenance measurements

Luminaire Ambient Temperature Factor

AMBIENT TEMP (°C)	INITIAL FLUX FACTOR	AMBIENT TEMP (°C)	INITIAL FLUX FACTOR
10	1.02	30	0.99
20	1.01	40	0.98
25	1.00		

Ratings

Operating Temperature:	-40°C to 50°C (Nx Optic Codes are -40°C to 40°C)
Vibration: LM-79:	3G per ANSI C136.31-2010 Testing in accordance with IESNA Standards

Controls

Dimming:	Standard – 0-10V ☐ Optional – DALI (Option U) ☐
Sensors:	Photo Electric Sensors (PE) available LightGrid+™ and Daintree Compatible

Warranty

☐ 5 Year (Standard) ☐ 10 Year (Optional)

IP66 IK07

© 2025 Current Lighting Solutions, LLC. All rights reserved. Information and specifications subject to change without notice. All values are design or typical values when measured under laboratory conditions.

Evolve®

EALS Series
LED Outdoor Area Light

CUSTOMER NAME _____

PROJECT NAME _____

DATE _____ TYPE _____

CATALOG NUMBER _____

Ordering Information

EALS 04 _ _ _ _ _ _ _ _ 7 _ _ _ _ _ _ _ _ _ _ _ _

PRODUCT ID	GENERATION	VOLTAGE	OPTICAL CODE	DISTRIBUTION	CRI	CCT	DIMMING[1]	CONTROLS	MOUNTING ARM	COLOR	OPTIONS
E= Evolve ALs= Area Light S = Standard	04	0*=120-277V H* = 347-480V E*[2] = 277-480V 1 = 120V 2 = 208V 3 = 240V 4 =277V D = 347V 5 = 480V	Cx =7500K[3,19] Dx = 10000 lm/ft[4,19] Fx = 15000 lm Hx = 20000 lm Jx = 25000 lm Kx = 30000 lm Lx = 35000 lm Mx = 40000 lm Nx = 50000 lm	SM = Symmetric Medium SW = Symmetric Wide SH = Symmetric High Angle AF = Asymmetric Forward AH = Asymmetric High Angle AW = Asymmetric Wide AN = Asymmetric Narrow/Auto	7 = 70 (min)	27* = 2700K 30* = 3000K 40 = 4000K 50 = 5000K	N = Dimming thru PE receptacle D = External Dimming 18/2 3 ft Cable	A = ANSI C136.41 7-Pin Receptacle (No Control) D = ANSI C136.41 7-Pin Receptacle with Shorting Cap E* = ANSI C136.41 7-pin with Non-Dimming PE Control	C** = Integral Slipfitter: Standard D** = Universal Mounting Arm: Fitted for round or square pole mounting 4" min. square poles. K**,* = Knuckle Slipfitter: For 1.9 in. - 2.3 in OD Tenon S**,* = Knuckle Slipfitter: For 2.3 in. - 3.0 in OD Tenon V**,* = Knuckle Wall Mount	BLCK = Black GRAY = Gray WHTE = White DKBZ = Dark Bronze	F= Fusing H2 = Daintree (WHS-1120) enabled motion sensor.*,16 H4 = Motion Sensor (WattStopper) L = Tool-Less Entry J = cUL/Canada R = Enhanced Surge Protection (10kV/5kA) SL** = Rotated Left SR** = Rotated Right T = Extreme Surge Protection (20kV/10kA) UF = DALI Programmable V0 = 3 Position Terminal Block V** = Coastal Finish XXX = Special Options

1 Not Available with Fusing, Must Choose a Discrete Voltage with "F" Option Code
2 Note Standard Dimming is 0-10V
3 Not available in 277-480V
4 Supplied with 3ft leads
5 Supplied with 16/3 ft Cable
6 Restricted Aiming Angle of 0-45°
7 Compatible with LightGrid+™ Wireless Control Nodes, Not Compatible with Motion Sensor Control
8 Not available in 347V, 480V or 347-480V
9 Only available with F, H, J, K, L, M, N option
10 Recommended for installations within 750 feet from coast. Lead time varies, check with factory.
11 Select 2700K or 3000K CCT for DarkSky Approved fixtures.
12 For aimed left or right light distribution orientation, as assembled in manufacturing. Not applicable for Symmetric Distributions
13 DALI option not available with 347V, 480V, or 347-480V
14 Not available with 20kV/10kA SPD
15 When mounting fixtures at 90 degrees, round pole must be 3.5" OD minimum

© 2025 Current Lighting Solutions, LLC. All rights reserved. Information and specifications subject to change without notice. All values are design or typical values when measured under laboratory conditions.

Evolve®

EALS Series
LED Outdoor Area Light

CUSTOMER NAME _____

PROJECT NAME _____

DATE _____ TYPE _____

CATALOG NUMBER _____

TYPE	OPTIC CODE	DISTRIBUTION	TYPICAL INITIAL LUMENS			TYPICAL SYSTEM WATTAGE		BUG RATINGS		
			2700K	3000K	4000K & 5000K	120-277	347-480V	2700K	3000K	4000 & 5000K
TYPE V	C5	Symmetric Medium (SM)	6800	7340	7730	45	47	B3-U0-G1	B3-U0-G1	B3-U0-G1
	D5		9060	9790	10300	61		B3-U0-G2	B3-U0-G2	B3-U0-G2
	F5		13600	14680	15450	91		B4-U0-G2	B4-U0-G2	B4-U0-G2
	H5		18130	19570	20600	123		B4-U0-G2	B4-U0-G2	B4-U0-G2
	J5		22660	24460	25750	156		B4-U0-G2	B5-U0-G3	B5-U0-G3
	K5		27190	29360	30900	191		B5-U0-G3	B5-U0-G3	B5-U0-G3
	L5		31720	34250	36050	231		B5-U0-G3	B5-U0-G4	B5-U0-G4
	M5		36260	39140	41200	273		B5-U0-G4	B5-U0-G4	B5-U0-G4
	N5		45320	48930	51500	372		B5-U0-G4	B5-U0-G4	B5-U0-G4
	C5	Symmetric Wide (SW)	6930	7480	7880	45	47	B3-U0-G1	B3-U0-G1	B3-U0-G1
	D5		9240	9980	10500	61		B3-U0-G1	B3-U0-G1	B3-U0-G1
	F5		13860	14960	15750	91		B3-U0-G2	B3-U0-G2	B3-U0-G2
	H5		18480	19950	21000	123		B4-U0-G2	B4-U0-G2	B4-U0-G2
	J5		23100	24940	26250	156		B4-U0-G2	B4-U0-G2	B5-U0-G2
	K5		27720	29930	31500	191		B4-U0-G2	B4-U0-G2	B5-U0-G2
	L5		32340	34910	36750	231		B5-U0-G2	B5-U0-G3	B5-U0-G3
	M5		36960	39900	42000	273		B5-U0-G3	B5-U0-G3	B5-U0-G3
	N5		46200	49880	52500	372		B5-U0-G3	B5-U0-G4	B5-U0-G4
	C5	Symmetric High Angle (SH)	6600	7130	7500	45	47	B3-U0-G1	B3-U0-G2	B3-U0-G2
	D5		8800	9500	10000	61		B3-U0-G2	B3-U0-G2	B4-U0-G2
	F5		13200	14250	15000	91		B4-U0-G2	B4-U0-G2	B4-U0-G2
	H5		17600	19000	20000	123		B4-U0-G3	B4-U0-G3	B5-U0-G3
	J5		22000	23750	25000	156		B5-U0-G3	B5-U0-G3	B5-U0-G3
	K5		26400	28500	30000	191		B5-U0-G3	B5-U0-G3	B5-U0-G4
	L5		30800	33250	35000	231		B5-U0-G4	B5-U0-G4	B5-U0-G4
	M5		35200	38000	40000	273		B5-U0-G4	B5-U0-G4	B5-U0-G4
	N5		44000	47500	50000	372		B5-U0-G4	B5-U0-G5	B5-U0-G5

For additional information on Non-Shielded and Shielded EALS files, please refer to LED.com

© 2025 Current Lighting Solutions, LLC. All rights reserved. Information and specifications subject to change without notice. All values are design or typical values when measured under laboratory conditions.

PRAXIS3

100 Peachtree St NW
Suite 1450
Atlanta, GA 30303

404-875-4500 tel
www.praxis3.com

GEORGIA REGISTERED No. 043508 PROFESSIONAL ENGINEER RAHN ONEAL WILLIAMS

Copyright (c) 2024 Praxis3, LLC

All reports, plans, specifications, computer files, field data, notes and other documents and instruments prepared by Praxis3 shall retain all common law, statutory and other reserved rights, including copyright thereto.

This drawing may not be reproduced in whole or in part without written permission of Praxis3. It is to be returned upon request. Scales as stated are valid on the original drawings.

Rev	Date	Comments
	07/02/2026	PERMIT SET

Client:

FIFTH THIRD BANK

Project Number: 26032
Project Name:

FIFTH THIRD BANK WATSON 1,900 SF

2711 WATSON BOULEVARD
WARNER ROBBINS, GA 31093

Key Plan:

Sheet Title:

EXTERIOR LIGHTING CUTSHEETS

Sheet Number:

E-601

6/30/2026 2:32:08 PM

Catalog #: _____ Project: _____

Prepared By: _____ Date: _____ Type: _____

XSPS

LED Soffit Light



OVERVIEW	
Lumen Package	4000 - 8000
Wattage Range	43 -59
Efficacy Range (LPW)	96 -104
Weight lbs (kg)	7.6 (3.5)

QUICK LINKS

Ordering Guide | Performance | Photometrics | Dimensions

FEATURES & SPECIFICATIONS

Construction

- Housing is die-formed aluminum with diffuse acrylic lens providing a water-resistant seal. Enclosure contains factory prewired driver and optical unit containing LEDs.
- Recess mount into an enclosed soffit with screws through the mounting frame. 8" clearance required for ease of installation.
- Finished with LSI's DuraGrip® polyester powder coat finishing process. The DuraGrip finish withstands extreme weather changes without cracking or peeling. Other standard LSI finishes available. Consult factory.
- Max shipping weight: 30lbs in carton

Optical System

- Symmetric distribution with excellent uniformity and a BUG rating of B2-U0-G1. Diffuse lens is standard to minimizing visibility of LEDs.
- Select high-brightness LEDs.
- Available in 5000K, 4000K and 3000K
- Color temperatures per ANSI C78.377.
- Minimum CRI of 80.

Electrical

- High-performance factory programmable driver features over-voltage, under voltage, short-circuit and over temperature protection with integral surge protection that meets IEEE C62.41.2 and ANSI C82.77. -5 Location Category C Low standards.
- 0-10 volt dimming (10% - 100%) standard.
- 120-347VAC 50/60Hz
- Thermal protector standard on 5000-8000 lumen versions.
- L80 Calculated Life: >100k Hours (See Lumen Maintenance chart)
- Total harmonic distortion: <20%
- Operating temperature: -40°C to 40°C (-40°F to 104°F) for HO and VHO. -40°C to 45°C (-40°F to 113°F) for SS. -40°C to 35°C (-40°F to 95°F) for SHO .
- Power factor: >0.90
- Input power stays constant over life.
- High-efficacy LEDs with integrated circuit board mount to the housing to maximize heat dissipation and promote long life.
- Driver components are fully encased in potting material for moisture resistance. Driver complies with FCC standards.

Warranty

- LSI luminaires carry a 5-year limited warranty. Refer to https://www.lsicorp.com/resources/terms-conditions-warranty/ for more information.

Listings

- Listed to UL 1598 and UL 8750
- Suitable For Damp Locations
- Meets Buy American Act requirements.
- DesignLights Consortium® (DLC) qualified product. Not all versions of this product may be DLC qualified. Please check the DLC Qualified Products List at www.designlights.org/GPL to confirm which versions are qualified.
- IDA compliant with 3000K or lower color temperature.

Type: _____

XSPS LED Soffit Light

Back to Quick Links

ORDERING GUIDE

TYPICAL ORDER EXAMPLE: **XSPS S LED SS CW 120 GWT DFL**

Prefix	Distribution	Light Source	Drive Current	Color Temperature	Input Voltage	Finish	Lens	Options
XSPS - LED Soffit	**S** - Symmetric	**LED**	**SS** - 4,000 Lumens **HO** - 5,000 Lumens **VHO** - 6,000 Lumens	**CW** - 5000K 80 CRI **NW** - 4000K 80 CRI **WW** - 3000K 80 CRI	**120** - 120V **208** - 208V **240** - 240V **277** - 277V **347** - 347V	**GWT** - Gloss White	**DFL** - Diffused Acrylic Lens	**CMT** - Channel Bar Mounting Kit **BB** - Emergency Battery Pack[1]

1 - Emergency Battery Pack only available on the SS - 4000 lumen version (120, 208, 240 & 277V versions).

PERFORMANCE

DELIVERED LUMENS

Lumen Package	Distribution	Lens Type	CRI	3000K CCT			4000K CCT			5000K CCT			Wattage
				Delivered Lumens	Efficacy	Bug Rating	Delivered Lumens	Efficacy	Bug Rating	Delivered Lumens	Efficacy	Bug Rating	
SS	S	DFL	80	3816	123	B2-U0-G1	4022	129	B2-U0-G1	3966	128	B2-U0-G1	31
HO	S	DFL	80	4756	120	B2-U0-G1	5011	127	B2-U0-G1	4941	125	B2-U0-G1	40
VHO	S	DFL	80	5733	118	B2-U0-G1	6041	124	B2-U0-G1	5957	122	B2-U0-G1	49
SHO	S	DFL	80	7559	113	B3-U0-G1	7965	119	B3-U0-G1	7853	118	B3-U0-G1	67

LEDs are frequently updated therefore values are nominal.

Electrical Data (Amps)*

Lumen Package	Wattage	120V	208V	240V	277V	347V
SS	31	0.26	0.15	0.13	0.11	0.09
HO	40	0.33	0.19	0.16	0.14	0.11
VHO	49	0.41	0.23	0.2	0.18	0.14
SHO	67	0.56	0.32	0.28	0.24	0.19

*Electrical data at 25C (77F). Actual wattage may differ by +/-10%.

RECOMMENDED LUMEN MAINTENANCE

Ambient Temp C	Initial[1]	25K hrs.[1]	50K hrs.[1]	75K hrs.[2]	100K hrs.[2]
25 C	100%	95%	91%	86%	82%

1 - In accordance with IESNA TM-21-11, Projected Values represent interpolated value based on time durations that are within six times the IESNA LM-80-08 total test duration for the device under testing.
2 - In accordance with IESNA TM-21-11, Calculated Values represent time durations that exceed six times the IESNA LM-80-08 total test duration for the device under testing.

Catalog # : _____ Project : _____ Type : _____

Prepared By : _____ Date : _____

Mirada Medium Wall Sconce (XWM)

Outdoor Wall Sconce

IP65 IK08



OVERVIEW	
Lumen Package	3,000 - 21,000
Wattage Range	23 - 175
Efficacy Range (LPW)	125 - 158
Weight lbs(kg)	27 (12.2)
Control Options	IMSBT, ALB, ALS, PCI

QUICK LINKS

Ordering Guide | Performance | Photometrics | Dimensions

FEATURES & SPECIFICATIONS

Construction

- Rugged die-cast aluminum housing contains factory prewired driver and optical unit. Hinged die-cast aluminum wiring access door located underneath.
- Galvanized-steel universal wall mount bracket comes standard with hinging mechanism to easily access the junction box wire connections without removing the luminaire.
- Optional pole-mounting bracket (XPMA) permits mounting to standard poles.
- Fixtures are finished with LSI's DuraGrip® polyester powder coat finishing process. The DuraGrip finish withstands extreme weather changes without cracking or peeling. Other standard LSI finishes available. Consult factory.
- Max shipping weight: 30lbs in carton

Optical System

- State-of-the-Art one piece silicone optic provides industry leading optical control while also acting as an integrated gasket reducing system complexity and improving fixture reliability.
- Proprietary silicone refractor optics provide exceptional coverage and uniformity in Types 2, 3, 4, and FT distributions.
- Silicone optical material does not yellow or crack with age and provides a typical light transmittance of 93-95%.
- Zero uplight.
- Available in 5000K, 4000K and 3000K color temperatures per ANSI C78.377. Also Available in Phosphor Converted Amber with Peak intensity at 610nm.
- Minimum CRI of 70.

Electrical

- High-performance programmable driver features over-voltage, under-voltage, short-circuit and over temperature protection. Custom lumen and wattage packages available.
- 0-10V dimming (10% - 100%) standard.
- Standard Universal Voltage (120-277 Vac) Input 50/60 Hz or optional High Voltage (347-480 Vac).
- L80 Calculated Life: >100k Hours
- Total harmonic distortion (THD): <20%
- 3L to 12L operating temperature: -40°C to +50°C (-40°F to +122°F)
- 15L operating temperature: -40°C to +45°C (-40°F to +113°F).
- 18L operating temperature: -40°C to +40°C (-40°F to +104°F).
- 21L operating temperature: -40°C to +35°C (-40°F to + 95°F).
- Power factor (PF): >.90
- Input power stays constant over life.
- Optional 10kV surge protection device meets a minimum Category C Low operation (per ANSI/IEEE C62.41.2).
- High-efficacy LEDs mounted to metal-core circuit board to maximize heat dissipation
- Components are fully encased in potting material for moisture resistance. Driver complies with FCC standards. Driver and key electronic components can easily be accessed via hinged door.
- Optional integral emergency battery pack provides 90-minutes of constant power to the LED system, ensuring code compliance. A test switch/indicator button is installed on the housing for ease of maintenance. The fixture delivers 1500 lumens during emergency mode.

Controls

- Integral passive infrared Bluetooth™ motion sensor options. Fixtures operate independently and can be commissioned via an iOS or Android configuration app. Updates and modifications to the control strategy are easily implemented via an intuitive app.
- LSI's AirLink™ Blue lighting control system is a simple feature rich wireless Bluetooth mesh network. The integrated fixture sensor module provides wireless control of grouped fixtures based on motion sensors, daylight or a fully customizable schedule.

Installation

- Universal wall mounting plate easily mounts directly to 4" octagonal or square junction box.
- 2 fasteners secure the hinged door underneath the housing and provide quick & easy access to the electrical compartment for installing/servicing.
- Optional terminal block accepts up to 12 ga wire.

Warranty

- LSI luminaires carry a 5-year limited warranty. Refer to https://www.lsicorp.com/resources/terms-conditions-warranty/ for more information.
- 1 Year warranty on Battery Back-up option.

Listings

- Listed to UL 1598 and UL 8750.
- Meets Buy American Act requirements.
- IDA compliant; with 3000K or lower color temperature selection.
- Title 24 Compliant; see local ordinance for qualification information.
- Suitable for wet Locations.
- IP65 rated luminaire per IEC 60598.
- 3G rated for ANSI C136.31 high vibration applications when pole mounted (using optional XPMA bracket) or wall mounted.
- IK08 rated luminaire per IEC 66262 mechanical impact code
- DesignLights Consortium® (DLC) Premium qualified product. Not all versions of this product may be DLC Premium qualified. Please check the DLC Qualified Products List at www.designlights.org/QPL to confirm which versions are qualified.

Type : _____

Mirada Medium Wall Sconce (XWM) Outdoor Wall Sconce

Have questions? Call us at (800) 436-7800

ORDERING GUIDE

Back to Quick Links

TYPICAL ORDER EXAMPLE: **XWM 2 LED 03L 30 UE BRZ ALSC**

Family	Distribution	Light Source	Lumen Package	Color Temperature
XWM - Mirada Medium Wall Sconce	**2** - Type 2 **3** - Type 3 **4** - Type 4 **FT** - Type 4 Forward Throw	**LED**	**3L** - 3,000 **4L** - 4,000 **6L** - 6,000 **8L** - 8,000 **12L** - 12,000 **15L** - 15,000 **18L** - 18,000 **21L** - 21,000 **Custom Lumen Packages**[1]	**30** - 3000K **40** - 4000K **50** - 5000K **AMB** - Phosphor Converted Amber[2]

Voltage	Finish	Controls	Options
UE - Universal Voltage (120-277V) **HV** - High Voltage (347-480V)	**BLK** - Black **BRZ** - Dark Bronze **GMG** - Gun Metal Gray **GPT** - Graphite **MSV** - Metallic Silver **PLP** - Platinum Plus **SVG** - Satin Verde Green **WHT** - White	**Blank** - None **Wireless Controls** **ALSC** - Airlink Synapse Control System **ALSCS01** - AirLink Synapse Control System with 8-12' Motion Sensor **ALSCS02** - AirLink Synapse Control System with 12-20' Motion Sensor **ALBCS1** - AirLink Blue Wireless Motion & Photo Sensor Controller (8-24' MH)[3] **ALBCS2** - AirLink Blue Wireless Motion & Photo Sensor Controller (25-40' MH)[3] **Standalone Controls** **DIM** - 0-10v Dimming leads extended to housing exterior **IMSBT1** - Integral Bluetooth™ Motion and Photocell Sensor (8-24' MH)[3,4] **IMSBT2** - Integral Bluetooth™ Motion and Photocell Sensor (25-40' MH)[3,4] **Button Type Photocells** **PCI120** - 120V **PCI208-277** - 208 -277V **PCI347** - 347V	**Blank** - None **BB** - Battery Back-up (0°C)[5] **CWBB** - Cold Weather Battery Backup (-20°C)[5] **XPMA** - Pole Mounting Bracket **SP1** - 10kV Surge Protection **TB** - Terminal Block

Need more information? Click here for our glossary

Have additional questions? Call us at (800) 436-7800

FUSING ACCESSORY ORDERING INFORMATION[6]

Part Number	Description
FK120[7]	FK120 - Single Fusing
FK277[7]	FK277 - Single Fusing
FK347[7]	FK347 - Single Fusing
DFK208[7]	DFK - Double Fusing
DFK240[7]	DFK - Double Fusing (240V)
DFK480[7]	DFK - Double Fusing (480V)

MOUNTING ACCESSORY ORDERING INFORMATION[6]

Part Number[8]	Description
8093742CLB	XWM Wet Location Surface Conduit/Wiring Box
751652	10' Linear Bird Spike Kit (2' Recommended per Luminaire)

1 Custom lumen and wattage packages available consult factory, Values are within industry standard tolerances but not DLC listed.
2 Only available in 6L Lumen Package. Consult factory for lead time and availability.
3 IMSBT and ALBCS control options are not available in 3L or 4L lumen packages when high voltage (HV) is specified.
4 IMSBTxL is field configurable via the Lewitron app that can be downloaded from your smartphone's app store.
5 Not available in HV.
6 Accessories are shipped separately and field installed.
7 Fusing must be located in a hand hole for pole or in the junction box.
8 "CSB" to be replaced by paint finish selection. See Finish options for paint color selections.

6/30/2026 2:32:09 PM

CSL | ECO DOWNLIGHTS

Spec-00273 NEW ECO 5", V-9.0 Revised 05/15/24

Project: _____


Type: _____

Note: _____

ECO 5" LED DOWNLIGHT



ED5ANC, ED5LANC

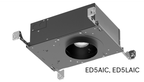


ED5AIC, ED5LAIC



ED5NC, ED5LNIC



ED5RM, ED5LRIC

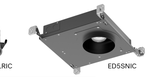

ED5SNIC

LED LIGHT ENGINE	
RATED WATTAGES	29.5W, 24W, 15.3W
DELIVERED LUMENS	Up to 2657 lm
EFFICACY	Up to 104 LPW
CCT @ 90CRI	2700K, 3000K, 3500K, 4000K, Warm Dim
COLOR QUALITY	90+ CRI, 2-Step SDCM
LED LIFETIME	55,000 hours @ L90

SILENT VU™ OPTICS TECHNOLOGY	
OPTICS	50° Installed, 10°, 30°, 80° available
ADJUSTABLE	0° to 45° tilt (Adjustable housings only)
MEDIA	Clear, Solite, Frosted, Linear Spread

POWER SUPPLY	
INPUT VOLTAGE	120/277V 50/60Hz
DIMMING	TRIAC, ELV and 0-10V, dims to 1%
SERVICABILITY	Below ceiling access

DELIVERED LUMENS MATRIX

ED5 (29.5W)	10° OPTIC	30° OPTIC	50° OPTIC	80° OPTIC
2700K (90CRI)	2275 lm	2403 lm	2139 lm	1624 lm
3000K (90CRI)	2458 lm	2597 lm	2311 lm	1755 lm
3500K (90CRI)	2516 lm	2657 lm	2366 lm	1796 lm
4000K (90CRI)	2590 lm	2735 lm	2435 lm	1849 lm

ED5 NIC, RIC (15.3W)	10° OPTIC	30° OPTIC	50° OPTIC	80° OPTIC
Warm Dim (98 CRI, R9>90)	1030 lm	1081 lm	992 lm	723 lm

ED5 AIC, ANC (24W)	10° OPTIC	30° OPTIC	50° OPTIC	80° OPTIC
Warm Dim (98 CRI, R9>90)	1472 lm	1545 lm	1418 lm	1033 lm

ED5L (15.3W)	10° OPTIC	30° OPTIC	50° OPTIC	80° OPTIC
2700K (90CRI)	1348 lm	1424 lm	1268 lm	963 lm
3000K (90CRI)	1457 lm	1539 lm	1370 lm	1040 lm
3500K (90CRI)	1491 lm	1575 lm	1402 lm	1065 lm
4000K (90CRI)	1535 lm	1621 lm	1443 lm	814 lm

ED5S (24W)	10° OPTIC	30° OPTIC	50° OPTIC	80° OPTIC
2700K (90CRI)	1953 lm	2063 lm	1836 lm	1394 lm
3000K (90CRI)	2110 lm	2229 lm	1984 lm	1507 lm
3500K (90CRI)	2160 lm	2282 lm	2031 lm	1542 lm
4000K (90CRI)	2223 lm	2348 lm	2090 lm	1587 lm
Warm Dim (98 CRI, R9>90)	1472 lm	1545 lm	1418 lm	1033 lm

TRIM OPTIONS

- Fixed or Adjustable
- Round or Square
- Standard or Trimless
- Wall Wash
- Wet Location

TRIM COLORS

- White
- Black
- Champagne
- Champagne w/White Flange
- Black w/White Flange
- Silver w/White Flange

HOUSING

- New Construction includes (2) galvanized steel adjustable hanger bars
- Remodel option available
- 5/8"-2" ceiling thickness
- Min Plenum Height: 2 ½" Shallow
- Ceiling Material: Drywall, T-bar grid
- Steel junction box with up to (4) ½" knockouts
- AIC, NIC, RIC, SNIC models are Air Tight. .
- AIC, SNIC models are CCEA compliant. (Note: polycell spray-in foam insulation must be kept 3" from housing)

LISTING/WARRANTY

- cULus Listed
- UL Listed for Damp Location (All Styles)
- IC Rated and Non IC Rated Available
- CCEA Approved (AIC, SNIC Models)
- Five (5) years limited warranty
- UL Listed for Wet Location (Wet Location Trim Style)
- CA Title 24-JA8 Compliant (AIC, NIC, RIC, SNIC Models)
- ASTM E283 Certified Airtight (AIC, NIC, RIC, SNIC Models)

WET LOCATION IC RATED AIRTIGHT WARM DIM DIMMABLE JA8 TITLE 24 2022 READY 5 YEAR LIMITED WARRANTY CCEA GREEN

14508 Nelson Ave. City of Industry, CA 91744 • tel: 626.336.4511 • fax: 626.330.4266 • www.cslighting.com
©2024 Creative Systems Lighting, A Division of Troy-CSL Lighting, Inc. All rights reserved. Subject to change without notice.
Patent: cslighting.com/patents

CSL CREATIVE SYSTEMS LIGHTING

CSL | ECO DOWNLIGHTS

Spec-00273 NEW ECO 5", V-9.0 Revised 05/15/24

Project: _____

Type: _____

Note: _____

ECO 5" LED DOWNLIGHT

ORDER MATRIX

ED5

ECO 5" HOUSING + LIGHT ENGINE ORDER MATRIX (Example: ED5AIC-309050-30S)

HOUSING BASE		LED PERFORMANCE				DRIVER ASSEMBLY	
FAMILY APERTURE	INSTALLATION TYPE	CCT	CRI	OPTIC		WATTAGE	LED DIMMING DRIVER
○ **ED5** ECO 5"	○ **AIC** Adjustable New Construction, IC, CCEA ○ **ANC** Adjustable New Construction ○ **NC** New Construction ○ **RM** Remodel	○ **-27** 2700K ○ **-30** 3000K ○ **-35** 3500K ○ **-40** 4000K	**90** 90 CRI	**50** 50° Flood Installed **10°, 30°, 80°** optics available from the Additional Optics Accessories table below		○ **-30** 29.5W	**S**[1] Universal Dimming Driver (1%-100% 0-10V, TRIAC, ELV, 120V/277V)

FAMILY APERTURE	INSTALLATION TYPE	CCT	CRI	OPTIC	WATTAGE	LED DIMMING DRIVER
○ **ED5** ECO 5" Warm Dim	○ **AIC**[1] Adjustable New Construction, IC, CCEA ○ **ANC**[1] Adjustable New Construction ○ **NIC**[1] New Construction IC ○ **RIC**[1] Remodel IC	**-WD**[2] 1800K-3000K Warm Dim	**98** 98 CRI Warm Dim	**50** 50° Flood Installed **10°, 30°, 80°** optics available from the Additional Optics Accessories table below	○ **-16**[3] 15.3W NIC or RIC Installation Type Only ○ **-25**[1,3] 24W AIC or ANC Installation Type Only	**S**[3] Universal Dimming Driver (1%-100% 0-10V, TRIAC, ELV, 120V/277V)

1. AIC or ANC Installation Type and Wattage Code -25, NIC or RIC Installation Type and Wattage Code -16.
2. Wattage Code -25 Title 24 JA-8 compliant only with 10°, 30° or 50° optic installed.
3. TRIAC, ELV dimming for 120V only.

ED5L

ECO 5" HOUSING + LIGHT ENGINE ORDER MATRIX (Example: ED5LAIC-309050-16S2)

HOUSING BASE		LED PERFORMANCE			DRIVER ASSEMBLY	
FAMILY APERTURE	INSTALLATION TYPE	CCT	CRI	OPTIC	WATTAGE	LED DIMMING DRIVER
○ **ED5L** ECO 5" LPD	○ **AIC** Adjustable New Construction, IC, CCEA ○ **ANC** Adjustable New Construction ○ **NIC** New Construction IC ○ **RIC** Remodel IC	○ **-27** 2700K ○ **-30** 3000K ○ **-35** 3500K ○ **-40** 4000K	**90** 90 CRI	**50** 50° Flood Installed **10°, 30°, 80°** optics available from the Additional Optics Accessories table below	○ **-16** 15.3W	**S2**[1] Phase Control Dimming Driver (1%-100% TRIAC, ELV, 120V/277V)

1. TRIAC, ELV dimming for 120V only.

ED5S

ECO 5" HOUSING + LIGHT ENGINE ORDER MATRIX (Example: ED5SNIC-309050-15S)

HOUSING BASE		LED PERFORMANCE			DRIVER ASSEMBLY	
FAMILY APERTURE	INSTALLATION TYPE	CCT	CRI	OPTIC	WATTAGE	LED DIMMING DRIVER
○ **ED5S** ECO 5" Shallow	**NIC** Shallow Plenum New Construction, IC, CCEA	○ **-27** 2700K ○ **-30** 3000K ○ **-35** 3500K ○ **-40** 4000K	**90** 90 CRI	**50** 50° Flood Installed **10°, 30°, 80°** optics available from the Additional Optics Accessories table below	**-25** 24W	**S**[1] Universal Dimming Driver (1%-100% 0-10V, TRIAC, ELV, 120V/277V)

FAMILY APERTURE	INSTALLATION TYPE	CCT	CRI	OPTIC	WATTAGE	LED DIMMING DRIVER
○ **ED5S** ECO 5" Shallow Warm Dim	**NIC** Shallow Plenum New Construction, IC, CCEA	**-WD** 1800K-3000K Warm Dim	**98** 98 CRI Warm Dim	**50** 50° Flood Installed	**-25** 24W	**S**[1] Universal Dimming Driver (1%-100% 0-10V, TRIAC, ELV, 120V/277V)

1. TRIAC, ELV dimming for 120V only.

14508 Nelson Ave. City of Industry, CA 91744 • tel: 626.336.4511 • fax: 626.330.4266 • www.cslighting.com
©2024 Creative Systems Lighting, A Division of Troy-CSL Lighting, Inc. All rights reserved. Subject to change without notice.
Patent: cslighting.com/patents

CSL CREATIVE SYSTEMS LIGHTING

PRAXIS3
100 Peachtree St NW
Suite 1450 404-875-4500 tel
Atlanta, GA 30303 www.praxis3.com

GEORGIA REGISTERED No. 041508 PROFESSIONAL ENGINEER RAHN ONEAL WILLIAMS

Copyright (c) 2024 Praxis3, LLC

All reports, plans, specifications, computer files, field data, notes and other documents and instruments prepared by Praxis3 shall retain all common law, statutory and other reserved rights, including copyright thereto.

This drawing may not be reproduced in whole or in part without written permission of Praxis3. It is to be returned upon request. Scales as stated are valid on the original drawings.

Rev	Date	Comments
	07/02/2026	PERMIT SET

Client:

FIFTH THIRD BANK

Project Number: 26032
Project Name:

FIFTH THIRD BANK WATSON 1,900 SF

2711 WATSON BOULEVARD
WARNER ROBBINS, GA 31093

Key Plan:

Sheet Title:

EXTERIOR LIGHTING CUTSHEETS


Sheet Number:

E-602

Project Name _____ Qty _____

Type _____ Catalog / Part Number _____



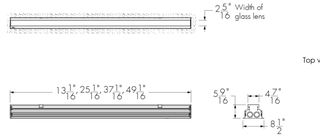


Photometric Summary

	Delivered output (lm)	Intensity (peak cd)
WW	3,634	10,795
8"x8"	4,512	59,238
10"x10"	4,410	33,872
10"x30"	4,586	25,296
10"x60"	3,876	12,062
10"x90"	4,077	6,927
15"x25"	4,346	19,773
30"x30"	4,730	16,886
30"x60"	4,035	5,317
35"x35"	4,612	11,616
50"x80"	4,656	3,904
60"x60"	3,868	3,368
80"x80"	4,548	2,992
90"x90"	4,070	2,132

Based on HO 40K full output, 4ft [1219mm].
DMX/RDM configuration.
2.5° factory-set tilt setting for WW optic, 0° tilt setting for all other optics.
Photometric performance is measured in compliance with IESNA LM-79-08.

Optics

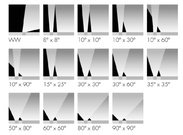

Description

The Lumenfacade Inground is an LED luminaire designed for ground-recessed lighting applications, including asymmetric wall washing, grazing, and linear wayfinding. An innovative, plug and play design simplifies installation, protecting the system from water infiltration and ensuring long-lasting performance. Featuring second generation LED technology, the Lumenfacade Inground is available in four different sizes (12 in, 24 in, 36 in or 48 in), with a wide choice of outputs, color temperatures, color-mixing systems, optics and controls. A unique asymmetric wallwash distribution is also available, providing exceptional uniformity and brightness for walls and signage.

Features

Construction	Walk over compliant up to 500 kg in any type of ground, Walk over compliant up to 1000 kg in concrete
Color and Color Temperature	2200K, 2700K, 3000K, 3500K, 4000K, Red, Green, Blue
Length (nominal)	12 in, 24 in, 36 in, 48 in
Optics	Asymmetric wallwash, 8° x 8°, 10° x 10°, 10° x 30°, 10° x 60°, 10° x 90°, 15° x 25°, 30° x 30°, 30° x 60°, 35° x 35°, 50° x 80°, 60° x 60°, 80° x 80°, 90° x 90°
Tilt Setting (factory set)	0 degrees, 2.5 degrees, 5 degrees, 20 degrees
Optical Option	Internal louver
Options	Anti-slip lens, CE (certification covers European Economic Area)
Power Consumption	5 W/ft (meets ASHRAE standards for linear lighting on building facades - not available for 12 in fixture lengths), 8.5 W/ft (RO version), 15.25 W/ft (HO version). Typically 20% higher for 12 in fixture lengths
Warranty	5-year limited warranty

Specification Sheet

lumenfacade
Inground
LOI

WHITE AND STATIC COLORS

Colors and Color Temperatures

2200K 2700K 3000K 3500K 4000K

Red Green Blue

Controls

ON/OFF 0-10V DALI

lumentalk DMXrdm EcoSystem Enabled

Ratings

IP68 IK10

Certifications

Performance

Maximum Delivered Output	4,730 lm (48 in fixture, 4000K, 30° x 30°, 0° tilt setting, DMX/RDM)
Maximum Delivered Intensity	59,238 cd at nadir (48 in fixture, 4000K, 8° x 8°, 0° tilt setting, DMX/RDM)
Illuminance at Distance	Minimum 1 fc at 243 ft (48 in fixture, 4000K, 8° x 8°, 0° tilt setting, DMX/RDM)
Color Consistency	2 SDCM, 3 SDCM (2200K)
Color Rendering	Minimum CRI 80
Lumen Maintenance	L70 280,000 hrs, L95 35,000 hrs

Physical

Optical Chamber Material	Aluminum
Blockout Material	Polymer recycled PVC reinforced with a stainless steel frame
Trim Material	Anodized aluminum
Lens Material	Tempered glass
End Cap Material	Die cast aluminum
Hardware Material	Stainless steel
Weight	12 in: 7.5 lbs, 24 in: 15.3 lbs, 36 in: 21.4 lbs, 48 in: 27 lbs

Electrical and control

Voltage	120 to 277 volts
Fixture Cable	Power and data in one cable
Leader Cable Conductor	5C #16-5
Connectors	IP68 push-lock
Control	On/Off control, Lumentalk, 0-10V dimming, DALI dimming, Lutron® EcoSystem® Enabled dimming, DMX/RDM enabled
Resolution (DMX/RDM)	Per foot or per fixture (configured with LumenID V3 software), 8-bit or 16-bit

Environmental

Storage Temperature	-40 °F to 185 °F (device must reach start-up temperature value before operating)
Start-up Temperature	-13 °F to 122 °F
Operating Temperature	-40 °F to 122 °F
Ingress Protection Rating	IP68 rated for up to 1 ft, not suitable for permanent immersion applications
Impact Resistance Rating	IK10

Accessories (order separately)

Cables	Lumenfacade Inground Leader Cable, Lumenfacade Inground Jumper Cable
Electrical Accessories	Lumenfacade Inground Junction Box

lumenpulse™ 1220 Marie-Victorin Blvd., Longueuil, QC, J4G 2H9, CA info@lumenpulse.com www.lumenpulse.com T United States 617.307.5700 | Canada 1.877.937.3003 | 514.937.3003 www.lumenpulse.com/products/2556 F 514.937.6289

LMPG Inc., reserves the right to make changes to this product at any time without prior notice and such modification shall be effective immediately
2022.12.19 copyright © 2022 LMPG Inc.
EM - R24

PRAXIS3

100 Peachtree St NW
Suite 1450
Atlanta, GA 30303

404-875-4500 tel
www.praxis3.com

GEORGIA REGISTERED No. 044560 PROFESSIONAL ENGINEER RAHN ONEAL WILLIAMS

Copyright (c) 2024 Praxis3, LLC

All reports, plans, specifications, computer files, field data, notes and other documents and instruments prepared by Praxis3 shall retain all common law, statutory and other reserved rights, including copyright thereto.

This drawing may not be reproduced in whole or in part without written permission of Praxis3. It is to be returned upon request. Scales as stated are valid on the original drawings.

Rev	Date	Comments
	07/02/2026	PERMIT SET

Client:

FIFTH THIRD BANK

Project Number: 26032
Project Name:

FIFTH THIRD BANK WATSON 1,900 SF

2711 WATSON BOULEVARD
WARNER ROBBINS, GA 31093

Key Plan:

Sheet Title:

EXTERIOR LIGHTING CUTSHEETS

Sheet Number:

E-603

6/30/2026 2:32:09 PM

(NEW)

PANEL PP

VOLTAGE: 208 / 120 **AMP: 400**
PHASE: 3 **MAIN: MCB**

DESCRIPTION	KW	BKR	CK	PH	CK	BKR	KW	DESCRIPTION
RTU-1	15.6	90/3	1	A	2	30/3	0.0	SPD
-----	15.6	---	3	B	4	---	0.0	-----
-----	15.6	---	5	C	6	---	0.0	-----
RTU-1	15.6	90/3	7	A	8	30/2	2.3	CU-1/FCU-1
-----	15.6	---	9	B	10	---	2.3	-----
-----	15.6	---	11	C	12	20/2	1.3	WH-WATER HEATER
SPACE		---	13	A	14	---	1.3	-----
SPACE		---	15	B	16	---		SPACE
SPACE		---	17	C	18	---		SPARE
SPACE		---	19	A	20	---		SPARE
SPACE		---	21	B	22	---		SPARE
SPACE		---	23	C	24	---		SPARE
PANEL RP-A	12.2	225/3	25	A	26	---		
-----	13.6	---	27	B	28	---		SPACE SUBFEED SECTION
-----	16.9	---	29	C	30	---		

NOTE: PROVIDE EQUIPMENT GROUND BUS

Phase A Load (kVA)	46.8	Connected kVA	143.0	100%	A-B Balance
Phase B Load (kVA)	47.0	Dem. kVA	129.2	95%	B-C Balance
Phase C Load (kVA)	49.2	Dem. Amps	358.8	95%	C-A Balance

(NEW)

PANEL RP-A

VOLTAGE: 208 / 120 **AMP: MLO**
PHASE: 3 **MAIN: 225**

	DESCRIPTION	KW	BKR	CK	PH	CK	BKR	KW	DESCRIPTION	
	MISC. FIRE ALARM CONTROL PANEL	0.2	20/1	1	A	2	20/1	0.4	LTG-BACK OF HOUSE	
	LTG - PARPET LIGHTING	0.5	20/1	3	B	4	20/1	0.4	LTG-BUILDING CANOPY	
	LTG - ENTRY/WEATHER VESTIBULE	0.1	20/1	5	C	6	20/1	1.2	SIGN-BUILDING SIGN - BACK	
	REC - EMPLOYEE LOUNGE	0.4	20/1	7	A	8	20/1	0.1	LTG-TRANSACTION BAR	
	LTG - RELAXED SEATING	0.2	20/1	9	B	10	20/1	0.5	LTG VESTIBULE	
	SIGN-BUILDING SIGN - FRONT	1.2	20/1	11	C	12	20/1	0.9	REC-PRINTER TRANSACTION	
	REC - COPIER LOBBY	0.8	20/1	13	A	14	20/1	0.0	MISC-LIGHTING CONTROL PANEL	
	LTG - ELEC/IT/MEETING/BOOTHS	0.2	20/1	15	B	16	20/1	0.7	REC-RESTROOM/JAN	
	REC - BOOTH 104	0.5	20/1	17	C	18	20/1	0.9	REC-MEETING ROOM	
#	REC - REFIGERATOR	1.2	20/1	19	A	20	20/1	0.5	MISC-DDCV HOTBOX	*
	REC - WORK ROOM	0.4	20/1	21	B	22	20/1	0.4	REC-PRINTER -TRANSACTION	
	MISC - MECHOSHADES	0.5	20/1	23	C	24	20/1	0.2	REC-TECH WALL/GATHERING	
	MISC - RECIRCULATING PUMP	0.2	20/1	25	A	26	20/1	0.3	MISC-DOOR MOTOR/PUSH...	
	MISC - CONDENSATE PUMP	0.1	20/1	27	B	28	20/1	1.5	REC-TCR TRANSACTION BAR	
	MID- IRRIGATION BACKFLOW	0.5	20/1	29	C	30	20/1	1.1	REC-QUAD ELEC/IT	
	REC - TRANSACTION BAR	0.7	20/1	31	A	32	20/1	0.4	REC-ROOF	
	REC - TRANSACTION BAR	0.7	20/1	33	B	34	20/2	0.0	LTG-LIGHT POLES	
	MISC-DOOR MOTOR/PUSH...	0.3	20/1	35	C	36	---	0.0	------	
	REC-TRANSACTION	0.4	20/1	37	A	38	20/1	1.8	MISC-DRIVE-UP ATM	
	REC-VESTIBULE/ELEC/IT	0.4	20/1	39	B	40	20/1	0.5	MISC-VTM	
	REC-TECH WALL	0.4	20/1	41	C	42	20/1	0.5	REC-PHONE RM	
	REC-EMPLOYEE LOUNGE	0.5	20/1	43	A	44	20/1	1.2	SIGN-BUILDING SIGN - BACK	
	REC-QUAD ELEC/IT	1.4	20/1	45	B	46	20/1	1.1	REC-QUAD ELEC/IT	
	MISC-CRITICAL LIGHTING...	0.2	20/1	47	C	48	20/1	1.5	REC-DISH WASHER	#
	MISC-MECHOSHADES-MEETING..	0.5	20/1	49	A	50	20/1	0.7	REC-NIGHT DEPOSITORY	
	REC-RELAXED SEATING	0.5	20/1	51	B	52	20/1	1.4	REC-QUAD ELEC/IT	
	REC-MICROWAVE LOUNGE	1.5	20/1	53	C	54	20/1	0.4	REC-LIBRARY COUNTER	
	MISC-VAT BLOWER	0.5	20/1	55	A	56	20/1	0.2	MISC-DTOPEN/CLOSE SIGN	
	MISC-LIGHTING CONTACTOR	0.2	20/1	57	B	58	20/1	0.5	MISC-TRANSAC MECHOSHADES	
	REC-LIBRARY COUNTER	0.4	20/1	59	C	60	20/1	0.6	LTG-DRIVE UP ATM TOPPER	
	REC-PHONE RM	0.2	20/1	61	A	62	20/1	0.6	LTG-DRIVE UP ATM TOPPER	
	REC-TRANSACTION DISPLAY	0.4	20/1	63	B	64	20/1	0.5	MISC-BOOTH MECHOSHADES	
	LTG-LIGHT POLES	0.0	20/2	65	C	66	20/1	0.9	REC-WORK ROOM	
	-----	0.0	---	67	A	68	20/1	0.2	REC-DRINKING FOUNTAIN	#
	MISC-VAT DIVERTER	0.5	20/1	69	B	70	20/1	0.2	MISC-IRRIGATION CONTROL	
	REC-ADA COUNTER	0.9	20/1	71	C	72	20/1	1.0	OPEN/CLOSE SIGN	
	LTG-ATM CANOPY	0.1	20/1	73	A	74	20/1	0.1	LIGHTING CONTACTOR	
	REC-WORK 111	0.4	20/1	75	B	76	20/1		SPARE	
	SIGN-MONUMENT SIGN	1.2	20/1	77	C	78	20/1		SPARE	
	REC-MONUMENT SIGN RECEPT	0.2	20/1	79	A	80	20/1		SPARE	
	SPARE		20/1	81	B	82	20/1		SPARE	
	SPARE		20/1	83	C	84	20/1		SPARE	

NOTE: PROVIDE EQUIPMENT GROUND BUS
- PROVIDE CONNECTION TO NEW GFCI CIRCUIT BREAKER.
* - PROVIDE CONNECTION TO NEW GFPE CIRCUIT BREAKER.

Phase A Load (kVA)	12.2	Connected kVA	42.6	90%	A-B Balance
Phase B Load (kVA)	13.6	Dem. kVA	31.4	81%	B-C Balance
Phase C Load (kVA)	16.9	Dem. Amps	87.1	72%	C-A Balance

PANELBOARD NOTES:

1. PROVIDE PANELBOARD AS SPECIFIED ON ELECTRICAL PANEL SCHEDULES AND RISER DIAGRAM.
2. CONTRACTOR SHALL ENSURE ALL NEC WORKING SPACE AND DEDICATED EQUIPMENT SPACE CLEARANCES ARE PROVIDED PER NEC 110. IF FIELD CONDITIONS DO NOT ALLOW FOR ADEQUATE CLEARANCE AT THE LOCATION SHOWN ON THE PLANS, THE CONTACTOR SHALL PROPOSE AN ALTERNATE LOCATION FOR REVIEW AND APPROVAL BY ENGINEER PRIOR TO ROUGH-IN OF PANEL.
3. FIELD COORDINATE INSTALLATION WITH OTHER TRADES TO ENSURE NO FOREIGN SYSTEMS ARE LOCATED WITHIN THE DEDICATED EQUIPMENT SPACE OF THE ELECTRICAL EQUIPMENT.
4. ALL BUSING SHALL BE COPPER.
5. BOLT-ON BREAKERS ONLY.
6. PROVIDE DOOR-IN-DOOR TRIM.
7. PROVIDE TYPEWRITTEN CIRCUIT DIRECTORY CARD.
8. ALL PANELBOARDS SHALL BE SUPPLIED FROM THE SAME MANUFACTURER.
9. IN EXISTING INSTALLATIONS, NEW CIRCUIT BREAKERS SHALL MATCH EXISTING IN TYPE AND AIC RATING, UNO.
10. LOAD TYPES IN DESCRIPTION AS FOLLOWS:

BOLD TEXT	NEW LOAD, WIRE, CONDUIT, CIRCUIT BREAKER(AS APPLICABLE)
GREY TEXT	EXISTING LOAD, WIRE, CONDUIT, CIRCUIT BREAKER(AS APPLICABLE) TO REMAIN
(OLD X-#)	RELOCATED CIRCUIT FROM OLD PANEL 'X', CIRCUIT '#'
CLG	COOLING
EWH	ELECTRIC WATER HEATER
HTG	HEATING
KIT	KITCHEN
LTG	LIGHTING
MISC	MISCELLANEOUS
MTR	MOTOR
REC	RECEPTACLE
REF	REFRIGERATION

11. CIRCUIT BREAKER TYPE ABBREVIATIONS ARE AS FOLLOWS:

AFCI	ARC-FAULT CIRCUIT INTERRUPTER
F/RED	RED MARKING & "FIRE ALARM CIRCUIT"
GFCI	GROUND-FAULT CIRCUIT INTERRUPTER
GFPE	30 mA EQUIPMENT GROUND FAULT PROTECTION
HT2	HANDLE TIE FOR SHARED NEUTRAL CIRCUIT (2 POLE)
HT3	HANDLE TIE FOR SHARED NEUTRAL CIRCUIT (3 POLE)
L/ON	LOCKABLE "LOCK ON" HANDLE HARDWARE
L/OFF	"LOCK OFF"
TAN	TANDEM
SHNT	SHUNT TRIP
SWD	SWITCH DUTY RATED
SWN	SWITCHED NEUTRAL

12. CIRCUIT BREAKER FURNISHED AS FOLLOWS:

ETR	EXISTING TO REMAIN
FW	FACTORY WIRED
NEW	NEW TO MATCH EXISTING
REM	REMOVE EXISTING AND PROVIDE NEW

13. LOAD FUNCTION AS FOLLOWS:

CONT	CIRCUIT CONTROLLED BY CONTRACTOR
HOOD	CIRCUIT CONTROLLED BY HOOD FIRE SUPPRESSION SYSTEM
T/C	CIRCUIT THRU TIME CLOCK
PHO	CIRCUIT THRU PHOTOCELL
LCP	CIRCUIT THRU LIGHTING CONTROL PANEL
L/C	CIRCUIT THRU LIGHTING CONTACTOR

PRAXIS3

100 Peachtree St NW
Suite 1450
Atlanta, GA 30303
404-875-4500 tel
www.praxis3.com

GEORGIA REGISTERED No. 041508 PROFESSIONAL ENGINEER RAHN ONEAL WILLIAMS

Copyright (c) 2024 Praxis3, LLC

All reports, plans, specifications, computer files, field data, notes and other documents and instruments prepared by Praxis3 shall retain all common law, statutory and other reserved rights, including copyright thereto.

This drawing may not be reproduced in whole or in part without written permission of Praxis3. It is to be returned upon request. Scales as stated are valid on the original drawings.

Rev	Date	Comments
	07/02/2026	PERMIT SET

Client:
FIFTH THIRD BANK

Project Number: 26032
Project Name:
FIFTH THIRD BANK WATSON
1,900 SF

2711 WATSON BOULEVARD
WARNER ROBBINS, GA 31093

Key Plan:

Sheet Title:
ELECTRICAL PANEL SCHEDULES

Sheet Number:
E-610

6/30/2026 2:32:09 PM



1 E-700 ELECTRICAL DEVICE PLAN
1/4" = 1'-0"

6/30/2026 2:32:10 PM

PRAXIS3

100 Peachtree St NW
Suite 1450
Atlanta, GA 30303

404-875-4500 tel
www.praxis3.com

GEORGIA REGISTERED No. 041508 PROFESSIONAL ENGINEER RAHN ONEAL WILLIAMS

Copyright (c) 2024 Praxis3, LLC

All reports, plans, specifications, computer files, field data, notes and other documents and instruments prepared by Praxis3 shall retain all common law, statutory and other reserved rights, including copyright thereto.

This drawing may not be reproduced in whole or in part without written permission of Praxis3. It is to be returned upon request. Scales as stated are valid on the original drawings.

Rev	Date	Comments
	07/02/2026	PERMIT SET

Client:
FIFTH THIRD BANK


Project Number: 26032
Project Name:
FIFTH THIRD BANK WATSON 1,900 SF

2711 WATSON BOULEVARD
WARNER ROBBINS, GA 31093


Key Plan:

Sheet Title:
ELECTRICAL DEVICE PLAN


Sheet Number:
E-700

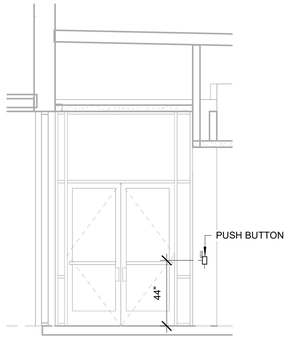


4 E-701 ELEVATION ENTRY 101/2
1/4" = 1'-0"

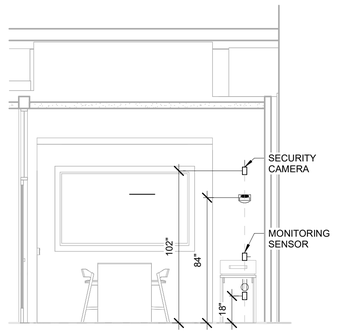


3 E-701 ELEVATION ENTRY 101/1
1/4" = 1'-0"

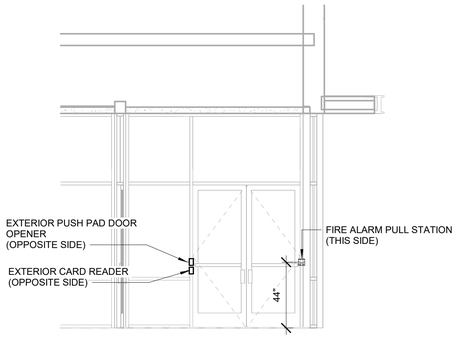


2 E-701 ELEVATION WEATHER VESTIBULE 100/2
1/4" = 1'-0"

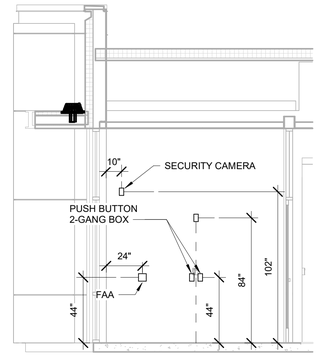


1 E-701 ELEVATION WEATHER VESTIBULE 100/1
1/4" = 1'-0"

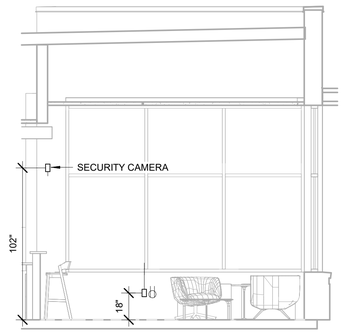


8 E-701 ELEVATION RELAXED SEATING 102/1
1/4" = 1'-0"

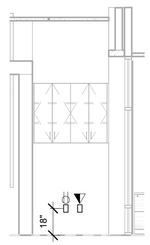


7 E-701 ELEVATION GATHERING AREA
1/4" = 1'-0"

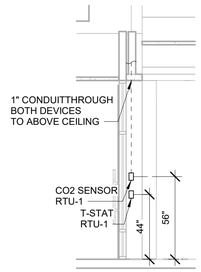


6 E-701 ELEVATION GATHERING AREA 103/3
1/4" = 1'-0"

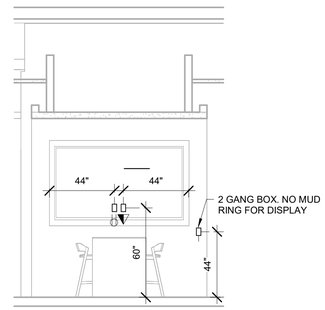


5 E-701 ELEVATION GATHERING AREA 103/1
1/4" = 1'-0"

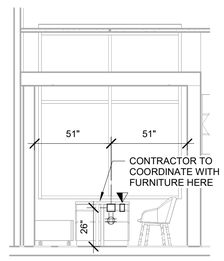

11 E-701 ELEVATION BOOTH 104/2
1/4" = 1'-0"

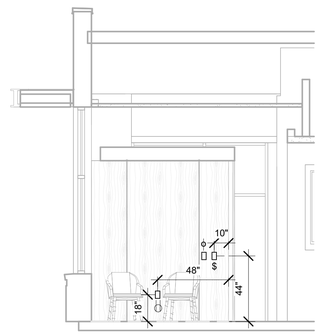

10 E-701 ELEVATION BOOTH 104/1
1/4" = 1'-0"

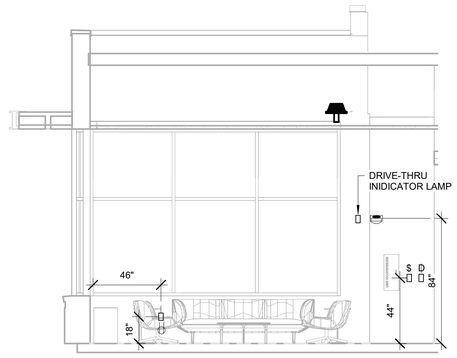

9 E-701 ELEVATION RELAXED SEATING 102/2
1/4" = 1'-0"

6/30/2026 2:32:13 PM

PRAXIS3
100 Peachtree St NW
Suite 1450
Atlanta, GA 30303
404-875-4500 tel
www.praxis3.com

GEORGIA REGISTERED No. 041408 PROFESSIONAL ENGINEER RAHN ONEAL WILLIAMS

Copyright (c) 2024 Praxis3, LLC

All reports, plans, specifications, computer files, field data, notes and other documents and instruments prepared by Praxis3 shall retain all common law, statutory and other reserved rights, including copyright thereto.

This drawing may not be reproduced in whole or in part without written permission of Praxis3. It is to be returned upon request. Scales as stated are valid on the original drawings.

Rev	Date	Comments
	07/02/2026	PERMIT SET

Client:
FIFTH THIRD BANK


Project Number: 26032
Project Name:
FIFTH THIRD BANK WATSON 1,900 SF

2711 WATSON BOULEVARD
WARNER ROBBINS, GA 31093


Key Plan:

Sheet Title:
ELECTRICAL ELEVATIONS


Sheet Number:
E-701

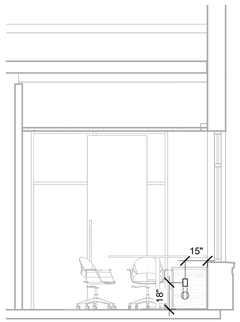


4 E-702 ELEVATION MEETING ROOM 105/4
1/4" = 1'-0"

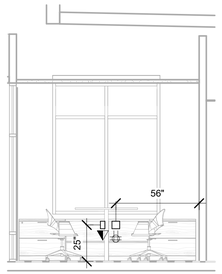


3 E-702 ELEVATION MEETING ROOM 105/3
1/4" = 1'-0"

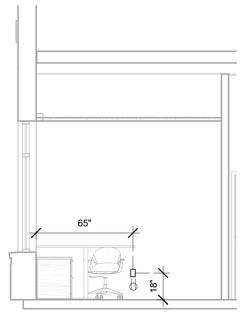


2 E-702 ELEVATION MEETING ROOM 105/2
1/4" = 1'-0"

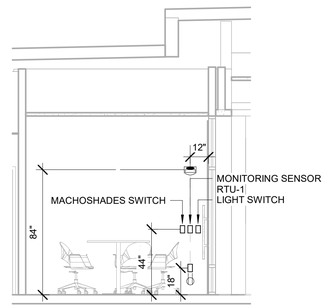


1 E-702 ELEVATION MEETING ROOM 105/1
1/4" = 1'-0"

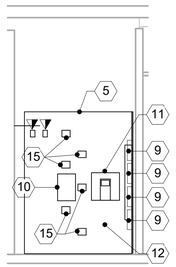


8 E-702 ELEVATION ELEC/IT 106/4
1/4" = 1'-0"

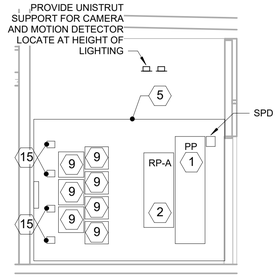

7 E-702 ELEVATION ELEC/IT 106/3
1/4" = 1'-0"

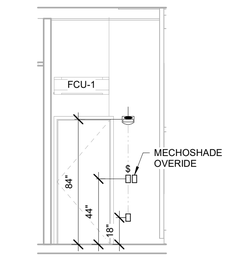

6 E-702 ELEVATION ELEC/IT 106/2
1/4" = 1'-0"

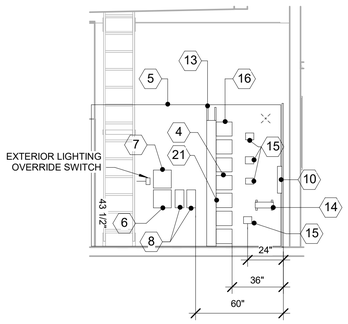


5 E-702 ELEVATION ELEC/IT 106/1
1/4" = 1'-0"

KEYED NOTES:


1. PANEL PP
2. PANEL RP-A SEC I
3. NOT USED
4. DATA RACK
5. PLYWOOD BACKBOARD: PROVIDE 8' X (LENGTH AS REQUIRED) X 3/4" FIRE-RATED PLYWOOD BACKBOARDS MOUNTED VERTICALLY ALONG ALL NER ROOM WALLS. UL FIRE RATING LABEL SHALL REMAIN VISIBLE AFTER INSTALLATION.
6. LIGHTING CONTROL PANEL
7. DIMMER PANEL
8. LIGHTING CONTACTOR
9. SECURITY PANEL
10. TELECOMMUNICATION BOX
11. FIRE ALARM CONTROL PANEL: FIRE ALARM CONTROL PANEL WITH TOP OF CABINET NOT TO EXCEED 72" ABOVE THE FINISHED FLOOR.
12. DIGITAL ALARM COMMUNICATOR TRANSMITTER
13. CABLE TRAY
14. GROUND BUS BAR: PROVIDE A 12" X 2" X 1/4" COPPER GROUND BAR WITH STANDOFF INSULATORS ON TELEPHONE BACKBOARD. PROVIDE #2 AWG COPPER GROUND ROUTED IN 1" CONDUIT FROM TELEPHONE BACKBOARD GROUNDING BAR TO ELECTRICAL SERVICE GROUNDING ELECTRODE SYSTEM. COORDINATE EXACT LOCATION ON BACKBOARD WITH TELEPHONE SERVICE PROVIDER.
15. QUAD RECEPTACLE
16. PROVIDE A PANDUIT (PART NUMBER: R2P) TWO POST CABLE MANAGEMENT RACK SYSTEM IN IT/ELEC ROOM
17. PROVIDE PANDUIT (PART NUMBER: WMPV45E) VERTICAL CABLE MANAGER AND PANDUIT (PART NUMBER: WMP1E) HORIZONTAL CABLE MANAGER IN ELECTRICAL/IT ROOM AS REQUIRED.
18. PROVIDE 18" STEEL HOMACO LADDER RACK ABOVE TBB AT 90" AFF. BOND ALL SECTIONS WITH #6 AWG GREEN INSULATED COPPER GROUND TO GROUND BUS ON TBB.
19. PROVIDE (1) CAT 6 CABLE RUN FROM RACK TO DRIVE UP EQUIPMENT MATRIX LOCATION. COORDINATE EXACT LOCATION WITH OWNER VENDOR.
20. ELECTRICAL CONTRACTOR TO PULL CABLES FOR MOOD MEDIA. EQUIPMENT PROVIDED BY OWNER

ELEC/IT 106 ELEVATION GENERAL NOTES:


1. ELEVATIONS ARE SHOWN FOR REFERENCE ONLY. COORDINATE WITH RESPECTIVE EQUIPMENT SUPPLIERS FOR EXACT DIMENSIONS, REQUIRED CLEARANCES, LOCATIONS, MOUNTING HEIGHTS, AND ROUGH-IN REQUIREMENTS AND ADJUST IN FIELD AS REQUIRED.
2. MAINTAIN A MINIMUM OF 36" CLEAR IN THE FRONT OF THE ELECTRICAL PANELS PER NEC 110.26.
3. EXPOSED CONDUIT IN ELECTRICAL/IT ROOM SHALL BE EMT; MC CABLE SHALL NOT BE EXPOSED.
4. ALL WIRING DEVICES IN NEC AND ELECTRICAL ROOM SHALL BE FLUSH MOUNTED.
5. LOW VOLTAGE CONDUITS SHALL BE PROVIDED WITH PLASTIC INSULATED CONDUIT BUSHINGS ON EACH END AND NYLON PULL STRING.

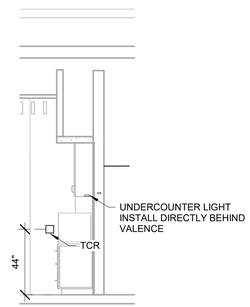


12 E-702 ELEVATION LIBRARY 107/3
1/4" = 1'-0"

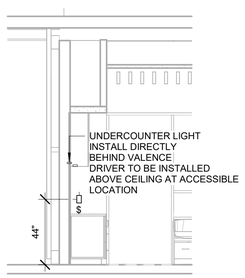

11 E-702 ELEVATION LIBRARY 107/2
1/4" = 1'-0"

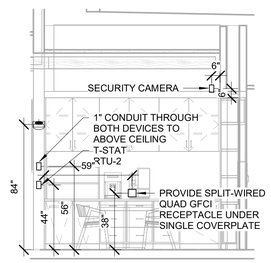

10 E-702 ELEVATION LIBRARY 107/1
1/4" = 1'-0"

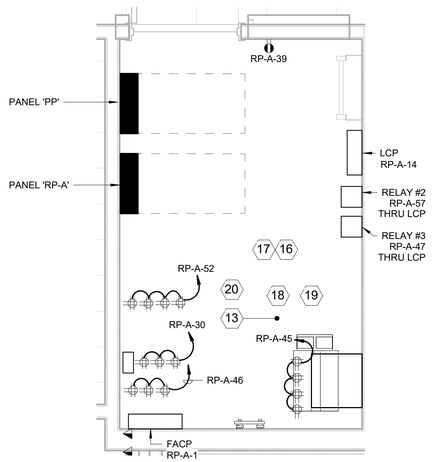

9 E-702 ENLARGED ELEC/IT ROOM 1
1/2" = 1'-0"

PRAXIS3
100 Peachtree St NW
Suite 1450
Atlanta, GA 30303
404-875-4500 tel
www.praxis3.com

GEORGIA REGISTERED No. 041508 PROFESSIONAL ENGINEER RAHN ONEAL WILLIAMS

Copyright (c) 2024 Praxis3, LLC

All reports, plans, specifications, computer files, field data, notes and other documents and instruments prepared by Praxis3 shall retain all common law, statutory and other reserved rights, including copyright thereto.

This drawing may not be reproduced in whole or in part without written permission of Praxis3. It is to be returned upon request. Scales as stated are valid on the original drawings.

Rev	Date	Comments
	07/02/2026	PERMIT SET

Client:
FIFTH THIRD BANK

Project Number: 26032
Project Name:
FIFTH THIRD BANK WATSON 1,900 SF


2711 WATSON BOULEVARD
WARNER ROBBINS, GA 31093

Key Plan:

Sheet Title:
ELECTRICAL ELEVATIONS

Sheet Number:
E-702


6/30/2026 2:32:16 PM

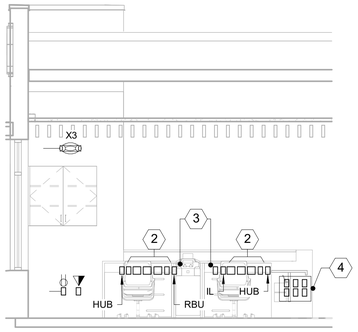


NOTE:

1. TRANSACTION BAR DEVICE LAYOUT IS DIAGRAMMATIC FOR REFERENCE AND NOT TO SCALE. COORDINATE WITH MILLWORK SHOP DRAWINGS AND ARCHITECTURAL ELEVATIONS FOR EXACT PLACEMENT.
2. ELECTRICAL CONTRACTOR SHALL SUPPORT ALL LOW VOLTAGE WIRING AND TIE TOGETHER MULTIPLE RUNS CABLES WITH VELCRO AS REQUIRED FOR A NEAT INSTALLATION.
3. ELECTRICAL CONTRACTOR SHALL COORDINATE WITH MILLWORK SHOP DRAWINGS TO PLAN ALL CONDUIT ROUTING. SUPPORT ALL RACEWAYS PER NEC.


4 E-703 ELEVATION TRANSACTION 108/4
1/4" = 1'-0"

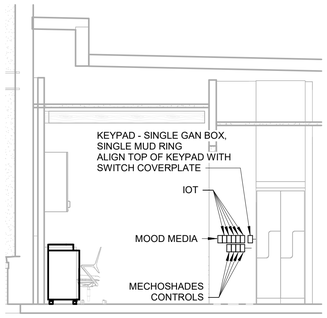

3 E-703 ELEVATION TRANSACTION 108/3
1/4" = 1'-0"

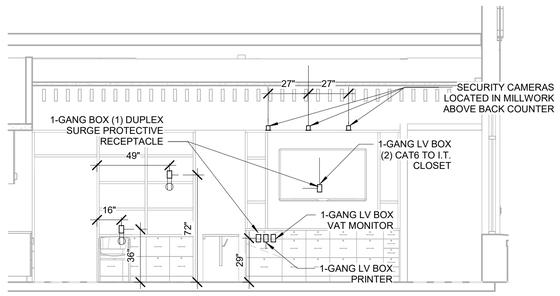


2 E-703 ELEVATION TRANSACTION BAR 108/2
1/4" = 1'-0"

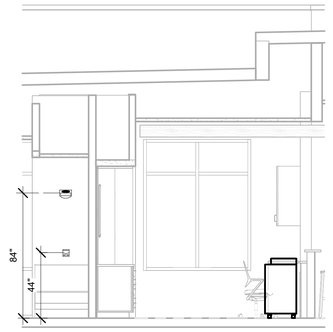


1 E-703 ELEVATION TRANSACTION 108/1
1/4" = 1'-0"

KEYED NOTES:


1. TCR POWER & DATA OUTLET - MOUNT SO THAT TCR CAN BE PLACED UP AGAINST THE MILLWORK AND SO THAT THE POWER & DATA CORD OF THE EQUIPMENT WILL REACH THE OUTLET. IDENTIFY RECEPTACLE 'TCR'.
2. OUTLETS SHALL BE PLACED IN OPENINGS MADE AVAILABLE FROM MILLWORK. DIAGRAM SHOWS GENERAL PLACEMENT OF OUTLETS WITHIN THE OPENINGS. COORDINATE WITH MILLWORK SHOP DRAWINGS AND ARCHITECTURAL ELEVATIONS FOR EXACT PLACEMENT.
3. ALL POWER WIRING AND DATA WIRING SHALL BE RUN THROUGH OPENINGS PROVIDED BY MILLWORK PROVIDER. GENERAL LOCATION - COORDINATE WITH MILLWORK SHOP DRAWINGS AND ARCHITECTURAL ELEVATIONS FOR EXACT DIMENSIONS.
4. RECESSED ELECTRICAL BOXES (ARLINGTON BOXES TVBS507 3-GANG) FOR POWER & DATA - SEE NOTES ON FLOOR PLAN FOR REQUIREMENTS.

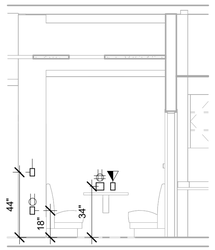


8 E-703 ELEVATION EMPLOYEE LOUNGE 110/4
1/4" = 1'-0"

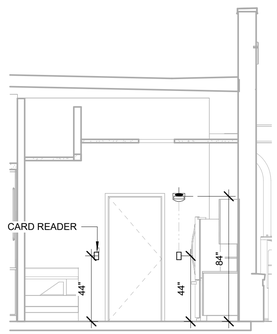


7 E-703 ELEVATION EMPLOYEE LOUNGE 110/3
1/4" = 1'-0"

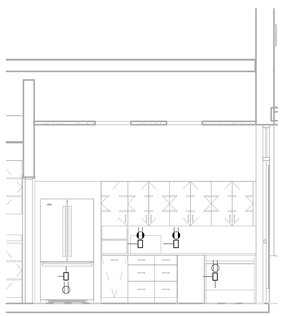


6 E-703 ELEVATION EMPLOYEE LOUNGE 110/2
1/4" = 1'-0"

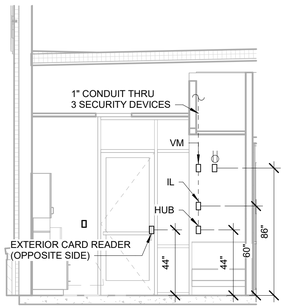


5 E-703 ELEVATION EMPLOYEE LOUNGE 110/1
1/4" = 1'-0"

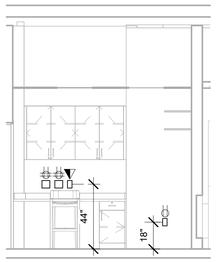

11 E-703 ELEVATION WORK ROOM 111/3
1/4" = 1'-0"

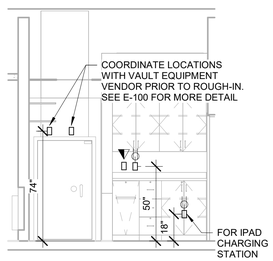

10 E-703 ELEVATION WORK ROOM 111/2
1/4" = 1'-0"

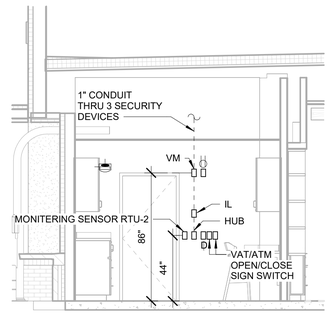

9 E-703 ELEVATION WORK ROOM 111/1
1/4" = 1'-0"

6/30/2026 2:32:19 PM

PRAXIS3
100 Peachtree St NW
Suite 1450
Atlanta, GA 30303
404-875-4500 tel
www.praxis3.com

GEORGIA REGISTERED No. 041508 PROFESSIONAL ENGINEER RAHN ONEAL WILLIAMS

Copyright (c) 2024 Praxis3, LLC

All reports, plans, specifications, computer files, field data, notes and other documents and instruments prepared by Praxis3 shall retain all common law, statutory and other reserved rights, including copyright thereto.

This drawing may not be reproduced in whole or in part without written permission of Praxis3. It is to be returned upon request. Scales as stated are valid on the original drawings.

Rev	Date	Comments
	07/02/2026	PERMIT SET

Client:
FIFTH THIRD BANK


Project Number: 26032
Project Name:
FIFTH THIRD BANK WATSON 1,900 SF

2711 WATSON BOULEVARD
WARNER ROBBINS, GA 31093


Key Plan:

Sheet Title:
ELECTRICAL ELEVATIONS


Sheet Number:
E-703

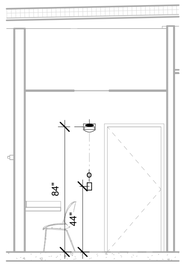


4 E-704 ELEVATION PHONE ROOM 114/1
1/4" = 1'-0"

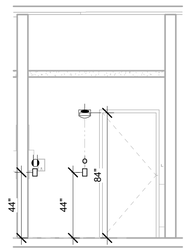


3 E-704 ELEVATION MENS 113/2
1/4" = 1'-0"

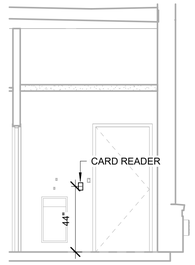


2 E-704 ELEVATION MENS 113/1
1/4" = 1'-0"

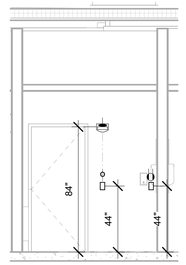


1 E-704 ELEVATION WOMENS 112/1
1/4" = 1'-0"

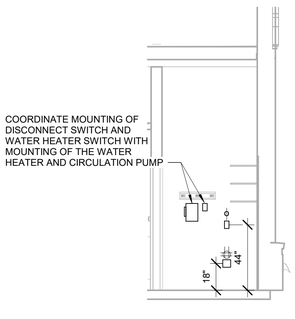


8 E-704 ELEVATION JANITOR 115/2
1/4" = 1'-0"

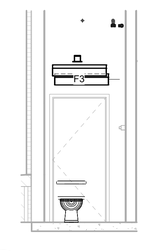


7 E-704 ELEVATION JANITOR 115/1
1/4" = 1'-0"

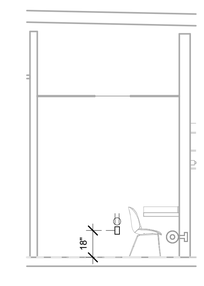


6 E-704 ELEVATION PHONE ROOM 114/3
1/4" = 1'-0"

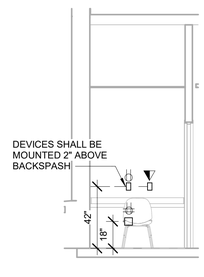


5 E-704 ELEVATION PHONE ROOM 114/2
1/4" = 1'-0"

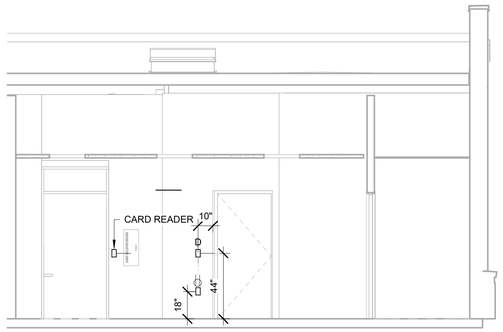

11 E-704 ELEVATION VESTIBULE 116/3
1/4" = 1'-0"

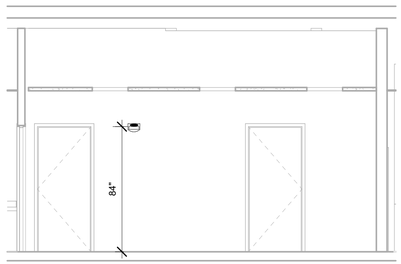

10 E-704 ELEVATION VESTIBULE 116/2
1/4" = 1'-0"

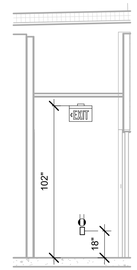

9 E-704 ELEVATION VESTIBULE 116/1
1/4" = 1'-0"

6/30/2026 2:32:21 PM

PRAXIS3

100 Peachtree St NW
Suite 1450
Atlanta, GA 30303

404-875-4500 tel
www.praxis3.com

GEORGIA REGISTERED No. 041508 PROFESSIONAL ENGINEER RAHN ONEAL WILLIAMS

Copyright (c) 2024 Praxis3, LLC

All reports, plans, specifications, computer files, field data, notes and other documents and instruments prepared by Praxis3 shall retain all common law, statutory and other reserved rights, including copyright thereto.

This drawing may not be reproduced in whole or in part without written permission of Praxis3. It is to be returned upon request. Scales as stated are valid on the original drawings.

Rev	Date	Comments
	07/02/2026	PERMIT SET

Client:

FIFTH THIRD BANK

Project Number: 26032
Project Name:

FIFTH THIRD BANK WATSON 1,900 SF

2711 WATSON BOULEVARD
WARNER ROBBINS, GA 31093

Key Plan:

Sheet Title:


ELECTRICAL ELEVATIONS

Sheet Number:

E-704

NOTE:
PREFERRED SUPPLIER FOR SWITCHGEAR IS WESCO.


CONTACT DELENA STUART-WATSON, GLOBAL ACCOUNT MANAGER
TEL: 214-549-1164
EMAIL: DELENA.WATSON@ANIXTER.COM

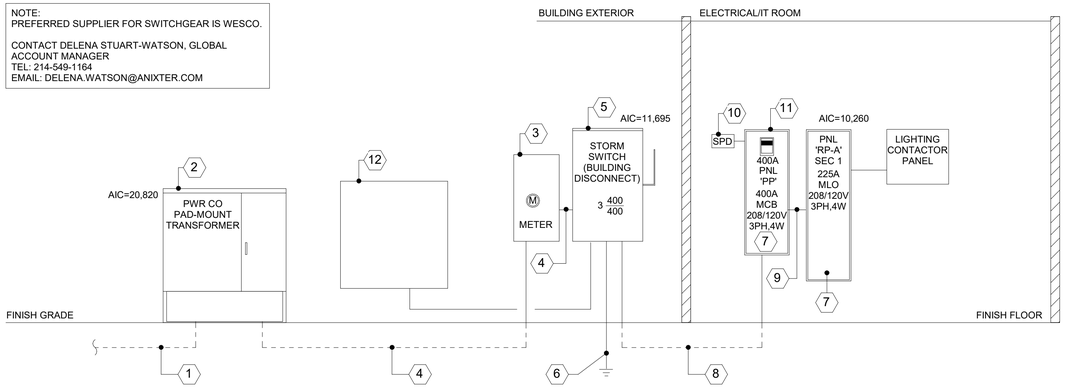

1 E-800 ELECTRICAL RISER DIAGRAM
N.T.S.

KEYED NOTES:

1. ELECTRIC UTILITY PRIMARY FEEDERS: PROVIDE COMPLETE UNDERGROUND CONDUIT SYSTEMS IF REQUIRED BY THE LOCAL POWER COMPANY FROM TRANSFORMER TO POINT OF INTERCEPTION AT EDGE OF PROPERTY LINE. REFER TO ELECTRICAL SITE PLAN FOR ROUTING AND ADDITIONAL REQUIREMENTS.
2. ELECTRIC UTILITY XFMR (PAD-MOUNTED): REFER TO ELECTRICAL SITE PLAN FOR LOCATION AND ADDITIONAL REQUIREMENTS.
3. ELECTRIC UTILITY METER (SELF-CONTAINED): PROVIDE 320A CONTINUOUS 400A MAX, 600V, 3PH, 4W, SELF-CONTAINED METER BASE AND ENCLOSURE. COORDINATE METER BASE SELECTION AND INSTALLATION WITH POWER COMPANY.
4. 400A SERVICE ENTRANCE: PROVIDE 2 SETS OF 4-#3/0 KCMIL EACH IN 4" CONDUIT.
5. STORM SWITCH - MANUAL TRANSFER SWITCH: MANUFACTURED BY ESL POWER SYSTEMS INC, PART# 3042-10V: SFD4-400C-400C-208-311-S-C, 400A, 208Y/120VAC, 65KAIC,3PH, 4W SAFETY INTERLOCK MANUAL TRANSFER SWITCH, WALL MOUNT, TYPE 3R, 14GA GALVANNEALED STEEL, POWDER COATED WRINKLE GRAY (RAL7035). FACTORY WIRED COMPLETE USING INSULATED FLEXIBLE BUS WITH 400A MOLDED CASE 3-POLE C/B FOR UTILITY SIDE (ACCEPTS (2) 2/0-500KCMIL WIRE PER PHASE/NEUTRAL), 400A MOLDED CASE 3-POLE C/B FOR GENERATOR SIDE, MALE CAM-STYLE RECEPTACLES: (1) A-PHASE - BLACK, (1) B-PHASE-RED, (1) C-PHASE-BLUE,(1) NEUTRAL-WHITE, (1) GROUND-GREEN (MATING PLUGS NOT PROVIDED). INCLUDES DEADFRONT, PAD LOCKABLE DOOR WITH STOP AND HANDLE COVER. LOAD WIRE RANGE (2) 2/0-500KCMIL PER PHASE/NEUTRAL. CONDUIT ENTRY AREA THROUGH BOTTOM LEFT SIDE OR LEFT SIDE AT BOTTOM. SUITABLE FOR USE AS SERVICE EQUIPMENT. USE COPPER WIRE. UL/cUL 1008 LISTED.
6. GROUND ELECTRODE CONDUCTOR: PROVIDE #3/0 CU GROUNDING ELECTRODE CONDUCTOR (GEC). TO GROUNDING ELECTRODE SYSTEM CONSISTING OF MIN (2) 3/4" CU CLAD GROUND RODS, BUILDING STEEL, CONCRETE ENCASED ELECTRODE, INTERSYSTEM BONDING JUMPER, AND METALLIC COLD WATER PIPE.
7. ELECTRICAL PANEL: PROVIDE PANELBOARD AS SPECIFIED ON ELECTRICAL PANEL SCHEDULES.
8. 400A FEEDER: PROVIDE 2 SETS OF 4-#3/0 KCMIL, #3 GND EACH IN 4" CONDUIT.
9. 225A FEEDER: PROVIDE 4-#4/0, #4 GND IN 3" CONDUIT.
10. SURGE PROTECTION DEVICE: PROVIDE SURGE PROTECTION DEVICE (SPD) SURGE APT-TE-02-XDS-10-4X-KITFMXF, REFER TO "SPD PANELBOARD INSTALLATION DETAIL" ON SHEET E-501.
11. PROVIDE POWER SCOUT METER, PSHD3, WITH CONNECTION TO THE BUILDING MANAGEMENT SYSTEM AND 400A CTS WITHIN THE MAIN PANEL. PROVIDE ALL CONDUIT AND WIRE TO THE BMS & CONNECT WITH 4#12 & 1#12(G).
COORDINATE WITH STEVE SMITH AT IOT - CONTACT:
STEPHEN SMITH
STEPHENS@IOFTEAM.COM
OFFICE PHONE: 512-649-5142 EXT. 105
DIRECT LINE:
512-686-3978.
12. TEMPORARY GENERATOR WITH OVERCURRENT PROTECTION AND CABLE BY OTHERS

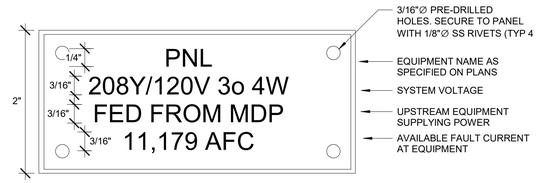




NOTES:

1. ALL ELECTRICAL EQUIPMENT, SUCH AS SWITCHBOARDS, SWITCHGEAR, PANELBOARDS, INDUSTRIAL CONTROL PANELS, METER SOCKET ENCLOSURES, MOTOR CONTROL CENTERS, AND SAFETY DISCONNECT SWITCHES SHALL BE PROVIDED WITH AN ARC FLASH HAZARD WARNING LABEL.
2. THE LABEL SHALL BE OF SUFFICIENT DURABILITY TO WITHSTAND THE ENVIRONMENT INVOLVED.
3. THE LABEL SHALL BE PERMANENTLY AFFIXED TO THE EQUIPMENT AND SHALL NOT BE HAND WRITTEN.
4. THOROUGHLY CLEAN SURFACE PRIOR TO ADHERING LABEL.
5. PROVIDE BRADY B-302 SERIES 3.5"x5" POLYESTER LABEL WITH PERMANENT ACRYLIC ADHESIVE, CATALOG #101950 (5 PACK), #102307 (100 PACK), OR APPROVED EQUAL.

2 ARC FLASH HAZARD WARNING LABEL REQUIREMENTS
N.T.S.

NOTES:

1. ALL DISTRIBUTION EQUIPMENT SUCH AS PANELBOARDS, SWITCHBOARDS, DISCONNECTS, TRANSFORMERS, ETC. SHALL BE PROVIDED WITH AN EQUIPMENT LABEL PER THE REQUIREMENTS OF THIS DETAIL.
2. LABELS SHALL BE 2-PLY ENGRAVED PLASTIC LAMINATE WITH BLACK TYPEFACE LETTERS. LABEL BACKGROUND SHALL FOLLOW THE BELOW COLOR SCHEME:
   A. NORMAL POWER - WHITE
   B. UPS POWER - BLUE
   C. LIFE SAFETY POWER - YELLOW
3. LABEL MATERIAL SHALL BE DURABLE, UV STABLE, RATED FOR OUTDOOR USE, AND ABRASION RESISTANT. WHERE ATTACHED TO NEMA 4X EQUIPMENT, LABELS SHALL IN ADDITION BE CHEMICAL RESISTANT.
4. LABELS SHALL BE PERMANENTLY ATTACHED TO ENCLOSURE COVER WITH RIVETS UNLESS DOING SO COMPROMISES ITS NEMA / IP RATING. LABELS FOR ENCLOSURES WITH WELDED SEAMS AND GASKETED DOORS SUCH AS THOSE RATED NEMA 12 OR NEMA 4 SHALL BE INSTALLED USING PERMANENT WEATHER-, UV-, AND TEMPERATURE-RESISTANT DOUBLE-SIDED MOUNTING TAPE ONLY.
5. A SUBMITTAL WITH A COMPLETE LIST OF EQUIPMENT LABELS SHALL BE PROVIDED FOR ENGINEER APPROVAL PRIOR TO ORDERING.
6. LABELS SHALL INDICATE NO LESS THAN THE FOLLOWING:
   A. EQUIPMENT NAME
   B. THE NOMINAL SYSTEM VOLTAGE WHICH SAID EQUIPMENT IS CONNECTED TO
   C. THE EQUIPMENT NAME SUPPLYING POWER TO SAID EQUIPMENT
   D. THE AVAILABLE FAULT CURRENT AT SAID EQUIPMENT

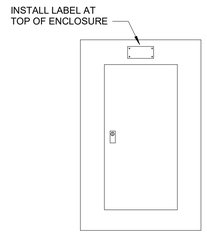

3 EQUIPMENT LABEL DETAIL
N.T.S.

6/30/2026 2:32:22 PM

PRAXIS3
100 Peachtree St NW
Suite 1450
Atlanta, GA 30303
404-875-4500 tel
www.praxis3.com

GEORGIA REGISTERED No. 041508 PROFESSIONAL ENGINEER RAHN ONEAL WILLIAMS

Copyright (c) 2024 Praxis3, LLC

All reports, plans, specifications, computer files, field data, notes and other documents and instruments prepared by Praxis3 shall retain all common law, statutory and other reserved rights, including copyright thereto.

This drawing may not be reproduced in whole or in part without written permission of Praxis3. It is to be returned upon request. Scales as stated are valid on the original drawings.

Rev	Date	Comments
	07/02/2026	PERMIT SET

Client:
FIFTH THIRD BANK


Project Number: 26032
Project Name:
FIFTH THIRD BANK WATSON
1,900 SF

2711 WATSON BOULEVARD
WARNER ROBBINS, GA 31093


Key Plan:

Sheet Title:
ELECTRICAL RISER DIAGRAM

Sheet Number:
E-800

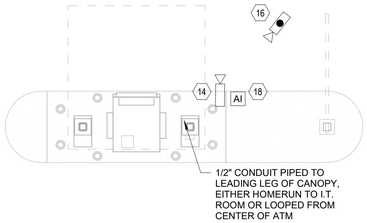

2 E-150 SECURITY PLAN REMOTE DRIVE THRU
1/4" = 1'-0"

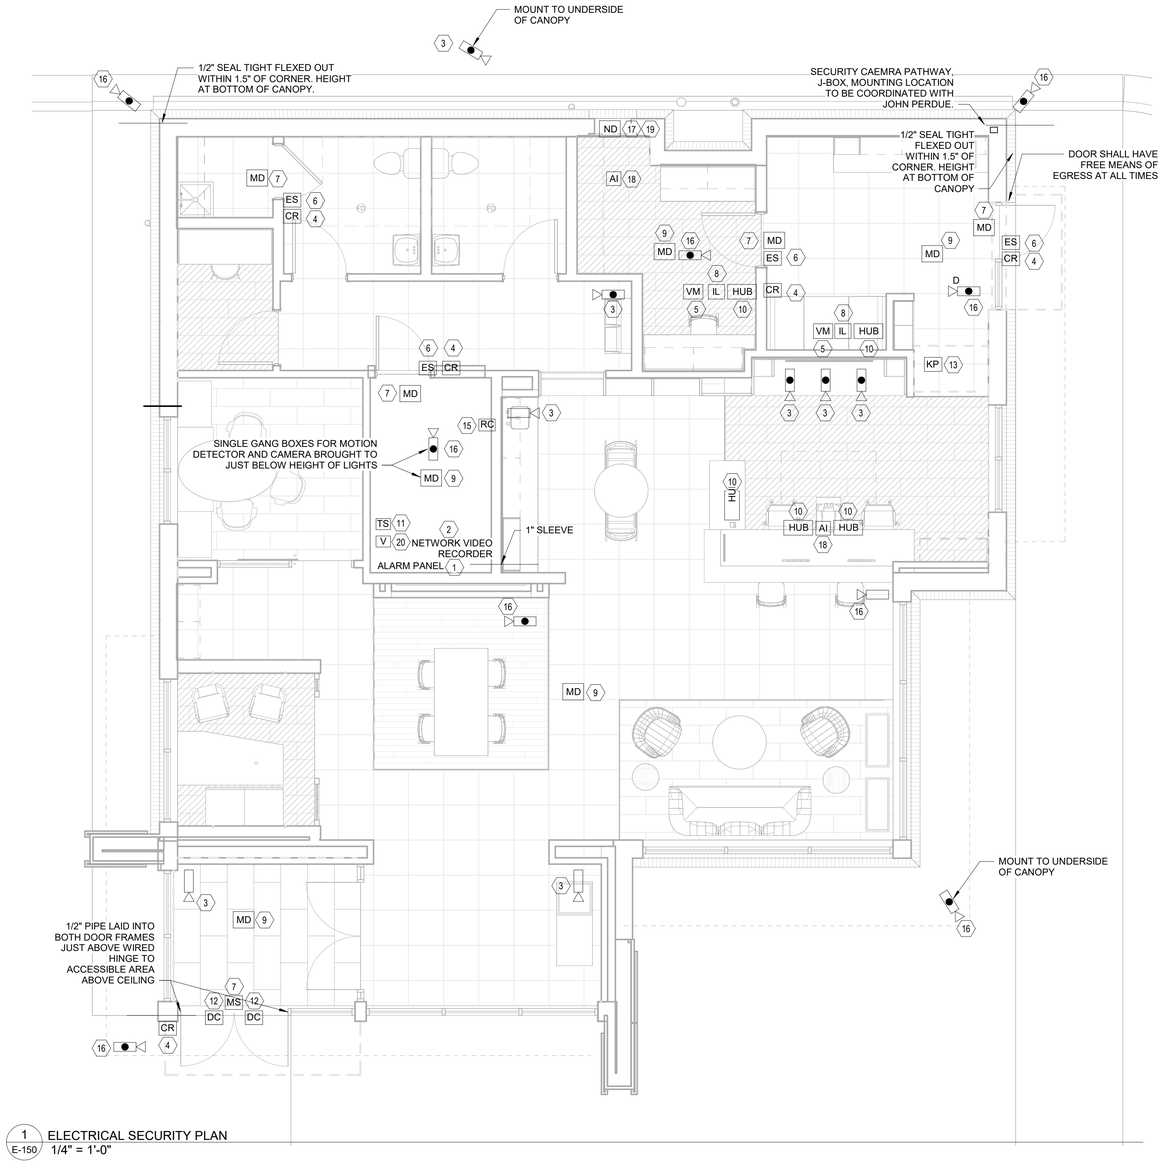

1 E-150 ELECTRICAL SECURITY PLAN
1/4" = 1'-0"

SHEET NOTES:

1. SECURITY DEVICES SHOWING ON THIS SHEET IS FOR COORDINATION PURPOSES ONLY. REFER TO SECURITY DRAWING FOR FINAL LOCATION AND REQUIREMENTS AND PROVIDE ACCORDINGLY.
2. ELECTRICAL CONTRACTOR SHALL PROVIDE ALL RACEWAYS, BOXES, PULLSTRINGS, ETC. SECURITY CABLING SHALL BE BY SECURITY VENDOR.
3. "RED" COLORED WIRE TO BE RESERVED FOR FIRE SYSTEMS AND "YELLOW" WIRES TO BE RESERVED FOR SECURITY SYSTEMS.
4. NOT ALL DEVICES MAY BE USED**
5. ALL CABLES SHALL BE PLENUM RATED
6. SUPPORT DATA / VOICE CABLES ON JHOOKS, 6' O.C., BACK TO THE SECURITY PANEL
7. PROVIDE 3/4" EMT CONDUIT WITH 3/4" BUSHING STUBBED UP TO ACCESSIBLE CEILING AND A 2 GANG BACKBOX FOR THE FOLLOWING: EACH ALARM ACTIVATING DEVICE; EXTERIOR ATM AND / OR NIGHT DEPOSIT; CCTV; CARD READERS; ALL WALL MOUNTED DEVICES.
8. PROVIDE 3/4" C. TO KNOX BOX AND STUB ABOVE TO NEAREST ACCESSIBLE CEILING.
9. ALL EXTERIOR CAMERAS SHALL HAVE A 3/4"C. STUBBED BACK TO THE NEAREST ACCESSIBLE CEILING.
10. ALL EXTERIOR CAMERAS SHALL BE INSTALLED BELOW THE CANOPIES TO MAXIMIZE CAMERA SIGHT LINES CONFIRM FINAL LOCATION WITH SECURITY VENDOR
11. ALL DOORS SHALL HAVE FREE EGRESS. COORDINATE WITH ARCHITECTURAL DOOR HARDWARE.
12. EXTERIOR JUNCTION BOX TO MOUNTED FOR 360 CAMERA TO BE INSTALLED AT CORNERS OF THE BUILDING.

SECURITY DEVICE SCHEDULE

#	DESCRIPTION	WIRE (FOR REFERENCE SEE NOTE A)	INSTALLATION REQUIREMENTS
1	ALARM PANEL	(4) 110VAC DUPLEX	(4) DUPLEX OUTLETS MOUNTED VERTICALLY FROM 6' TO 4' NEXT TO SECURITY PANELS. FIELD VERIFY LOCATION.
2	NETWORK VIDEO RECORDER	(1) 110VAC QUAD	QUAD OUTLET ADJACENT TO DATA RACK. EXACT LOCATION TBD BY SITE.
3	IP DOME CAMERA - INDOOR	CAT6	SINGLE GANG BOX, 2-3/4" ROUND MUD RING, STUB UP INTO ACCESSIBLE AREA ABOVE CEILING. SEE ELEVATION FOR AFF HEIGHT. NO PROVISIONS REQUIRED FOR MOUNTING ON DROP-IN CEILING.
4	CARD READER	22/3 PAIR IN BANANA CABLE	SINGLE GANG BOX, 44" AFF, STUB UP INTO ACCESSIBLE AREA ABOVE CEILING, FLEX FROM BOTTOM OF BOX TO ELECTRIC STRIKE. PROVIDE SLIM/MULLION METAL BACK BOX FOR MOUNTING ON MULLION.
5	VIDEO MONITOR	110VAC OUTLET, RG59 COAX	SINGLE GANG BOX, 86" AFF, SERIALLY PIPED WITH HUB AND IL, STUB UP INTO ACCESSIBLE AREA ABOVE CEILING.
6	ELECTRIC STRIKE WITH LBM	18/4 IN BANANA CABLE	WIRING FROM CARD READER.
7	MOTION DETECTOR (TO SHUNT DOOR CONTACT)	22/4 BANANA CABLE	SINGLE GANG BOX MOUNTED LONG SIDE PARALLEL TO DOOR(S) WITH RING, SEE ELEVATION FOR HEIGHT, NO PROVISIONS REQUIRED FOR MOUNTING ON DROP-IN CEILING TILES.
8	ALARM LAMP/INDICATOR LIGHT	18/2	SINGLE GANG BOX WITH RING, 60" AFF, STUB UP INTO ACCESSIBLE AREA ABOVE CEILING.
9	360 MOTION DETECTOR	22/4	SINGLE GANG BOX WITH ROUND MUD RING IN CEILING, STUB UP INTO ACCESSIBLE AREA ABOVE CEILING, NO PROVISIONS REQUIRED FOR DROP-IN TILE CEILINGS.
10	HOLD UP BUTTON	22/4	FOR TELLER LINE, STUB CONDUIT AT 18" AFF UNDER COUNTERTOP WITH STUB UP INTO ACCESSIBLE AREA ABOVE CEILING. FOR CASH/BREAK ROOMS, SINGLE GANG BOX WITH RING, 44" AFF WITH STUB UP INTO ACCESSIBLE AREA ABOVE CEILING. FOR OFFICE DESK LOCATIONS, SINGLE GANG BOX WITH RING, 18" AFF ON WALL ADJACENT TO DESK WITH STUB UP INTO ACCESSIBLE AREA ABOVE CEILING.
11	TEMPERATURE SENSOR	22/4	FOR ATM ROOM, SINGLE GANG BOX WITH RING, 60" AFF, STUB UP INTO ACCESSIBLE AREA ABOVE CEILING. FOR IT ROOMS, NO PROVISIONS REQUIRED.
12	DOOR CONTACT	22/2 IN BANANA CABLE	1/2" PIPE LAID INTO BOTH DOOR FRAMES JUST ABOVE WIRED HINGE INTO ACCESSIBLE AREA ABOVE CEILING.
13	ALARM KEYPAD	22/4	SINGLE GANG BOX WITH RING, 44" AFF, STUB UP INTO ACCESSIBLE AREA ABOVE CEILING.
14	ANALOG MINIATURE BOARD CAMERA	CAT6	SINGE GANG BOX WITH RING, STUB UP INTO ACCESSIBLE AREA ABOVE CEILING. SEE ELEVATION FOR HEIGHT.
15	ROOF CONTACT	22/4	NO PROVISIONS REQUIRED.
16	360 IP DOME CAMERA	CAT6	SINGLE GANG BOX WITH 2-3/4" ROUND MUD RING, 8'-6" AFF OR TO CEILING FOR CEILING OR CANOPY MOUNT, STUB UP INTO ACCESSIBLE AREA ABOVE CEILING. NO PROVISIONS REQUIRED FOR MOUNTING ON DROP-IN CEILING TILES.
17	IP MINIATURE BOARD CAMERA	CAT6	SINGLE GANG BOX WITH RING, 74" AFF, STUB UP INTO ACCESSIBLE AREA ABOVE CEILING. SEE ELEVATION FOR HEIGHT.
18	ALARM INTERFACE	22/8	SINGLE GANG BOX WITH RING, STUB UP INTO ACCESSIBLE AREA ABOVE CEILING. HEIGHT TO BE DETERMINED BY SHOP PRINTS PER JOB. NO PROVISIONS REQUIRED FOR VAULT.
19	NIGHT DEPOSIT	110VAC	110VAC OUTLET, 74" AFF, ADJACENT TO CAMERA JBOX. SEE POWER PLAN FOR CIRCUIT.
20	VENUS ROUTER		NO PROVISIONS REQUIRED.

PRAXIS3
100 Peachtree St NW
Suite 1450
Atlanta, GA 30303
404-875-4500 tel
www.praxis3.com

GEORGIA REGISTERED No. 041500 PROFESSIONAL ENGINEER RAHN ONEAL WILLIAMS

Copyright (c) 2024 Praxis3, LLC

All reports, plans, specifications, computer files, field data, notes and other documents and instruments prepared by Praxis3 shall retain all common law, statutory and other reserved rights, including copyright thereto.

This drawing may not be reproduced in whole or in part without written permission of Praxis3. It is to be returned upon request. Scales as stated are valid on the original drawings.

Rev	Date	Comments
	07/02/2026	PERMIT SET

Client:
FIFTH THIRD BANK

Project Number: 26032
Project Name:
FIFTH THIRD BANK WATSON 1,900 SF

2711 WATSON BOULEVARD
WARNER ROBBINS, GA 31093

Key Plan:

Sheet Title:
ELECTRICAL SECURITY PLAN

Sheet Number:
E-150

6/30/2026 2:32:05 PM



1 E-160 ELECTRICAL FIRE ALARM PLAN
1/4" = 1'-0"

SHEET NOTES:

1. ALL FIRE ALARM DEVICES, INCLUDING SPEAKERS, VISUALS, SMOKE DETECTORS, ETC. SHALL BE CONNECTED TO THE BASE BUILDING BY A LANDLORD APPROVED, LICENSED FIRE ALARM CONTRACTOR WHO'S BUSINESS IS FIRE ALARM INSTALLATION AND/OR SERVICE.
2. ALL DEVICES ARE TO BE MOUNTED A MINIMUM OF 80" FROM BOTTOM OF STROBE TO FINISHED FLOOR. DEVICES ARE TO BE MOUNTED IN PROPER BOXES (NOT TO BE MOUNTED IN EXTENSION RINGS). JUNCTION BOXES ARE TO BE CLEARLY LABELED "F/A". FLEX CONDUIT WITH INTERNAL CONNECTORS ARE TO BE USED FROM DEVICE BOX TO HOME RUN JUNCTION BOX. IN FULL WALL PENETRATIONS, CONDUIT OR FLEX MUST BE KEPT AT 12" MINIMUM ABOVE THE CEILING.
3. STROBE AND HORN WIRING TO BE 14 AWG THIN STRANDED WIRED, RED/BLACK AND SPEAKER TO BE "BELDON 8760" WITH SHIELD, GRAY JACKET OR EQUIVALENT. FOUR CONDUCTOR OR CABLES ARE NOT TO BE USED ON FIRE ALARM DEVICES. SOLID WIRE IS NOT TO BE USED. SPLICING OF WIRE BETWEEN DEVICES IS PROHIBITED. ALL FIRE ALARM WIRING TO BE PUT IN MINIMUM 1/2" EMT CONDUIT, DEDICATED HANGERS OR STRAPPED, TO BE LOCATED AT THE HIGHEST POINT ABOVE THE CEILING. FIRE ALARM WIRE MUST NOT OCCUPY THE SAME WALL PENETRATION WITH DUCTWORK, PIPING, ELECTRICAL DEVICES OR CIRCUITS. ALL CONDUIT SHALL BE TERMINATED WITH INSULATION BUSHINGS.
4. PROVIDE AND INSTALL POWER SUPPLY FOR NEW STROBES - MATCH BUILDING STANDARD - WITH NECESSARY BATTERIES, BASED ON MAXIMUM OF 20 DEVICES PER POWER SUPPLY. POWER SUPPLY TO BE CONNECTED TO A DEDICATED CIRCUIT AND SUPERVISED FOR FAILURE.
5. WIRING METHOD TO MEET THE ABOVE BUILDING STANDARDS AND COMPLY WITH ARTICLE 760 OF NEC-70 CODE REQUIREMENTS.
6. ALL DEVICES SHALL BE 110 CANDELA UNLESS OTHERWISE NOTED. THE ENTIRE LENS OF VISUAL FIRE ALARM DEVICES SHALL BE MOUNTED AT LEAST 80" AFF.
7. COORDINATE FIRE ALARM SYSTEM SHUTDOWNS AND REPROGRAMMING WITH OWNER.
8. PROVIDE LETTER OF CERTIFICATION FOR NEW FIRE ALARM DEVICES.

PRAXIS3

100 Peachtree St NW
Suite 1450
Atlanta, GA 30303

404-875-4500 tel
www.praxis3.com

GEORGIA REGISTERED No. 041450 PROFESSIONAL ENGINEER RAHN ONEAL WILLIAMS

Copyright (c) 2024 Praxis3, LLC

All reports, plans, specifications, computer files, field data, notes and other documents and instruments prepared by Praxis3 shall retain all common law, statutory and other reserved rights, including copyright thereto.

This drawing may not be reproduced in whole or in part without written permission of Praxis3. It is to be returned upon request. Scales as stated are valid on the original drawings.

Rev	Date	Comments
	07/02/2026	PERMIT SET

Client:
FIFTH THIRD BANK

Project Number: 26032
Project Name:
FIFTH THIRD BANK WATSON 1,900 SF


2711 WATSON BOULEVARD
WARNER ROBBINS, GA 31093

Key Plan:

Sheet Title:
ELECTRICAL FIRE ALARM PLAN

Sheet Number:
E-160


6/30/2026 2:32:06 PM

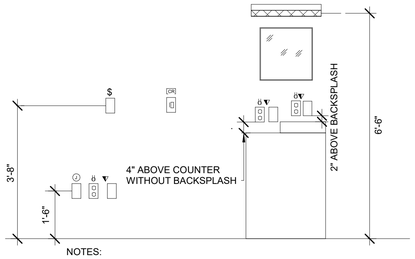

NOTES:

1. MOUNTING HEIGHTS SHOWN ARE FROM FINISHED FLOOR TO CENTERLINE OF OUTLET, UNLESS OTHERWISE NOTED.
2. LOCATIONS OF OUTLETS SHOWN ON ARCHITECTURAL ELEVATIONS SHALL TAKE PRECEDENCE OVER THESE MOUNTING HEIGHTS. FIELD LOCATE OUTLETS WITH ARCHITECT DURING ROUGH-IN.
3. INSTALL OUTLETS THAT ARE IN CLOSE PROXIMITY ON THE SAME CENTERLINE. OUTLETS THAT ARE WITHIN 2'-0" HORIZONTALLY AND WITHIN 1'-0" VERTICALLY SHALL BE INSTALLED ON THE SAME HORIZONTAL CENTERLINE LOCATED HALF WAY BETWEEN THE HEIGHTS SHOWN. OUTLETS THAT ARE MORE THAN 1'-0" APART VERTICALLY SHALL BE INSTALLED ON THE SAME VERTICAL CENTERLINE


6 E-500 STANDARD MOUNTING HEIGHT
N.T.S.

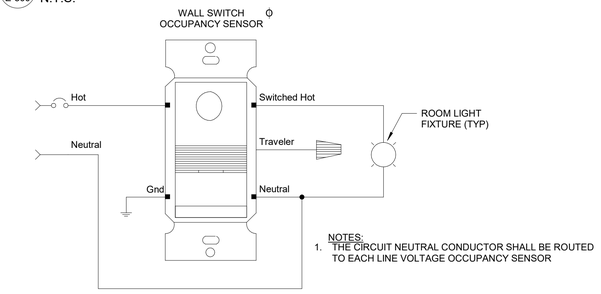

NOTES:

1. THE CIRCUIT NEUTRAL CONDUCTOR SHALL BE ROUTED TO EACH LINE VOLTAGE OCCUPANCY SENSOR


7 E-500 LINE VOLTAGE OCCUPANCY SENSOR WIRING DIAGRAM
N.T.S.

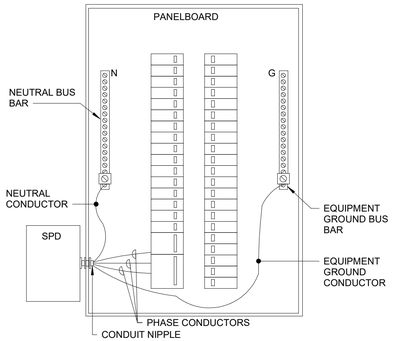


INSTALLATION NOTES:

1. REFER TO SURGE PROTECTION DEVICE (SPD) MANUFACTURER CUTSHEET FOR BREAKER AMPERE RATING. PROVIDE 2P BREAKER FOR 1 PHASE PANELBOARDS AND 3P BREAKER FOR 3 PHASE PANELBOARDS FOR CONNECTING SPD.
2. RELOCATE BREAKER IN PANEL AS NECESSARY TO PROVIDE THE SHORTEST WIRE LENGTH TO SPD.
3. DIRECT CONNECTION TO BUS IS NOT PERMITTED.
4. USE A NIPPLE CONNECTION VIA KNOCKOUT.
5. USE #10 AWG OR LARGER CONDUCTORS AS RECOMMENDED BY SPD MANUFACTURER.
6. LIMIT WIRE LENGTH TO BE AS SHORT AS POSSIBLE, 18" OR LESS.
7. KEEP WIRE FREE OF ANY SHARP BENDS.


8 E-500 SPD PANELBOARD INSTALLATION DETAIL
N.T.S.

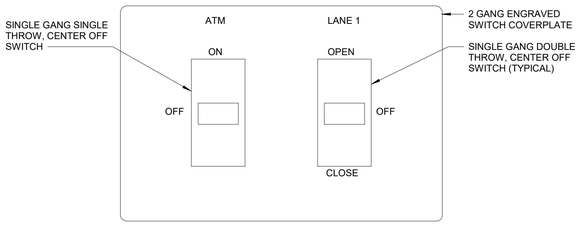


9 E-500 DRIVE THRU LIGHT SWITCH
N.T.S.

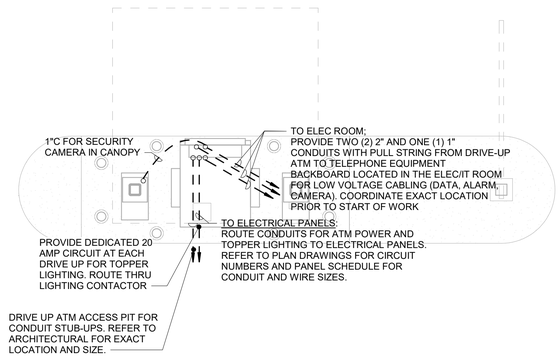

1 E-500 DRIVE-UP ATM DETAIL
N.T.S.

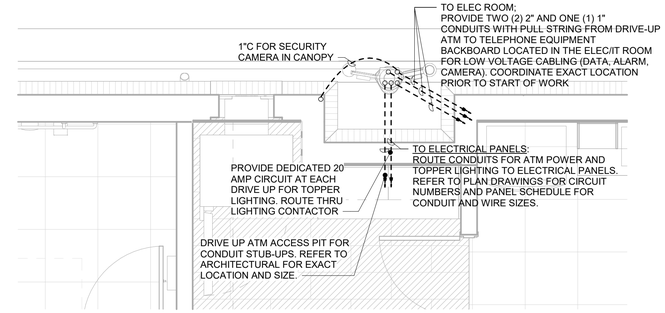


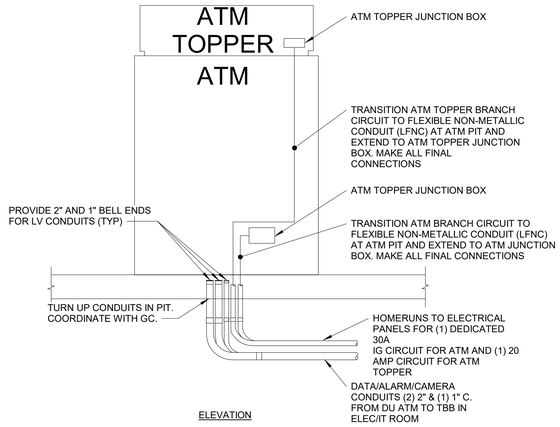

ELEVATION


NOTES:

1. REFER TO ARCHITECTURAL PLANS FOR ATM MODEL NUMBER AND INSTALLATION REQUIREMENTS RELATED TO VEHICULAR AND ANTI-THEFT BOLLARDS, CONDUIT PIT, AND MEDIAN.
2. REFER TO ATM VENDOR CUT SHEETS FOR SPECIFIC REQUIREMENTS PRIOR TO ROUGH-IN.
3. COORDINATE EXACT/FINAL STUB-UP LOCATIONS WITH GC AND ATM CUT SHEETS.
4. EC SHALL BE ON SITE DURING ATM DELIVERY TO MAKE ALL FINAL CONNECTIONS.
5. COORDINATE WITH THE OWNER AND GENERAL CONTRACTOR FOR SCHEDULING WORK.
6. REFER TO ELECTRICAL PANEL SCHEDULES FOR BRANCH CIRCUIT CONDUIT AND WIRE SIZES.
7. REFER TO ELECTRICAL FLOOR PLAN FOR CIRCUIT NUMBERS.
8. CONDUITS SHALL BE SEALED TO PREVENT RODENT INTRUSION.
9. ALL CONDUITS SHALL BE ROUTED CONCEALED.

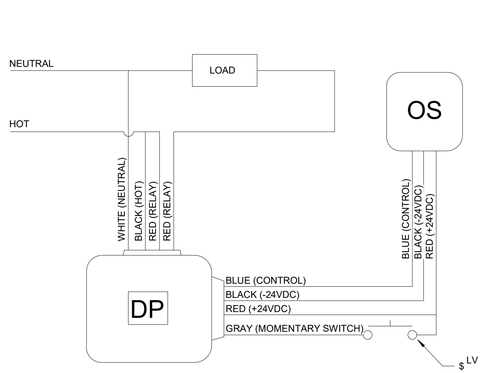


NOTE:
SEE GENERAL NOTES ON THE LIGHTING FLOOR PLANS. LIGHTING CONTROLS SHALL BE INSTALLED AND WIRED PER MANUFACTURER INSTALLATION INSTRUCTIONS. WIRING IN THE DETAIL SHOWN IS FOR REFERENCE AND SHALL BE CONFIRMED WITH THE MANUFACTURER INSTALLATION INSTRUCTIONS

3 E-500 CEILING OCCUPANCY SENSOR NO DIMMING
N.T.S.

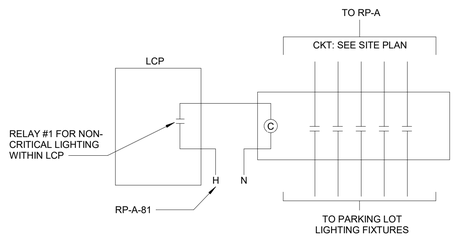


5 E-500 CRITICAL LIGHTING CONTACTOR
N.T.S.

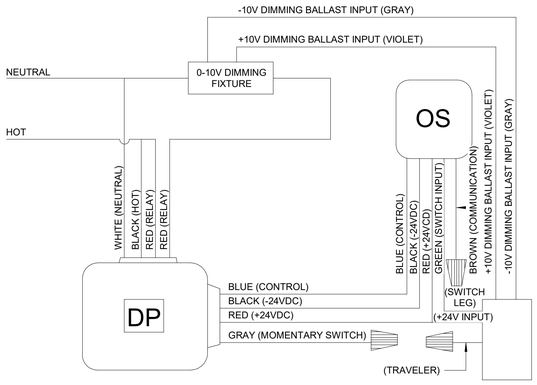

NOTE:
SEE GENERAL NOTES ON THE LIGHTING FLOOR PLANS. LIGHTING CONTROLS SHALL BE INSTALLED AND WIRED PER MANUFACTURER INSTALLATION INSTRUCTIONS. WIRING IN THE DETAIL SHOWN IS FOR REFERENCE AND SHALL BE CONFIRMED WITH THE MANUFACTURER INSTALLATION INSTRUCTIONS.

2 E-500 CEILING OCCUPANCY SENSOR WITH DIMMING
N.T.S.

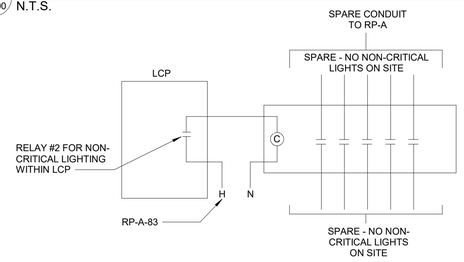

4 E-500 NON-CRITICAL LIGHTING CONTACTOR
N.T.S.

PRAXIS3
100 Peachtree St NW
Suite 1450
Atlanta, GA 30303
404-875-4500 tel
www.praxis3.com

GEORGIA REGISTERED No. 041508 PROFESSIONAL ENGINEER RAHN ONEAL WILLIAMS

Copyright (c) 2024 Praxis3, LLC

All reports, plans, specifications, computer files, field data, notes and other documents and instruments prepared by Praxis3 shall retain all common law, statutory and other reserved rights, including copyright thereto.

This drawing may not be reproduced in whole or in part without written permission of Praxis3. It is to be returned upon request. Scales as stated are valid on the original drawings.

Rev	Date	Comments
	07/02/2026	PERMIT SET

Client:
FIFTH THIRD BANK

Project Number: 26032
Project Name:
FIFTH THIRD BANK WATSON 1,900 SF


2711 WATSON BOULEVARD
WARNER ROBBINS, GA 31093

Key Plan:

Sheet Title:
ELECTRICAL DETAILS

Sheet Number:
E-500

6/30/2026 2:32:06 PM

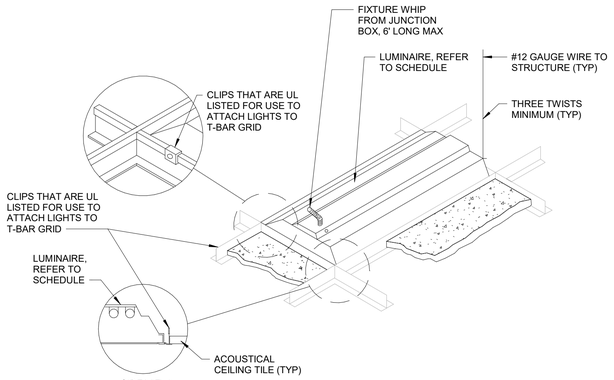


SIDE VIEW:

NOTES:

1. REFER TO ARCHITECTURAL PLANS FOR CEILING GRID SUPPORT REQUIREMENTS. THIS DETAIL SHOWS FIXTURE SUPPORT REQUIREMENTS ONLY.
2. INSTALL IN ACCORDANCE WITH MANUFACTURER'S MOUNTING INSTRUCTIONS AND USING RECOMMENDED MOUNTING HARDWARE.
3. THERMAL INSULATION SHALL NOT BE INSTALLED ABOVE A RECESSED LUMINAIRE OR WITHIN 3" OF THE RECESSED LUMINAIRE'S ENCLOSURES, WIRING COMPARTMENT, BALLAST, TRANSFORMER, LED DRIVER, OR POWER SUPPLY UNLESS THE LUMINAIRE ISIDENTIFIED AS TYPE IC FOR INSULATION CONTACT.


2 E-600 TROFFER MOUNTING - LAY-IN-CEILING
N.T.S.

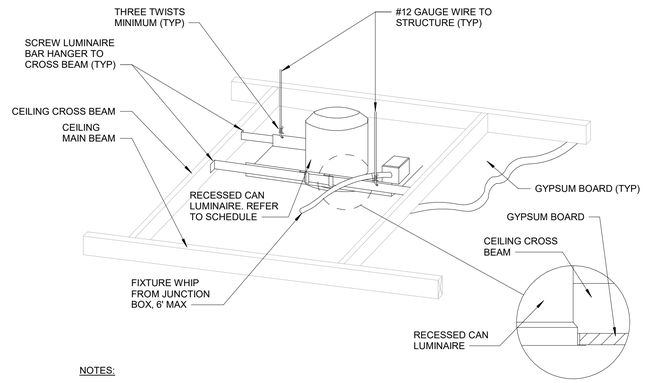

NOTES:

1. INSTALL IN ACCORDANCE WITH MANUFACTURER'S MOUNTING INSTRUCTIONS AND USING RECOMMENDED MOUNTING HARDWARE.
2. THERMAL INSULATION SHALL NOT BE INSTALLED ABOVE A RECESSED LUMINAIRE OR WITHIN 3" OF THE RECESSED LUMINAIRE'S ENCLOSURES, WIRING COMPARTMENT, BALLAST, TRANSFORMER, LED DRIVER, OR POWER SUPPLY UNLESS THE LUMINAIRE IS IDENTIFIED AS TYPE IC FOR INSULATION CONTACT.
3. ALL JUNCTION BOXES SHALL BE ACCESSIBLE.

3 E-600 DOWNLIGHT MOUNTING - GYPBOARD CEILING
N.T.S.

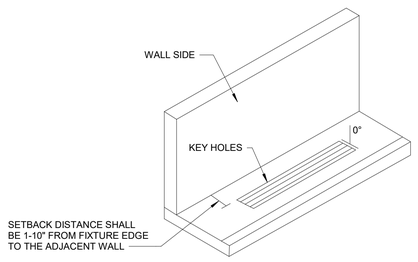

GENERAL NOTES:

1. INGROUND LED, WALK-OVER COMPLIANT, IP68 RATED, ASYMMETRIC WALLWASH WITH ANTI-SLIP LENS.
2. COORDINATE LOCATION WITH ARCHITECT PRIOR TO ROUGH-IN, AIM KEYHOLES AND FROSTED SECTION OF LENS TOWARD THE WALL SIDE.

4 E-600 INGROUND LED INSTALLATION
N.T.S.

LIGHTING FIXTURE SCHEDULE (INTERIOR)

LABEL	DESCRIPTION	LIGHT FIXTURE		MOUNTING	QTY. OF LAMPS	VOLTS	WATTS	NOTES:
		MFG.	MODEL NUMBER					
A	2' X 2' LED RECESSED LUMINAIRE, TRANSMITTANCE DIFFUSER WITH CONCAVE RIBBED REFRACTOR, L90/60,000, STEEL HOUSING, 010V DIMMING DRIVER	GE	LVT-22-B-0-33-MM-835-VQ-LT-WHTE	RECESSED	LED	120	29	
AE	2' X 2' LED RECESSED LUMINAIRE, TRANSMITTANCE DIFFUSER WITH CONCAVE RIBBED REFRACTOR, L90/60,000, STEEL HOUSING, 010V DIMMING DRIVER WITH EMERGENCY BATTERY BACKUP	GE	LVT-22-B-0-33-MM-835-VQ-LT-WHTE-EL	RECESSED	LED	120	29	
B	RECESSED EXTRUDED ALUMINUM, 010V DIMMING STANDARD, LENSED DIFFUSER, STANDARD OUTPUT, HE TECH OPTICS, MUD OVER FLANGE	CORONET	LSR4-8-35-LTG2-UNV-DB-W-NT-SD	RECESSED	LED	120		
C	TACADA PENDANT, BLACK CORD, AGED BRASS HARDWARE SEE REFLECTED CEILING PLANS FOR PENDANT LENGTHS.	MICHAEL OREN	700TDDALVPMC-B-R-LEDWD	PENDANT	LED	120		* VERIFY FINISH WITH ARCHITECT PRIOR TO ORDERING **PROVIDE TEN (10) EXTRA FIXTURES FOR ATTIC STOCK COORDINATE WITH OWNER
F3	WALL MOUNTED 3' LED STRIPLIGHT WITH DIFFUSED LENS AND STEEL HOUSING	LSI	PST-3-3-47L-FAD-UNV-835-GWT	WALL MOUNT (ABOVE DOOR)	LED	120		
FEM	48" SUSPENDED STRIP LIGHT, ACRYLIC DROP LENS, 80 CRI, WHITE FINISH, AIRCRAFT CABLE MOUNTING, WIREGUARD WITH EMERGENCY BATTERY BACKUP	GE	ALV2-0-4T-03-T-C8-1D-S-Q-Q-E-51-A-Q-W	SUSPENDED	LED	120		
G	LINEAR LED COVE WALL WASHER, 5W/ft, MEDIUM OUTPUT, 30 X 80 LENS VIEWING ANGLE, 80CRI	GE	L-LW-SO-B-0-04-CV-8-35-V-Q-TM-WHITE (LENGTH AS SPECIFIED ON PLANS)	COVE	LED	120		
G1	RECESSED LED OPEN ROUND DOWNLIGHT, 5" DIA. APERTURE, WIDE BEAM SPREAD,SEMI-DIFFUSED REFLECTOR FINISH. U.L. LISTED WET LOCATION	CSL	ED5AIC-359050-16-S; ED5-RFWLWT; ED5-TC2	RECESSED	LED	120		
GEM	RECESSED LED OPEN ROUND DOWNLIGHT, 5" DIA. APERTURE, WIDE BEAM SPREAD, SEMI-DIFFUSED REFLECTOR FINISH. U.L. LISTED WET LOCATION WITH EMERGENCY BATTERY BACKUP	CSL	ED5AIC-359050-16-S; ED5-RFWLWT; ED5-TC2; EM-1006	RECESSED	LED	120		
J	6" SQUARE DOWNLIGHT, 010V DIMMING DRIVER, SEMISPECULAR, CLEAR REFLECTOR.	GE	LDX-6S-A-1-15-T-35-VQ / RD-I6S-W-SD-WT	RECESSED	LED	120		
JE	6" SQUARE DOWNLIGHT, 010V DIMMING DRIVER, SEMISPECULAR, CLEAR REFLECTOR WITH EMERGENCY BATTERY BACKUP	GE	LDX-6S-A-1-15-T-35-VQ-EL / RD-I6S-WSD-WT	RECESSED	LED	120		
L	TETRA CONTOUR LS LED LIGHTING SYSTEM, 2W/ft, GREEN LIGHT ENGINE AND GREEN LIGHT GUIDE 180W POWER SUPPLY	GE	GEGNGLE1-A (LENGTH AS SPECIFIED ON PLANS)	RECESSED	LED	120		LOCATE AT PARAPET REVEAL. PROVIDE ALL COMPONENTS AND ACCESSORIES FOR A COMPLETE INSTALLATION
PB	PARAVO PENDANT FIXTURE WHITE FINISH FIBERGLASS SHADE, ALUMINUM EXOSTRUCTURE, FROSTED GLASS PLATE DIFFUSER, MEDIUM BASE LED A21 2700K DIMMABLE LAMP	TECH LIGHTING	700TDPRVP-WW-LED927	PENDANT	LED	120		PROVIDE 4" ROUND BOX
S	STRIP LED, 4' LENGTH, DIFFUSING LENS, MEDIUM WARM CCT, DIMMABLE REMOTE DRIVER. 96W LED DRIVER POWER SUPPLY.	NOVA FLEX	DES-LED-SWH-24-3.0-IP20-35/ CHN-SUR-2217-SL-SOFT-2M/ NF-PS-UNV-80W-24V	RECESSED	LED	120		
T	TBAR LED, 2' LENGTH, DIFFUSING LENS, MEDIUM WARM CCT, DIMMABLE REMOTE DRIVER. 30W POWER SUPPLY	SLG LIGHTING	TG-2-13-W-G1-35K / TG-2-30W	RECESSED	LED	120		COORDINATE AND CONFIRM GRID TYPE WITH ARCHITECTURAL.
TE	TBAR LED, 2' LENGTH, DIFFUSING LENS, MEDIUM WARM CCT, DIMMABLE REMOTE DRIVER. 30W POWER SUPPLY WITH EMERGENCY BATTERY BACKUP	SLG LIGHTING	TG-2-13-W-G1-35K / TG-2-30W-EMH--8	RECESSED	LED	120		COORDINATE AND CONFIRM GRID TYPE WITH ARCHITECTURAL.
U1	INGROUND LED, WALKOVER COMPLIANT, IP68 RATED, ASYMMETRIC WALLWASH WITH ANTISLIP LENS	LUMENFACADE	LOI RO-120-12-35K-WW-NO-ASL	RECESSED	LED	120		COORDINATE LOCATION WITH ARCHITECT PRIOR TO ROUGHIN, AIM KEYHOLES AND FROSTED SECTION OF LENS TOWARD THE WALL SIDE.
U3	INGROUND LED, WALKOVER COMPLIANT, IP68 RATED, ASYMMETRIC WALLWASH WITH ANTISLIP LENS.	LUMENFACADE	LOI RO-120-36-35K-WW-NO-ASL	RECESSED	LED	120		COORDINATE LOCATION WITH ARCHITECT PRIOR TO ROUGHIN, AIM KEYHOLES AND FROSTED SECTION OF LENS TOWARD THE WALL SIDE.
UC	STRIP LED, PERMANENT HOUSING LENGTH WITH LED TAPE THAT SHALL BE FIELD CUT TO THE SIZE OF THE HOUSING, DIFFUSING LENDS, MEDIUM WARM CCT, DIMMABLE REMOTE DRIVER, 80W LED DRIVER POWER SUPPLY.	NOVA FLEX	DES-LED-HO-24V-3.0-IP20-35; NF-CH-1707-SL-SOFT-2M; NF-PS-UNV-80W-24V (LENGTH AS SPECIFIED ON PLANS)	UNDER CABINET	LED	120		* VERIFY FINISH WITH ARCHITECT PRIOR TO ORDERING **PROVIDE TEN (10) EXTRA FIXTURES FOR ATTIC STOCK COORDINATE WITH OWNER
X1	LED EDGE LIT EXIT SIGN, SINGLE FACE, RECESSED IN THE CEILING	EVENLITE	SOVII-EM-R-1M-BA-RC-UC-FP-FT	RECESSED	LED	120		PROVIDE ARROWS AS SHOWN ON FLOOR PLAN
X2	LED EDGE LIT EXIT SIGN, SINGLE FACE, SURFACE WALL MOUNTED	EVENLITE	SOVII-EM-R-1M-BA-SW-UC-FP	RECESSED	LED	120		PROVIDE ARROWS AS SHOWN ON FLOOR PLAN
X3	NORMALLY OFF, EMERGENCY EGRESS CONCEALED WALLPACK	EVENLITE	APLNCUI	RECESSED	LED	120		PROVIDE ALL MOUNTING ACCESSORIES.

LIGHTING FIXTURE SCHEDULE NOTES:

1. MANUFACTURER CATALOG NUMBERS ARE SHOWN FOR GENERAL DESCRIPTIVE PURPOSES AND TO ESTABLISH STANDARD OF QUALITY ONLY. CONTACT CHRIS YOUNG (cyoung@southernlightingsource.com) OR ADAM MAGGIO (amaggio@southernlightingsource.com) (770-242-4000) (53lights@southernlightingsource.com) SOUTHERN LIGHTING SOURCE ON LIGHTING AND LIGHTING CONTROLS. GC/EC SHALL PROVIDE LUMINAIRES COMPLETE WITH ALL OPTIONS AND ACCESSORIES REQUIRED FOR A COMPLETE INSTALLATION. ALL PRODUCTS SHALL BE UL LISTED. POLE MOUNTED LIGHT FIXTURES SHALL MATCH EXISTING DEVELOPMENT AS SPECIFIED. NO EQUALS FOR POLE MOUNTED FIXTURES.
2. REFER TO ELECTRICAL SPECIFICATIONS FOR ADDITIONAL REQUIREMENTS WHICH MAY NOT NECESSARILY BE REFLECTED IN CATALOG NUMBER AND/OR DESCRIPTION IN THIS SCHEDULE
3. PROVIDE FUSES FOR UNGROUNDED CONDUCTORS SUPPLYING LED DRIVERS. PROVIDE FUSE SIZED FOR RATING OF LED DRIVER.
4. VERIFY CONSTRUCTION OF CEILINGS BEING INSTALLED AND PROVIDE THE LUMINAIRES SPECIFIED IN APPROPRIATE CONFIGURATION WITH ALL HARDWARE AND ACCESSORIES REQUIRED FOR A COMPLETE INSTALLATION.
5. PROVIDE LUMINAIRES WITH JOINING PLATES, END CAPS, CANOPIED, MOUNTING HARDWARE, ETC. AS REQUIRED FOR COMPLETE INSTALLATION.
6. EXIT LIGHTS SHALL BE PROVIDED WITH COLOR OF LETTERS REQUIRED BY LOCAL CODE AUTHORITY. FURNISH WITH CHEVRON DIRECTIONAL INDICATORS AS INDICATED AND REQUIRED.
7. PROVIDE DEVICES FOR SECURING LAY-IN TYPE LUMINAIRES TO CEILING GRID TO COMPLY WITH ARTICLE 410 OF THE NATIONAL ELECTRIC CODE.
8. FURNISH LINEAR LUMINAIRES IN CONTINUOUS ROWS OR PATTERNS AS INDICATED ON DRAWINGS. PROVIDE WITH CORNER, ANGLE AND END PIECES AS REQUIRED FOR A COMPLETE INSTALLATION.
9. FURNISH LUMINAIRES IN MECHANICAL SPACES COMPLETE WITH PENDANT STEMS OR CHAIN HANGERS AS REQUIRED TO MOUNT BELOW PIPING, DUCT, CONDUIT, ETC. MAINTAIN UNIFORM MOUNTING HEIGHT FOR ALL LUMINAIRES THROUGHOUT THE MECHANICAL AREA.
10. PENDANT MOUNTED LUMINAIRES WITH AIRCRAFT CABLE SUSPENSION SYSTEMS SHALL BE FURNISHED WITH ADJUSTABLE CABLE GRIP HARDWARE. CABLE SIZE SHALL BE SELECTED MY MANUFACTURER TO PROVIDE ADEQUATE SUPPORT OF LUMINAIRES SPECIFIED.

PRAXIS3
100 Peachtree St NW
Suite 1450
Atlanta, GA 30303
404-875-4500 tel
www.praxis3.com

GEORGIA REGISTERED No. 041500 PROFESSIONAL ENGINEER RAHN ONEAL WILLIAMS

Copyright (c) 2024 Praxis3, LLC

All reports, plans, specifications, computer files, field data, notes and other documents and instruments prepared by Praxis3 shall retain all common law, statutory and other reserved rights, including copyright thereto.

This drawing may not be reproduced in whole or in part without written permission of Praxis3. It is to be returned upon request. Scales as stated are valid on the original drawings.

Rev	Date	Comments
	07/02/2026	PERMIT SET

Client:
FIFTH THIRD BANK

Project Number: 26032
Project Name:
FIFTH THIRD BANK WATSON 1,900 SF

2711 WATSON BOULEVARD
WARNER ROBBINS, GA 31093

Key Plan:

Sheet Title:
LUMINAIRE AND SENSOR SCHEDULE AND DETAILS

Sheet Number:
E-600

6/30/2026 2:32:07 PM

Evolve®



CUSTOMER NAME _____

PROJECT NAME _____

DATE _____ TYPE _____

CATALOG NUMBER _____

EALS Series
LED Outdoor Area Light

The EALS Area Light luminaire offers a wide range of optical patterns, color temperatures, lumen packages and mounting configurations to optimize area light applications, as well as provide versatility in lighting design within one form-factor. They are ideal for commercial property site-lighting applications such as retail and commercial exteriors.

Construction

Housing:	Aluminum die cast enclosure. Integral heat sink for maximum heat transfer
Lens:	Impact resistant tempered glass
Paint:	Corrosion resistant polyester powder paint, minimum 2.0 mil thickness Standard = Black, Dark Bronze Gray, White (RAL & custom colors available) Optional = Coastal Finish
Weight:	27 lbs

Optical System

Lumens:	7,000 - 50,000
Photometry:	Type II, III, IV & V
Efficacy:	118-177LPW
CCT:	2700K, 3000K, 4000K, 5000K
CRI:	≥70
Upward Light Output Ratio (ULOR):	0 Horizontal Orientation

Electrical

Input Voltage:	120-277V, 277-480V & 347-480V
Input Frequency:	50/60 Hz
Power Factor (PH):	≥ 0.9 at rated watts
Total Harmonic Distortion (THD):	≤ 20% at rated watts

Surge Protection

☐ 6kV/3kA ☐ 10kV/5kA ☐ 20kV/10kA

Per ANSI C136.2-2023

Lumen Maintenance

Projected Lxx per IES TM-21-11 at 25°C

OPTICS	LXX/50K) @ HOURS		
	25,000 HR	50,000 HR	60,000 HR
C2, C3, C4, C5 D2, D3, D4, D5 F2, F3, F4, F5	L99	L97	L96
H2, H3, H4, H5 J2, J3, J4, J5 K2, K3, K4, K5	L98	L96	L96
L2, L3, L4, L5 M2, M3, M4, M5	L96	L93	L91
N2, N3, N4, N5	L94	L85	L82

Note: Projected Lxx based on LM80 (> 17,000 hour testing). Accepted industry tolerances apply to initial luminous flux and lumen maintenance measurements

Luminaire Ambient Temperature Factor

AMBIENT TEMP (°C)	INITIAL FLUX FACTOR	AMBIENT TEMP (°C)	INITIAL FLUX FACTOR
10	1.02	30	0.99
20	1.01	40	0.98
25	1.00		

Ratings

Operating Temperature:	-40°C to 50°C (Nx Optic Codes are -40°C to 40°C)
Vibration: LM-79:	3G per ANSI C136.31-2010 Testing in accordance with IESNA Standards

Controls

Dimming:	Standard – 0-10V ☐ Optional – DALI (Option U) ☐
Sensors:	Photo Electric Sensors (PE) available LightGrid+™ and Daintree Compatible

Warranty

☐ 5 Year (Standard) ☐ 10 Year (Optional)

IP66 IK07

© 2025 Current Lighting Solutions, LLC. All rights reserved. Information and specifications subject to change without notice. All values are design or typical values when measured under laboratory conditions.

Evolve®

EALS Series
LED Outdoor Area Light

CUSTOMER NAME _____

PROJECT NAME _____

DATE _____ TYPE _____

CATALOG NUMBER _____

Ordering Information

EALS 04 _ _ _ _ _ _ _ _ 7 _ _ _ _ _ _ _ _ _ _ _ _

PRODUCT ID	GENERATION	VOLTAGE	OPTICAL CODE	DISTRIBUTION	CRI	CCT	DIMMING[1]	CONTROLS	MOUNTING ARM	COLOR	OPTIONS
E= Evolve ALs= Area Light S = Standard	04	0*=120-277V H* = 347-480V E*[2] = 277-480V 1 = 120V 2 = 208V 3 = 240V 4 =277V D = 347V 5 = 480V	Cx =7500K[3,19] Dx = 10000 lm/ft[4,19] Fx = 15000 lm Hx = 20000 lm Jx = 25000 lm Kx = 30000 lm Lx = 35000 lm Mx = 40000 lm Nx = 50000 lm	SM = Symmetric Medium SW = Symmetric Wide SH = Symmetric High Angle AF = Asymmetric Forward AH = Asymmetric High Angle AW = Asymmetric Wide AN = Asymmetric Narrow/Auto	7 = 70 (min)	27* = 2700K 30* = 3000K 40 = 4000K 50 = 5000K	N = Dimming thru PE receptacle D = External Dimming 18/2 3 ft Cable	A = ANSI C136.41 7-Pin Receptacle (No Control) D = ANSI C136.41 7-Pin Receptacle with Shorting Cap E* = ANSI C136.41 7-pin with Non-Dimming PE Control	C** = Integral Slipfitter: Standard D** = Universal Mounting Arm: Fitted for round or square pole mounting 4" min. square poles. K**,* = Knuckle Slipfitter: For 1.9 in. - 2.3 in OD Tenon S**,* = Knuckle Slipfitter: For 2.3 in. - 3.0 in OD Tenon V**,* = Knuckle Wall Mount	BLCK = Black GRAY = Gray WHTE = White DKBZ = Dark Bronze	F= Fusing H2 = Daintree (WHS-1120) enabled motion sensor.*,16 H4 = Motion Sensor (WattStopper) L = Tool-Less Entry J = cUL/Canada R = Enhanced Surge Protection (10kV/5kA) SL** = Rotated Left SR** = Rotated Right T = Extreme Surge Protection (20kV/10kA) UF = DALI Programmable V0 = 3 Position Terminal Block V** = Coastal Finish XXX = Special Options

1 Not Available with Fusing, Must Choose a Discrete Voltage with "F" Option Code
2 Note Standard Dimming is 0-10V
3 Not available in 277-480V
4 Supplied with 3ft leads
5 Supplied with 16/3 ft Cable
6 Restricted Aiming Angle of 0-45°
7 Compatible with LightGrid+™ Wireless Control Nodes, Not Compatible with Motion Sensor Control
8 Not available in 347V, 480V or 347-480V
9 Only available with F, H, J, K, L, M, N option
10 Recommended for installations within 750 feet from coast. Lead time varies, check with factory.
11 Select 2700K or 3000K CCT for DarkSky Approved fixtures.
12 For aimed left or right light distribution orientation, as assembled in manufacturing. Not applicable for Symmetric Distributions
13 DALI option not available with 347V, 480V, or 347-480V
14 Not available with 20kV/10kA SPD
15 When mounting fixtures at 90 degrees, round pole must be 3.5" OD minimum

© 2025 Current Lighting Solutions, LLC. All rights reserved. Information and specifications subject to change without notice. All values are design or typical values when measured under laboratory conditions.

Evolve®

EALS Series
LED Outdoor Area Light

CUSTOMER NAME _____

PROJECT NAME _____

DATE _____ TYPE _____

CATALOG NUMBER _____

TYPE	OPTIC CODE	DISTRIBUTION	TYPICAL INITIAL LUMENS			TYPICAL SYSTEM WATTAGE		BUG RATINGS		
			2700K	3000K	4000K & 5000K	120-277	347-480V	2700K	3000K	4000 & 5000K
TYPE V	C5	Symmetric Medium (SM)	6800	7340	7730	45	47	B3-U0-G1	B3-U0-G1	B3-U0-G1
	D5		9060	9790	10300	61		B3-U0-G2	B3-U0-G2	B3-U0-G2
	F5		13600	14680	15450	91		B4-U0-G2	B4-U0-G2	B4-U0-G2
	H5		18130	19570	20600	123		B4-U0-G2	B4-U0-G2	B4-U0-G2
	J5		22660	24460	25750	156		B4-U0-G2	B5-U0-G3	B5-U0-G3
	K5		27190	29360	30900	191		B5-U0-G3	B5-U0-G3	B5-U0-G3
	L5		31720	34250	36050	231		B5-U0-G3	B5-U0-G4	B5-U0-G4
	M5		36260	39140	41200	273		B5-U0-G4	B5-U0-G4	B5-U0-G4
	N5		45320	48930	51500	372		B5-U0-G4	B5-U0-G4	B5-U0-G4
	C5	Symmetric Wide (SW)	6930	7480	7880	45	47	B3-U0-G1	B3-U0-G1	B3-U0-G1
	D5		9240	9980	10500	61		B3-U0-G1	B3-U0-G1	B3-U0-G1
	F5		13860	14960	15750	91		B3-U0-G2	B3-U0-G2	B3-U0-G2
	H5		18480	19950	21000	123		B4-U0-G2	B4-U0-G2	B4-U0-G2
	J5		23100	24940	26250	156		B4-U0-G2	B4-U0-G2	B5-U0-G2
	K5		27720	29930	31500	191		B4-U0-G2	B4-U0-G2	B5-U0-G2
	L5		32340	34910	36750	231		B5-U0-G2	B5-U0-G3	B5-U0-G3
	M5		36960	39900	42000	273		B5-U0-G3	B5-U0-G3	B5-U0-G3
	N5		46200	49880	52500	372		B5-U0-G3	B5-U0-G4	B5-U0-G4
	C5	Symmetric High Angle (SH)	6600	7130	7500	45	47	B3-U0-G1	B3-U0-G2	B3-U0-G2
	D5		8800	9500	10000	61		B3-U0-G2	B3-U0-G2	B4-U0-G2
	F5		13200	14250	15000	91		B4-U0-G2	B4-U0-G2	B4-U0-G2
	H5		17600	19000	20000	123		B4-U0-G3	B4-U0-G3	B5-U0-G3
	J5		22000	23750	25000	156		B5-U0-G3	B5-U0-G3	B5-U0-G3
	K5		26400	28500	30000	191		B5-U0-G3	B5-U0-G3	B5-U0-G4
	L5		30800	33250	35000	231		B5-U0-G4	B5-U0-G4	B5-U0-G4
	M5		35200	38000	40000	273		B5-U0-G4	B5-U0-G4	B5-U0-G4
	N5		44000	47500	50000	372		B5-U0-G4	B5-U0-G5	B5-U0-G5

For additional information on Non-Shielded and Shielded EALS files, please refer to LED.com

© 2025 Current Lighting Solutions, LLC. All rights reserved. Information and specifications subject to change without notice. All values are design or typical values when measured under laboratory conditions.

PRAXIS3

100 Peachtree St NW
Suite 1450
Atlanta, GA 30303

404-875-4500 tel
www.praxis3.com

GEORGIA REGISTERED No. 043508 PROFESSIONAL ENGINEER RAHN ONEAL WILLIAMS

Copyright (c) 2024 Praxis3, LLC

All reports, plans, specifications, computer files, field data, notes and other documents and instruments prepared by Praxis3 shall retain all common law, statutory and other reserved rights, including copyright thereto.

This drawing may not be reproduced in whole or in part without written permission of Praxis3. It is to be returned upon request. Scales as stated are valid on the original drawings.

Rev	Date	Comments
	07/02/2026	PERMIT SET

Client:

FIFTH THIRD BANK

Project Number: 26032
Project Name:

FIFTH THIRD BANK WATSON 1,900 SF

2711 WATSON BOULEVARD
WARNER ROBBINS, GA 31093

Key Plan:

Sheet Title:

EXTERIOR LIGHTING CUTSHEETS

Sheet Number:

E-601

6/30/2026 2:32:08 PM

Catalog #: _____ Project: _____

Prepared By: _____ Date: _____ Type: _____

XSPS

LED Soffit Light



OVERVIEW	
Lumen Package	4000 - 8000
Wattage Range	43 -59
Efficacy Range (LPW)	96 -104
Weight lbs (kg)	7.6 (3.5)

QUICK LINKS

Ordering Guide | Performance | Photometrics | Dimensions

FEATURES & SPECIFICATIONS

Construction

- Housing is die-formed aluminum with diffuse acrylic lens providing a water-resistant seal. Enclosure contains factory prewired driver and optical unit containing LEDs.
- Recess mount into an enclosed soffit with screws through the mounting frame. 8" clearance required for ease of installation.
- Finished with LSI's DuraGrip® polyester powder coat finishing process. The DuraGrip finish withstands extreme weather changes without cracking or peeling. Other standard LSI finishes available. Consult factory.
- Max shipping weight: 30lbs in carton

Optical System

- Symmetric distribution with excellent uniformity and a BUG rating of B2-U0-G1. Diffuse lens is standard to minimizing visibility of LEDs.
- Select high-brightness LEDs.
- Available in 5000K, 4000K and 3000K
- Color temperatures per ANSI C78.377.
- Minimum CRI of 80.

Electrical

- High-performance factory programmable driver features over-voltage, under voltage, short-circuit and over temperature protection with integral surge protection that meets IEEE C62.41.2 and ANSI C82.77. -5 Location Category C Low standards.
- 0-10 volt dimming (10% - 100%) standard.
- 120-347VAC 50/60Hz
- Thermal protector standard on 5000-8000 lumen versions.
- L80 Calculated Life: >100k Hours (See Lumen Maintenance chart)
- Total harmonic distortion: <20%
- Operating temperature: -40°C to 40°C (-40°F to 104°F) for HO and VHO. -40°C to 45°C (-40°F to 113°F) for SS. -40°C to 35°C (-40°F to 95°F) for SHO .
- Power factor: >0.90
- Input power stays constant over life.
- High-efficacy LEDs with integrated circuit board mount to the housing to maximize heat dissipation and promote long life.
- Driver components are fully encased in potting material for moisture resistance. Driver complies with FCC standards.

Warranty

- LSI luminaires carry a 5-year limited warranty. Refer to https://www.lsicorp.com/resources/terms-conditions-warranty/ for more information.

Listings

- Listed to UL 1598 and UL 8750
- Suitable For Damp Locations
- Meets Buy American Act requirements.
- DesignLights Consortium® (DLC) qualified product. Not all versions of this product may be DLC qualified. Please check the DLC Qualified Products List at www.designlights.org/GPL to confirm which versions are qualified.
- IDA compliant with 3000K or lower color temperature.

Type: _____

XSPS LED Soffit Light

Back to Quick Links

ORDERING GUIDE

TYPICAL ORDER EXAMPLE: **XSPS S LED SS CW 120 GWT DFL**

Prefix	Distribution	Light Source	Drive Current	Color Temperature	Input Voltage	Finish	Lens	Options
XSPS - LED Soffit	**S** - Symmetric	**LED**	**SS** - 4,000 Lumens **HO** - 5,000 Lumens **VHO** - 6,000 Lumens	**CW** - 5000K 80 CRI **NW** - 4000K 80 CRI **WW** - 3000K 80 CRI	**120** - 120V **208** - 208V **240** - 240V **277** - 277V **347** - 347V	**GWT** - Gloss White	**DFL** - Diffused Acrylic Lens	**CMT** - Channel Bar Mounting Kit **BB** - Emergency Battery Pack[1]

1 - Emergency Battery Pack only available on the SS - 4000 lumen version (120, 208, 240 & 277V versions).

PERFORMANCE

DELIVERED LUMENS

Lumen Package	Distribution	Lens Type	CRI	3000K CCT			4000K CCT			5000K CCT			Wattage
				Delivered Lumens	Efficacy	Bug Rating	Delivered Lumens	Efficacy	Bug Rating	Delivered Lumens	Efficacy	Bug Rating	
SS	S	DFL	80	3816	123	B2-U0-G1	4022	129	B2-U0-G1	3966	128	B2-U0-G1	31
HO	S	DFL	80	4756	120	B2-U0-G1	5011	127	B2-U0-G1	4941	125	B2-U0-G1	40
VHO	S	DFL	80	5733	118	B2-U0-G1	6041	124	B2-U0-G1	5957	122	B2-U0-G1	49
SHO	S	DFL	80	7559	113	B3-U0-G1	7965	119	B3-U0-G1	7853	118	B3-U0-G1	67

LEDs are frequently updated therefore values are nominal.

Electrical Data (Amps)*

Lumen Package	Wattage	120V	208V	240V	277V	347V
SS	31	0.26	0.15	0.13	0.11	0.09
HO	40	0.33	0.19	0.16	0.14	0.11
VHO	49	0.41	0.23	0.2	0.18	0.14
SHO	67	0.56	0.32	0.28	0.24	0.19

*Electrical data at 25C (77F). Actual wattage may differ by +/-10%.

RECOMMENDED LUMEN MAINTENANCE

Ambient Temp C	Initial[1]	25K hrs.[1]	50K hrs.[1]	75K hrs.[2]	100K hrs.[2]
25 C	100%	95%	91%	86%	82%

1 - In accordance with IESNA TM-21-11, Projected Values represent interpolated value based on time durations that are within six times the IESNA LM-80-08 total test duration for the device under testing.
2 - In accordance with IESNA TM-21-11, Calculated Values represent time durations that exceed six times the IESNA LM-80-08 total test duration for the device under testing.

Catalog # : _____ Project : _____ Type : _____

Prepared By : _____ Date : _____

Mirada Medium Wall Sconce (XWM)

Outdoor Wall Sconce

IP65 IK08



OVERVIEW	
Lumen Package	3,000 - 21,000
Wattage Range	23 - 175
Efficacy Range (LPW)	125 - 158
Weight lbs(kg)	27 (12.2)
Control Options	IMSBT, ALB, ALS, PCI

QUICK LINKS

Ordering Guide | Performance | Photometrics | Dimensions

FEATURES & SPECIFICATIONS

Construction

- Rugged die-cast aluminum housing contains factory prewired driver and optical unit. Hinged die-cast aluminum wiring access door located underneath.
- Galvanized-steel universal wall mount bracket comes standard with hinging mechanism to easily access the junction box wire connections without removing the luminaire.
- Optional pole-mounting bracket (XPMA) permits mounting to standard poles.
- Fixtures are finished with LSI's DuraGrip® polyester powder coat finishing process. The DuraGrip finish withstands extreme weather changes without cracking or peeling. Other standard LSI finishes available. Consult factory.
- Max shipping weight: 30lbs in carton

Optical System

- State-of-the-Art one piece silicone optic provides industry leading optical control while also acting as an integrated gasket reducing system complexity and improving fixture reliability.
- Proprietary silicone refractor optics provide exceptional coverage and uniformity in Types 2, 3, 4, and FT distributions.
- Silicone optical material does not yellow or crack with age and provides a typical light transmittance of 93-95%.
- Zero uplight.
- Available in 5000K, 4000K and 3000K color temperatures per ANSI C78.377. Also Available in Phosphor Converted Amber with Peak intensity at 610nm.
- Minimum CRI of 70.

Electrical

- High-performance programmable driver features over-voltage, under-voltage, short-circuit and over temperature protection. Custom lumen and wattage packages available.
- 0-10V dimming (10% - 100%) standard.
- Standard Universal Voltage (120-277 Vac) Input 50/60 Hz or optional High Voltage (347-480 Vac).
- L80 Calculated Life: >100k Hours
- Total harmonic distortion (THD): <20%
- 3L to 12L operating temperature: -40°C to +50°C (-40°F to +122°F)
- 15L operating temperature: -40°C to +45°C (-40°F to +113°F).
- 18L operating temperature: -40°C to +40°C (-40°F to +104°F).
- 21L operating temperature: -40°C to +35°C (-40°F to + 95°F).
- Power factor (PF): >.90
- Input power stays constant over life.
- Optional 10kV surge protection device meets a minimum Category C Low operation (per ANSI/IEEE C62.41.2).
- High-efficacy LEDs mounted to metal-core circuit board to maximize heat dissipation
- Components are fully encased in potting material for moisture resistance. Driver complies with FCC standards. Driver and key electronic components can easily be accessed via hinged door.
- Optional integral emergency battery pack provides 90-minutes of constant power to the LED system, ensuring code compliance. A test switch/indicator button is installed on the housing for ease of maintenance. The fixture delivers 1500 lumens during emergency mode.

Controls

- Integral passive infrared Bluetooth™ motion sensor options. Fixtures operate independently and can be commissioned via an iOS or Android configuration app. Updates and modifications to the control strategy are easily implemented via an intuitive app.
- LSI's AirLink™ Blue lighting control system is a simple feature rich wireless Bluetooth mesh network. The integrated fixture sensor module provides wireless control of grouped fixtures based on motion sensors, daylight or a fully customizable schedule.

Installation

- Universal wall mounting plate easily mounts directly to 4" octagonal or square junction box.
- 2 fasteners secure the hinged door underneath the housing and provide quick & easy access to the electrical compartment for installing/servicing.
- Optional terminal block accepts up to 12 ga wire.

Warranty

- LSI luminaires carry a 5-year limited warranty. Refer to https://www.lsicorp.com/resources/terms-conditions-warranty/ for more information.
- 1 Year warranty on Battery Back-up option.

Listings

- Listed to UL 1598 and UL 8750.
- Meets Buy American Act requirements.
- IDA compliant; with 3000K or lower color temperature selection.
- Title 24 Compliant; see local ordinance for qualification information.
- Suitable for wet Locations.
- IP65 rated luminaire per IEC 60598.
- 3G rated for ANSI C136.31 high vibration applications when pole mounted (using optional XPMA bracket) or wall mounted.
- IK08 rated luminaire per IEC 66262 mechanical impact code
- DesignLights Consortium® (DLC) Premium qualified product. Not all versions of this product may be DLC Premium qualified. Please check the DLC Qualified Products List at www.designlights.org/QPL to confirm which versions are qualified.

Type : _____

Mirada Medium Wall Sconce (XWM) Outdoor Wall Sconce

Have questions? Call us at (800) 436-7800

ORDERING GUIDE

Back to Quick Links

TYPICAL ORDER EXAMPLE: **XWM 2 LED 03L 30 UE BRZ ALSC**

Family	Distribution	Light Source	Lumen Package	Color Temperature
XWM - Mirada Medium Wall Sconce	**2** - Type 2 **3** - Type 3 **4** - Type 4 **FT** - Type 4 Forward Throw	**LED**	**3L** - 3,000 **4L** - 4,000 **6L** - 6,000 **8L** - 8,000 **12L** - 12,000 **15L** - 15,000 **18L** - 18,000 **21L** - 21,000 **Custom Lumen Packages**[1]	**30** - 3000K **40** - 4000K **50** - 5000K **AMB** - Phosphor Converted Amber[2]

Voltage	Finish	Controls	Options
UE - Universal Voltage (120-277V) **HV** - High Voltage (347-480V)	**BLK** - Black **BRZ** - Dark Bronze **GMG** - Gun Metal Gray **GPT** - Graphite **MSV** - Metallic Silver **PLP** - Platinum Plus **SVG** - Satin Verde Green **WHT** - White	**Blank** - None **Wireless Controls** **ALSC** - Airlink Synapse Control System **ALSCS01** - AirLink Synapse Control System with 8-12' Motion Sensor **ALSCS02** - AirLink Synapse Control System with 12-20' Motion Sensor **ALBCS1** - AirLink Blue Wireless Motion & Photo Sensor Controller (8-24' MH)[3] **ALBCS2** - AirLink Blue Wireless Motion & Photo Sensor Controller (25-40' MH)[3] **Standalone Controls** **DIM** - 0-10v Dimming leads extended to housing exterior **IMSBT1** - Integral Bluetooth™ Motion and Photocell Sensor (8-24' MH)[3,4] **IMSBT2** - Integral Bluetooth™ Motion and Photocell Sensor (25-40' MH)[3,4] **Button Type Photocells** **PCI120** - 120V **PCI208-277** - 208 -277V **PCI347** - 347V	**Blank** - None **BB** - Battery Back-up (0°C)[5] **CWBB** - Cold Weather Battery Backup (-20°C)[5] **XPMA** - Pole Mounting Bracket **SP1** - 10kV Surge Protection **TB** - Terminal Block

Need more information? Click here for our glossary

Have additional questions? Call us at (800) 436-7800

FUSING ACCESSORY ORDERING INFORMATION[6]

Part Number	Description
FK120[7]	FK120 - Single Fusing
FK277[7]	FK277 - Single Fusing
FK347[7]	FK347 - Single Fusing
DFK208[7]	DFK - Double Fusing
DFK240[7]	DFK - Double Fusing (240V)
DFK480[7]	DFK - Double Fusing (480V)

MOUNTING ACCESSORY ORDERING INFORMATION[6]

Part Number[8]	Description
8093742CLB	XWM Wet Location Surface Conduit/Wiring Box
751652	10' Linear Bird Spike Kit (2' Recommended per Luminaire)

1 Custom lumen and wattage packages available consult factory, Values are within industry standard tolerances but not DLC listed.
2 Only available in 6L Lumen Package. Consult factory for lead time and availability.
3 IMSBT and ALBCS control options are not available in 3L or 4L lumen packages when high voltage (HV) is specified.
4 IMSBTxL is field configurable via the Lewitron app that can be downloaded from your smartphone's app store.
5 Not available in HV.
6 Accessories are shipped separately and field installed.
7 Fusing must be located in a hand hole for pole or in the junction box.
8 "CSB" to be replaced by paint finish selection. See Finish options for paint color selections.

6/30/2026 2:32:09 PM

CSL | ECO DOWNLIGHTS

Spec-00273 NEW ECO 5", V-9.0 Revised 05/15/24

Project: _____


Type: _____

Note: _____

ECO 5" LED DOWNLIGHT



ED5ANC, ED5LANC

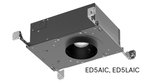


ED5AIC, ED5LAIC



ED5NC, ED5LNIC



ED5RM, ED5LRIC

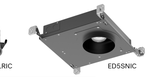

ED5SNIC

LED LIGHT ENGINE	
RATED WATTAGES	29.5W, 24W, 15.3W
DELIVERED LUMENS	Up to 2657 lm
EFFICACY	Up to 104 LPW
CCT @ 90CRI	2700K, 3000K, 3500K, 4000K, Warm Dim
COLOR QUALITY	90+ CRI, 2-Step SDCM
LED LIFETIME	55,000 hours @ L90

SILENT VU™ OPTICS TECHNOLOGY	
OPTICS	50° Installed, 10°, 30°, 80° available
ADJUSTABLE	0° to 45° tilt (Adjustable housings only)
MEDIA	Clear, Solite, Frosted, Linear Spread

POWER SUPPLY	
INPUT VOLTAGE	120/277V 50/60Hz
DIMMING	TRIAC, ELV and 0-10V, dims to 1%
SERVICABILITY	Below ceiling access

DELIVERED LUMENS MATRIX

ED5 (29.5W)	10° OPTIC	30° OPTIC	50° OPTIC	80° OPTIC
2700K (90CRI)	2275 lm	2403 lm	2139 lm	1624 lm
3000K (90CRI)	2458 lm	2597 lm	2311 lm	1755 lm
3500K (90CRI)	2516 lm	2657 lm	2366 lm	1796 lm
4000K (90CRI)	2590 lm	2735 lm	2435 lm	1849 lm

ED5 NIC, RIC (15.3W)	10° OPTIC	30° OPTIC	50° OPTIC	80° OPTIC
Warm Dim (98 CRI, R9>90)	1030 lm	1081 lm	992 lm	723 lm

ED5 AIC, ANC (24W)	10° OPTIC	30° OPTIC	50° OPTIC	80° OPTIC
Warm Dim (98 CRI, R9>90)	1472 lm	1545 lm	1418 lm	1033 lm

ED5L (15.3W)	10° OPTIC	30° OPTIC	50° OPTIC	80° OPTIC
2700K (90CRI)	1348 lm	1424 lm	1268 lm	963 lm
3000K (90CRI)	1457 lm	1539 lm	1370 lm	1040 lm
3500K (90CRI)	1491 lm	1575 lm	1402 lm	1065 lm
4000K (90CRI)	1535 lm	1621 lm	1443 lm	814 lm

ED5S (24W)	10° OPTIC	30° OPTIC	50° OPTIC	80° OPTIC
2700K (90CRI)	1953 lm	2063 lm	1836 lm	1394 lm
3000K (90CRI)	2110 lm	2229 lm	1984 lm	1507 lm
3500K (90CRI)	2160 lm	2282 lm	2031 lm	1542 lm
4000K (90CRI)	2223 lm	2348 lm	2090 lm	1587 lm
Warm Dim (98 CRI, R9>90)	1472 lm	1545 lm	1418 lm	1033 lm

TRIM OPTIONS

- Fixed or Adjustable
- Round or Square
- Standard or Trimless
- Wall Wash
- Wet Location

TRIM COLORS

- White
- Black
- Champagne
- Champagne w/White Flange
- Black w/White Flange
- Silver w/White Flange

HOUSING

- New Construction includes (2) galvanized steel adjustable hanger bars
- Remodel option available
- 5/8"-2" ceiling thickness
- Min Plenum Height: 2 ½" Shallow
- Ceiling Material: Drywall, T-bar grid
- Steel junction box with up to (4) ½" knockouts
- AIC, NIC, RIC, SNIC models are Air Tight. .
- AIC, SNIC models are CCEA compliant. (Note: polycell spray-in foam insulation must be kept 3" from housing)

LISTING/WARRANTY

- cULus Listed
- UL Listed for Damp Location (All Styles)
- IC Rated and Non IC Rated Available
- CCEA Approved (AIC, SNIC Models)
- Five (5) years limited warranty
- UL Listed for Wet Location (Wet Location Trim Style)
- CA Title 24-JA8 Compliant (AIC, NIC, RIC, SNIC Models)
- ASTM E283 Certified Airtight (AIC, NIC, RIC, SNIC Models)

WET LOCATION IC RATED AIRTIGHT WARM DIM DIMMABLE JA8 TITLE 24 2022 READY 5 YEAR LIMITED WARRANTY CCEA GREEN

14508 Nelson Ave. City of Industry, CA 91744 • tel: 626.336.4511 • fax: 626.330.4266 • www.cslighting.com
©2024 Creative Systems Lighting, A Division of Troy-CSL Lighting, Inc. All rights reserved. Subject to change without notice.
Patent: cslighting.com/patents

CSL CREATIVE SYSTEMS LIGHTING

CSL | ECO DOWNLIGHTS

Spec-00273 NEW ECO 5", V-9.0 Revised 05/15/24

Project: _____

Type: _____

Note: _____

ECO 5" LED DOWNLIGHT

ORDER MATRIX

ED5

ECO 5" HOUSING + LIGHT ENGINE ORDER MATRIX (Example: ED5AIC-309050-30S)

HOUSING BASE		LED PERFORMANCE				DRIVER ASSEMBLY	
FAMILY APERTURE	INSTALLATION TYPE	CCT	CRI	OPTIC		WATTAGE	LED DIMMING DRIVER
○ **ED5** ECO 5"	○ **AIC** Adjustable New Construction, IC, CCEA ○ **ANC** Adjustable New Construction ○ **NC** New Construction ○ **RM** Remodel	○ **-27** 2700K ○ **-30** 3000K ○ **-35** 3500K ○ **-40** 4000K	**90** 90 CRI	**50** 50° Flood Installed **10°, 30°, 80°** optics available from the Additional Optics Accessories table below		○ **-30** 29.5W	**S**[1] Universal Dimming Driver (1%-100% 0-10V, TRIAC, ELV, 120V/277V)

FAMILY APERTURE	INSTALLATION TYPE	CCT	CRI	OPTIC	WATTAGE	LED DIMMING DRIVER
○ **ED5** ECO 5" Warm Dim	○ **AIC**[1] Adjustable New Construction, IC, CCEA ○ **ANC**[1] Adjustable New Construction ○ **NIC**[1] New Construction IC ○ **RIC**[1] Remodel IC	**-WD**[2] 1800K-3000K Warm Dim	**98** 98 CRI Warm Dim	**50** 50° Flood Installed **10°, 30°, 80°** optics available from the Additional Optics Accessories table below	○ **-16**[3] 15.3W NIC or RIC Installation Type Only ○ **-25**[1,3] 24W AIC or ANC Installation Type Only	**S**[3] Universal Dimming Driver (1%-100% 0-10V, TRIAC, ELV, 120V/277V)

1. AIC or ANC Installation Type and Wattage Code -25, NIC or RIC Installation Type and Wattage Code -16.
2. Wattage Code -25 Title 24 JA-8 compliant only with 10°, 30° or 50° optic installed.
3. TRIAC, ELV dimming for 120V only.

ED5L

ECO 5" HOUSING + LIGHT ENGINE ORDER MATRIX (Example: ED5LAIC-309050-16S2)

HOUSING BASE		LED PERFORMANCE			DRIVER ASSEMBLY	
FAMILY APERTURE	INSTALLATION TYPE	CCT	CRI	OPTIC	WATTAGE	LED DIMMING DRIVER
○ **ED5L** ECO 5" LPD	○ **AIC** Adjustable New Construction, IC, CCEA ○ **ANC** Adjustable New Construction ○ **NIC** New Construction IC ○ **RIC** Remodel IC	○ **-27** 2700K ○ **-30** 3000K ○ **-35** 3500K ○ **-40** 4000K	**90** 90 CRI	**50** 50° Flood Installed **10°, 30°, 80°** optics available from the Additional Optics Accessories table below	○ **-16** 15.3W	**S2**[1] Phase Control Dimming Driver (1%-100% TRIAC, ELV, 120V/277V)

1. TRIAC, ELV dimming for 120V only.

ED5S

ECO 5" HOUSING + LIGHT ENGINE ORDER MATRIX (Example: ED5SNIC-309050-15S)

HOUSING BASE		LED PERFORMANCE			DRIVER ASSEMBLY	
FAMILY APERTURE	INSTALLATION TYPE	CCT	CRI	OPTIC	WATTAGE	LED DIMMING DRIVER
○ **ED5S** ECO 5" Shallow	**NIC** Shallow Plenum New Construction, IC, CCEA	○ **-27** 2700K ○ **-30** 3000K ○ **-35** 3500K ○ **-40** 4000K	**90** 90 CRI	**50** 50° Flood Installed **10°, 30°, 80°** optics available from the Additional Optics Accessories table below	**-25** 24W	**S**[1] Universal Dimming Driver (1%-100% 0-10V, TRIAC, ELV, 120V/277V)

FAMILY APERTURE	INSTALLATION TYPE	CCT	CRI	OPTIC	WATTAGE	LED DIMMING DRIVER
○ **ED5S** ECO 5" Shallow Warm Dim	**NIC** Shallow Plenum New Construction, IC, CCEA	**-WD** 1800K-3000K Warm Dim	**98** 98 CRI Warm Dim	**50** 50° Flood Installed	**-25** 24W	**S**[1] Universal Dimming Driver (1%-100% 0-10V, TRIAC, ELV, 120V/277V)

1. TRIAC, ELV dimming for 120V only.

14508 Nelson Ave. City of Industry, CA 91744 • tel: 626.336.4511 • fax: 626.330.4266 • www.cslighting.com
©2024 Creative Systems Lighting, A Division of Troy-CSL Lighting, Inc. All rights reserved. Subject to change without notice.
Patent: cslighting.com/patents

CSL CREATIVE SYSTEMS LIGHTING

PRAXIS3
100 Peachtree St NW
Suite 1450 404-875-4500 tel
Atlanta, GA 30303 www.praxis3.com

GEORGIA REGISTERED No. 041508 PROFESSIONAL ENGINEER RAHN ONEAL WILLIAMS

Copyright (c) 2024 Praxis3, LLC

All reports, plans, specifications, computer files, field data, notes and other documents and instruments prepared by Praxis3 shall retain all common law, statutory and other reserved rights, including copyright thereto.

This drawing may not be reproduced in whole or in part without written permission of Praxis3. It is to be returned upon request. Scales as stated are valid on the original drawings.

Rev	Date	Comments
	07/02/2026	PERMIT SET

Client:

FIFTH THIRD BANK

Project Number: 26032
Project Name:

FIFTH THIRD BANK WATSON 1,900 SF

2711 WATSON BOULEVARD
WARNER ROBBINS, GA 31093

Key Plan:

Sheet Title:

EXTERIOR LIGHTING CUTSHEETS


Sheet Number:

E-602

Project Name _____ Qty _____

Type _____ Catalog / Part Number _____



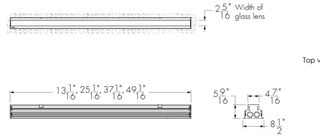


Photometric Summary

	Delivered output (lm)	Intensity (peak cd)
WW	3,634	10,795
8"x8"	4,512	59,238
10"x10"	4,410	33,872
10"x30"	4,586	25,296
10"x60"	3,876	12,062
10"x90"	4,077	6,927
15"x25"	4,346	19,773
30"x30"	4,730	16,886
30"x60"	4,035	5,317
35"x35"	4,612	11,616
50"x80"	4,656	3,904
60"x60"	3,868	3,368
80"x80"	4,548	2,992
90"x90"	4,070	2,132

Based on HO 40K full output, 4ft [1219mm].
DMX/RDM configuration.
2.5° factory-set tilt setting for WW optic, 0° tilt setting for all other optics.
Photometric performance is measured in compliance with IESNA LM-79-08.

Optics

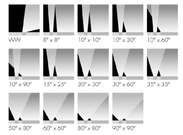

Description

The Lumenfacade Inground is an LED luminaire designed for ground-recessed lighting applications, including asymmetric wall washing, grazing, and linear wayfinding. An innovative, plug and play design simplifies installation, protecting the system from water infiltration and ensuring long-lasting performance. Featuring second generation LED technology, the Lumenfacade Inground is available in four different sizes (12 in, 24 in, 36 in or 48 in), with a wide choice of outputs, color temperatures, color-mixing systems, optics and controls. A unique asymmetric wallwash distribution is also available, providing exceptional uniformity and brightness for walls and signage.

Features

Construction	Walk over compliant up to 500 kg in any type of ground, Walk over compliant up to 1000 kg in concrete
Color and Color Temperature	2200K, 2700K, 3000K, 3500K, 4000K, Red, Green, Blue
Length (nominal)	12 in, 24 in, 36 in, 48 in
Optics	Asymmetric wallwash, 8° x 8°, 10° x 10°, 10° x 30°, 10° x 60°, 10° x 90°, 15° x 25°, 30° x 30°, 30° x 60°, 35° x 35°, 50° x 80°, 60° x 60°, 80° x 80°, 90° x 90°
Tilt Setting (factory set)	0 degrees, 2.5 degrees, 5 degrees, 20 degrees
Optical Option	Internal louver
Options	Anti-slip lens, CE (certification covers European Economic Area)
Power Consumption	5 W/ft (meets ASHRAE standards for linear lighting on building facades - not available for 12 in fixture lengths), 8.5 W/ft (RO version), 15.25 W/ft (HO version). Typically 20% higher for 12 in fixture lengths
Warranty	5-year limited warranty

Specification Sheet

lumenfacade
Inground
LOI

WHITE AND STATIC COLORS

Colors and Color Temperatures

2200K 2700K 3000K 3500K 4000K

Red Green Blue

Controls

ON/OFF 0-10V DALI

lumentalk DMXrdm EcoSystem Enabled

Ratings

IP68 IK10

Certifications

Performance

Maximum Delivered Output	4,730 lm (48 in fixture, 4000K, 30° x 30°, 0° tilt setting, DMX/RDM)
Maximum Delivered Intensity	59,238 cd at nadir (48 in fixture, 4000K, 8° x 8°, 0° tilt setting, DMX/RDM)
Illuminance at Distance	Minimum 1 fc at 243 ft (48 in fixture, 4000K, 8° x 8°, 0° tilt setting, DMX/RDM)
Color Consistency	2 SDCM, 3 SDCM (2200K)
Color Rendering	Minimum CRI 80
Lumen Maintenance	L70 280,000 hrs, L95 35,000 hrs

Physical

Optical Chamber Material	Aluminum
Blockout Material	Polymer recycled PVC reinforced with a stainless steel frame
Trim Material	Anodized aluminum
Lens Material	Tempered glass
End Cap Material	Die cast aluminum
Hardware Material	Stainless steel
Weight	12 in: 7.5 lbs, 24 in: 15.3 lbs, 36 in: 21.4 lbs, 48 in: 27 lbs

Electrical and control

Voltage	120 to 277 volts
Fixture Cable	Power and data in one cable
Leader Cable Conductor	5C #16-5
Connectors	IP68 push-lock
Control	On/Off control, Lumentalk, 0-10V dimming, DALI dimming, Lutron® EcoSystem® Enabled dimming, DMX/RDM enabled
Resolution (DMX/RDM)	Per foot or per fixture (configured with LumenID V3 software), 8-bit or 16-bit

Environmental

Storage Temperature	-40 °F to 185 °F (device must reach start-up temperature value before operating)
Start-up Temperature	-13 °F to 122 °F
Operating Temperature	-40 °F to 122 °F
Ingress Protection Rating	IP68 rated for up to 1 ft, not suitable for permanent immersion applications
Impact Resistance Rating	IK10

Accessories (order separately)

Cables	Lumenfacade Inground Leader Cable, Lumenfacade Inground Jumper Cable
Electrical Accessories	Lumenfacade Inground Junction Box

lumenpulse™ 1220 Marie-Victorin Blvd., Longueuil, QC, J4G 2H9, CA info@lumenpulse.com www.lumenpulse.com T United States 617.307.5700 | Canada 1.877.937.3003 | 514.937.3003 www.lumenpulse.com/products/2556 F 514.937.6289

LMPG Inc., reserves the right to make changes to this product at any time without prior notice and such modification shall be effective immediately
2022.12.19 copyright © 2022 LMPG Inc.
EM - R24

PRAXIS3

100 Peachtree St NW
Suite 1450
Atlanta, GA 30303

404-875-4500 tel
www.praxis3.com

GEORGIA REGISTERED No. 044560 PROFESSIONAL ENGINEER RAHN ONEAL WILLIAMS

Copyright (c) 2024 Praxis3, LLC

All reports, plans, specifications, computer files, field data, notes and other documents and instruments prepared by Praxis3 shall retain all common law, statutory and other reserved rights, including copyright thereto.

This drawing may not be reproduced in whole or in part without written permission of Praxis3. It is to be returned upon request. Scales as stated are valid on the original drawings.

Rev	Date	Comments
	07/02/2026	PERMIT SET

Client:

FIFTH THIRD BANK

Project Number: 26032
Project Name:

FIFTH THIRD BANK WATSON 1,900 SF

2711 WATSON BOULEVARD
WARNER ROBBINS, GA 31093

Key Plan:

Sheet Title:

EXTERIOR LIGHTING CUTSHEETS

Sheet Number:

E-603

6/30/2026 2:32:09 PM

(NEW)

PANEL PP

VOLTAGE: 208 / 120 **AMP: 400**
PHASE: 3 **MAIN: MCB**

DESCRIPTION	KW	BKR	CK	PH	CK	BKR	KW	DESCRIPTION
RTU-1	15.6	90/3	1	A	2	30/3	0.0	SPD
-----	15.6	---	3	B	4	---	0.0	-----
-----	15.6	---	5	C	6	---	0.0	-----
RTU-1	15.6	90/3	7	A	8	30/2	2.3	CU-1/FCU-1
-----	15.6	---	9	B	10	---	2.3	-----
-----	15.6	---	11	C	12	20/2	1.3	WH-WATER HEATER
SPACE		---	13	A	14	---	1.3	-----
SPACE		---	15	B	16	---		SPACE
SPACE		---	17	C	18	---		SPARE
SPACE		---	19	A	20	---		SPARE
SPACE		---	21	B	22	---		SPARE
SPACE		---	23	C	24	---		SPARE
PANEL RP-A	12.2	225/3	25	A	26	---		
-----	13.6	---	27	B	28	---		SPACE SUBFEED SECTION
-----	16.9	---	29	C	30	---		

NOTE: PROVIDE EQUIPMENT GROUND BUS

Phase A Load (kVA)	46.8	Connected kVA	143.0	100%	A-B Balance
Phase B Load (kVA)	47.0	Dem. kVA	129.2	95%	B-C Balance
Phase C Load (kVA)	49.2	Dem. Amps	358.8	95%	C-A Balance

(NEW)

PANEL RP-A

VOLTAGE: 208 / 120 **AMP: MLO**
PHASE: 3 **MAIN: 225**

	DESCRIPTION	KW	BKR	CK	PH	CK	BKR	KW	DESCRIPTION	
	MISC. FIRE ALARM CONTROL PANEL	0.2	20/1	1	A	2	20/1	0.4	LTG-BACK OF HOUSE	
	LTG - PARPET LIGHTING	0.5	20/1	3	B	4	20/1	0.4	LTG-BUILDING CANOPY	
	LTG - ENTRY/WEATHER VESTIBULE	0.1	20/1	5	C	6	20/1	1.2	SIGN-BUILDING SIGN - BACK	
	REC - EMPLOYEE LOUNGE	0.4	20/1	7	A	8	20/1	0.1	LTG-TRANSACTION BAR	
	LTG - RELAXED SEATING	0.2	20/1	9	B	10	20/1	0.5	LTG VESTIBULE	
	SIGN-BUILDING SIGN - FRONT	1.2	20/1	11	C	12	20/1	0.9	REC-PRINTER TRANSACTION	
	REC - COPIER LOBBY	0.8	20/1	13	A	14	20/1	0.0	MISC-LIGHTING CONTROL PANEL	
	LTG - ELEC/IT/MEETING/BOOTHS	0.2	20/1	15	B	16	20/1	0.7	REC-RESTROOM/JAN	
	REC - BOOTH 104	0.5	20/1	17	C	18	20/1	0.9	REC-MEETING ROOM	
#	REC - REFIGERATOR	1.2	20/1	19	A	20	20/1	0.5	MISC-DDCV HOTBOX	*
	REC - WORK ROOM	0.4	20/1	21	B	22	20/1	0.4	REC-PRINTER -TRANSACTION	
	MISC - MECHOSHADES	0.5	20/1	23	C	24	20/1	0.2	REC-TECH WALL/GATHERING	
	MISC - RECIRCULATING PUMP	0.2	20/1	25	A	26	20/1	0.3	MISC-DOOR MOTOR/PUSH...	
	MISC - CONDENSATE PUMP	0.1	20/1	27	B	28	20/1	1.5	REC-TCR TRANSACTION BAR	
	MID- IRRIGATION BACKFLOW	0.5	20/1	29	C	30	20/1	1.1	REC-QUAD ELEC/IT	
	REC - TRANSACTION BAR	0.7	20/1	31	A	32	20/1	0.4	REC-ROOF	
	REC - TRANSACTION BAR	0.7	20/1	33	B	34	20/2	0.0	LTG-LIGHT POLES	
	MISC-DOOR MOTOR/PUSH...	0.3	20/1	35	C	36	---	0.0	------	
	REC-TRANSACTION	0.4	20/1	37	A	38	20/1	1.8	MISC-DRIVE-UP ATM	
	REC-VESTIBULE/ELEC/IT	0.4	20/1	39	B	40	20/1	0.5	MISC-VTM	
	REC-TECH WALL	0.4	20/1	41	C	42	20/1	0.5	REC-PHONE RM	
	REC-EMPLOYEE LOUNGE	0.5	20/1	43	A	44	20/1	1.2	SIGN-BUILDING SIGN - BACK	
	REC-QUAD ELEC/IT	1.4	20/1	45	B	46	20/1	1.1	REC-QUAD ELEC/IT	
	MISC-CRITICAL LIGHTING...	0.2	20/1	47	C	48	20/1	1.5	REC-DISH WASHER	#
	MISC-MECHOSHADES-MEETING..	0.5	20/1	49	A	50	20/1	0.7	REC-NIGHT DEPOSITORY	
	REC-RELAXED SEATING	0.5	20/1	51	B	52	20/1	1.4	REC-QUAD ELEC/IT	
	REC-MICROWAVE LOUNGE	1.5	20/1	53	C	54	20/1	0.4	REC-LIBRARY COUNTER	
	MISC-VAT BLOWER	0.5	20/1	55	A	56	20/1	0.2	MISC-DTOPEN/CLOSE SIGN	
	MISC-LIGHTING CONTACTOR	0.2	20/1	57	B	58	20/1	0.5	MISC-TRANSAC MECHOSHADES	
	REC-LIBRARY COUNTER	0.4	20/1	59	C	60	20/1	0.6	LTG-DRIVE UP ATM TOPPER	
	REC-PHONE RM	0.2	20/1	61	A	62	20/1	0.6	LTG-DRIVE UP ATM TOPPER	
	REC-TRANSACTION DISPLAY	0.4	20/1	63	B	64	20/1	0.5	MISC-BOOTH MECHOSHADES	
	LTG-LIGHT POLES	0.0	20/2	65	C	66	20/1	0.9	REC-WORK ROOM	
	-----	0.0	---	67	A	68	20/1	0.2	REC-DRINKING FOUNTAIN	#
	MISC-VAT DIVERTER	0.5	20/1	69	B	70	20/1	0.2	MISC-IRRIGATION CONTROL	
	REC-ADA COUNTER	0.9	20/1	71	C	72	20/1	1.0	OPEN/CLOSE SIGN	
	LTG-ATM CANOPY	0.1	20/1	73	A	74	20/1	0.1	LIGHTING CONTACTOR	
	REC-WORK 111	0.4	20/1	75	B	76	20/1		SPARE	
	SIGN-MONUMENT SIGN	1.2	20/1	77	C	78	20/1		SPARE	
	REC-MONUMENT SIGN RECEPT	0.2	20/1	79	A	80	20/1		SPARE	
	SPARE		20/1	81	B	82	20/1		SPARE	
	SPARE		20/1	83	C	84	20/1		SPARE	

NOTE: PROVIDE EQUIPMENT GROUND BUS
- PROVIDE CONNECTION TO NEW GFCI CIRCUIT BREAKER.
* - PROVIDE CONNECTION TO NEW GFPE CIRCUIT BREAKER.

Phase A Load (kVA)	12.2	Connected kVA	42.6	90%	A-B Balance
Phase B Load (kVA)	13.6	Dem. kVA	31.4	81%	B-C Balance
Phase C Load (kVA)	16.9	Dem. Amps	87.1	72%	C-A Balance

PANELBOARD NOTES:

1. PROVIDE PANELBOARD AS SPECIFIED ON ELECTRICAL PANEL SCHEDULES AND RISER DIAGRAM.
2. CONTRACTOR SHALL ENSURE ALL NEC WORKING SPACE AND DEDICATED EQUIPMENT SPACE CLEARANCES ARE PROVIDED PER NEC 110. IF FIELD CONDITIONS DO NOT ALLOW FOR ADEQUATE CLEARANCE AT THE LOCATION SHOWN ON THE PLANS, THE CONTACTOR SHALL PROPOSE AN ALTERNATE LOCATION FOR REVIEW AND APPROVAL BY ENGINEER PRIOR TO ROUGH-IN OF PANEL.
3. FIELD COORDINATE INSTALLATION WITH OTHER TRADES TO ENSURE NO FOREIGN SYSTEMS ARE LOCATED WITHIN THE DEDICATED EQUIPMENT SPACE OF THE ELECTRICAL EQUIPMENT.
4. ALL BUSING SHALL BE COPPER.
5. BOLT-ON BREAKERS ONLY.
6. PROVIDE DOOR-IN-DOOR TRIM.
7. PROVIDE TYPEWRITTEN CIRCUIT DIRECTORY CARD.
8. ALL PANELBOARDS SHALL BE SUPPLIED FROM THE SAME MANUFACTURER.
9. IN EXISTING INSTALLATIONS, NEW CIRCUIT BREAKERS SHALL MATCH EXISTING IN TYPE AND AIC RATING, UNO.
10. LOAD TYPES IN DESCRIPTION AS FOLLOWS:

BOLD TEXT	NEW LOAD, WIRE, CONDUIT, CIRCUIT BREAKER(AS APPLICABLE)
GREY TEXT	EXISTING LOAD, WIRE, CONDUIT, CIRCUIT BREAKER(AS APPLICABLE) TO REMAIN
(OLD X-#)	RELOCATED CIRCUIT FROM OLD PANEL 'X', CIRCUIT '#'
CLG	COOLING
EWH	ELECTRIC WATER HEATER
HTG	HEATING
KIT	KITCHEN
LTG	LIGHTING
MISC	MISCELLANEOUS
MTR	MOTOR
REC	RECEPTACLE
REF	REFRIGERATION

11. CIRCUIT BREAKER TYPE ABBREVIATIONS ARE AS FOLLOWS:

AFCI	ARC-FAULT CIRCUIT INTERRUPTER
F/RED	RED MARKING & "FIRE ALARM CIRCUIT"
GFCI	GROUND-FAULT CIRCUIT INTERRUPTER
GFPE	30 mA EQUIPMENT GROUND FAULT PROTECTION
HT2	HANDLE TIE FOR SHARED NEUTRAL CIRCUIT (2 POLE)
HT3	HANDLE TIE FOR SHARED NEUTRAL CIRCUIT (3 POLE)
L/ON	LOCKABLE "LOCK ON" HANDLE HARDWARE
L/OFF	"LOCK OFF"
TAN	TANDEM
SHNT	SHUNT TRIP
SWD	SWITCH DUTY RATED
SWN	SWITCHED NEUTRAL

12. CIRCUIT BREAKER FURNISHED AS FOLLOWS:

ETR	EXISTING TO REMAIN
FW	FACTORY WIRED
NEW	NEW TO MATCH EXISTING
REM	REMOVE EXISTING AND PROVIDE NEW

13. LOAD FUNCTION AS FOLLOWS:

CONT	CIRCUIT CONTROLLED BY CONTRACTOR
HOOD	CIRCUIT CONTROLLED BY HOOD FIRE SUPPRESSION SYSTEM
T/C	CIRCUIT THRU TIME CLOCK
PHO	CIRCUIT THRU PHOTOCELL
LCP	CIRCUIT THRU LIGHTING CONTROL PANEL
L/C	CIRCUIT THRU LIGHTING CONTACTOR

PRAXIS3

100 Peachtree St NW
Suite 1450
Atlanta, GA 30303
404-875-4500 tel
www.praxis3.com

GEORGIA REGISTERED No. 041508 PROFESSIONAL ENGINEER RAHN ONEAL WILLIAMS

Copyright (c) 2024 Praxis3, LLC

All reports, plans, specifications, computer files, field data, notes and other documents and instruments prepared by Praxis3 shall retain all common law, statutory and other reserved rights, including copyright thereto.

This drawing may not be reproduced in whole or in part without written permission of Praxis3. It is to be returned upon request. Scales as stated are valid on the original drawings.

Rev	Date	Comments
	07/02/2026	PERMIT SET

Client:
FIFTH THIRD BANK

Project Number: 26032
Project Name:
FIFTH THIRD BANK WATSON
1,900 SF

2711 WATSON BOULEVARD
WARNER ROBBINS, GA 31093

Key Plan:

Sheet Title:
ELECTRICAL PANEL SCHEDULES

Sheet Number:
E-610

6/30/2026 2:32:09 PM



1 E-700 ELECTRICAL DEVICE PLAN
1/4" = 1'-0"

6/30/2026 2:32:10 PM

PRAXIS3

100 Peachtree St NW
Suite 1450
Atlanta, GA 30303

404-875-4500 tel
www.praxis3.com

GEORGIA REGISTERED No. 041508 PROFESSIONAL ENGINEER RAHN ONEAL WILLIAMS

Copyright (c) 2024 Praxis3, LLC

All reports, plans, specifications, computer files, field data, notes and other documents and instruments prepared by Praxis3 shall retain all common law, statutory and other reserved rights, including copyright thereto.

This drawing may not be reproduced in whole or in part without written permission of Praxis3. It is to be returned upon request. Scales as stated are valid on the original drawings.

Rev	Date	Comments
	07/02/2026	PERMIT SET

Client:
FIFTH THIRD BANK


Project Number: 26032
Project Name:
FIFTH THIRD BANK WATSON 1,900 SF

2711 WATSON BOULEVARD
WARNER ROBBINS, GA 31093


Key Plan:

Sheet Title:
ELECTRICAL DEVICE PLAN


Sheet Number:
E-700

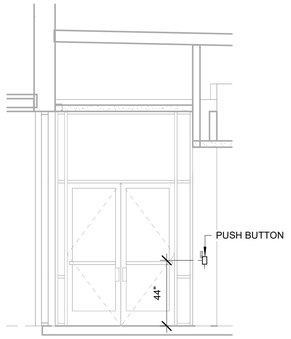


4 E-701 ELEVATION ENTRY 101/2
1/4" = 1'-0"

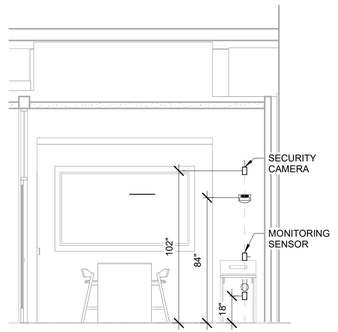


3 E-701 ELEVATION ENTRY 101/1
1/4" = 1'-0"

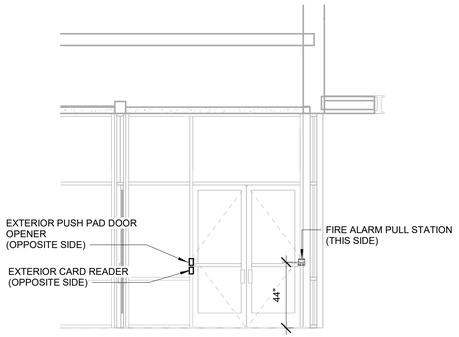


2 E-701 ELEVATION WEATHER VESTIBULE 100/2
1/4" = 1'-0"

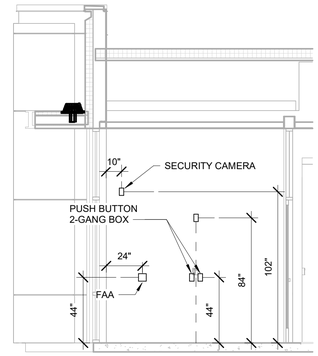


1 E-701 ELEVATION WEATHER VESTIBULE 100/1
1/4" = 1'-0"

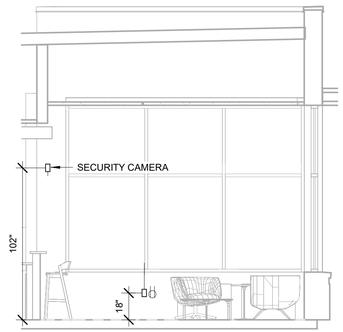


8 E-701 ELEVATION RELAXED SEATING 102/1
1/4" = 1'-0"

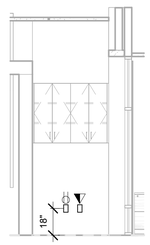


7 E-701 ELEVATION GATHERING AREA
1/4" = 1'-0"

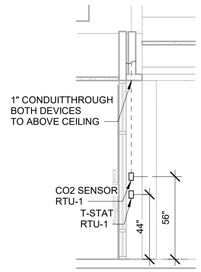


6 E-701 ELEVATION GATHERING AREA 103/3
1/4" = 1'-0"

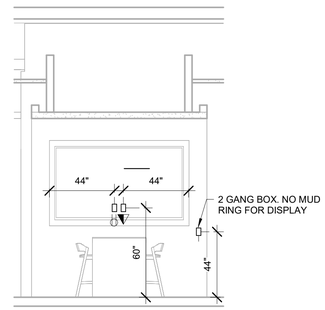


5 E-701 ELEVATION GATHERING AREA 103/1
1/4" = 1'-0"

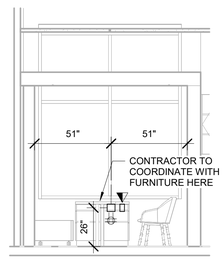

11 E-701 ELEVATION BOOTH 104/2
1/4" = 1'-0"

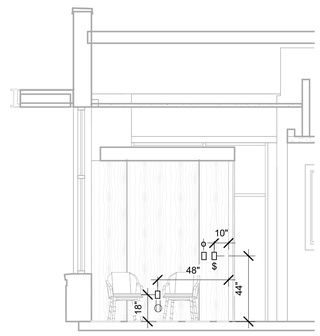

10 E-701 ELEVATION BOOTH 104/1
1/4" = 1'-0"

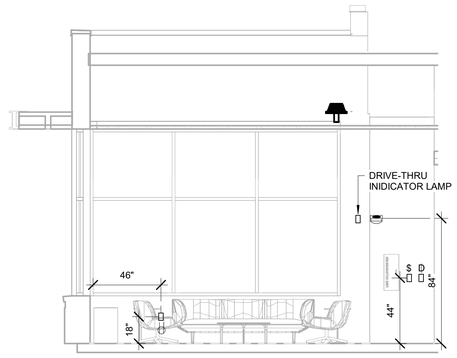

9 E-701 ELEVATION RELAXED SEATING 102/2
1/4" = 1'-0"

6/30/2026 2:32:13 PM

PRAXIS3
100 Peachtree St NW
Suite 1450
Atlanta, GA 30303
404-875-4500 tel
www.praxis3.com

GEORGIA REGISTERED No. 041408 PROFESSIONAL ENGINEER RAHN ONEAL WILLIAMS

Copyright (c) 2024 Praxis3, LLC

All reports, plans, specifications, computer files, field data, notes and other documents and instruments prepared by Praxis3 shall retain all common law, statutory and other reserved rights, including copyright thereto.

This drawing may not be reproduced in whole or in part without written permission of Praxis3. It is to be returned upon request. Scales as stated are valid on the original drawings.

Rev	Date	Comments
	07/02/2026	PERMIT SET

Client:
FIFTH THIRD BANK


Project Number: 26032
Project Name:
FIFTH THIRD BANK WATSON 1,900 SF

2711 WATSON BOULEVARD
WARNER ROBBINS, GA 31093


Key Plan:

Sheet Title:
ELECTRICAL ELEVATIONS


Sheet Number:
E-701

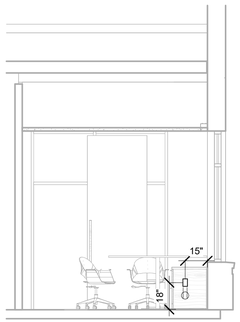


4 E-702 ELEVATION MEETING ROOM 105/4
1/4" = 1'-0"

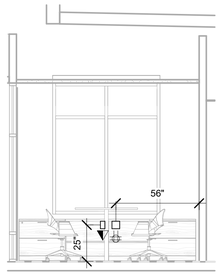


3 E-702 ELEVATION MEETING ROOM 105/3
1/4" = 1'-0"

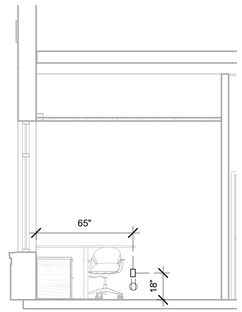


2 E-702 ELEVATION MEETING ROOM 105/2
1/4" = 1'-0"

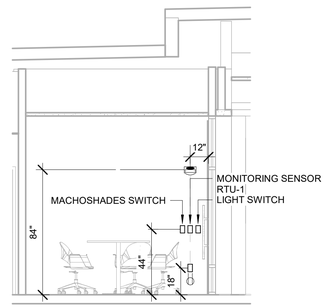


1 E-702 ELEVATION MEETING ROOM 105/1
1/4" = 1'-0"

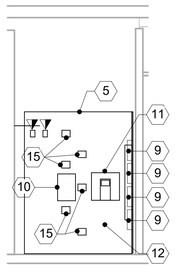


8 E-702 ELEVATION ELEC/IT 106/4
1/4" = 1'-0"

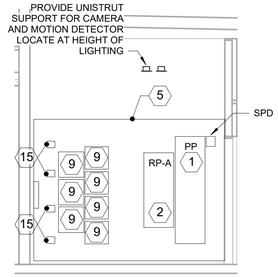

7 E-702 ELEVATION ELEC/IT 106/3
1/4" = 1'-0"

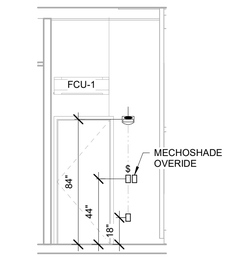

6 E-702 ELEVATION ELEC/IT 106/2
1/4" = 1'-0"

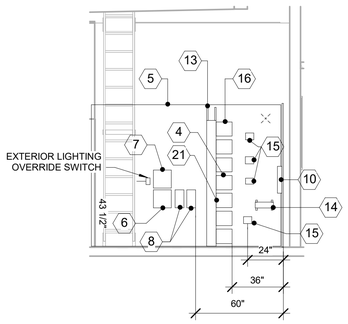


5 E-702 ELEVATION ELEC/IT 106/1
1/4" = 1'-0"

KEYED NOTES:


1. PANEL PP
2. PANEL RP-A SEC I
3. NOT USED
4. DATA RACK
5. PLYWOOD BACKBOARD: PROVIDE 8' X (LENGTH AS REQUIRED) X 3/4" FIRE-RATED PLYWOOD BACKBOARDS MOUNTED VERTICALLY ALONG ALL NER ROOM WALLS. UL FIRE RATING LABEL SHALL REMAIN VISIBLE AFTER INSTALLATION.
6. LIGHTING CONTROL PANEL
7. DIMMER PANEL
8. LIGHTING CONTACTOR
9. SECURITY PANEL
10. TELECOMMUNICATION BOX
11. FIRE ALARM CONTROL PANEL: FIRE ALARM CONTROL PANEL WITH TOP OF CABINET NOT TO EXCEED 72" ABOVE THE FINISHED FLOOR.
12. DIGITAL ALARM COMMUNICATOR TRANSMITTER
13. CABLE TRAY
14. GROUND BUS BAR: PROVIDE A 12" X 2" X 1/4" COPPER GROUND BAR WITH STANDOFF INSULATORS ON TELEPHONE BACKBOARD. PROVIDE #2 AWG COPPER GROUND ROUTED IN 1" CONDUIT FROM TELEPHONE BACKBOARD GROUNDING BAR TO ELECTRICAL SERVICE GROUNDING ELECTRODE SYSTEM. COORDINATE EXACT LOCATION ON BACKBOARD WITH TELEPHONE SERVICE PROVIDER.
15. QUAD RECEPTACLE
16. PROVIDE A PANDUIT (PART NUMBER: R2P) TWO POST CABLE MANAGEMENT RACK SYSTEM IN IT/ELEC ROOM
17. PROVIDE PANDUIT (PART NUMBER: WMPV45E) VERTICAL CABLE MANAGER AND PANDUIT (PART NUMBER: WMP1E) HORIZONTAL CABLE MANAGER IN ELECTRICAL/IT ROOM AS REQUIRED.
18. PROVIDE 18" STEEL HOMACO LADDER RACK ABOVE TBB AT 90" AFF. BOND ALL SECTIONS WITH #6 AWG GREEN INSULATED COPPER GROUND TO GROUND BUS ON TBB.
19. PROVIDE (1) CAT 6 CABLE RUN FROM RACK TO DRIVE UP EQUIPMENT MATRIX LOCATION. COORDINATE EXACT LOCATION WITH OWNER VENDOR.
20. ELECTRICAL CONTRACTOR TO PULL CABLES FOR MOOD MEDIA. EQUIPMENT PROVIDED BY OWNER

ELEC/IT 106 ELEVATION GENERAL NOTES:


1. ELEVATIONS ARE SHOWN FOR REFERENCE ONLY. COORDINATE WITH RESPECTIVE EQUIPMENT SUPPLIERS FOR EXACT DIMENSIONS, REQUIRED CLEARANCES, LOCATIONS, MOUNTING HEIGHTS, AND ROUGH-IN REQUIREMENTS AND ADJUST IN FIELD AS REQUIRED.
2. MAINTAIN A MINIMUM OF 36" CLEAR IN THE FRONT OF THE ELECTRICAL PANELS PER NEC 110.26.
3. EXPOSED CONDUIT IN ELECTRICAL/IT ROOM SHALL BE EMT; MC CABLE SHALL NOT BE EXPOSED.
4. ALL WIRING DEVICES IN NEC AND ELECTRICAL ROOM SHALL BE FLUSH MOUNTED.
5. LOW VOLTAGE CONDUITS SHALL BE PROVIDED WITH PLASTIC INSULATED CONDUIT BUSHINGS ON EACH END AND NYLON PULL STRING.

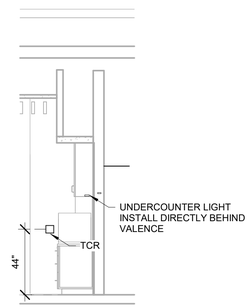


12 E-702 ELEVATION LIBRARY 107/3
1/4" = 1'-0"

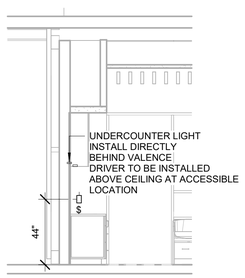

11 E-702 ELEVATION LIBRARY 107/2
1/4" = 1'-0"

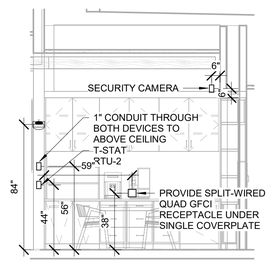

10 E-702 ELEVATION LIBRARY 107/1
1/4" = 1'-0"

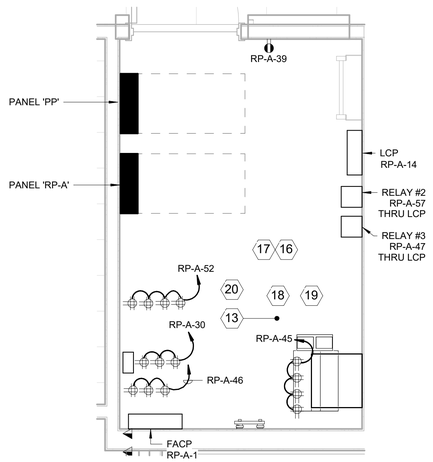

9 E-702 ENLARGED ELEC/IT ROOM 1
1/2" = 1'-0"

PRAXIS3
100 Peachtree St NW
Suite 1450
Atlanta, GA 30303
404-875-4500 tel
www.praxis3.com

GEORGIA REGISTERED No. 041508 PROFESSIONAL ENGINEER RAHN ONEAL WILLIAMS

Copyright (c) 2024 Praxis3, LLC

All reports, plans, specifications, computer files, field data, notes and other documents and instruments prepared by Praxis3 shall retain all common law, statutory and other reserved rights, including copyright thereto.

This drawing may not be reproduced in whole or in part without written permission of Praxis3. It is to be returned upon request. Scales as stated are valid on the original drawings.

Rev	Date	Comments
	07/02/2026	PERMIT SET

Client:
FIFTH THIRD BANK

Project Number: 26032
Project Name:
FIFTH THIRD BANK WATSON 1,900 SF


2711 WATSON BOULEVARD
WARNER ROBBINS, GA 31093

Key Plan:

Sheet Title:
ELECTRICAL ELEVATIONS

Sheet Number:
E-702


6/30/2026 2:32:16 PM

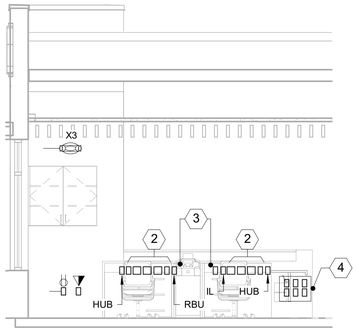


NOTE:

1. TRANSACTION BAR DEVICE LAYOUT IS DIAGRAMMATIC FOR REFERENCE AND NOT TO SCALE. COORDINATE WITH MILLWORK SHOP DRAWINGS AND ARCHITECTURAL ELEVATIONS FOR EXACT PLACEMENT.
2. ELECTRICAL CONTRACTOR SHALL SUPPORT ALL LOW VOLTAGE WIRING AND TIE TOGETHER MULTIPLE RUNS CABLES WITH VELCRO AS REQUIRED FOR A NEAT INSTALLATION.
3. ELECTRICAL CONTRACTOR SHALL COORDINATE WITH MILLWORK SHOP DRAWINGS TO PLAN ALL CONDUIT ROUTING. SUPPORT ALL RACEWAYS PER NEC.


4 E-703 ELEVATION TRANSACTION 108/4
1/4" = 1'-0"

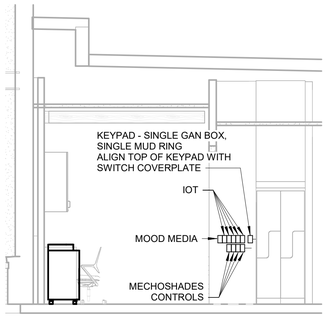

3 E-703 ELEVATION TRANSACTION 108/3
1/4" = 1'-0"

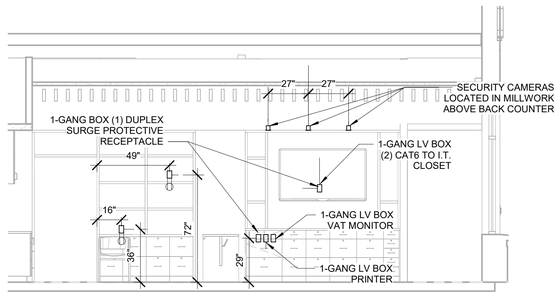


2 E-703 ELEVATION TRANSACTION BAR 108/2
1/4" = 1'-0"

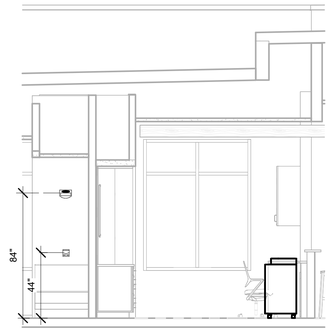


1 E-703 ELEVATION TRANSACTION 108/1
1/4" = 1'-0"

KEYED NOTES:


1. TCR POWER & DATA OUTLET - MOUNT SO THAT TCR CAN BE PLACED UP AGAINST THE MILLWORK AND SO THAT THE POWER & DATA CORD OF THE EQUIPMENT WILL REACH THE OUTLET. IDENTIFY RECEPTACLE 'TCR'.
2. OUTLETS SHALL BE PLACED IN OPENINGS MADE AVAILABLE FROM MILLWORK. DIAGRAM SHOWS GENERAL PLACEMENT OF OUTLETS WITHIN THE OPENINGS. COORDINATE WITH MILLWORK SHOP DRAWINGS AND ARCHITECTURAL ELEVATIONS FOR EXACT PLACEMENT.
3. ALL POWER WIRING AND DATA WIRING SHALL BE RUN THROUGH OPENINGS PROVIDED BY MILLWORK PROVIDER. GENERAL LOCATION - COORDINATE WITH MILLWORK SHOP DRAWINGS AND ARCHITECTURAL ELEVATIONS FOR EXACT DIMENSIONS.
4. RECESSED ELECTRICAL BOXES (ARLINGTON BOXES TVBS507 3-GANG) FOR POWER & DATA - SEE NOTES ON FLOOR PLAN FOR REQUIREMENTS.

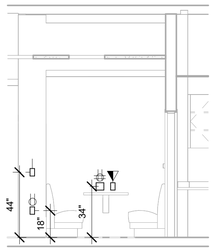


8 E-703 ELEVATION EMPLOYEE LOUNGE 110/4
1/4" = 1'-0"

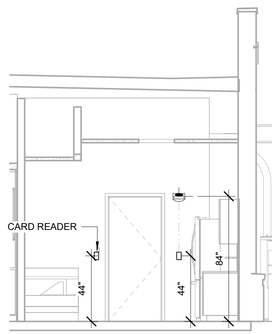


7 E-703 ELEVATION EMPLOYEE LOUNGE 110/3
1/4" = 1'-0"

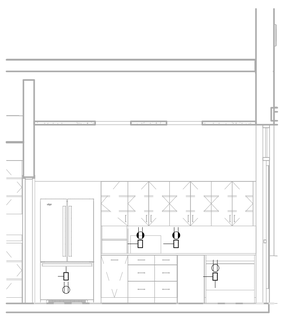


6 E-703 ELEVATION EMPLOYEE LOUNGE 110/2
1/4" = 1'-0"

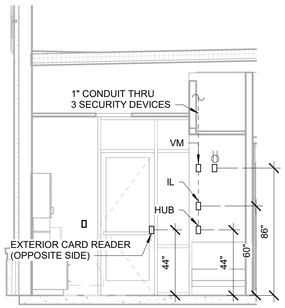


5 E-703 ELEVATION EMPLOYEE LOUNGE 110/1
1/4" = 1'-0"

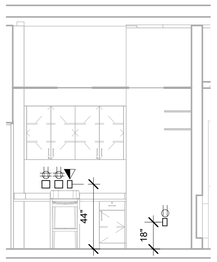

11 E-703 ELEVATION WORK ROOM 111/3
1/4" = 1'-0"

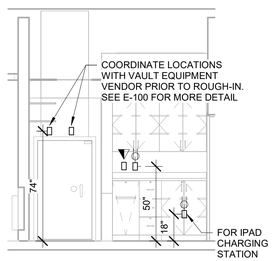

10 E-703 ELEVATION WORK ROOM 111/2
1/4" = 1'-0"

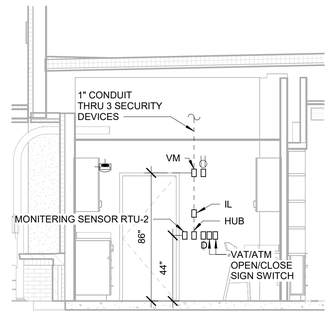

9 E-703 ELEVATION WORK ROOM 111/1
1/4" = 1'-0"

6/30/2026 2:32:19 PM

PRAXIS3
100 Peachtree St NW
Suite 1450
Atlanta, GA 30303
404-875-4500 tel
www.praxis3.com

GEORGIA REGISTERED No. 041508 PROFESSIONAL ENGINEER RAHN ONEAL WILLIAMS

Copyright (c) 2024 Praxis3, LLC

All reports, plans, specifications, computer files, field data, notes and other documents and instruments prepared by Praxis3 shall retain all common law, statutory and other reserved rights, including copyright thereto.

This drawing may not be reproduced in whole or in part without written permission of Praxis3. It is to be returned upon request. Scales as stated are valid on the original drawings.

Rev	Date	Comments
	07/02/2026	PERMIT SET

Client:
FIFTH THIRD BANK


Project Number: 26032
Project Name:
FIFTH THIRD BANK WATSON 1,900 SF

2711 WATSON BOULEVARD
WARNER ROBBINS, GA 31093


Key Plan:

Sheet Title:
ELECTRICAL ELEVATIONS


Sheet Number:
E-703

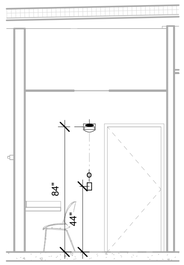


4 E-704 ELEVATION PHONE ROOM 114/1
1/4" = 1'-0"

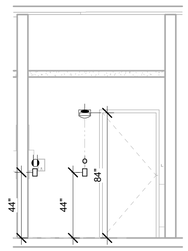


3 E-704 ELEVATION MENS 113/2
1/4" = 1'-0"

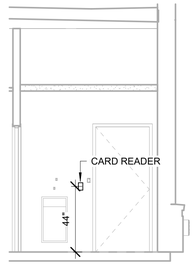


2 E-704 ELEVATION MENS 113/1
1/4" = 1'-0"

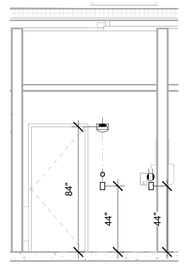


1 E-704 ELEVATION WOMENS 112/1
1/4" = 1'-0"

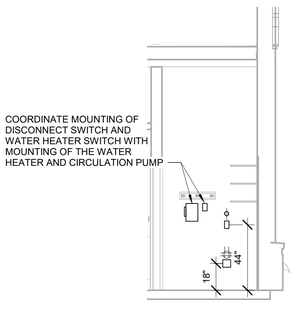


8 E-704 ELEVATION JANITOR 115/2
1/4" = 1'-0"

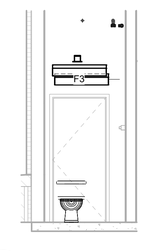


7 E-704 ELEVATION JANITOR 115/1
1/4" = 1'-0"

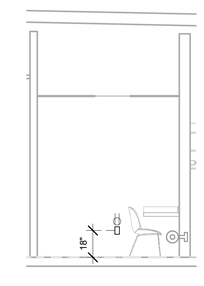


6 E-704 ELEVATION PHONE ROOM 114/3
1/4" = 1'-0"

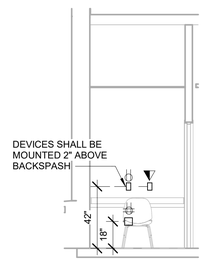


5 E-704 ELEVATION PHONE ROOM 114/2
1/4" = 1'-0"

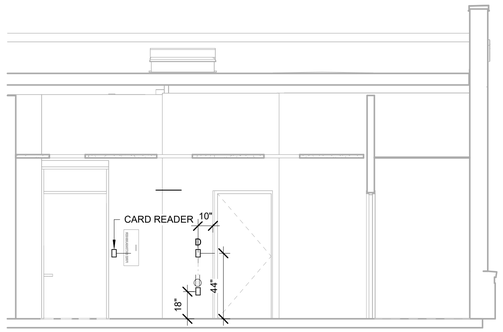

11 E-704 ELEVATION VESTIBULE 116/3
1/4" = 1'-0"

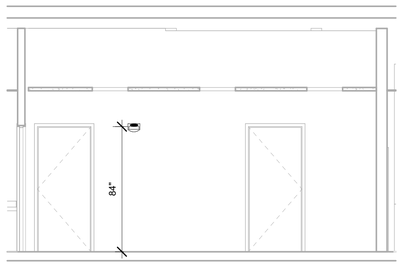

10 E-704 ELEVATION VESTIBULE 116/2
1/4" = 1'-0"

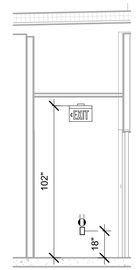

9 E-704 ELEVATION VESTIBULE 116/1
1/4" = 1'-0"

6/30/2026 2:32:21 PM

PRAXIS3

100 Peachtree St NW
Suite 1450
Atlanta, GA 30303

404-875-4500 tel
www.praxis3.com

GEORGIA REGISTERED No. 041508 PROFESSIONAL ENGINEER RAHN ONEAL WILLIAMS

Copyright (c) 2024 Praxis3, LLC

All reports, plans, specifications, computer files, field data, notes and other documents and instruments prepared by Praxis3 shall retain all common law, statutory and other reserved rights, including copyright thereto.

This drawing may not be reproduced in whole or in part without written permission of Praxis3. It is to be returned upon request. Scales as stated are valid on the original drawings.

Rev	Date	Comments
	07/02/2026	PERMIT SET

Client:

FIFTH THIRD BANK

Project Number: 26032
Project Name:

FIFTH THIRD BANK WATSON 1,900 SF

2711 WATSON BOULEVARD
WARNER ROBBINS, GA 31093

Key Plan:

Sheet Title:


ELECTRICAL ELEVATIONS

Sheet Number:

E-704

NOTE:
PREFERRED SUPPLIER FOR SWITCHGEAR IS WESCO.


CONTACT DELENA STUART-WATSON, GLOBAL ACCOUNT MANAGER
TEL: 214-549-1164
EMAIL: DELENA.WATSON@ANIXTER.COM

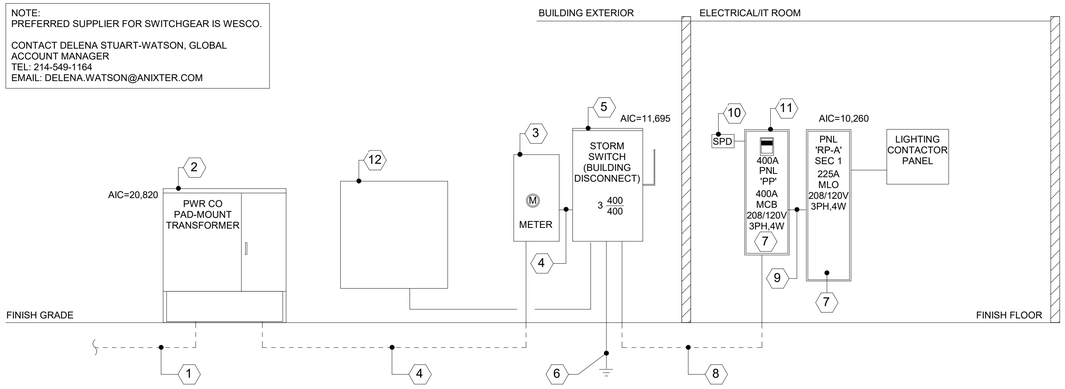

1 E-800 ELECTRICAL RISER DIAGRAM
N.T.S.

KEYED NOTES:

1. ELECTRIC UTILITY PRIMARY FEEDERS: PROVIDE COMPLETE UNDERGROUND CONDUIT SYSTEMS IF REQUIRED BY THE LOCAL POWER COMPANY FROM TRANSFORMER TO POINT OF INTERCEPTION AT EDGE OF PROPERTY LINE. REFER TO ELECTRICAL SITE PLAN FOR ROUTING AND ADDITIONAL REQUIREMENTS.
2. ELECTRIC UTILITY XFMR (PAD-MOUNTED): REFER TO ELECTRICAL SITE PLAN FOR LOCATION AND ADDITIONAL REQUIREMENTS.
3. ELECTRIC UTILITY METER (SELF-CONTAINED): PROVIDE 320A CONTINUOUS 400A MAX, 600V, 3PH, 4W, SELF-CONTAINED METER BASE AND ENCLOSURE. COORDINATE METER BASE SELECTION AND INSTALLATION WITH POWER COMPANY.
4. 400A SERVICE ENTRANCE: PROVIDE 2 SETS OF 4-#3/0 KCMIL EACH IN 4" CONDUIT.
5. STORM SWITCH - MANUAL TRANSFER SWITCH: MANUFACTURED BY ESL POWER SYSTEMS INC, PART# 3042-10V: SFD4-400C-400C-208-311-S-C, 400A, 208Y/120VAC, 65KAIC,3PH, 4W SAFETY INTERLOCK MANUAL TRANSFER SWITCH, WALL MOUNT, TYPE 3R, 14GA GALVANNEALED STEEL, POWDER COATED WRINKLE GRAY (RAL7035). FACTORY WIRED COMPLETE USING INSULATED FLEXIBLE BUS WITH 400A MOLDED CASE 3-POLE C/B FOR UTILITY SIDE (ACCEPTS (2) 2/0-500KCMIL WIRE PER PHASE/NEUTRAL), 400A MOLDED CASE 3-POLE C/B FOR GENERATOR SIDE, MALE CAM-STYLE RECEPTACLES: (1) A-PHASE - BLACK, (1) B-PHASE-RED, (1) C-PHASE-BLUE,(1) NEUTRAL-WHITE, (1) GROUND-GREEN (MATING PLUGS NOT PROVIDED). INCLUDES DEADFRONT, PAD LOCKABLE DOOR WITH STOP AND HANDLE COVER. LOAD WIRE RANGE (2) 2/0-500KCMIL PER PHASE/NEUTRAL. CONDUIT ENTRY AREA THROUGH BOTTOM LEFT SIDE OR LEFT SIDE AT BOTTOM. SUITABLE FOR USE AS SERVICE EQUIPMENT. USE COPPER WIRE. UL/cUL 1008 LISTED.
6. GROUND ELECTRODE CONDUCTOR: PROVIDE #3/0 CU GROUNDING ELECTRODE CONDUCTOR (GEC). TO GROUNDING ELECTRODE SYSTEM CONSISTING OF MIN (2) 3/4" CU CLAD GROUND RODS, BUILDING STEEL, CONCRETE ENCASED ELECTRODE, INTERSYSTEM BONDING JUMPER, AND METALLIC COLD WATER PIPE.
7. ELECTRICAL PANEL: PROVIDE PANELBOARD AS SPECIFIED ON ELECTRICAL PANEL SCHEDULES.
8. 400A FEEDER: PROVIDE 2 SETS OF 4-#3/0 KCMIL, #3 GND EACH IN 4" CONDUIT.
9. 225A FEEDER: PROVIDE 4-#4/0, #4 GND IN 3" CONDUIT.
10. SURGE PROTECTION DEVICE: PROVIDE SURGE PROTECTION DEVICE (SPD) SURGE APT-TE-02-XDS-10-4X-KITFMXF, REFER TO "SPD PANELBOARD INSTALLATION DETAIL" ON SHEET E-501.
11. PROVIDE POWER SCOUT METER, PSHD3, WITH CONNECTION TO THE BUILDING MANAGEMENT SYSTEM AND 400A CTS WITHIN THE MAIN PANEL. PROVIDE ALL CONDUIT AND WIRE TO THE BMS & CONNECT WITH 4#12 & 1#12(G).
COORDINATE WITH STEVE SMITH AT IOT - CONTACT:
STEPHEN SMITH
STEPHENS@IOFTEAM.COM
OFFICE PHONE: 512-649-5142 EXT. 105
DIRECT LINE:
512-686-3978.
12. TEMPORARY GENERATOR WITH OVERCURRENT PROTECTION AND CABLE BY OTHERS

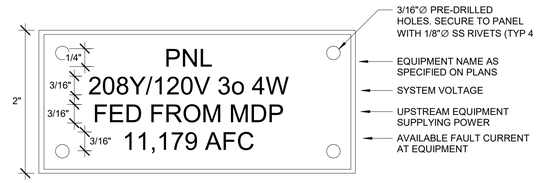




NOTES:

1. ALL ELECTRICAL EQUIPMENT, SUCH AS SWITCHBOARDS, SWITCHGEAR, PANELBOARDS, INDUSTRIAL CONTROL PANELS, METER SOCKET ENCLOSURES, MOTOR CONTROL CENTERS, AND SAFETY DISCONNECT SWITCHES SHALL BE PROVIDED WITH AN ARC FLASH HAZARD WARNING LABEL.
2. THE LABEL SHALL BE OF SUFFICIENT DURABILITY TO WITHSTAND THE ENVIRONMENT INVOLVED.
3. THE LABEL SHALL BE PERMANENTLY AFFIXED TO THE EQUIPMENT AND SHALL NOT BE HAND WRITTEN.
4. THOROUGHLY CLEAN SURFACE PRIOR TO ADHERING LABEL.
5. PROVIDE BRADY B-302 SERIES 3.5"x5" POLYESTER LABEL WITH PERMANENT ACRYLIC ADHESIVE, CATALOG #101950 (5 PACK), #102307 (100 PACK), OR APPROVED EQUAL.

2 ARC FLASH HAZARD WARNING LABEL REQUIREMENTS
N.T.S.

NOTES:

1. ALL DISTRIBUTION EQUIPMENT SUCH AS PANELBOARDS, SWITCHBOARDS, DISCONNECTS, TRANSFORMERS, ETC. SHALL BE PROVIDED WITH AN EQUIPMENT LABEL PER THE REQUIREMENTS OF THIS DETAIL.
2. LABELS SHALL BE 2-PLY ENGRAVED PLASTIC LAMINATE WITH BLACK TYPEFACE LETTERS. LABEL BACKGROUND SHALL FOLLOW THE BELOW COLOR SCHEME:
   A. NORMAL POWER - WHITE
   B. UPS POWER - BLUE
   C. LIFE SAFETY POWER - YELLOW
3. LABEL MATERIAL SHALL BE DURABLE, UV STABLE, RATED FOR OUTDOOR USE, AND ABRASION RESISTANT. WHERE ATTACHED TO NEMA 4X EQUIPMENT, LABELS SHALL IN ADDITION BE CHEMICAL RESISTANT.
4. LABELS SHALL BE PERMANENTLY ATTACHED TO ENCLOSURE COVER WITH RIVETS UNLESS DOING SO COMPROMISES ITS NEMA / IP RATING. LABELS FOR ENCLOSURES WITH WELDED SEAMS AND GASKETED DOORS SUCH AS THOSE RATED NEMA 12 OR NEMA 4 SHALL BE INSTALLED USING PERMANENT WEATHER-, UV-, AND TEMPERATURE-RESISTANT DOUBLE-SIDED MOUNTING TAPE ONLY.
5. A SUBMITTAL WITH A COMPLETE LIST OF EQUIPMENT LABELS SHALL BE PROVIDED FOR ENGINEER APPROVAL PRIOR TO ORDERING.
6. LABELS SHALL INDICATE NO LESS THAN THE FOLLOWING:
   A. EQUIPMENT NAME
   B. THE NOMINAL SYSTEM VOLTAGE WHICH SAID EQUIPMENT IS CONNECTED TO
   C. THE EQUIPMENT NAME SUPPLYING POWER TO SAID EQUIPMENT
   D. THE AVAILABLE FAULT CURRENT AT SAID EQUIPMENT

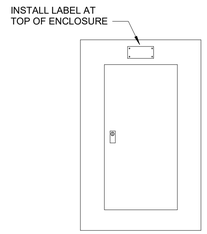

3 EQUIPMENT LABEL DETAIL
N.T.S.

6/30/2026 2:32:22 PM

PRAXIS3
100 Peachtree St NW
Suite 1450
Atlanta, GA 30303
404-875-4500 tel
www.praxis3.com

GEORGIA REGISTERED No. 041508 PROFESSIONAL ENGINEER RAHN ONEAL WILLIAMS

Copyright (c) 2024 Praxis3, LLC

All reports, plans, specifications, computer files, field data, notes and other documents and instruments prepared by Praxis3 shall retain all common law, statutory and other reserved rights, including copyright thereto.

This drawing may not be reproduced in whole or in part without written permission of Praxis3. It is to be returned upon request. Scales as stated are valid on the original drawings.

Rev	Date	Comments
	07/02/2026	PERMIT SET

Client:
FIFTH THIRD BANK

Project Number: 26032
Project Name:
FIFTH THIRD BANK WATSON
1,900 SF

2711 WATSON BOULEVARD
WARNER ROBBINS, GA 31093

Key Plan:

Sheet Title:
ELECTRICAL RISER DIAGRAM

Sheet Number:
E-800