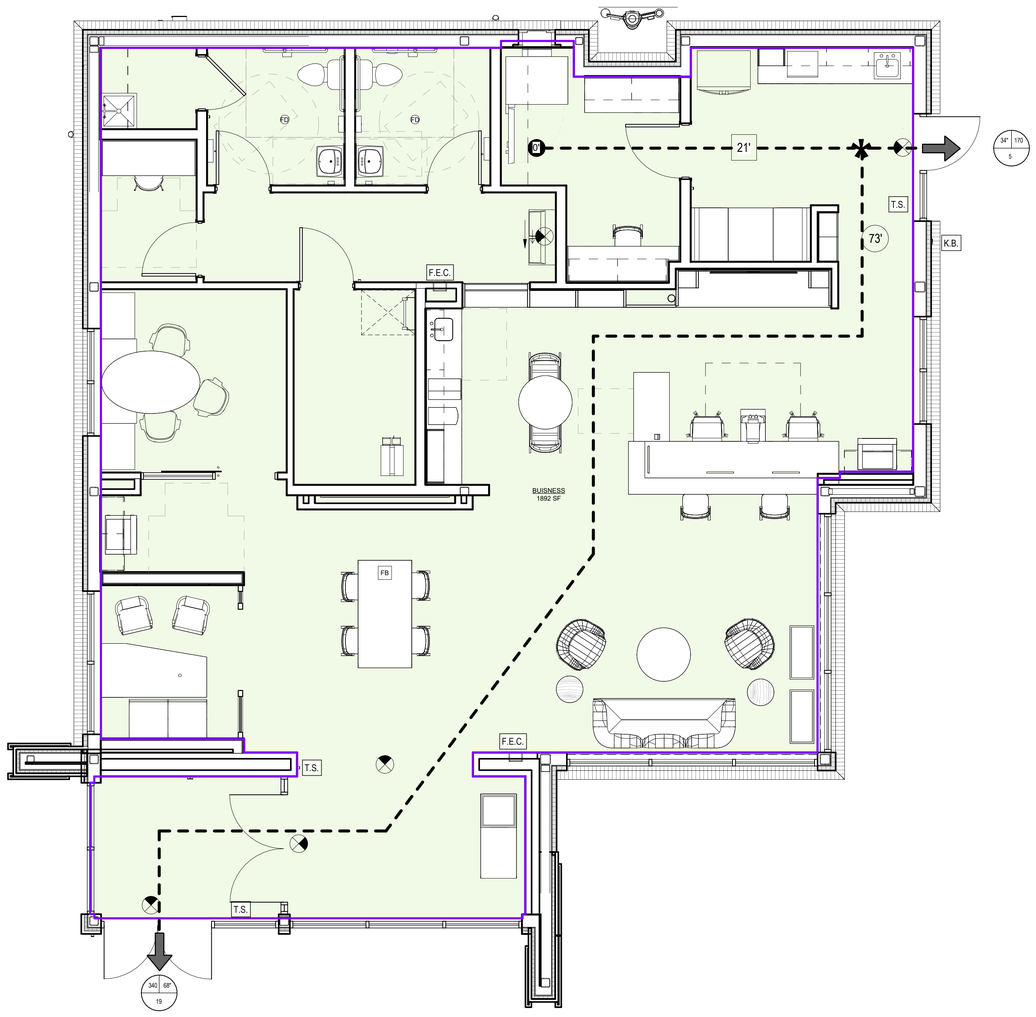


LIFE SAFETY GENERAL NOTES

1. PROVIDE FIRE EXTINGUISHERS PER NFPA10 AS REQUIRED
2. PROVIDE 1 FOOTCANDLE FOR EMERGENCY LIGHTING

LIFE SAFETY NOTES

- EMERGENCY EXIT
- TRAVEL DISTANCE
- COMMON PATH OF TRAVEL
- EXIT SIGN
- F.E. — SURFACE MOUNTED FIRE EXTINGUISHER 10LB UL RATED 4A:80B:C
- F.E.C. — RECESSED FIRE EXTINGUISHER CABINET 10LB UL RATED 4A:80B:C
- M.C.# — MAXIMUM CAPACITY SIGNAGE TO READ AS FOLLOWS: "MAXIMUM OCCUPANT LOAD XXX PERSONS BY ORDER OF THE FIRE MARSHAL" REFER TO A-410 FOR MOUNTING INFORMATION
- T.S. — TACTILE SIGNAGE PER NFPA 101-7.10.13, REFER TO G-002 FOR MOUNTING INFORMATION
- K.B. — KNOX BOX. VERIFY LOCATION WITH LOCAL MUNICIPALITY TO INSURE COMPLIANCE
- COMMON PATH OF TRAVEL POINT OF DECISION
- MOST REMOTE POINT ON FLOOR FROM AN EXIT
- A. CLEAR EXIT WIDTH
  B. MAXIUM CALCULATED OCCUPANT LOAD EACH EXIT DOOR CAN ACCOMMODATE BASED ON EGRESS WIDTH (1005.3.2)
  C. ACTUAL OCCUPANT LOAD FOR EACH DOOR

CODE INFORMATION

JURISDICTION: CITY OF WARNER ROBINS, GA

APPLICABLE CODES

- 2024 INTERNATIONAL BUILDING CODE WITH GA AMENDMENTS
- 2024 INTERNATIONAL FIRE CODE
- 2024 INTERNATIONAL PLUMBING CODE WITH GA AMENDMENTS
- 2024 INTERNATIONAL MECHANICAL CODE WITH GA AMENDMENTS
- 2024 INTERNATIONAL FUEL & GAS CODE WITH GA AMENDMENTS
- 2023 NATIONAL ELECTRICAL CODE WITH GA AMENDMENTS
- 2015 INTERNATIONAL ENERGY CONSERVATION CODE WITH GA AMENDMENTS
- 2018 LIFE SAFETY CODE WITH GA AMENDMENTS NFPA 101
- GEORGIA ACCESSIBILITY CODE
- STANDARDS FOR ACCESSIBLE DESIGN ADA (2010)

PROJECT DATA

OCCUPANCY LOAD	(TBL 1004.5/ SEC. 1004)	AREA	TOTAL
BUSINESS	1 PER 150 GSF	1900 GSF	13 OCC
TOTAL		1900 GSF	13 OCC

MEANS OF EGRESS	REQUIRED	PROVIDED
EXIT ACCESS TRAVEL DISTANCE (NFPA 38.2.6.2)	200' MAX	94'-2" MAX
COMMON PATH OF TRAVEL (NFPA 38.2.5.2.3)	100' MAX	N/A
DEAD END CORRIDOR (NFPA 38.2.5.3.2)	20' MAX	N/A
CORRIDOR WIDTH (NFPA 7.3.4.1 (2) <50 OCC PER 38.2.3.2)	44" MIN	60" MIN
MINIMUM NUMBER OF EXITS REQUIRED (NFPA 38.2.4.3)	1 EXIT	2 EXITS
EXIT WIDTH (NFPA TBL 7.3.3.1)	(0.2") 4" REQ'D PER OCCUPANT	68"
STAIR WIDTH (NFPA TBL 7.3.3.1)	(0.3") 6" REQ'D PER OCCUPANT	N/A

CONSTRUCTION TYPE (TBL 601)		VB
FIRE RESISTANCE REQUIREMENTS	**REQUIRED**	**PROVIDED**
STRUCTURAL FRAMING	0 HOUR	0 HOUR
EXTERIOR & INTERIOR BEARING WALLS	0 HOUR	0 HOUR
EXTERIOR NON-BEARING WALLS	0 HOUR	0 HOUR
INTERIOR NON-BEARING WALLS	0 HOUR	0 HOUR
FLOOR CONSTRUCTION	0 HOUR	0 HOUR
ROOF CONSTRUCTION	0 HOUR	0 HOUR

ALLOWABLE BUILDING HEIGHTS & AREA	REQUIRED	PROVIDED
ALLOWABLE AREA (506.2)	9,000 SF	1892 S.F.
ALLOWABLE HEIGHT (504.3)	40 FT	18'-8"
ALLOWABLE STORIES (504.4)	2 STORIES	1 STORY

INTERIOR FINISHES (803.11)	REQUIRED	PROVIDED
EXIT ENCLOSURES, EXIT PASSAGEWAYS & CORRIDORS	CLASS A	CLASS A
ROOMS AND ENCLOSED SPACES	CLASS C	CLASS C

FIRE PROTECTION SYSTEMS (901.2) (NFPA 38.3.5)	REQUIRED	PROVIDED
SPRINKLER SYSTEM (903.1)	N/A	N/A
FIRE EXTINGUISHERS (906.1)	PER 906.3	2

PLUMBING FIXTURE COUNT	M /F (REQUIRED)	MALE (PROVIDED)	FEMALE (PROVIDED)
OCCUPANCY LOAD/ 2	13/2 = 7 EA	-	-
WATER CLOSET (1:25)	1 PER 25 (FOR THE FIRST 50 OCCUP)	1 W.C.	1 W.C.
URINALS (2/3 SUBSTITUTION ALLOWED)	N/A	N/A	N/A
LAVATORIES (1:40)	1 PER 40 (1ST 80 OCC)	1 LAVS.	1 LAVS.
UNISEX RESTROOMS	N/A	N/A	N/A
TOTAL W.C. REQUIRED		1 W.C.	1 W.C.
DRINKING FOUNTAINS (1 / 500)	1 REQUIRED	2 PROVIDED	
SERVICE SINK	1 REQUIRED	1 PROVIDED	

NFPA REQUIREMENTS	
OCCUPANCY (6.1.11)	BUSINESS
CONSTRUCTION TYPE (TBL A.4.1.1)	V

ALLOWABLE BUILDING HEIGHTS & AREA	REQUIRED	PROVIDED
ALLOWABLE AREA	9,000 SF	1,900 GSF
ALLOWABLE HEIGHT	40 FT	18'-8"
ALLOWABLE STORIES	2 STORIES	1 STORY
EXIT REQUIREMENTS (13.2.4)	1 EXIT	2 EXITS

INTERIOR FINISHES (10.2.2.1)	REQUIRED	PROVIDED
EXIT ENCLOSURE WALL & CEILING FINISHES (7.1.4.1)	CLASS A	CLASS A
FLOOR FINISHES (7.1.4.2)	CLASS I or II	CLASS I or II

FIRE PROTECTION SYSTEMS	REQUIRED	PROVIDED
SPRINKLER SYSTEM (9.7.1.1)	--	--
FIRE EXTINGUISHER (38.3.5)	--	--

NOTE: PROJECT NORTH IS FOR CONSTRUCTION PURPOSES ONLY. REFER TO CIVIL DRAWING FOR TRUE NORTH AND CORRECT BUILDING ORIENTATION AS IT RELATES TO THE SITE.

LIFE SAFETY PLAN | 1/4" = 1'-0" | 1

PRAXIS3
100 Peachtree St NW
Suite 1450
Atlanta, GA 30303
404-875-4500 tel
www.praxis3.com

STATE OF GEORGIA
STUART M. ROMM
07/02/26
CERTIFICATE NO. 3457
REGISTERED ARCHITECT

Copyright (c) 2026 Praxis3, LLC

All reports, plans, specifications, computer files, field data, notes and other documents and instruments prepared by Praxis3 shall retain all common law, statutory and other reserved rights, including copyright thereto.

This drawing may not be reproduced in whole or in part without written permission of Praxis3. It is to be returned upon request. Scales as stated are valid on the original drawings.

Rev	Date	Comments
	07/02/2026	PERMIT SET

Client:
FIFTH THIRD BANK

Project Number: 26302
Project Name:
WATSON BLVD.

2711 WATSON BOULEVARD
WARNER ROBINS, GA 31093

Key Plan:

Sheet Title:
LIFE SAFETY PLAN

Sheet Number:
G-001

7/8/2026 2:37:34 PM