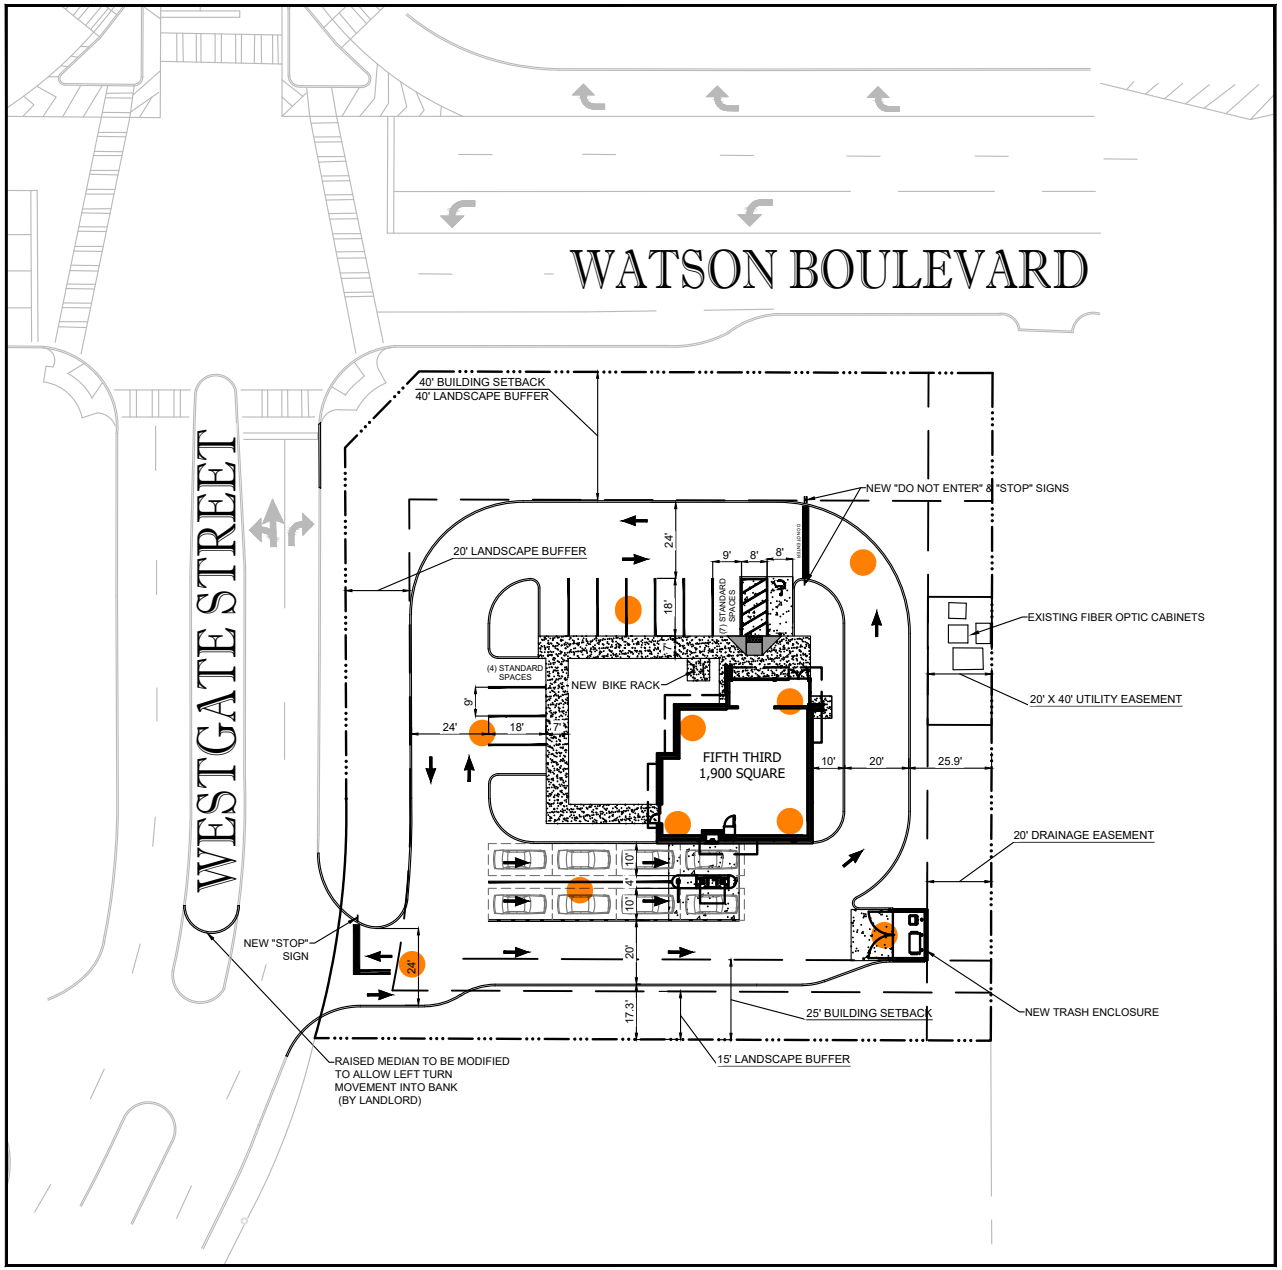


SITE DATA

SITE ADDRESS:	2711 WATSON BLVD WARNER ROBINS, GEORGIA 31093
PIN:	0W07800 05000
BUILDING AREA:	1,900 SF BUILDING
ZONING:	C2
SITE AREA:	42,253 SQ. FT. / 0.97 AC
EXISTING USE:	OFFICE GENERAL C MEDICAL DENTAL B
FUTURE USE:	BANK WITH DRIVE THRU

PARKING DATA

BANK PARKING REQUIRED:	1 SPACE PER 300 SF OF G.F.A. 1,900 SF x (1 / 300 SF) = 7 SPACES
TOTAL PARKING PROVIDED:	STANDARD PARKING = 11 SPACES ACCESSIBLE PARKING = 1 SPACE TOTAL PARKING PROVIDED = 12 SPACES
PARKING SPACE SIZE:	9' x 18' MINIMUM
DRIVE THROUGH QUEUE:	4 SPACES PER ATM LANE 4 SPACES PER TELLER LANE 9' x 18' QUEUE SIZE
LOADING ZONE:	*NOTE-FINANCIAL INSTITUTIONS DO NOT USE LOADING ZONES FOR SECURITY PURPOSES DELIVERY TRUCK WILL PARK DIRECTLY IN FRONT OF MAIN ENTRANCE.

LANDSCAPE REQUIREMENTS:	REQUIRED
LANDSCAPE BUFFER - FRONT (WATSON BLVD)	= 40'
LANDSCAPE BUFFER - SIDE (WESTGATE ST)	= 20'
LANDSCAPE BUFFER - SIDE	= 0'
LANDSCAPE BUFFER - REAR	= 15'

BUILDING REQUIREMENTS:	REQUIRED
BUILDING SETBACK - FRONT (WATSON BLVD)	= 40'
BUILDING SETBACK - SIDE (WESTGATE ST)	= 0'
BUILDING SETBACK - SIDE	= 0'
BUILDING SETBACK - REAR	= 25'

FLOOD ZONE:

DESCRIBED PROPERTY LIES IN FLOOD ZONE X, PER FEMA MAP NO. 13153C0085E DATED DECEMBER 28, 2007.

APPROVAL SIGNATURE

SCALE

0 ' 60 ' 120 '

ARCHITECT/ ENGINEER OF RECORD

BDG ARCHITECTS
400 N Ashley Dr Ste 600
Tampa, Florida 33602

P: 813.323.9233
F: 813.323.9238
www.bdgllp.com

bdg architects

THIS DRAWING AND ANY REPRODUCTIONS ARE THE PROPERTY OF THE ARCHITECTS, AND MAY NOT BE REPRODUCED, PUBLISHED, MODIFIED, OR USED IN ANY WAY WITHOUT EXPRESS WRITTEN NOTICE FROM THE ARCHITECT. DRAWINGS AND ANY REPRODUCTIONS OF THEM SHALL NOT BE SCALED OFF FOR ANY PURPOSE. ANY DISCREPANCIES IN THE DRAWINGS SHALL BE REFERRED IMMEDIATELY TO THE ARCHITECT FOR CLARIFICATION PRIOR TO CONTINUING WITH THE WORK. COMMENCEMENT WITH THE WORK SHALL BE CONSIDERED ACCEPTANCE OF THE INTEGRITY THE DRAWINGS. THE CONTRACTOR IS RESPONSIBLE FOR THE COORDINATION, SCHEDULING, AND CONFORMANCE OF THE WORK OF INVOLVED TRADES. COPYRIGHT 2018, BDG ARCHITECTS, INC. ALL RIGHTS RESERVED.

FIFTH THIRD BANK
WATSON BOULEVARD & WESTGATE ROAD
2711 WATSON BOULEVARD
WARNER ROBINS, GEORGIA 31093

FIFTH THIRD

JOB NO.	260607
DATE:	02-05-26
DRAWN BY:	IEG
SCALE:	1" = 60'

SHEET TITLE:
TEST FOR FIT

SHEET NUMBER:
1B