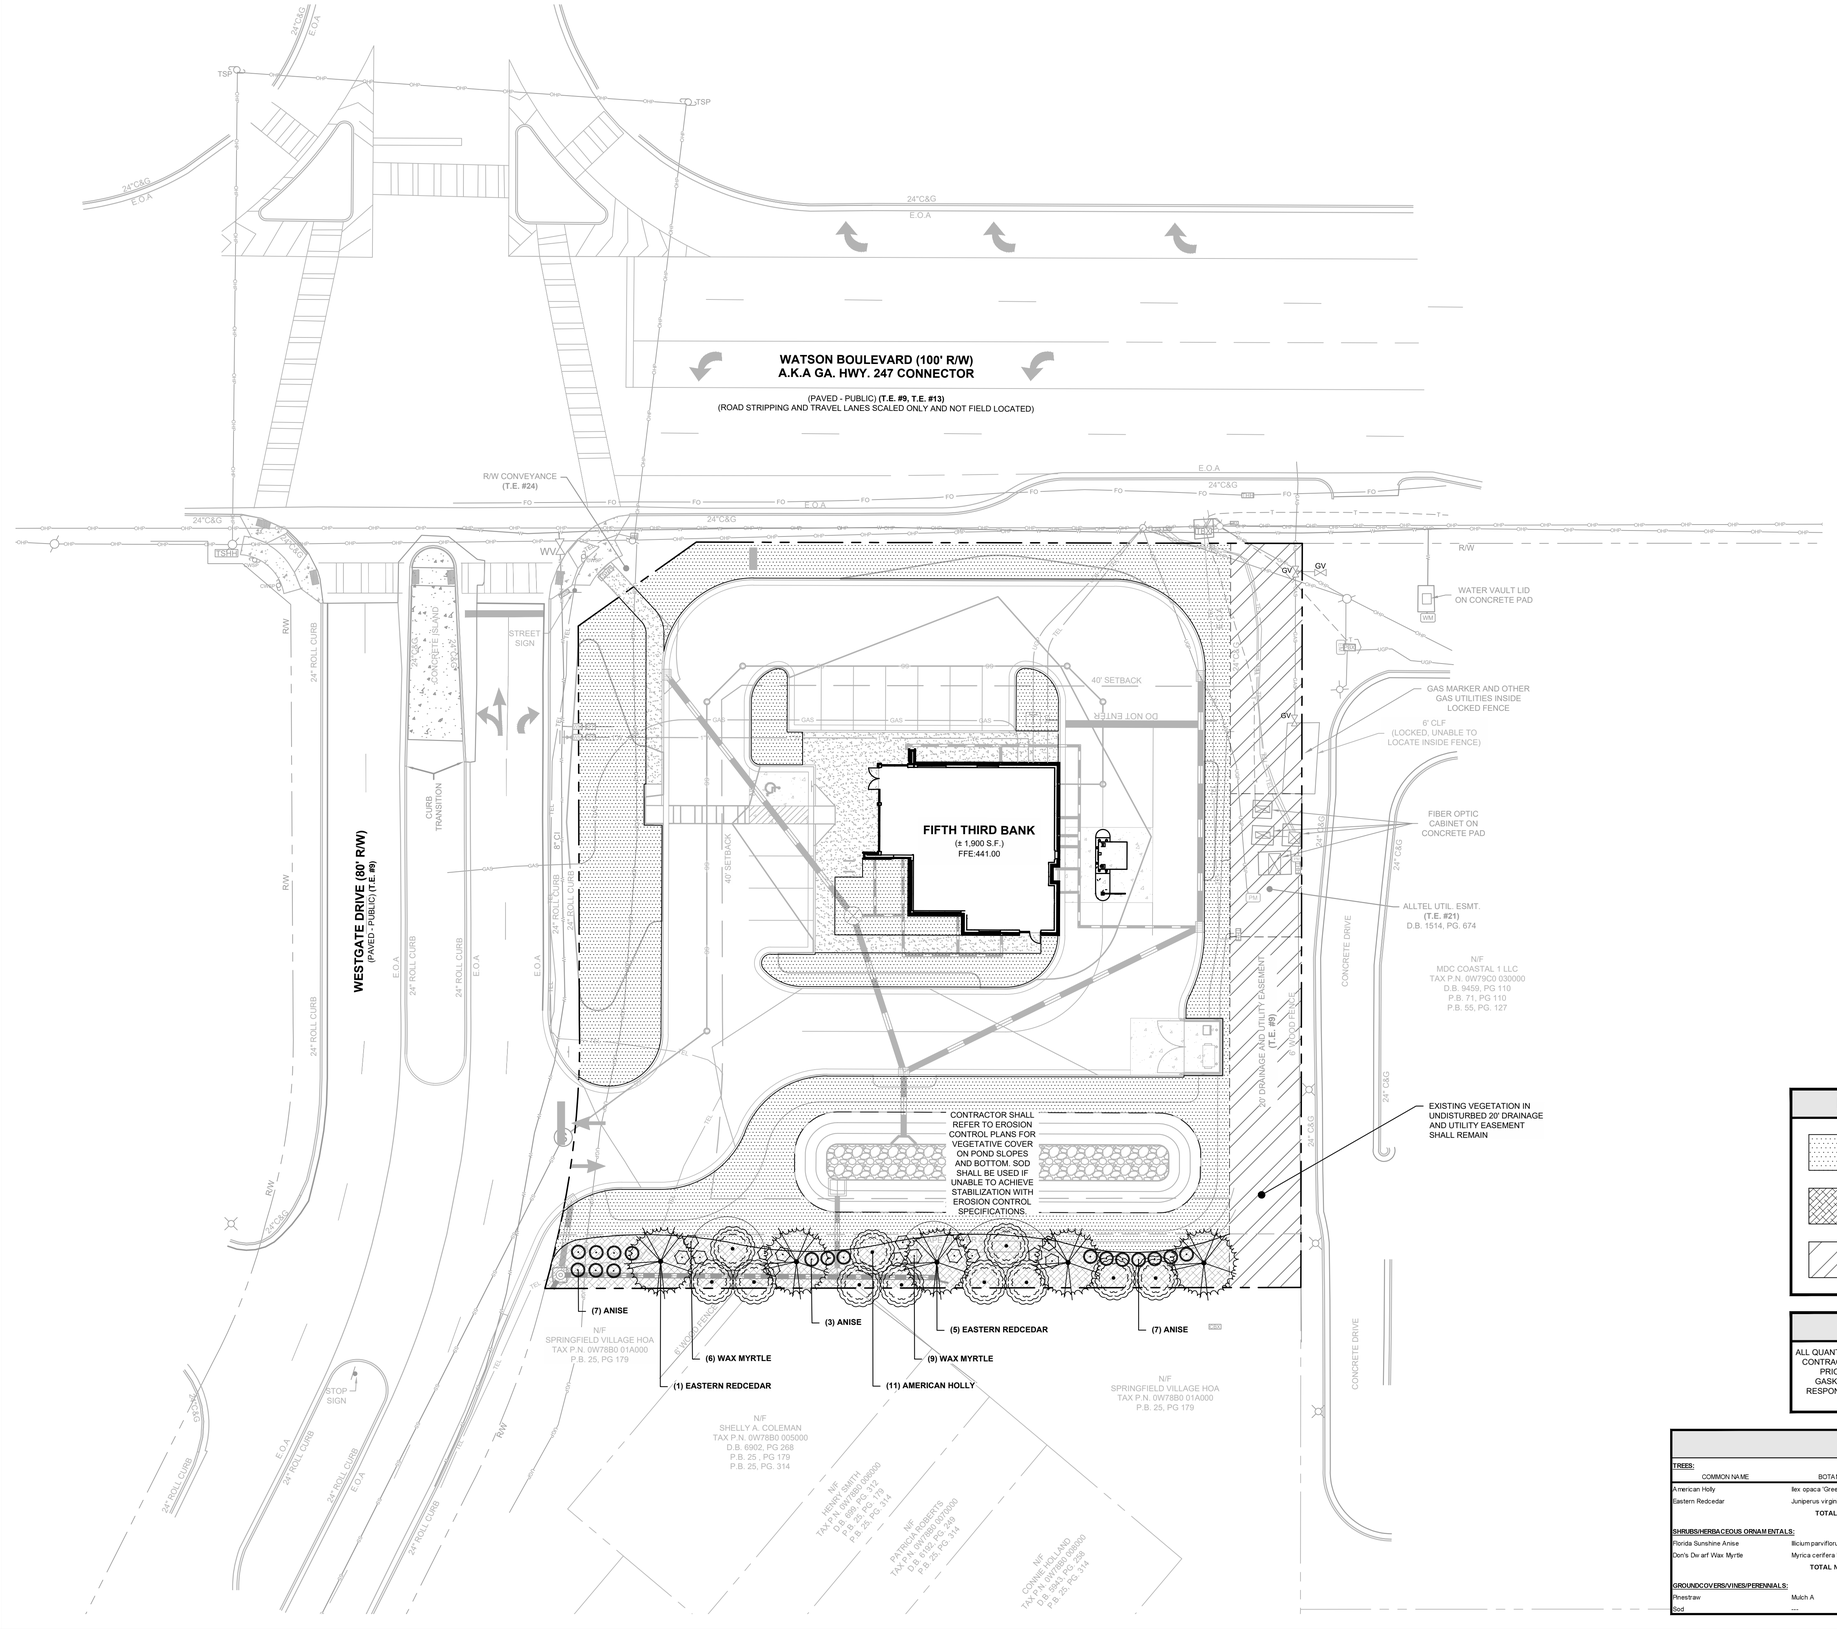


ORDINANCE REQUIREMENTS

15' LANDSCAPE BUFFER

A BUFFER CONSISTING OF A DENSE PLANTING OF TREES AND/OR SHRUBS SHALL BE ESTABLISHED ON A STRIP OF LAND NOT LESS THAN FIFTEEN (15) FEET IN WIDTH OR A FENCE OF SOLID APPEARANCE WITH A MINIMUM HEIGHT OF SIX (6) FEET EIGHT (8) INCHES FROM THE PAVEMENT ON A STRIP OF LAND NOT LESS THAN FIVE (5) FEET ALONG THOSE LOT LINES OF THE PARKING AREAS WHICH ABUT RESIDENTIAL DISTRICTS. IF A PLANTED BUFFER IS USED, IT SHALL BE ESTABLISHED TO A MINIMUM HEIGHT OF SIX (6) FEET WITHIN TWO (2) YEARS OF PLANTING. (SECTION 62.4.4)

SITE SUMMARY

SITE AREA	
SITE AREA:	0.96 ACRES (41,909 S.F.)
IMPERVIOUS AREA:	21,033 S.F. (50.2%)
PERVIOUS AREA:	20,876 S.F. (49.8%)
ZONING CLASSIFICATION	
JURISDICTION:	CITY OF WARNER ROBINS
ZONING:	C-2 (GENERAL COMMERCIAL DISTRICT)
ADJACENT ZONING:	C-2 / R-3
BUILDING SETBACKS	
FRONT:	40'
SIDE:	0'
REAR:	25'
BUILDING SUMMARY	
BUILDING AREA:	1,900 S.F.
BUILDING COVERAGE:	4.5%
PARKING SUMMARY	
PARKING REQ.:	1 SPACE / 300 S.F.
	7 SPACES
PARKING PROV.:	11 SPACES
STANDARD STALL DIMENSIONS:	9' x 18'
MIN. DRIVE WIDTH:	24'

HATCH LEGEND

- SOD / GRASS
- MULCH
- 20' DRAINAGE & UTILITY EASEMENT

NOTE

ALL QUANTITIES ARE FOR A GENERAL GUIDE ONLY. CONTRACTOR SHALL CONFIRM ALL QUANTITIES PRIOR TO BIDDING AND INSTALLATION. GASKINS + LECRAW, INC. SHALL TAKE NO RESPONSIBILITY FOR THE ACCURACY OF THE QUANTITIES PROVIDED.

PLANT LEGEND

SYMBOL	COMMON NAME
TREES	
	AMERICAN HOLLY
	EASTERN REDCEDAR
SHRUBS	
	ANISE
	WAX MYRTLE

PLANT LIST

TREES:

COMMON NAME	BOTANICAL NAME	QUANTITY	MIN. SIZE	MIN. SPACING	NOTES
American Holly	Ilex opaca 'Greenleaf'	5	6' HT.	12' O.C.	B&B - HEALTHY, SINGLE LEADER, FULL TO GROUND
Eastern Redcedar	Juniperus virginiana	11	6' HT.	40' O.C.	B&B - HEALTHY, ONE CENTRAL LEADER
	TOTAL NUMBER OF TREES:	**16**			

SHRUBS/HERBACEOUS ORNAMENTALS:

Florida Sunshine Anise	Illicium parviflorum 'Florida Sunshine'	17	3 GAL	5' O.C.	FULL, FREE OF PEST & DISEASE
Don's Dwarf Wax Myrtle	Myrica cerifera 'Don's Dwarf'	15	3 GAL	5' O.C.	FULL, FREE OF PEST & DISEASE
	TOTAL NUMBER OF SHRUBS:	**32**			

GROUNDCOVERS/VINES/PERENNIALS:

Pinestraw	Mulch A	2,500 S.F.	
Sod	---	11,500 S.F.	

PREPARED IN THE OFFICE OF:
GASKINS +LECRAW
a PAPE-DAWSON company

© 2026 GASKINS + LECRAW

3475 CORPORATE WAY
SUITE A
DULUTH, GA 30096
PHONE - 678.546.8100
www.gaskinslecraw.com
PEF008127

REVISIONS:

REV. #	DATE	DRAWN BY:	CHECKED BY:
1			

CLIENT
PRAXIS3
100 PEACHTREE STREET NW, SUITE 1450, ATLANTA, GEORGIA 30303

PROJECT
FIFTH THIRD BANK - WARNER ROBINS, GA
2711 WATSON BLVD
PARCEL ID: 0W0780-005000
WARNER ROBINS, HOUSTON COUNTY, GEORGIA

SEAL:

GEORGIA REGISTERED No. 3693 MICHAEL TOOTHAKER
1/9/26

CALL BEFORE YOU DIG
811 Know what's below. Call before you dig.

SCALE & NORTH ARROW:

NORTH ARROW
0' 10' 20' 40'
SCALE: 1" = 20'

DESIGN INFO:

DRAWN BY:	JOA
DESIGNED BY:	JOA
REVIEWED BY:	MAT
JOB #:	75670007
DATE:	JULY 9, 2026

LANDSCAPE PLAN

L-1.0

Drawing name: C:\Users\cklentz\Gaskins+LeCraw Dropbox\Shared Folders\Engineering\75670007 - Praxis3 - Fifth Third - Warner Robins_GA\CADD\CONSTR\75670007 - 11 - LANDSCAPE.dwg LANDSCAPE PLAN Jul 09, 2026 10:53am by cklentz

This document, together with the concepts and designs presented herein, as an instrument of service, is intended only for the specific purpose and client for which it was prepared. Reuse of and improper reliance on this document without written authorization and adaptation by Gaskins + LeCraw, a Pape-Dawson Company shall be without liability to Gaskins + LeCraw, a Pape-Dawson Company, Copyright Gaskins + LeCraw, a Pape-Dawson Company, 2026