

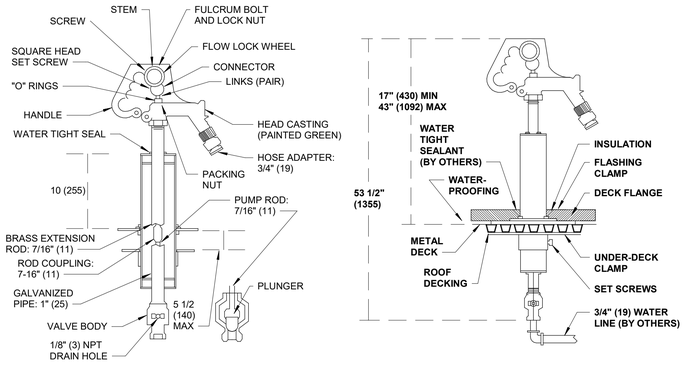



1 P-501 DETAIL OF ROOF HYDRANT
NTS

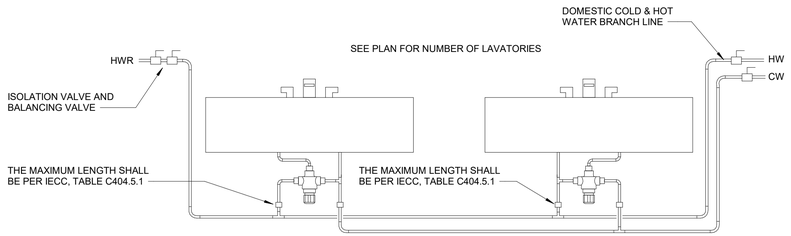


2 P-501 PUBLIC LAVATORY SUPPLY DETAIL
NOT TO SCALE

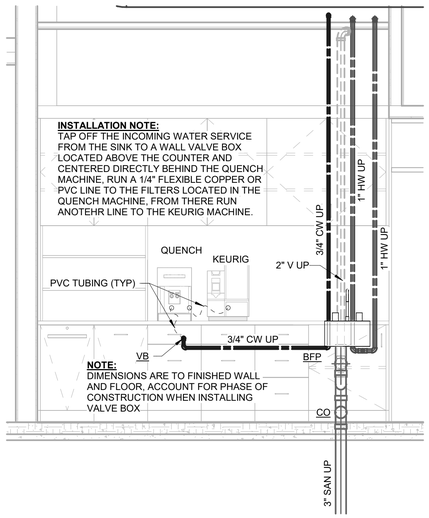


3 P-501 LIBRARY COUNTERTOP DRINKING EQUIPMENT ELEVATION
1/2" = 1'-0"

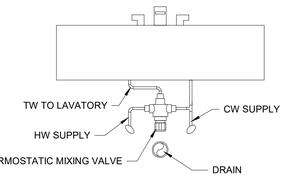


4 P-501 DETAIL OF TMV BELOW LAVATORY
NOT TO SCALE

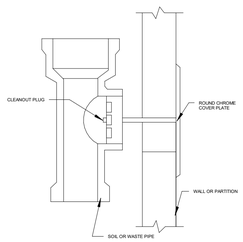


5 P-501 WALL CLEANOUT DETAIL
12" = 1'-0"

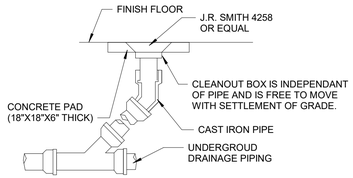


6 P-501 DETAIL OF CLEANOUT TO GRADE
NOT TO SCALE

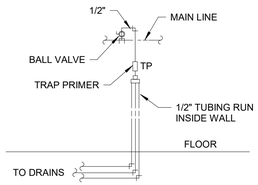


7 P-501 DETAIL OF PIPING AT TRAP PRIMER
NOT TO SCALE

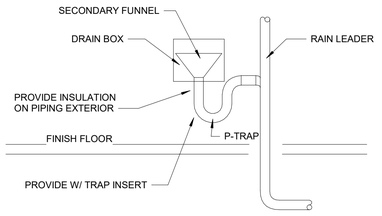


8 P-501 CONDENSATE DRAIN TO RAIN LEADER DETAIL
NOT TO SCALE

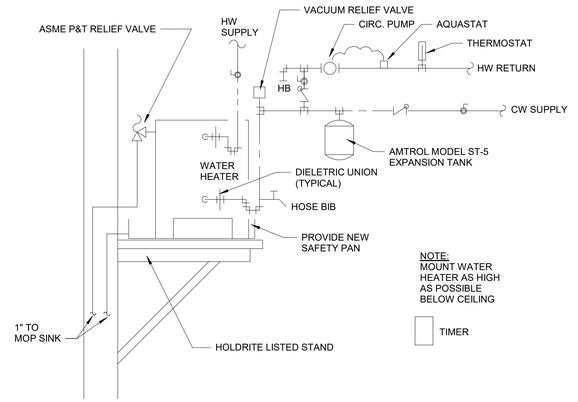

9 P-501 DETAIL OF PIPING AT WATER HEATER
NOT TO SCALE

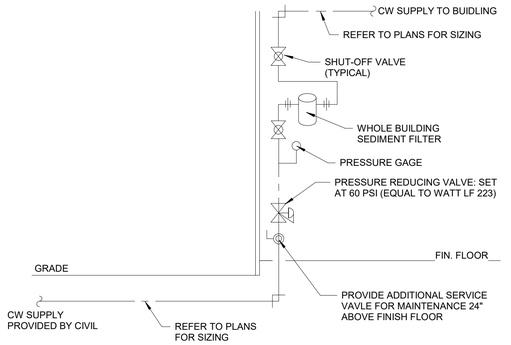

10 P-501 DETAIL FOR WATER ENTRY
12" = 1'-0"

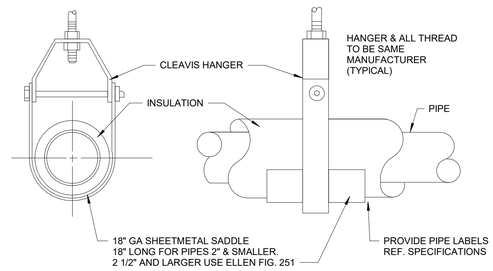

11 P-501 SUSPENDED PIPE SUPPORT
NOT TO SCALE

6/30/2026 4:55:19 PM

PRAXIS3
100 Peachtree St NW
Suite 1450
Atlanta, GA 30303
404-875-4500 tel
www.praxis3.com

GEORGIA REGISTERED 032221 PROFESSIONAL ENGINEER GARRY M. JENKINS

Copyright (c) 2024 Praxis3, LLC

All reports, plans, specifications, computer files, field data, notes and other documents and instruments prepared by Praxis3 shall retain all common law, statutory and other reserved rights, including copyright thereto.

This drawing may not be reproduced in whole or in part without written permission of Praxis3. It is to be returned upon request. Scales as stated are valid on the original drawings.

Rev	Date	Comments
	07/02/2026	PERMIT SET

Client:
FIFTH THIRD BANK

Project Number: 26032
Project Name:
FIFTH THIRD BANK WATSON
1,900 SF

2711 WATSON BOULEVARD
WARNER ROBBINS, GA 31093

Key Plan:

Sheet Title:
PLUMBING DETAILS

Sheet Number:
P-501