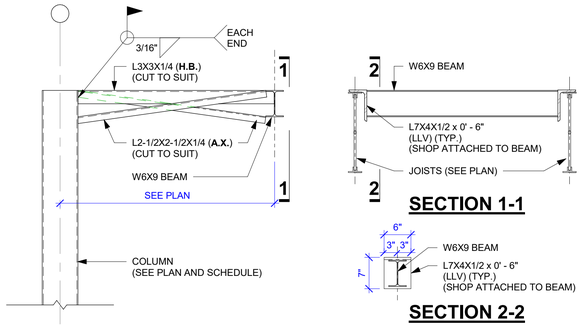



SECTION 1-1

SECTION 2-2


Typical Horizontal Brace (H.B.) and Additional X-Type Bridging (A.X.) at Column

1 / S-682

3/4" = 1'-0"

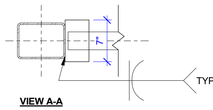


VIEW A-A

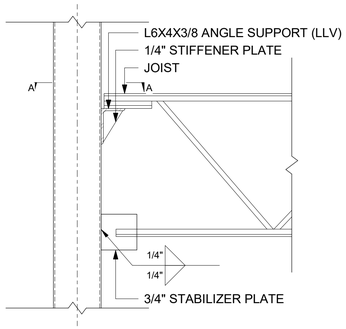

Joist-Column Connection (HSS)

2 / S-682


1" = 1'-0"

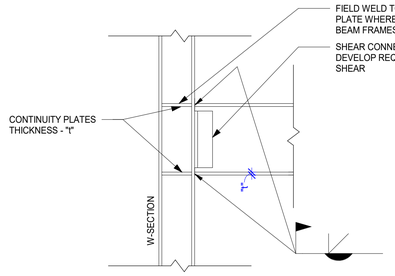


Typical Moment Connection of Steel Beam to Column

3 / S-682

1" = 1'-0"

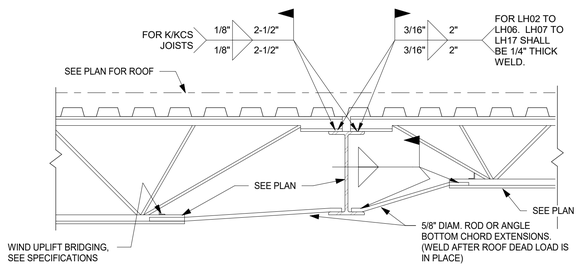

BEAM DETAIL AT JOIST CLOSEST TO BEAM MIDSPAN

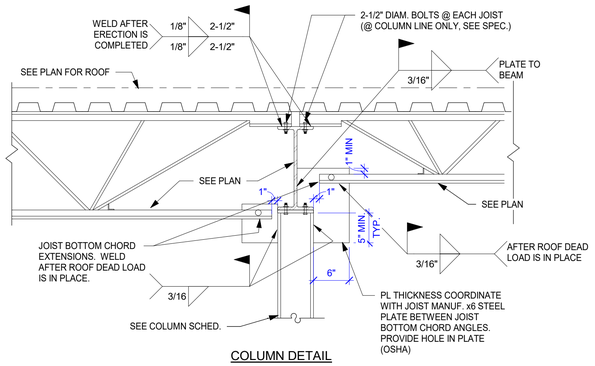


COLUMN DETAIL

Typical Detail of Bar Joist Roof Construction

4 / S-682

1" = 1'-0"

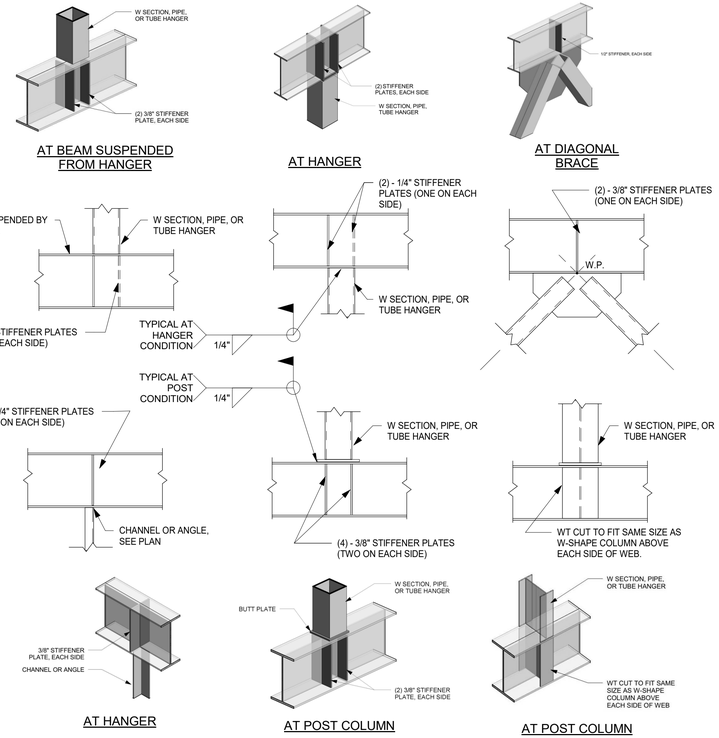

Typical Beam Stiffener at Steel Hangers or Steel Posts (U.N.O.)

5 / S-682

3/4" = 1'-0"

PRAXIS3

100 Peachtree St NW
Suite 1450
Atlanta, GA 30303

404-875-4500 tel
404-876-8884 fax
www.praxis3.com

GEORGIA REGISTERED No. SE001277 STRUCTURAL ENGINEER MARK W. NANNIS

Copyright © 2026 Praxis3, LLC

All reports, plans, specifications, computer files, field data, notes and other documents and instruments prepared by Praxis3 shall retain all common law, statutory and other reserved rights, including copyright thereto.

This drawing may not be reproduced in whole or in part without written permission of Praxis3. It is to be returned upon request. Scales as stated are valid on the original drawings.

Rev	Date	Comments
1	07/02/2026	PERMIT SET

MARK NANNIS STRUCTURAL ENGINEERS

Mark Nannis Structural Engineers
2060 Buford Highway NE, Suite 106
Buford, GA 30518

All drawings, specifications, and other work product of Mark Nannis Structural Engineers (henceforth referred to as "The Engineer") for this project are instruments of service for this project only and shall remain the property of The Engineer whether the project is complete or not. Reuse of any of the instruments of service of The Engineer by the owner or extensions of this project without the written permission of The Engineer shall be at the owner's risk and the owner agrees to defend, indemnify, and hold harmless The Engineer from all claims, damages, and expenses including attorney's fees arising out of such unauthorized reuse of The Engineer's instruments of service by the owner or others acting through the owner.
© 2026

Client:

FIFTH THIRD BANK

Project Number: 26302
Project Name:

WATSON BLVD.

2711 WATSON BOULEVARD
WARNER ROBINS, GA 31093

Sheet Title:

Typical Details (Steel)

Sheet Number:

S-682

RELEASED FOR CONSTRUCTION AND PERMIT

6/26/2026 12:52:33 PM