GENERAL NOTES

CONCRETE NOTES

1. REINFORCING BARS THAT ARE TO BE WELDED SHALL BE OF A WELDABLE GRADE AND WELDED IN ACCORDANCE WITH A.W.S. RECOMMENDATIONS.
2. PROTECTIVE COVERING OF REINFORCEMENT (SEE DETAILS) SHALL BE AS FOLLOWS:
   A. FOOTINGS AND GRADE BEAMS 3" CLEAR BOTTOM AND SIDES, 1 1/2" CLEAR SIDES.
   B. BEAMS 1 1/2" CLEAR TO STIRRUPS.
   C. CONCRETE COLUMNS AND PIERS 1 1/2" CLEAR TO TIES
   D. 3/4" CLEAR FOR CONCRETE JOIST TOP BARS
3. WHERE THE LENGTH OF A BAR IS GIVEN, AND IT IS TO BE HOOKED, THE HOOK SHALL BE IN ADDITION TO THE LENGTH GIVEN.
4. WHERE OPENINGS OCCUR IN SLABS, PLACE THE REINFORCING THAT WOULD OCCUR IN LINE WITH THE OPENING EQUALLY TO EITHER SIDE OF THE OPENING. CUT NO STEEL IN THE FIELD.
5. BACKFILL SHALL NOT BE PLACED AGAINST BASEMENT WALLS UNTIL THE BASEMENT FLOOR SLAB AND THAT PORTION OF THE FIRST SLAB OVER THE BASEMENT ARE IN PLACE.

CONTRACTOR'S NOTES

1. SEE ARCHITECTURAL, MECHANICAL, PLUMBING AND ELECTRICAL DRAWING. AND SPECIFICATIONS FOR SIZE AND LOCATION OF DRIPS, CHAMFERS, SLEEVES, ANCHORS, INSERTS AND OPENINGS REQUIRED. THE LOCATION AND SIZE OF SLEEVES OR OPENINGS NOT SHOWN ON THE DRAWINGS IN STRUCTURAL MEMBERS SHALL BE SUBJECT TO THE APPROVAL OF THE ARCHITECT. ANY CONFLICT SHALL BE BROUGHT TO THE ATTENTION OF THE ARCHITECT BEFORE PROCEEDING WITH THE WORK AFFECTED. PRINCIPAL OPENINGS IN THE STRUCTURE ARE INDICATED ON THE CONTRACT DRAWINGS. ANY SUBSTITUTIONS RESULTING IN REVISIONS TO THE STRUCTURE SHALL BE THE RESPONSIBILITY OF THE CONTRACTOR TO COORDINATE WITH THE ARCHITECT.
2. THE CONTRACTOR SHALL NOT SCALE THE CONTRACT DRAWINGS FOR THE PURPOSE OF ESTABLISHING CORRECT DIMENSIONS.
3. U.N.O. DENOTES: "UNLESS NOTED OTHERWISE".
4. GENERAL CONTRACTOR SHALL FIELD VERIFY EXISTING SIZES, DIMENSIONS, NOTES OR CONDITIONS PRIOR TO ANY DETAILING, OR FABRICATION OF MATERIALS.
5. WHERE THE CONTRACTOR ELECTS TO POUR THE SLAB ON GRADE PRIOR TO ERECTING THE SUPERSTRUCTURE, THE CONTRACTOR SHALL TAKE INTO CONSIDERATION THAT THE SLAB ON GRADE IS NOT DESIGNED FOR SUPPORT OF ANY CRANES OR SIMILAR DEVICES USED TO ERECT THE STRUCTURAL FRAME. DO NOT PLACE THIS EQUIPMENT ON THE SLAB.
6. WHERE OVERHEAD LIFTS OCCUR ON THE PROJECT, NO KEYED OR SAW CUT JOINT SHALL BE PLACED WITHIN 6" OF THE LIFT SUPPORT ANCHORAGE AS PER THE LIFT MANUFACTURER RECOMMENDATIONS. GENERAL CONTRACTOR COORDINATE WITH FINAL LIFT PLACEMENT PLAN PRIOR TO POURING THE SLAB.
7. GENERAL CONTRACTOR SHALL ENGAGE A SURVEYOR TO PROVIDE LOCATIONS OF ALL EXISTING UTILITES, TRENCHES, ETC. TO ENSURE THAT NEW FOUNDATIONS WILL NOT INTERFERE, UNDERMINE, OR BEAR ON EXISTING UTILITIES.

DECKING NOTES

1. NO PIPING, DUCTWORK, OR CONDUIT LARGER THAN 3/4" DIAMETER OR STUD WALLS SHALL BE SUPPORTED DIRECTLY FROM METAL DECK OR PERMANENT METAL FORM.
2. ALL METAL ROOF DECKS SHALL BE WIDE RIB AND GALVANIZED TYPE "B" DECKS UNLESS NOTED OTHERWISE.

FOUNDATION NOTES

1. BUILDING FOOTINGS ARE DESIGNED TO BEAR ON ORIGINAL EARTH OR LABORATORY CONTROLLED COMPACTED FILL WITH AN ALLOWABLE BEARING CAPACITY OF 3,000 PSF. ALLOWABLE BEARING CAPACITY AT CONTINUOUS WALL FOOTINGS SHALL BE 3,000 PSF. SOIL BEARING CAPACITY SHALL BE VERIFIED BY A REGISTERED GEOTECHNICAL ENGINEER AT THE TIME OF EXCAVATION. ELEVATIONS GIVEN ARE FOR PURPOSES OF CONTRACT AND SHALL BE ADJUSTED AT THE TIME OF EXCAVATION TO MEET SOILS CONDITIONS. SITE SHALL BE PREPARED IN ACCORDANCE TO THE GEOTECHNICAL REPORT PREPARED BY "TERRACON" DATED MAY 4, 2026. PROJECT NO. 49265099
2. WALL FOOTINGS, UNLESS SHOWN OTHERWISE, SHALL BE 12" THICK WITH A 6" SPREAD EACH SIDE OF MASONRY WALL, REINFORCED WITH 2 #6 CONTINUOUS. (UNLESS NOTED OTHERWISE)
3. THE MAXIMUM WALL FOOTING STEP-OFF SHALL BE 2'-0" VERTICAL SPACED NOT LESS THAN: 4'-0" o.c. FOOTING STEP-OFFS ARE INDICATED BY THE SYMBOL: ⟋0⟍
4. WHERE PIPES OR CONDUITS RUN PERPENDICULAR TO A FOOTING, STEP TOP OF FOOTING DOWN TO ALLOW PIPES OR CONDUIT TO RUN OVER TOP OF FOOTINGS.
5. WHERE PIPES OR CONDUIT RUN PARALLEL TO A FOOTING, STEP DOWN BOTTOM OF FOOTING SO THAT A LINE DRAWN BETWEEN INVERT OF PIPE AND BOTTOM OF FOOTING SHALL NOT EXCEED 30 DEGREES, SEE "TRENCHES NEAR FOOTINGS" DETAIL.
6. NO PIPES OR CONDUIT SHALL BE PLACED IN THE FOOTINGS, OR SLAB ON GRADE.

SLAB-ON-GRADE NOTES

1. WHERE SLABS REST ON FILL, FILL SHALL BE COMPACTED IN ACCORDANCE WITH THE SPECIFICATIONS.
2. SLABS ON GROUND MAY BE PLACED IN LANE FASHION USING GALVANIZED STEEL, PREFORMED KEYED FORMS AT FLOOR JOINT LOCATION INDICATED. REINFORCING SHALL NOT CROSS CONSTRUCTION OR KEYED JOINTS.
3. SLABS-ON-GRADE REQUIRE CONTROL JOINTS PER THE TYPICAL DETAILS UNLESS NOTED OTHERWISE. LOCATE CONSTRUCTION AND CONTROL JOINTS IN SUCH A WAY TO MINIMIZE THE EFFECTS OF SHRINKAGE AND CURLING OF THE CONCRETE SLAB SECTIONS. SUBMIT TO THE ARCHITECT/ENGINEER/EQUIPMENT VENDOR THE SEQUENCE AND METHOD OF CASTING CONCRETE SLABS-ON-GRADE PRIOR TO PLACING THESE ELEMENTS.
   A. JOINT SPACING SHALL NOT EXCEED **15 FEET**, AND THE RESULTING PLAN ASPECT RATIO (PANEL LENGTH TO PANEL WIDTH) OF ANY GIVEN SECTION OF SLAB SHALL NOT EXCEED **1.5**.
   B. WHERE POSSIBLE, CONTROL JOINT LAYOUT SHALL BE SUCH THAT JOINTS ALIGN WITH THE VERTICES OF COLUMN ISOLATION BLOCKOUTS AND SHALL BE ARRANGED IN A GENERALLY ORTHOGONAL MANNER.
   C. IN AREAS WHERE NON-STRUCTURAL BONDED OVERLAY MATERIAL OR GROUT-BEDDED FLOORING ARE TO BE INSTALLED, FEATURES SUCH AS CRACK-SUPPRESSION MEMBRANES AND FLOORING DIVIDER STRIPS ALIGNED WITH SLAB CONTROL JOINTS SHALL BE DESIGNED AND INSTALLED BY OTHERS AS PART OF THE NON-STRUCTURAL FLOORING ASSEMBLY IN ORDER TO MITIGATE SUBSTRATE-INDUCED CRACKING.
4. SEE CIVIL AND ARCH. DRAWINGS AND SPECIFICATIONS FOR EXTERIOR SLAB WORK AND JOINTING. HORIZONTAL RUNS OF CONDUIT AND PIPE SHALL NOT BE PLACED IN SLABS ON GROUND, PLACE IN SUB-GRADE.
5. AT ALL TRUCK DOCK SLABS OR SERVICE COURT SLABS, PROVIDE AN 8" CONCRETE SLAB REINFORCED WITH #4 @ 12" o.c. EACH WAY, TOP AND BOTTOM. PROVIDE KEYED AND DOWELED JOINTS AT 15'-0" x 15'-0" PATTERN. TYPICAL, UNLESS NOTED OTHERWISE.
6. SLAB ON GRADE AT BUILDING SHALL BE:
   4" THICK, 3000 PSI CONCRETE REINFORCED WITH FLAT SHEETS OF WELDED WIRE FABRIC 6x6-W2.9xW2.9. SLAB SHALL BEAR ON A VAPOR BARRIER ON A NON EXPANSIVE FILL SUBGRADE AS RECOMMENDED BY THE GEOTECHNICAL ENGINEER.
7. SLAB ON GRADE AT DUMPSTER ENCLOSURE PAD SHALL BE:
   6" THICK, 4000 PSI CONCRETE REINFORCED WITH FLAT SHEETS OF WELDED WIRE FABRIC 6x6-W2.9xW2.9. SLAB SHALL BEAR ON A VAPOR BARRIER ON A NON EXPANSIVE FILL SUBGRADE AS RECOMMENDED BY THE GEOTECHNICAL ENGINEER.

COLD-FORMED STEEL NOTES

1. ALL EXTERIOR METAL STUDS ARE TO BE C.S.J. (U.N.O.)
2. ALL EXTERIOR METAL STUDS SHALL BE DESIGNED FOR LATERAL WIND PRESSURE BASED UPON ULTIMATE DESIGN WIND SPEED AS SHOWN ON DESIGN NOTES AND SHOULD BE LIMITED TO LATERAL DEFLECTION OF L/600 WHEN BACKING MASONRY, AND L/360 WHEN BACKING E.I.F.S., AND METAL PANELS
3. ALL EXTERIOR FLANGES OF STUD WALLS SHALL BE BRACED BY SHEATHING PROPERLY ATTACHED TO THEM.
4. CONTRACTOR SHALL FURNISH DETAILED DESIGN CALCULATIONS INCLUDING CONNECTION AND GAUGE OF ALL EXTERIOR METAL STUDS, METAL STUD TRUSSES AND METAL STUD TRUSS GIRDERS SEALED BY A REGISTERED ENGINEER IN THE STATE IN WHICH THE PROJECT IS BUILT.
5. THE TOP COMPRESSION FLANGES OF JOISTS & TRUSSES ARE TO BE LATERALLY BRACED BY PROPER ATTACHMENT OF THE DECKING.
6. THE TOP FLANGES OF BOTTOM CHORDS OF TRUSSES, SHALL BE BRACED LATERALLY AT INTERVALS NOT EXCEEDING 3'-0" o.c. BY CONTINUOUS C STUDS WELDED TO TOP FLANGES OR BY SHEATHING ATTACHED DIRECTLY TO BOTTOM FLANGE.
7. TOP FLANGE OF CEILING STUD SHALL BE BRACED LATERALLY BY CONTINUOUS C STUDS WELDED TO EACH JOIST. EACH BRACE SHALL BE CAPABLE OF TRANSMITTING A MINIMUM OF 200 POUNDS IN TENSION OR COMPRESSION. BOTTOM FLANGE OF CEILING SHALL BE BRACED BY SHEATHING PROPERLY ATTACHED TO BOTTOM FLANGE.
8. ALL INTERIOR FLANGES OF STUD WALLS SHALL BE BRACED EITHER BY SHEATHING OR BY CONTINUOUS CHANNELS WELDED TO FLANGE AT INTERVALS NOT EXCEEDING 2'-0" o.c. OR AS DETERMINED BY DETAIL DESIGN DOCUMENTS FURNISHED BY A REGISTERED ENGINEER IN THE STATE IN WHICH THE PROJECT IS BUILT.
9. ALL NON-LOAD-BEARING METAL STUD WALLS (INTERIOR AND EXTERIOR) SHALL BE CONNECTED TO ALLOW FOR 3/4" VERTICAL MOVEMENT BETWEEN STUD WALL AND STRUCTURE.
10. ALL OTHER INTERIOR METAL STUD PARTITIONS, BULKHEADS, CEILING STUDS AND ECT. SHALL BE FURNISHED UNDER THE DIRECTION OF THE ARCHITECTURAL DOCUMENTS . ANY ADDITIONAL STUD DESIGN REQUIREMENTS SHALL BE PROVIDED BY THE GENERAL CONTRACTOR'S METAL STUD DESIGN ENGINEER.
11. METAL STUD WALLS SHALL NOT BE ERECTED UNTIL AFTER DEAD LOADS AND ALL CONCRETE FLOORS ON FRAMING ABOVE ABOVE ARE IN PLACE.

STRUCTURAL STEEL NOTES

1. FABRICATION AND ERECTION OF ALL STEEL SHALL BE IN ACCORDANCE WITH THE AISC SPECIFICATIONS.
2. WHERE BEAMS REST ON MASONRY OR CONCRETE WALLS THEY SHALL BEAR A MINIMUM OF 8" AND SHALL HAVE BEARING PLATES AND ANCHORS.
3. WHERE NOT SHOWN OTHERWISE, ALL COLUMNS SHALL HAVE BASE PLATES AND (4) 3/4" Ø x 14" LONG ANCHOR BOLTS.
4. UNLESS SHOWN OTHERWISE, PROVIDE 5/8"x12"x7-1/2" BEARING PLATES ON 1" GROUT WITH (2) 3/4" DIAMETER ANCHOR BOLTS UNDER ALL STEEL BEAMS THAT BEAR ON MASONRY WALLS.
5. COLUMN BASES ARE DESIGNED AS UNRESTRAINED, THEREFORE COLUMNS MUST BE BRACED DURING ERECTION.
6. AS ERECTION PROGRESSES, FRAMING SHALL BE ADEQUATELY GUYED AND BRACED AND CONNECTIONS SHALL BE SECURELY BOLTED OR WELDED.
7. NO SHOP SPLICE OR OTHER CONNECTION WILL BE PERMITTED UNLESS THIS SPLICE OR DETAIL IS SHOWN ON SHOP DRAWINGS AND REVIEWED BY THE ENGINEERS.
8. ALL FASTENERS SHALL CONSIST OF ONE NUT, ONE BOLT, AND ONE WASHER.
9. ALL WELDING SHALL CONFORM TO THE "STRUCTURAL WELDING CODE - AMERICAN WELDING SOCIETY." FOR WELD TESTING REQUIREMENTS, SEE SPECIFICATIONS.
10. NO SLOTTED HOLES ARE PERMITTED UNLESS SPECIFICALLY DETAILED BY THE ENGINEER OF RECORD.
11. IT SHALL BE THE RESPONSIBILITY OF THE CONTRACTOR TO SECURE STEEL AGAINST DISPLACEMENT DURING ERECTION AND TO MAINTAIN IT AGAINST DISPLACEMENT UNTIL THE ERECTION OF ALL STEEL IS COMPLETED, ALL FLOOR AND ROOF DECKS ARE IN PLACE, AND ALL EXTERIOR MASONRY IS COMPLETED. ALL STRUCTURAL METAL WORK SHALL HAVE TEMPORARY GUYS, BRACES AND STAYS TO HOLD IT IN POSITION UNTIL IT IS PERMANENTLY SECURE.
12. WHERE ROOF DECKS FRAME ONTO A ROOF MEMBER, AND DECK IS IN A DIFFERENT PLANE THAN THE ROOF MEMBER, PROVIDE A 3/16" CONTINUOUS BENT PLATE WELDED ACROSS THE TOP OF THE ROOF MEMBER SLOPED TO MATCH PLANE OF ROOF DECK.
13. ANCHORS SHALL BE AUTOMATICALLY END WELDED WITH SUITABLE STUD WELDING EQUIPMENT IN ACCORDANCE WITH THE RECOMMENDATIONS OF THE MANUFACTURER.
14. WHERE A ROOF FRAMING MEMBER DOES NOT FRAME OVER A COLUMN, PROVIDE A 1/2" THICK CAP PLATE (i.e. TUBES AND PIPES)
15. FABRICATOR SHALL SUBMIT COMPLETE CALCULATIONS OF ALL CONNECTIONS SEALED BY AN ENGINEER LICENSED IN THE STATE IN WHICH THE PROJECT IS BUILT.
16. WHERE HSS OUTLOOKERS OCCUR PROVIDE 1/4" CAP PLATE AT END.
17. ALL EXTERIOR EXPOSED STEEL SHALL BE GALVANIZED G90 UNLESS NOTED OTHERWISE BY THE ARCHITECT.
18. ALL BEAM SHOP CONNECTIONS SHALL BE WELDED. BEAM SHOP CONNECTIONS MAY BE BOLTED IN LIEU OF WELDING PROVIDED THAT THE CONTRACTOR ASKS AND RECEIVES AN AFFIRMATIVE ANSWER BY THE ENGINEER OF RECORD IN WRITING. FURTHERMORE, ACCEPTANCE OF A BOLTED CONNECTION WILL ONLY OCCUR IF THE FABRICATOR FOLLOWS THE ECCENTRIC LOAD TABLES PROVIDED ON PAGES 7-30 THROUGH 7-53 OF THE AISC MANUAL.

CONCRETE MASONRY NOTES

1. MORTAR SHALL COMPLY WITH ASTM C 270, TYPE S, UNLESS GREATER STRENGTH IS SPECIFIED ELSEWHERE.
2. MASONRY GROUT SHALL BE COMPLYING WITH ASTM C 476, MINIMUM REQUIRED GROUT COMPRESSIVE STRENGTH f'_g = 2250 PSI, U.N.O.
3. REQUIRED MASONRY NET AREA COMPRESSIVE STRENGTH f'_m = 2250 PSI, U.N.O.
4. CONCRETE GROUT, CONFORMING TO ASTM C476, NOT MORTAR, SHALL BE USED AT CELLS AND BOND BEAMS CONTAINING REINFORCING BARS. DO NOT FILL CELLS NOT CONTAINING REINFORCING BARS, EXCEPT BELOW GRADE, UNLESS SO INDICATED.
5. UNLESS NOTED OTHERWISE, MAXIMUM CONTROL JOINT SPACING SHALL BE 32'-0", 16'-0" FROM CORNERS, COORDINATE WITH ARCHITECTURAL. ALL HORIZONTAL REINFORCING SHALL BE DISCONTINUED AT WALL CONTROL JOINTS.
6. LOAD BEARING MASONRY WALLS SHALL BE LATERALLY BRACED UNTIL ALL FLOOR / ROOF DIAPHRAGM IS IN PLACE.
7. AT ALL NON-LOAD BEARING MASONRY WALLS (INTERIOR AND EXTERIOR), PROVIDE A 3/4" CAULKED JOINT BETWEEN UNDERSIDE OF BEAM, JOIST, DECK, OR STRUCTURE AND TOP OF MASONRY WALL.
8. PROVIDE MASONRY HORIZONTAL JOINT REINFORCEMENT 16" o.c. VERTICAL IN ALL CONCRETE BLOCK WALLS. REINFORCEMENT SHALL BE FOR TOTAL WIDTH OF CAVITY WALLS.
9. PROVIDE A 2 SQUARE INCH INSPECTION HOLE AT THE BOTTOM CELL FOR EACH LIFT TO ALLOW VISUAL INSPECTION AND TO REMOVE MORTAR DROPPING PRIOR TO GROUTING.
10. ALL MASONRY SHALL BE RUNNING BOND UNLESS NOTED OTHERWISE.
11. SLEEVE ALL PLUMBING OR FIRE PROTECTION PIPING THROUGH CMU WALL.
12. SEE ARCHITECT DRAWINGS AND SPECIFICATIONS FOR MASONRY FINISHES.
13. AT LOAD-BEARING MASONRY WHERE JOISTS OR BEAMS BEAR ON MASONRY WALLS, GROUT POCKET SOLID WITH GROUT TO THE SAME FINISH FACE AS MASONRY ABOVE AND BELOW. DO THIS ONLY AFTER JOIST SEAT CONNECTION HAS BEEN INSPECTED.

POST-INSTALLED ANCHOR NOTES

THE BELOW PRODUCTS ARE THE DESIGN BASIS FOR THIS PROJECT. PRODUCT DIAMETER AND EMBEDMENT SHALL BE AS SHOWN IN THE DETAILS. INSTALL PRODUCTS IN ACCORDANCE WITH MANUFACTURER'S PRINTED INSTALLATION INSTRUCTIONS (MPII). SUBSTITUTION REQUESTS FOR PRODUCTS OTHER THAN THOSE LISTED BELOW MAY BE SUBMITTED BY THE CONTRACTOR TO THE ENGINEER-OF-RECORD (EOR) FOR REVIEW. SUBSTITUTIONS WILL ONLY BE CONSIDERED FOR PRODUCTS HAVING A CODE REPORT RECOGNIZING THE PRODUCT FOR THE APPROPRIATE APPLICATION. SUBSTITUTION REQUESTS SHALL INCLUDE CALCULATIONS THAT DEMONSTRATE THE SUBSTITUTED PRODUCT IS CAPABLE OF ACHIEVING THE EQUIVALENT PERFORMANCE VALUES OF THE DESIGN BASIS PRODUCT. CONTRACTOR SHALL CONTACT MANUFACTURER'S REPRESENTATIVE (800-999-5099) FOR PRODUCT INSTALLATION TRAINING AND A LETTER SHALL BE SUBMITTED TO THE EOR INDICATING TRAINING HAS TAKEN PLACE. SPECIAL INSPECTIONS ARE REQUIRED PER THE IBC AND ICC-ES REPORTS.

A. FOR ANCHORING INTO CONCRETE:

1. MECHANICAL ANCHORS SHALL HAVE BEEN TESTED AND QUALIFIED FOR USE IN ACCORDANCE WITH ACI 355.2 AND ICC-ES AC193 FOR CRACKED CONCRETE AND SEISMIC APPLICATIONS. PRE-APPROVED ANCHORS INCLUDE:
   - SIMPSON STRONG TIE "STRONG-BOLT 2" (IAPMO-UES ESR ER-240)
2. ADHESIVE FOR REBAR AND ANCHORS SHALL HAVE BEEN TESTED AND QUALIFIED FOR USE IN ACCORDANCE WITH ACI 355.4 AND ICC-ES AC308 FOR CRACKED CONCRETE AND SEISMIC APPLICATIONS. ADHESIVE ANCHORS SHALL BE INSTALLED BY A CERTIFIED ADHESIVE ANCHOR INSTALLER PER ACI 318-11 D.9.2.2 WHERE INDICATED ON THE CONTRACT DOCUMENTS. INSTALLATIONS REQUIRING CERTIFIED INSTALLERS SHALL BE INSPECTED PER ACI 318-11 D.9.2.4. PRE-APPROVED ANCHORS INCLUDE:
   - SIMPSON STRONG TIE "SET-XP" (ICC-ES ESR-2508)
   - SIMPSON STRONG TIE "AT-XP" (IAPMO-UES ESR-263)
3. POWDER-ACTUATED FASTENERS SHALL HAVE BEEN TESTED IN ACCORDANCE WITH ICC-ES AC70. PRE-APPROVED ANCHORS INCLUDE:
   - SIMPSON STRONG TIE "GAS ACTUATED PINS" (ICC-ES ESR-2811)
   - SIMPSON STRONG TIE "POWDER ACTUATED PINS" (ICC-ES ESR-2138)

B. FOR ANCHORING INTO MASONRY:

1. ANCHORAGE TO SOLID-GROUTED CONCRETE MASONRY
   a. MECHANICAL ANCHORS SHALL HAVE BEEN TESTED AND QUALIFIED FOR USE IN ACCORDANCE WITH ICC ES AC01 OR ICC-ES AC106 PRE-APPROVED ANCHORS INCLUDE:
      - SIMPSON STRONG TIE "TITEN-HD" (ICC-ES ESR-1056)
      - SIMPSON STRONG TIE "STRONG-BOLT 2" (IAPMO-ES ER-240)
   b. ADHESIVE FOR REBAR AND ANCHORS SHALL HAVE BEEN TESTED AND QUALIFIED FOR USE IN ACCORDANCE WITH ICC-ES AC58. PRE-APPROVED ANCHORS INCLUDE:
      - SIMPSON STRONG TIE "TITEN-HD" (ICC-ES ESR-1056)
      - SIMPSON STRONG TIE "STRONG-BOLT 2" (IAPMO-ES ER-240)
   c. POWDER-ACTUATED FASTENERS SHALL HAVE BEEN TESTED IN ACCORDANCE WITH ICC-ES AC70. PRE-APPROVED ANCHORS INCLUDE:
      - SIMPSON STRONG TIE "GAS ACTUATED PINS" (ICC-ES ESR-2811)
      - SIMPSON STRONG TIE "POWDER ACTUATED PINS" (ICC-ES ESR-2138)
2. ANCHORAGE TO HOLLOW CONCRETE MASONRY
   a. MECHANICAL ANCHORS SHALL HAVE BEEN TESTED AND QUALIFIED FOR USE IN ACCORDANCE WITH ICC-ES AC106 PRE-APPROVED ANCHORS INCLUDE:
      - SIMPSON STRONG TIE "TITEN-HD"
   b. ADHESIVE FOR REBAR AND ANCHORS WITH SCREEN TUBES SHALL HAVE BEEN TESTED AND QUALIFIED FOR USE IN ACCORDANCE WITH ICC-ES AC58. THE APPROPRIATE SCREEN TUBE SHALL BE USED AS RECOMMENDED BY THE ADHESIVE MANUFACTURER. PRE-APPROVED ANCHORS WITH SCREEN TUBES INCLUDE:
      - SIMPSON STRONG TIE "SET" (ICC-ES ESR-1772)
   c. POWDER-ACTUATED FASTENERS SHALL HAVE BEEN TESTED IN ACCORDANCE WITH ICC-ES AC70. PRE-APPROVED ANCHORS INCLUDE:
      - SIMPSON STRONG TIE "GAS ACTUATED PINS" (ICC-ES ESR-2811)
      - SIMPSON STRONG TIE "POWDER ACTUATED PINS" (ICC-ES ESR-2138)

C. FOR ANCHORING INTO STEEL POWDER-ACTUATED FASTENERS SHALL HAVE BEEN TESTED IN ACCORDANCE WITH ICC-ES AC70. PRE-APPROVED ANCHORS INCLUDE:

1. SIMPSON STRONG TIE "GAS ACTUATED PINS" (ICC-ES ESR-2811)
2. SIMPSON STRONG TIE "POWDER-ACTUATED PINS" (ICC-ES ESR-2138)

STEEL BAR JOIST NOTES

1. JOIST BRIDGING SHALL NOT BE USED TO SUPPORT CONDUIT, PIPING, DUCTWORK, ETC.
2. JOISTS SHALL NOT BE FIELD MODIFIED EXCEPT AS SHOWN.
3. WHERE JOISTS CANNOT ACHIEVE THE REQUIRED BEARING ON STEEL BEAMS, STAGGER JOISTS TO PROVIDE ADEQUATE BEARING.
4. STEEL JOISTS SHALL BE OPEN WEB STEEL JOISTS OF THE SIZES AND SERIES SHOWN ON THE DRAWINGS. JOISTS, BRIDGING AND SPACING OF BRIDGING SHALL MEET THE REQUIREMENTS OF THE LATEST EDITION OF THE "STANDARD SPECIFICATIONS" OF THE STEEL JOIST INSTITUTE, EXCEPT WHERE OTHERWISE INDICATED BY THE DRAWINGS OR SPECIFICATIONS.
5. WHERE ANGLE BRACES ARE SHOWN ON STRUCTURAL SECTIONS, JOIST MANUFACTURER SHALL RESOLVE AN AXIAL LOAD OF 2000 POUNDS FROM THE BRACE INTO THE JOIST - TYPICAL UNLESS NOTED OTHERWISE.
6. IN ADDITION TO WHAT IS CALLED FOR ON PLAN, BAR JOISTS SHALL BE DESIGNED TO SUPPORT AN ADDITIONAL CONCENTRATED LOAD OF 300 POUNDS AT TOP OR BOTTOM CHORD AT ANY ONE LOCATION ALONG THE SPAN.
7. AT THE END OF EACH ROOF JOIST, PROVIDE A CONTINUOUS ROW OF BRIDGING AT THE LAST BOTTOM CHORD PANEL POINT FOR UPLIFT. TYPICAL AT EACH END OF JOIST.
8. NET WIND UPLIFT SHALL BE CONSIDERED USING THE ASD COMPONENTS AND CLADDING PRESSURES (THIS SHEET) AND A DEAD LOAD OF 8 PSF.

REPAIR, PROTECT, AND STRENGTHENING NOTES

THE BELOW PRODUCTS ARE THE DESIGN BASIS FOR THIS PROJECT. CONTRACTOR SHALL FOLLOW MANUFACTURER'S INSTALLATION INSTRUCTIONS AND CONTACT MANUFACTURER'S REPRESENTATIVE (800-999-5099) WITH PRODUCT RELATED QUESTIONS. SUBSTITUTION REQUESTS FOR PRODUCTS OTHER THAN THOSE LISTED BELOW MAY BE SUBMITTED BY THE CONTRACTOR TO THE ENGINEER-OF-RECORD (EOR) FOR REVIEW AND APPROVAL. SUBSTITUTIONS WILL ONLY BE CONSIDERED FOR PRODUCTS HAVING INDEPENDENT TEST RESULTS OR OTHER DOCUMENTATION INDICATING THE PRODUCT IS APPROPRIATE FOR THE INTENDED APPLICATION.

A. REBAR PRIMER: REBAR PRIMER SHALL BE USED TO PROTECT EXISTING STEEL REINFORCING AND ENCOURAGE POSITIVE BOND FROM EXISTING STEEL REINFORCING TO NEW REPAIR MATERIAL. PRE-APPROVED PRODUCTS INCLUDE:
   1. SIMPSON STRONG TIE "FX-406"

B. BONDING AGENTS: BONDING AGENTS SHALL BE USED TO ENCOURAGE POSITIVE BOND OF NEW REPAIR MATERIAL TO EXISTING CONCRETE. PRE-APPROVED PRODUCTS INCLUDE:
   1. SIMPSON STRONG TIE "FX-762"

C. REPAIR MORTARS: REPAIR MATERIAL SHALL BE USED TO REPAIR AREAS OF DAMAGED CONCRETE. PRE-APPROVED PRODUCTS INCLUDE:
   1. SIMPSON STRONG TIE "FX-263" (FOR USE IN OVERHEAD AND VERTICAL APPLICATIONS)
   2. SIMPSON STRONG TIE "FX-261" (FOR USE IN HORIZONTAL AND FORM & POUR APPLICATIONS)

D. CRACK REPAIR SYSTEM: CRACK REPAIR SYSTEM SHALL CONSIST OF CRACK INJECTION MATERIAL AND PASTE OVER ADHESIVE AND SHALL BE USED TO PRESSURE INJECT CRACKS. PRE-APPROVED SYSTEMS INCLUDE:
   1. SIMPSON STRONG TIE "FX-751 LV" INJECTION MATERIAL WITH "FX-763" PASTE OVER ADHESIVE

E. NON-SHRINK GROUT MATERIAL: NON-SHRINK GROUT MATERIAL SHALL BE USED TO GROUT BENEATH BASEPLATES, BEARING PLATES AND EQUIPMENT BASES. PRE-APPROVED PRODUCTS INCLUDE:
   1. SIMPSON STRONG TIE "FX-228"

SUBMITTAL NOTES

1. THE GENERAL CONTRACTOR SHALL SUBMIT A SCHEDULE OF SUBMITTALS PRIOR TO CONSTRUCTION BEGINNING ON THE PROJECT. THE SCHEDULE SHOULD DESCRIBE WHAT EACH SUBMITTAL IS, WHETHER IT IS THE ENTIRE PACKAGE, OR BROKEN INTO PHASES FOR REVIEW.
2. THE GENERAL CONTRACTOR SHALL ALLOW FOR 10 BUSINESS DAYS OF ALL STRUCTURAL SUBMITTALS. IF THE CONTRACTOR WISHES TO EXPEDITE OR REDUCE THE REVIEW TIME, IT SHALL BE DONE FOR AN ADDITIONAL CHARGE AND MUST BE NEGOTIATED WITH THE ARCHITECT AND ENGINEER PRIOR TO THE SUBMISSION OF THE PACKAGE.
3. IN THE EVENT THE CONTRACTOR ATTEMPTS TO SUBMIT THE ENTIRE PROJECT AT THE SAME TIME FOR SUBMISSION, ADDITIONAL TIME WILL BE REQUIRED BEYOND THE STANDARD 10 DAY REVIEW TIME.
4. WHERE GLASS REQUIRES ADDITIONAL DESIGN OF MISCELLANEOUS STEEL AND MULLIONS, CONTRACTOR SHALL FURNISH DETAILED DESIGN CALCULATIONS SEALED BY A REGISTERED ENGINEER IN THE STATE IN WHICH THE PROJECT IS BUILT.
5. STRUCTURAL STEEL SUPPLIER SHALL PROVIDE COMPLETE SHOP DRAWINGS INCLUDING AN ANCHOR SETTING PLAN, ERECTION DRAWINGS WITH ALL PIECE MARKS, AND ASSOCIATED FABRICATION DRAWINGS SHOWING ALL MATERIAL AND CONNECTIONS. CONNECTIONS SHALL BE DESIGNED BASED UPON THE END SHEAR TABLES PROVIDED IN THE AISC UNLESS NOTED OTHERWISE.
6. REBAR SUPPLIER SHALL PROVIDE COMPLETE SHOP DRAWINGS INCLUDING PLAN VIEWS WITH MARKS ILLUSTRATING BAR SIZES AND BAR BENDING DETAILS. INCLUDE ALL LOCATION OF STEPS NOTED IN THE GENERAL NOTES FOR PLUMBING AND CIVIL LINES WHERE APPLICABLE. WHERE CONCRETE PIER AND STEM WALLS OCCUR PROVIDE SECTION CUTS, AND ELEVATIONS ILLUSTRATING THE MATERIAL SPECIFIED
7. REBAR SUPPLIER SHALL PROVIDE COMPLETE SHOP DRAWINGS FOR LOAD BEARING MASONRY. PROVIDE ALL WALLS INCLUDING NON LOAD BEARING PARTITIONS IN ELEVATIONS DEPICTING THE VERTICAL WALL REINFORCEMENT/ LAPS, ALL LINTELS AT OPENINGS , REINFORCING AND BOND BEAMS AS DESCRIBED IN TYPICAL DETAILS AND WALL SECTIONS INCLUDING MASONRY CONTROL JOINT LOCATIONS.
8. JOIST AND DECK SUPPLIER SHALL PROVIDE COMPLETE SHOP DRAWINGS INCLUDING ERECTION DRAWINGS, SECTIONS INCLUDING MATERIALS PROVIDED, ALL ASSOCIATED CONNECTIONS AS OUTLINED IN THE CONTRACT DOCUMENTS AND SPECIFICATIONS. SHOP DRAWINGS SHALL INCLUDE ALL EDGE OF DECK DIMENSIONS, EDGE OF JOIST DIMENSIONS .
9. SEE DISCIPLINE SPECIFIC NOTES AND SPECIFICATIONS FOR ALL ADDITIONAL SUBMITTAL REQUIREMENTS.
10. FOR THIRD-PARTY DESIGN SUBMITTALS INCLUDING, BUT NOT LIMITED TO, PRECAST, HOLLOW CORE SLABS, METAL STUDS, STAIRS & HANDRAILS, GLASS DESIGN, AND WOOD TRUSSES, PLEASE SUBMIT MANUFACTURER'S DRAWINGS WITH ACCOMPANYING CALCULATIONS SEALED BY A REGISTERED ENGINEER IN THE STATE IN WHICH THE PROJECT IS BUILT.

PRAXIS3

100 Peachtree St NW
Suite 1450
Atlanta, GA 30303

404-875-4500 tel
404-876-8884 fax
www.praxis3.com

GEORGIA REGISTERED No. SE001277 STRUCTURAL ENGINEER MARK W. NANNIS

Copyright © 2026 Praxis3, LLC

All reports, plans, specifications, computer files, field data, notes and other documents and instruments prepared by Praxis3 shall retain all common law, statutory and other reserved rights, including copyright thereto.

This drawing may not be reproduced in whole or in part without written permission of Praxis3. It is to be returned upon request. Scales as stated are valid on the original drawings.

Rev	Date	Comments
1	07/02/2026	PERMIT SET

MARK NANNIS STRUCTURAL ENGINEERS

Mark Nannis Structural Engineers

2060 Buford Highway NE, Suite 106
Buford, GA 30518

All drawings, specifications, and other work product of Mark

Abbreviations

Ø	DIAMETER	HGT	HEIGHT
#/FT	PER FOOT	HORIZ	HORIZONTAL
@	AT	HSA	HEADED STUD ANCHOR
		HSS	HOLLOW STEEL SECTION
AB	ANCHOR BOLT		
ABV	ABOVE	IAW	IN ACCORDANCE WITH
ADJ	ADJACENT	IBC	INTERNATIONAL BUILDING CODE
AFF	ABOVE FINISHED FLOOR	IF	INSIDE FACE
AISC	AMERICAN INSTITUTE OF STEEL CONSTRUCTION	INT	INTERIOR
ALT	ALTERNATE		
APPROX	APPROXIMATE	JT	JOINT
ARCH	ARCHITECT		
ASCE	AMERICAN SOCIETY OF CIVIL ENGINEERS	KSI	KIPS PER SQUARE INCH
ASTM	AMERICAN SOCIETY FOR TESTING AND MATERIALS		
		LLH	LONG LEG HORIZONTAL
B/	BOTTOM OF	LLV	LONG LEG VERTICAL
BC	BOTTOM CHORD	LSV	LONG SIDE VERTICAL
BLDG	BUILDING		
BLW	BELOW	MAX	MAXIMUM
BM	BEAM	MC	MISCELLANEOUS CHANNEL
BRG	BEARING	MECH	MECHANICAL
BTWN	BETWEEN	MFR	MANUFACTURER
		MIN	MINIMUM
C	CHANNEL	MISC	MISCELLANEOUS
CFMF	COLD-FORMED METAL FRAMING	MO	MASONRY OPENING
CIP	CAST-IN-PLACE	MOD	MODIFIED
CJ	CONTROL JOINT	MTL	METAL
CL	CENTER LINE		
CLR	CLEAR	NIC	NOT IN CONTRACT
CMU	CONCRETE MASONRY UNIT	NTS	NOT TO SCALE
COL	COLUMN		
CONC	CONCRETE	OAE	OR APPROVED EQUAL
CONT	CONTINUOUS	OC	ON CENTER
		OPNG	OPENING
DBA	DEFORMED BAR ANCHOR		
DBL	DOUBLE	PAF	POWDER ACTUATED FASTENER
DET	DETAIL	PL	PLATE
DIA	DIAMETER	PSF	POUNDS PER SQUARE FOOT
DIAG	DIAGONAL	PSI	POUNDS PER SQUARE INCH
DWG	DRAWING		
		RAD	RADIUS
E/	EDGE OF	REINF	REINFORCED
EA	EACH	REQD	REQUIRED
EB	EXPANSION BOLT		
EFOB	EXTERIOR FACE OF BRICK	SIM	SIMILAR
EIFS	EXTERIOR INSULATION FINISHING SYSTEM	SLV	SHORT LEG VERTICAL
EJ	EXPANSION JOINT	SQ	SQUARE
EL	ELEVATION	SS	STAINLESS STEEL
EOD	EDGE OF DECK	STD	STANDARD
EOS	EDGE OF SLAB	STL	STEEL
EQ	EQUAL	STRUCT	STRUCTURAL
ES	EACH SIDE		
EW	EACH WAY	T/	TOP OF
EXP	EXPANSION	THK	THICKNESS
EXT	EXTERIOR	TRANS	TRANSVERSE
		t/s	TOP OF STEEL
F/	FACE OF	TYP	TYPICAL
FAB	FABRICATE		
FDN	FOUNDATION	UNO	UNLESS NOTED OTHERWISE
FFE	FINISH FLOOR ELEVATION		
FIN	FINISH	VERT	VERTICAL
FLR	FLOOR	VIF	VERIFY IN FIELD
FOS	FACE OF STUD		
FTG	FOOTING	W/	WITH
FV	FIELD VERIFY	WF	WIDE FLANGE
		WP	WORK POINT
GA	GAUGE	WWF	WELDED WIRE FABRIC
GALV	GALVANIZED		
GC	GENERAL CONTRACTOR		
GR	GRADE		

EXTERIOR SCHEDULE OF METAL STUD SIZES
115 MPH, EXPOSURE C, Fy = 33 ksi

WALL HEIGHT	6" STUD		8" STUD	
WIND ZONE 4	L/360	L/600	L/360	L/600
Up to 11'-0"	600S 162-43 @ 16" o/c	600S 162-43 @ 16" o/c	800S 162-43 @ 16" o/c	800S 162-43 @ 16" o/c
Over 11'-0" to 12'-6"	600S 162-43 @ 16" o/c	600S 162-68 @ 16" o/c	800S 162-54 @ 16" o/c	800S 162-54 @ 16" o/c
Over 12'-6" to 15'-6"	600S 162-68 @ 16" o/c	600S 200-97 @ 16" o/c	800S 162-54 @ 16" o/c	800S 162-54 @ 16" o/c
Over 15'-6" to 16'-6"	600S 162-97 @ 16" o/c	600S 200-97 @ 12" o/c	800S 162-54 @ 16" o/c	800S 162-68 @ 16" o/c
Over 16'-6" to 20'-0"	600S 200-97 @ 12" o/c	N/A	800S 162-68 @ 16" o/c	800S 250-97 @ 16" o/c
Over 20'-0" to 21'-0"	600S 250-97 @ 12" o/c	N/A	800S 162-97 @ 16" o/c	800S 200-97 @ 12" o/c
WIND ZONE 5	L/360	L/600	L/360	L/600
Up to 11'-0"	600S 162-43 @ 16" o/c	600S 162-54 @ 16" o/c	800S 162-54 @ 16" o/c	800S 162-54 @ 16" o/c
Over 11'-0" to 12'-6"	600S 162-54 @ 16" o/c	600S 162-68 @ 16" o/c	800S 162-54 @ 16" o/c	800S 162-54 @ 16" o/c
Over 12'-6" to 15'-6"	600S 162-97 @ 16" o/c	600S 250-97 @ 16" o/c	800S 162-54 @ 16" o/c	800S 162-68 @ 16" o/c
Over 15'-6" to 16'-6"	600S 162-97 @ 16" o/c	600S 200-97 @ 12" o/c	800S 162-54 @ 16" o/c	800S 162-97 @ 16" o/c
Over 16'-6" to 20'-0"	600S 200-97 @ 12" o/c	N/A	800S 162-97 @ 16" o/c	800S 250-97 @ 16" o/c
Over 20'-0" to 21'-0"	N/A	N/A	800S 162-97 @ 16" o/c	800S 200-97 @ 12" o/c

NOTES:
1. WHERE EXTERIOR FINISH IS EXTERIOR FINISHES, EFIS OR METAL PANEL USE DEFLECTION LIMITATION OF L/360.
2. WHERE EXTERIOR FINISH IS MASONRY OR BRICK USE DEFLECTION LIMITATION OF L/600.

STRUCTURAL SUBMITTALS

SPECIFICATION SECTION	SUBMITTAL	SUBMITTAL TYPE		DESIGN BY CONTRACTOR'S LICENSED ENGINEER
		ACTION	INFORMATIONAL	
03 1000 - CONCRETE FORMING AND ACCESSORIES	PRODUCT DATA	•		
	FORMWORK SHOP DRAWINGS (ELEVATED CONCRETE ONLY)	•		•
03 2000 - CONCRETE REINFORCING	PRODUCT DATA	•		
	REINFORCING SHOP DRAWINGS	•		
	CONSTRUCTION JOINT LAYOUT	•		
	REINFORCING MATERIAL CERTIFICATES		•	
	REINFORCING MATERIAL TEST REPORTS		•	
03 3000 - CAST-IN-PLACE CONCRETE	PRODUCT DATA	•		
	CONCRETE DESIGN MIXTURES	•		
	SLAB-ON-GRADE JOINT LAYOUT	•		
	MATERIAL CERTIFICATES		•	
	MATERIAL TEST REPORTS		•	
04 2200 - CONCRETE UNIT MASONRY	PRODUCT DATA	•		
	SHOP DRAWINGS	•		
	MATERIAL CERTIFICATES		•	
	MIX DESIGNS FOR MORTAR AND GROUT		•	
	STATEMENT OF COMPRESSIVE STRENGTH FOR MASONRY		•	
05 1200 - STRUCTURAL STEEL FRAMING	PRODUCT DATA	•		
	SHOP DRAWINGS	•		
	CONNECTION DESIGN CALCULATIONS	•		•
	PAINT COMPATIBILITY CERTIFICATES		•	
	MILL TEST REPORTS		•	
	PRODUCT TEST REPORTS		•	
05 2100 - STEEL JOIST FRAMING	STEEL JOIST SHOP DRAWINGS	•		
05 3100 - STEEL DECKING	STEEL DECKING PRODUCT DATA & SHOP DRAWINGS	•		
05 4000 - COLD-FORMED METAL FRAMING	PRODUCT DATA	•		
	SHOP DRAWINGS	•		
	EXTERIOR METAL STUD DESIGN CALCULATIONS	•		•
	LOAD-BEARING METAL STUD DESIGN CALCULATIONS	•		
	PRODUCT CERTIFICATES		•	
	PRODUCT TEST REPORTS		•	
05 5113 - , HAND RAILS, & GUARDS	PRODUCT DATA	•		
	SHOP DRAWINGS	•		
	DESIGN CALCULATIONS	•		•
	PAINT COMPATIBILITY CERTIFICATES		•	

MINIMUM REINFORCED CONCRETE STRENGTHS
F_c AT 28 DAYS (U.N.O. ON SCHEDULES)
(TYPE 1 CEMENT ONLY. DO NOT SUBSTITUTE FLYASH OR SLAG FOR CEMENT)

LOCATION	DENSITY	STRENGTH
SLAB-ON-GRADE	145 PCF	3000 PSI
FOUNDATIONS AND PIERS	145 PCF	3000 PSI
SLAB ON GRADE AT BIN-SUPPORTED MEZZANINE	145 PCF	5000 PSI
FRAMED SLABS IN COMPOSITE STEEL CONSTRUCTION	115 PCF	4000 PSI
FRAMED SLABS IN BAR JOIST FLOOR CONSTRUCTION	145 PCF	3500 PSI
STAIR TREADS AND LANDINGS	145 PCF	3000 PSI
BASEMENT, TIEBACK, AND RETAINING WALLS	145 PCF	3000 PSI
NON-SHRINK GROUT AT STEEL COLUMN BASEPLATES	145 PCF	5000 PSI

MINIMUM LAP SPLICE LENGTH SCHEDULE

BAR TYPE	3000 PSI CONC.								
	#3	#4	#5	#6	#7	#8	#9	#10	#11
TOP BARS	29"	38"	47"	56"	82"	94"	105"	118"	131"
OTHER BARS	22"	29"	36"	43"	62"	72"	81"	91"	101"
BAR TYPE	4000 PSI CONC.								
	#3	#4	#5	#6	#7	#8	#9	#10	#11
TOP BARS	25"	33"	40"	48"	70"	81"	91"	103"	113"
OTHER BARS	20"	25"	31"	38"	55"	62"	70"	79"	87"

MINIMUM PRETENSION OF BOLTS (KIPS)

BOLT DIAMETER	A325 BOLTS	A490 BOLTS
3/4" DIAMETER	28	35
7/8" DIAMETER	39	49
1" DIAMETER	51	64


NON-LOAD-BEARING BRICK LINTEL SCHEDULE

SPAN	LINTEL SIZE
≤ 2'-0"	1 FLAT PLATE - 3-1/2" x 3/8"
2'-0" TO 5'-0"	1 ANGLE - 3-1/2" x 3-1/2" x 5/16"
5'-0" TO 6'-0"	1 ANGLE - 4" x 3-1/2" x 5/16" S.L.O.
6'-0" TO 7'-0"	1 ANGLE - 5" x 3-1/2" x 5/16" S.L.O.
7'-0" TO 8'-0"	1 ANGLE - 5" x 3-1/2" x 3/8" S.L.O.
8'-0" TO 9'-0"	1 ANGLE - 6" x 4" x 3/8" S.L.O.
9'-0" TO 10'-0"	1 ANGLE - 8" x 4" x 7/16" S.L.O.

NOTES:
1. SEE SCHEDULE FOR STEEL GRADE AND STRENGTH
2. ANGLES ARE FOR 4" BRICKWORK
3. BEAR ALL LINTELS A MINIMUM OF 8" AT EACH END
4. ANGLES SHALL BE PLACED SHORT LEG OUT (S.L.O.)
5. FOR PAINTING OR GALVANIZING OF ANGLES, SEE ARCHITECT

MINIMUM ANCHOR BOLT WASHER DIMENSIONS

ANCHOR BOLT DIAMETER	MINIMUM WASHER "B" DIMENSION	MINIMUM WASHER THICKNESS
3/4"	2"	1/4"
7/8"	2-1/2"	5/16"
1"	3"	3/8"
1-1/8" OR 1-1/4"	3"	1/2"
1-3/8" OR 1-1/2"	3-1/2"	1/2"
1-5/8" OR 1-3/4"	4"	5/8"
1-7/8" OR 2"	5"	3/4"
2-1/4" OR 2-1/2"	5-1/2"	7/8"

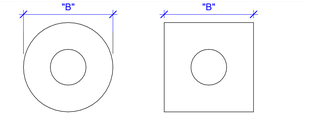

CIRCULAR WASHER SQUARE WASHER

STRUCTURAL STEEL STRENGTHS

STEEL SHAPE	ASTM	F_y (ksi)	F_u (ksi)
ANGLES, PLATES, S SHAPE, AND MISC., CHANNELS MC15 AND SMALLER, AND CHANNELS C8 AND SMALLER	A36	36	58
W SHAPES, MISC CHANNELS MC18 AND LARGER, CHANNELS C10 AND LARGER	A992	50	65
HSS RECTANGULAR AND SQUARE	A500 GRADE C	50	62
HSS ROUND	A500 GRADE C	46	62
PIPE	A53 GRADE B	35	60
SHEAR STUDS	A108	-	65
ANCHOR RODS	F1554 GRADE 36	36	58
HIGH STRENGTH BOLTS 3/4" TO 1" Ø 1-1/8" TO 1-1/2" Ø 1-1/8" TO 1-1/2" Ø AT SE CONN.	F3125 A325 F3125 A325 F3125 A490	- - -	120 105 150
WELDED WIRE FABRIC 6x6-W.9xW2.9	A185	-	-
CONCRETE REINFORCING	A615 GRADE 60	60	-
CONCRETE REINFORCING STIRRUPS, TIES, AND HOOPS	A615 GRADE 40	40	-

DESIGN NOTES

REFERENCE CODES

INTERNATIONAL BUILDING CODE	IBC 2024 w/ Georgia Amendments
MINIMUM DESIGN LOADS	ASCE 7-22
STRUCTURAL CONCRETE	ACI 318-19
STRUCTURAL STEEL	AISC 360-22
STRUCTURAL STEEL SEISMIC	AISC 341-22
STRUCTURAL MASONRY	TMS 402-16
COLD-FORMED STEEL	AISI S100-16

LIVE LOADS

OCCUPANCY OR USE	UNIFORM (PSF)	CONC. (LBS)	OCCUPANCY OR USE	UNIFORM (PSF)	CONC. (LBS)
ROOF	20	300	HANDRAILS AND GUARDS GRAB BARS		200 250

ROOF SNOW LOAD

FLAT-ROOF SNOW LOAD (p_f)	6 PSF	SNOW IMPORTANCE FACTOR (I_s)	1.0
SNOW EXPOSURE FACTOR (C_e)	1.0	THERMAL FACTOR (C_t)	1.15
DESIGN FROST DEPTH	12"		

ROOF RAIN LOAD


RAIN INTENSITY (i)	7.39 INCHES/HOUR
DESIGN EVENT	15-MINUTE/100-YEAR RETURN PERIOD

WIND DESIGN CRITERIA

DESIGN WIND SPEED ULTIMATE (V) NOMINAL (V_{asd})	 107 MPH 83 MPH	INT. PRESSURE COEFFICIENT	±0.18
RISK CATEGORY	2		
WIND EXPOSURE (X-X)	C	COMPONENTS AND CLADDING WIND PRESSURES: SEE TABLES, THIS SHEET	
WIND EXPOSURE (Y-Y)	C		

SEISMIC DESIGN CRITERIA

RISK CATEGORY	2
SEISMIC IMPORTANCE FACTOR	I_e = 1.0
MAPPED SPECTRAL RESPONSE ACCELERATIONS	S_s = 0.230 g S_1 = 0.084 g
SITE CLASS	D
MAPPED SPECTRAL RESPONSE ACCELERATIONS	S_{DS} = 0.190 g S_{D1} = 0.120 g
SEISMIC DESIGN CATEGORY	B
BASIC SEISMIC FORCE-RESISTING SYSTEM(S)	STEEL SYSTEMS NOT SPECIFICALLY DETAILED FOR SEISMIC RESISTANCE
DESIGN BASE SHEAR	$F_x = F_y$ = 4 k
RESPONSE MODIFICATION FACTOR(S)	R = 3
ANALYSIS PROCEDURE	EQUIVALENT LATERAL FORCE

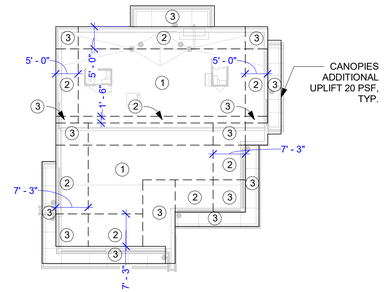


COMPONENTS AND CLADDING ROOF (ENCLOSED) 107 MPH EXP. "C" 'ULT' EXTERNAL PRESSURES (PSF)				
A_e (EFFECTIVE AREA)	ZONE 1'	ZONE 1	ZONE 2	ZONE 3
A_e = 10 SQ. FT.	+16.0, -23.2	+16.0, -40.3	+16.0, -53.2	+16.0, -72.5
A_e = 20 SQ. FT.	+16.0, -30.7	+16.0, -38.2	+16.0, -49.9	+16.0, -66.0
A_e = 50 SQ. FT.	+16.0, -26.4	+16.0, -33.9	+16.0, -44.6	+16.0, -57.0
A_e = 100 SQ. FT.	+16.0, -23.2	+16.0, -31.7	+16.0, -42.4	+16.0, -50.4

COMPONENTS AND CLADDING WALL (ENCLOSED) 107 MPH EXP. "C" 'ULT' EXTERNAL PRESSURES (PSF)			
A_e (EFFECTIVE AREA)	ZONE 4	ZONE 5	
A_e = 10 SQ. FT.	+23.2, -25.1	+23.2, -30.9	
A_e = 20 SQ. FT.	+22.1, -24.1	+22.1, -28.8	
A_e = 50 SQ. FT.	+20.8, -22.7	+20.8, -26.1	
A_e = 100 SQ. FT.	+19.7, -21.7	+19.7, -24.1	

NOTES:
1. *INTERPOLATION MAY BE UTILIZED FOR EFFECTIVE AREAS THAT OCCUR BETWEEN VALUES SHOWN ON THE TABLE.*
2. *PLUS AND MINUS SIGN INDICATES THE PRESSURE ACTING TOWARD AND AWAY FROM THE SURFACES, RESPECTIVELY.*
3. *FORCES AND DIAGRAMS ARE BASED ON IBC / ASCE 7.*

End zone width, a = 5' - 2"

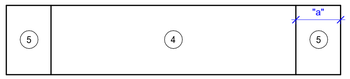

WALL ELEVATION

PRAXIS3

100 Peachtree St NW
Suite 1450
Atlanta, GA 30303

404-875-4500 tel
404-876-8884 fax
www.praxis3.com

GEORGIA REGISTERED No. SE001277 STRUCTURAL ENGINEER MARK W. NANNIS

Copyright © 2026 Praxis3, LLC

All reports, plans, specifications, computer files, field data, notes and other documents and instruments prepared by Praxis3 shall retain all common law, statutory and other reserved rights, including copyright thereto.

This drawing may not be reproduced in whole or in part without written permission of Praxis3. It is to be returned upon request. Scales as stated are valid on the original drawings.

Rev	Date	Comments
1	07/02/2026	PERMIT SET

MARK NANNIS STRUCTURAL ENGINEERS

Mark Nannis Structural Engineers
2060 Buford Highway NE, Suite 106
Buford, GA 30518

All drawings, specifications, and other work product of Mark Nannis Structural Engineers (henceforth referred to as "The Engineer") for this project are instruments of service for this project only and shall remain the property of The Engineer whether the project is complete or not. Reuse of any of the instruments of service of The Engineer by the owner or extensions of this project without the written permission of The Engineer shall be at the owner's risk and the owner agrees to defend, indemnify, and hold harmless The Engineer from all claims, damages, and expenses including attorney's fees arising out of such unauthorized reuse of The Engineer's instruments of service by the owner or others acting through the owner.
© 2026

Client:
FIFTH THIRD BANK

Project Number: 26302
Project Name:
WATSON BLVD.

2711 WATSON BOULEVARD
WARNER ROBINS, GA 31093

Sheet Title:
General Notes

Sheet Number:
S-002

RELEASED FOR CONSTRUCTION AND PERMIT

6/26/2026 12:52:16 PM

1704.2.5 Inspection of Fabricators

MATERIAL / ACTIVITY	SERVICE	APPLICABLE TO THIS PROJECT Y/N	EXTENT	AGENT*	DATE COMP.
Verify fabrication/quality control procedures	In-plant review (3)	Y	Periodic - If fabricator is not AISC certified, (structural steel) or certified by the standard code/spec. for the fabricated assembly or material, special inspection required as indicated within structural steel welding portion of this document or applicable code/specification. If fabricator is approved as specified in section 1704.2.5.1, fabricator inspection is not required. At completion of fabrication, fabricator shall submit certificate of compliance to building official in accordance with Section 1704.2.5.1.	1	

1705.1.1 Special Cases

MATERIAL / ACTIVITY	SERVICE	APPLICABLE TO THIS PROJECT Y/N	EXTENT	AGENT*	DATE COMP.
HY-150 (or equal epoxy system/anchor)	The special inspector must record product description (including product name), adhesive expiration date, concrete or masonry type and strength, anchor diameter and steel grade, compliance of drill bit with this report, hole diameter and location, cleanliness of hole and anchor adhesive application, and anchor embedment. Additionally, the special inspector must state in the report supplied to the building official whether the anchor installation is in accordance with the manufacturer's published instructions and this evaluation report.	Y	Continuous during the first 36-hour period of anchor installation for each anchor type (special inspector must be on site and observing installation of operations while installations are taking place). Remaining anchor installations: periodic - random 25% of anchor installation inspected. If any installations do not meet specifications, all anchors/installations will be inspected (anchors installed and remaining anchors to be installed). Inspections may require continuous inspection if required by building official - special inspector to confirm prior to inspections.	1	
Kwik Bolt 3 (or equal wedge/expansion anchor system/anchor)	The special inspector must record product description (including product name), masonry type and condition, anchor type, diameter and steel grade, compliance of the drill bit with this report, hole diameter and location; and anchor embedment. Additionally, the special inspector must state in the report supplied to the building official whether the anchor installation is in accordance with the manufacturer's published instructions and this evaluation report.	Y	Continuous during the first 36-hour period of anchor installation for each anchor type (special inspector must be on site and observing installation of operations while installations are taking place). Remaining anchor installations: periodic - random 25% of anchor installation inspected. If any installations do not meet specifications, all anchors/installations will be inspected (anchors installed and remaining anchors to be installed). Inspections may require continuous inspection if required by building official - special inspector to confirm prior to inspections.	1	

1705.2 Steel Construction

MATERIAL / ACTIVITY	SERVICE	APPLICABLE TO THIS PROJECT Y/N	EXTENT	AGENT*	DATE COMP.
1. Fabricator and erector documents (Verify reports and certificates as listed in AISC 360, chapter N, paragraph 3.2 for compliance with construction documents)	Submittal Review	Y	Each submittal	1&2	
2. Material verification of structural steel	Shop (3) and field inspection	Y	Periodic		
3. Embedments (Verify diameter, grade, type, length, embedment. See 1705.3 for anchors)	Field inspection	Y	Periodic	1	
4. Verify member locations, braces, stiffeners, and application of joint details at each connection comply with construction documents	Field inspection	Y	Periodic - random selection of 25% of all frame joints.	1	
5. Structural steel welding:					
a. Inspection tasks Prior to Welding (Observe, or perform for each welded joint or member, the QA tasks listed in AISC 360, Table N5.4-1)	Shop (3) and field inspection	Y	Observe or Perform as noted (4)	1	
b. Inspection tasks During Welding (Observe, or perform for each welded joint or member, the QA tasks listed in AISC 360, Table N5.4-2)	Shop (3) and field inspection	Y	Observe (4)	1	
c. Inspection tasks After Welding (Observe, or perform for each welded joint or member, the QA tasks listed in AISC 360, Table N5.4-3)	Shop (3) and field inspection	Y	Observe or Perform as noted (4)	1	
d. Nondestructive testing (NDT) of welded joints: *see Commentary*					
1) Complete penetration groove welds 5/16" or greater in risk category III or IV	Shop (3) or field ultrasonic testing - 100%	N	Periodic	1	
2) Complete penetration groove welds 5/16" or greater in risk category II	Shop (3) or field ultrasonic testing - 10% of welds minimum	Y	Periodic	1	
3) Thermally cut surfaces of access holes when material t > 2"	Shop (3) or field magnetic Partical or Penetrant testing	N	Periodic	1	
4) Welded joints subject to fatigue when required by AISC 360, Appendix 3, Table A-3.1	Shop (3) or field radiographic or Ultrasonic testing	N	Periodic	1	
5) Fabricator's NDT reports when fabricator performs NDT	Verify reports	N	Each submittal (5)	1	
6. Structural steel bolting:					
a. Inspection tasks Prior to Bolting (Observe, or perform tasks for each bolted connection, in accordance with QA tasks listed in AISC 360, Table N5.6-1)	Shop (3) and field inspection	N	Observe or Perform as noted (4)	1	
b. Inspection tasks during bolting (observe the QA tasks listed in AISC 360, Table N5.6-2)	Shop (3) and field inspection	Y	Observe (4)	1	
1) Pre-tensioned and slip-critical joints					
a) Turn-of-nut with matching markings	Shop (3) and field inspection	N	Periodic	1	
b) Direct tension indicator	Shop (3) and field inspection	Y	Periodic - observe all connections; measure 10% of connections	1	
c) Twist-off type tension control bolt	Shop (3) and field inspection	Y	Periodic - observe all connections	1	
d) Turn-of-nut without matching markings	Shop (3) and field inspection	N	Continuous	1	
e) Calibrated wrench	Shop (3) and field inspection	Y	Continuous	1	
2) Snug-tight joints	Shop (3) and field inspection	N	Periodic	1	
c. Inspection tasks After Bolting (Perform tasks for each bolted connection in accordance with QA tasks listed in AISC 360, Table N5.6-3)	Shop (3) and field inspection	Y	Perform (4)	1	
7. Inspection of steel elements of composite construction prior to concrete placement in accordance with QA tasks listed in AISC 360, Table N6.1	Shop (3) and field inspection and testing	N	Observe or Perform as noted (4)	1	

1705.2.2 Steel Construction Other Than Structural Steel

MATERIAL / ACTIVITY	SERVICE	APPLICABLE TO THIS PROJECT Y/N	EXTENT	AGENT*	DATE COMP.
1. Material verification of cold-formed steel deck:					
a. Identification markings	Field inspection	Y	Periodic	1	
b. Manufacturer's certified test reports	Submittal Review	Y	Each submittal	1	
2. Connection of cold-formed steel deck to supporting structure:		Y		1	
a. Welding	Shop (3) and field inspection	Y	Periodic - inspect all deck welds & side laps	1	
b. Other fasteners (in accordance with AISC 360,Section N6)					
1) Verify fasteners are in conformance with approved submittal	Shop (3) and field inspection	Y	Periodic	1	
2) Verify fastener installation is in conformance with approved submittal and manufacturer's recommendations	Shop (3) and field inspection	Y	Periodic	1	
3. Reinforcing steel					
a. Verification of weldability of steel other than ASTM A706	Shop (3) and field inspection	Y	Periodic - verify correct, specified weld electrodes and reinforcing steel for each material shipment. Verify compliance with specified connection, construction for each connection type at the start of construction for that connection type.	1	
b. Reinforcing steel resisting flexural and axial forces in intermediate and special moment frames, boundary elements of special concrete structural walls and shear reinforcement	Shop (3) and field inspection	N	Continuous	1	
c. Shear reinforcement	Shop (3) and field inspection	N	Continuous	1	
d. Other reinforcing steel	Shop (3) and field inspection	N	Periodic - verify correct, specified weld electrodes and reinforcing steel for each material shipment. Verify compliance with specified connection, construction for each connection type at the start of construction for that connection type.	1	
4. Cold-formed steel trusses spanning 60 feet or greater					
a. Verify temporary and permanent restraint/bracing are installed in accordance with the approved truss submittal package	Field inspection	N	Periodic	1	

1705.6 Soils

MATERIAL / ACTIVITY	SERVICE	APPLICABLE TO THIS PROJECT Y/N	EXTENT	AGENT*	DATE COMPLETED
1. Verify materials below shallow foundations are adequate to achieve the design bearing capacity.	Field inspection	Y	Periodic	1	
2. Verify excavations are extended to proper depth and have reached proper material.	Field inspection	Y	Periodic	1	
3. Perform classification and testing of controlled fill materials.	Field inspection	Y	Periodic	1	
4. Verify use of proper materials, densities, and lift thicknesses during placement and compaction of controlled fill	Field inspection	Y	Continuous	1	
5. Prior to placement of controlled fill, observe subgrade and verify that site has been prepared properly	Field inspection	Y	Periodic	1	

1705.3 Concrete Construction

MATERIAL / ACTIVITY	SERVICE	APPLICABLE TO THIS PROJECT Y/N	EXTENT	AGENT*	DATE COMP.
1. Inspection of reinforcing steel installation (see 1705.3.1 for welding)	Shop (3) and field inspection	Y	Periodic - before each concrete pour of ftgs., walls, columns, and elevated slabs with sufficient time allowed for inspection of completed installed reinforcing prior to pour.	1	
2. Inspection of prestressing steel installation	Shop (3) and field inspection	N	Periodic - before each concrete pour of ftgs., walls, columns, and elevated slabs with sufficient time allowed for inspection of completed installed reinforcing prior to pour.		
3. Inspection of anchors cast in concrete where allowable loads have been increased per Section 1901.3/ACI 318:17.8.2 or where strength design is used	Shop (3) and field inspection	N	Periodic		
4. Inspection of anchors and reinforcing steel post-installed in hardened concrete: Per research reports including verification of anchor type, anchor dimensions, hole dimensions, hole cleaning procedures, anchor spacing, edge distances, concrete minimum thickness, anchor embedment and tightening torque	Field inspection	Y	Periodic or as required by the research report issued by an approved source	1	
5. Verify use of approved design mix	Shop (3) and field inspection	Y	Periodic	1 & 2	
6. Fresh concrete sampling, perform slump and air content tests and determine temperature of concrete	Shop (3) and field inspection	Y	Continuous - sample every 75 cubic yds or each day (whichever is more stringent) and each change in concrete strength.	1	
7. Inspection of concrete and shotcrete placement for proper application techniques	Shop (3) and field inspection	Y	Continuous	1	
8. Inspection for maintenance of specified curing temperature and techniques	Shop (3) and field inspection	Y	Periodic	1	
9. Inspection of prestressed concrete:					
a. Application of prestressing force	Shop (3) and field inspection	N	Continuous	1	
b. Grouting of bonded prestressing tendons in the seismic-force-resisting system	Shop (3) and field inspection	N	Continuous	1	
10. Erection of precast concrete members					
a. Inspect in accordance with construction documents	Field inspection	N	In accordance with construction documents - 1) Sample grout: (3) test samples every day of masonry construction for first three days of masonry construction with additional (3) samples every 30 cubic yards placed/once per week/every 5000 SF of wall, whichever is most stringent. 2) Inspect erection, bearing conditions and general conformance to erection drawings (2) times per week minimum.	1	
b. Perform inspections of welding and bolting in accordance with Table 1705.3	Field inspection	N	In accordance with Section 1705.2 - (1) time per week minimum	1	
11. Verification of in-situ concrete strength, prior to stressing of tendons in post tensioned concrete and prior to removal of shores and forms from beams and structural slabs	Review field testing and laboratory reports	Y	Periodic - additional cylinder for 3-day/7-day tests (contractor's option) on time of testing with same sampling frequency as typical fresh concrete sampling. Verify that adequate concrete strength has been obtained on concrete test cylinders.	1	
12. Inspection of formwork for shape, lines, location, and dimensions	Field inspection	Y	Periodic - inspect prior to each concrete placement.	1	
13. Concrete strength testing and verification of compliance with construction documents	Field testing and review of laboratory reports	Y	Periodic	1 & 2	

*Inspection Agents

FIRM
1. Special Inspector
2. Structural Engineer
3. Architect
4. Mech. & Plumbing

Notes:

1. *The inspection and testing agent(s) shall be engaged by the Owner or the Owner's Agent, and not by the Contractor or Subcontractor whose work is to be inspected or tested. Any conflict of interest must be disclosed to the Building Official prior to commencing work. The qualifications of the Special Inspector(s) and/or testing agencies may be subject to the approval of the Building Official and/or the Design Professional.*
2. *The list of Special Inspectors may be submitted as a separate document, if noted so above.*
3. *Special Inspections as required by Section 1704.2.5 are not required where the fabricator is approved in accordance with IBC Section 1704.2.5.2*
4. *Observe on a random basis, operations need not be delayed pending these inspections. Perform these tasks for each welded joint, bolted connection, or steel element.*
5. *NDT of welds completed in an approved fabricator's shop may be performed by that fabricator when approved by the AHJ. Refer to AISC 360, N7.*
6. *For all other disciplines refer to relevant documents provided by the design professional.*

PRAXIS3

100 Peachtree St NW
Suite 1450
Atlanta, GA 30303

404-875-4500 tel
404-876-8884 fax
www.praxis3.com

GEORGIA REGISTERED No. SE001277 STRUCTURAL ENGINEER MARK W. NANNIS

Copyright © 2026 Praxis3, LLC

All reports, plans, specifications, computer files, field data, notes and other documents and instruments prepared by Praxis3 shall retain all common law, statutory and other reserved rights, including copyright thereto.

This drawing may not be reproduced in whole or in part without written permission of Praxis3. It is to be returned upon request. Scales as stated are valid on the original drawings.

Rev	Date	Comments
1	07/02/2026	PERMIT SET

MARK NANNIS STRUCTURAL ENGINEERS

Mark Nannis Structural Engineers

2060 Buford Highway NE, Suite 106
Buford, GA 30518

All drawings, specifications, and other work product of Mark Nannis Structural Engineers (henceforth referred to as "The Engineer") for this project are instruments of service for this project only and shall remain the property of The Engineer whether the project is complete or not. Reuse of any of the instruments of service of The Engineer by the owner or extensions of this project without the written permission of The Engineer shall be at the owner's risk and the owner agrees to defend, indemnify, and hold harmless The Engineer from all claims, damages, and expenses including attorney's fees arising out of such unauthorized reuse of The Engineer's instruments of service by the owner or others acting through the owner.
© 2026

Client:

FIFTH THIRD BANK

Project Number: 26302
Project Name:

WATSON BLVD.

2711 WATSON BOULEVARD
WARNER ROBINS, GA 31093

Sheet Title:

Special Inspections Schedules

Sheet Number:

S-003

RELEASED FOR CONSTRUCTION AND PERMIT

6/26/2026 12:52:17 PM

: INDICATES TO SLOPE SLAB. SEE ARCHITECTURAL FOR AMOUNT OF SLOPE AND EXACT LOCATION.

[0'-0"] INDICATES ELEVATION OF FINISH FLOOR SLAB. SEE CIVIL DRAWINGS FOR DATUM.

[ ]: NUMBER INSIDE OF BRACKETS INDICATES TOP OF FOOTING ELEVATION

INDICATES A STEP IN FOOTING. SEE GENERAL NOTES FOR CRITERIA. SEE DETAIL 5 / S-680

S.C.J. : INDICATES A SAW-CUT JOINT IN THE SLAB ON GRADE. SEE TYPICAL SAW-CUT JOINT DETAIL 3 / S-680

C.J. : INDICATES A CONSTRUCTION JOINT. USE 24 GAUGE KEYED TYPE. DISCONTINUE MESH AT JOINT. SEE TYPICAL CONTROL JOINT DETAIL AND SPECIFICATIONS. SEE DETAIL 2 / S-680

R.B.: INDICATES TO PROVIDE 2#4 X 3'-0" LONG. CENTER AT INTERSECTION OF DUMMY JOINT WHERE JOINT IS NOT CONTINUOUS NOR ALIGNED. PLACE 1 BAR 1" CLEAR TOP, AND A SECOND BAR 3" CLEAR TOP OF SLAB.

NOTE: ALL ELEVATIONS SHOWN ARE TOP OF FOOTING ELEVATION.

NOTE: SEE TYPICAL DETAIL AT BASE OF STEEL COLUMNS. WHERE CONCRETE PIERS ARE NOT SPECIFICALLY DETAILED, PROVIDE A PIER AS NOTED ON DETAIL.

FOUNDATION PLAN NOTES

NOTE: UNLESS NOTED OTHERWISE ON PLANS, TOP OF FOOTINGS AT ALL INTERIOR FOOTINGS SHALL BE [-2'-0"] BELOW FINISH FLOOR SLAB.

NOTE: MAXIMUM SPACING OF VERTICAL CONTROL JOINTS IN EXTERIOR MASONRY VENEER IS 16'-0" FROM CORNERS AND 32'-0" FOR INTERMEDIATE VERTICAL JOINTS. SEE ARCHITECT FOR EXACT LOCATIONS.


NOTE: FOR ISOLATION JOINT AT COLUMN BASES, SEE TYPICAL DETAIL: 8 / S-680

NOTE: MAXIMUM EARTH DIFFERENTIAL WHEN BACKFILLING SHOULD NOT EXCEED 2'-0"

NOTE: SLABS-ON-GRADE REQUIRE CONTROL JOINTS PER THE TYPICAL DETAILS UNLESS NOTED OTHERWISE. LOCATE CONSTRUCTION AND CONTROL JOINTS IN SUCH A WAY TO MINIMIZE THE EFFECTS OF SHRINKAGE AND CURLING OF THE CONCRETE SLAB SECTIONS. SUBMIT TO THE ARCHITECT/ENGINEER/EQUIPMENT VENDOR THE SEQUENCE AND METHOD OF CASTING CONCRETE SLABS-ON-GRADE PRIOR TO PLACING THESE ELEMENTS. JOINT SPACING SHALL NOT EXCEED **12'-6"**, AND THE RESULTING PLAN ASPECT RATIO (PANEL LENGTH TO PANEL WIDTH) OF ANY GIVEN SECTION OF SLAB SHALL NOT EXCEED **1.5**. WHERE POSSIBLE, CONTROL JOINT LAYOUT SHALL BE SUCH THAT JOINTS ALIGN WITH THE VERTICES OF COLUMN ISOLATION BLOCKOUTS AND SHALL BE ARRANGED IN A GENERALLY ORTHOGONAL MANNER.

NOTE: GENERAL CONTRACTOR SHALL ENGAGE A SURVEYOR TO PROVIDE LOCATIONS OF ALL EXISTING UTILITES, TRENCHES, ETC. TO ENSURE THAT NEW FOUNDATIONS WILL NOT INTERFERE, UNDERMINE, OR BEAR ON EXISTING UTILITIES.

NOTE: CONTRACTOR SHALL COORDINATE EXACT LOCATIONS OF ALL FLOOR JOINTS AND DUMMY JOINTS WITH THE ARCHITECTURAL JOINTS IN FINISHES. ALL FLOOR JOINTS SHOULD COINCIDE DIRECTLY UNDER A JOINT IN THE ARCHITECTURAL FINISH ABOVE. SEE ARCHITECTURAL DRAWINGS.

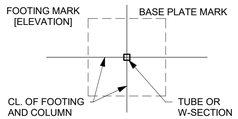

FOOTING KEY

NOTE: UNLESS NOTED OTHERWISE ON PLANS, TOP OF FOOTINGS AT ALL EXTERIOR FOOTINGS SHALL BE [-2'-0"] BELOW FINISH FLOOR SLAB.

STEEL COLUMN SCHEDULE

High Roof											High Roof
16' - 0" Low Roof											16' - 0" Low Roof
13' - 0" Level 1	HSS7X7X1/2	HSS6X6X3/8	HSS5X5X3/8	HSS6X6X3/8	HSS6X6X3/8	HSS6X6X1/2	HSS7X7X1/2	HSS6X6X3/8	HSS5X5X3/8	HSS6X6X1/4	13' - 0" Level 1
0' - 0"											0' - 0"
Column Locations	A-1, A.5-1, B-1, C-2	A-2.6, A-4, A.5-6	A-2.9	A-6, B-2	B-4	B-6	C-3	C-6, D-6, E-3	C-7	D-5	

SLAB AND DECK SCHEDULE


MARK	DESCRIPTION
RD-1.5	DECK: 1-1/2" WIDE RIB TYPE B GAUGE: 22 (t = 0.0295") FINISH: GALVANIZED (G90) GRADE: 50 ksi FASTENER TYPE AT SUPPORT: 5/8" Ø PUDDLE WELDS WITH WELDING WASHERS END SUPPORT ATTACHMENT PATTERN: 36/4 INTERMEDIATE SUPPORT ATTACHMENT PATTERN: 36/4 PERIMETER SUPPORT ATTACHMENT PATTERN: 12" o.c. MAX. SIDE LAP FASTENER: #10 TEK SCREWS @ 18" o.c. MAX. MINIMUM END LAP = 4" (AT SUPPORTS ONLY)
SOG-4	4" CONCRETE SLAB ON A VAPOR RETARDER ON A GRAVEL BED OR SAND CUSHION AS RECOMMENDED BY THE GEOTECHNICAL REPORT. REINFORCE SLAB WITH WELDED WIRE FABRIC 6/6-W2.9xW2.9 IN FLAT SHEETS. FINISH FLOOR SLAB ELEVATION SEE CIVIL FOR DATUM

ANCHOR BOLT SCHEDULE (F1554 GRADE 36)


ANCHOR BOLT DIAMETER	ANCHOR BOLT PROJECTION ABOVE TOP OF FOUNDATION	GROUT THICKNESS	MIN. WASHER WIDTH	MIN. WASHER THICKNESS	COUNT
3/4"	8"	2"	2"	1/4"	56
1"	8"	2"	3"	3/8"	24

BASE PLATE SCHEDULE (36 KSI)

MARK	PLATE WIDTH	PLATE LENGTH	PLATE THICKNESS	ANCHOR BOLT DIAMETER	ANCHOR BOLT EMBEDMENT	COUNT
BP12	12"	12"	3/4"	HEADED ANCHOR BOLT : 3/4" Ø	8"	10
BP14	14"	14"	1"	HEADED ANCHOR BOLT : 3/4" Ø	8"	4
BP1518	15"	18"	3/4"	HEADED ANCHOR BOLT : 1" Ø	8"	4

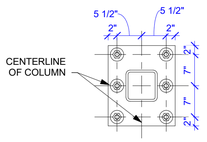


BP1518

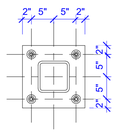


BP14


NOTE: WELD ALL WASHERS TO BASE PLATES AT ALL BRACE FRAME AND MOMENT FRAME COLUMN LOCATIONS.

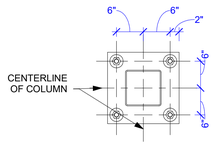

BP16

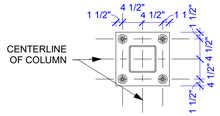

BP12

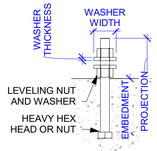

NOTE: SQUARE OR CIRCULAR WASHERS ARE ACCEPTABLE.


HEADED ANCHOR BOLT & WASHER

WALL FOOTING SCHEDULE

MARK	WIDTH	THICKNESS	BOTTOM REINFORCEMENT	TOP REINFORCEMENT
WF20	2' - 0"	1' - 0"	2 #6	

SPREAD FOOTING SCHEDULE

MARK	LENGTH	WIDTH	THICKNESS	BOTTOM REINFORCEMENT	TOP REINFORCEMENT	COUNT
F30	3' - 0"	3' - 0"	1' - 0"	4 #4 EA. WAY		3
F38	3' - 8"	3' - 8"	1' - 0"	5 #4 EA. WAY		3
F50	5' - 0"	5' - 0"	1' - 2"	5 #5 EA. WAY		6
F60	6' - 0"	6' - 0"	1' - 4"	7 #5 EA. WAY		1
F70	7' - 0"	7' - 0"	1' - 4"	7 #6 EA. WAY		1
F7040	4' - 0"	7' - 0"	1' - 4"	7 #6 SW, 5 #6 LW	7 #6 SW, 5 #6 LW	1
F10050	5' - 0"	10' - 0"	1' - 2"	9 #6 SW, 5 #6 LW	9 #6 SW, 5 #6 LW	1

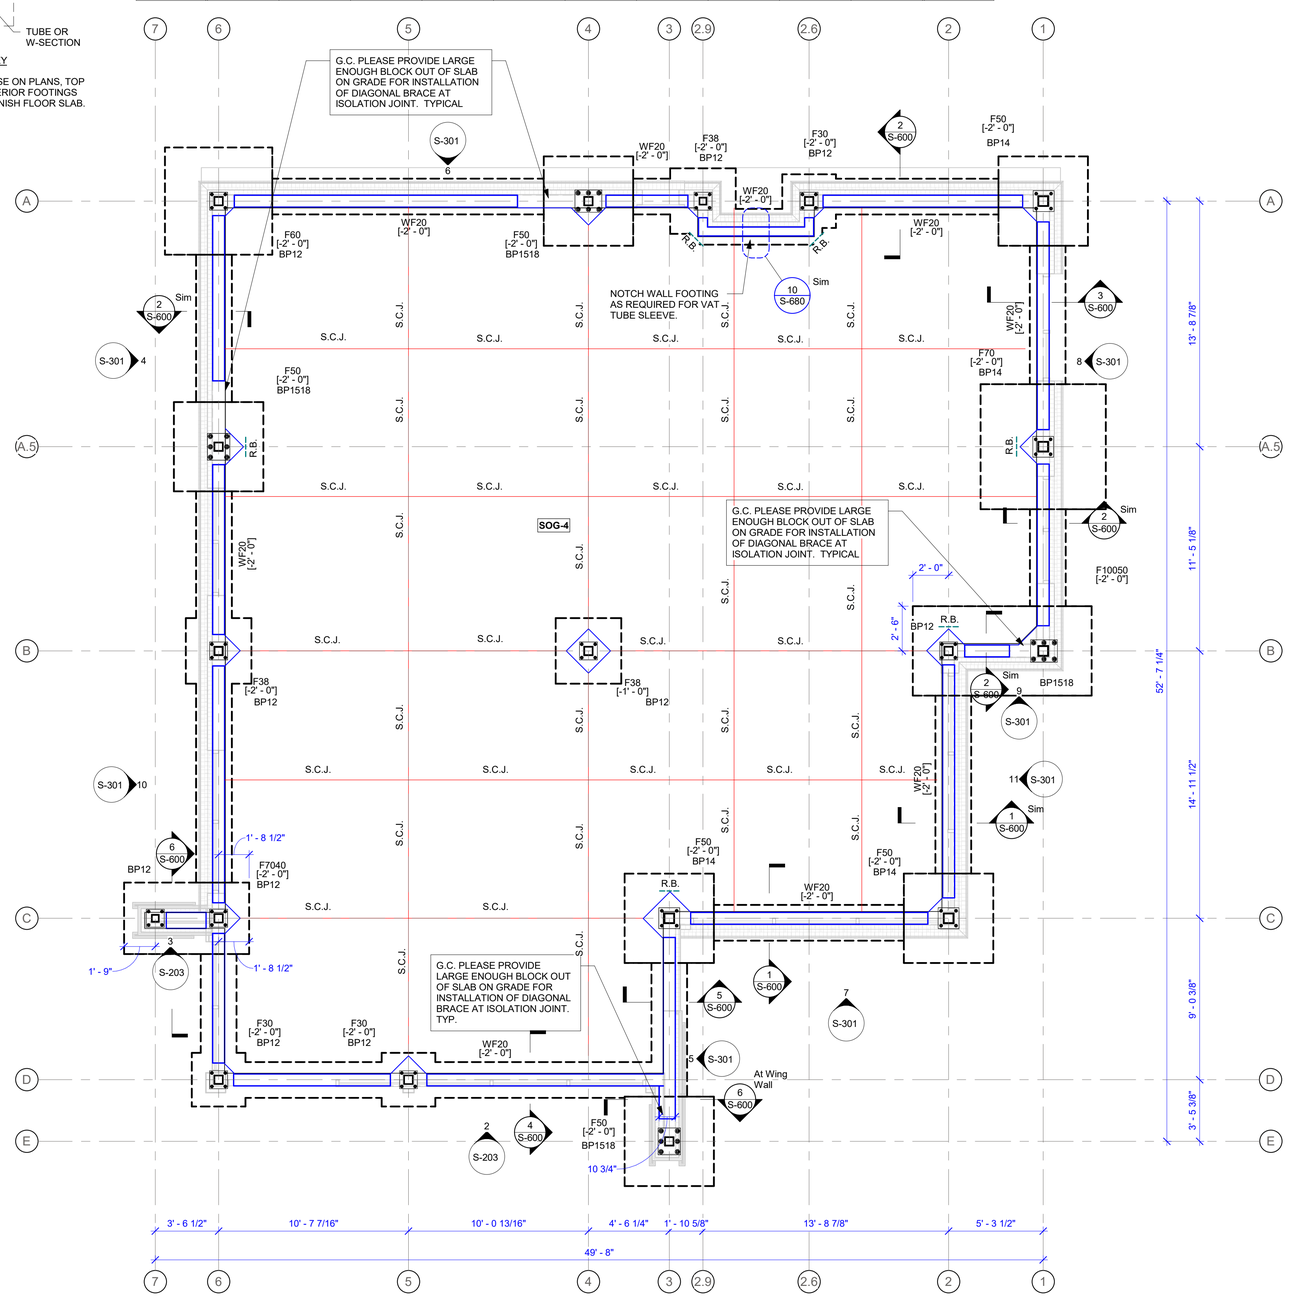

1 S-201 Foundation Plan

1/4" = 1'-0"

Gridline Type Legend

NEW GRIDLINE

PRAXIS3

100 Peachtree St NW
Suite 1450
Atlanta, GA 30303

404-875-4500 tel
404-876-8884 fax
www.praxis3.com

GEORGIA REGISTERED No. SE001277 STRUCTURAL ENGINEER MARK W. NANNIS

Copyright © 2026 Praxis3, LLC

All reports, plans, specifications, computer files, field data, notes and other documents and instruments prepared by Praxis3 shall retain all common law, statutory and other reserved rights, including copyright thereto.

This drawing may not be reproduced in whole or in part without written permission of Praxis3. It is to be returned upon request. Scales as stated are valid on the original drawings.

Rev	Date	Comments
1	07/02/2026	PERMIT SET

MARK NANNIS STRUCTURAL ENGINEERS

Mark Nannis Structural Engineers
2060 Buford Highway NE, Suite 106
Buford, GA 30518

All drawings, specifications, and other work product of Mark Nannis Structural Engineers (henceforth referred to as "The Engineer") for this project are instruments of service for this project only and shall remain the property of The Engineer whether the project is complete or not. Reuse of any of the instruments of service of The Engineer by the owner or extensions of this project without the written permission of The Engineer shall be at the owner's risk and the owner agrees to defend, indemnify, and hold harmless The Engineer from all claims, damages, and expenses including attorney's fees arising out of such unauthorized reuse of The Engineer's instruments of service by the owner or others acting through the owner.
© 2026

Client:

FIFTH THIRD BANK

Project Number: 26302
Project Name:

WATSON BLVD.

2711 WATSON BOULEVARD
WARNER ROBINS, GA 31093

Sheet Title:

Structural Plan - Foundation

Sheet Number:

S-201

RELEASED FOR CONSTRUCTION AND PERMIT

6/26/2026 12:52:19 PM

ROOF FRAMING PLAN NOTES

##k BEAM SIZE ##k

ASD REACTION IN KIPS

FRAMING KEY

— · — · — : INDICATES CONTINUOUS HORIZONTAL RIGID BRACING AT TOP AND BOTTOM CHORD OF JOIST. ADD "X" TYPE BRIDGING IN FIRST PANEL AND AT EVERY SIXTH PANEL. WELD TO JOIST, FRAMING, AND AT CROSSOVER POINTS. SEE SPECIFICATIONS.

: INDICATES THE DIRECTION THE DECK IS SPANNING.

±FORCE (KIPS) INDICATES COLLECTOR ELEMENT FORCE IN JOIST OR BEAM.

#.#k INDICATES LOAD ON JOIST FROM HOSE REEL, FOR SUPPORT DETAILS SEE: 9 / zS686

INDICATES A MOMENT CONNECTION AT EACH END OF BEAM TO COLUMN. SEE TYPICAL DETAIL FOR FULL PENETRATION WELD OF FLANGES AT EACH END. SEE DETAIL 3 / S-682

H.B. : INDICATES ANGLE 3"x3"x1/4" HORIZONTAL BRACE EXTENDING FROM TOP CHORD OF JOIST OR BEAM TO FACE OF COLUMN. WELD ALL AROUND EACH END WITH A 3/16" FILLET WELD.

A.X. : INDICATES ADDITIONAL "X" TYPE BRIDGING. USE 2"x2"x1/4" ANGLE

S.J. : INDICATES A STRUT JOIST, SEE SPECIFICATIONS.

S.P. : INDICATES A BEAM SPLICE POINT, SEE TYPICAL SPLICE POINT DETAIL9 / S-681

NOTE: WHERE STEEL FRAMING IS USED FOR LATERAL RESISTANCE, SEE STEEL FRAMING ELEVATIONS. FOR WORK POINT AND CONNECTION DETAILS AT BRACING AND KNEE BRACING, SEE DETAILS 1 / S-301 AND 3 / S-301

NOTE: AFTER ALL ROOF DEAD LOAD HAS BEEN INSTALLED, PROVIDE ANGLE BRACES, OR TENSION RODS AS NOTED IN "TYPICAL BAR JOIST ROOF CONSTRUCTION" SEE DETAIL 4 / S-682

NOTE: WHERE CONDENSING UNITS BEAR ON ROOF STRUCTURE, PROVIDE A SUPPORT FRAME SIMILAR TO A ROOF OPENING SUPPORT AT THE PERIMETER OF THE UNIT. PROVIDE ANGLES AS SHOWN IN DETAIL 10 / S-681

NOTE : WHERE TUBE FRAME MEMBERS CONNECT TO COLUMNS, PROVIDE A WELDED CONNECTION ALL AROUND FROM TUBE TO COLUMN, TYP.

NOTE: STEEL REINF. TO BE WELDED SHALL CONFORM TO THE REQUIREMENTS OF ASTM A-706 AND THAT WELDING SHALL BE IN ACCORDANCE WITH AWS D1.4, STRUCTURAL WELDING CODE - REINFORCING STEEL BY AMERICAN WELDING SOCIETY FOR COMPLIANCE WITH ACI 318.

NOTE: FOR FRAMING AROUND ROOF HATCH, PROVIDE CHANNEL FRAMING AS SHOWN ON THE TYPICAL DETAIL FOR FRAMING AROUND MECHANICAL UNITS. (UNLESS NOTED OTHERWISE)

NOTE: KEEP STRUCTURE GUYED AND BRACED UNTIL ALL MASONRY/CONCRETE SHEAR WALLS, DIAGONAL BRACES, MOMENT FRAMES, FRAMED FLOORS AND ROOF DECKS ARE IN PLACE.

NOTE: SEE ARCHITECT AND PLUMBING DRAWINGS FOR LOCATIONS OF ROOF DRAINS. ROOF IS DESIGNED FOR A MAXIMUM DEPTH OF 4" OF WATER AT ANY LOCATION OF THE ROOF. WATER SHALL BE RELIEVED BY EITHER SCUPPERS OR AN INDEPENDENT EMERGENCY OVERFLOW DRAIN AT THE 4" LEVEL.

NOTE: FOR FRAMING AROUND THE PERIMETER OF A MECHANICAL UNIT, SEE TYPICAL DETAIL: 3 / S-681

NOTE: FOR FRAMING AROUND ROOF OPENINGS INCLUDING EXHAUST FANS, ROOF DRAINS AND ANY PENETRATIONS LARGER THAN 12", SEE TYPICAL DETAIL: 10 / S-681


NOTE: CONTRACTOR COORDINATE LOCATION OF OPENINGS AND WEIGHTS OF MECHANICAL UNITS, WITH THE MECHANICAL DRAWINGS. IF WEIGHTS EXCEED WHAT IS SHOWN ON THE STRUCTURAL PLAN, THEN NOTIFY THE STRUCTURAL ENGINEER OF THE CHANGE PRIOR TO ANY DETAILING OR FABRICATION OF JOIST, DECK OR STEEL.

NOTE: AT PERIMETER OF ALL ROOFS, EXPANSION JOINTS, AND TRANSITIONS FROM HIGH TO LOW ROOFS, PROVIDE ROOF CLOSURE ANGLES AS PER SECTIONS DETAILED. WHERE NOT SHOWN, PROVIDE A 4" x 3" x 1/4" CONT. ANGLE LONG LEG VERTICAL. WHERE ANGLE BEARS ON JOIST SEATS, FIELD WELD TO EACH JOIST WITH A 3/16" FILLET WELD. WHERE ANGLE BEARS ON A ROOF BEAM, FIELD WELD WITH A 3/16" FILLET WELD 2" at 12" o.c. MAX.

NOTE: FOR SUPPORT OF ROOF PIPING PERPENDICULAR TO JOIST, AND PARALLEL TO JOIST, SEE DETAIL - / ---


SLAB AND DECK SCHEDULE

MARK	DESCRIPTION
RD-1.5	DECK: 1-1/2" WIDE RIB TYPE B GAUGE: 22 (t = 0.0295") FINISH: GALVANIZED (G90) GRADE: 50 ksi FASTENER TYPE AT SUPPORT: 5/8" Ø PUDDLE WELDS WITH WELDING WASHERS END SUPPORT ATTACHMENT PATTERN: 36/4 INTERMEDIATE SUPPORT ATTACHMENT PATTERN: 36/4 PERIMETER SUPPORT ATTACHMENT PATTERN: 12" o.c. MAX. SIDE LAP FASTENER: #10 TEK SCREWS @ 18" o.c. MAX. MINIMUM END LAP = 4" (AT SUPPORTS ONLY)
SOG-4	4" CONCRETE SLAB ON A VAPOR RETARDER ON A GRAVEL BED OR SAND CUSHION AS RECOMMENDED BY THE GEOTECHNICAL REPORT. REINFORCE SLAB WITH WELDED WIRE FABRIC 6/6-W2.9xW2.9 IN FLAT SHEETS. FINISH FLOOR SLAB ELEVATION SEE CIVIL FOR DATUM

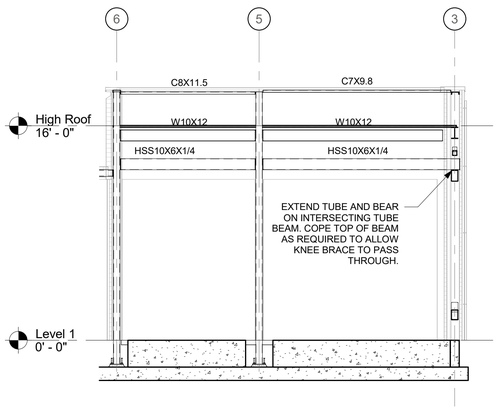


2 / S-203 Frame Elevation

3/16" = 1'-0"

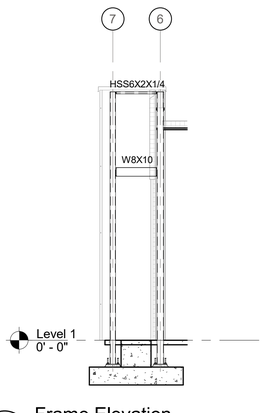

3 / S-203 Frame Elevation

3/16" = 1'-0"

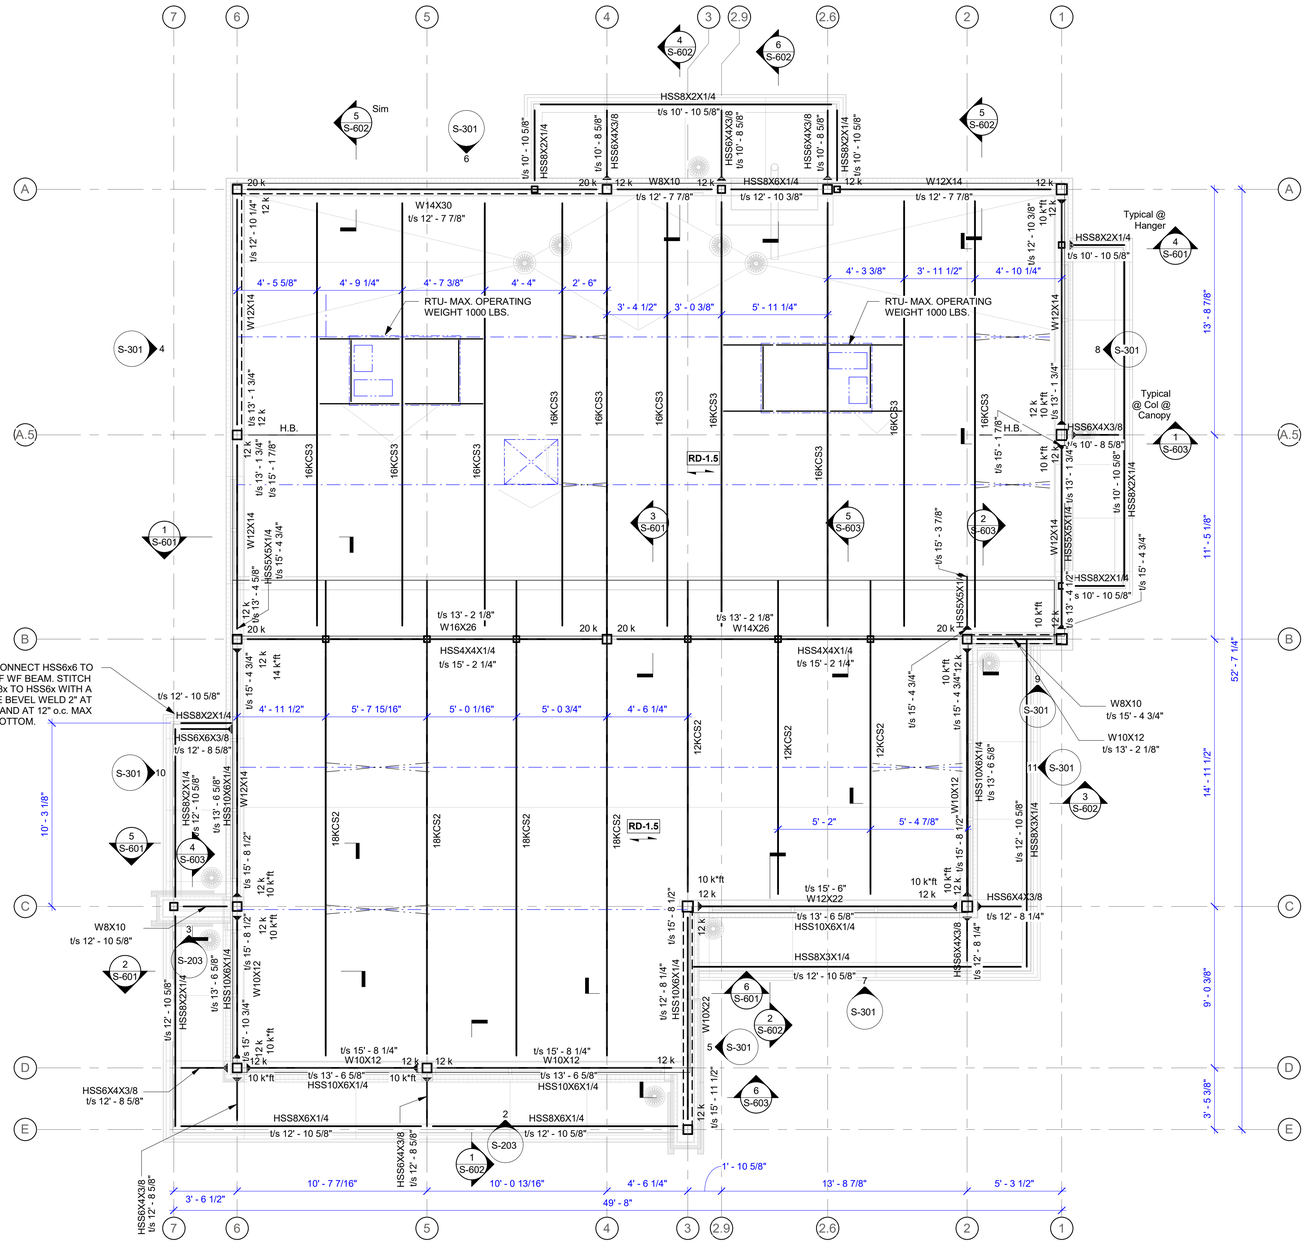

1 / S-203 Roof Framing Plan

1/4" = 1'-0"

Gridline Type Legend

NEW GRIDLINE

PRAXIS3

100 Peachtree St NW
Suite 1450
Atlanta, GA 30303

404-875-4500 tel
404-876-8884 fax
www.praxis3.com

GEORGIA REGISTERED No. SE001277 STRUCTURAL ENGINEER MARK W. NANNIS

Copyright © 2026 Praxis3, LLC

All reports, plans, specifications, computer files, field data, notes and other documents and instruments prepared by Praxis3 shall retain all common law, statutory and other reserved rights, including copyright thereto.

This drawing may not be reproduced in whole or in part without written permission of Praxis3. It is to be returned upon request. Scales as stated are valid on the original drawings.

Rev	Date	Comments
1	07/02/2026	PERMIT SET

MARK NANNIS STRUCTURAL ENGINEERS

Mark Nannis Structural Engineers

2060 Buford Highway NE, Suite 106
Buford, GA 30518

All drawings, specifications, and other work product of Mark Nannis Structural Engineers (henceforth referred to as "The Engineer") for this project are instruments of service for this project only and shall remain the property of The Engineer whether the project is complete or not. Reuse of any of the instruments of service of The Engineer by the owner or extensions of this project without the written permission of The Engineer shall be at the owner's risk and the owner agrees to defend, indemnify, and hold harmless The Engineer from all claims, damages, and expenses including attorney's fees arising out of such unauthorized reuse of The Engineer's instruments of service by the owner or others acting through the owner.
© 2026

Client:

FIFTH THIRD BANK

Project Number: 26302
Project Name:

WATSON BLVD.

2711 WATSON BOULEVARD
WARNER ROBINS, GA 31093

Sheet Title:


Structural Plan - Roof

Sheet Number:

S-203


RELEASED FOR CONSTRUCTION/ AND PERMIT

6/26/2026 12:52:19 PM

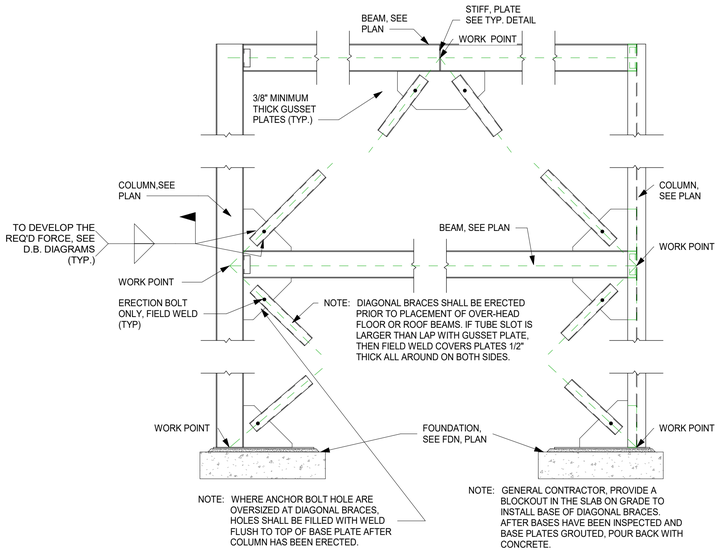

1 S-301 Typical Diagonal Brace Construction and Work Points Detail


3/8" = 1'-0"

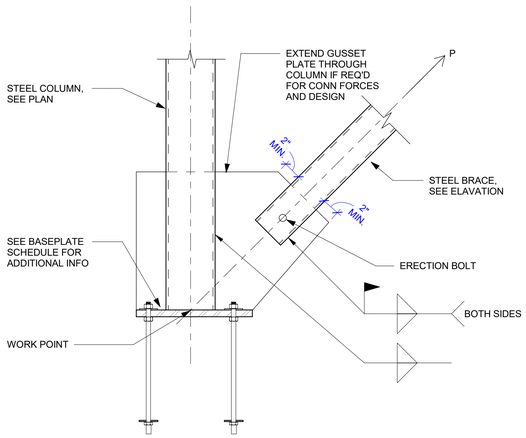

HSS COLUMN BASE WITH BRACE CONNECTION

NOTES:

1. FABRICATOR TO SUBMIT BRACE CONNECTION CALCS WITH SHOP DRAWINGS.
2 "P" - BRACE UNFACTORED (ASD) AXIAL FORCE IN KIPS, SEE ELEVATION FOR FORCES.

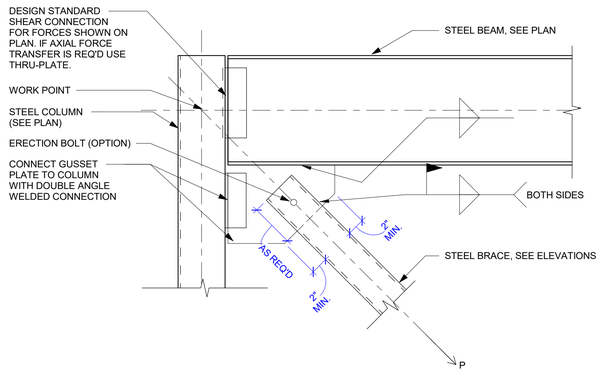


BRACE CONNECTION OF WIDE FLANGE BEAM TO HSS COLUMN

NOTES:

1. FABRICATOR TO SUBMIT BRACE CONNECTION CALCS WITH SHOP DRAWINGS. CONNECTIONS SHALL BE DESIGNED FOR FORCES SHOWN ON BRACE ELEVATIONS AND FRAMING PLANS.
2. FABRICATIOR HAS OPTION TO USE BOLTED GUSSET CONNECTIONS, SUBMIT DETAIL FOR ACCEPTANCE PRIOR TO SUBMITTING SHOP DRAWINGS.
3. TOP OR BOTTOM BRACE MAY NOT BE PRESENT AT SIMILAR CONDITIONS.
4. "P" - BRACE UNFACTORED (ASD) AXIAL FORCE IN KIPS, SEE ELEVATION FOR FORCES.


2 S-301 Typical Detail At Brace Connections

1 1/2" = 1'-0"

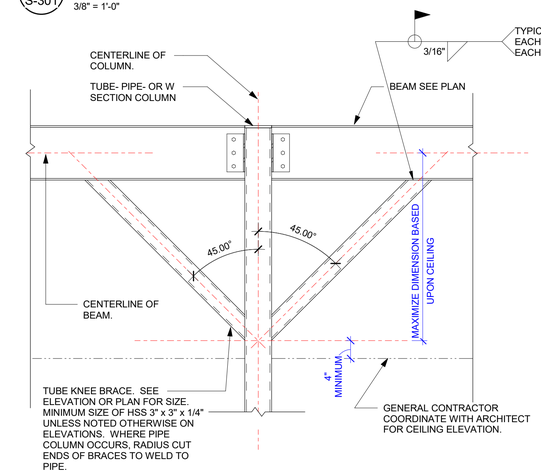


3 S-301 Typical Knee Brace Detail

3/4" = 1'-0"

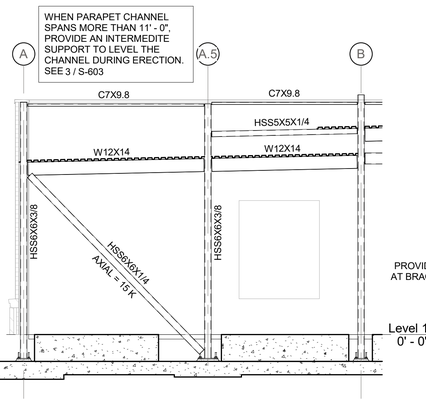


4 S-301 Framing Elevation

3/16" = 1'-0"

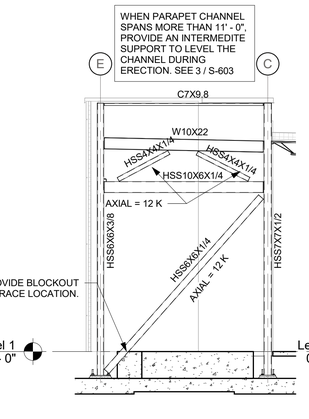


5 S-301 Framing Elevation

3/16" = 1'-0"

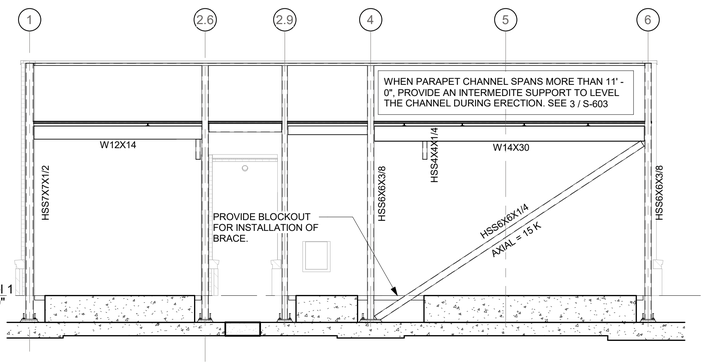


6 S-301 Framing Elevation

3/16" = 1'-0"

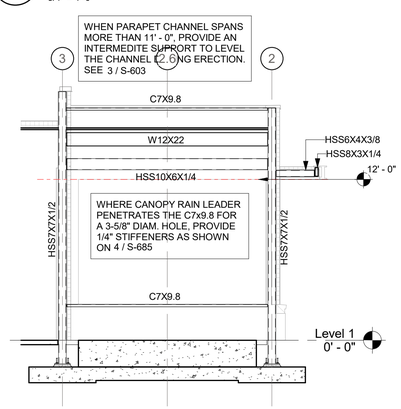


7 S-301 Framing Elevation

3/16" = 1'-0"

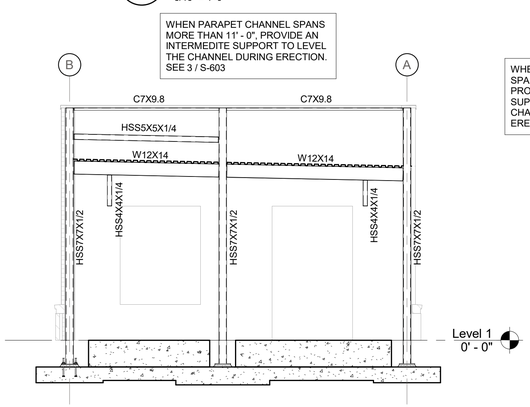


8 S-301 Framing Elevation

3/16" = 1'-0"

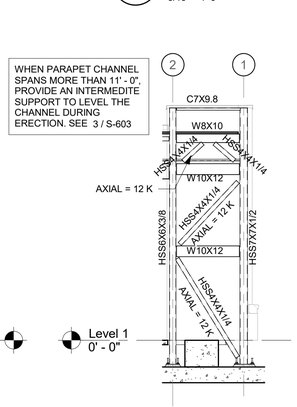


9 S-301 Framing Elevation

3/16" = 1'-0"

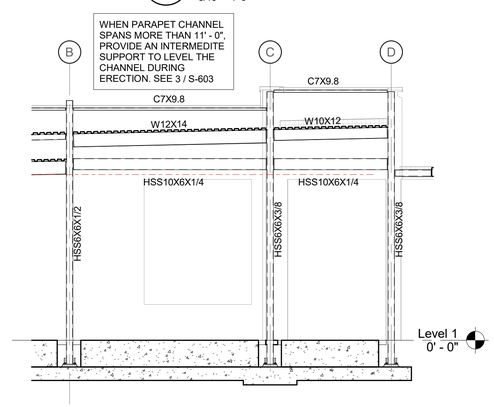

10 S-301 Framing Elevation

3/16" = 1'-0"

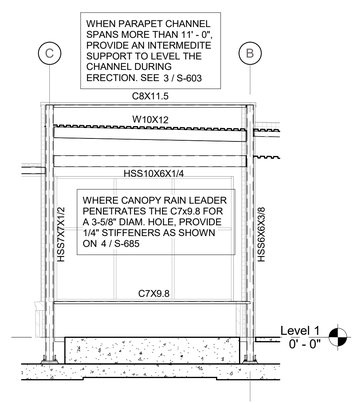

11 S-301 Framing Elevation

3/16" = 1'-0"

PRAXIS3
100 Peachtree St NW
Suite 1450
Atlanta, GA 30303
404-875-4500 tel
404-876-8884 fax
www.praxis3.com

GEORGIA REGISTERED No. SE001277 STRUCTURAL ENGINEER MARK W. NANNIS

Copyright © 2026 Praxis3, LLC

All reports, plans, specifications, computer files, field data, notes and other documents and instruments prepared by Praxis3 shall retain all common law, statutory and other reserved rights, including copyright thereto.

This drawing may not be reproduced in whole or in part without written permission of Praxis3. It is to be returned upon request. Scales as stated are valid on the original drawings.

Rev	Date	Comments
1	07/02/2026	PERMIT SET

MARK NANNIS STRUCTURAL ENGINEERS

Mark Nannis Structural Engineers
2060 Buford Highway NE, Suite 106
Buford, GA 30518

All drawings, specifications, and other work product of Mark Nannis Structural Engineers (henceforth referred to as "The Engineer") for this project are instruments of service for this project only and shall remain the property of The Engineer whether the project is complete or not. Reuse of any of the instruments of service of The Engineer by the owner or extensions of this project without the written permission of The Engineer shall be at the owner's risk and the owner agrees to defend, indemnify, and hold harmless The Engineer from all claims, damages, and expenses including attorney's fees arising out of such unauthorized reuse of The Engineer's instruments of service by the owner or others acting through the owner.
© 2026

Client:

FIFTH THIRD BANK

Project Number: 26302
Project Name:

WATSON BLVD.

2711 WATSON BOULEVARD
WARNER ROBINS, GA 31093

Sheet Title:


Elevations - Steel Frames

Sheet Number:


S-301

RELEASED FOR CONSTRUCTION AND PERMIT

6/26/2026 12:52:22 PM

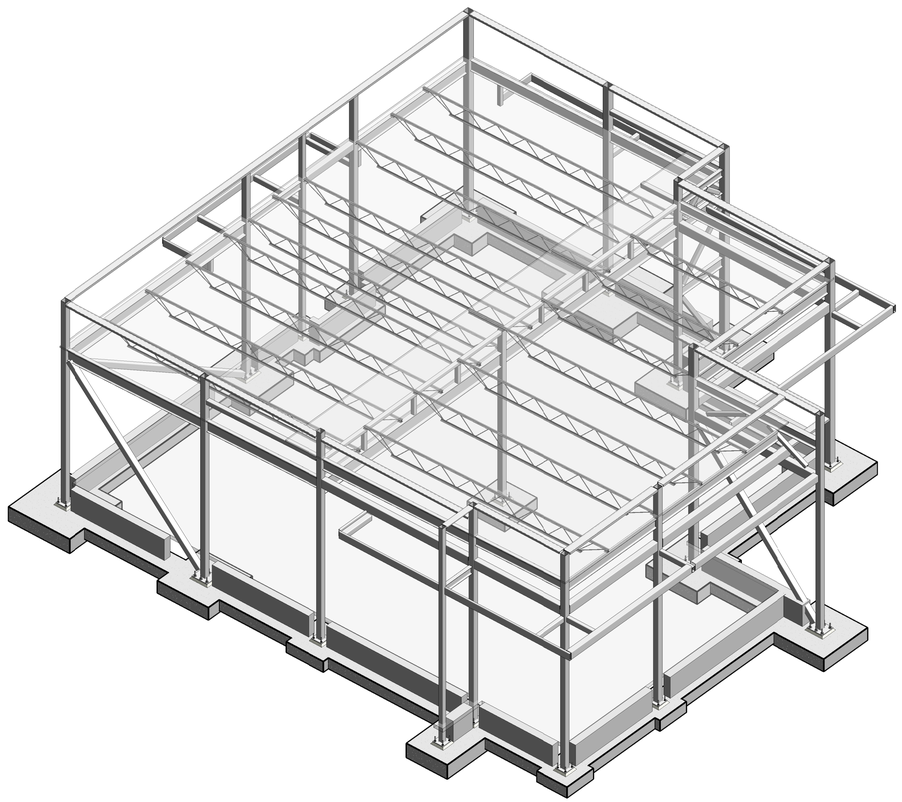

1 S-410 Axon 1

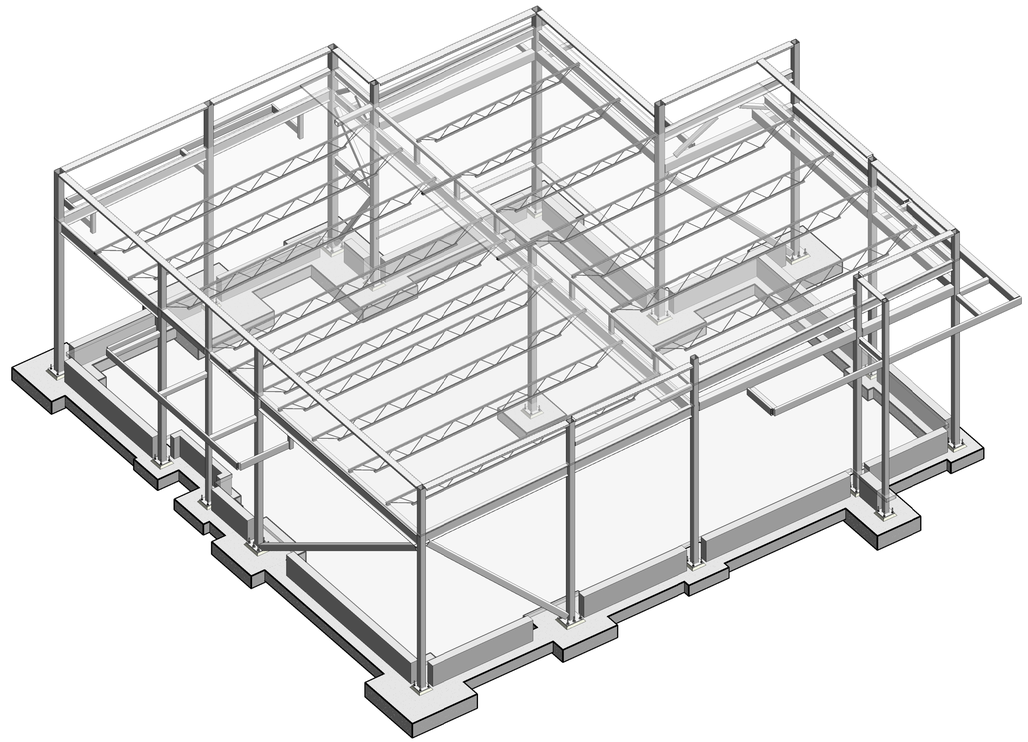

2 S-410 Axon 2

NOTE: AXONOMETRIC VIEWS ARE SHOWN FOR VISUAL REFERENCE ONLY AND MAY NOT ACCURATELY REPRESENT ACTUAL DESIGN OR DIMENSIONS. USE ONLY IN CONJUNCTION WITH PLANS, DETAILS, AND SECTIONS.

6/26/2026 12:52:24 PM

PRAXIS3

100 Peachtree St NW
Suite 1450
Atlanta, GA 30303

404-875-4500 tel
404-876-8884 fax
www.praxis3.com

GEORGIA REGISTERED No. SE001277 STRUCTURAL ENGINEER MARK W. NANNIS

Copyright © 2026 Praxis3, LLC

All reports, plans, specifications, computer files, field data, notes and other documents and instruments prepared by Praxis3 shall retain all common law, statutory and other reserved rights, including copyright thereto.

This drawing may not be reproduced in whole or in part without written permission of Praxis3. It is to be returned upon request. Scales as stated are valid on the original drawings.

Rev	Date	Comments
1	07/02/2026	PERMIT SET

MARK NANNIS STRUCTURAL ENGINEERS

Mark Nannis Structural Engineers

2060 Buford Highway NE, Suite 106
Buford, GA 30518

All drawings, specifications, and other work product of Mark Nannis Structural Engineers (henceforth referred to as "The Engineer") for this project are instruments of service for this project only and shall remain the property of The Engineer whether the project is complete or not. Reuse of any of the instruments of service of The Engineer by the owner or extensions of this project without the written permission of The Engineer shall be at the owner's risk and the owner agrees to defend, indemnify, and hold harmless The Engineer from all claims, damages, and expenses including attorney's fees arising out of such unauthorized reuse of The Engineer's instruments of service by the owner or others acting through the owner.
© 2026

Client:

FIFTH THIRD BANK

Project Number: 26302
Project Name:

WATSON BLVD.

2711 WATSON BOULEVARD
WARNER ROBINS, GA 31093

Sheet Title:

Exterior Axonometrics


Sheet Number:

S-410

RELEASED FOR CONSTRUCTION AND PERMIT



1 S-411 Axon 3

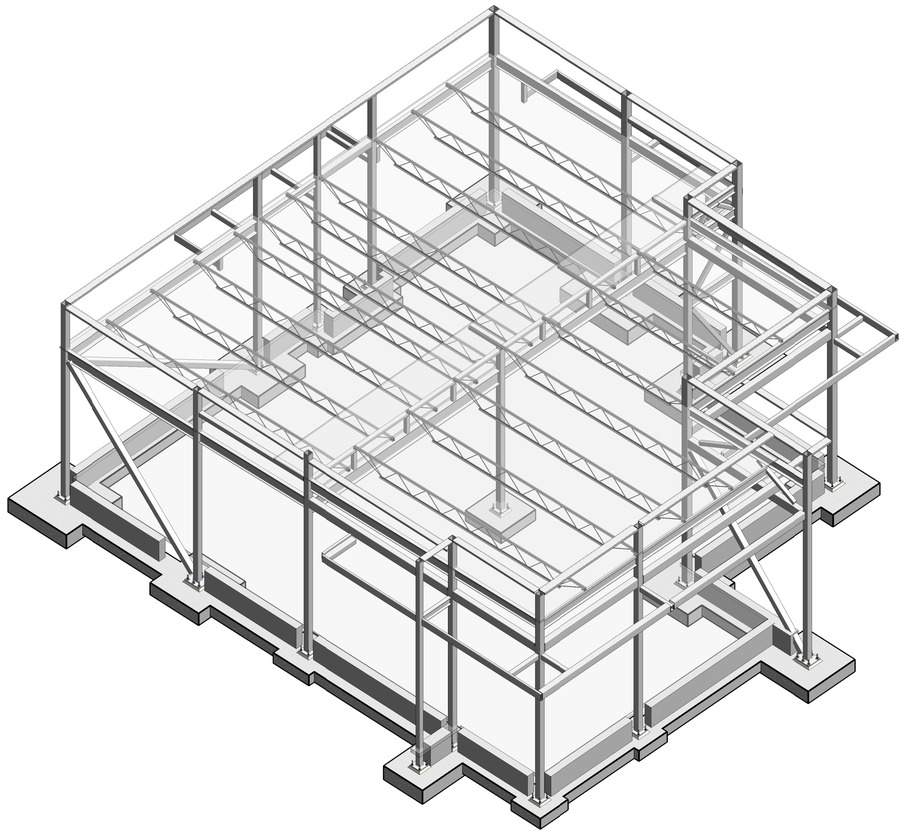

2 S-411 Axon 4

NOTE: AXONOMETRIC VIEWS ARE SHOWN FOR VISUAL REFERENCE ONLY AND MAY NOT ACCURATELY REPRESENT ACTUAL DESIGN OR DIMENSIONS. USE ONLY IN CONJUNCTION WITH PLANS, DETAILS, AND SECTIONS.

6/26/2026 12:52:26 PM

PRAXIS3

100 Peachtree St NW
Suite 1450
Atlanta, GA 30303

404-875-4500 tel
404-876-8884 fax
www.praxis3.com

GEORGIA REGISTERED No. SE001277 STRUCTURAL ENGINEER MARK W. NANNIS

Copyright © 2026 Praxis3, LLC

All reports, plans, specifications, computer files, field data, notes and other documents and instruments prepared by Praxis3 shall retain all common law, statutory and other reserved rights, including copyright thereto.

This drawing may not be reproduced in whole or in part without written permission of Praxis3. It is to be returned upon request. Scales as stated are valid on the original drawings.

Rev	Date	Comments
1	07/02/2026	PERMIT SET

MARK NANNIS STRUCTURAL ENGINEERS

Mark Nannis Structural Engineers

2060 Buford Highway NE, Suite 106
Buford, GA 30518

All drawings, specifications, and other work product of Mark Nannis Structural Engineers (henceforth referred to as "The Engineer") for this project are instruments of service for this project only and shall remain the property of The Engineer whether the project is complete or not. Reuse of any of the instruments of service of The Engineer by the owner or extensions of this project without the written permission of The Engineer shall be at the owner's risk and the owner agrees to defend, indemnify, and hold harmless The Engineer from all claims, damages, and expenses including attorney's fees arising out of such unauthorized reuse of The Engineer's instruments of service by the owner or others acting through the owner.
© 2026

Client:

FIFTH THIRD BANK

Project Number: 26302
Project Name:

WATSON BLVD.

2711 WATSON BOULEVARD
WARNER ROBINS, GA 31093


Sheet Title:

Exterior Axonometrics

Sheet Number:


S-411

RELEASED FOR CONSTRUCTION AND PERMIT

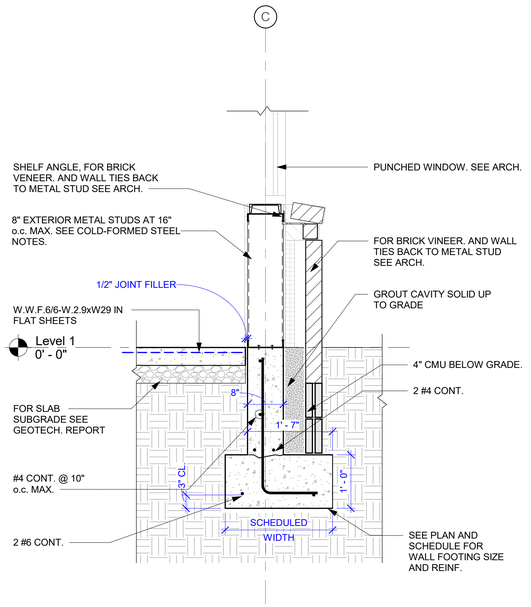


1 S-600 **Section at Exterior Wall**

3/4" = 1'-0"

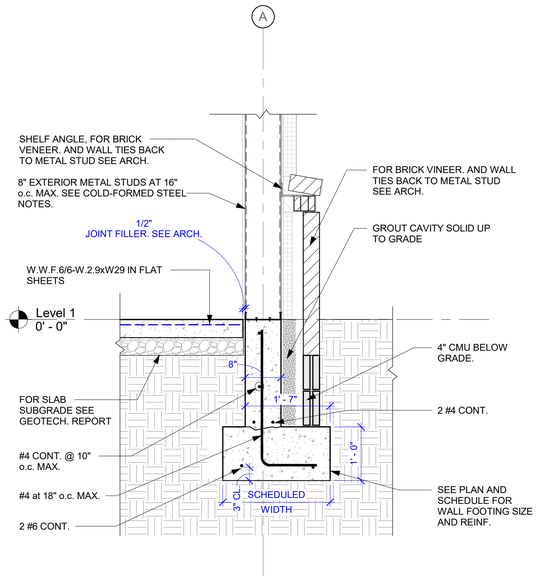


2 S-600 **Section at Exterior Wall**

3/4" = 1'-0"

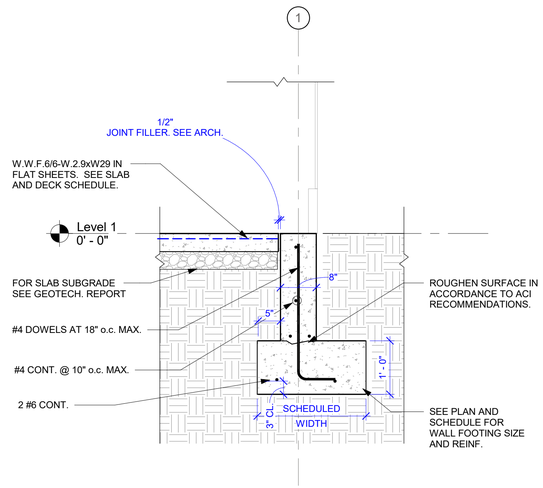


3 S-600 **Section at Exterior Wall and Opening**

3/4" = 1'-0"

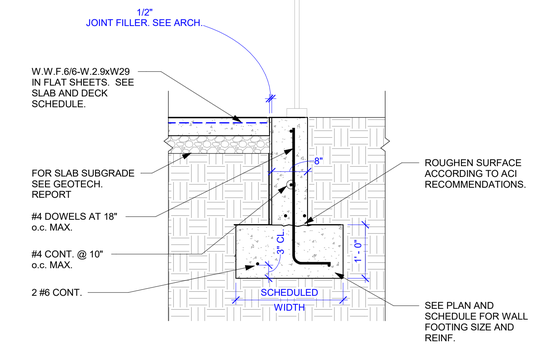


4 S-600 **Section at Exterior Wall and Storefront**

3/4" = 1'-0"

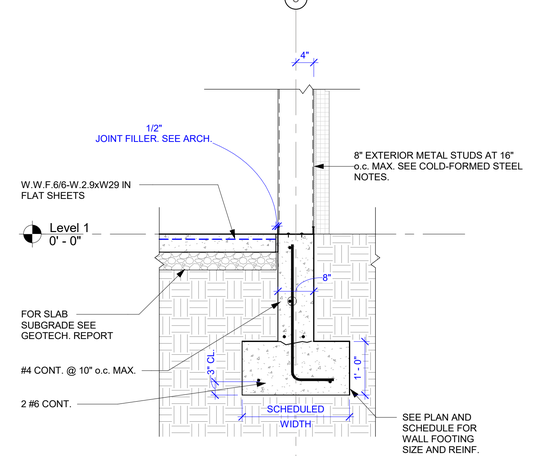

5 S-600 **Section at Exterior Wall**

3/4" = 1'-0"

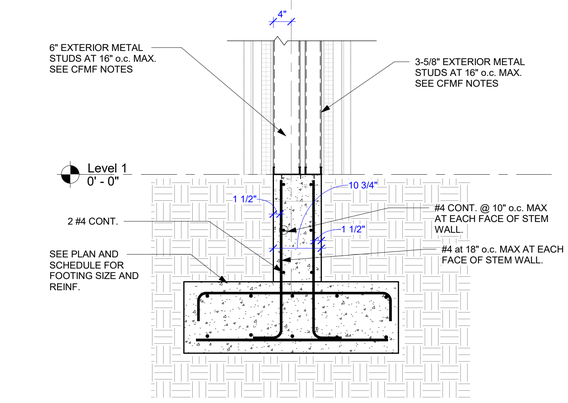

6 S-600 **Section At Foundation And Wing Wall**

3/4" = 1'-0"

6/26/2026 12:52:27 PM

PRAXIS3

100 Peachtree St NW
Suite 1450
Atlanta, GA 30303

404-875-4500 tel
404-876-8884 fax
www.praxis3.com

GEORGIA REGISTERED No. SE001277 STRUCTURAL ENGINEER MARK W. NANNIS

Copyright © 2026 Praxis3, LLC

All reports, plans, specifications, computer files, field data, notes and other documents and instruments prepared by Praxis3 shall retain all common law, statutory and other reserved rights, including copyright thereto.

This drawing may not be reproduced in whole or in part without written permission of Praxis3. It is to be returned upon request. Scales as stated are valid on the original drawings.

Rev	Date	Comments
1	07/02/2026	PERMIT SET

MARK NANNIS STRUCTURAL ENGINEERS

Mark Nannis Structural Engineers

2060 Buford Highway NE, Suite 106
Buford, GA 30518

All drawings, specifications, and other work product of Mark Nannis Structural Engineers (henceforth referred to as "The Engineer") for this project are instruments of service for this project only and shall remain the property of The Engineer whether the project is complete or not. Reuse of any of the instruments of service of The Engineer by the owner or extensions of this project without the written permission of The Engineer shall be at the owner's risk and the owner agrees to defend, indemnify, and hold harmless The Engineer from all claims, damages, and expenses including attorney's fees arising out of such unauthorized reuse of The Engineer's instruments of service by the owner or others acting through the owner.
© 2026

Client:

FIFTH THIRD BANK

Project Number: 26302
Project Name:

WATSON BLVD.

2711 WATSON BOULEVARD
WARNER ROBINS, GA 31093


Sheet Title:

Wall Sections - Foundation

Sheet Number:


S-600

RELEASED FOR CONSTRUCTION AND PERMIT

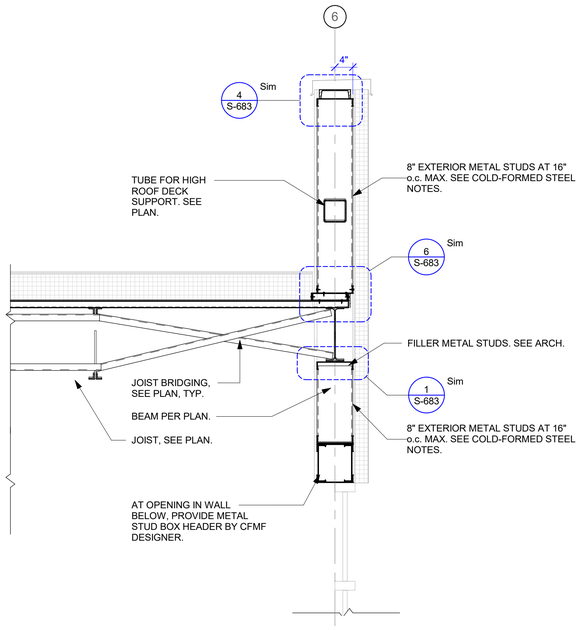


1 S-601 **Section at Roof - Joist Parallel**

3/4" = 1'-0"

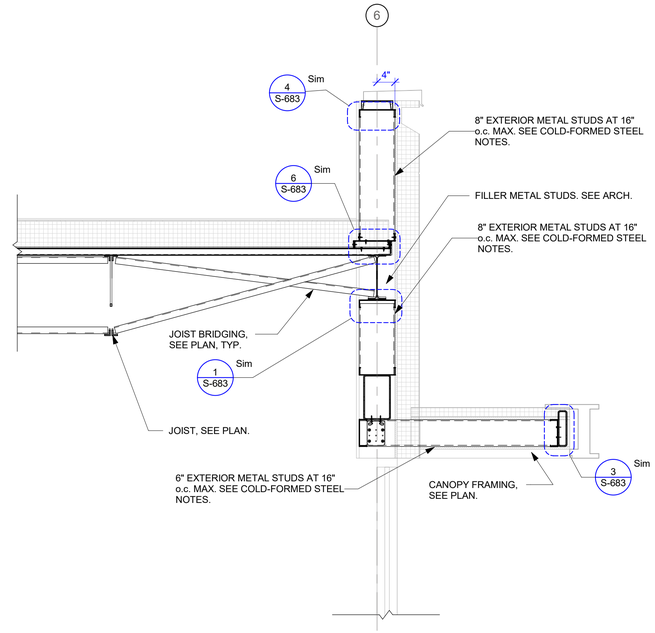


2 S-601 **Section at Roof at Canopy**

3/4" = 1'-0"

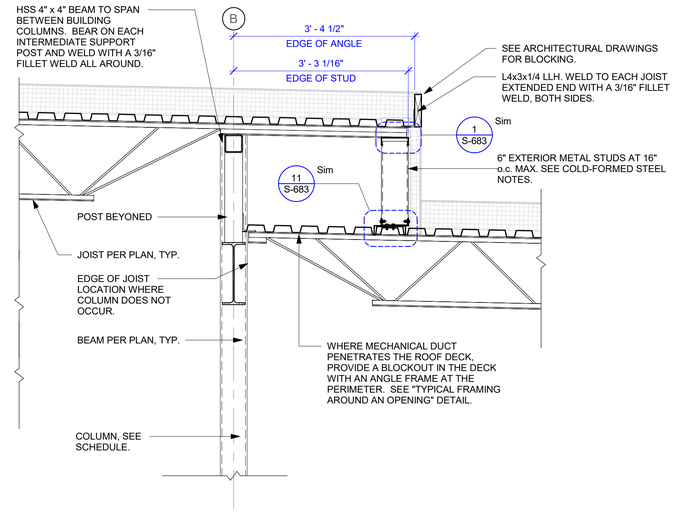


3 S-601 **Section at Exterior Wall**

3/4" = 1'-0"

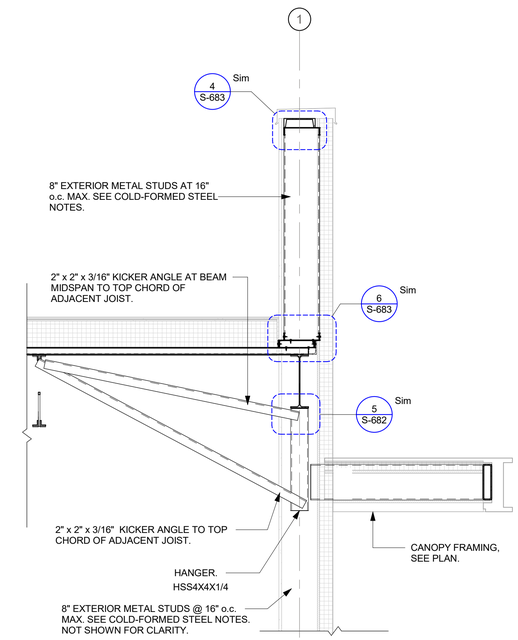


4 S-601 **Section at Canopy at Hanger**

3/4" = 1'-0"

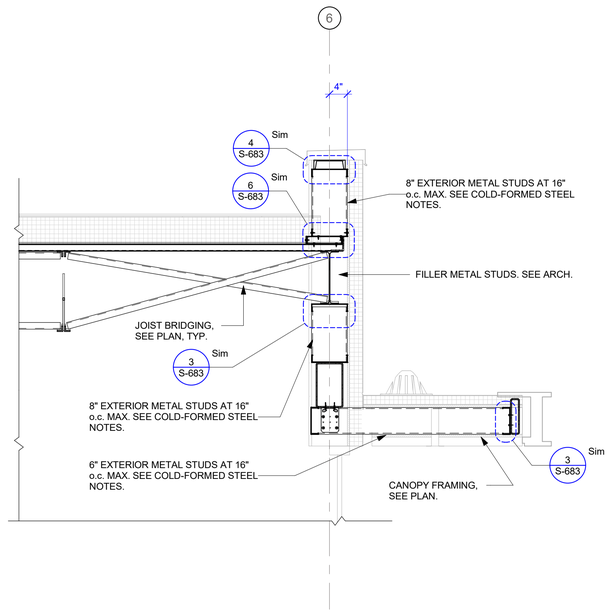

5 S-601 **Section at Canopy**

3/4" = 1'-0"

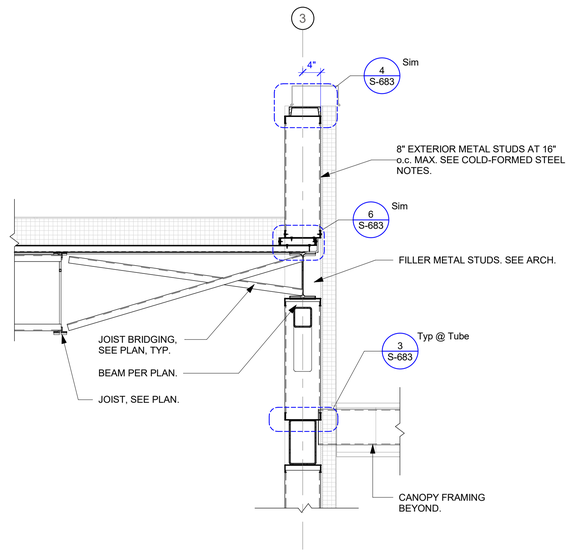

6 S-601 **Section at Exterior Wall**

3/4" = 1'-0"

PRAXIS3

100 Peachtree St NW
Suite 1450
Atlanta, GA 30303

404-875-4500 tel
404-876-8884 fax
www.praxis3.com

GEORGIA REGISTERED No. SE001277 STRUCTURAL ENGINEER MARK W. NANNIS

Copyright © 2026 Praxis3, LLC

All reports, plans, specifications, computer files, field data, notes and other documents and instruments prepared by Praxis3 shall retain all common law, statutory and other reserved rights, including copyright thereto.

This drawing may not be reproduced in whole or in part without written permission of Praxis3. It is to be returned upon request. Scales as stated are valid on the original drawings.

Rev	Date	Comments
1	07/02/2026	PERMIT SET

MARK NANNIS STRUCTURAL ENGINEERS

Mark Nannis Structural Engineers

2060 Buford Highway NE, Suite 106
Buford, GA 30518

All drawings, specifications, and other work product of Mark Nannis Structural Engineers (henceforth referred to as "The Engineer") for this project are instruments of service for this project only and shall remain the property of The Engineer whether the project is complete or not. Reuse of any of the instruments of service of The Engineer by the owner or extensions of this project without the written permission of The Engineer shall be at the owner's risk and the owner agrees to defend, indemnify, and hold harmless The Engineer from all claims, damages, and expenses including attorney's fees arising out of such unauthorized reuse of The Engineer's instruments of service by the owner or others acting through the owner.
© 2026

Client:

FIFTH THIRD BANK

Project Number: 26302
Project Name:

WATSON BLVD.

2711 WATSON BOULEVARD
WARNER ROBINS, GA 31093

Sheet Title:


Wall Sections

Sheet Number:

S-601


RELEASED FOR CONSTRUCTION AND PERMIT

6/26/2026 12:52:28 PM

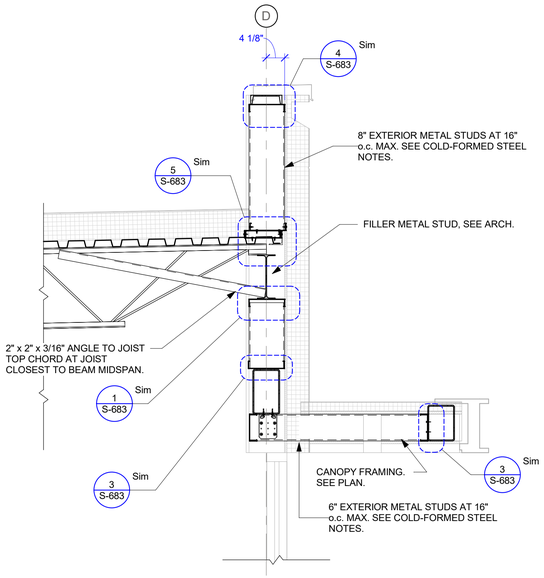


1 S-602 Section at Exterior Wall

3/4" = 1'-0"

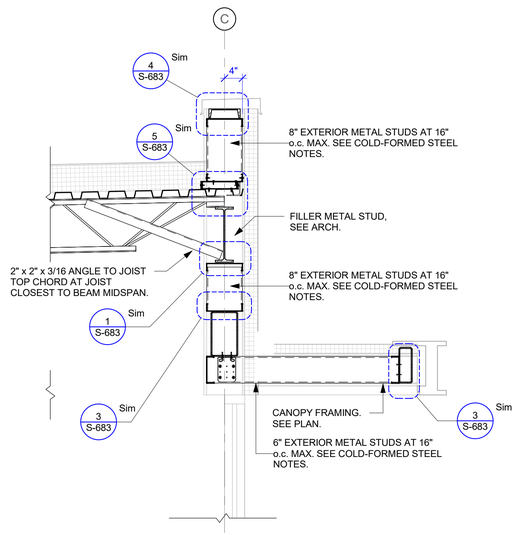


2 S-602 Section at Exterior Wall

3/4" = 1'-0"

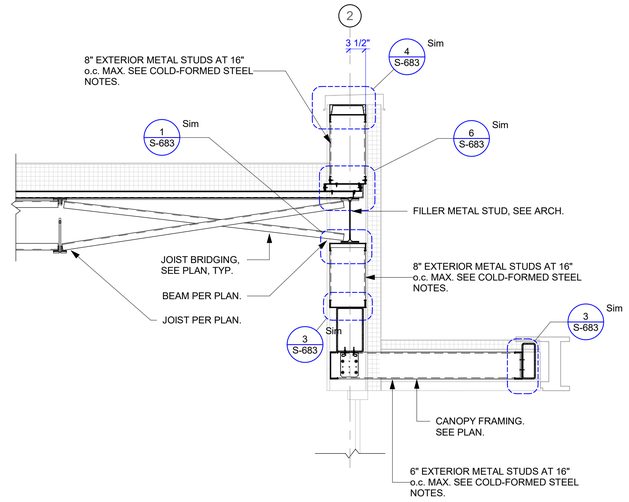


3 S-602 Section at Exterior Wall

3/4" = 1'-0"

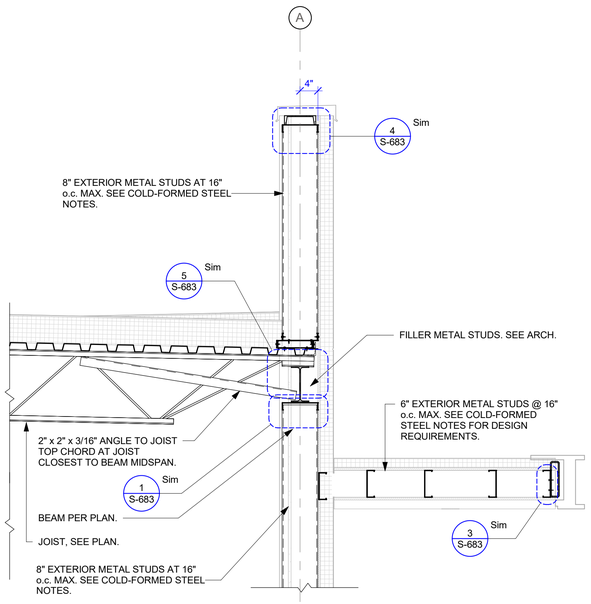


4 S-602 Section at Roof and Canopy

3/4" = 1'-0"

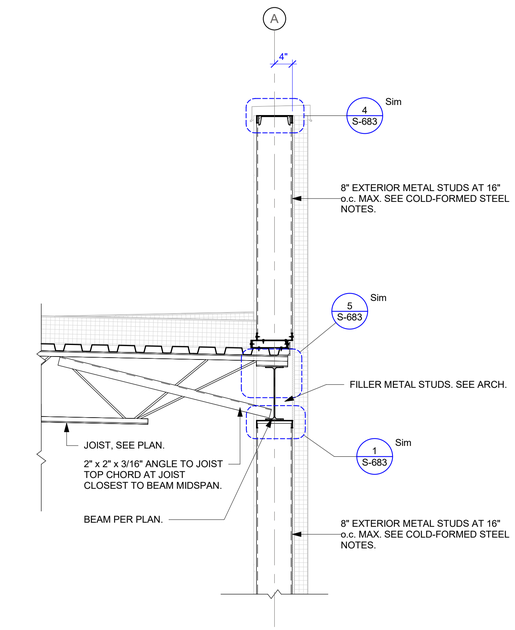

5 S-602 Section at Exterior Wall

3/4" = 1'-0"

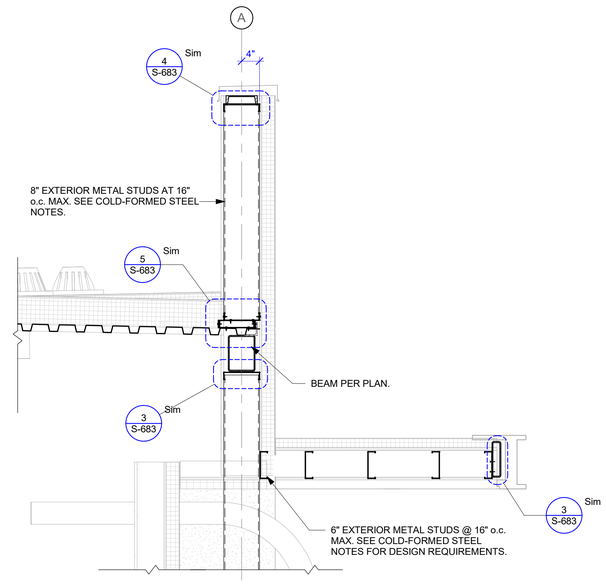

6 S-602 Section at Roof and Canopy

3/4" = 1'-0"

6/26/2026 12:52:28 PM

PRAXIS3

100 Peachtree St NW
Suite 1450
Atlanta, GA 30303

404-875-4500 tel
404-876-8884 fax
www.praxis3.com

GEORGIA REGISTERED No. SE001277 STRUCTURAL ENGINEER MARK W. NANNIS

Copyright © 2026 Praxis3, LLC

All reports, plans, specifications, computer files, field data, notes and other documents and instruments prepared by Praxis3 shall retain all common law, statutory and other reserved rights, including copyright thereto.

This drawing may not be reproduced in whole or in part without written permission of Praxis3. It is to be returned upon request. Scales as stated are valid on the original drawings.

Rev	Date	Comments
1	07/02/2026	PERMIT SET

MARK NANNIS STRUCTURAL ENGINEERS

Mark Nannis Structural Engineers

2060 Buford Highway NE, Suite 106
Buford, GA 30518

All drawings, specifications, and other work product of Mark Nannis Structural Engineers (henceforth referred to as "The Engineer") for this project are instruments of service for this project only and shall remain the property of The Engineer whether the project is complete or not. Reuse of any of the instruments of service of The Engineer by the owner or extensions of this project without the written permission of The Engineer shall be at the owner's risk and the owner agrees to defend, indemnify, and hold harmless The Engineer from all claims, damages, and expenses including attorney's fees arising out of such unauthorized reuse of The Engineer's instruments of service by the owner or others acting through the owner.
© 2026

Client:

FIFTH THIRD BANK

Project Number: 26302
Project Name:

WATSON BLVD.

2711 WATSON BOULEVARD
WARNER ROBINS, GA 31093


Sheet Title:

Wall Sections

Sheet Number:


S-602

RELEASED FOR CONSTRUCTION AND PERMIT

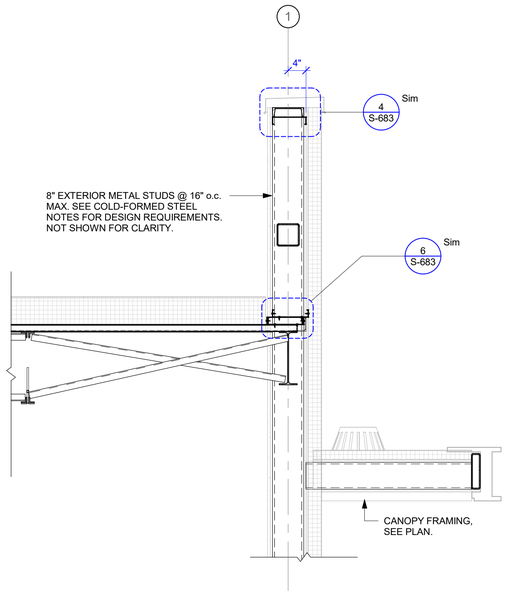


1 S-603 **Section at Canopy Outrigger at Column**

3/4" = 1'-0"

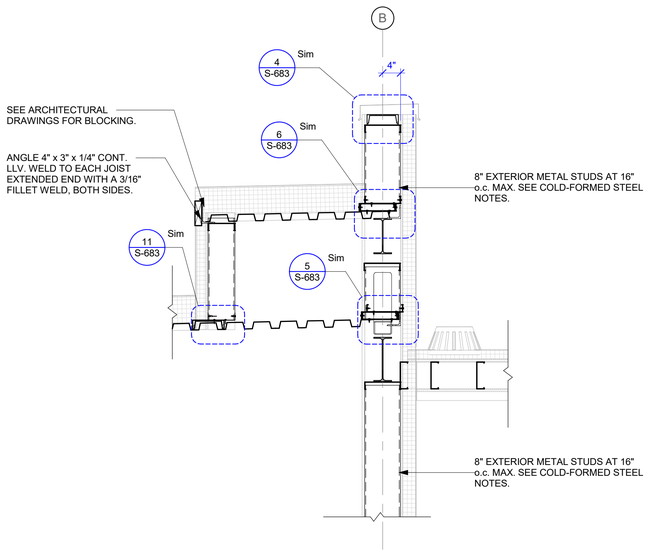


2 S-603 **Section At Roof And Canopy**

3/4" = 1'-0"

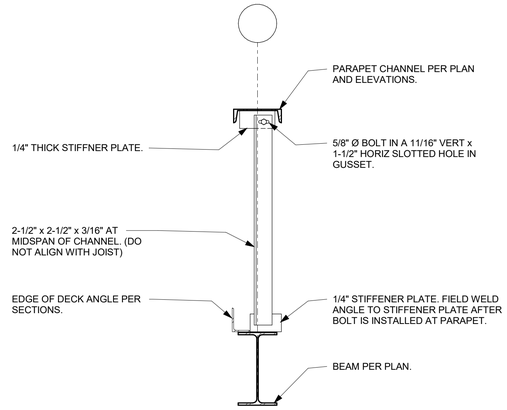


3 S-603 **Typical Detail Of Shoring At Channel**

1" = 1'-0"

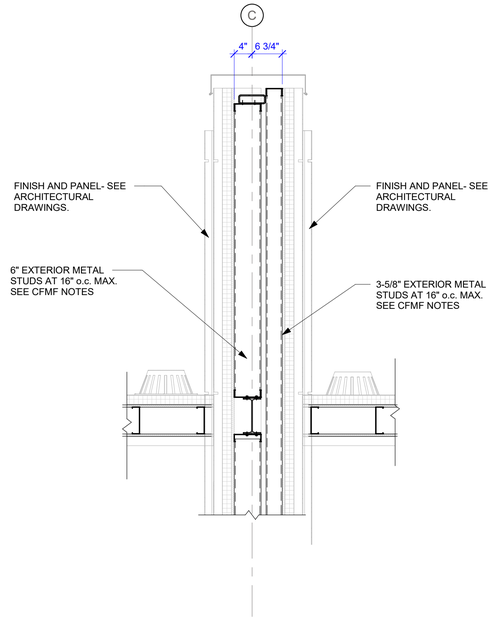


4 S-603 **Section At Wing Wall And Roof**

3/4" = 1'-0"

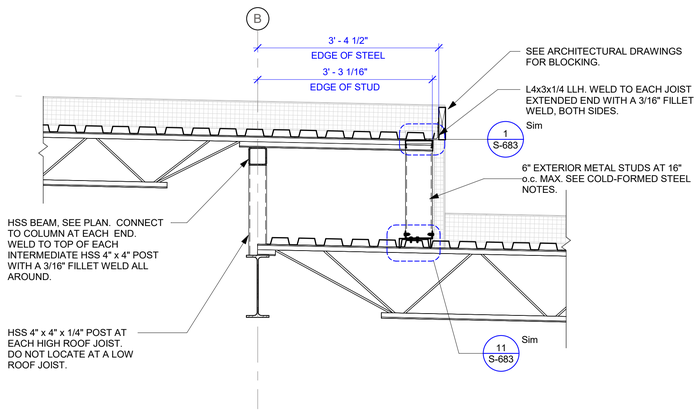

5 S-603 **Section at Exterior Wall**

3/4" = 1'-0"

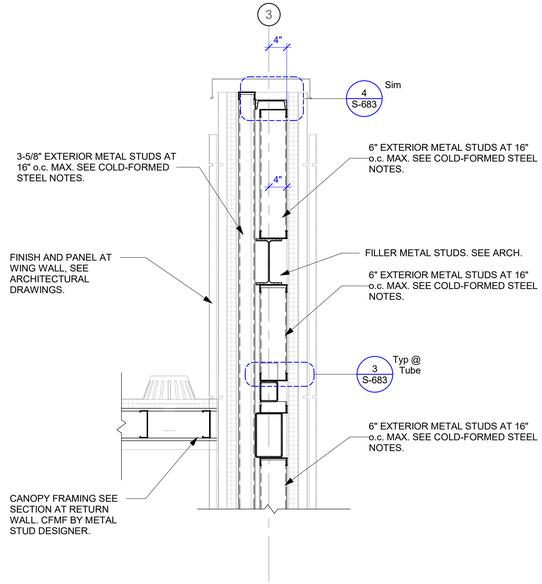

6 S-603 **Section At Wing Wall**

3/4" = 1'-0"

PRAXIS3

100 Peachtree St NW
Suite 1450
Atlanta, GA 30303

404-875-4500 tel
404-876-8884 fax
www.praxis3.com

GEORGIA REGISTERED No. SE001277 STRUCTURAL ENGINEER MARK W. NANNIS

Copyright © 2026 Praxis3, LLC

All reports, plans, specifications, computer files, field data, notes and other documents and instruments prepared by Praxis3 shall retain all common law, statutory and other reserved rights, including copyright thereto.

This drawing may not be reproduced in whole or in part without written permission of Praxis3. It is to be returned upon request. Scales as stated are valid on the original drawings.

Rev	Date	Comments
1	07/02/2026	PERMIT SET

MARK NANNIS STRUCTURAL ENGINEERS

Mark Nannis Structural Engineers

2060 Buford Highway NE, Suite 106
Buford, GA 30518

All drawings, specifications, and other work product of Mark Nannis Structural Engineers (henceforth referred to as "The Engineer") for this project are instruments of service for this project only and shall remain the property of The Engineer whether the project is complete or not. Reuse of any of the instruments of service of The Engineer by the owner or extensions of this project without the written permission of The Engineer shall be at the owner's risk and the owner agrees to defend, indemnify, and hold harmless The Engineer from all claims, damages, and expenses including attorney's fees arising out of such unauthorized reuse of The Engineer's instruments of service by the owner or others acting through the owner.
© 2026

Client:

FIFTH THIRD BANK

Project Number: 26302
Project Name:

WATSON BLVD.

2711 WATSON BOULEVARD
WARNER ROBINS, GA 31093

Sheet Title:


Wall Sections

Sheet Number:


S-603

RELEASED FOR CONSTRUCTION AND PERMIT

6/26/2026 12:52:29 PM

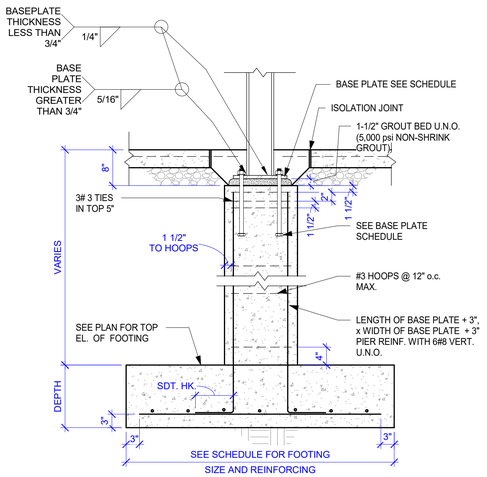


TYPICAL DETAIL OF STEEL COLUMN, PIER AND FOOTING WHERE FOOTINGS ARE MORE THAN 2'-0" BELOW FLOOR

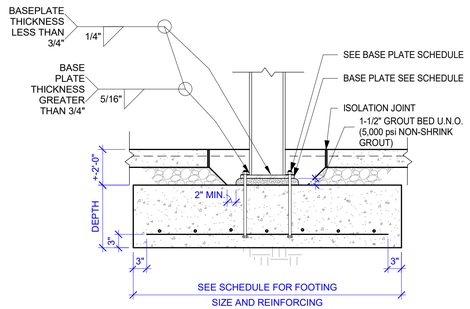

TYPICAL DETAIL OF STEEL COLUMN AND FOOTING WHERE FOOTING IS UP TO 2'-0" BELOW FLOOR


1 S-680 **Typical Steel Column Connection to Footing**

3/4" = 1'-0"

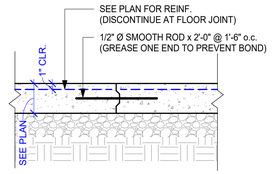


2 S-680 **Typical Detail of Construction Joint (C.J.)**

1" = 1'-0"

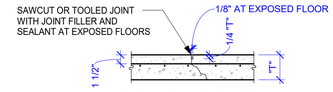


3 S-680 **Typical Detail of Saw-Cut Joint (S.C.J.)**

1" = 1'-0"

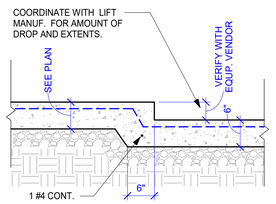


4 S-680 **Typical Detail at Parts Lift Slab**

3/4" = 1'-0"

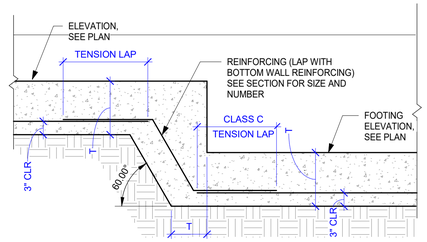

5 S-680 **Typical Step in Footing**


3/4" = 1'-0"

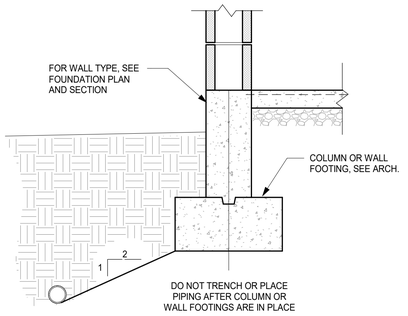


6 S-680 **Typical Detail of Trenches Near Footings**

1" = 1'-0"


INTERIOR SLAB ISOLATION JOINT

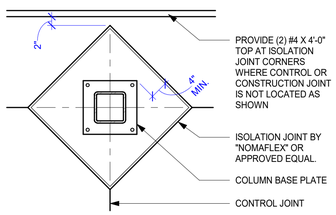


SLAB ISOLATION JOINT AT CORNER

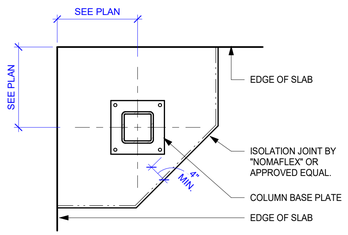


SLAB ISOLATION JOINT AT EDGE

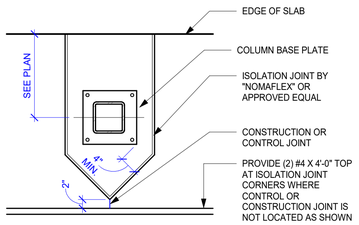

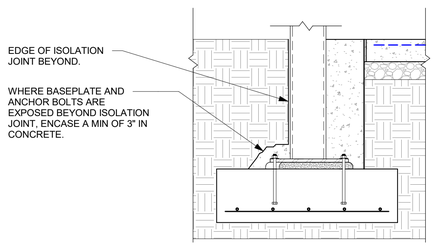

8 S-680 **Typical Detail of Slab Isolation Joints**

3/4" = 1'-0"

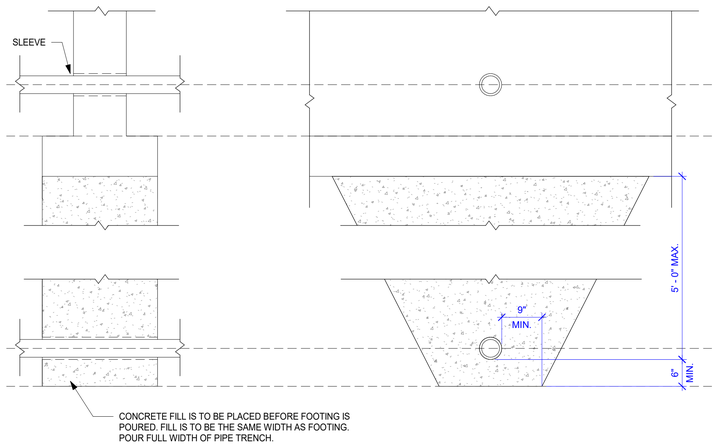

10 S-680 **Typical Detail at Pipe Penetration Through Wall**

3/4" = 1'-0"

6/26/2026 12:52:30 PM

PRAXIS3
100 Peachtree St NW
Suite 1450
Atlanta, GA 30303
404-875-4500 tel
404-876-8884 fax
www.praxis3.com

GEORGIA REGISTERED No. SE001277 STRUCTURAL ENGINEER MARK W. NANNIS

Copyright © 2026 Praxis3, LLC

All reports, plans, specifications, computer files, field data, notes and other documents and instruments prepared by Praxis3 shall retain all common law, statutory and other reserved rights, including copyright thereto.

This drawing may not be reproduced in whole or in part without written permission of Praxis3. It is to be returned upon request. Scales as stated are valid on the original drawings.

Rev	Date	Comments
1	07/02/2026	PERMIT SET

MARK NANNIS STRUCTURAL ENGINEERS
Mark Nannis Structural Engineers
2060 Buford Highway NE, Suite 106
Buford, GA 30518

All drawings, specifications, and other work product of Mark Nannis Structural Engineers (henceforth referred to as "The Engineer") for this project are instruments of service for this project only and shall remain the property of The Engineer whether the project is complete or not. Reuse of any of the instruments of service of The Engineer by the owner or extensions of this project without the written permission of The Engineer shall be at the owner's risk and the owner agrees to defend, indemnify, and hold harmless The Engineer from all claims, damages, and expenses including attorney's fees arising out of such unauthorized reuse of The Engineer's instruments of service by the owner or others acting through the owner.
© 2026

Client:

FIFTH THIRD BANK

Project Number: 26302
Project Name:

WATSON BLVD.

2711 WATSON BOULEVARD
WARNER ROBINS, GA 31093


Sheet Title:


Typical Details (Foundation)

Sheet Number:

S-680

RELEASED FOR CONSTRUCTION AND PERMIT

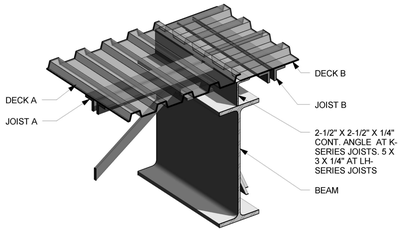


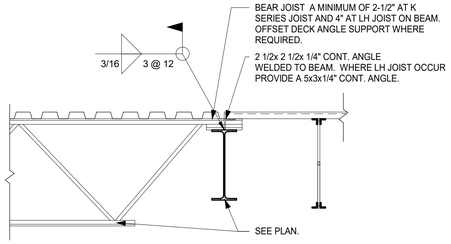


NOTE: WHERE DECK JOIST CHANGE DIRECTION OR, WHERE JOIST FRAME TO BEAM AT OTHER THAN 90 DEGREES.

2 S-681 Typical Detail Where Joist Changes Direction


3/4" = 1'-0"

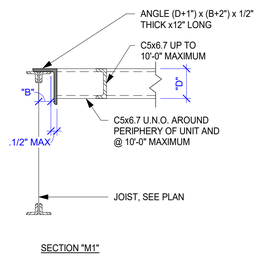

SECTION "M1"
(ONE SIDE)

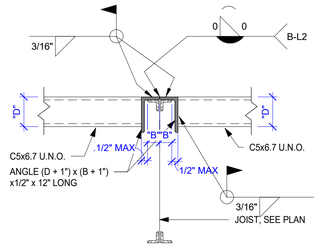

SECTION "M2"
(BOTH SIDES)

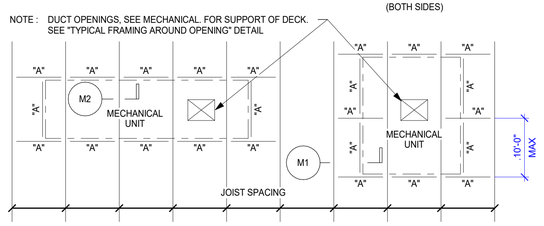


"A" : INDICATES C5x6.7


NOTE: FOR MECHANICAL UNIT CURB ATTACHMENT TO STRUCTURE AND TIE DOWN CONNECTION OF UNIT SEE MECHANICAL

3 S-681 Typical Framing for Mechanical Units Detail

1" = 1'-0"

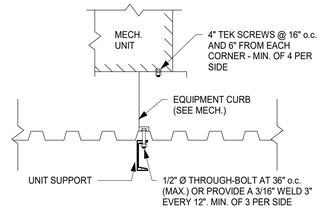


AT CURB OF MECHANICAL UNIT

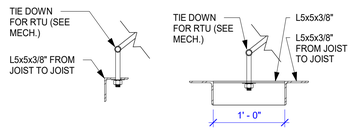

AT TIE-DOWN STRAPS FOR MECHANICAL UNIT

4 S-681 Typical Anchorage of Mechanical Units

1" = 1'-0"

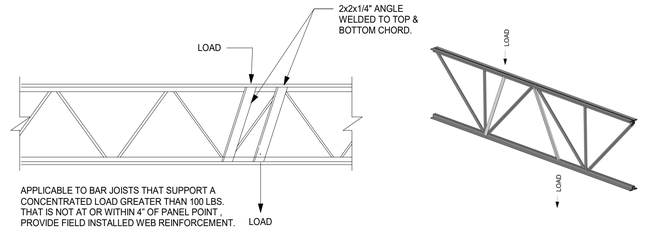


5 S-681 Typical Detail of Bar Joist Field Reinforcement at concentrated loads

1" = 1'-0"

7 S-681 Typical Connection of Tube Steel to Steel Columns

1" = 1'-0"

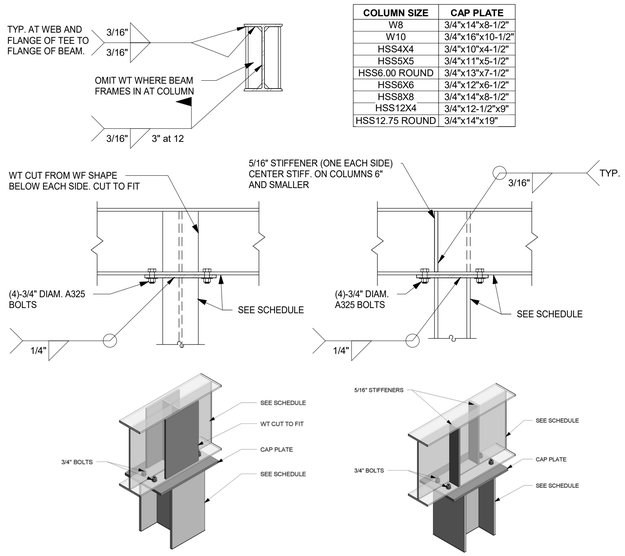


COLUMN SIZE	CAP PLATE
W8	3/4"x14"x8-1/2"
W10	3/4"x16"x10-1/2"
HSS4X4	3/4"x10"x4-1/2"
HSS5X5	3/4"x11"x5-1/2"
HSS6.00 ROUND	3/4"x13"x7-1/2"
HSS6X6	3/4"x12"x6-1/2"
HSS8X8	3/4"x14"x8-1/2"
HSS12X4	3/4"x12-1/2"x9"
HSS12.75 ROUND	3/4"x14"x19"

8 S-681 Typical Cap Plate Detail


1" = 1'-0"

*** INDICATED ON PLAN BY S.P. ***

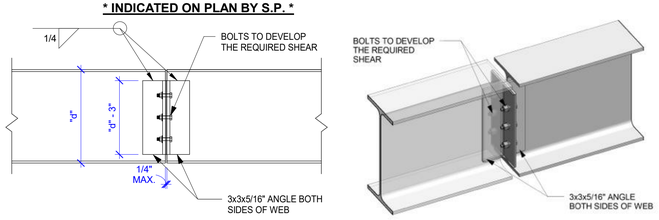

9 S-681 Typical Splice Point Detail

1" = 1'-0"

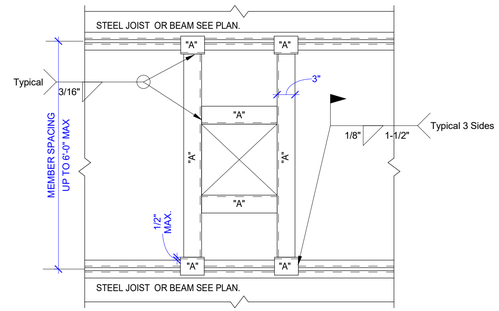

NOTE "A" : INDICATES ANGLE 4" x 3" x 1/4", LONG LEG DOWN. WHERE BEAM SPACING IS 6'-1" AND GREATER, PROVIDE A W6 x 9 FOR THE "A" MEMBERS SPANNING BETWEEN THE JOIST OR BEAMS.

NOTE : GENERAL CONTRACTOR COORDINATE ROOF OPENING REQUIREMENTS WITH MECHANICAL, ELECTRICAL AND PLUMBING PLANS.

NOTE : PROVIDE AT ALL ROOF DRAIN LOCATIONS

10 S-681 Typical Framing Around Roof Opening Detail

1" = 1'-0"

PRAXIS3

100 Peachtree St NW
Suite 1450
Atlanta, GA 30303

404-875-4500 tel
404-876-8884 fax
www.praxis3.com

GEORGIA REGISTERED No. SE001277 STRUCTURAL ENGINEER MARK W. NANNIS

Copyright © 2026 Praxis3, LLC

All reports, plans, specifications, computer files, field data, notes and other documents and instruments prepared by Praxis3 shall retain all common law, statutory and other reserved rights, including copyright thereto.

This drawing may not be reproduced in whole or in part without written permission of Praxis3. It is to be returned upon request. Scales as stated are valid on the original drawings.

Rev	Date	Comments
1	07/02/2026	PERMIT SET

MARK NANNIS STRUCTURAL ENGINEERS

Mark Nannis Structural Engineers
2060 Buford Highway NE, Suite 106
Buford, GA 30518

All drawings, specifications, and other work product of Mark Nannis Structural Engineers (henceforth referred to as "The Engineer") for this project are instruments of service for this project only and shall remain the property of The Engineer whether the project is complete or not. Reuse of any of the instruments of service of The Engineer by the owner or extensions of this project without the written permission of The Engineer shall be at the owner's risk and the owner agrees to defend, indemnify, and hold harmless The Engineer from all claims, damages, and expenses including attorney's fees arising out of such unauthorized reuse of The Engineer's instruments of service by the owner or others acting through the owner.
© 2026

Client:

FIFTH THIRD BANK

Project Number: 26302
Project Name:

WATSON BLVD.

2711 WATSON BOULEVARD
WARNER ROBINS, GA 31093

Sheet Title:


Typical Details (Steel)

Sheet Number:

S-681

RELEASED FOR CONSTRUCTION AND PERMIT

6/26/2026 12:52:32 PM

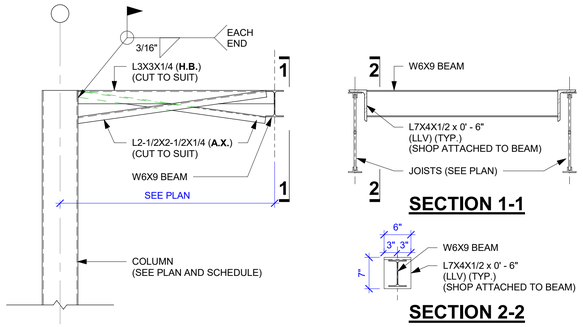


SECTION 1-1

SECTION 2-2


Typical Horizontal Brace (H.B.) and Additional X-Type Bridging (A.X.) at Column

1 / S-682

3/4" = 1'-0"

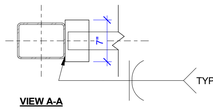


VIEW A-A

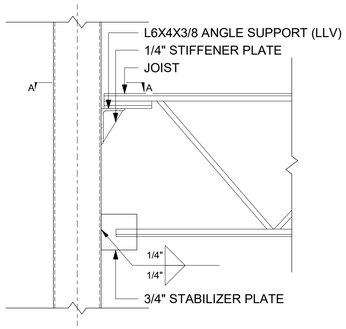

Joist-Column Connection (HSS)

2 / S-682


1" = 1'-0"

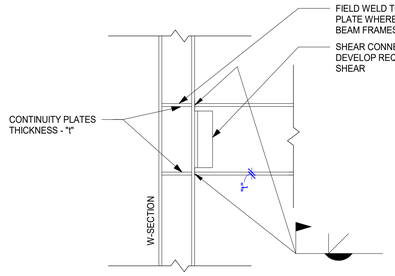


Typical Moment Connection of Steel Beam to Column

3 / S-682

1" = 1'-0"

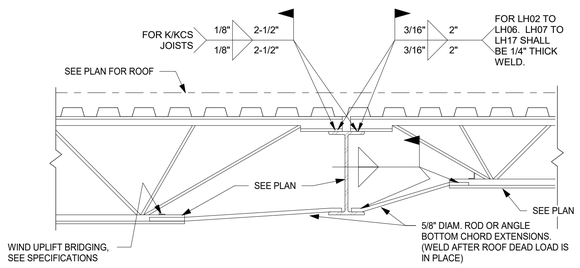

BEAM DETAIL AT JOIST CLOSEST TO BEAM MIDSPAN

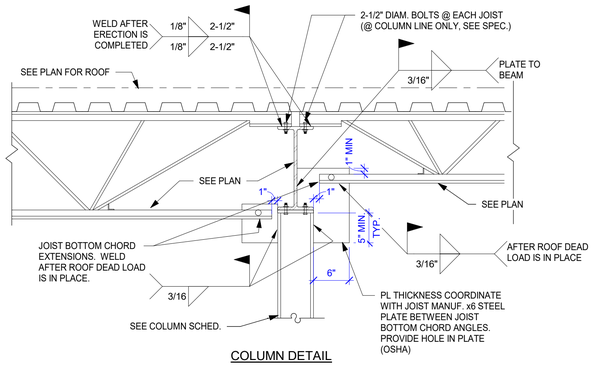


COLUMN DETAIL

Typical Detail of Bar Joist Roof Construction

4 / S-682

1" = 1'-0"

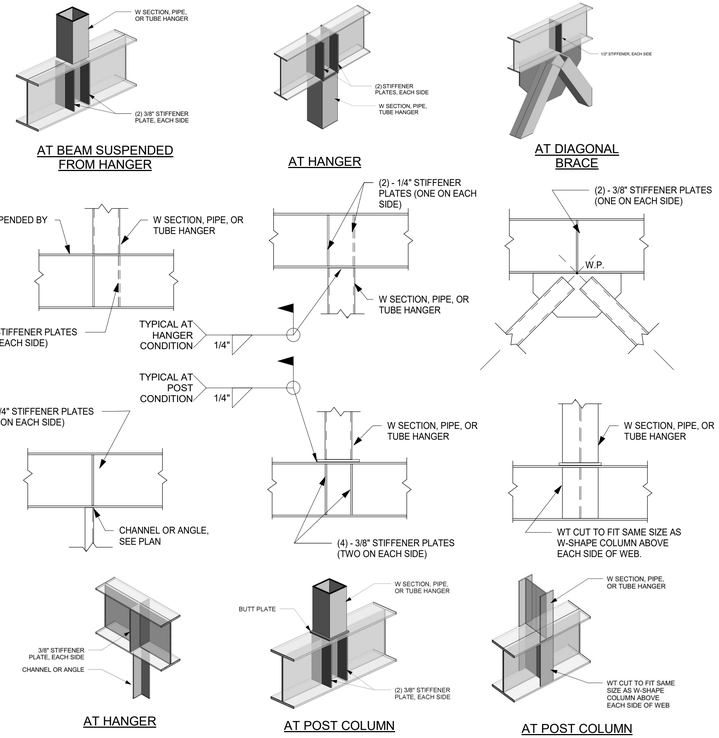

Typical Beam Stiffener at Steel Hangers or Steel Posts (U.N.O.)

5 / S-682

3/4" = 1'-0"

PRAXIS3

100 Peachtree St NW
Suite 1450
Atlanta, GA 30303

404-875-4500 tel
404-876-8884 fax
www.praxis3.com

GEORGIA REGISTERED No. SE001277 STRUCTURAL ENGINEER MARK W. NANNIS

Copyright © 2026 Praxis3, LLC

All reports, plans, specifications, computer files, field data, notes and other documents and instruments prepared by Praxis3 shall retain all common law, statutory and other reserved rights, including copyright thereto.

This drawing may not be reproduced in whole or in part without written permission of Praxis3. It is to be returned upon request. Scales as stated are valid on the original drawings.

Rev	Date	Comments
1	07/02/2026	PERMIT SET

MARK NANNIS STRUCTURAL ENGINEERS

Mark Nannis Structural Engineers
2060 Buford Highway NE, Suite 106
Buford, GA 30518

All drawings, specifications, and other work product of Mark Nannis Structural Engineers (henceforth referred to as "The Engineer") for this project are instruments of service for this project only and shall remain the property of The Engineer whether the project is complete or not. Reuse of any of the instruments of service of The Engineer by the owner or extensions of this project without the written permission of The Engineer shall be at the owner's risk and the owner agrees to defend, indemnify, and hold harmless The Engineer from all claims, damages, and expenses including attorney's fees arising out of such unauthorized reuse of The Engineer's instruments of service by the owner or others acting through the owner.
© 2026

Client:

FIFTH THIRD BANK

Project Number: 26302
Project Name:

WATSON BLVD.

2711 WATSON BOULEVARD
WARNER ROBINS, GA 31093

Sheet Title:


Typical Details (Steel)

Sheet Number:

S-682


RELEASED FOR CONSTRUCTION AND PERMIT

6/26/2026 12:52:33 PM

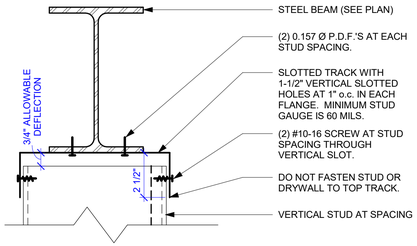


1 S-683 Metal Stud to Bottom of Beam (Slip Clip)

3" = 1'-0"

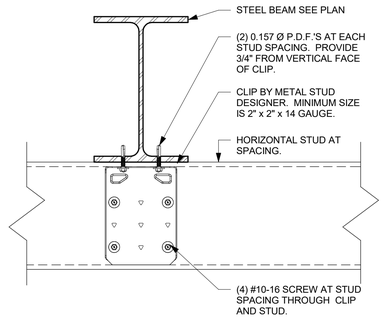


2 S-683 Metal Stud to Bottom of Beam

3" = 1'-0"

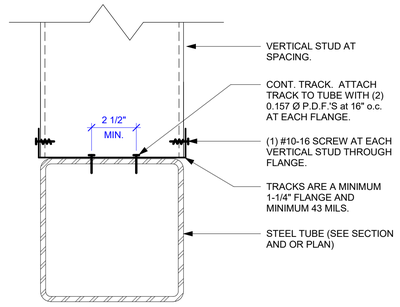


3 S-683 Metal Stud to Steel Tube (In-Line)

3" = 1'-0"

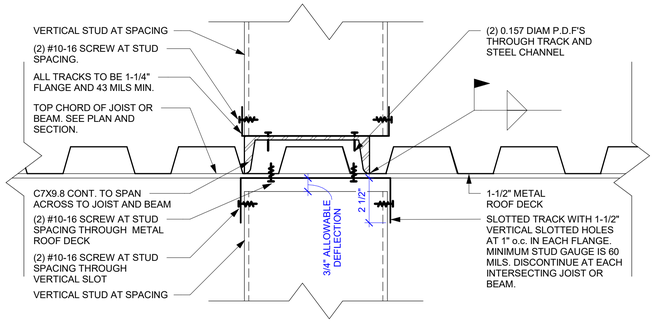


11 S-683 Metal Stud to Steel Deck (deck parallel)

3" = 1'-0"

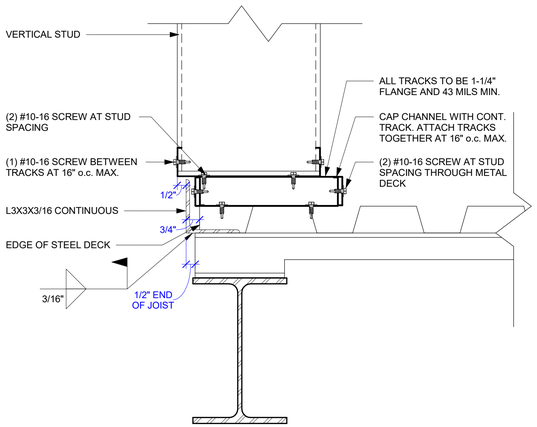

5 S-683 Metal Stud to Steel Deck Edge - Joist Bearing

3" = 1'-0"

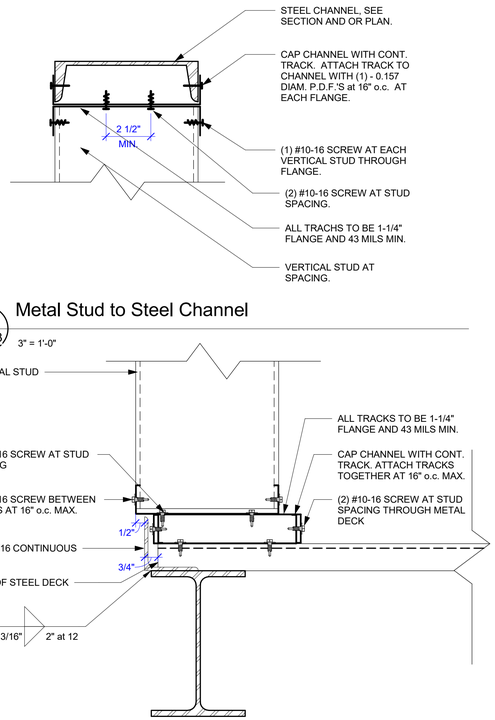

4 S-683 Metal Stud to Steel Channel


3" = 1'-0"

6 S-683 Metal Stud to Steel Deck Edge - Deck Bearing

3" = 1'-0"


7 S-683 Metal Stud Bypassing Roof - Joist Bearing on Beam (Fix Clip)

1 1/2" = 1'-0"

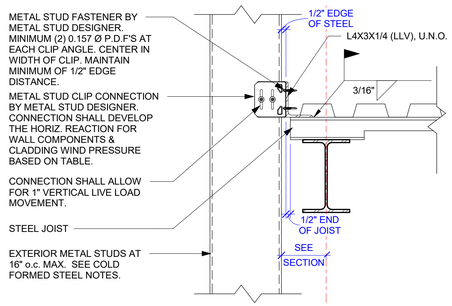


8 S-683 Metal Stud Bypassing Roof - Joist Bearing on Beam (Slip Clip)

1 1/2" = 1'-0"

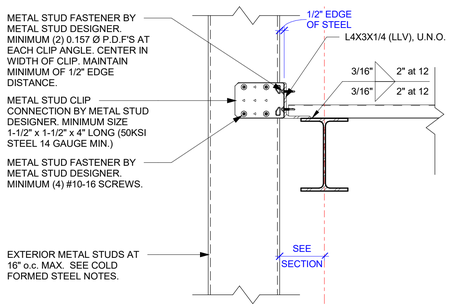

9 S-683 Metal Stud Bypassing Roof - Deck Bearing on Beam (Fix Clip)

1 1/2" = 1'-0"

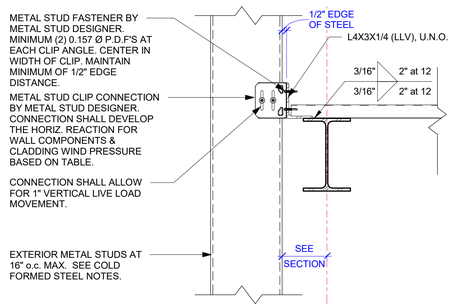

10 S-683 Metal Stud Bypassing Roof - Deck Bearing on Beam (Slip Clip)

1 1/2" = 1'-0"

PRAXIS3

100 Peachtree St NW
Suite 1450
Atlanta, GA 30303

404-875-4500 tel
404-876-8884 fax
www.praxis3.com

GEORGIA REGISTERED No. SE001277 STRUCTURAL ENGINEER MARK W. NANNIS

Copyright © 2026 Praxis3, LLC

All reports, plans, specifications, computer files, field data, notes and other documents and instruments prepared by Praxis3 shall retain all common law, statutory and other reserved rights, including copyright thereto.

This drawing may not be reproduced in whole or in part without written permission of Praxis3. It is to be returned upon request. Scales as stated are valid on the original drawings.

Rev	Date	Comments
1	07/02/2026	PERMIT SET

MARK NANNIS STRUCTURAL ENGINEERS

Mark Nannis Structural Engineers

2060 Buford Highway NE, Suite 106
Buford, GA 30518

All drawings, specifications, and other work product of Mark Nannis Structural Engineers (henceforth referred to as "The Engineer") for this project are instruments of service for this project only and shall remain the property of The Engineer whether the project is complete or not. Reuse of any of the instruments of service of The Engineer by the owner or extensions of this project without the written permission of The Engineer shall be at the owner's risk and the owner agrees to defend, indemnify, and hold harmless The Engineer from all claims, damages, and expenses including attorney's fees arising out of such unauthorized reuse of The Engineer's instruments of service by the owner or others acting through the owner.
© 2026

Client:

FIFTH THIRD BANK

Project Number: 26302
Project Name:

WATSON BLVD.

2711 WATSON BOULEVARD
WARNER ROBINS, GA 31093

Sheet Title:


Enlarged Steel Details

Sheet Number:

S-683

RELEASED FOR CONSTRUCTION AND PERMIT

6/26/2026 12:52:34 PM

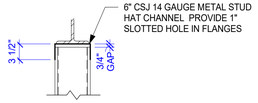


2 S-685


Typical Stud-to-Beam Slip Connection

3/4" = 1'-0"

JAMB AND HEADER SCHEDULED (EXTERIOR)		
SPAN (FT)	HEADER	JAMB STUDS
≤ 4	(2) 60S200-43	1
6	(2) 60S200-43	2
8	(2) 725S200-54	2
10	(2) 800s200-68	3

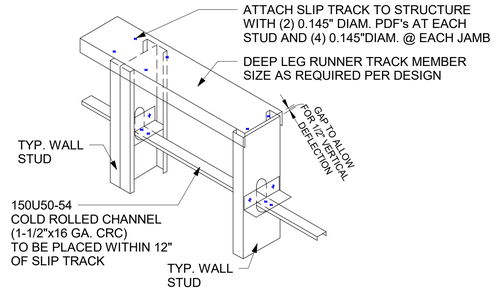


SLIP TRACK DETAIL

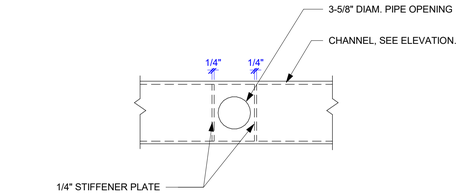


4 S-685

Channel Penetration Detail


1 1/2" = 1'-0"

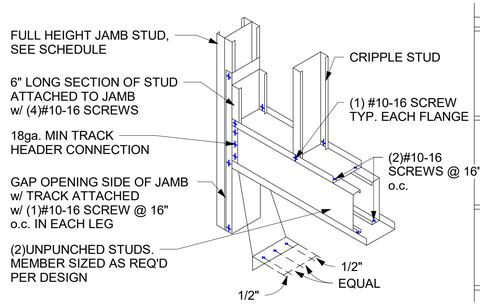


HEADER DETAIL (A)

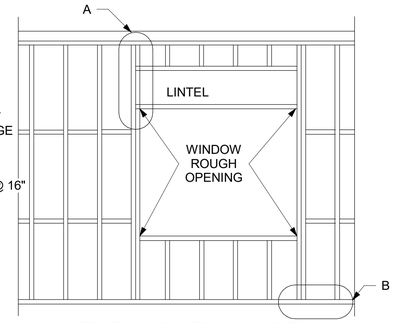

TYP LIGHT GAUGE STEEL WALL FRAMING

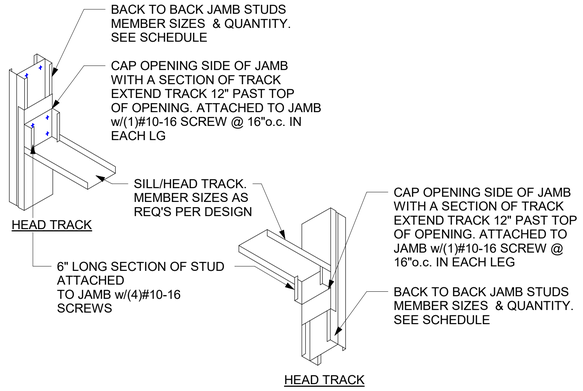


SILL HEAD TRACK CONNECTION

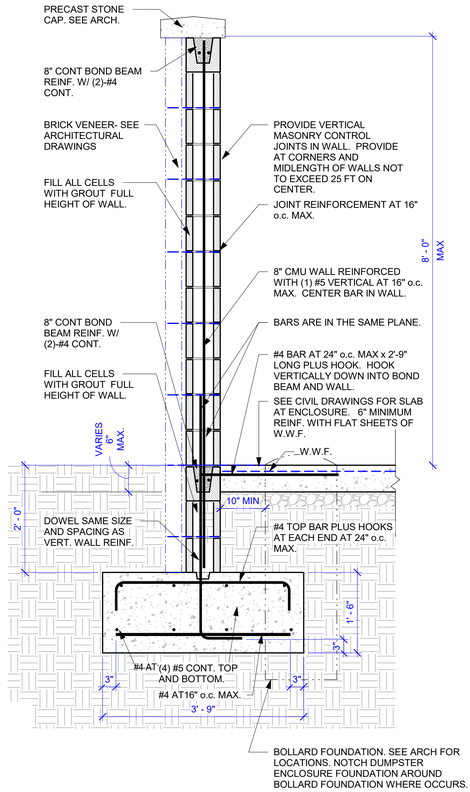

3 S-685

Typical Detail of Dumpster Enclosure

3/4" = 1'-0"

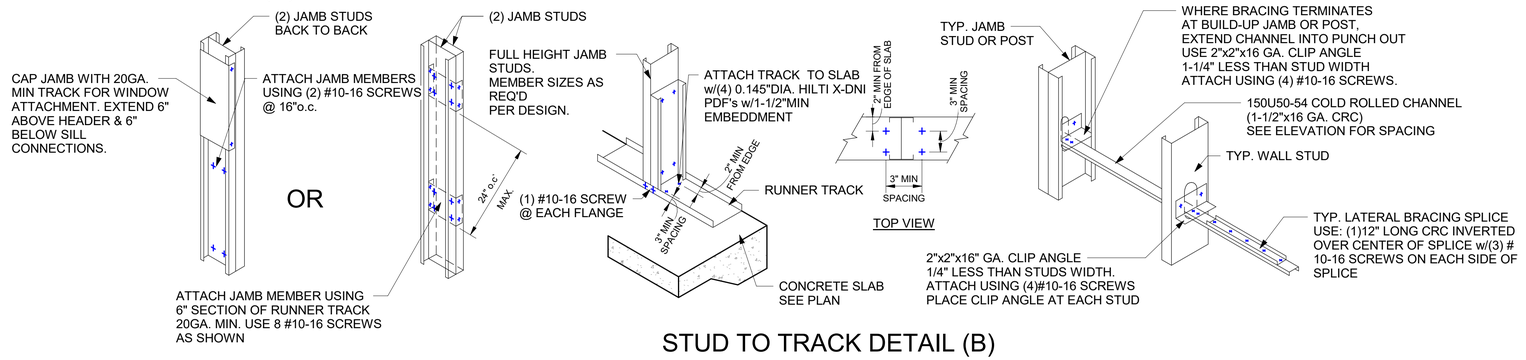

TIED JAMB STUDS

STUD TO TRACK DETAIL (B)

BRIDGING DETAIL

1 S-685

Typical Metal Stud Detail

12" = 1'-0"

PRAXIS3

100 Peachtree St NW
Suite 1450
Atlanta, GA 30303

404-875-4500 tel
404-876-8884 fax
www.praxis3.com

GEORGIA REGISTERED No. SE001277 STRUCTURAL ENGINEER MARK W. NANNIS

Copyright © 2026 Praxis3, LLC

All reports, plans, specifications, computer files, field data, notes and other documents and instruments prepared by Praxis3 shall retain all common law, statutory and other reserved rights, including copyright thereto.

This drawing may not be reproduced in whole or in part without written permission of Praxis3. It is to be returned upon request. Scales as stated are valid on the original drawings.

Rev	Date	Comments
1	07/02/2026	PERMIT SET

MARK NANNIS STRUCTURAL ENGINEERS

Mark Nannis Structural Engineers
2060 Buford Highway NE, Suite 106
Buford, GA 30518

All drawings, specifications, and other work product of Mark Nannis Structural Engineers (henceforth referred to as "The Engineer") for this project are instruments of service for this project only and shall remain the property of The Engineer whether the project is complete or not. Reuse of any of the instruments of service of The Engineer by the owner or extensions of this project without the written permission of The Engineer shall be at the owner's risk and the owner agrees to defend, indemnify, and hold harmless The Engineer from all claims, damages, and expenses including attorney's fees arising out of such unauthorized reuse of The Engineer's instruments of service by the owner or others acting through the owner.
© 2026

Client:

FIFTH THIRD BANK

Project Number: 26302
Project Name:

WATSON BLVD.

2711 WATSON BOULEVARD
WARNER ROBINS, GA 31093

Sheet Title:

Typical Details (Misc)

Sheet Number:

S-685

RELEASED FOR CONSTRUCTION AND PERMIT

6/26/2026 12:52:34 PM