
CLERK OF THE SUPERIOR COURT RECORDING INFORMATION


ABBREVIATION LEGEND

P.O.C.	POINT OF COMMENCEMENT
RBF	REBAR FOUND
CTPF	CRIMP TOP PIPE FOUND
SSE	SANITARY SEWER EASEMENT
CMP	CORRUGATED METAL PIPE
HDPE	HIGH DENSITY POLYETHYLENE PIPE
RCP	REINFORCED CONCRETE PIPE
CI	CURB INLET
I.E.	INVERT ELEVATION
BW	BOTTOM OF WALL
FFE	FINISHED FLOOR ELEVATION
N/F	NOW OR FORMERLY
CLF	CHAIN LINK FENCE
P.O.B.	POINT OF BEGINNING
R/W	RIGHT-OF-WAY
OTPF	OPEN TOP PIPE FOUND
AE	ACCESS EASEMENT
DE	DRAINAGE EASEMENT
DIP	DUCTILE IRON PIPE
PVC	POLYVINYL CHLORIDE PIPE
TW	TOP OF WALL
BSL	BUILDING SETBACK LINE
C&G	CURB AND GUTTER
MAGNS	MAG NAIL SET
MAGNF	MAG NAIL FOUND

SYMBOL LEGEND

	AIR CONDITIONER UNIT
CBX	CABLE BOX
	JUNCTION BOX
	HOOD AND GRATE INLET
	SANITARY SEWER CLEANOUT
CWSP	CROSS WALK SIGNAL POLE
	GRATE INLET
	CONCRETE MONUMENT FOUND
EBX	ELECTRICAL BOX
EM	ELECTRIC METER
	FLARED END SECTION
	FIRE HYDRANT
FOMKR	FIBER OPTIC MARKER
	SINGLE WING CATCH BASIN
GM	GAS METER
	EXISTING GUY POLE
	EXISTING GREASE TRAP
	ADA PARKING
	HEADWALL
	IRRIGATION CONTROL VALVE
	IRON PIN FOUND (TYPE NOTED)
	IRON PIN SET
	LIGHT POLE
	LANDSCAPE LIGHT
	OUTLET CONTROL STRUCTURE
PBX	UG POWER TRANSFORMER
PM	POWER METER
	SANITARY SEWER MANHOLE
	SINGLE WING CATCH BASIN
	STREET SIGN
	PAINTED TRAFFIC MARKING
TBX	TELEPHONE BOX
T	TELEPHONE MANHOLE
	TELEPHONE PEDESTAL
TSBX	TRAFFIC SIGNAL BOX
TSHH	TRAFFIC SIGNAL HANDHOLE
TSP	TRAFFIC SIGNAL POLE
TP	CABLE PEDESTAL
GMKR	GAS MARKER
	UTILITY POLE
WM	WATER METER
	YARD INLET
	DOUBLE WING CATCH BASIN
10	PARKING COUNT

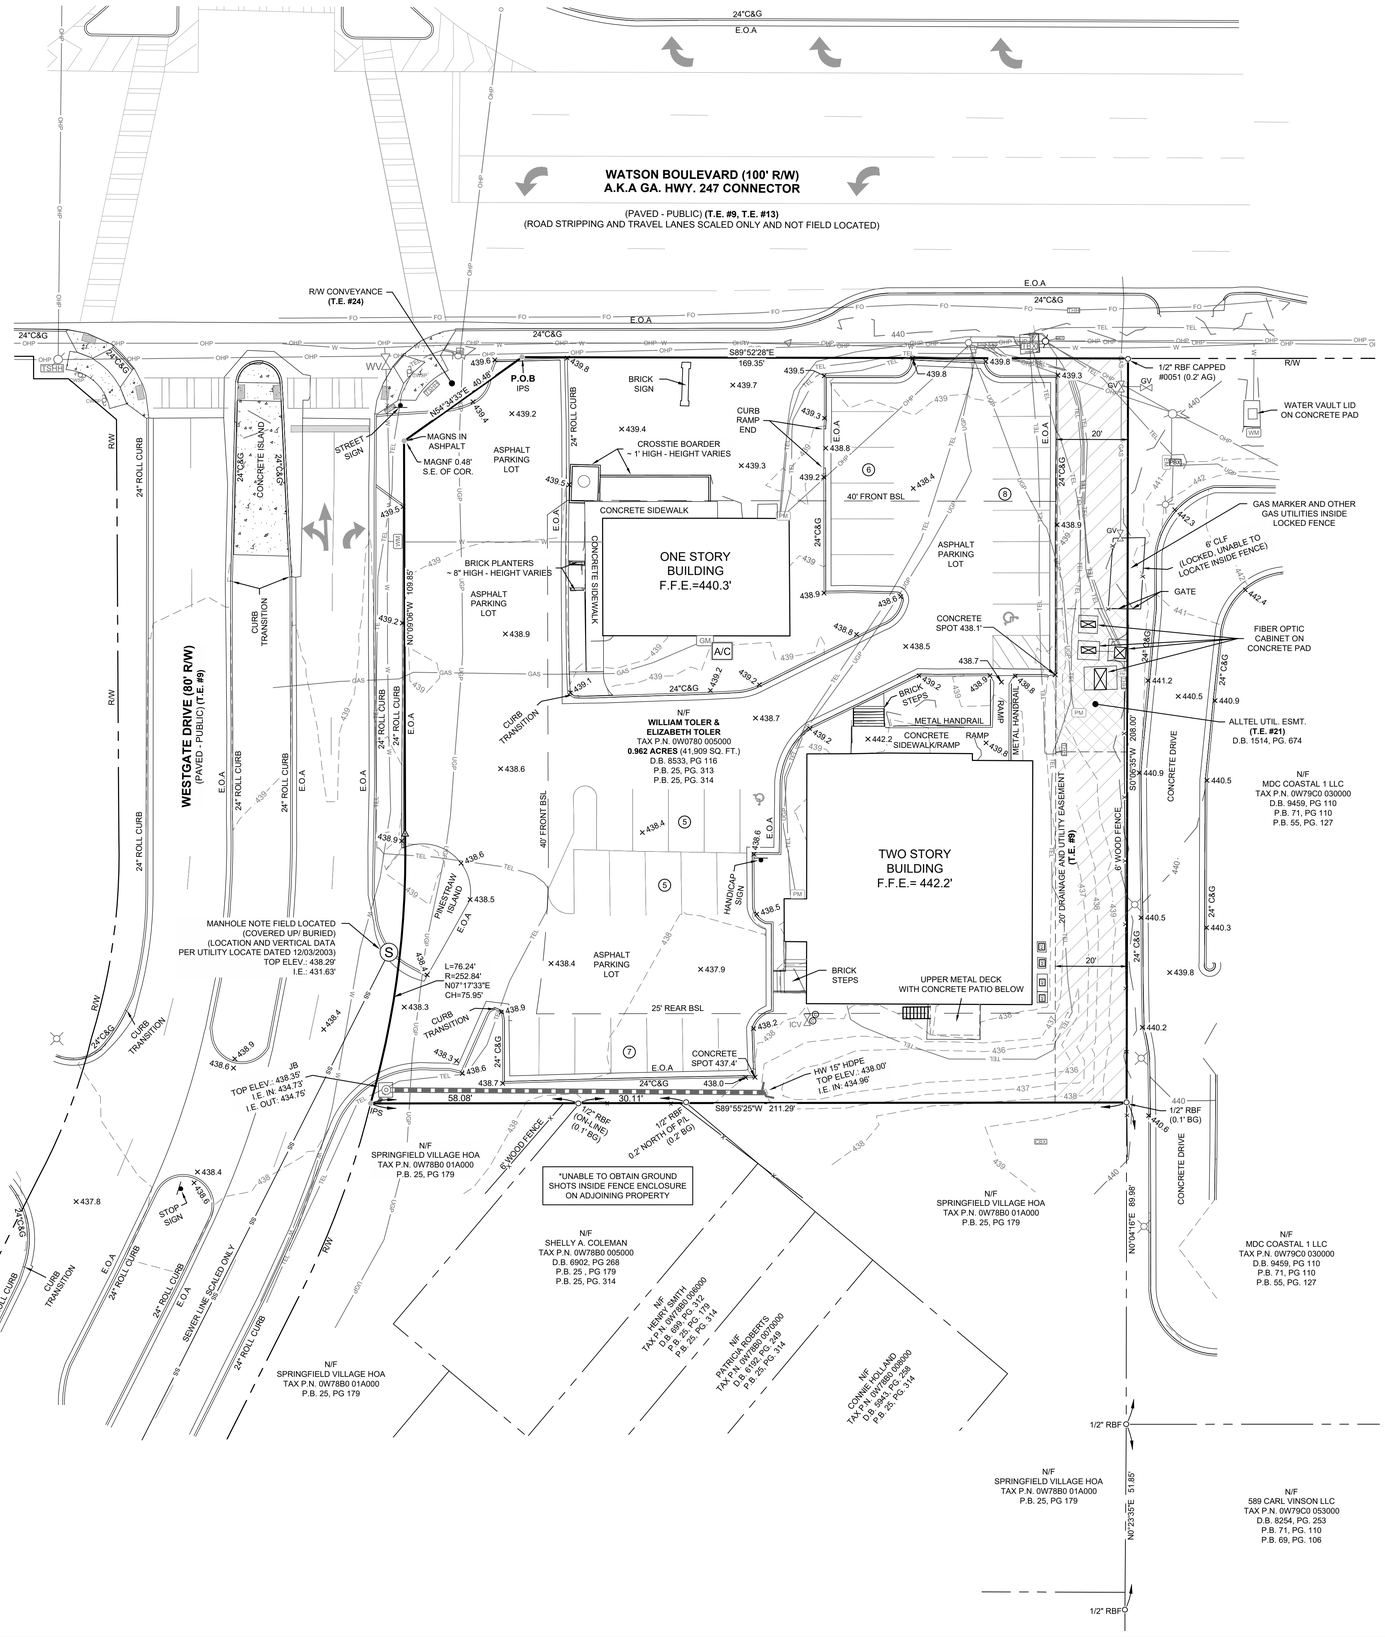

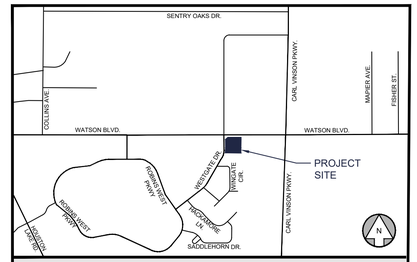

LOCATION MAP

IMAGE OBTAINED FROM "© GOOGLE MAPS"

LINE LEGEND

	STORM SEWER
FO	FIBER OPTIC
OHP	OVERHEAD POWER
	MAJOR CONTOUR
X X	FENCE
	PROPERTY LINE
	ADJOINING LOT LINE
SS	SANITARY SEWER
W W	WATER MAIN
UGP	UNDERGROUND POWER
GAS	GAS
	MINOR CONTOUR
	LAND LOT LINE
	RIGHT OF WAY
	EASEMENT
TEL	TELECOMMUNICATIONS

ALTA/NSPS LAND TITLE SURVEY CERTIFICATION:

TO: FIFTH THIRD BANK, NATIONAL ASSOCIATION; PRAXIS3; COMMONWEALTH LAND TITLE INSURANCE COMPANY:

THIS IS TO CERTIFY THAT THIS MAP OR PLAT AND THE SURVEY ON WHICH IT IS BASED WERE MADE IN ACCORDANCE WITH THE 2026 MINIMUM STANDARD DETAIL REQUIREMENTS FOR ALTA/NSPS LAND TITLE SURVEYS, JOINTLY ESTABLISHED AND ADOPTED BY ALTA AND NSPS, AND INCLUDES ITEMS 1, 2, 3, 4, 5, 6(a), 8, 11(b), 13, 16, 17 OF TABLE A THEREOF.
THE FIELDWORK WAS COMPLETED ON 4/17/26.
DATE OF PLAT OR MAP: 5/8/2026

JASON A. HOPKINS / GEORGIA LAND SURVEYOR No. 3215 DATE: 5/8/2026

SURVEYOR'S CERTIFICATION

(iii) THIS PLAT IS A RETRACEMENT OF AN EXISTING PARCEL OR PARCELS OF LAND AND DOES NOT SUBDIVIDE OR CREATE A NEW PARCEL OR MAKE ANY CHANGES TO ANY REAL PROPERTY BOUNDARIES. THE RECORDING INFORMATION OF THE DOCUMENTS, MAPS, PLATS, OR OTHER INSTRUMENTS WHICH CREATED THE PARCEL OR PARCELS ARE STATED HEREON. **RECORDATION OF THIS PLAT DOES NOT IMPLY APPROVAL OF ANY LOCAL JURISDICTION, AVAILABILITY OF PERMITS, COMPLIANCE WITH LOCAL REGULATIONS OR REQUIREMENTS, OR SUITABILITY FOR ANY USE OR PURPOSE OF THE LAND.** FURTHERMORE, THE UNDERSIGNED LAND SURVEYOR CERTIFIES THAT THIS PLAT COMPLIES WITH THE MINIMUM TECHNICAL STANDARDS FOR PROPERTY SURVEYS IN GEORGIA AS SET FORTH IN THE RULES AND REGULATIONS OF THE GEORGIA BOARD OF REGISTRATION FOR PROFESSIONAL ENGINEERS AND LAND SURVEYORS AND AS SET FORTH IN O.C.G.A. SECTION 15-6-67.

GEORGIA PROFESSIONAL 3215 LAND SURVEYOR JASON A. HOPKINS

AS SURVEYOR FOR GASKINS + LECRAW, INC.

JASON A. HOPKINS GEORGIA PLS No. 3215 DATE: 05/08/2026

PREPARED IN THE OFFICE OF:

GASKINS +LECRAW

© 2026 GASKINS + LECRAW, INC.
24 JACKSON STREET
NEWNAN, GA 30265
PHONE - 770.253.5195
www.gaskinslecraw.com

LSF001371

REVISIONS:

REV. #	DATE	DRAWN BY:	CHECKED BY:

ALTA/NSPS LAND TITLE SURVEY FOR
FIFTH THIRD BANK, NATIONAL ASSOCIATION; PRAXIS3; COMMONWEALTH LAND TITLE INSURANCE COMPANY

PROJECT LOCATION
2711 WATSON BLVD.
TAX P.N. 0W0780 005000
LAND LOT 121, 5 DISTRICT
CITY OF WARNER ROBINS, HOUSTON COUNTY, GEORGIA

CALL BEFORE YOU DIG

811 Know what's below. Call before you dig.

SCALE & NORTH ARROW:

GRID NORTH, GEORGIA WEST ZONE
0' 10' 20' 40'
SCALE: 1" = 20'

SURVEY INFO:

DRAWN BY:	JJV
REVIEWED BY:	JAH
JOB #:	75670007.000
DATE:	5/8/2026

SHEET NUMBER

2 OF 2

This document, together with the concepts and designs presented herein, as an instrument of service, is intended only for the specific purpose and client for which it was prepared. Reuse of and improper reliance on this document without written authorization and adaptation by Gaskins + LeCraw, Inc. shall be without liability to Gaskins + LeCraw, Inc. Copyright Gaskins + LeCraw, Inc., 2026

Drawing name: C:\Users\nstaat\Gaskins+LeCraw Dropbox\Shared Folders\Survey_Boundary\Houston\5th District\05_012175670007.000 - WARNER ROBINS - FIFTH THIRD BANK\BND\DWG\Fifth Third ALTA-TOPO _ Warner Robins.dwg 24X36 BND ALTA BND TOPO May 26, 2026 8:18am by: nstaat