CLERK OF THE SUPERIOR COURT RECORDING INFORMATION

SCHEDULE B, PART II - EXCEPTIONS

COMMONWEALTH LAND TITLE INSURANCE COMPANY
COMMITMENT NUMBER: CW 18-25-0846
COMMITMENT DATE: DECEMBER 8, 2025 AT 12:00AM

9. ALL MATTERS SHOWN ON PLAT RECORDED IN PLAT BOOK 25, PAGE 314 , HOUSTON COUNTY, GEORGIA RECORDS.

   (ALL MATTERS SHOWN AFFECTING SUBJECT PROPERTY)

10. ALL MATTERS SHOWN ON PLAT RECORDED IN PLAT BOOK 25, PAGE 179 , AFORESAID RECORDS.

    (DOES NOT AFFECT SUBJECT PROPERTY, PLAT SUPERSEDED BY PLAT BOOK 25, PAGE 314)

11. ALL MATTERS SHOWN ON PLAT RECORDED IN PLAT BOOK 15, PAGE 209 , AFORESAID RECORDS.

    (SUBJECT PROPERTY IS A PORTION OF PARCEL "C")

12. ALL MATTERS SHOWN ON PLAT RECORDED IN PLAT BOOK 1, PAGE 248 , AFORESAID RECORDS.

    (SUBJECT PROPERTY IS A PORTION OF TRACT 4)

13. RURAL POST ROADS RIGHT OF WAY DEED FROM THURSTON H. TRUEWORTHY TO HOUSTON COUNTY, DATED OCTOBER 3, 1949, FILED FOR RECORD JULY 27, 1950, RECORDED IN DEED BOOK 69, PAGE 84 , AFORESAID RECORDS.

    (APPEARS TO BE THE ORIGINAL RIGHT OF WAY DEDICATION OF WATSON BLVD. FROM THE PARENT TRACT OF THE SUBJECT PROPERTY, RIGHT OF WAY DEDICATION PLANS NOT PROVIDED IN EXHIBIT B, PART II - SPECIAL EXCEPTIONS RECORD DOCUMENTS, AND WOULD BE NEEDED TO CONFIRM)

14. RIGHT OF WAY EASEMENT FROM MRS. LOUISE V. TRUEWORTHY TO FLINT ELECTRIC MEMBERSHIP CORPORATION, DATED JUNE 28,1971, FILED FOR RECORD JUNE 30, 1971, RECORDED IN DEED BOOK 374, PAGE 360 , AFORESAID RECORDS.

    (MAY AFFECT SUBJECT PROPERTY, VAGUE DESCRIPTION, PLAT REFERENCED IN DESCRIPTION NOT INCLUDED IN PROVIDED EXHIBIT B, PART II - SPECIAL EXCPETIONS RECORD DOCUMENTS, UNABLE TO PLOT)

15. INTENTIONALLY DELETED

16. RIGHT OF WAY EASEMENT BY AND BETWEEN SECURITY SERVICES, AND FLINT ELECTRIC MEMBERSHIP CORPORATION, DATED SEPTEMBER 16, 1976, FILED FOR RECORD NOVEMBER 16, 1976, RECORDED IN DEED BOOK 487, PAGE 105 , AFORESAID RECORDS.

    (MAY AFFECT SUBJECT PROPERTY, VAGUE DESCRIPTION, UNABLE TO PLOT)

17. EASEMENT FROM GEORGIA ASSOCIATED SERVICES, INC., AND MID-CONTINENT TELEPHONE CORPORATION, DATED NOVEMBER 17, 1982, FILED FOR RECORD NOVEMBER 23, 1982, RECORDED IN DEED BOOK 618, PAGE 727, AFORESAID RECORDS.

    (MAY AFFECT SUBJECT PROPERTY, VAGUE DESCRIPTION, UNABLE TO PLOT)

18. EASEMENT FROM PURCHASER OF LOT FROM DEVELOPER OF URD FACILITIES BETWEEN GEORGIA ASSOCIATED SERVICES, INC., TO FLINT ELECTRIC MEMBERSHIP CORPORATION, DATED OCTOBER 26, 1982, FILED FOR RECORD MARCH 24, 1983, RECORDED IN DEED BOOK 625, PAGE 367 , AFORESAID RECORDS.

    (DOES NOT APPEAR TO AFFECT SUBJECT PROPERTY, PLAT REFERENCED IN DESCRIPTION NOT INCLUDED IN PROVIDED EXHIBIT B, PART II - SPECIAL EXCEPTIONS RECORD DOCUMENTS, UNABLE TO PLOT)

19. DEPARTMENT OF TRANSPORTATION RIGHT OF WAY DEED FROM SECURITY SERVICES, INC., NKA GEORGIA ASSOCIATED SERVICES, INC., AND HOUSTON COUNTY, DATED JULY 17, 1985, FILED FOR RECORD JULY 23, 1985 AT 10:17 A.M., RECORDED IN DEED BOOK 690, PAGE 89 , AFORESAID RECORDS.

    (DOES NOT AFFECT SUBJECT PROPERTY)

20. DEPARTMENT OF TRANSPORTATION CONVEYANCE OF ACCESS RIGHTS BY AND BETWEEN HOUSTON COUNTY AND SECURITY SERVICES, INC., NKA GEORGIA ASSOCIATED SERVICES, INC., DATED JULY 17, 1985, FILED FOR RECORD AUGUST 27, 1985 AT 10:49 A.M., RECORDED IN DEED BOOK 693, PAGE 343 , AFORESAID RECORDS.

    (DOES NOT TO AFFECT SUBJECT PROPERTY)

21. EASEMENT FROM WILLIAM TOLER TO ALLTEL GEORGIA COMMUNICATIONS CORPORATION, DATED FEBRUARY 29, 2000, FILED FOR RECORD MARCH 3, 2000 AT 11:16 A.M., RECORDED IN DEED BOOK 1514, PAGE 671 , AFORESAID RECORDS.

    (AFFECTS SUBJECT PROPERTY AS SHOWN)

22. QUITCLAIM DEED BETWEEN WILLIAM TOLER, AND JOE E. ROBINSON AND THIRZA L. ROBINSON, DATED MARCH 1, 2000, FILED FOR RECORD MARCH 7, 2000 AT 10:15 A.M., RECORDED IN DEED BOOK 1515, PAGE 515 , AFORESAID RECORDS.

    (AFFECTS SUBJECT PROPERTY, RELEASES ANY INTEREST SUBJECT PROPERTY MAY HAVE IN ADJOINING TRACT SSF-1 AS SHOWN IN PLAT BOOK 55, PAGE 127, UNABLE TO BE PLOTTED)

23. ACCESS EASEMENT FROM WILLIAM TOLER TO ALLTEL GEORGIA COMMUNICATIONS CORPORATION, DATED APRIL 25, 2000, FILED FOR RECORD APRIL 25, 2000 AT 4:24 P.M., RECORDED IN DEED BOOK 1526, PAGE 506 , AFORESAID RECORDS.

    (AFFECTS SUBJECT PROPERTY, BLANKET IN NATURE, PROVIDES ACCESS TO EXISTING ACCESS USED BY SUBJECT PROPERTY TO SERVICE EQUIPMENT, UNABLE TO BE PLOTTED)

24. RIGHT OF WAY DEED FROM WILLIAM TOLER TO DEPARTMENT OF TRANSPORTATION, DATED SEPTEMBER 23, 2009, FILED FOR RECORD OCTOBER 22, 2009 AT 1:44 P.M., RECORDED IN DEED BOOK 5074, PAGE 283 , AFORESAID RECORDS.

    (AFFECTS SUBJECT PROPERTY AS SHOWN)

ALTA/NSPS LAND TITLE SURVEY - TABLE "A" NOTES:

1. MONUMENTS PLACED OR FOUND AS SHOWN ON SURVEY.
2. ADDRESS OF PROPERTY: 2711 WATSON BLVD, WARNER ROBINS, GA, 31093
   (SOURCE OF INFORMATION: QPUBLIC.NET HOUSTON COUNTY BOARD OF ASSESSORS)
3. FLOOD ZONE CLASSIFICATION **DESCRIBED UNDER GENERAL NOTE C.**
4. GROSS LAND AREA **SHOWN ON SURVEY**.
5. VERTICAL RELIEF WITH THE SOURCE OF INFORMATION (E.G., GROUND SURVEY, AERIAL MAP), CONTOUR INTERVAL, DATUM, WITH ORIGINATING BENCHMARK, WHEN APPROPRIATE. **(AS SHOWN ON SURVEY, SEE TOPOGRAPHIC DATA NOTES)**
6. (A) NO ZONING REPORT PROVIDED TO SURVEYOR. CURRENT ZONING CLASSIFICATION **SHOWN UNDER GENERAL NOTE F**
8. SUBSTANTIAL FEATURES OBSERVED IN THE PROCESS OF CONDUCTING THE FIELDWORK (IN ADDITION TO THE IMPROVEMENTS AND FEATURES REQUIRED PURSUANT TO SECTION 5 ABOVE) (E.G., PARKING LOTS, BILLBOARDS, SIGNS, SWIMMING POOLS, LANDSCAPED AREAS, SUBSTANTIAL AREAS OF REFUSE). **(AS SHOWN ON SURVEY)**
11. EVIDENCE OF UNDERGROUND UTILITIES EXISTING ON OR SERVING THE SURVEYED PROPERTY (IN ADDITION TO THE OBSERVED EVIDENCE OF UTILITIES REQUIRED PURSUANT TO SECTION 5.E.IV.) AS DETERMINED BY:
    (B) UNDERGROUND UTILITIES SHOWN HEREON ARE BASED ON SUE LEVEL B PAINT MARKINGS BY GROUNDHAWK ON 04-13-2026 AND WERE LOCATED AT THE TIME OF FIELD SURVEY. OTHER NON-METALLIC UTILITIES WITHOUT TRACER WIRE AND/OR OTHER BURIED STRUCTURES MAY EXIST ON THE PROPERTY.
13. NAMES OF ADJOINING OWNERS ACCORDING TO CURRENT TAX RECORDS ARE **SHOWN FROM QPUBLIC.NET HOUSTON COUNTY BOARD OF ASSESSORS**
16. NO EVIDENCE OF RECENT EARTH MOVING WORK, BUILDING CONSTRUCTION OR BUILDING ADDITIONS OBSERVED IN THE PROCESS OF CONDUCTING THE FIELD WORK.
17. NO PROPOSED CHANGES IN STREET RIGHT-OF-WAY LINES RECEIVED BY SURVEYOR. NO EVIDENCE OF RECENT STREET OR SIDEWALK CONSTRUCTION OR REPAIRS OBSERVED AT TIME OF SURVEY.

GENERAL NOTES:

A. PROPERTY ADDRESS: 2711 WATSON BLVD., WARNER ROBINS, GA 31093

B. TAX PARCEL ID: 0W0780-005000
   (SOURCE OF INFORMATION: QPUBLIC.NET HOUSTON COUNTY BOARD OF ASSESSORS)

C. THIS PARCEL OF LAND IS NOT IN THE 100 YEAR FLOODPLAIN ACCORDING TO F.E.M.A. FLOOD INFORMATION RATE MAP. COMMUNITY NUMBER: 130111, MAP NUMBER:13153C0085E, DATED: 9/28/07.

D. UNDERGROUND UTILITIES SHOWN HEREON ARE BASED ON SUE LEVEL B PAINT MARKINGS BY GROUND HAWK ON 04-13-2026 AND WERE LOCATED AT TIME OF FIELD SURVEY. OTHER NON-METALLIC UTILITIES WITHOUT TRACER WIRE AND/OR OTHER BURIED STRUCTURES MAY EXIST ON THE PROPERTY.

E. IT IS THE RECOMMENDATION OF GASKINS + LECRAW TO HAVE EASEMENTS AND RIGHTS-OF-WAY MARKED AND VERIFIED BY THE APPROPRIATE UTILITY OWNER, ROAD JURISDICTION OR RAILROAD PRIOR TO ANY CONSTRUCTION NEAR SAID EASEMENT OR RIGHT-OF-WAY. SOURCE OF INFORMATION USED TO ESTABLISH EASEMENTS AND RIGHTS-OF-WAY REFERENCED HEREON, IF PROVIDED BY CLIENT. SURVEYED PROPERTY IS SUBJECT TO COVENANTS, EASEMENTS, AND RESTRICTIONS OF RECORD THAT MAY NOT BE SHOWN HEREON.

F. CURRENT ZONING: C2 (GENERAL COMMERCIAL)
   ZONING CLASSIFICATION IS BASED ON: CITY OF WARNER ROBINS ZONING MAP

G. SETBACKS: FRONT - 40 FEET
   BACK - 25 FEET
   SIDE - 0 FEET (UNLESS ABUTTING RESIDENTIAL DISTRICT AND THEN NOT LESS THAN 25 FEET)
   SOURCE OF SETBACK INFORMATION: MUNICODE.COM/ WARNER ROBINS

TOPOGRAPHIC DATA:

A. VERTICAL DATUM: NAVD 88 AND WAS OBTAINED BY PERFORMING REDUNDANT RTK GPS OBSERVATIONS ON PRIMARY SURVEY CONTROL POINTS UTILIZING eGPS GNSS REAL TIME NETWORK USING CARLSON BRX7 GNSS RECEIVER .

B. THE TOPOGRAPHIC DATA WAS COLLECTED USING A GEOMAX ZOOM 80 TOTAL STATION. THE FIELD DATA UPON WHICH THIS TOPOGRAPHIC DATA IS BASED HAS A CLOSURE PRECISION OF 1 FOOT IN 22,612 FEET AND WAS NOT ADJUSTED.

C. CONTOURS SHOWN HEREON ARE BASED ON FIELD RUN SURVEY DATA AND COMPLETED ON 4/17/2026.

TITLE COMMITMENT PROPERTY DESCRIPTION

All that tract or parcel of land lying situate, lying and being in Land Lot 121, of the 5th Land District, of Houston County, Georgia, being known and designated as Tract "E", Springfield Village Subdivision, Phase 1, Part of the Robins West, as per plat recorded in Plat Book 25, Page 314 , Houston County Superior Court, said plat and the recorded copy thereof are hereby made a part of this description by reference thereto for all purposes.

Less and Except all that tract of land as shown on that certain Right of Way Deed, dated September 23, 2009, filed for record October 22, 2009 at 1:44 p.m., recorded in Deed Book 5074, Page 283 , aforesaid Records.

Parcel ID: 0W078 0 005 000

SURVEYED LEGAL DESCRIPTION

ALL THAT TRACT OR PARCEL OF LAND LYING AND BEING IN LAND LOT 121, OF THE 5TH LAND DISTRICT, CITY OF WARNER ROBINS, HOUSTON COUNTY, GEORGIA, AND BEING MORE PARTICULARLY DESCRIBED AS FOLLOWS:

BEGINNING AT AN IRON PIN SET, SAID IRON PIN SET BEING THE NORTHERLY END OF A MITER THAT FORMS THE INTERSECTION OF THE SOUTHERLY 100' RIGHT-OF-WAY OF WATSON BOULEVARD WITH THE EASTERLY 80' RIGHT-OF-WAY OF WESTGATE DRIVE AND BEING THE TRUE POINT OF BEGINNING;

THENCE SOUTH 89 DEGREES 52 MINUTES 28 SECONDS EAST A DISTANCE OF 169.35' ALONG SAID SOUTHERLY 100' RIGHT-OF-WAY OF WATSON BOULEVARD TO A CAPPED 1/2" IRON PIN FOUND;

THENCE SOUTH 00 DEGREES 06 MINUTES 35 SECONDS WEST A DISTANCE OF 208.00' LEAVING SAID 100' RIGHT-OF-WAY OF WATSON BOULEVARD TO A 1/2" REBAR FOUND;

THENCE SOUTH 89 DEGREES 55 MINUTES 25 SECONDS A DISTANCE OF 211.29' TO AN IRON PIN SET ON THE EASTERLY 80' RIGHT-OF-WAY OF WESTGATE DRIVE;

THENCE A CURVE TO THE LEFT HAVING A RADIUS OF 252.84', AN ARC LENGTH OF 76.24', A CHORD BEARING NORTH 07 DEGREES 17 MINUTES 33 SECONDS EAST AND A CHORD LENGTH 75.95' ALONG SAID EASTERLY 80' RIGHT-OF-WAY OF WESTGATE DRIVE TO A POINT;

THENCE NORTH 00 DEGREES 09 MINUTES 06 SECONDS WEST A DISTANCE OF 109.85' ALONG SAID RIGHT-OF-WAY OF WESTGATE DRIVE TO A MAG NAIL SET, SAID MAG NAIL SET BEING THE SOUTHERN END OF SAID MITERED INTERSECTION OF WATSON BOULEVARD AND WESTGATE DRIVE;

THENCE NORTH 54 DEGREES 34 MINUTES 33 SECONDS EAST A DISTANCE OF 40.48' ALONG SAID MITERED INTERSECTION OF WATSON BOULEVARD AND WESTAGE DRIVE TO AN IRON PIN SET, SAID IRON PIN SET BEING THE POINT OF BEGINNING;

SAID TRACT OR PARCEL CONTAINS 0.962 ACRES (41,909 SQUARE FEET) MORE OR LESS.

GEORGIA SURVEY NOTES:

A. THE FIELD WORK FOR THIS SURVEY WAS PERFORMED ON 4/17/26. ANY CHANGES IN SITE CONDITIONS AFTER THIS DATE ARE NOT REFLECTED ON THE SURVEY.

B. THE FIELD DATA UPON WHICH THIS BOUNDARY IS BASED WAS GATHERED BY USING RTK BASE AND ROVER OCCUPYING MULTIPLE BASE LOCATIONS AND DUPLICATE OBSERVATIONS ON CORNERS. THE PROCESSED DATA HAS A HORIZONTAL POSITIONAL ACCURACY OF LESS THAN 0.07 FEET. THE SCALE FACTOR USED TO CALCULATE GRID COORDINATES TO GROUND COORDINATES IS 1.000086357.


C. HORIZONTAL DATUM IS BASED ON NAD 83, GEORGIA STATE PLANE COORDINATE SYSTEM, GAWEST, AS ESTABLISHED BY PERFORMING REDUNDANT RTK GPS OBSERVATIONS ON PRIMARY SURVEY CONTROL POINTS UTILIZING eGPS GNSS REAL TIME NETWORK USING CARLSON BRX7.

D. ALL DISTANCES SHOWN ARE HORIZONTAL GROUND DISTANCES.

E. EQUIPMENT USED:GEOMAX ZOOM 80, CARLSON BRx7 GPS BASE AND ROVER

F. SOURCE OF TITLE: WILLIAM L. TOLER AND ELIZABETH TOLER
   DEED BOOK 8533, PAGE 116

G. PROPERTY CORNERS SET (#4RBS) ARE 1/2 INCH REBAR WITH PLASTIC CAP STAMPED "G+L LSF 1371", UNLESS OTHERWISE NOTED, ALL CORNERS SET ARE ~0.2' ABOVE GROUND UNLESS OTHERWISE NOTED.

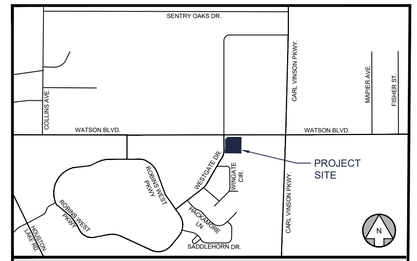

LOCATION MAP

IMAGE OBTAINED FROM "© GOOGLE MAPS"

ALTA/NSPS LAND TITLE SURVEY CERTIFICATION:

TO: FIFTH THIRD BANK, NATIONAL ASSOCIATION; PRAXIS3; COMMONWEALTH LAND TITLE INSURANCE COMPANY:

THIS IS TO CERTIFY THAT THIS MAP OR PLAT AND THE SURVEY ON WHICH IT IS BASED WERE MADE IN ACCORDANCE WITH THE 2026 MINIMUM STANDARD DETAIL REQUIREMENTS FOR ALTA/NSPS LAND TITLE SURVEYS, JOINTLY ESTABLISHED AND ADOPTED BY ALTA AND NSPS, AND INCLUDES ITEMS 1, 2, 3, 4, 5, 8(a), 8, 11(b), 13, 16, 17 OF TABLE A THEREOF.
THE FIELDWORK WAS COMPLETED ON 4/17/26.
DATE OF PLAT OR MAP: 5/8/2026

JASON A. HOPKINS, GEORGIA LAND SURVEYOR No. 3215 DATE: 5/8/2026

SURVEYOR'S CERTIFICATION

(iii) THIS PLAT IS A RETRACEMENT OF AN EXISTING PARCEL OR PARCELS OF LAND AND DOES NOT SUBDIVIDE OR CREATE A NEW PARCEL OR MAKE ANY CHANGES TO ANY REAL PROPERTY BOUNDARIES. THE RECORDING INFORMATION OF THE DOCUMENTS, MAPS, PLATS, OR OTHER INSTRUMENTS WHICH CREATED THE PARCEL OR PARCELS ARE STATED HEREON. **RECORDATION OF THIS PLAT DOES NOT IMPLY APPROVAL OF ANY LOCAL JURISDICTION, AVAILABILITY OF PERMITS, COMPLIANCE WITH LOCAL REGULATIONS OR REQUIREMENTS, OR SUITABILITY FOR ANY USE OR PURPOSE OF THE LAND.** FURTHERMORE, THE UNDERSIGNED LAND SURVEYOR CERTIFIES THAT THIS PLAT COMPLIES WITH THE MINIMUM TECHNICAL STANDARDS FOR PROPERTY SURVEYS IN GEORGIA AS SET FORTH IN THE RULES AND REGULATIONS OF THE GEORGIA BOARD OF REGISTRATION FOR PROFESSIONAL ENGINEERS AND LAND SURVEYORS AND AS SET FORTH IN O.C.G.A. SECTION 15-6-67.

GEORGIA PROFESSIONAL LAND SURVEYOR 3215 JASON A. HOPKINS

AS SURVEYOR FOR GASKINS + LECRAW, INC.

JASON A. HOPKINS GEORGIA PLS No. 3215 DATE: 05-08-2026

PREPARED IN THE OFFICE OF:

GASKINS +LECRAW

© 2026 GASKINS + LECRAW, INC.

24 JACKSON STREET
NEWNAN, GA 30265
PHONE - 770.253.5195
www.gaskinslecraw.com

LSF001371

REVISIONS:

REV. #	DATE	DRAWN BY:	CHECKED BY:

ALTA/NSPS LAND TITLE SURVEY FOR
FIFTH THIRD BANK, NATIONAL ASSOCIATION; PRAXIS3;
COMMONWEALTH LAND TITLE INSURANCE COMPANY

PROJECT LOCATION
2711 WATSON BLVD.
TAX P.N. 0W0780 005000
LAND LOT 121, 5 DISTRICT
CITY OF WARNER ROBINS, HOUSTON COUNTY, GEORGIA

CALL BEFORE YOU DIG

811 Know what's below. Call before you dig.

SCALE & NORTH ARROW:

N

GRID NORTH, GEORGIA WEST ZONE

0' 10' 20' 40'

SCALE: 1" = 20'

SURVEY INFO:

DRAWN BY:	JJV
REVIEWED BY:	JAH
JOB #:	75670007.000
DATE:	05-08-2026

SHEET NUMBER

1 OF 2

Drawing name: C:\Users\nstaat\Gaskins+LeCraw Dropbox\Shared Folders\Survey_Boundary\Houston\5th District\05_012\1756700O7.000 - WARNER ROBINS - FIFTH THIRD BANK\BND\DWG\Fifth Third ALTA-TOPO_ Warner Robins.dwg 24X36 COVER May 26, 2026 8:17am by: nstaat

This document, together with the concepts and designs presented herein, as an instrument of service, is intended only for the specific purpose and client for which it was prepared. Reuse of and improper reliance on this document without written authorization and adaptation by Gaskins + LeCraw, Inc. shall be without liability to Gaskins + LeCraw, Inc. Copyright Gaskins + LeCraw, Inc., 2026


CLERK OF THE SUPERIOR COURT RECORDING INFORMATION


ABBREVIATION LEGEND

P.O.C.	POINT OF COMMENCEMENT
RBF	REBAR FOUND
CTPF	CRIMP TOP PIPE FOUND
SSE	SANITARY SEWER EASEMENT
CMP	CORRUGATED METAL PIPE
HDPE	HIGH DENSITY POLYETHYLENE PIPE
RCP	REINFORCED CONCRETE PIPE
CI	CURB INLET
I.E.	INVERT ELEVATION
BW	BOTTOM OF WALL
FFE	FINISHED FLOOR ELEVATION
N/F	NOW OR FORMERLY
CLF	CHAIN LINK FENCE
P.O.B.	POINT OF BEGINNING
R/W	RIGHT-OF-WAY
OTPF	OPEN TOP PIPE FOUND
AE	ACCESS EASEMENT
DE	DRAINAGE EASEMENT
DIP	DUCTILE IRON PIPE
PVC	POLYVINYL CHLORIDE PIPE
TW	TOP OF WALL
BSL	BUILDING SETBACK LINE
C&G	CURB AND GUTTER
MAGNS	MAG NAIL SET
MAGNF	MAG NAIL FOUND

SYMBOL LEGEND

	AIR CONDITIONER UNIT
CBX	CABLE BOX
	JUNCTION BOX
	HOOD AND GRATE INLET
	SANITARY SEWER CLEANOUT
CWSP	CROSS WALK SIGNAL POLE
	GRATE INLET
	CONCRETE MONUMENT FOUND
EBX	ELECTRICAL BOX
EM	ELECTRIC METER
	FLARED END SECTION
	FIRE HYDRANT
FOMKR	FIBER OPTIC MARKER
	SINGLE WING CATCH BASIN
GM	GAS METER
	EXISTING GUY POLE
	EXISTING GREASE TRAP
	ADA PARKING
	HEADWALL
	IRRIGATION CONTROL VALVE
	IRON PIN FOUND (TYPE NOTED)
	IRON PIN SET
	LIGHT POLE
	LANDSCAPE LIGHT
	OUTLET CONTROL STRUCTURE
PBX	UG POWER TRANSFORMER
PM	POWER METER
	SANITARY SEWER MANHOLE
	SINGLE WING CATCH BASIN
	STREET SIGN
	PAINTED TRAFFIC MARKING
TBX	TELEPHONE BOX
T	TELEPHONE MANHOLE
	TELEPHONE PEDESTAL
TSBX	TRAFFIC SIGNAL BOX
TSHH	TRAFFIC SIGNAL HANDHOLE
TSP	TRAFFIC SIGNAL POLE
TP	CABLE PEDESTAL
GMKR	GAS MARKER
	UTILITY POLE
WM	WATER METER
	YARD INLET
	DOUBLE WING CATCH BASIN
10	PARKING COUNT

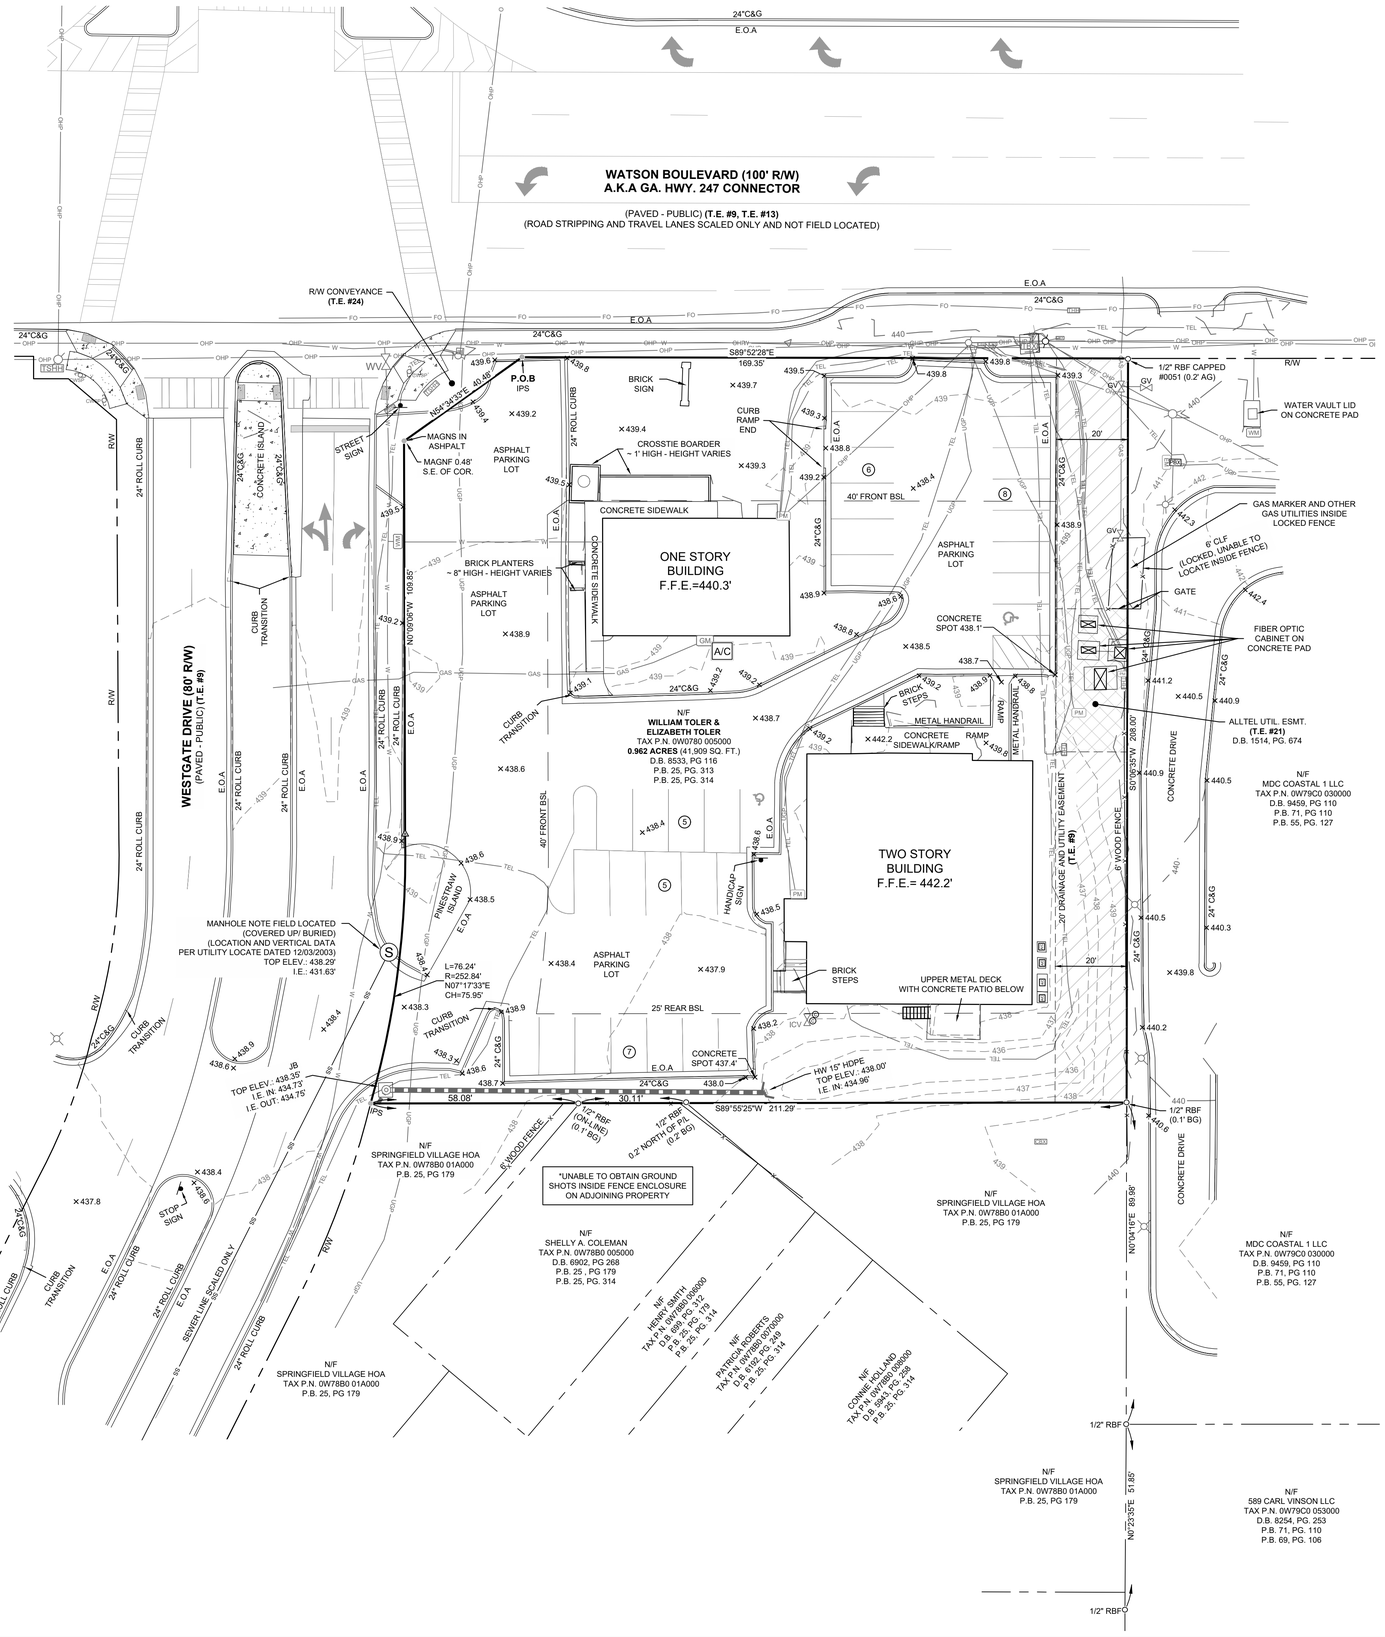

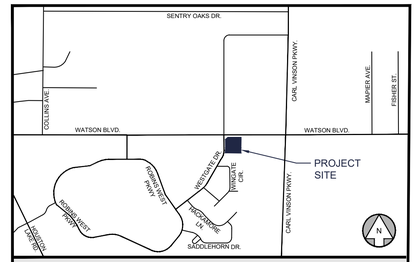

LOCATION MAP

IMAGE OBTAINED FROM "© GOOGLE MAPS"

LINE LEGEND

	STORM SEWER
FO	FIBER OPTIC
OHP	OVERHEAD POWER
	MAJOR CONTOUR
X X	FENCE
	PROPERTY LINE
	ADJOINING LOT LINE
SS	SANITARY SEWER
W W	WATER MAIN
UGP	UNDERGROUND POWER
GAS	GAS
	MINOR CONTOUR
	LAND LOT LINE
	RIGHT OF WAY
	EASEMENT
TEL	TELECOMMUNICATIONS

ALTA/NSPS LAND TITLE SURVEY CERTIFICATION:

TO: FIFTH THIRD BANK, NATIONAL ASSOCIATION; PRAXIS3; COMMONWEALTH LAND TITLE INSURANCE COMPANY:

THIS IS TO CERTIFY THAT THIS MAP OR PLAT AND THE SURVEY ON WHICH IT IS BASED WERE MADE IN ACCORDANCE WITH THE 2026 MINIMUM STANDARD DETAIL REQUIREMENTS FOR ALTA/NSPS LAND TITLE SURVEYS, JOINTLY ESTABLISHED AND ADOPTED BY ALTA AND NSPS, AND INCLUDES ITEMS 1, 2, 3, 4, 5, 6(a), 8, 11(b), 13, 16, 17 OF TABLE A THEREOF.
THE FIELDWORK WAS COMPLETED ON 4/17/26.
DATE OF PLAT OR MAP: 5/8/2026

JASON A. HOPKINS / GEORGIA LAND SURVEYOR No. 3215 DATE: 5/8/2026

SURVEYOR'S CERTIFICATION

(iii) THIS PLAT IS A RETRACEMENT OF AN EXISTING PARCEL OR PARCELS OF LAND AND DOES NOT SUBDIVIDE OR CREATE A NEW PARCEL OR MAKE ANY CHANGES TO ANY REAL PROPERTY BOUNDARIES. THE RECORDING INFORMATION OF THE DOCUMENTS, MAPS, PLATS, OR OTHER INSTRUMENTS WHICH CREATED THE PARCEL OR PARCELS ARE STATED HEREON. **RECORDATION OF THIS PLAT DOES NOT IMPLY APPROVAL OF ANY LOCAL JURISDICTION, AVAILABILITY OF PERMITS, COMPLIANCE WITH LOCAL REGULATIONS OR REQUIREMENTS, OR SUITABILITY FOR ANY USE OR PURPOSE OF THE LAND.** FURTHERMORE, THE UNDERSIGNED LAND SURVEYOR CERTIFIES THAT THIS PLAT COMPLIES WITH THE MINIMUM TECHNICAL STANDARDS FOR PROPERTY SURVEYS IN GEORGIA AS SET FORTH IN THE RULES AND REGULATIONS OF THE GEORGIA BOARD OF REGISTRATION FOR PROFESSIONAL ENGINEERS AND LAND SURVEYORS AND AS SET FORTH IN O.C.G.A. SECTION 15-6-67.

GEORGIA PROFESSIONAL 3215 LAND SURVEYOR JASON A. HOPKINS

AS SURVEYOR FOR GASKINS + LECRAW, INC.

JASON A. HOPKINS GEORGIA PLS No. 3215 DATE: 05/08/2026

PREPARED IN THE OFFICE OF:

GASKINS +LECRAW

© 2026 GASKINS + LECRAW, INC.
24 JACKSON STREET
NEWNAN, GA 30265
PHONE - 770.253.5195
www.gaskinslecraw.com

LSF001371

REVISIONS:

REV. #	DATE	DRAWN BY:	CHECKED BY:

ALTA/NSPS LAND TITLE SURVEY FOR
FIFTH THIRD BANK, NATIONAL ASSOCIATION; PRAXIS3; COMMONWEALTH LAND TITLE INSURANCE COMPANY

PROJECT LOCATION
2711 WATSON BLVD.
TAX P.N. 0W0780 005000
LAND LOT 121, 5 DISTRICT
CITY OF WARNER ROBINS, HOUSTON COUNTY, GEORGIA

CALL BEFORE YOU DIG

811 Know what's below. Call before you dig.

SCALE & NORTH ARROW:

GRID NORTH, GEORGIA WEST ZONE
0' 10' 20' 40'
SCALE: 1" = 20'

SURVEY INFO:

DRAWN BY:	JJV
REVIEWED BY:	JAH
JOB #:	75670007.000
DATE:	5/8/2026

SHEET NUMBER

2 OF 2

This document, together with the concepts and designs presented herein, as an instrument of service, is intended only for the specific purpose and client for which it was prepared. Reuse of and improper reliance on this document without written authorization and adaptation by Gaskins + LeCraw, Inc. shall be without liability to Gaskins + LeCraw, Inc. Copyright Gaskins + LeCraw, Inc., 2026

Drawing name: C:\Users\nstaat\Gaskins+LeCraw Dropbox\Shared Folders\Survey_Boundary\Houston\5th District\05_012175670007.000 - WARNER ROBINS - FIFTH THIRD BANK\BND\DWG\Fifth Third ALTA-TOPO _ Warner Robins.dwg 24X36 BND ALTA BND TOPO May 26, 2026 8:18am by: nstaat