FABRIC AND SUPPORTING FRAME FOR INLET PROTECTION

STEEL FRAME AND TYPE C SILT FENCE INSTALLATION

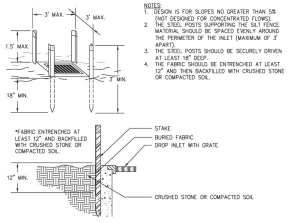

Figure 6-28.1 - Fabric and Supporting Frame For Inlet Projection

GSWCC 2018 Edition 6-153

PERFORATED HALF-ROUND PIPE WITH STONE FILTER

ISOMETRICS

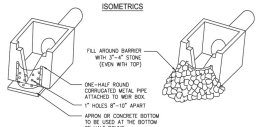

PLAN

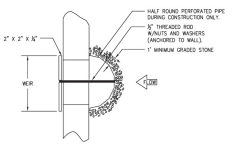

Figure 6-26.1 Perforated Half- Round Pipe with Stone Filter

GSWCC 2018 Edition 6-152

Table 6-5.1. Fertilizer Requirements

TYPE OF SPECIES	YEAR	ANALYSIS OR EQUIVALENT N-P-K	RATE	N TOP DRESSING RATE
1. Cool season grasses	First	6-12-12	1500 lbs./ac.	50-100 lbs./ac. 1/2/
	Second	6-12-12	1000 lbs./ac.	—
	Maintenance	10-10-10	400 lbs./ac.	30
2. Cool season grasses and legumes	First	6-12-12	1500 lbs./ac.	0-50 lbs./ac. 1/
	Second	0-10-10	1000 lbs./ac.	—
	Maintenance	0-10-10	400 lbs./ac.	—
3. Ground covers	First	10-10-10	1300 lbs./ac. 3/	—
	Second	10-10-10	1300 lbs./ac. 3/	—
	Maintenance	10-10-10	1100 lbs./ac.	—
4. Pine seedlings	First	20-10-5	one 21-gram pellet per seedling placed in the closing hole	—
5. Shrub Lespedeza	First	0-10-10	700 lbs./ac.	—
	Maintenance	0-10-10	700 lbs./ac. 4/	
6. Temporary cover crops seeded alone	First	10-10-10	500 lbs./ac.	30 lbs./ac. 5/
7. Warm season grasses	First	6-12-12	1500 lbs./ac.	50-100 lbs./ac. 2/6/
	Second	6-12-12	800 lbs./ac.	50-100 lbs./ac. 2/
	Maintenance	10-10-10	400 lbs./ac.	30 lbs./ac.
8. Warm season grasses and legumes	First	6-12-12	1500 lbs./ac.	50 lbs./ac./6/
	Second	0-10-10	1000 lbs./ac.	
	Maintenance	0-10-10	400 lbs./ac.	

1/ Apply in spring following seeding.
2/ Apply in split applications when high rates are used.
3/ Apply in 3 split applications.
4/ Apply when plants are pruned.
5/ Apply to grass species only.
6/ Apply when plants grow to a height of 2 to 4 inches.

CERTIFICATION STATEMENT (ENGINEER)

12 | 13 | 14

I CERTIFY THAT THE PERMITTEE'S EROSION, SEDIMENTATION AND POLLUTION CONTROL PLAN PROVIDES FOR AN APPROPRIATE AND COMPREHENSIVE SYSTEM OF BEST MANAGEMENT PRACTICES REQUIRED BY THE GEORGIA WATER QUALITY CONTROL ACT AND THE DOCUMENT "MANUAL FOR EROSION AND SEDIMENT CONTROL IN GEORGIA" PUBLISHED BY THE GEORGIA SOIL AND WATER CONSERVATION COMMISSION AS OF JANUARY 1 OF THE YEAR IN WHICH LAND-DISTURBING ACTIVITY WAS PERMITTED, PROVIDES FOR THE SAMPLING OF THE RECEIVING WATER(S) OR THE SAMPLING OF STORM WATER OUTFALLS AND THAT THE DESIGNED SYSTEM OF BEST MANAGEMENT PRACTICES AND SAMPLING METHODS IS EXPECTED TO MEET THE REQUIREMENTS CONTAINED IN THE GENERAL NPDES PERMIT NO. GAR 100001."

I CERTIFY UNDER PENALTY OF THE LAW THAT THIS PLAN WAS PREPARED AFTER A SITE VISIT TO THE LOCATIONS DESCRIBED HEREIN BY MYSELF OR MY AUTHORIZED AGENT, UNDER MY SUPERVISION."

UPON THE INSTALLATION OF THE PHASE 1 EROSION CONTROL MEASURES, I WILL VISIT THE SITE TO PERFORM THE INSPECTION CERTIFICATION WITHIN 7 DAYS, ONCE NOTIFIED BY THE CONTRACTOR AND CERTIFY THE INSTALLATION OF PHASE 1 BMPS.

GEORGIA LICENSED PROFESSIONAL (SIGN) — DATE: 7/9/26 — GEORGIA PE# 036681

TIMOTHY KYLE SHARPE — GEORGIA LICENSED PROFESSIONAL (PRINT) — GEORGIA EROSION CONTROL LEVEL 2 CERTIFICATION 3: 0000065749

2

GSWCC DESIGN PROFESSIONAL

GSWCC Georgia Soil and Water Conservation Commission

TIMOTHY KYLE SHARPE

Level II Certified Design Professional

Certification Number 0000065749

Issued: 02.17.2024 Expires: 02.17.2027

DETAIL

Table 6-4.1 - Temporary Cover or Companion Cover Crops

PLANT, PLANTING RATE, AND PLANTING DATE FOR TEMPORARY COVER OR COMPANION CROPS [1]

Species	Broadcast Rates		Resource Area[2]	Planting Dates by Resource Area (Solid lines indicate optimum dates, dotted lines indicate permissible but marginal dates. J F M A M J J A S O N D)	Remarks
	Rate Per Acre	Pure Live Seed (PLS) Per 1000 sqft			
BARLEY *Hordeum vulgare*					
alone	3 bu. (144 lbs)	3.3 lbs	M-L		14,000 seed per pound. Winter hardy. Use on productive soils.
in mixture	1/2 bu. (24lbs)	0.6 lb	P		
			C		
LESPEDEZA, ANNUAL *Lespedeza striata*					
alone	40 lbs	0.9 lb	M-L		200,000 seed per pound. May volunteer for several years. Use inoculant EL.
in mixture	10 lbs	0.2 lb	P		
			C		
LOVEGRASS, WEEPING *Eragrostis curvula*					
alone	4 lbs	0.1 lb	M-L		1,500,000 seed per pound. May last for several years. Mix with Sericea lespedeza.
in mixture	2 lbs	0.05 lb	P		
			C		
MILLET, BROWNTOP *Panicum fasciculatum*					
alone	40 lbs	0.9 lb	M-L		137,000 seed per pound. Quick dense cover. Will provide excessive competion in mixtures if seeded at high rate.
in mixture	10 lbs	0.2 lb	P		
			C		

Species	Broadcast Rates		Resource Area[2]	Planting Dates by Resource Area (Solid lines indicate optimum dates, dotted lines indicate permissible but marginal dates. J F M A M J J A S O N D)	Remarks
	Rate Per Acre	Pure Live Seed (PLS) Per 1000 sqft			
MILLET, PEARL *Pennisetum glaucum*					
alone	50 lbs	1.1 lbs	M-L		88,000 seed per pound. Quick dense cover. May reach 5 feet in height. Not recommended for mixtures.
			P		
			C		
OATS *Avena sativa*					
alone	4 bu. (128 lbs)	2.9 lbs	M-L		13,000 seed per pound. Use on productive soils. Not as a winter hardy as rye or barley.
in mixture	1 bu. (32 lbs)	0.7 lb	P		
			C		
RYE *Secale cereale*					
alone	3 bu. (168 lbs)	3.9 lbs	M-L		18,000 seed per pound. Quick cover. Drought tolerant and winter hardy.
in mixture	1/2 bu. (28 lbs)	0.6 lb	P		
			C		
RYEGRASS, ANNUAL *Lolium temulentum*					
alone	40 lbs	0.9 lb	M-L		227,000 seed per pound. Dense cover. Very competitive and is not to be used in mixtures.
			P		
			C		
SUDANGRASS *Sorghum sudanese*					
alone	60 lbs	1.4 lbs	M-L		55,000 seed per pound. Good on droughty sites. Not recommended for mixtures.
			P		
			C		

Species	Broadcast Rates		Resource Area[2]	Planting Dates by Resource Area (Solid lines indicate optimum dates, dotted lines indicate permissible but marginal dates. J F M A M J J A S O N D)	Remarks
	Rate Per Acre	Pure Live Seed (PLS) Per 1000 sqft			
TRITICALE *X Triticosecale*					
alone	3 bu. (144 lbs)	3.3 lbs	C		Use on lower part of Southern Coastal Plain and in Atlantic Coastal Flatwoods only.
in mixture	1/2 bu. (24 lbs)	0.6 lb			
WHEAT *Triticum aestivum*					
alone	3 bu. (180 lbs)	4.1 lbs	M-L		15,000 seed per pound. Winter hardy.
in mixture	1/2 bu. (30 lbs)	0.7 lb	P		
			C		

[1] Temporary cover crops are very competitive and will crowd out perennials if seeded too heavily
[2] Reduce seeding rates by 50% when drilled.
[3] M-L represents the Mountain, Blue Ridge, and Ridges and Valleys MLRAs
P represents the Southern Piedmont MLRA
C represents Southern Coastal Plain, Sand Hills, Black Lands, and Atlantic Coast Flatwoods MLRAs
(see Figure 6-4.1, p. 6-40)

PREPARED IN THE OFFICE OF:

GASKINS + LECRAW
a PAPE-DAWSON company
© 2026 GASKINS + LECRAW
3475 CORPORATE WAY
SUITE A
DULUTH, GA 30096
PHONE - 678.546.8100
www.gaskinslecraw.com
PEF008127

REVISIONS:

NO.	DATE	DRAWN BY	CHECKED BY
1			

CLIENT
PRAXIS3
100 PEACHTREE STREET NW, SUITE 1450, ATLANTA, GEORGIA 30303

PROJECT
FIFTH THIRD BANK - WARNER ROBINS, GA
2711 WATSON BLVD
PARCEL ID: 0W0780-005000
WARNER ROBINS, HOUSTON COUNTY, GEORGIA

SEAL:

7/9/2026

CALL BEFORE YOU DIG

811
Know what's below.
Call before you dig.

SCALE & NORTH ARROW:

DETAILS ARE NOT DRAWN TO SCALE

DESIGN INFO:

DRAWN BY:	JOA
DESIGNED BY:	MAT
REVIEWED BY:	TKS
JOB #:	75670007
DATE:	JULY 9, 2026

ESPC DETAILS - 2

C-2.6

SOD MAINTENANCE AND INSTALLATION

SOD LAYOUT AND PREPARATION

LAY SOD IN A STAGGERED PATTERN. BUTT THE STRIPS TIGHTLY AGAINST EACH OTHER. DO NOT LEAVE SPACES FOR SOIL TO FALL BETWEEN THE STRIPS. ROLL OR TROMEL IN A HANDY WAY. FOR TUCKING DOWN THE ENDS AND TRIMMING PIECES.

BUTTING ANGLED ENDS CAUSED BY THE AUTOMATIC SOD CUTTER MUST BE MATCHED CORRECTLY.

DIRECTIONS FOR INITIAL MAINTENANCE

Step 1: ROLL SOD IMMEDIATELY TO ACHIEVE FIRM CONTACT WITH THE SOIL

Step 2: WATER TO A DEPTH OF 4" AS NEEDED. WATER WELL AS SOON AS THE SOD IS LAID.

Step 3: NOW WHEN THE SOD IS ESTABLISHED --- IN 2--3 WEEKS, SET THE MOWER HIGH (2"--3").

APPEARANCE OF GOOD SOD

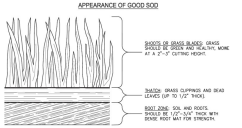

SODDED WATERWAYS

SOD DIRECTIONS

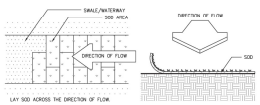

NETTING DIRECTIONS

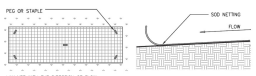

PEG DETAIL

USE PEGS OR STAPLES TO FASTEN SOD FIRMLY --- AT THE ENDS OF STRIPS AND IN THE MIDDLE OF EACH STRIP. IN STEEP OR CRITICAL AREAS, DRIVE PEGS TO WORK DRIVE PEGS OR STAPLES FLUSH WITH THE GROUND.

Source: Va. DSWC

Table 6-6.2 Sod Planting Requirements

Grass	Varieties	Resource Area	Growing Season
Bermudagrass	Common Tifway Tifgreen Tifdwarf	M-L,P,C P,C P,C	warm weather
Bahiagrass	Pensacola	P,C	warm weather
Centipede	–	P,C	warm weather
St. Augustine	Common Bitterblue Raleigh	C	warm weather
Zoysia	Emerald Myer	P,C	warm weather
Tall Fescue	Kentucky	M-L,P	cool weather

Table 6-6.3 Fertilizer Requirements for Sod

Types of Species	Planting Year	Fertilizer (N-P-K)	Rate (lbs./acre)	Nitrogen Top Dressing Rate (lbs./acre)
cool season grasses	first	6-12-12	1500	50-100
	second	6-12-12	1000	- -
	maintenance	10-10-10	400	30
warm season grasses	first	6-12-12	1500	50-100
	second	6-12-12	800	50-100
	maintenance	10-10-10	400	30

Mix fertilizer into soil surface. Fertilize based on soil tests or Table 6-6.1.

Table 6-6.1. Fertilizer Requirements for Soil Surface Application

Fertilizer Type	Fertilizer Rate (lbs/acre)	Fertilizer Rate (lbs/sq ft)	Season
10-10-10	1000	.025	Fall

Agricultural lime should be applied based on soil tests or at a rate of 1 to 2 tons per acre.

FABRIC AND SUPPORTING FRAME INLET PROTECTION (Sd2-F)

PERFORATED HALF-ROUND PIPE WITH STONE FILTER (Rt-P)

FERTILIZER REQUIREMENTS

DETAIL

DISTURBED AREA STABILIZATION - WITH SODDING (Ds4)

PERMANENT VEGETATIVE PRACTICES (Ds3)

TEMPORARY VEGETATIVE PRACTICES (Ds2)

This document, together with the concepts and designs presented herein, as an instrument of service, is intended only for the specific purpose and client for which it was prepared. Reuse of and improper reliance on this document without written authorization and adaptation by Gaskins + LeCraw, a Pape-Dawson Company shall be without liability to Gaskins + LeCraw, a Pape-Dawson Company. Copyright Gaskins + LeCraw, a Pape-Dawson Company, 2026

Drawing name: C:\Users\klarsh\Gaskins+LeCraw Dropbox\Shared Folders\Engineering\75670007 - Praxis3 - Fifth Third - Warner Robins, GA\CAD\CIVIL\75670007 - 05 - ESPC DETAILS.dwg - EROSION CONTROL DETAILS - 2 - Jul 09, 2026 10:51am - by: cbivins

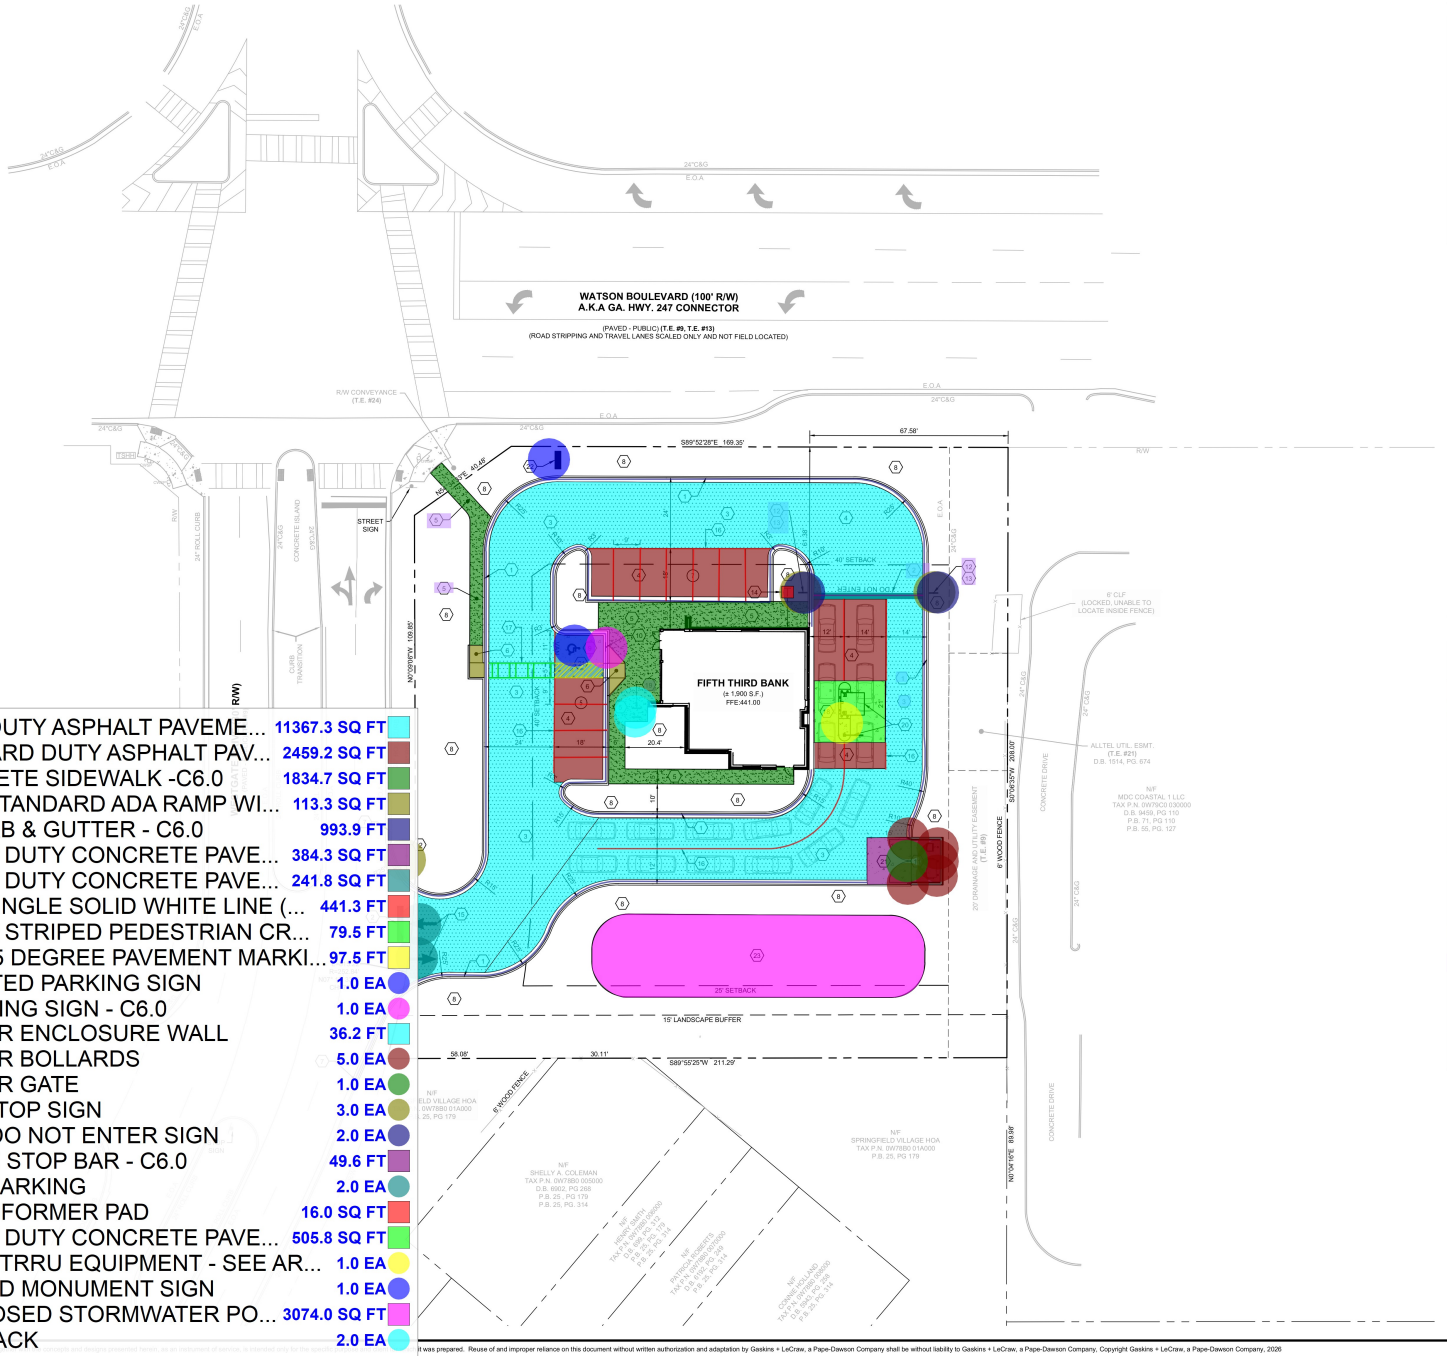

3:HEAVY DUTY ASPHALT PAVEME...	11367.3 SQ FT
4: STANDARD DUTY ASPHALT PAV...	2459.2 SQ FT
5: CONCRETE SIDEWALK -C6.0	1834.7 SQ FT
6: GDOT STANDARD ADA RAMP WI...	113.3 SQ FT
1: 24" CURB & GUTTER - C6.0	993.9 FT
21: HEAVY DUTY CONCRETE PAVE...	384.3 SQ FT
21: HEAVY DUTY CONCRETE PAVE...	241.8 SQ FT
16: 4" W SINGLE SOLID WHITE LINE (...	441.3 FT
17: WHITE STRIPED PEDESTRIAN CR...	79.5 FT
4" W DA 45 DEGREE PAVEMENT MARKI...	97.5 FT
ADA PAINTED PARKING SIGN	1.0 EA
ADA PARKING SIGN - C6.0	1.0 EA
DUMPSTER ENCLOSURE WALL	36.2 FT
DUMPSTER BOLLARDS	5.0 EA
DUMPSTER GATE	1.0 EA
12: R1-1:STOP SIGN	3.0 EA
13: RF-1: DO NOT ENTER SIGN	2.0 EA
24" WHITE STOP BAR - C6.0	49.6 FT
ARROW MARKING	2.0 EA
14: TRANSFORMER PAD	16.0 SQ FT
18: HEAVY DUTY CONCRETE PAVE...	505.8 SQ FT
20: DRIVE TRRU EQUIPMENT - SEE AR...	1.0 EA
PROPOSED MONUMENT SIGN	1.0 EA
23: PROPOSED STORMWATER PO...	3074.0 SQ FT
19:BIKE RACK	2.0 EA

GENERAL SITE NOTES

1) ALL DIMENSIONS ARE TO THE FACE OF CURB UNLESS SPECIFIED OTHERWISE.

2) ALL TREES SHALL HAVE PROPER PROTECTION DURING CONSTRUCTION UNLESS APPROVED PLANS INDICATE OTHERWISE.

3) BOUNDARY & TOPOGRAPHIC SURVEY BY GASKINS+LECRAW, A PAPE DAWSON COMPANY, DATED 05.08.2026. BENCHMARK IS NOTED ON SURVEY.

4) FLOOD PLAIN IS NOT PRESENT ON THIS SITE AS SHOWN ON THE FEMA FIRM MAP NUMBER 13153C0085E, DATED 09.28.2007.

5) 1 HANDICAP SPACE IS REQUIRED TO BE VAN ACCESSIBLE WITH A MINIMUM 96" WIDE ACCESS AREA.

6) ACCESSIBLE PARKING AREAS, INCLUDING AISLES, SHALL SLOPE NO MORE THAN 2% IN ANY DIRECTION.

7) THE OWNER IS RESPONSIBLE FOR OBTAINING ANY NECESSARY AGREEMENTS FROM ADJACENT PROPERTY OWNERS IN ORDER TO PERFORM THE REQUIRED OFFSITE WORK, INCLUDING, STORM DRAINAGE, CURB AND GUTTER AND PAVEMENT TIE-INS AND GRADING.

8) REFERENCE ARCH PLANS FOR DIRECTIONAL SIGNAGE, SITE SIGNAGE, BUILDING DIMENSIONS, ETC.

9) ALL NEW PAVEMENT SHALL MEET OR EXCEED GEOTECHNICAL SPECIFICATION. SEE REPORT PREPARED BY TERRACON, DATED 05.04.2026.

SITE SUMMARY

SITE AREA	
SITE AREA:	0.96 ACRES (41,909 S.F.)
IMPERVIOUS AREA:	21,033 S.F. (50.2%)
PERVIOUS AREA:	20,876 S.F. (49.8%)
ZONING CLASSIFICATION	
JURISDICTION:	CITY OF WARNER ROBINS
ZONING:	C-2 (GENERAL COMMERCIAL DISTRICT)
ADJACENT ZONING:	C-2 / R-3
BUILDING SETBACKS	
FRONT:	40'
SIDE:	0'
REAR:	25'
BUILDING SUMMARY	
BUILDING AREA:	1,900 S.F.
BUILDING COVERAGE:	4.5%
PARKING SUMMARY	
PARKING REQ.:	1 SPACE / 300 S.F.
	7 SPACES
PARKING PROV.:	11 SPACES
STANDARD STALL DIMENSIONS:	9' x 18'
MIN. DRIVE WIDTH:	24'

KEY NOTES

1	24" CURB & GUTTER, SEE SHEET C-6.0 FOR DETAIL
2	24" WHITE STOP BAR, SEE SHEET C-6.0 FOR DETAIL
3	HEAVY DUTY ASPHALT PAVEMENT, SEE SHEET C-6.2 FOR PAVEMENT SPECIFICATIONS
4	STANDARD DUTY ASPHALT PAVEMENT, SEE SHEET C-6.2 FOR PAVEMENT SPECIFICATIONS
5	CONCRETE SIDEWALK, SEE SHEET C-6.0 FOR DETAIL
6	GDOT STANDARD ADA RAMP WITH DETECTABLE WARNING, SEE SHEET C-6.1 FOR DETAIL
7	CONTRACTOR TO TIE INTO AND MATCH EXISTING CURB & GUTTER IN BOTH GRADE AND ALIGNMENT
8	LANDSCAPE AREA, SEE SHEET L-1.0 FOR LANDSCAPE PLANTING DESIGN
9	ADA PARKING AREA, SEE SHEET C-6.0 FOR DETAIL(S)
10	ADA PARKING SIGN, SEE SHEET C-6.0 FOR DETAIL
11	DUMPSTER ENCLOSURE, REFER TO ARCHITECTURAL PLANS FOR DETAILS
12	STOP SIGN (R1-1), SEE SHEET C-6.0 FOR MOUNTING DETAIL
13	DO NOT ENTER SIGN (RS-1), SEE SHEET C-6.0 FOR MOUNTING DETAIL
14	CONCRETE TRANSFORMER PAD PER UTILITY OWNER'S REQUIREMENTS
15	TYPICAL PAVEMENT MARKINGS, SEE SHEET C-6.0 FOR DETAILS
16	4" WIDE SINGLE SOLID WHITE LINE (SSWL)
17	9' WIDE, WHITE STRIPED PEDESTRIAN CROSSING/CROSSWALK
18	HEAVY DUTY CONCRETE PAVEMENT, SEE SHEET C-6.2 FOR PAVEMENT SPECIFICATIONS
19	BIKE RACK(S), SEE SHEET C-6.0 FOR DETAILS
20	DRIVE THRU EQUIPMENT / SIGNAGE, REFER TO ARCH PLANS FOR DETAILS
21	HEAVY DUTY CONCRETE PAVEMENT, SEE SHEET C-6.2 FOR PAVEMENT SPECIFICATIONS
22	PROPOSED MONUMENT SIGN, DESIGNED AND PERMITTED BY OTHERS
23	PROPOSED STORMWATER POND

IMPERVIOUS CALCULATIONS

	PERVIOUS (SF)	IMPERVIOUS (SF)
EXISTING CONDITION:	13,601 (32.5%)	28,308 (67.5%)
PROPOSED CONDITION:	20,876 (49.8%)	21,033 (50.2%)

NET DECREASE OF 7,275 SF OF IMPERVIOUS AREA

PAVEMENT LEGEND

*CONTRACTOR TO SUBMIT JOINT PLAN TO GEOTECH FOR REVIEW/APPROVAL PRIOR TO PAVING

CONCRETE PAVEMENT (SEE GEOTECH REPORT BY TERRACON, DATED 05.04.2026)

HEAVY DUTY PAVEMENT (SEE GEOTECH REPORT BY TERRACON, DATED 05.04.2026)

Drawings and designs presented herein, as an instrument of service, is intended only for the specific purpose and client for which it was prepared. Reuse of and improper reliance on this document without written authorization and adaptation by Gaskins + LeCraw, a Pape-Dawson Company shall be without liability to Gaskins + LeCraw, a Pape-Dawson Company. Copyright Gaskins + LeCraw, a Pape-Dawson Company, 2026

PREPARED IN THE OFFICE OF:
GASKINS + LECRAW
a PAPE-DAWSON company
© 2026 GASKINS + LECRAW
3475 CORPORATE WAY
SUITE A
DULUTH, GA 30096
PHONE - 678.546.8100
www.gaskinslecraw.com
PEF008127

REVISIONS:

DESCRIPTION	DATE	DRAWN BY	CHECKED BY
	-	-	-
	-	-	-
	-	-	-
	-	-	-
	-	-	-
	-	-	-
REV #	-	-	-

CLIENT
PRAXIS3
100 PEACHTREE STREET NW, SUITE 1450, ATLANTA, GEORGIA 30303

PROJECT
FIFTH THIRD BANK - WARNER ROBINS, GA
2711 WATSON BLVD
PARCEL ID: 0W0780-005000
WARNER ROBINS, HOUSTON COUNTY, GEORGIA

SEAL:
GEORGIA REGISTERED
No. PE036681
PROFESSIONAL
ENGINEER
TIMOTHY KYLE SHARPE
7/9/2026

CALL BEFORE YOU DIG
811
Know what's below.
Call before you dig.

SCALE & NORTH ARROW:
NORTH ARROW
0' 10' 20' 40'
SCALE: 1" = 20'

DESIGN INFO:

DRAWN BY:	JOA
DESIGNED BY:	MAT
REVIEWED BY:	TKS
JOB #:	75670007
DATE:	JULY 9, 2026

SITE PLAN

C-3.0

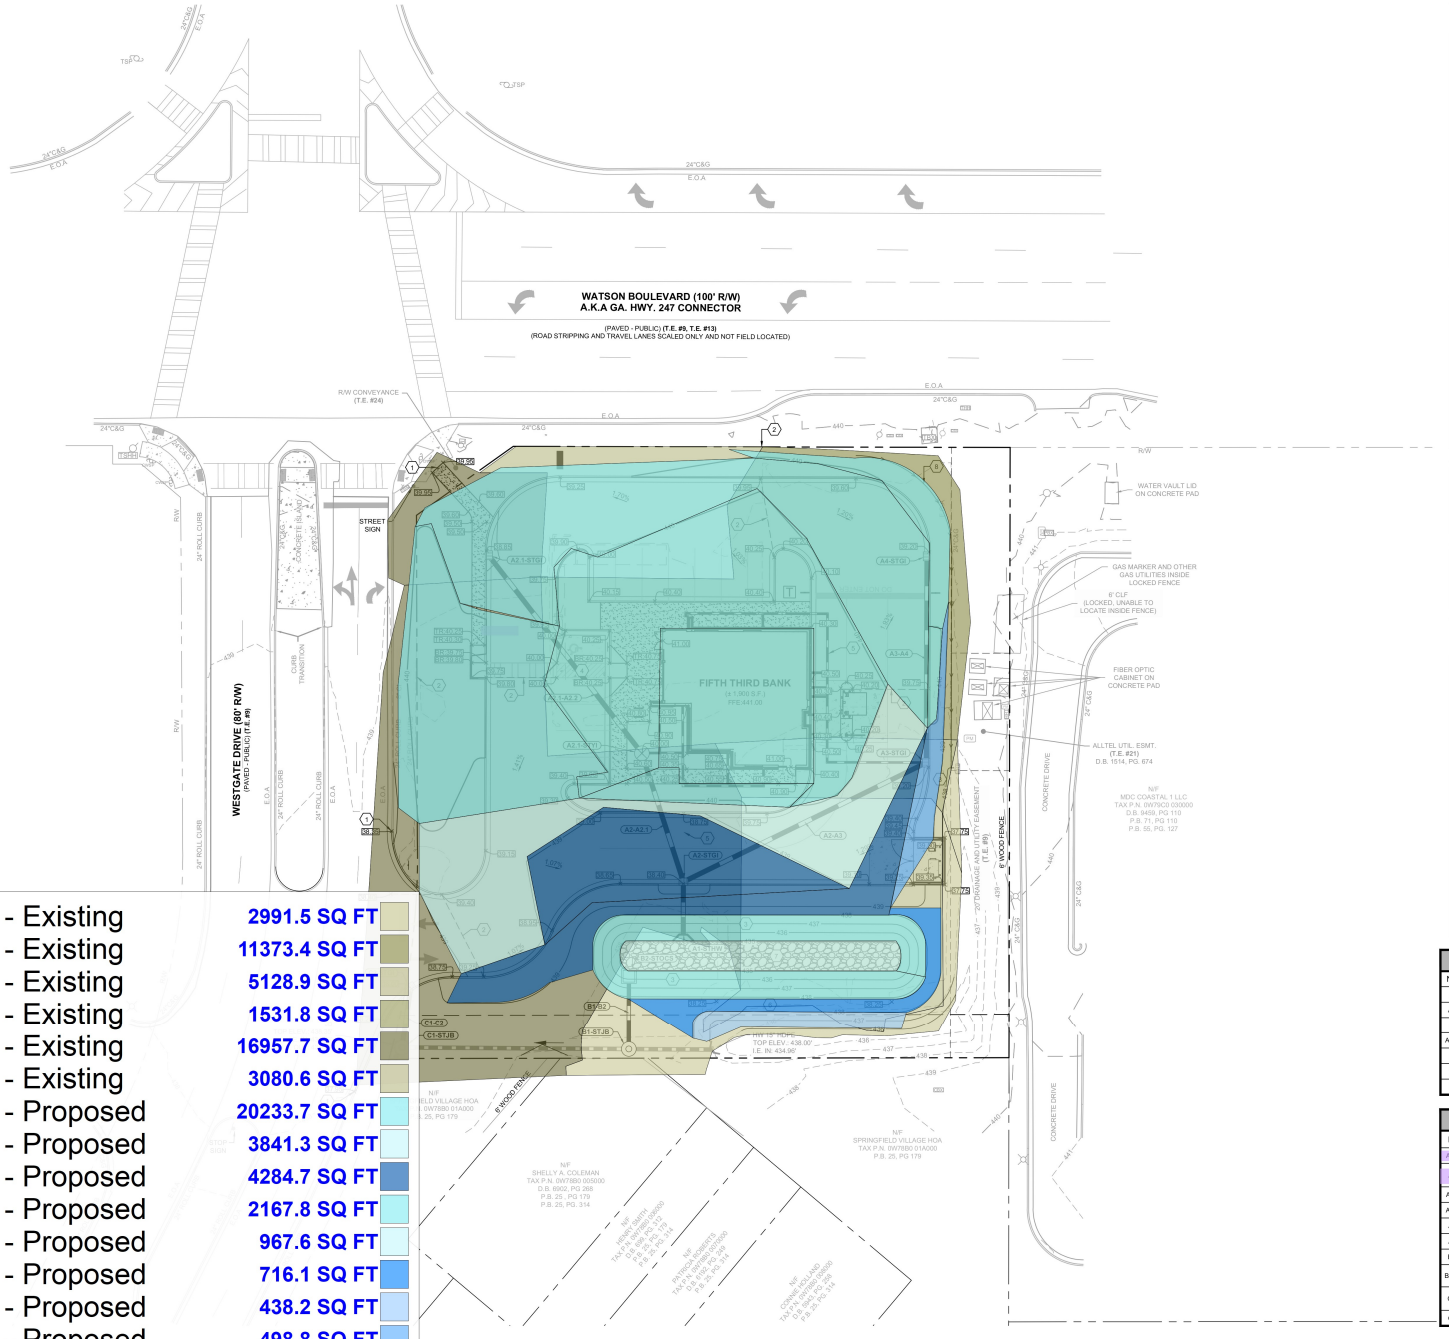

E 437.500 - Existing	2991.5 SQ FT
E 439.500 - Existing	11373.4 SQ FT
E 441.000 - Existing	5128.9 SQ FT
E 440.000 - Existing	1531.8 SQ FT
E 438.500 - Existing	16957.7 SQ FT
E 439.000 - Existing	3080.6 SQ FT
P 440.000 - Proposed	20233.7 SQ FT
P 439.500 - Proposed	3841.3 SQ FT
P 439.000 - Proposed	4284.7 SQ FT
P 436.500 - Proposed	2167.8 SQ FT
P 435.000 - Proposed	967.6 SQ FT
P 438.000 - Proposed	716.1 SQ FT
P 437.000 - Proposed	438.2 SQ FT
P 439.500 - Proposed	498.8 SQ FT

GENERAL GRADING NOTES

1) ALL CRITICAL SPOT GRADES ALONG CURB ARE BOTTOM OF CURB ELEVATIONS UNLESS OTHERWISE SPECIFIED.

2) NO SLOPES ARE TO BE STEEPER THAN 2:1.

3) ALL LAND DISTURBANCE TO BE STABILIZED WITH VEGETATION UPON COMPLETION OF DEMOLITION.

4) BOUNDARY & TOPOGRAPHIC INFORMATION FROM SURVEY BY GASKINS+LECRAW, A PAPE DAWSON COMPANY, DATED 05.06.2026.

5) FLOOD PLAIN IS NOT PRESENT ON THIS SITE AS SHOWN ON THE FEMA FIRM MAP NUMBER 13153C0085E, DATED 09.28.2007.

6) EROSION AND SEDIMENT CONTROL MEASURES ARE TO BE ACCOMPLISHED PRIOR TO ANY OTHER CONSTRUCTION ON THE SITE AND MAINTAINED UNTIL PERMANENT GROUND COVER IS ESTABLISHED.

7) OWNER IS RESPONSIBLE FOR MAINTENANCE OF ALL STORM SEWER ON PRIVATE PROPERTY.

8) THE OWNER IS RESPONSIBLE FOR OBTAINING ANY NECESSARY AGREEMENTS FROM ADJACENT PROPERTY OWNERS IN ORDER TO PERFORM THE REQUIRED OFFSITE WORK, INCLUDING, STORM DRAINAGE, CURB AND GUTTER AND PAVEMENT TIE-INS AND GRADING.

9) VERTICAL DEPTH OF ALL DRY AND PRESSURIZED UTILITIES IS UNKNOWN. CONTRACTOR TO NOTIFY OWNER AND ENGINEER IMMEDIATELY IF ANY CONFLICTS ARE FOUND.

10) SIDEWALKS ADJACENT TO BUILDING AND ALONG ADA ROUTES TO HAVE MAXIMUM CROSS SLOPE OF 2%.

KEY NOTES

1	CONTRACTOR TO TIE INTO AND MATCH EXISTING GRADE
2	RIDGE LINE
3	3:1 SLOPE
4	ADA PARKING AREA, MAXIMUM SLOPE OF 2% IN ANY DIRECTION
5	6" HDPE HEADER PIPE FOR ROOF DRAIN CONNECTION, MINIMUM SLOPE OF 1%
6	5' WIDE DAM, TOP OF DAM ELEVATION: 438.25
7	INFILTRATION BASIN. REFER TO SHEET C-4.2 FOR DETAIL
7	CONTRACTOR TO FINE GRADE 2' WIDE DRAINAGE SWALE @ 1% MIN. SLOPE

SPOT ELEVATION LEGEND

BR: BOTTOM OF RAMP
BW: BOTTOM OF WALL
LP: LOW POINT
TR: TOP OF RAMP
TW: TOP OF WALL
HP: HIGH POINT
*ALL CRITICAL SPOT GRADES ALONG CURB ARE BOTTOM OF CURB ELEVATIONS UNLESS OTHERWISE SPECIFIED.

STRUCTURE TYPES

STSWCB:	GDOT STD 1033D	STDWCB:	GDOT STD 1034D
STSWCB:	GDOT STD 1019A TYPE A	STYI:	NYOPLAST INLET W/DOME
STGI:	GDOT STD 1019A TYPE E	STFE:	GDOT STD 1120
STHW:	GDOT STD 1001B HEADWALL	STOCS:	SEE DETAILS SHEET C-6.2

DEFINITION OF STRUCTURE SPOT ELEVATIONS

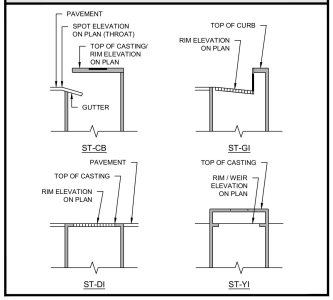

STORM PIPES

NAME:	SIZE:	LENGTH:	SLOPE:	INV UP:	INV DOWN:	MATERIAL:
A1-A2	18"	17.69	0.50%	435.09 (A2-STGI)	435.00 (A1-STHW)	HDPE
A2-A2.1	18"	45.97	0.50%	435.32 (A2.1-STYI)	435.09 (A2-STGI)	HDPE
A2-A3	18"	92.25	0.50%	435.55 (A3-STGI)	435.09 (A2-STGI)	HDPE
A2.1-A2.2	18"	85.26	0.50%	435.74 (A2.2-STGI)	435.32 (A2.1-STYI)	HDPE
A3-A4	18"	70.17	0.50%	435.90 (A4-STGI)	435.55 (A3-STGI)	HDPE
B1-B2	15"	25.11	0.50%	435.00 (B2-STOCS)	434.87 (B1-STJB)	HDPE
C1-C2	18"	21.08	0.50%	434.86 (C2-STGI)	434.75 (C1-STJB)	HDPE

STORM STRUCTURES

NAME:	TYPE:	STATION:	RIM:	INV IN: (PIPE)	INV OUT: (PIPE)
A1-STHW	HEADWALL	0+00.00	435.82	435.00 (A1-A2)	
A2-STGI	HOODED GRATE INLET	0+17.69	438.40	435.09 (A2-A2.1) 435.09 (A2-A3)	435.09 (A1-A2)
A2.1-STYI	YARD INLET	0+45.97	440.00	435.32 (A2.1-A2.2)	435.32 (A2-A2.1)
A2.2-STGI	HOODED GRATE INLET	1+31.22	438.85		435.74 (A2.1-A2.2)
A3-STGI	HOODED GRATE INLET	1+09.95	439.20	435.55 (A3-A4)	435.55 (A2-A3)
A4-STGI	HOODED GRATE INLET	1+80.11	439.20		435.90 (A3-A4)
B1-STJB	JUNCTION BOX	0+00.00	438.25	434.87 (B1-B2)	
B2-STOCS	OUTLET CONTROL STRUCTURE	0+25.11	435.67		435.00 (B1-B2)
C1-STJB	JUNCTION BOX (EXISTING)	0+00.00	438.40	434.75 (C1-C2)	
C2-STGI	HOODED GRATE INLET	0+21.08	438.01		434.86 (C1-C2)

PREPARED IN THE OFFICE OF:
GASKINS +LECRAW
a PAPE-DAWSON company
© 2026 GASKINS + LECRAW
3475 CORPORATE WAY
SUITE A
DULUTH, GA 30096
PHONE - 678.546.8100
www.gaskinslecraw.com
PEF008127

REVISIONS:

NO. #	DATE	DRAWN BY	CHECKED BY
1			

CLIENT
PRAXIS3
100 PEACHTREE STREET NW, SUITE 1450, ATLANTA, GEORGIA 30303

PROJECT
FIFTH THIRD BANK - WARNER ROBINS, GA
2711 WATSON BLVD
PARCEL ID: 0W0780-005000
WARNER ROBINS, HOUSTON COUNTY, GEORGIA

SEAL:
GEORGIA REGISTERED
No. PE036681 PROFESSIONAL ENGINEER
TIMOTHY KYLE SHARPE
7/9/2026

CALL BEFORE YOU DIG
811
Know what's below. Call before you dig.

SCALE & NORTH ARROW:
NORTH ARROW
0' 10' 20' 40'
SCALE: 1" = 20'

DESIGN INFO:

DRAWN BY:	JOA
DESIGNED BY:	MAT
REVIEWED BY:	TKS
JOB #:	75670007
DATE:	JULY 9, 2026

GRADING PLAN
C-4.0

It was prepared. Reuse of and improper reliance on this document without written authorization and adaptation by Gaskins + LeCraw, a Pape-Dawson Company shall be without liability to Gaskins + LeCraw, a Pape-Dawson Company. Copyright Gaskins + LeCraw, a Pape-Dawson Company, 2026

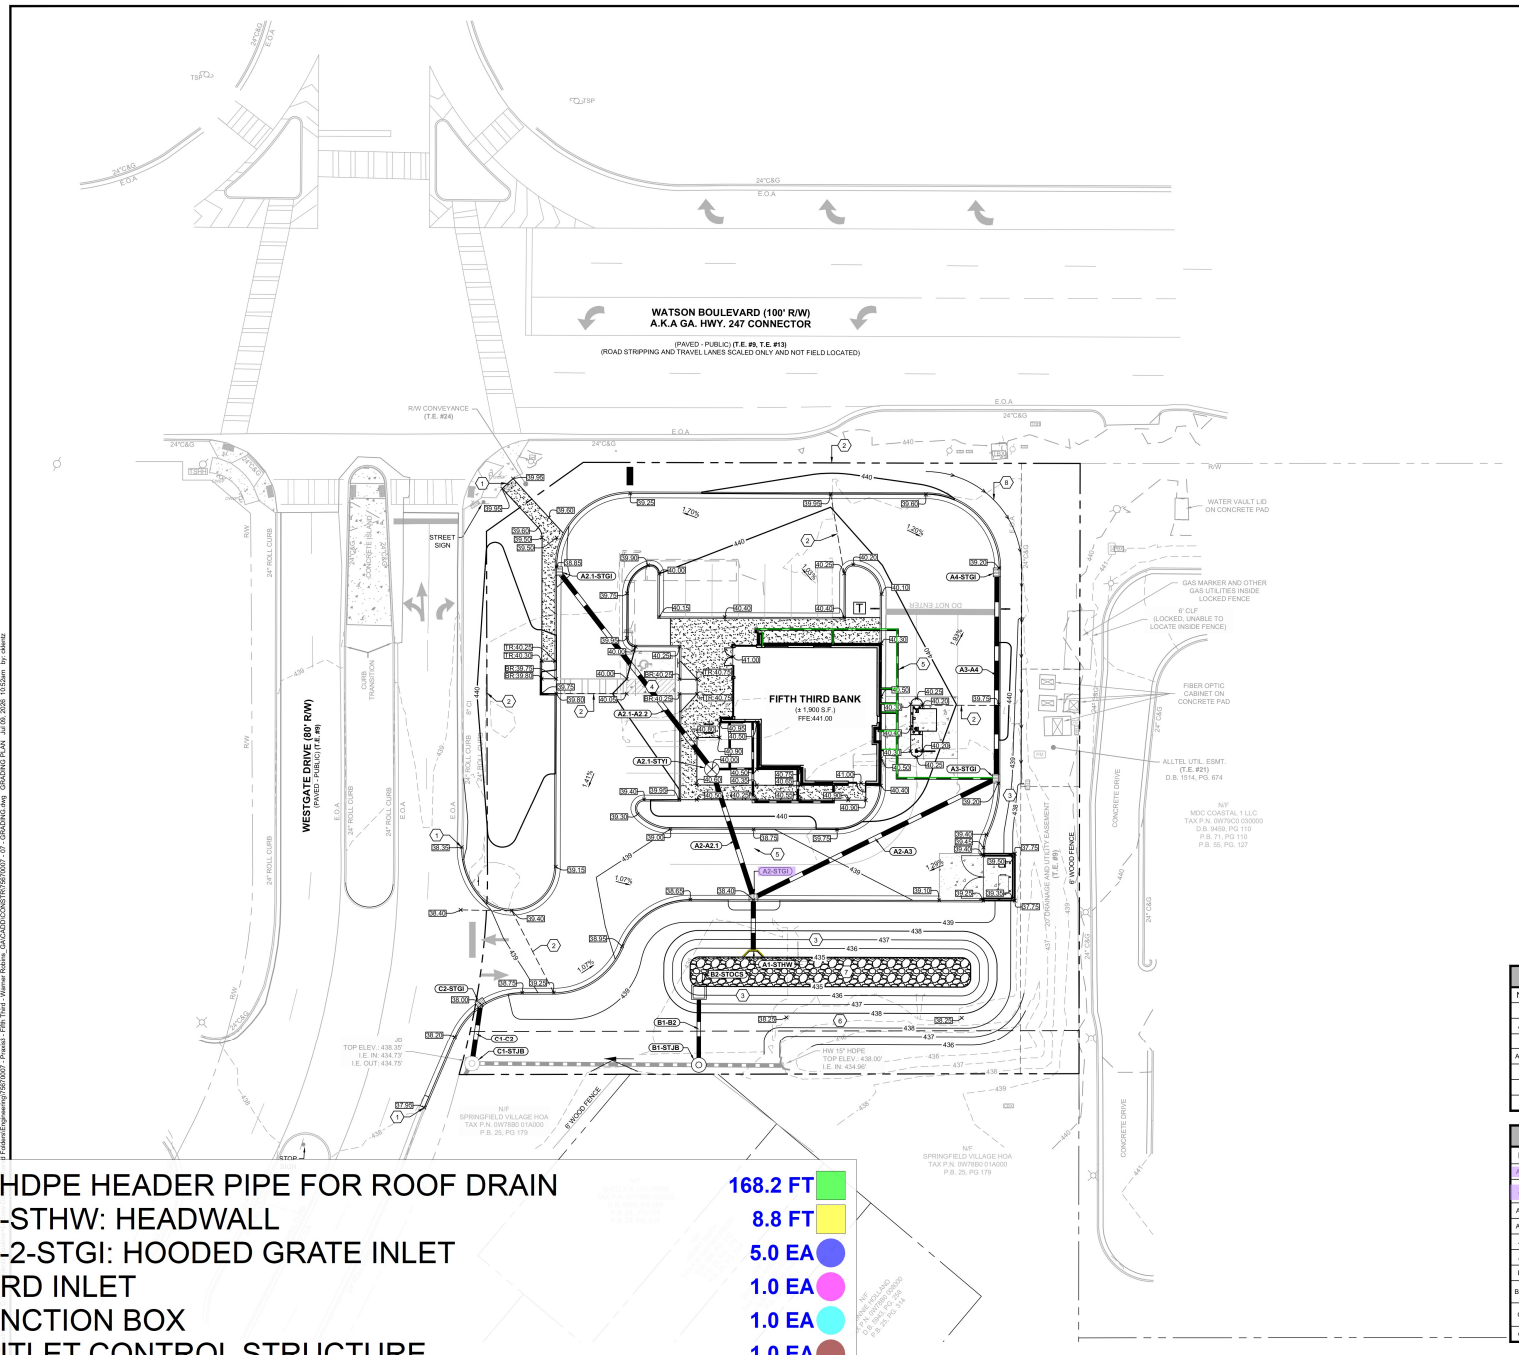

8" HDPE HEADER PIPE FOR ROOF DRAIN — 168.2 FT
A1-STHW: HEADWALL — 8.8 FT
A2-2-STGI: HOODED GRATE INLET — 5.0 EA
YARD INLET — 1.0 EA
JUNCTION BOX — 1.0 EA
OUTLET CONTROL STRUCTURE — 1.0 EA

GENERAL GRADING NOTES

1) ALL CRITICAL SPOT GRADES ALONG CURB ARE BOTTOM OF CURB ELEVATIONS UNLESS OTHERWISE SPECIFIED.

2) NO SLOPES ARE TO BE STEEPER THAN 2:1.

3) ALL LAND DISTURBANCE TO BE STABILIZED WITH VEGETATION UPON COMPLETION OF DEMOLITION.

4) BOUNDARY & TOPOGRAPHIC INFORMATION FROM SURVEY BY GASKINS+LECRAW, A PAPE DAWSON COMPANY, DATED 05.06.2026.

5) FLOOD PLAIN IS NOT PRESENT ON THIS SITE AS SHOWN ON THE FEMA FIRM MAP NUMBER 13153C0085E, DATED 09.28.2007.

6) EROSION AND SEDIMENT CONTROL MEASURES ARE TO BE ACCOMPLISHED PRIOR TO ANY OTHER CONSTRUCTION ON THE SITE AND MAINTAINED UNTIL PERMANENT GROUND COVER IS ESTABLISHED.

7) OWNER IS RESPONSIBLE FOR MAINTENANCE OF ALL STORM SEWER ON PRIVATE PROPERTY.

8) THE OWNER IS RESPONSIBLE FOR OBTAINING ANY NECESSARY AGREEMENTS FROM ADJACENT PROPERTY OWNERS IN ORDER TO PERFORM THE REQUIRED OFFSITE WORK, INCLUDING, STORM DRAINAGE, CURB AND GUTTER AND PAVEMENT TIE-INS AND GRADING.

9) VERTICAL DEPTH OF ALL DRY AND PRESSURIZED UTILITIES IS UNKNOWN. CONTRACTOR TO NOTIFY OWNER AND ENGINEER IMMEDIATELY IF ANY CONFLICTS ARE FOUND.

10) SIDEWALKS ADJACENT TO BUILDING AND ALONG ADA ROUTES TO HAVE MAXIMUM CROSS SLOPE OF 2%.

KEY NOTES

1	CONTRACTOR TO TIE INTO AND MATCH EXISTING GRADE
2	RIDGE LINE
3	3:1 SLOPE
4	ADA PARKING AREA, MAXIMUM SLOPE OF 2% IN ANY DIRECTION
5	8" HDPE HEADER PIPE FOR ROOF DRAIN CONNECTION, MINIMUM SLOPE OF 1%
6	5' WIDE DAM, TOP OF DAM ELEVATION: 438.25
7	INFILTRATION BASIN. REFER TO SHEET C-4.2 FOR DETAIL
7	CONTRACTOR TO FINE GRADE 2' WIDE DRAINAGE SWALE @ 1% MIN. SLOPE

SPOT ELEVATION LEGEND

BR: BOTTOM OF RAMP
BW: BOTTOM OF WALL
LP: LOW POINT
TR: TOP OF RAMP
TW: TOP OF WALL
HP: HIGH POINT
*ALL CRITICAL SPOT GRADES ALONG CURB ARE BOTTOM OF CURB ELEVATIONS UNLESS OTHERWISE SPECIFIED.

STRUCTURE TYPES

STSWCB:	GDOT STD 1033D	STDWCB:	GDOT STD 1034D
STSWCB:	GDOT STD 1019A TYPE A	STYI:	NYOPLAST INLET W/DOME
STGI:	GDOT STD 1019A TYPE E	STFE:	GDOT STD 1120
STHW:	GDOT STD 1001B HEADWALL	STOCS:	SEE DETAILS SHEET C-6.2

DEFINITION OF STRUCTURE SPOT ELEVATIONS

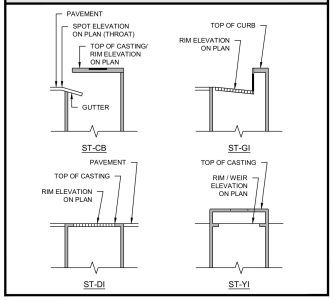

STORM PIPES

NAME:	SIZE:	LENGTH:	SLOPE:	INV UP:	INV DOWN:	MATERIAL:
A1-A2	18"	17.69	0.50%	435.09 (A2-STGI)	435.00 (A1-STHW)	HDPE
A2-A2.1	18"	45.97	0.50%	435.32 (A2.1-STYI)	435.09 (A2-STGI)	HDPE
A2-A3	18"	92.25	0.50%	435.55 (A3-STGI)	435.09 (A2-STGI)	HDPE
A2.1-A2.2	18"	85.26	0.50%	435.74 (A2.2-STGI)	435.32 (A2.1-STYI)	HDPE
A3-A4	18"	70.17	0.50%	435.90 (A4-STGI)	435.55 (A3-STGI)	HDPE
B1-B2	15"	25.11	0.50%	435.00 (B2-STOCS)	434.87 (B1-STJB)	HDPE
C1-C2	18"	21.08	0.50%	434.86 (C2-STGI)	434.75 (C1-STJB)	HDPE

STORM STRUCTURES

NAME:	TYPE:	STATION:	RIM:	INV IN: (PIPE)	INV OUT: (PIPE)
A1-STHW	HEADWALL	0+00.00	435.82	435.00 (A1-A2)	
A2-STGI	HOODED GRATE INLET	0+17.69	438.40	435.09 (A2-A2.1) 435.09 (A2-A3)	435.09 (A1-A2)
A2.1-STYI	YARD INLET	0+45.97	440.00	435.32 (A2.1-A2.2)	435.32 (A2-A2.1)
A2.2-STGI	HOODED GRATE INLET	1+31.22	438.85		435.74 (A2.1-A2.2)
A3-STGI	HOODED GRATE INLET	1+09.95	439.20	435.55 (A3-A4)	435.55 (A2-A3)
A4-STGI	HOODED GRATE INLET	1+80.11	439.20		435.90 (A3-A4)
B1-STJB	JUNCTION BOX	0+00.00	438.25	434.87 (B1-B2)	
B2-STOCS	OUTLET CONTROL STRUCTURE	0+25.11	435.67		435.00 (B1-B2)
C1-STJB	JUNCTION BOX (EXISTING)	0+00.00	438.40	434.75 (C1-C2)	
C2-STGI	HOODED GRATE INLET	0+21.08	438.01		434.86 (C1-C2)

PREPARED IN THE OFFICE OF:
GASKINS +LECRAW
a PAPE-DAWSON company

© 2026 GASKINS + LECRAW

3475 CORPORATE WAY
SUITE A
DULUTH, GA 30096
PHONE - 678.546.8100
www.gaskinslecraw.com
PEF008127

REVISIONS:

NO.	DATE	DRAWN BY:	CHECKED BY:
1			

CLIENT
PRAXIS3
100 PEACHTREE STREET NW, SUITE 1450, ATLANTA, GEORGIA 30303

PROJECT
FIFTH THIRD BANK - WARNER ROBINS, GA
2711 WATSON BLVD
PARCEL ID: 0W0780-005000
WARNER ROBINS, HOUSTON COUNTY, GEORGIA

SEAL:
GEORGIA REGISTERED
No. PE036681
PROFESSIONAL ENGINEER
TIMOTHY KYLE SHARPE
7/9/2026

CALL BEFORE YOU DIG
811
Know what's below. Call before you dig.

SCALE & NORTH ARROW:
NORTH ARROW
0' 10' 20' 40'
SCALE: 1" = 20'

DESIGN INFO:

DRAWN BY:	JOA
DESIGNED BY:	MAT
REVIEWED BY:	TKS
JOB #:	75670007
DATE:	JULY 9, 2026

GRADING PLAN
C-4.0

eCraw, a Pape-Dawson Company shall be without liability to Gaskins + LeCraw, a Pape-Dawson Company. Copyright Gaskins + LeCraw, a Pape-Dawson Company, 2026

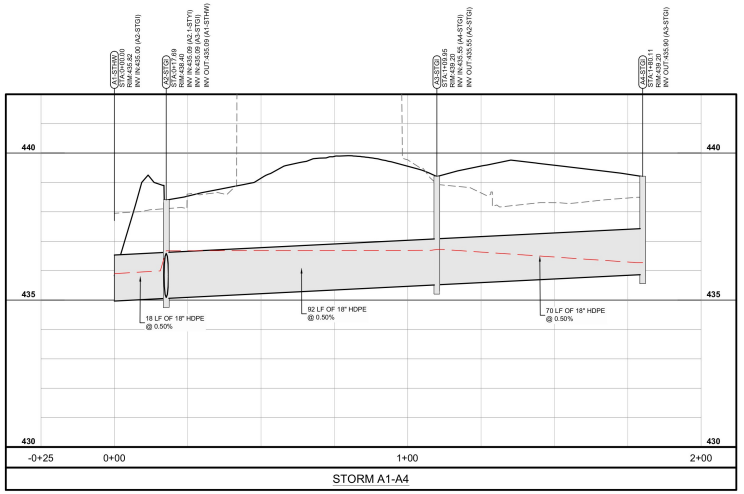

STORM A1-A4

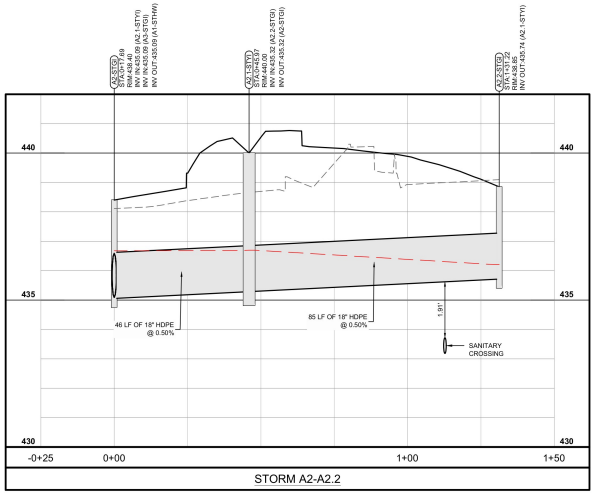

STORM A2-A2.2

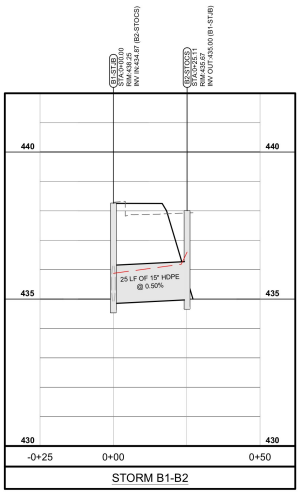

STORM B1-B2

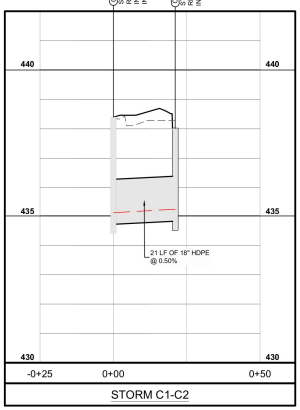

STORM C1-C2

HORIZONTAL SCALE IN FEET
0' 10' 20' 40'
SCALE: 1" = 20'

VERTICAL SCALE IN FEET
SCALE: 1" = 2'

STRUCTURE TYPES

STSWCB:	GDOT STD 1033D	STDWCB:	GDOT STD 1034D
STSWCB:	GDOT STD 1019A TYPE A	STYI:	NYOPLAST W/DOME
STGI:	GDOT STD 1019A TYPE E	STFE:	GDOT STD 1120
STHW:	GDOT STD 1001B HEADWALL	STOCS:	SEE DETAILS SHEET C-6.2

PROFILE LEGEND

EXISTING GRADE:

PROPOSED GRADE:

100 YR. HGL:

Storm Sewer Tabulation

Page 1

Station Line	To Line	Len (ft)	Drng Area Incr (ac)	Drng Area Total (ac)	Rnoff coeff (C)	Area x C Incr	Area x C Total	Tc Inlet (min)	Tc Syst (min)	Rain (I) (in/hr)	Total flow (cfs)	Cap full (cfs)	Vel (ft/s)	Pipe Size (in)	Pipe Slope (%)	Invert Elev Dn (ft)	Invert Elev Up (ft)	HGL Elev Dn (ft)	HGL Elev Up (ft)	Grnd / Rim Elev Dn (ft)	Grnd / Rim Elev Up (ft)	Line ID
1	End	7	692	0.22	0.55	0.90	0.20	0.50	5.0	7.1	11.0	5.44	3.11	4.91	18	0.51	435.00	435.09	435.90	435.99	437.03	438.40	A1-A2
2	1	92	253	0.07	0.16	0.90	0.06	0.14	5.0	5.6	11.9	1.71	3.03	1.08	18	0.50	435.09	435.55	436.68	436.69	438.40	439.20	A2-A3
3	2	70	167	0.09	0.09	0.90	0.08	0.08	5.0	5.0	12.4	1.00	3.03	1.80	18	0.50	435.55	435.90	436.72	436.27	439.20	439.20	A3-A4
4	1	45	966	0.03	0.17	0.90	0.03	0.15	5.0	5.7	11.9	1.82	3.05	1.05	18	0.50	435.09	435.32	436.68	436.68	438.40	440.00	A2-A2.1
5	4	85	257	0.14	0.14	0.90	0.13	0.13	5.0	5.0	12.4	1.56	7.98	2.11	18	0.49	435.32	435.74	436.70	436.21	440.00	438.94	A2.1-A2.
6	End	1	076	0.10	0.10	0.90	0.09	0.09	5.0	5.0	12.4	1.11	9.22	3.01	18	0.52	434.75	434.86	435.14	435.25	438.40	438.06	C1-C2
7	End	5	110	0.01	0.01	0.01	0.00	0.00	5.0	5.0	12.4	6.20	5.03	5.51	15	0.52	434.87	435.00	435.87	436.18	438.25	438.00	B1-B2

Project File: 75670007 - QAQC.stm | Number of lines: 7 | Run Date: 7/9/2026

NOTES:Intensity = 55.26 / (Inlet time + 5.30) ^ 0.64. Return period =Yrs. 100 ; c = cir e = ellip b = box

Storm Sewers v2024.00

Inlet Report

Page 1

Line No	Inlet ID	Q = CIA (cfs)	Q carry (cfs)	Q capt (cfs)	Q Byp (cfs)	Junc Type	Curb Inlet Ht (in)	Curb Inlet L (ft)	Grate Inlet Area (sq/ft)	Grate Inlet L (ft)	Grate Inlet W (ft)	Gutter So (ft/ft)	Gutter W (ft)	Gutter Sw (ft/ft)	Gutter Sx (ft/ft)	Gutter n	Inlet Depth (ft)	Inlet Spread (ft)	Inlet Depth (ft)	Inlet Spread (ft)	Inlet Depr (in)	Byp Line No
1	A2-STGI	2.45	0.00	2.45	0.00	Comb	3.0	4.00	2.24	2.42	1.42	Sag	1.50	0.060	0.020	0.000	0.26	9.99	0.26	9.99	0.0	Off
2	A3-STGI	0.78	0.00	0.78	0.00	Comb	3.0	4.00	2.24	2.42	1.42	Sag	1.50	0.030	0.020	0.000	0.12	5.11	0.12	5.11	0.0	Off
3	A4-STGI	1.00	0.00	1.00	0.00	Comb	3.0	4.00	2.24	2.42	1.42	Sag	1.50	0.060	0.020	0.000	0.17	5.30	0.17	5.30	0.0	Off
4	A2.1-ST	0.33	0.00	0.33	0.00	DrGrt	0.0	1.63	1.22	1.63	1.63	Sag	2.00	0.020	0.020	0.000	0.07	8.62	0.07	8.62	0.0	Off
5	A2.2-ST	1.56	0.00	1.56	0.00	Comb	3.0	4.00	2.24	2.42	1.42	Sag	1.50	0.060	0.020	0.000	0.21	7.27	0.21	7.27	0.0	Off
6	C2-STGI	1.11	0.00	1.11	0.00	Comb	3.0	4.00	2.24	2.42	1.42	Sag	1.50	0.060	0.020	0.000	0.17	5.72	0.17	5.72	0.0	Off
7	B2-STO	6.20*	0.00	0.00	6.20	MH	0.0	0.00	0.00	0.00	0.00	Sag	0.00	0.000	0.000	0.000	0.00	0.00	0.00	0.00	0.0	Off

Project File: 75670007 - QAQC.stm | Number of lines: 7 | Run Date: 7/9/2026

NOTES: Inlet N-Values = 0.016; Intensity = 55.28 / (Inlet time + 5.30) ^ 0.64. Return period = 100 Yrs. ; * Indicates Known Q added. All curb inlets are throat.

Storm Sewers v2024.00

PREPARED IN THE OFFICE OF:
GASKINS + LECRAW
a PAPE-DAWSON company

© 2026 GASKINS + LECRAW

3475 CORPORATE WAY
SUITE A
DULUTH, GA 30096
PHONE - 678.546.8100
www.gaskinslecraw.com
PEF008127

REVISIONS:

NO.	DATE	DRAWN BY	CHECKED BY
1			

CLIENT
PRAXIS3
100 PEACHTREE STREET NW, SUITE 1450, ATLANTA, GEORGIA 30303

PROJECT
FIFTH THIRD BANK - WARNER ROBINS, GA
2711 WATSON BLVD
PARCEL ID: 0W0780-005000
WARNER ROBINS, HOUSTON COUNTY, GEORGIA

SEAL:

GEORGIA REGISTERED ENGINEER
No. PE036681
PROFESSIONAL
TIMOTHY KYLE SHARPE
7/9/2026

CALL BEFORE YOU DIG

811
Know what's below.
Call before you dig.

SCALE & NORTH ARROW:

DESIGN INFO:

DRAWN BY:	JOA
DESIGNED BY:	MAT
REVIEWED BY:	TKS
JOB #:	75670007
DATE:	JULY 9, 2026

STORM PROFILES

C-4.1

This document, together with the concepts and designs presented herein, as an instrument of service, is intended only for the specific purpose and client for which it was prepared. Reuse of and improper reliance on this document without written authorization and adaptation by Gaskins + LeCraw, a Pape-Dawson Company shall be without liability to Gaskins + LeCraw, a Pape-Dawson Company. Copyright Gaskins + LeCraw, a Pape-Dawson Company, 2026

Drawing name: C:\Users\kdietz\Gaskins+LeCraw Dropbox\Shared Folders\Engineering\75670007 - Praxis3 - Fifth Third - Warner Robins, GA\CAD\CIVIL\75670007 - 09 - PROFILES.dwg, STORM PROFILES, Jul 09, 2026 10:53am, by kdietz

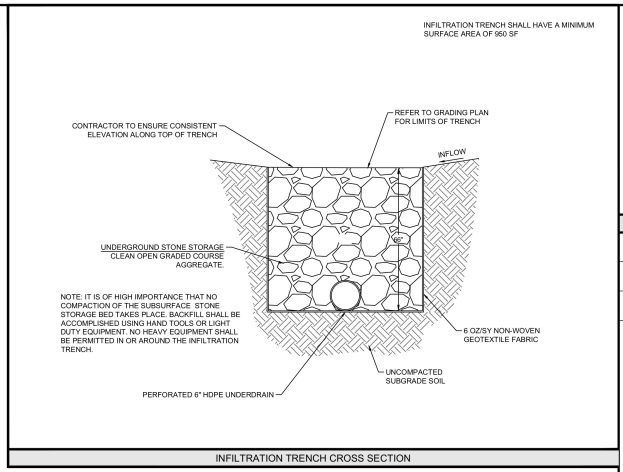

INFILTRATION TRENCH CROSS SECTION

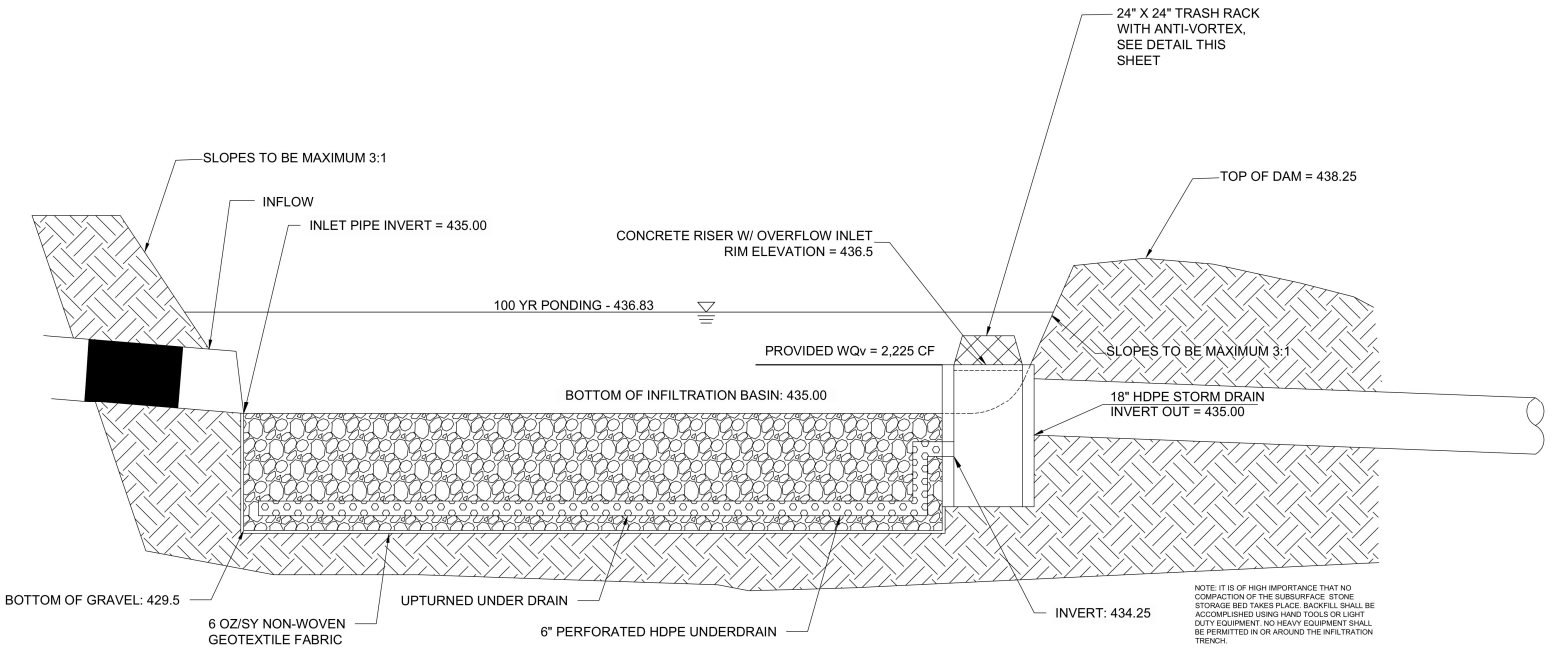

INFILTRATION BASIN DETAIL

PREPARED IN THE OFFICE OF:
GASKINS + LECRAW
a PAPE-DAWSON company
© 2026 GASKINS + LECRAW
3475 CORPORATE WAY
SUITE A
DULUTH, GA 30096
PHONE - 678.546.8100
www.gaskinslecraw.com
PEF008127

REVISIONS:

NO.	DATE	DRAWN BY	CHECKED BY
1			

CLIENT
PRAXIS3
100 PEACHTREE STREET NW, SUITE 1450, ATLANTA, GEORGIA 30303

PROJECT
FIFTH THIRD BANK - WARNER ROBINS, GA
2711 WATSON BLVD
PARCEL ID: 0W0780-005000
WARNER ROBINS, HOUSTON COUNTY, GEORGIA

SEAL:
GEORGIA REGISTERED ENGINEER
No. PE036681
PROFESSIONAL
TIMOTHY KYLE SHARPE
7/9/2026

CALL BEFORE YOU DIG
811
Know what's below. Call before you dig.

SCALE & NORTH ARROW:
NORTH ARROW
SCALE: 1" = 20'

DESIGN INFO:

DRAWN BY:	JOA
DESIGNED BY:	MAT
REVIEWED BY:	TKS
JOB #:	75670007
DATE:	JULY 9, 2026

INFILTRATION BASIN DETAIL

C-4.2

This document, together with the concepts and designs presented herein, as an instrument of service, is intended only for the specific purpose and client for which it was prepared. Reuse of and improper reliance on this document without written authorization and adaptation by Gaskins + LeCraw, a Pape-Dawson Company shall be without liability to Gaskins + LeCraw, a Pape-Dawson Company. Copyright Gaskins + LeCraw, a Pape-Dawson Company, 2026

Drawing name: C:\Users\JoeA\Gaskins+LeCraw Dropbox\Shared Folders\Engineering\75670007 - Praxis3 - Fifth Third - Warner Robins, GA\CAD\CONSTRUCTION\75670007_07 - GRADING.dwg INFILTRATION BASIN DETAIL Jul 09, 2026 11:05am by JoeA

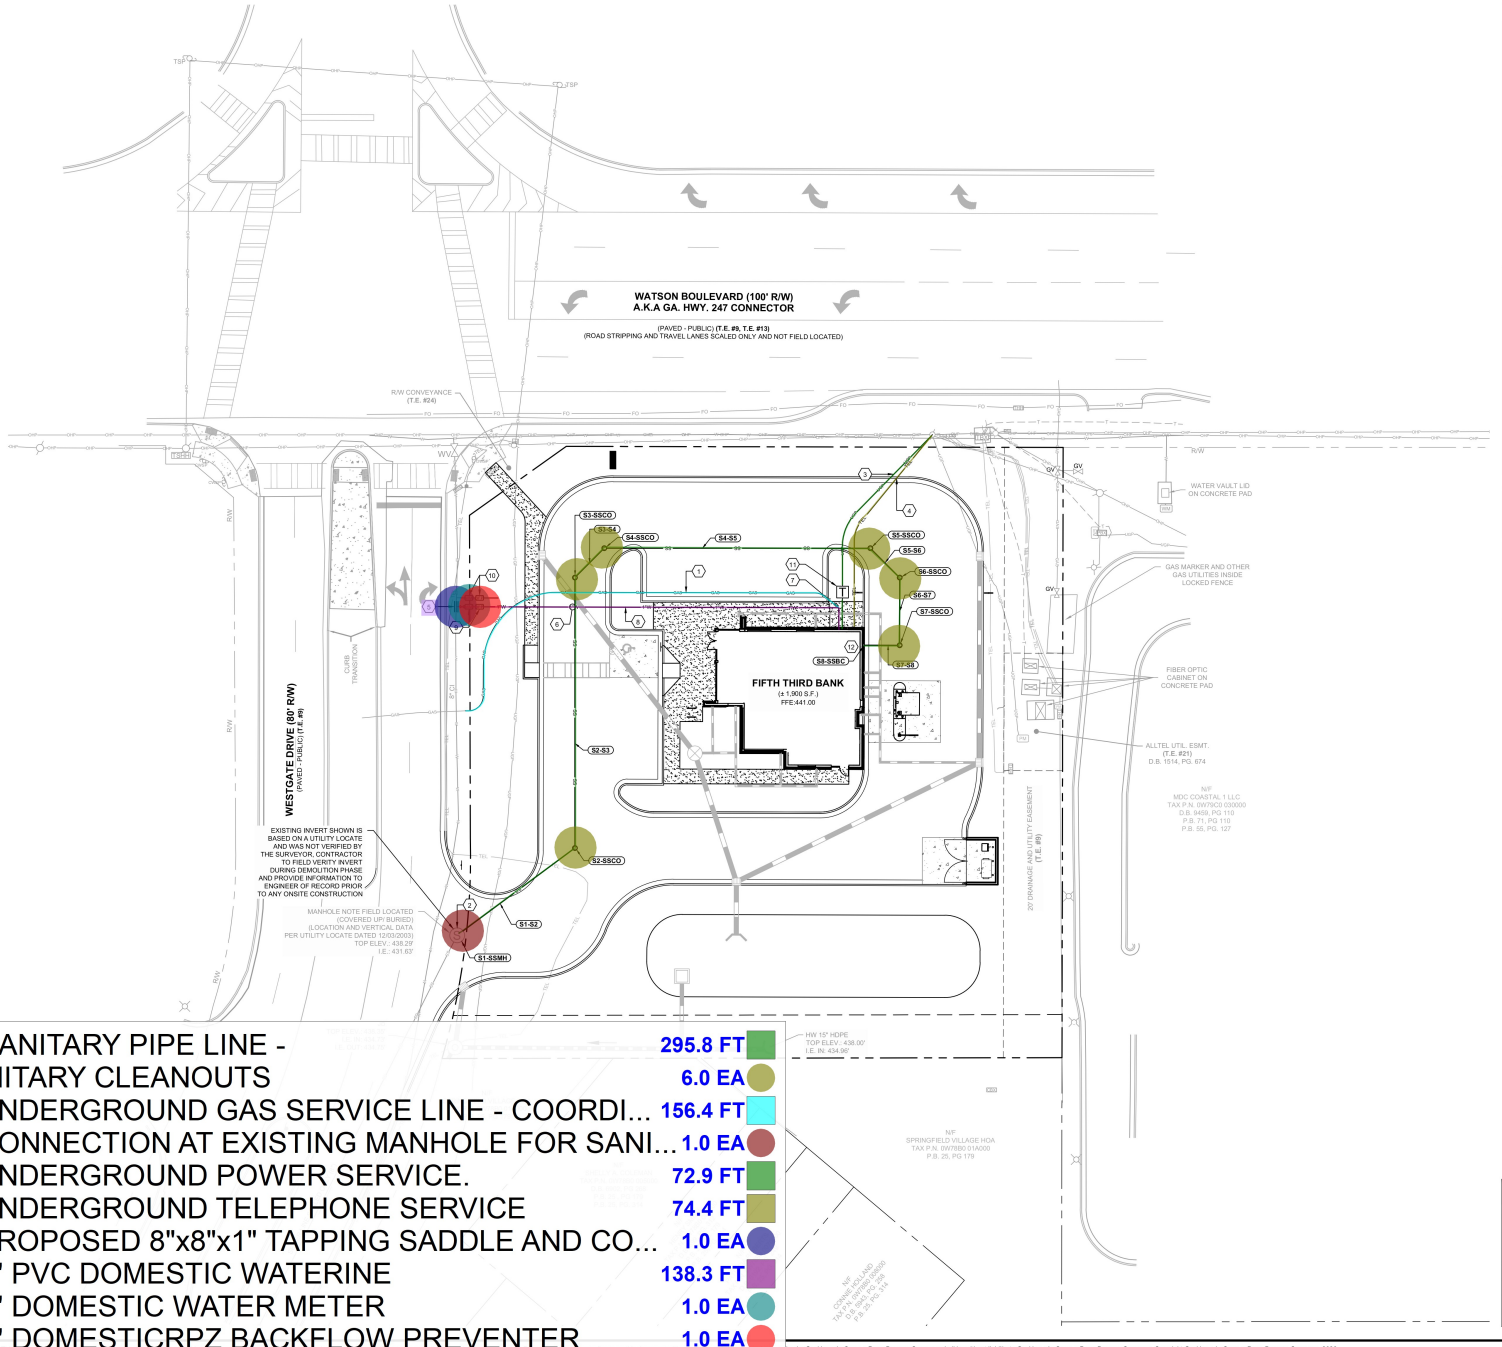

6" SANITARY PIPE LINE -	295.8 FT
SANITARY CLEANOUTS	6.0 EA
1: UNDERGROUND GAS SERVICE LINE - COORDI...	156.4 FT
2: CONNECTION AT EXISTING MANHOLE FOR SANI...	1.0 EA
3: UNDERGROUND POWER SERVICE.	72.9 FT
4: UNDERGROUND TELEPHONE SERVICE	74.4 FT
5: PROPOSED 8"x8"x1" TAPPING SADDLE AND CO...	1.0 EA
8: 1" PVC DOMESTIC WATERINE	138.3 FT
9: 1" DOMESTIC WATER METER	1.0 EA
9: 1" DOMESTICRPZ BACKFLOW PREVENTER	1.0 EA

GENERAL UTILITY NOTES

1.) CONTRACTOR TO NOTIFY OWNER/DEVELOPER AND ENGINEER IMMEDIATELY IF FIELD CONDITIONS DIFFER FROM DESIGN ASSUMPTIONS.

2.) LOCATION OF UNDERGROUND UTILITIES SHOWN IS BASED ON A SURVEY BY GASKINS+LECRAW, A PAPE DAWSON COMPANY, DATED 05.08.2026. APPROPRIATE UTILITY COMPANIES SHOULD BE CONTACTED FOR VERIFICATION OF LOCATIONS PRIOR TO ANY CONSTRUCTION ACTIVITY.

3.) MAINTAIN 10' HORIZONTAL SEPARATION BETWEEN WATER AND SEWER LINES.

4.) REFER TO ARCH/MEP PLANS FOR ON SITE UTILITY CONDUITS FOR SITE LIGHTING, ETC. AND UTILITY ENTRY AND EXIT LOCATIONS

5) VERTICAL DEPTH OF ALL DRY AND PRESSURIZED UTILITIES IS UNKNOWN. CONTRACTOR TO NOTIFY OWNER AND ENGINEER IMMEDIATELY IF ANY CONFLICTS ARE FOUND.

KEY NOTES

1	UNDERGROUND GAS SERVICE; CONTRACTOR TO COORDINATE WITH UTILITY PROVIDER FOR EXACT LOCATION AND CONTINUATION
2	LOCATION OF EXISTING MANHOLE FOR PROPOSED SANITARY SEWER CONNECTION. CORE MANHOLE FROM INSIDE AT INVERT ELEVATION SHOWN AND GROUT WATER TIGHT. CONTRACTOR TO CONFIRM EXISTING MANHOLE LOCATION AND INVERT ELEVATION AND SHALL NOTIFY ENGINEER IF FIELD CONDITIONS DIFFER FROM DESIGN CONDITIONS.
3	UNDERGROUND POWER SERVICE; CONTRACTOR TO COORDINATE WITH UTILITY PROVIDER FOR EXACT LOCATION AND CONTINUATION.
4	UNDERGROUND TELEPHONE SERVICE; CONTRACTOR TO COORDINATE WITH UTILITY PROVIDER FOR EXACT LOCATION AND CONTINUATION
5	PROPOSED 8"X8"X1" TAPPING SADDLE AND CORPORATION STOP
6	CONTRACTOR TO BEND WATER LINE AS NECESSARY TO ENSURE VERTICAL CLEARANCE
7	HORIZONTAL PIPE BEND, ALL BENDS TO BE MADE WITH 2 - 45°
8	1" PVC DOMESTIC WATER LINE
9	1" DOMESTIC WATER METER AND RPZ BACKFLOW PREVENTER PER UTILITY PROVIDER STANDARDS AND SPECIFICATIONS
10	CONTRACTOR TO REUSE EXISTING 1" IRRIGATION WATER METER. CONTRACTOR SHALL REPLACE EXISTING METER IF REQUIRED WITH NEW 1" IRRIGATION WATER METER AND RPZ BACKFLOW PREVENTER PER UTILITY PROVIDER STANDARDS AND SPECIFICATIONS
11	PROPOSED TRANSFORMER PAD PER UTILITY PROVIDER STANDARDS AND SPECIFICATIONS
12	REFER TO ARCH PLANS FOR ALL LOCATIONS AND INTERNAL CONNECTIONS

STRUCTURE TYPES

SSCO: CLEANOUT SSMH: MANHOLE
SSBC: BULDING CONNECTION

CAUTION

THE UTILITES SHOWN ARE SHOWN FOR THE CONTRACTORS CONVENIENCE ONLY. THERE MAY BE OTHER UTILITIES NOT SHOWN ON THESE PLANS. THE ENGINEER ASSUMES NO RESPONSIBILITY FOR THE LOCATIONS OF UNDERGROUND UTILITIES. AND IT SHALL BE THE CONTRACTORS RESPONSIBILITY TO VERIFY THE LOCATIONS OF ALL UTILITIES SHOWN AS WELL AS THOSE NOT SHOWN WITHIN THE CONSTRUCTION LIMITS. ALL DAMAGE MADE TO EXISTING UTILITIES BY THE CONTRACTOR SHALL BE THE RESPONSIBILITY OF THE CONTRACTOR.

SANITARY STRUCTURES

NAME:	TYPE:	STATION:	RIM:	INV IN: (PIPE)	INV OUT: (PIPE)
S1-SSMH	MANHOLE (EXISTING)	0+00.00	438.31	431.85 (S1-S2)	
S2-SSCO	CLEANOUT	0+49.92	439.06	432.35 (S2-S3)	432.35 (S1-S2)
S3-SSCO	CLEANOUT	1+41.96	439.39	433.27 (S3-S4)	433.27 (S2-S3)
S4-SSCO	CLEANOUT	1+56.10	439.66	433.41 (S4-S5)	433.41 (S3-S4)
S5-SSCO	CLEANOUT	2+46.80	439.96	434.32 (S5-S6)	434.32 (S4-S5)
S6-SSCO	CLEANOUT	2+60.94	439.86	434.46 (S6-S7)	434.46 (S5-S6)
S7-SSCO	CLEANOUT	2+83.96	440.12	434.69 (S7-S8)	434.69 (S6-S7)
S8-SSBC	BLDG CONNECTION	2+95.96	440.37		434.81 (S7-S8)

SANITARY PIPES

NAME:	SIZE:	LENGTH:	SLOPE:	INV UP:	INV DOWN:	MATERIAL:
S1-S2	6"	49.92	1.00%	432.35 (S2-SSCO)	431.85 (S1-SSMH)	PVC
S2-S3	6"	92.03	1.00%	433.27 (S3-SSCO)	432.35 (S2-SSCO)	PVC
S3-S4	6"	14.14	1.00%	433.41 (S4-SSCO)	433.27 (S3-SSCO)	PVC
S4-S5	6"	90.70	1.00%	434.32 (S5-SSCO)	433.41 (S4-SSCO)	PVC
S5-S6	6"	14.14	1.00%	434.46 (S6-SSCO)	434.32 (S5-SSCO)	PVC
S6-S7	6"	23.03	1.00%	434.69 (S7-SSCO)	434.46 (S6-SSCO)	PVC
S7-S8	6"	12.00	1.00%	434.81 (S8-SSBC)	434.69 (S7-SSCO)	PVC

PREPARED IN THE OFFICE OF:
GASKINS +LECRAW
a PAPE-DAWSON company
© 2026 GASKINS + LECRAW
3475 CORPORATE WAY
SUITE A
DULUTH, GA 30096
PHONE - 678.546.8100
www.gaskinslecraw.com
PEF008127

REVISIONS:

NO. #	DATE	DRAWN BY	CHECKED BY
1			

CLIENT
PRAXIS3
100 PEACHTREE STREET NW, SUITE 1450, ATLANTA, GEORGIA 30303

PROJECT
FIFTH THIRD BANK - WARNER ROBINS, GA
2711 WATSON BLVD
PARCEL ID: 0W0780-005000
WARNER ROBINS, HOUSTON COUNTY, GEORGIA

SEAL:
GEORGIA REGISTERED No. PE036681 PROFESSIONAL ENGINEER TIMOTHY KYLE SHARPE
7/9/2026

CALL BEFORE YOU DIG
811 Know what's below. Call before you dig.

SCALE & NORTH ARROW:
NORTH ARROW
0' 10' 20' 40'
SCALE: 1" = 20'

DESIGN INFO:

DRAWN BY:	JOA
DESIGNED BY:	MAT
REVIEWED BY:	TKS
JOB #:	75670007
DATE:	JULY 9, 2026

UTILITY PLAN

C-5.0

...ion by Gaskins + LeCraw, a Pape-Dawson Company shall be without liability to Gaskins + LeCraw, a Pape-Dawson Company. Copyright Gaskins + LeCraw, a Pape-Dawson Company, 2026

File: Third - Warner Robins_GA\CAD\CONSTR\75670007 - 08 - UTILITY.dwg UTILITY PLAN Jul 09, 2026 10:52am by: cbarns

HORIZONTAL SCALE: IN FEET

0' 10' 20' 40'

SCALE: 1" = 20'

VERTICAL SCALE: IN FEET

SCALE: 1" = 2'

STRUCTURE TYPES

SSCO:	CLEANOUT	SSDD:	DUMPSTER DRAIN
SSMH:	MANHOLE	SSGT:	GREASE TRAP
SSBC:	BUILDING CONNECTION	SSSW:	SAMPLING WELL

PROFILE LEGEND

EXISTING GRADE:

PROPOSED GRADE:

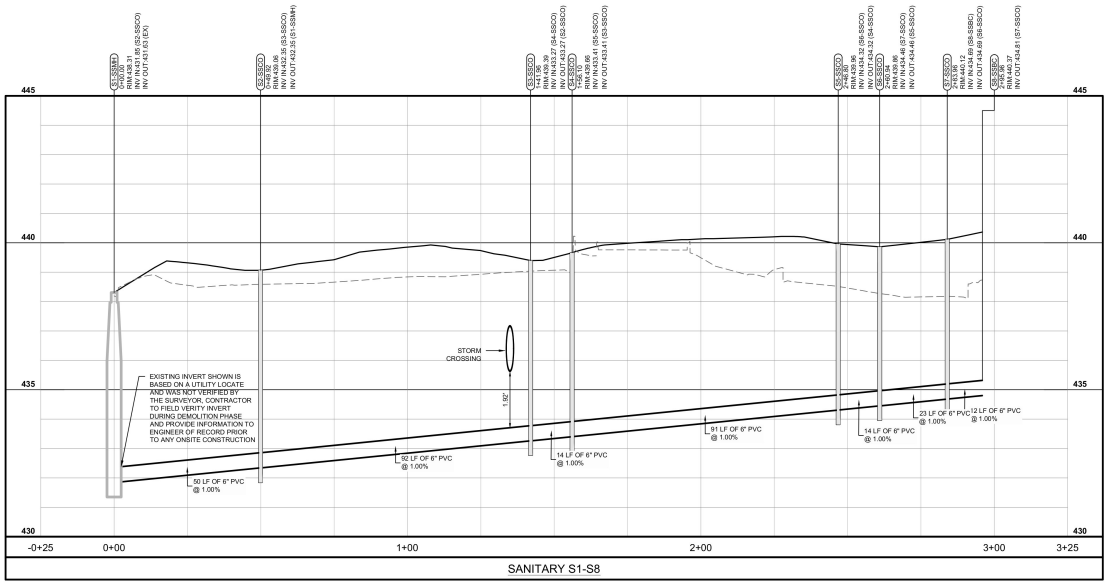

SANITARY S1-S8

PREPARED IN THE OFFICE OF:

GASKINS + LECRAW
a PAPE-DAWSON company

© 2026 GASKINS + LECRAW

3475 CORPORATE WAY
SUITE A
DULUTH, GA 30096
PHONE - 678.546.8100
www.gaskinslecraw.com
PEF008127

REVISIONS:

REV. #	DATE	DRAWN BY	CHECKED BY
1			

CLIENT
PRAXIS3
100 PEACHTREE STREET NW, SUITE 1450, ATLANTA, GEORGIA 30303

PROJECT
FIFTH THIRD BANK - WARNER ROBINS, GA
2711 WATSON BLVD
PARCEL ID: 0W0780-005000
WARNER ROBINS, HOUSTON COUNTY, GEORGIA

SEAL:

GEORGIA REGISTERED ENGINEER
No. PE036681 PROFESSIONAL
ENGINEER
TIMOTHY KYLE SHARPE
7/9/2026

CALL BEFORE YOU DIG

811 Know what's below. Call before you dig.

SCALE & NORTH ARROW:

DESIGN INFO:

DRAWN BY:	JOA
DESIGNED BY:	MAT
REVIEWED BY:	TKS
JOB #:	75670007
DATE:	JULY 9, 2026

SANITARY PROFILES

C-5.1

This document, together with the concepts and designs presented herein, as an instrument of service, is intended only for the specific purpose and client for which it was prepared. Reuse of and improper reliance on this document without written authorization and adaptation by Gaskins + LeCraw, a Pape-Dawson Company shall be without liability to Gaskins + LeCraw, a Pape-Dawson Company. Copyright Gaskins + LeCraw, a Pape-Dawson Company, 2026

Drawing name: C:\Users\JAdair\Gaskins+LeCraw Dropbox\Shared Folders\Engineering\75670007 - Praxis3 - Fifth Third - Warner Robins, GA\CAD\CONSTR\75670007 - 09 - PROFILES.dwg, SANITARY PROFILES Jul 09, 2026, 10:53am, by JAdair

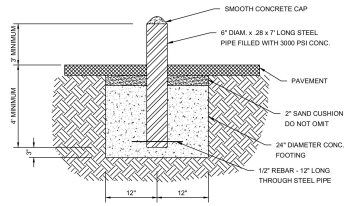

BOLLARD DETAIL

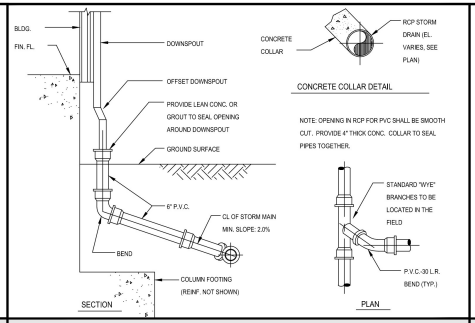

DOWNSPOUT CONNECTION DETAIL

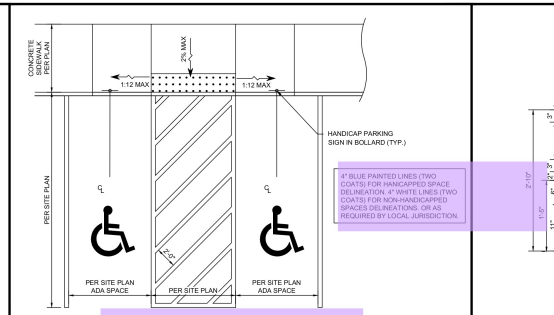

ADA PARKING DETAIL

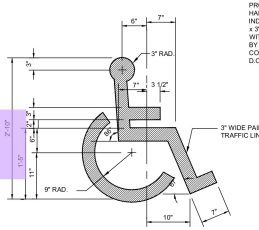

PROVIDE PAINTED SYMBOL IN ALL HANDICAPPED PARKING STALLS INDICATED ON SITE PLAN. PAINT 3'-0" x 3'-0" BLUE FIELD BACKGROUND WITH 3" WHITE BORDER OR AS REQ'D BY LOCAL H.C. CODE PAINT SHALL COMPLY WITH LOCAL OR STATE D.O.T. REQUIREMENTS.

ADA PARKING SYMBOL DETAIL

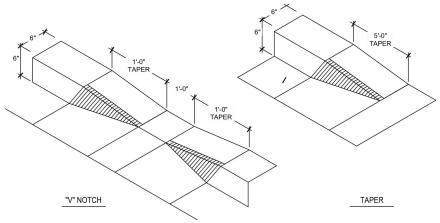

"V" NOTCH / TAPER CURB DETAIL

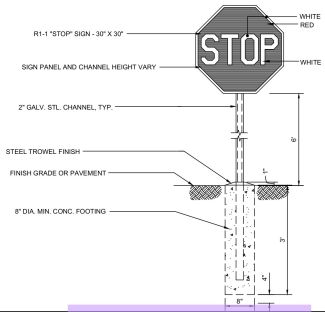

TRAFFIC SIGN MOUNTING DETAIL

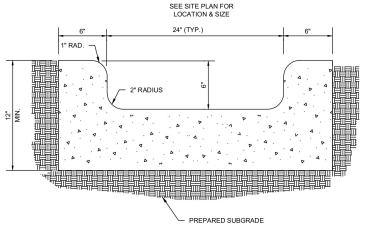

CONCRETE FLUME DETAIL

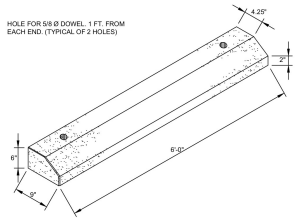

CONCRETE WHEELSTOP DETAIL

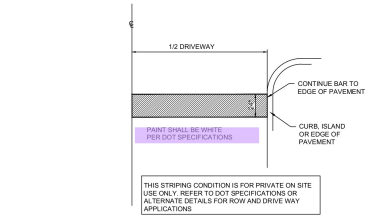

STOP BAR DETAIL

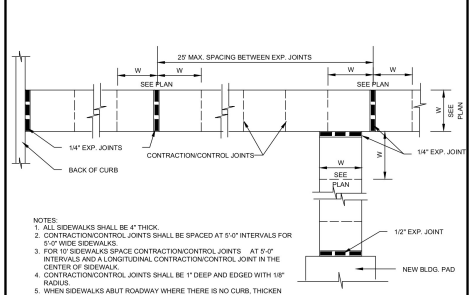

SIDEWALK DETAIL

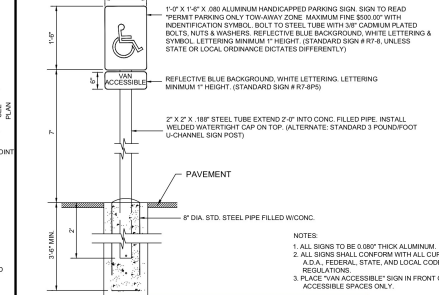

ADA SIGN MOUNTING DETAIL

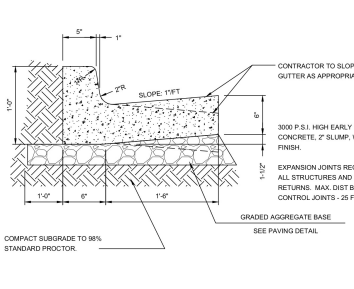

CURB & GUTTER DETAIL

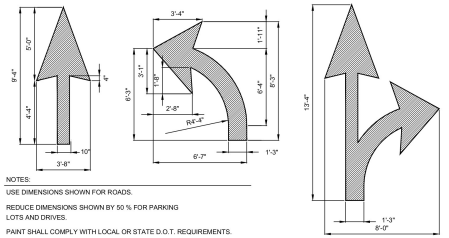

NOTES:
USE DIMENSIONS SHOWN FOR ROADS.
REDUCE DIMENSIONS SHOWN BY 50 % FOR PARKING LOTS AND DRIVES.
PAINT SHALL COMPLY WITH LOCAL OR STATE D.O.T. REQUIREMENTS.

PAVEMENT MARKING DETAIL

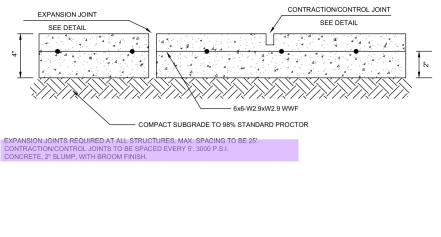

EXPANSION JOINTS REQUIRED AT ALL STRUCTURES, MAX. SPACING TO BE 25'. CONTRACTION/CONTROL JOINTS TO BE SPACED EVERY 9'. 3000 P.S.I. CONCRETE, 2" SLUMP, WITH BROOM FINISH.

SIDEWALK DETAIL

NOTE: CONTRACTOR TO CONFIRM COMPLIANCE WITH STATE OR LOCAL REQUIREMENTS.

ADA SIGN DETAIL

PREPARED IN THE OFFICE OF:
GASKINS +LECRAW
a PAPE-DAWSON company
© 2026 GASKINS + LECRAW
3475 CORPORATE WAY
SUITE A
DULUTH, GA 30096
PHONE - 678.546.8100
www.gaskinslecraw.com
PEF008127

REVISIONS:

NO.	DATE	DRAWN BY	CHECKED BY
1			

CLIENT
PRAXIS3
100 PEACHTREE STREET NW, SUITE 1450, ATLANTA, GEORGIA 30303

PROJECT
FIFTH THIRD BANK - WARNER ROBINS, GA
2711 WATSON BLVD
PARCEL ID: 0W0780-005000
WARNER ROBINS, HOUSTON COUNTY, GEORGIA

SEAL:
GEORGIA REGISTERED
No. PE036681
PROFESSIONAL
ENGINEER
TIMOTHY KYLE SHARPE
7/9/2026

CALL BEFORE YOU DIG
811
Know what's below. Call before you dig.

SCALE & NORTH ARROW:
DETAILS ARE NOT DRAWN TO SCALE

DESIGN INFO:

DRAWN BY:	JOA
DESIGNED BY:	MAT
REVIEWED BY:	TKS
JOB #	75670007
DATE:	JULY 9, 2026

CONSTRUCTION DETAILS - 1

C-6.0

This document, together with the concepts and designs presented herein, as an instrument of service, is intended only for the specific purpose and client for which it was prepared. Reuse of and improper reliance on this document without written authorization and adaptation by Gaskins + LeCraw, a Pape-Dawson Company shall be without liability to Gaskins + LeCraw, a Pape-Dawson Company. Copyright Gaskins + LeCraw, a Pape-Dawson Company, 2026

Drawing name: C:\Users\kdavis\Gaskins+LeCraw Dropbox\Shared Folders\Engineering\75670007 - Praxis3 - Fifth Third - Warner Robins, GA\CAD\CONSTR\75670007 - 10 - DETAILS.dwg CONSTRUCTION DETAILS - 1 Jul 09, 2026 10:53am by cdavis

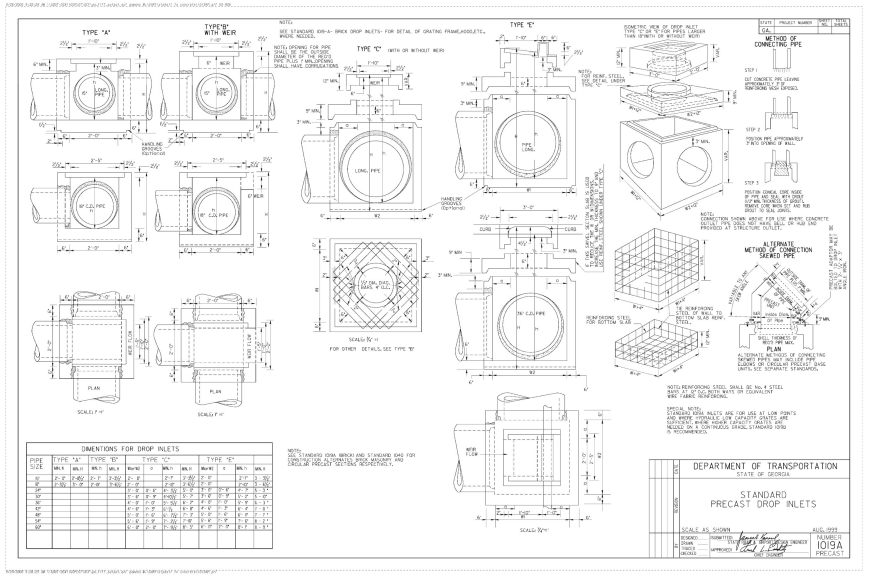

GDOT INLET DETAIL

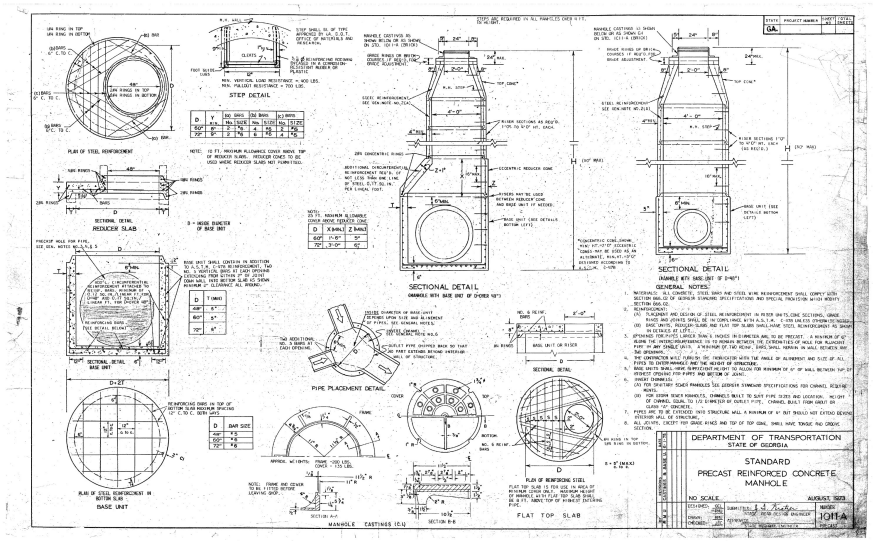

GDOT MANHOLE DETAIL

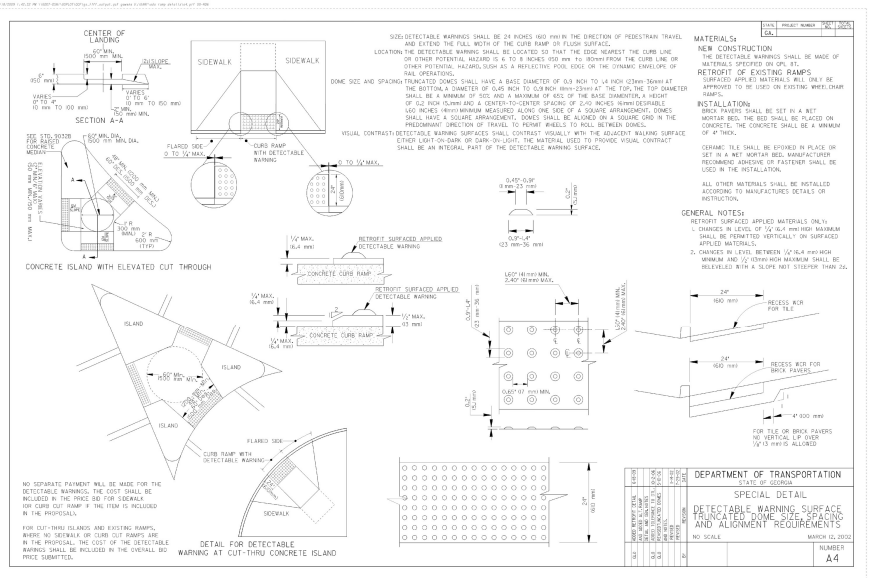

GDOT DETECTABLE WARNING DETAIL

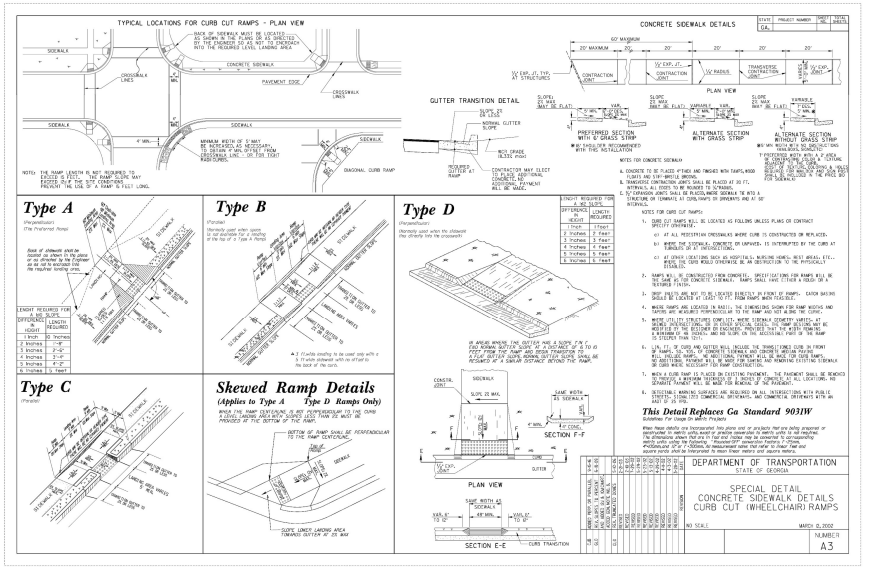

GDOT ADA RAMP DETAIL

PREPARED IN THE OFFICE OF:

GASKINS + LECRAW
a PAPE-DAWSON company
© 2026 GASKINS + LECRAW
3475 CORPORATE WAY
SUITE A
DULUTH, GA 30096
PHONE - 678.546.8100
www.gaskinslecraw.com

PEF008127

REVISIONS:

NO.	DESCRIPTION	DRAWN BY	CHECKED BY	DATE
1				
2				
CLIENT
PRAXIS3
100 PEACHTREE STREET NW, SUITE 1450, ATLANTA, GEORGIA 30303

PROJECT
FIFTH THIRD BANK - WARNER ROBINS, GA
2711 WATSON BLVD
PARCEL ID: 0W0780-005000
WARNER ROBINS, HOUSTON COUNTY, GEORGIA

SEAL:

FOR INFORMATIONAL PURPOSES ONLY

CALL BEFORE YOU DIG

811 Know what's below. Call before you dig.

SCALE & NORTH ARROW:

DETAILS ARE NOT DRAWN TO SCALE

DESIGN INFO:

DRAWN BY:	JOA
DESIGNED BY:	MAT
REVIEWED BY:	TKS
JOB #:	75670007
DATE:	JULY 9, 2026

CONSTRUCTION DETAILS - 2

C-6.1

This document, together with the concepts and designs presented herein, as an instrument of service, is intended only for the specific purpose and client for which it was prepared. Reuse of and improper reliance on this document without written authorization and adaptation by Gaskins + LeCraw, a Pape-Dawson Company shall be without liability to Gaskins + LeCraw, a Pape-Dawson Company. Copyright Gaskins + LeCraw, a Pape-Dawson Company, 2026